


9/03/2026 12:15:43 PM C:\Projects\STANWELL-Building\PC-Central\Files_jaydn.b.rvt

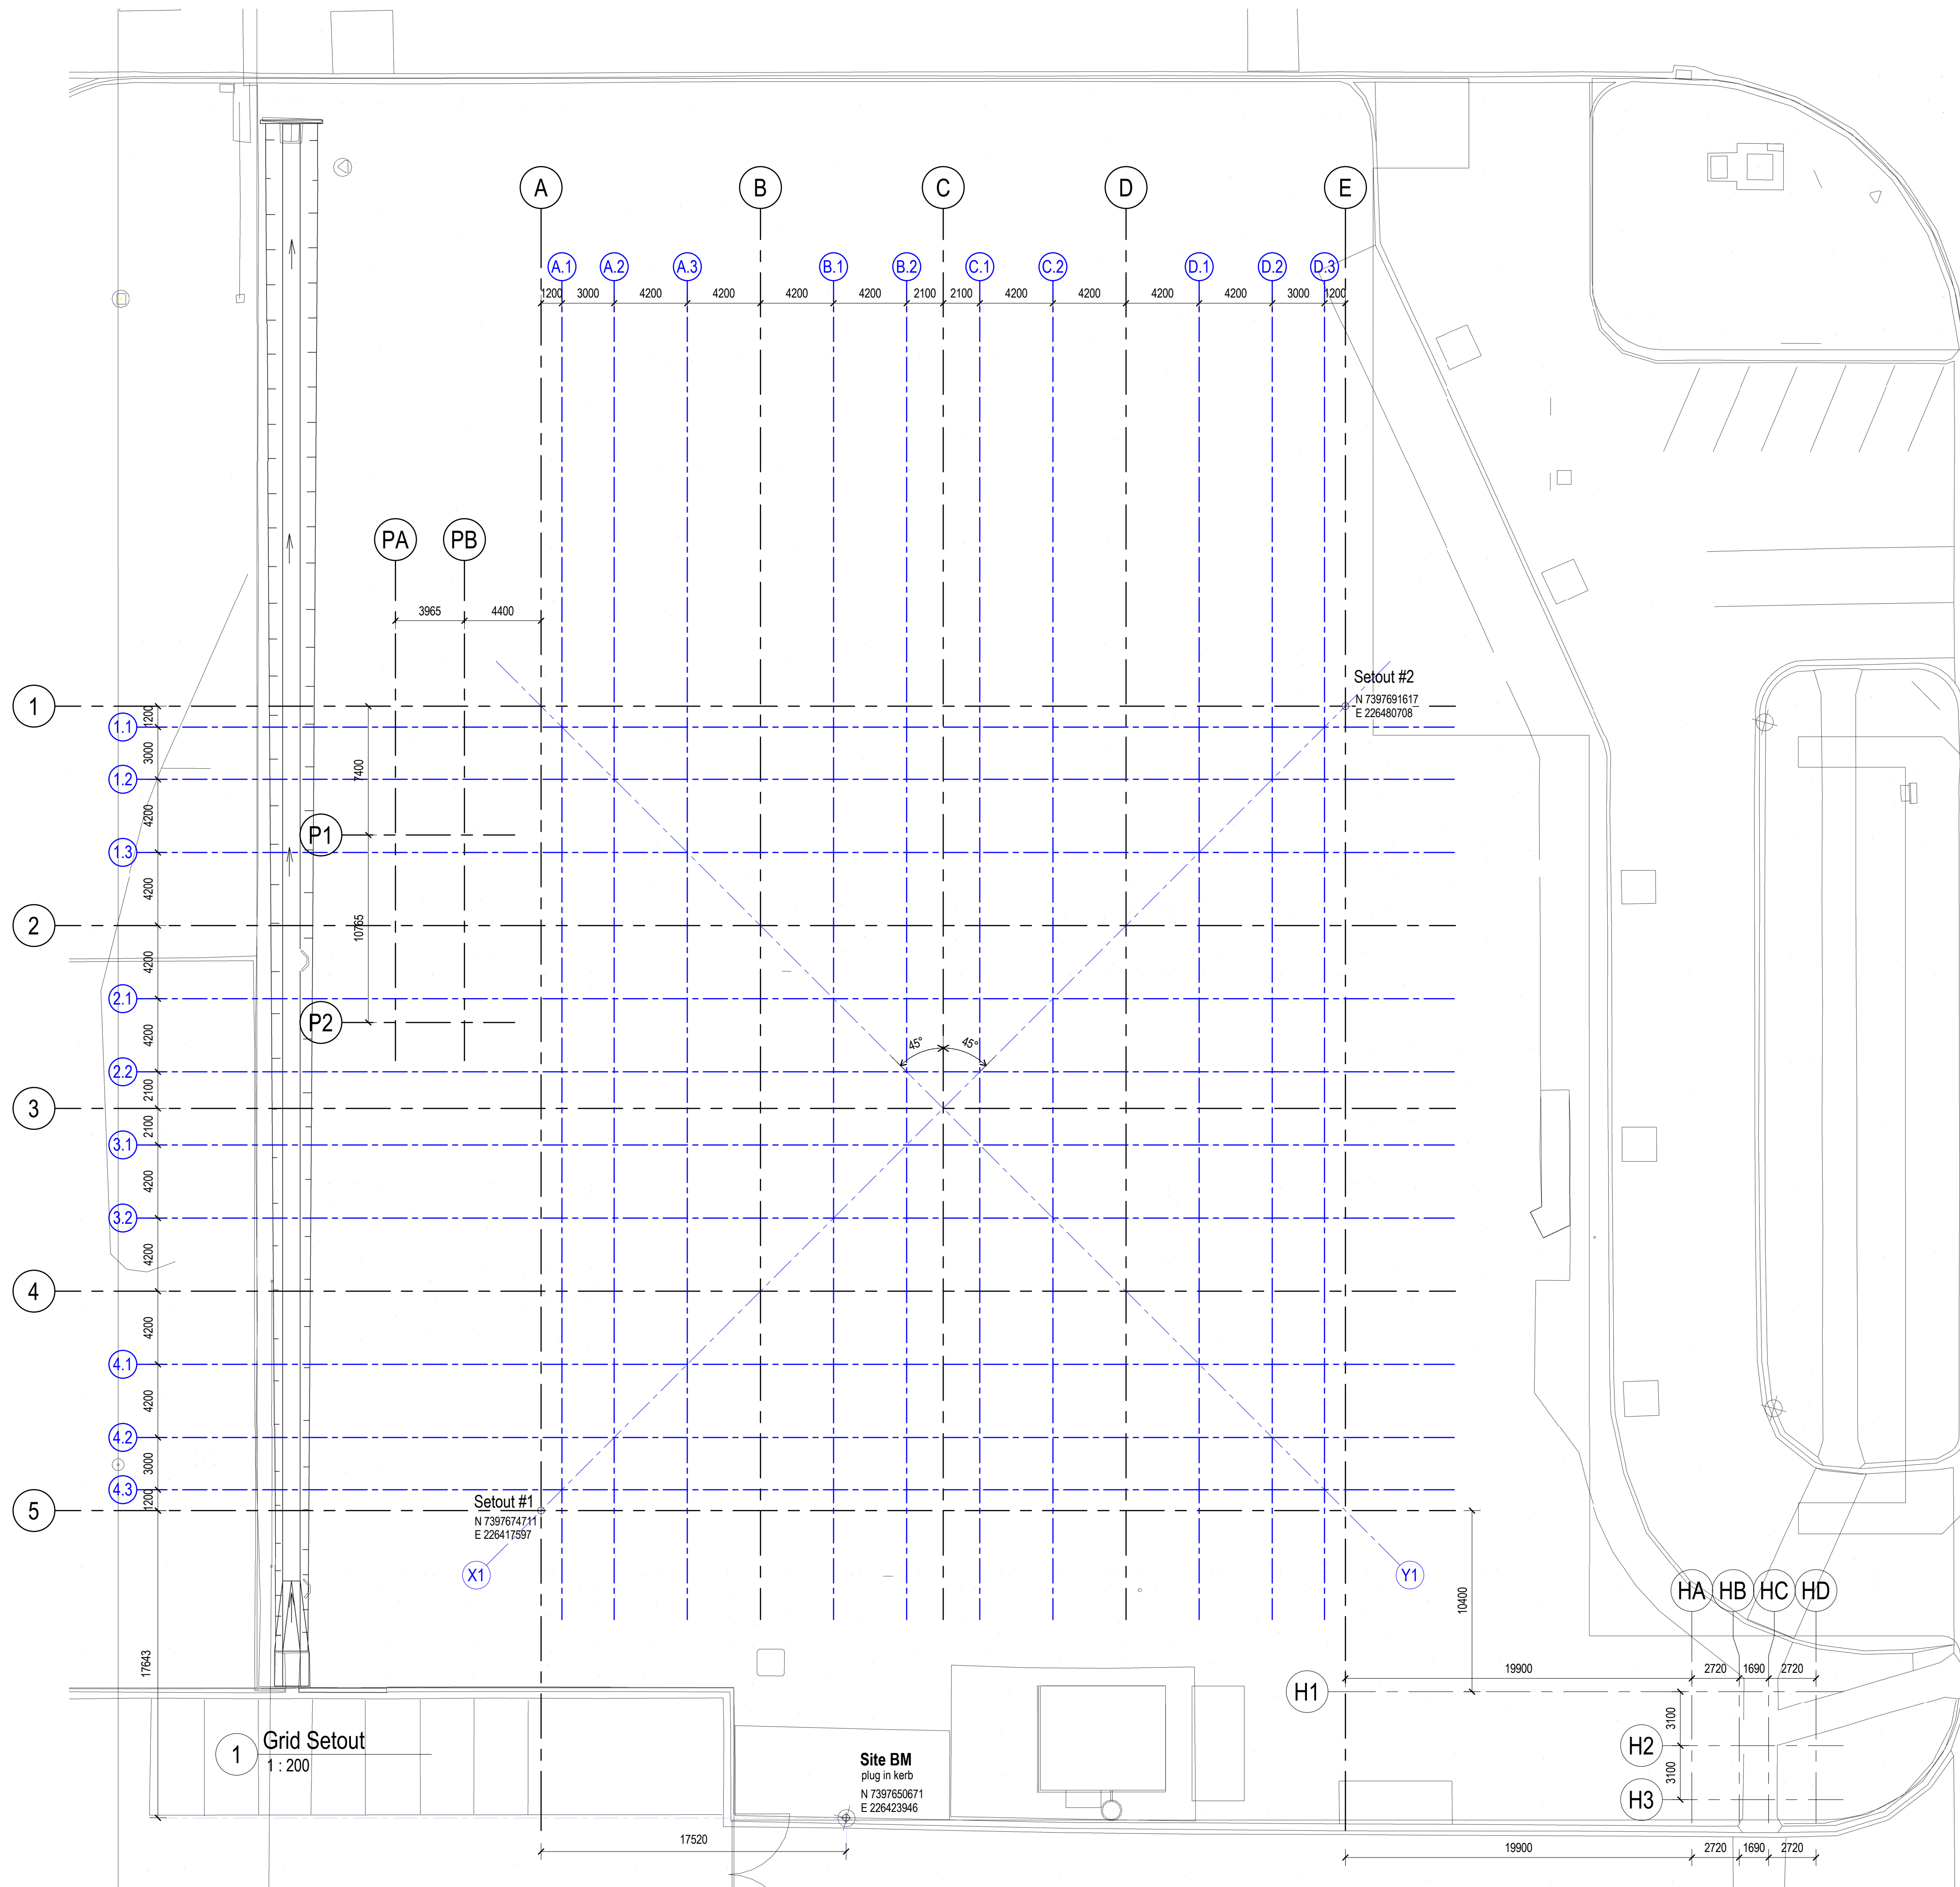

GRID NOTES

- Survey information has been taken from survey prepared by Capricorn Survey Group
Phone: (07) 4927 5199
CAD File: 955540 3D Final.dwg
PDF: 9555-40-DTL-A.pdf
- Survey is aligned to MGA (Map Grid Australia).
- Contractor to engage a registered surveyor for setout of grids & key points on site.

rev	date	description	initial
T1	11/03/2026	For Tender	JB

PRELIMINARY
NOT FOR CONSTRUCTION

Drawings include colour information. A black & white copy may not have all the information. This background is coloured blue.

brian hooper**architect**
m3architecture
ph: +61 7 3831 4644
11 saint james street petrie tce q 4000
info@m3architecture.com
www.m3architecture.com

client **stanwell**

project **Stanwell New Projects Office**
Switchyard Road,
Stanwell, QLD, 4702

title **Grid and Setout Plan**

drawn bg
checked jb
date March 2026
scale As indicated at A1
drawing **25010 / cd A-050001 / T1**

copyright ©
These designs, plans, specifications and the copyright herein are the property of the architect and must not be used, reproduced, or copied wholly or in part without the written permission of m3architecture Pty Ltd abn 23 079 044 545.
Use figured dimensions in preference to scale.
If there are any questions contact the architect.

1:200 at A1
0 1 2 3 4 5 6 7 8 9 10m