


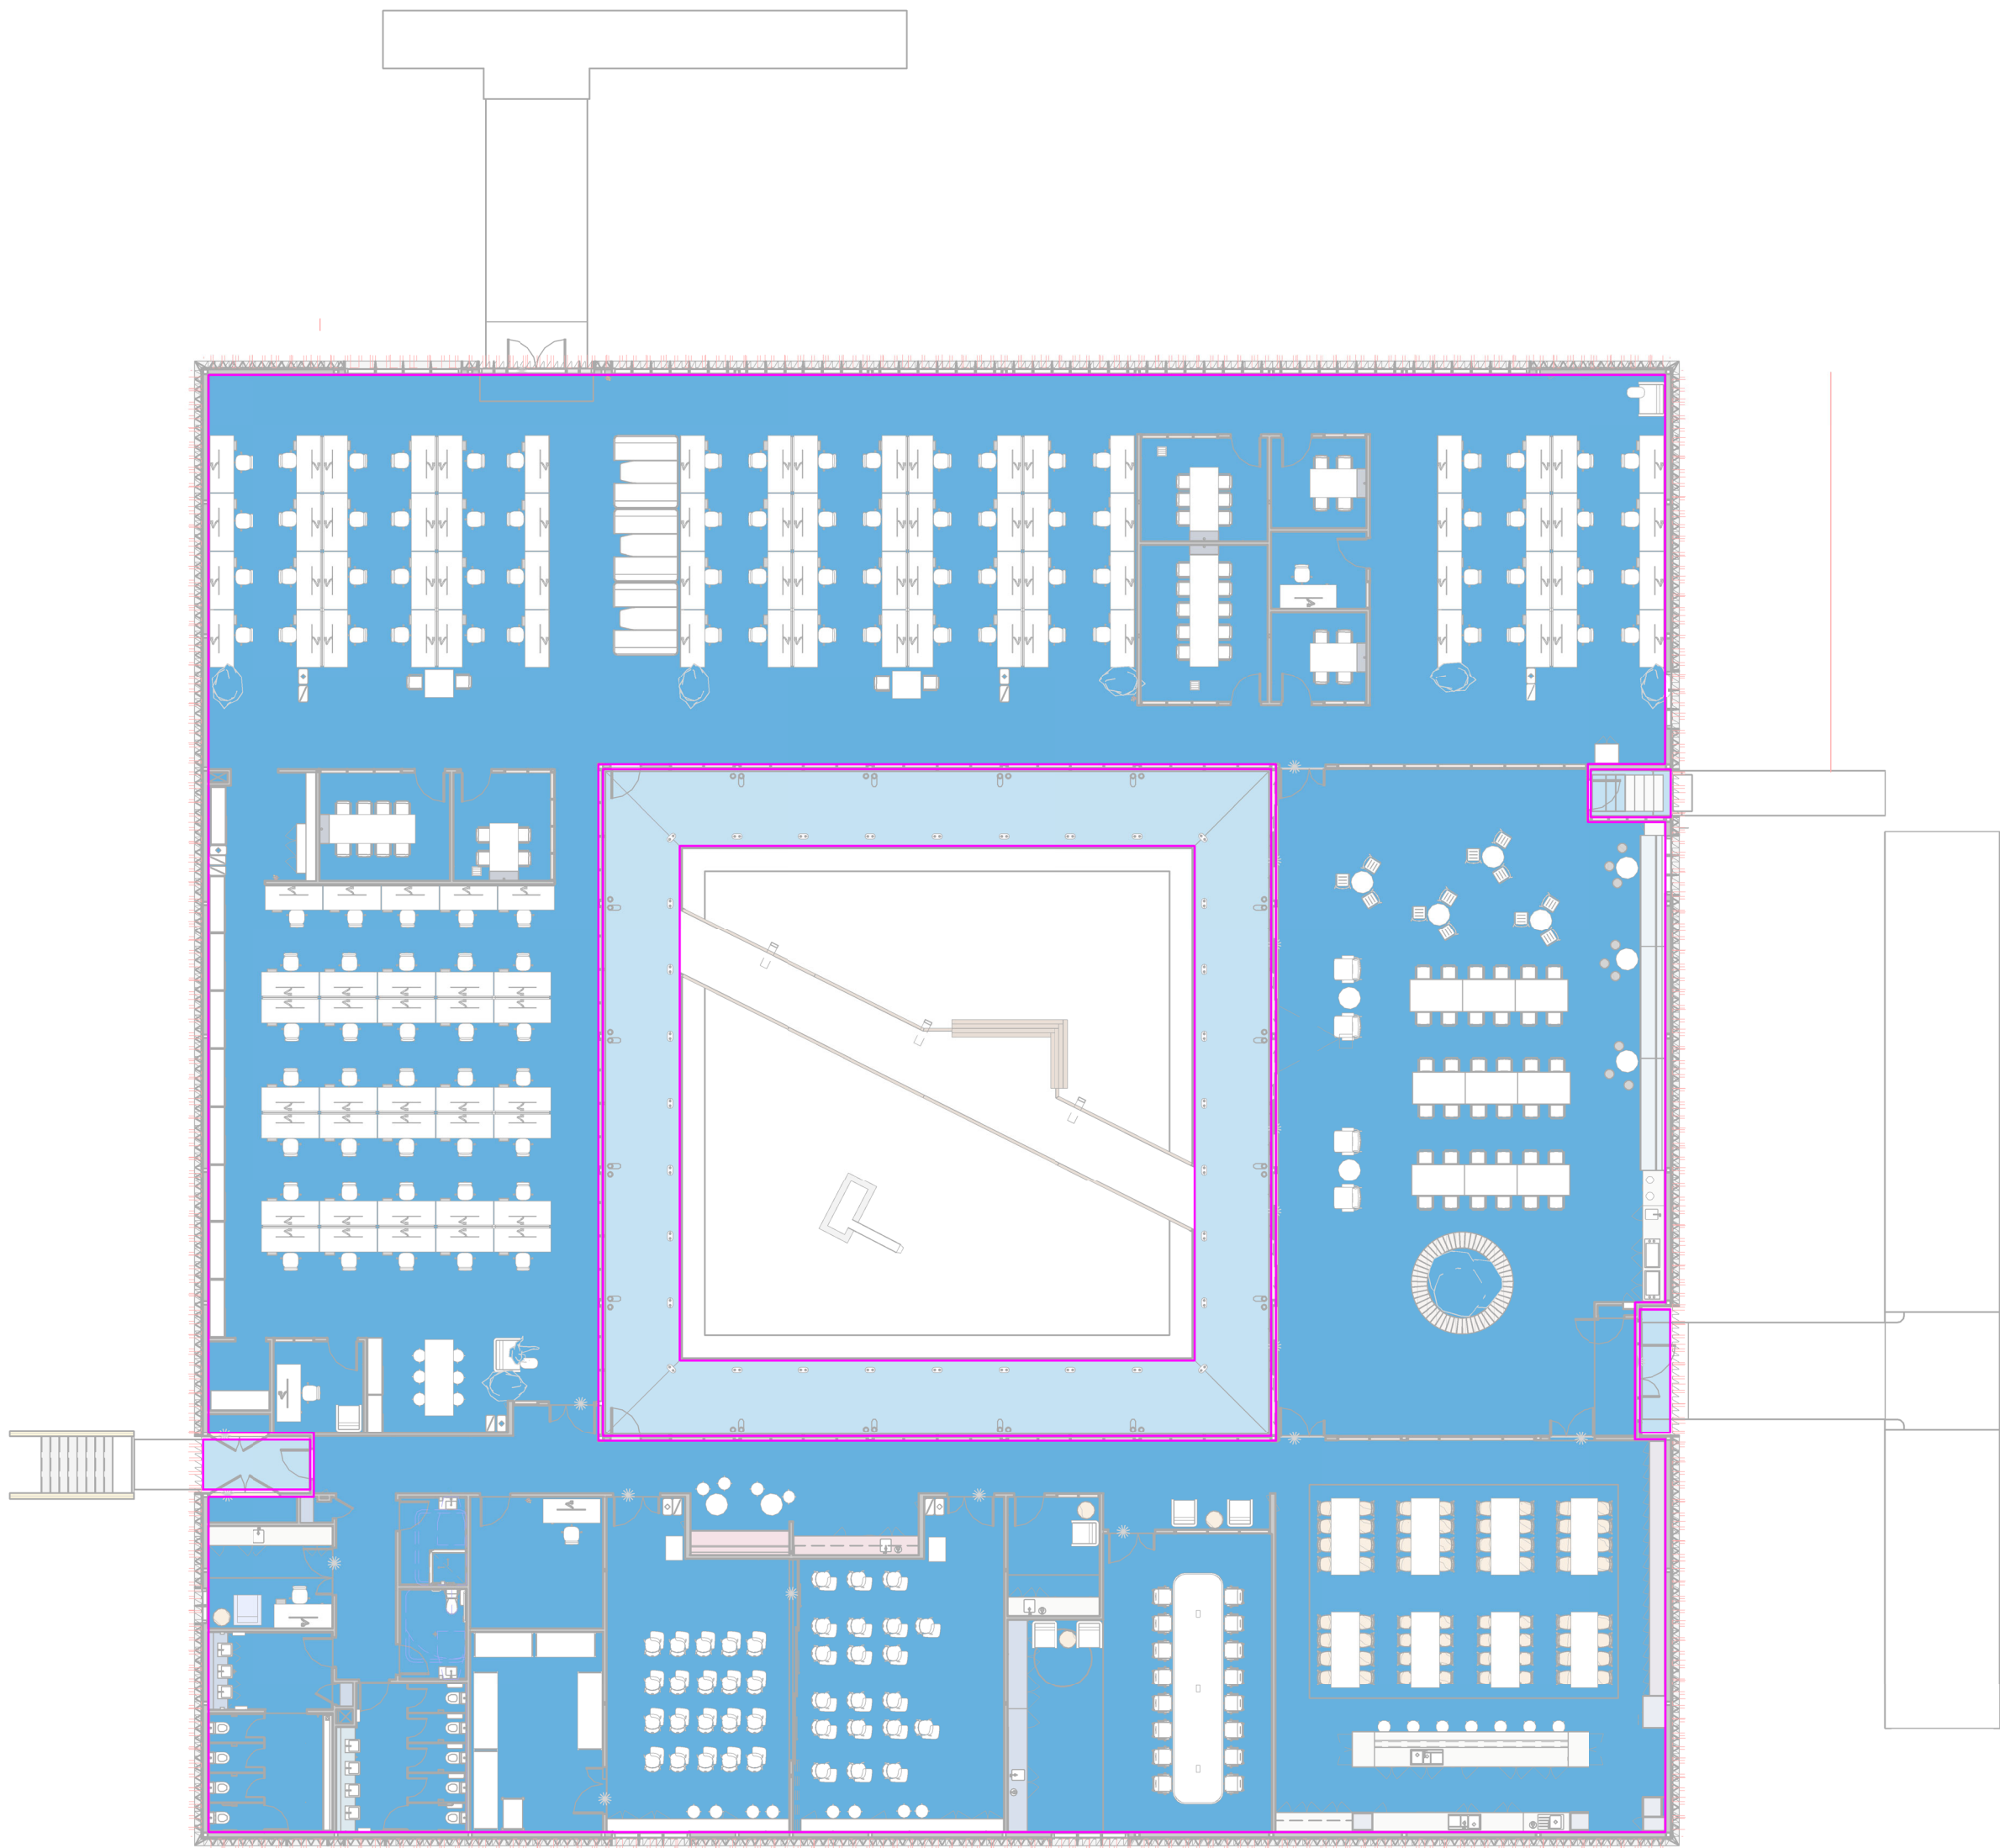

Proposed FECA	
Level	Area
Level 0	1633.94 m²
Total Area	1633.94 m²

Proposed UCA	
Level	Area
Level 0	191.28 m²
Total Area	191.28 m²

Proposed GFA	
Name	Area
FECA New	1633.94 m²
UCA New	191.28 m²
Total Area	1825.22 m²

Area Measurement and Definitions
The method of building area measurement is based on that used by the Australian Institute of Quantity Surveyors (AIQS). Area definitions are reprinted below from the AIQS Book of Areas (August 2000) for analysis and comparison of buildings.

Method of Measurement of Building Areas
Gross Floor Area (GFA)
The sum of the 'Fully Enclosed Covered Area' and 'Unenclosed Covered Area' as defined. Unit of Measurement: Square Metre (m2)

Fully Enclosed Covered Area (FECA)
The sum of all such areas at all building floor levels, including basements (except unexcavated portions), floored roof spaces and attics, garages, penthouses, enclosed porches and attached enclosed covered ways alongside buildings, equipment rooms, lift shafts, vertical ducts, staircases and any other fully enclosed spaces and useable areas of the building, computed by measuring from the normal inside face of exterior walls but ignoring any projections such as plinths, columns, piers and the like which project from the normal inside face of exterior walls. It shall not include open courts, light wells, connecting or isolated covered ways and net open areas of upper portions of rooms, lobbies, halls, interstitial spaces and the like which extend through the storey being computed. Unit of Measurement: Square Metres (m2)

Unenclosed Covered Area (UCA)
The sum of all such areas at all building floor levels, including roofed balconies, open verandahs, porches and porticos, attached open covered ways alongside buildings, undercrofts and useable space under buildings, unenclosed access galleries (including ground floor) and any other trafficable covered areas of the building which are not totally enclosed by full height walls, computed by measuring the area between the enclosing walls or balustrade (i.e. from the inside face of the U.C.A. excluding the wall or balustrade thickness). When the covering element (i.e. roof or upper floor) is supported by columns, is cantilevered or is suspended, or any combination of these, the measurements shall be taken to the edge of the paving or to the edge of the cover, whichever is the lesser. U.C.A. shall not include eaves overhangs, sun shading, awnings and the like where these do not relate to clearly defined trafficable covered areas, nor shall it include connecting or isolated covered ways. Unit of Measurement: Square Metres (m2)

PRELIMINARY
NOT FOR CONSTRUCTION

Drawings include colour information. A black & white copy may not have all the information. This background is coloured blue.

brian hooper**architect**
m3architecture
ph: +61 7 3831 4644
11 saint james street petrie tce q 4000
info@m3architecture.com
www.m3architecture.com



project **Stanwell New Projects Office**
Switchyard Road,
Stanwell, QLD, 4702
title **Area Plan - FECA and UCA**

drawn bg
checked jb
date March 2026
scale As indicated at A1
drawing **25010 / cd A-060001 / T1**

copyright ©
These designs, plans, specifications and the copyright herein are the property of the architect and must not be used, reproduced, or copied wholly or in part without the written permission of m3architecture Pty Ltd abn 23 079 044 545.
Use figured dimensions in preference to scale.
If there are any questions contact the architect.

