


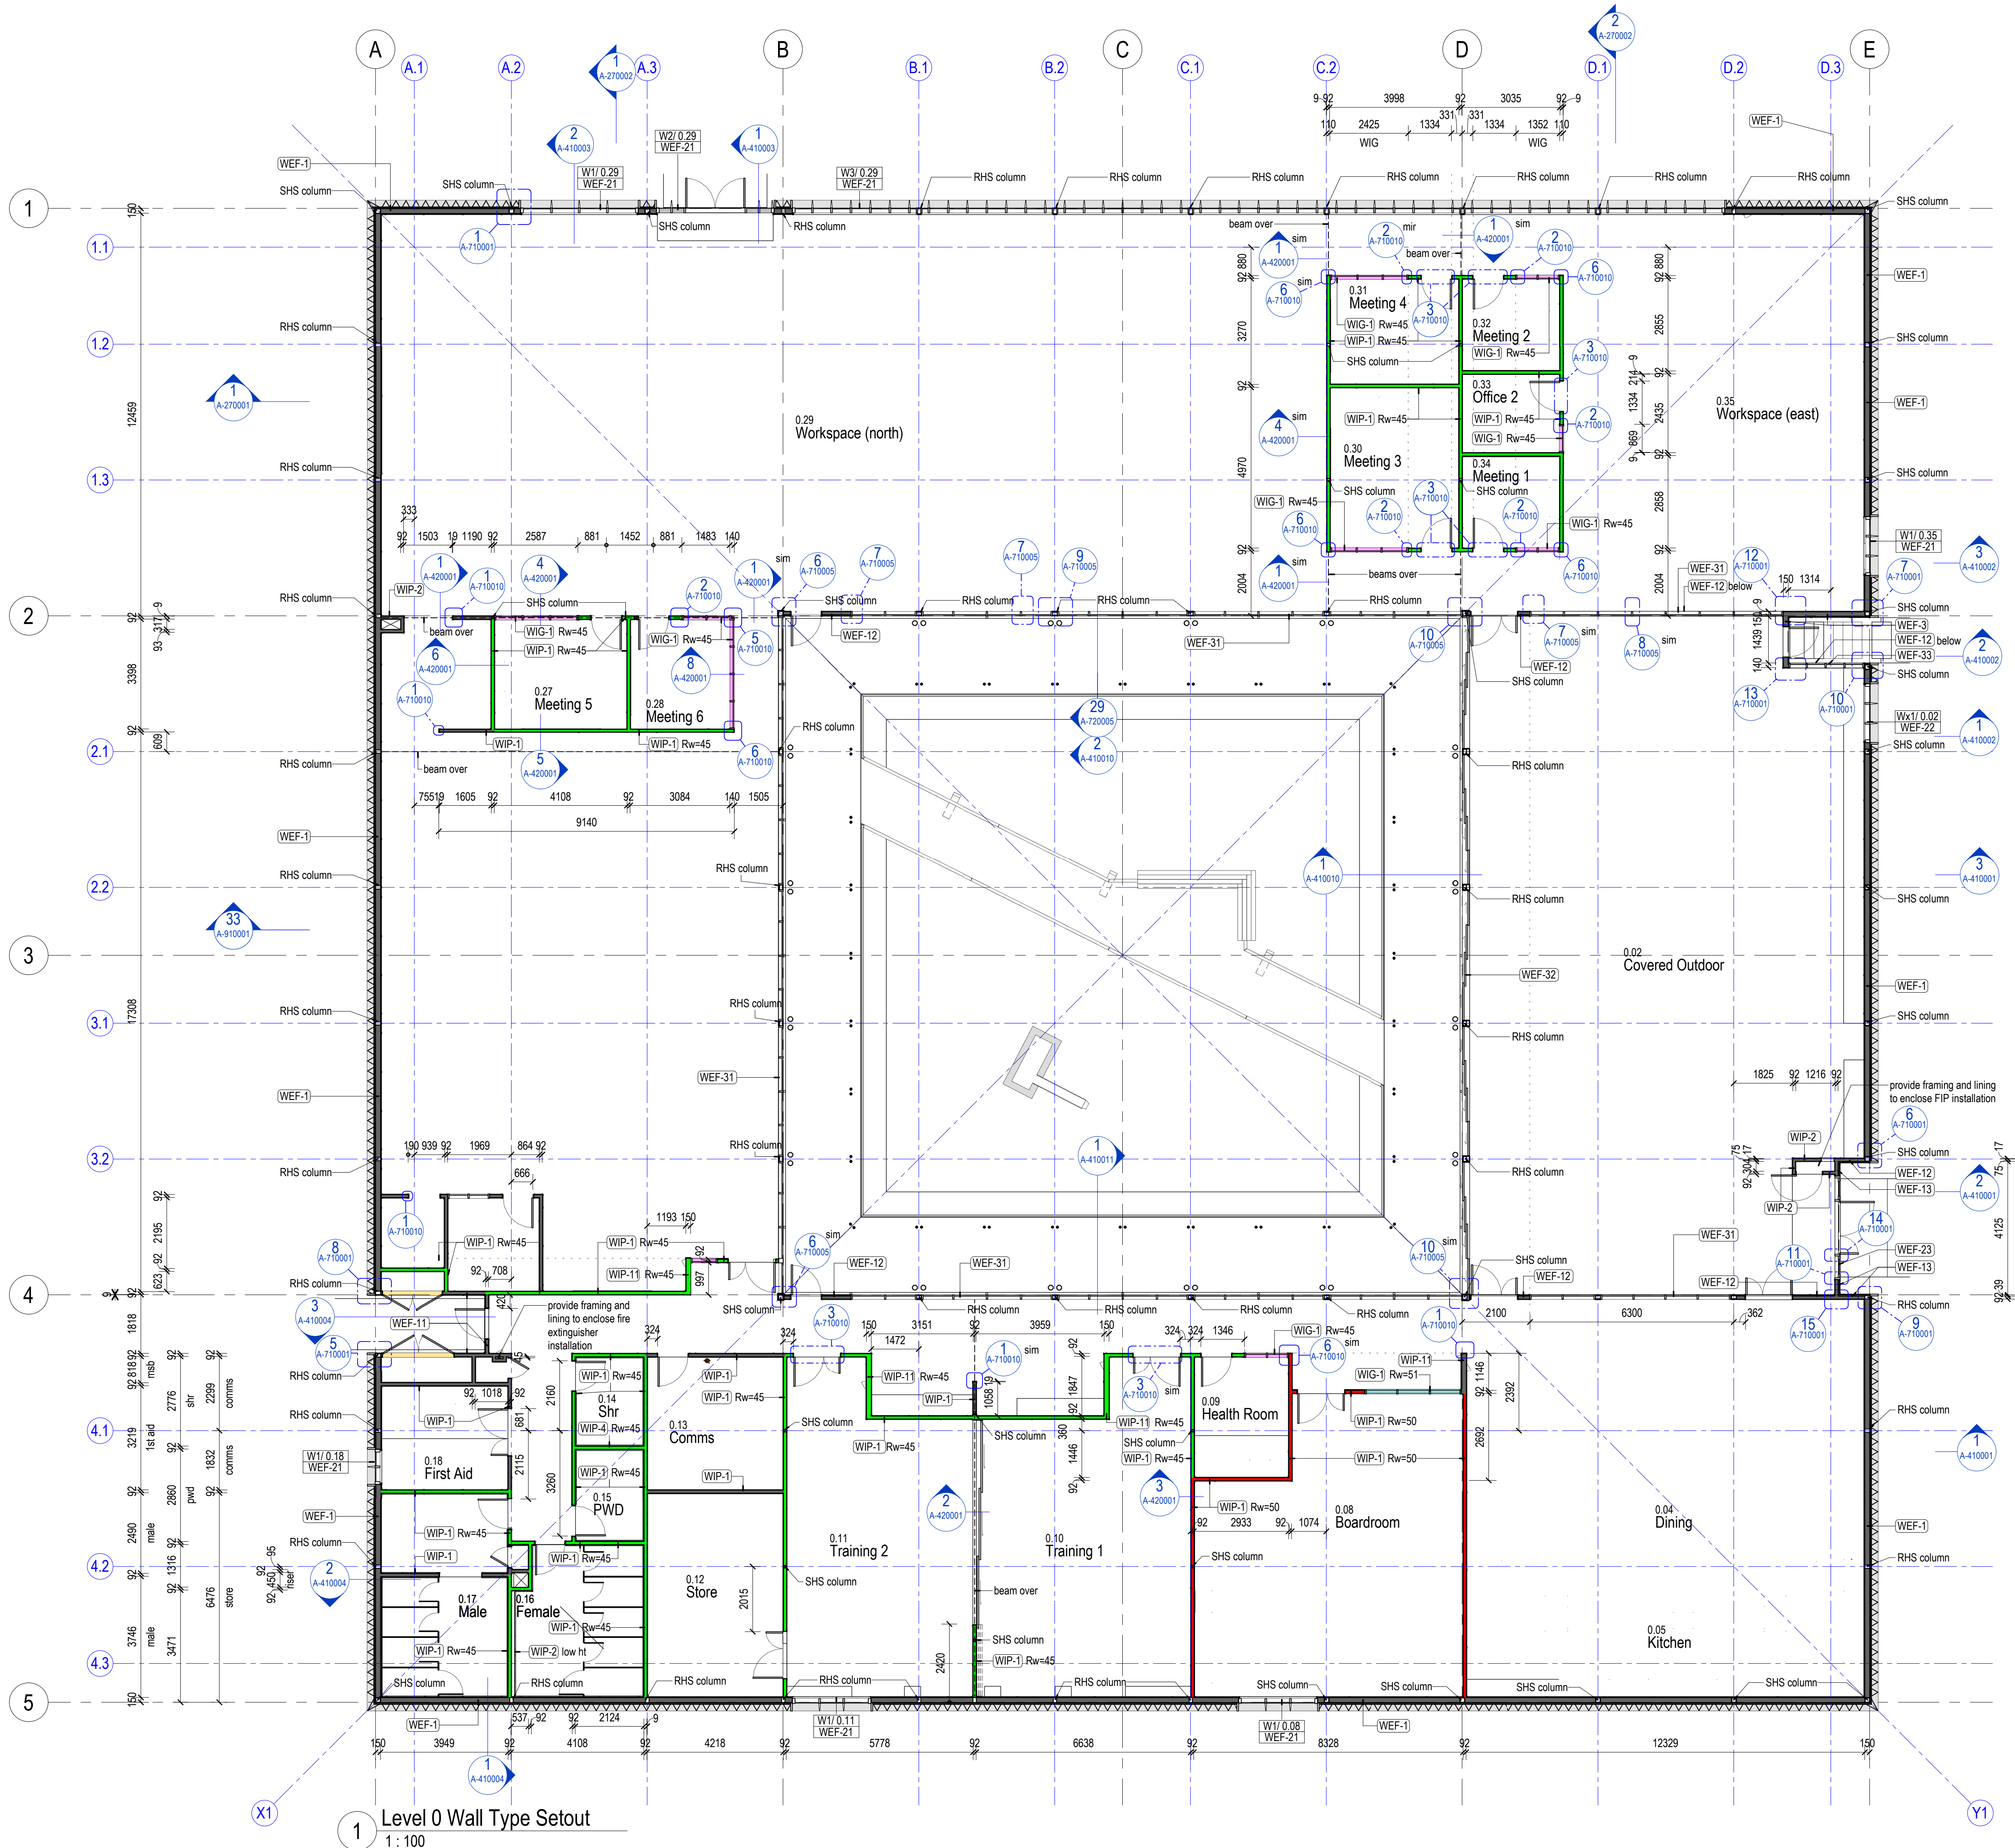

- WALL LEGEND**
- Solid Walls**
- Rw40 + R=1.4 (acoustic & thermal)
 - Rw45 (acoustic only)
 - Rw50 (acoustic only)
- Glazed Walls**
- Rw36 + R1.4 (acoustic + thermal)
 - Rw45 (acoustic only)
 - Rw51 (acoustic only)

- WALL NOTES**
- WN.01 Refer to Appendix B - Facade & Wall Schedule in addition to A-22 series drawings.
- WN.02 Refer to Acoustic Report for all acoustic requirements for partition walls, doors and glazing.
- WN.03 Refer to Structural Engineer for interface between wall types and structural design including bracing.
- WN.04 Refer to A-60 and A-61 series drawings for interior plans and elevations.
- WN.05 Refer to seismic design criteria.
- WN.06 External Facade: Refer to A-40 series plans for the external facade configuration including windows, cladding selections & setout and flashings. Note that not all windows are visible on this plan due to variations in heights.
- WN.07 Door setout is to critical side of door leaf, framing to allow for frame and rough opening dimensions.

Drawings include colour information. A black & white copy may not have all the information. This background is coloured blue.

brian hooperarchitect
m3architecture
ph: +61 7 3831 4644
11 saint james street petrie tce q 4000
info@m3architecture.com
www.m3architecture.com

client **stanwell**

project **Stanwell New Projects Office**
Switchyard Road,
Stanwell, QLD, 4702

title **Wall Types**

drawn bg
checked jb
date March 2026
scale 1:100 at A1
drawing 25010 / cd A-220001 / T1

copyright ©
These designs, plans, specifications and the copyright herein are the property of the architect and must not be used, reproduced, or copied wholly or in part without the written permission of m3architecture Pty Ltd abn 23 079 044 545.
Use figured dimensions in preference to scale.
If there are any questions contact the architect.

1:1 at A1
0 10 20 30 40 50mm