



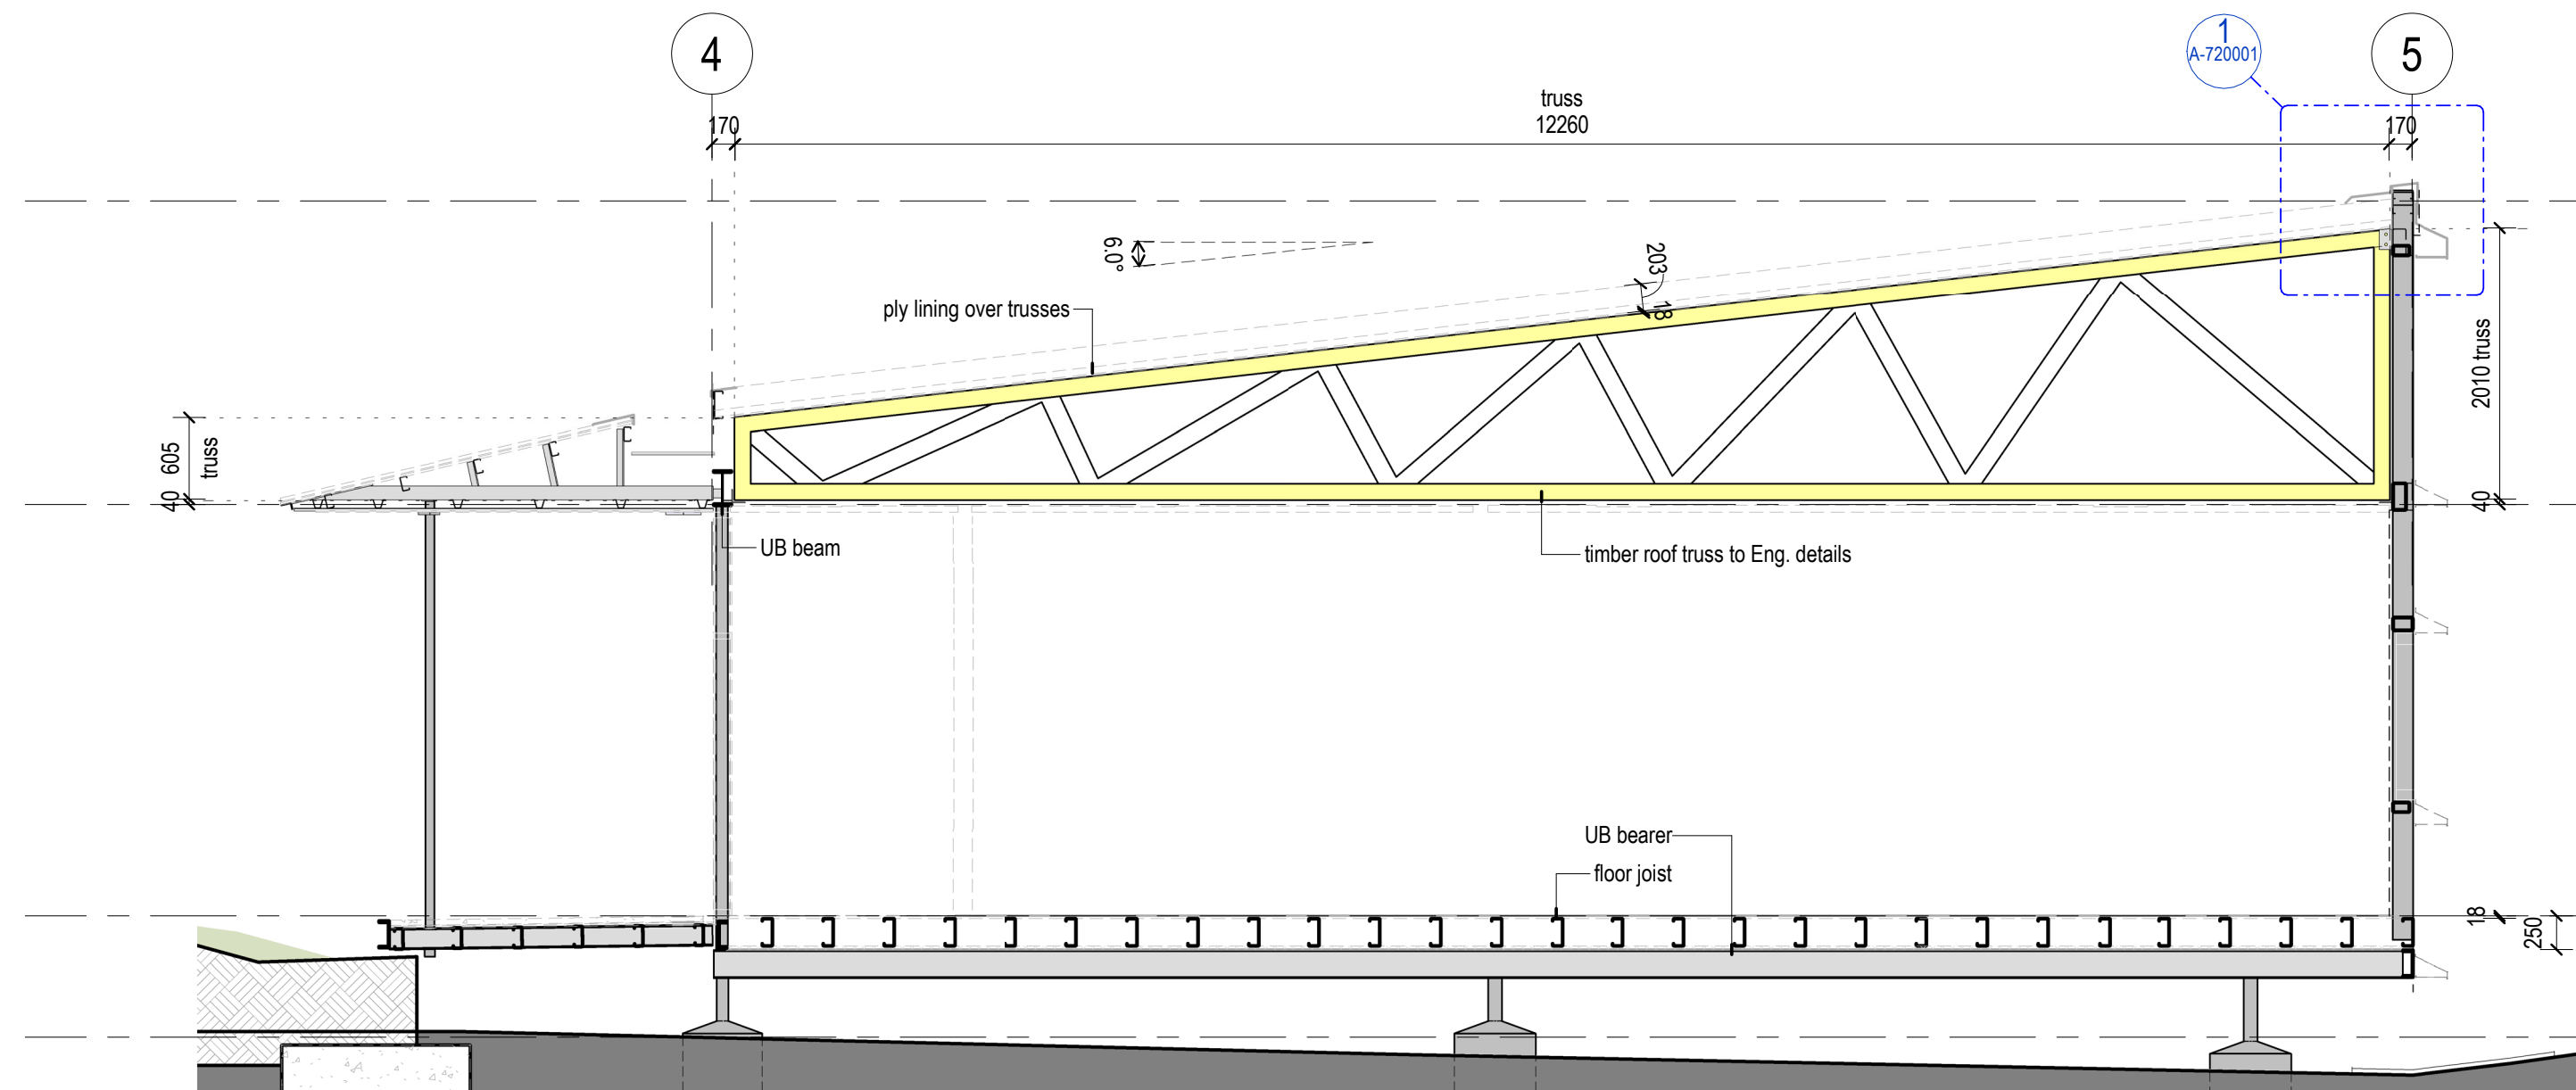


1 Detail Section - Typical
1 : 50 Full Truss Configuration

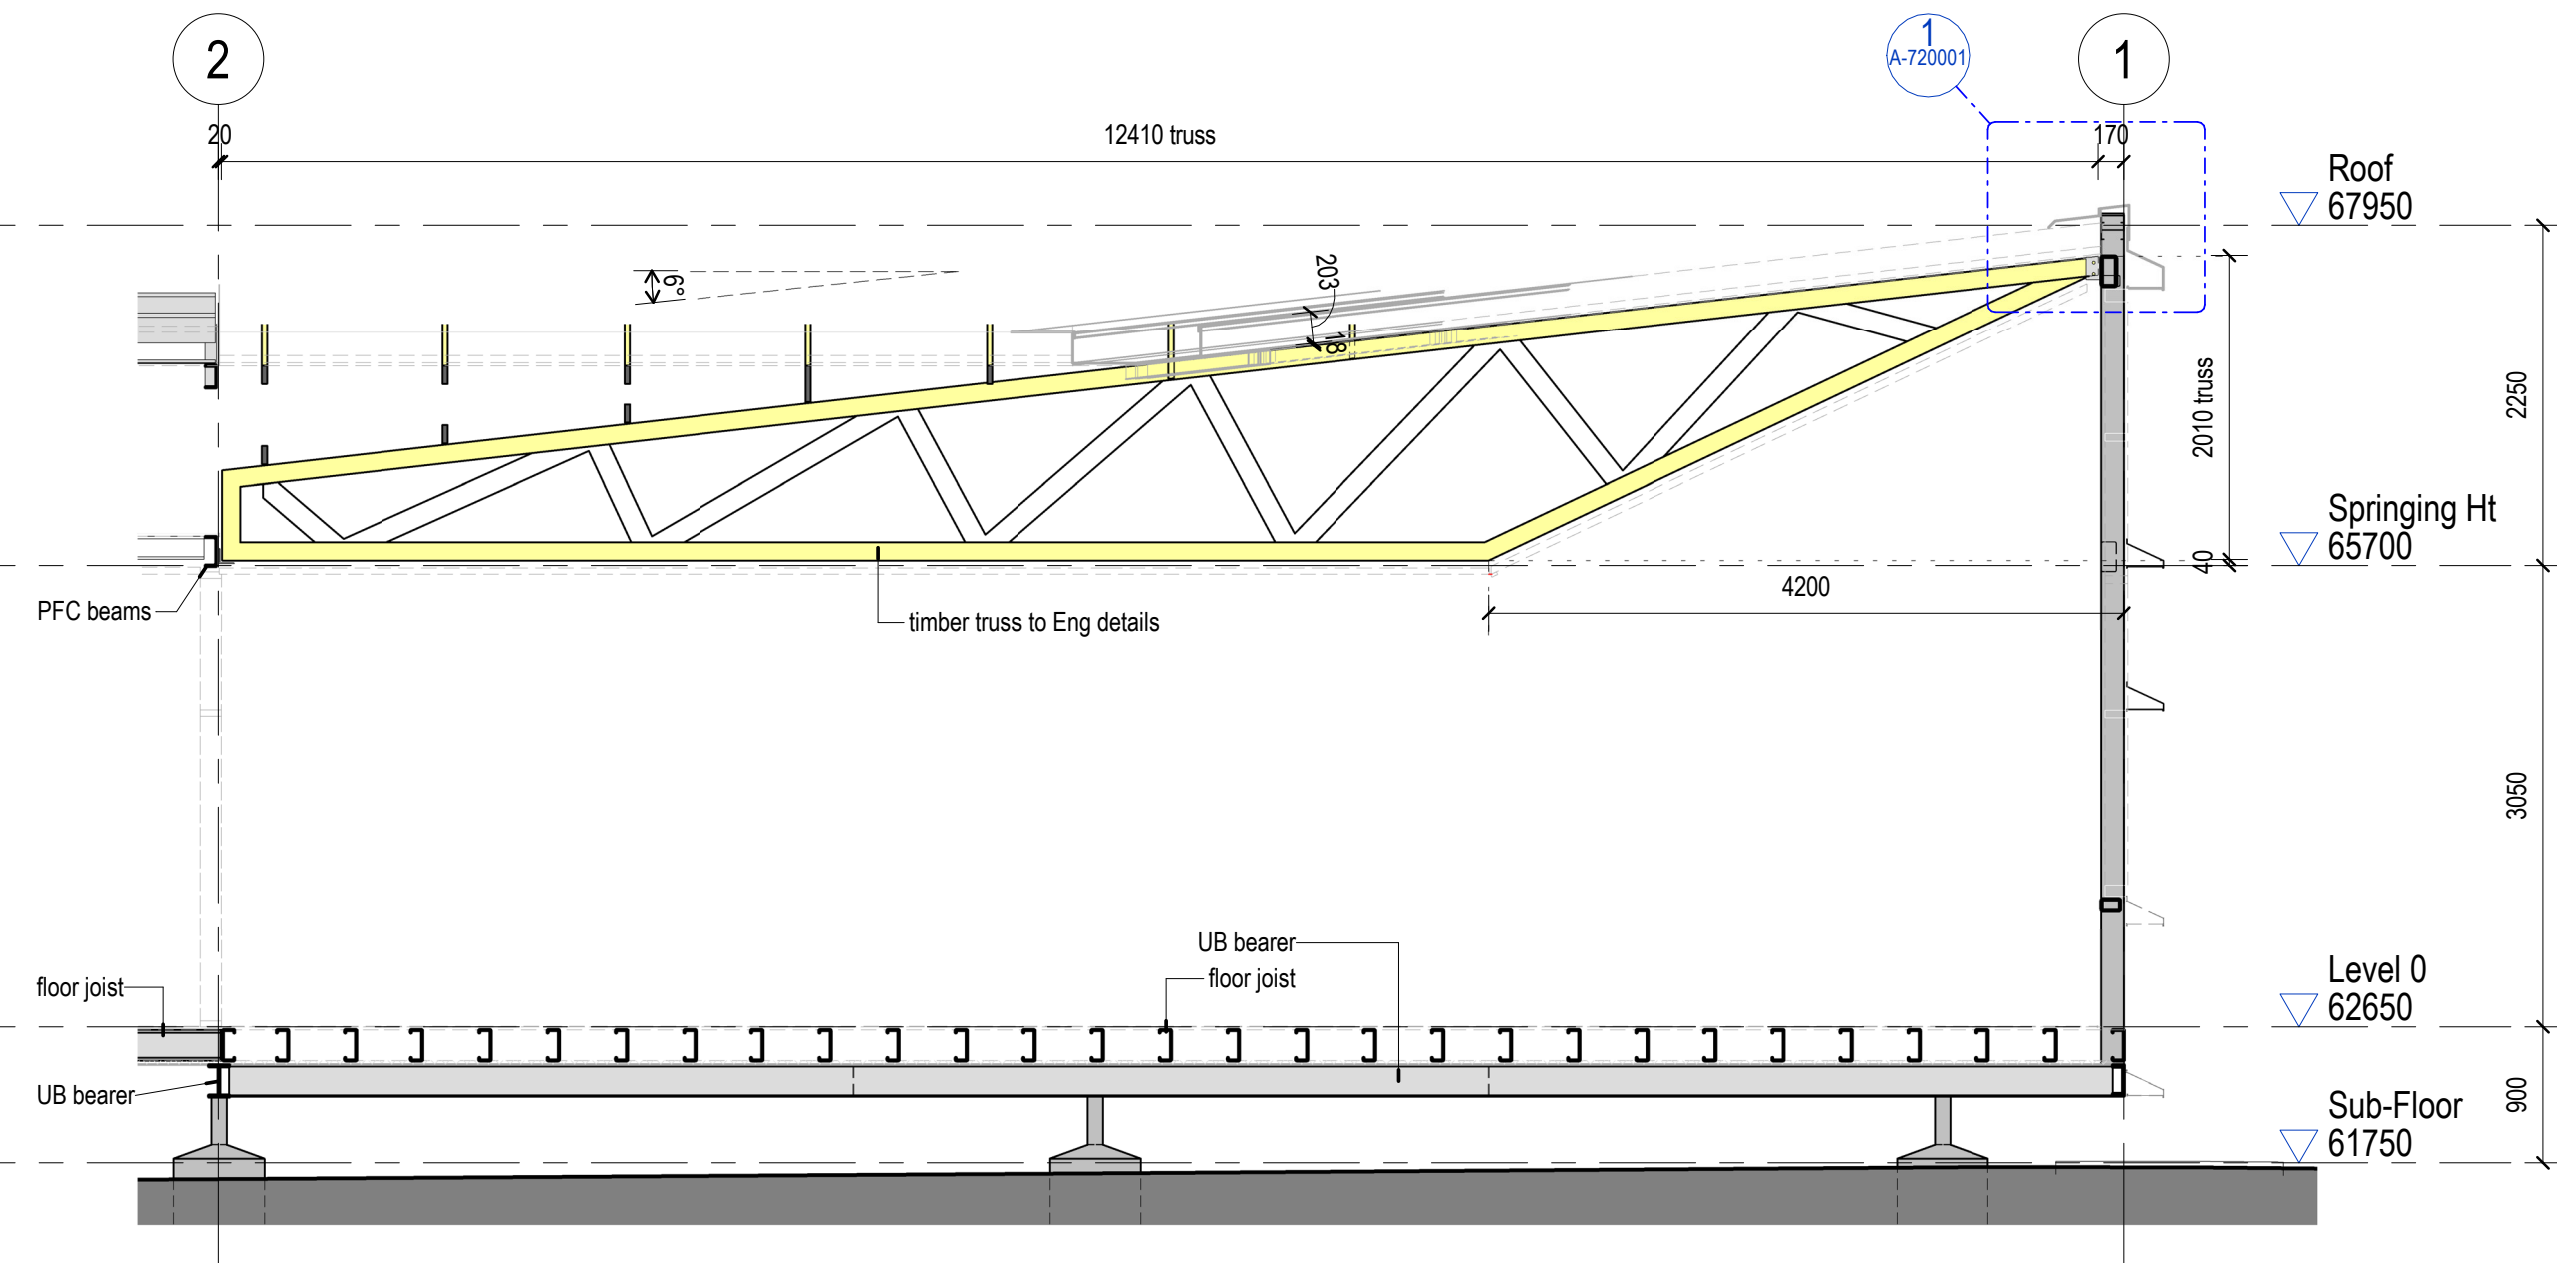


2 Detail Section - Raking Ceiling
1 : 50 Truncated Truss
Configuration

TRUSS NOTES

TN.1 For trusses refer to structural drawings. Trusses are shown indicatively. Truss set out is critical for mechanical servicing. Changes to the truss set out to be approved by the superintendent; contractor to coordinate services.

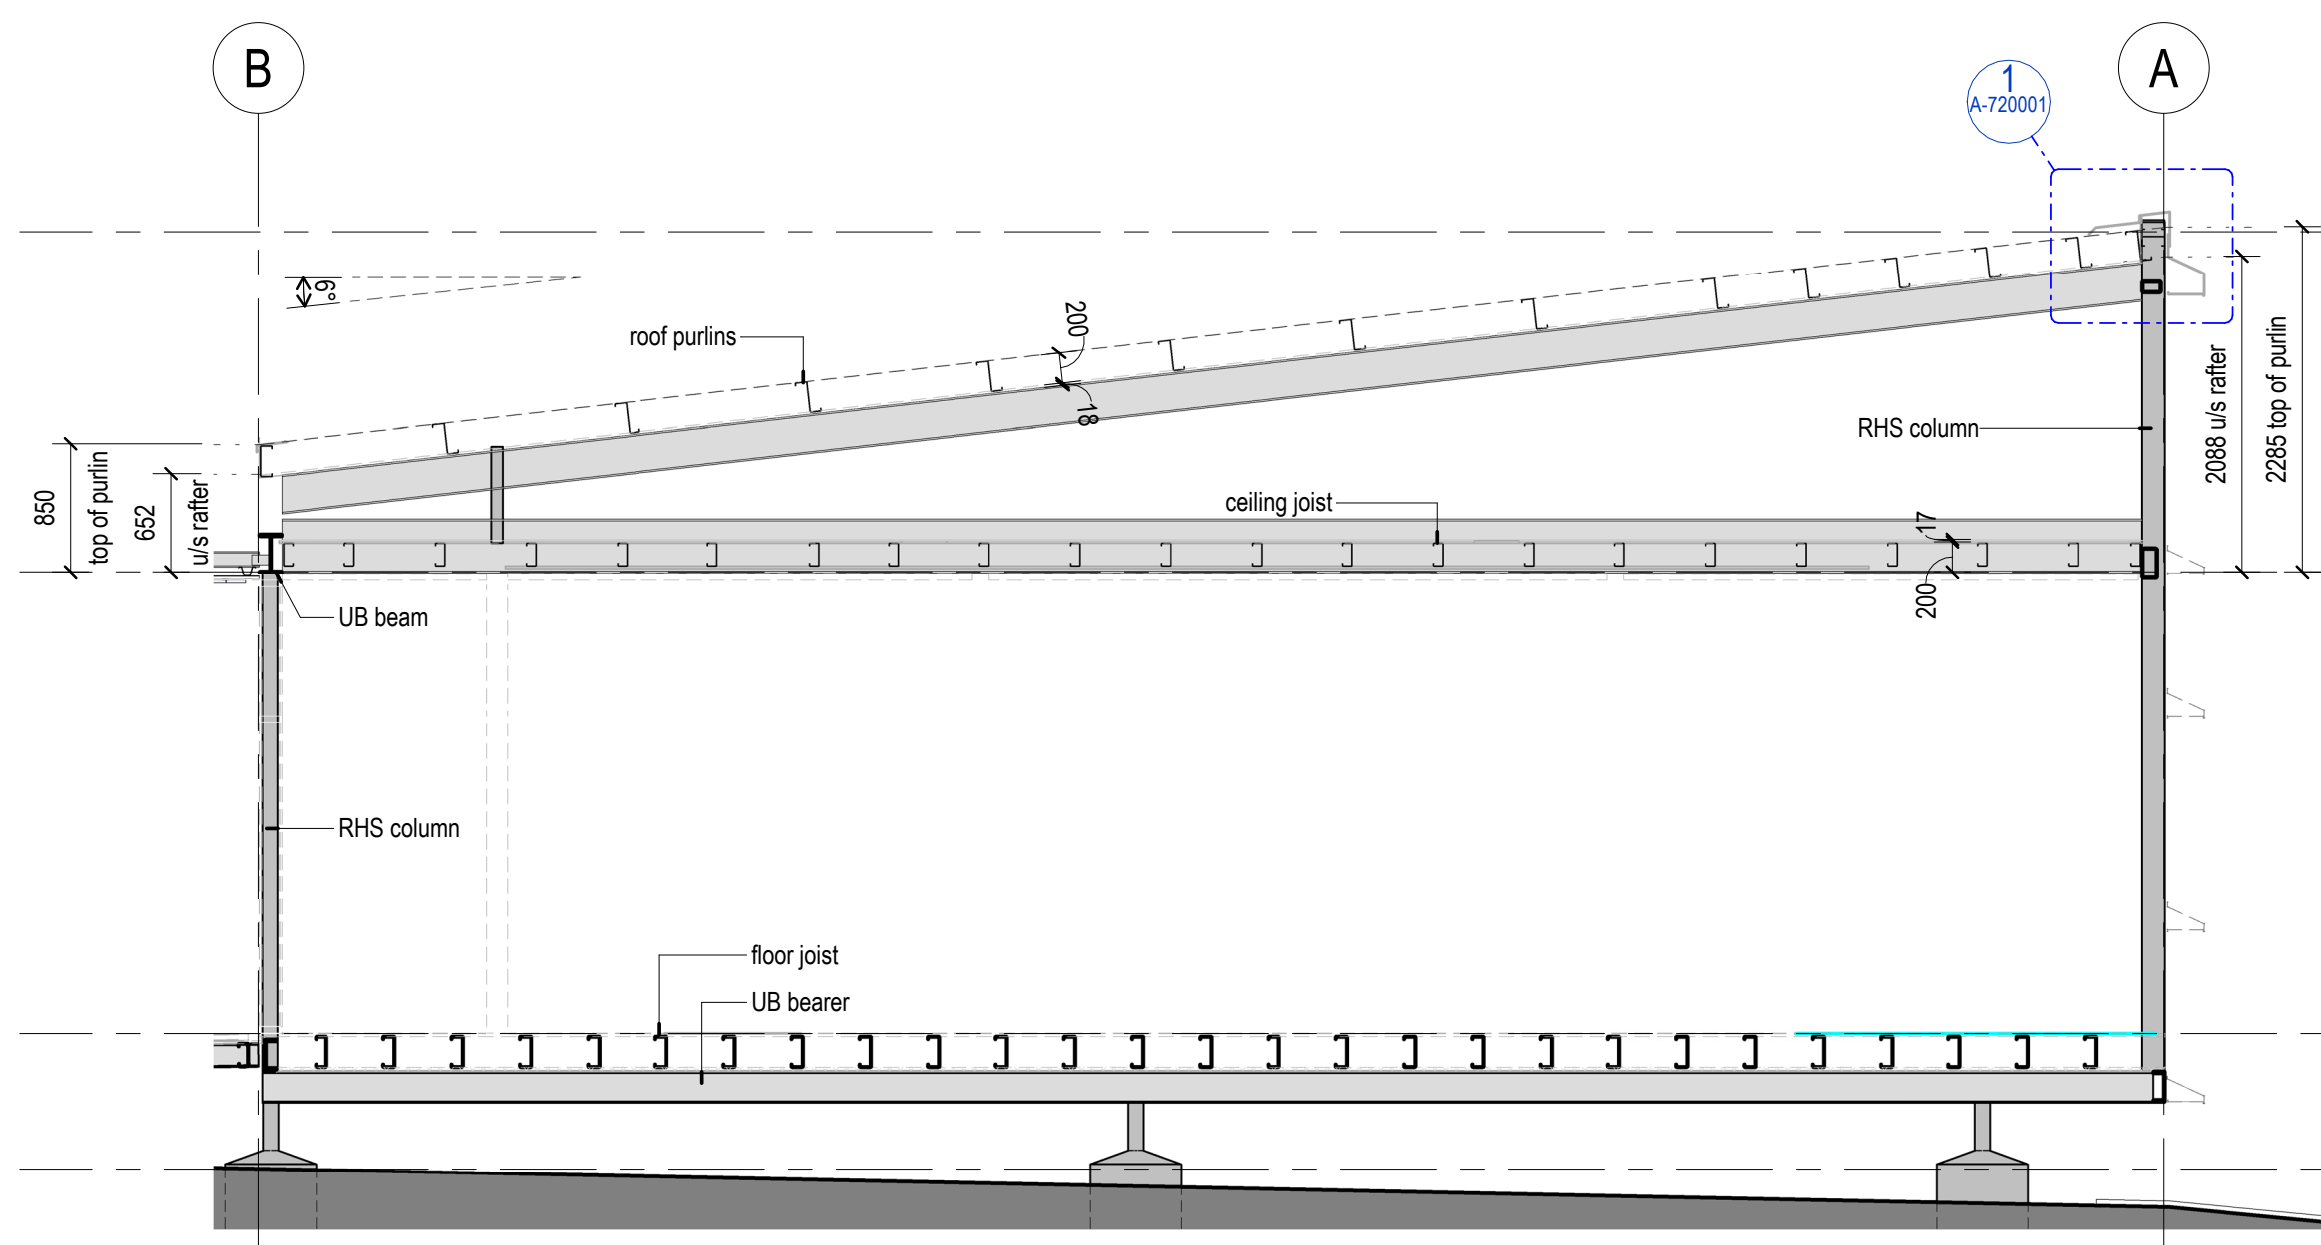

3 Detail Section - Plant Room Over Offices
1 : 50 Steel Roof Purlins

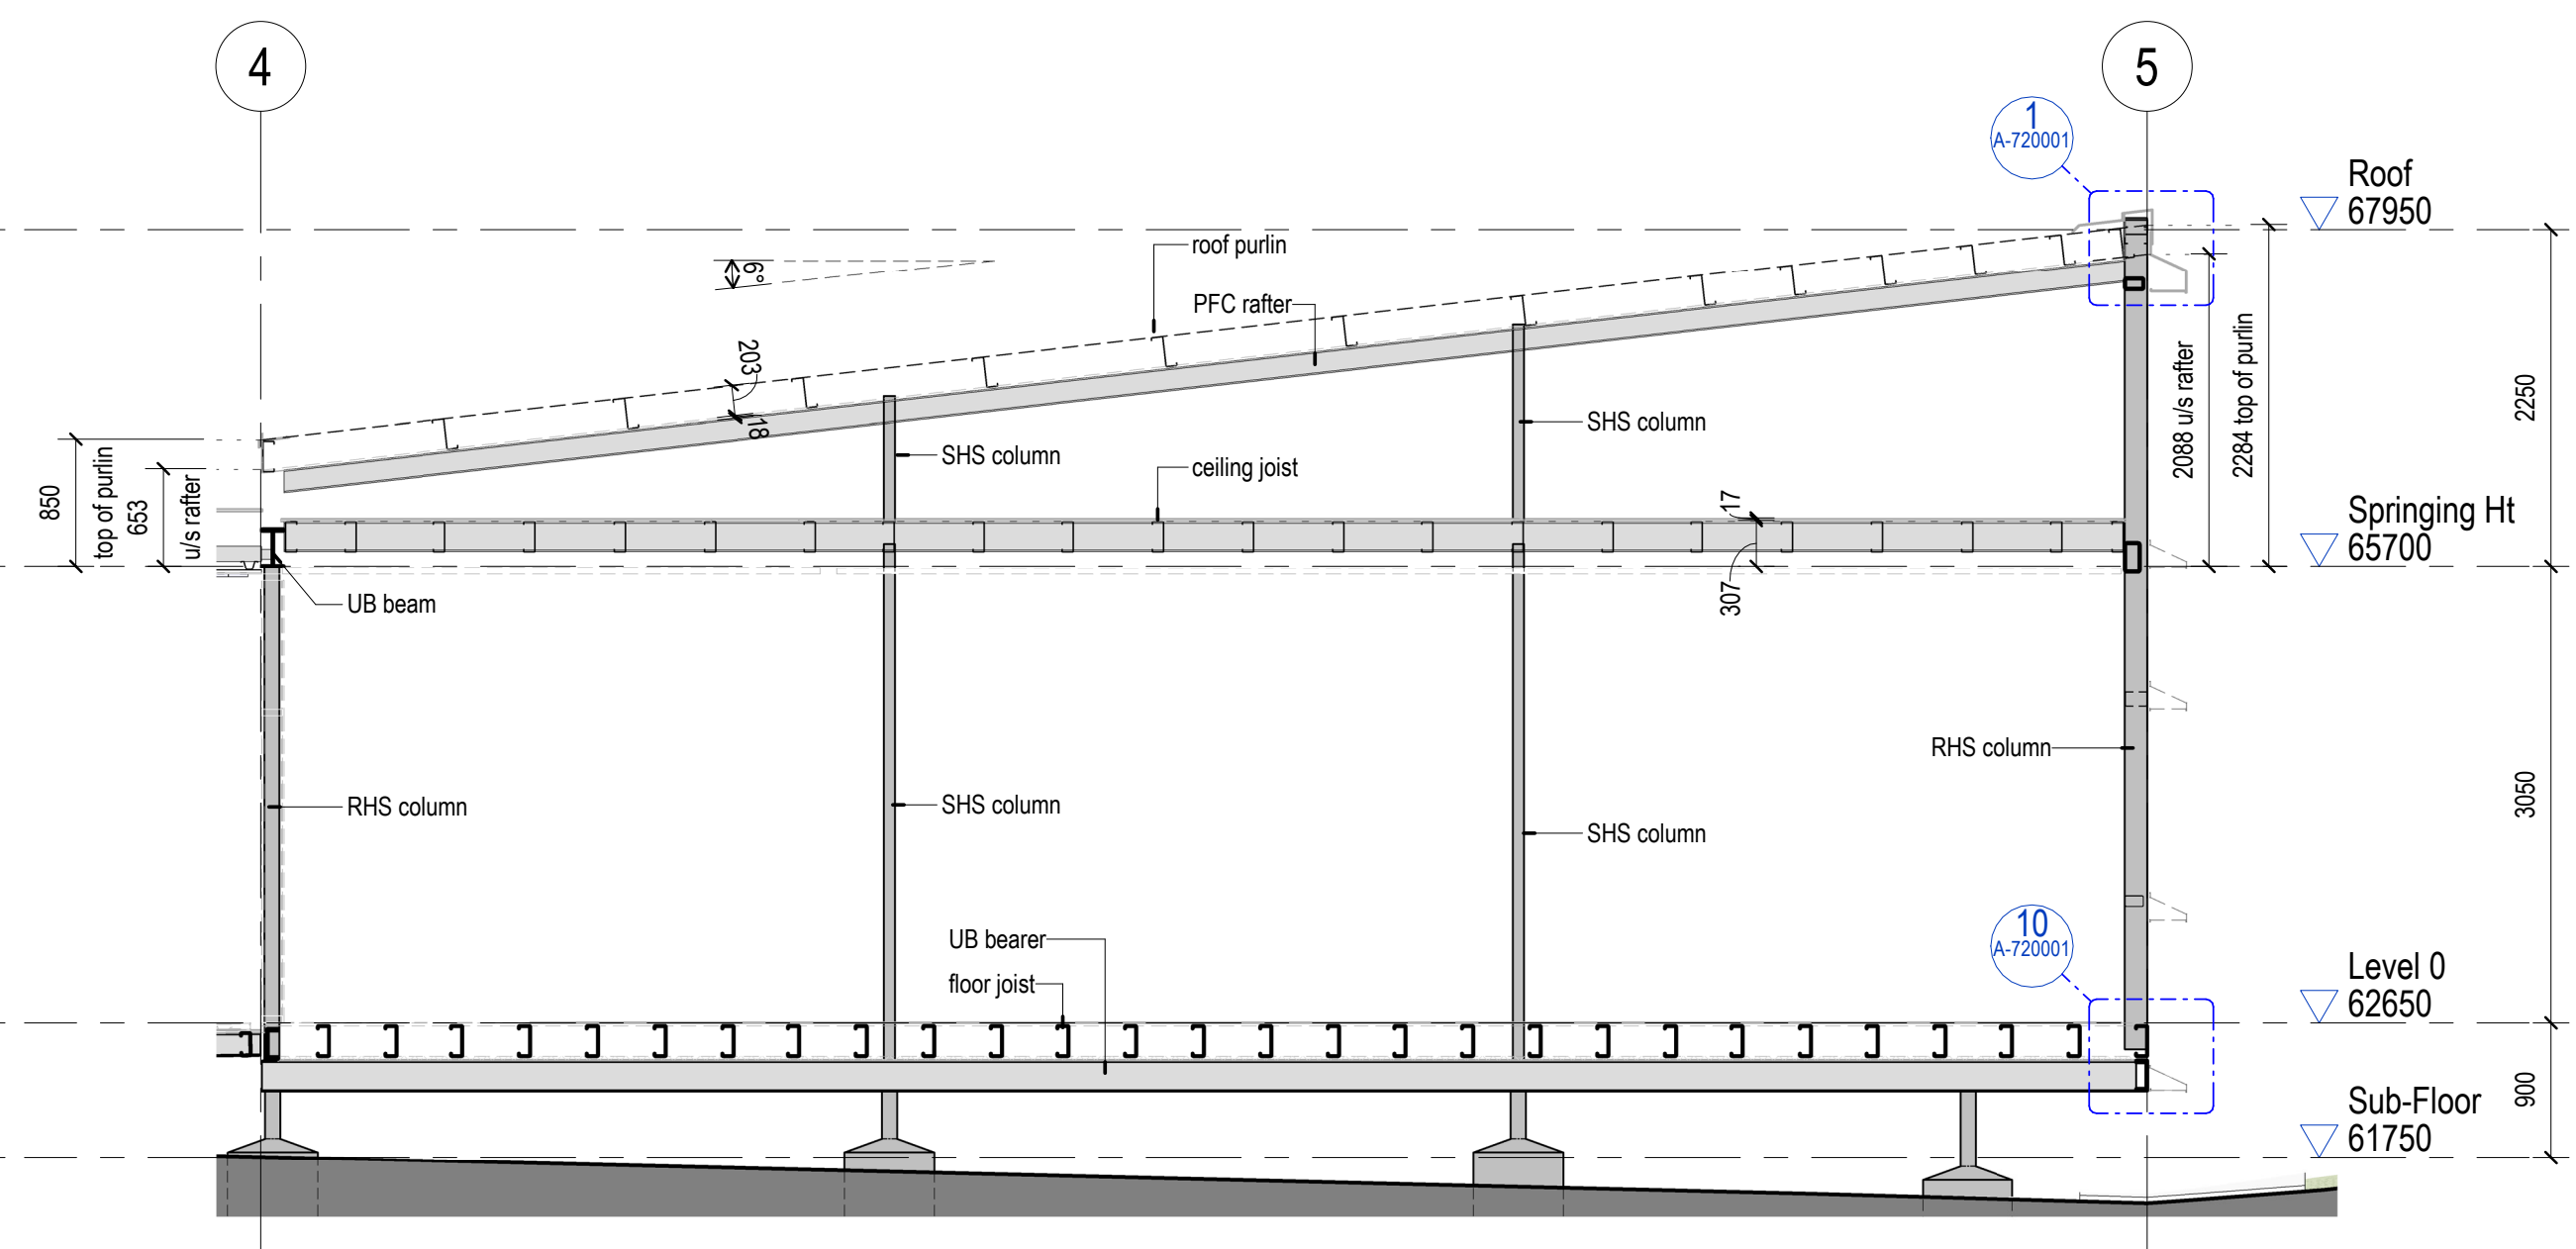

4 Detail Section - Plant Room Over Training
1 : 50 Steel Roof Purlins

PRELIMINARY
NOT FOR CONSTRUCTION

Drawings include colour information. A black & white copy may not have all the information. This background is coloured blue.

brian hooperarchitect
m3architecture

ph: +61 7 3831 4644
11 saint james street petrie tce q 4000
info@m3architecture.com
www.m3architecture.com

client  stanwell

Project Stanwell New Projects Office
Switchyard Road,
Stanwell, QLD, 4702

title	Structure Details
-------	-------------------

rawn	bg
cked	jb
date	March 2026
scale	As indicated at A1
wing	25010 / cd A-390001 / T1

copyright ©
These designs, plans, specifications and the copyright herein are the property of the architect and must not be used, reproduced, or copied wholly or in part without the written permission of m3architecture ply ltd abn 23 079 044 545. Use figured dimensions in preference to scale. If there are any questions contact the architect.

0 0.5 1.0 1.5 2.0 2.5m