



FACADE NOTES

- FN.01 Refer to Appendix B - Wall Schedule for wall types.
- FN.02 Refer to Window Schedule on A-740001 & Appendix B - Wall Schedule for window types.
- FN.03 Refer to T-Sheet for AM codes
- FN.04 Confirm positions on site for AM-3 vertical flashings to suit adjoining wall locations

GLASS TYPES

- LV - Glass louvers, refer to Wall Schedule for selection
- FG - Fixed clear single glazed, refer to Wall Schedule for selection
- IGU - Fixed clear double glazed, refer to Wall Schedule for selection
- Joint in AM-2 horizontal flashing

WINDOW SCHEDULE					
Room	No.	Name	Window No	Code	Ht x Width
0.02	Covered Outdoor	W2	WEF-22	1655h X 12632w	East-Row 4
0.02	Covered Outdoor	Wx1	WEF-22	1235h X 1836w	East-Row 2
0.05	Kitchen	W1	WEF-21	1655h X 3640w	South-Row 4
0.08	Boardroom	W1	WEF-21	1235h X 3945w	South-Row 2
0.08	Boardroom	W2	WEF-21	1655h X 3654w	South-Row 4
0.11	Training Kitchen	W1	WEF-21	1235h X 2439w	South-Row 2
0.16	Female Amenities	W1	WEF-21	740h X 1240w	South-Row 3
0.17	Male Amenities	W1	WEF-21	725h X 1240w	South-Row 3
0.18	First Aid	W1	WEF-21	1235h X 1084w	West-Row 2
0.29	Workspace (North)	W1	WEF-21	4019h X 3640w	North-Rows 2, 3 & 4
0.29	Workspace (North)	W2	WEF-21	2135h X 3640w	North-Rows 1 & 2
0.29	Workspace (North)	W3	WEF-21	1235h X 28840w	North-Row 2
0.35	Workspace (East)	W1	WEF-21	1235h X 1810w	East-Row 2
0.35	Workspace (East)	W2	WEF-21	1655h X 3640w	East-Row 4

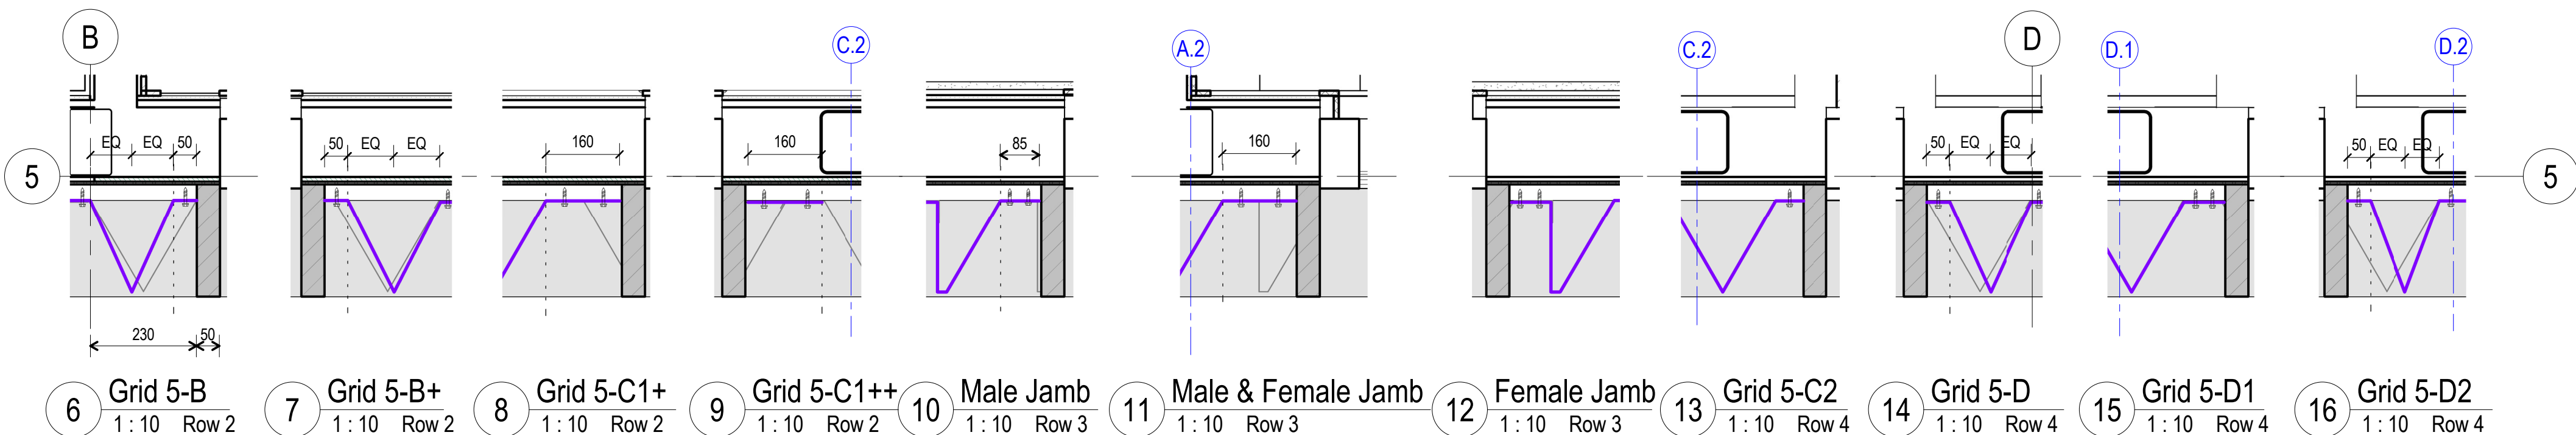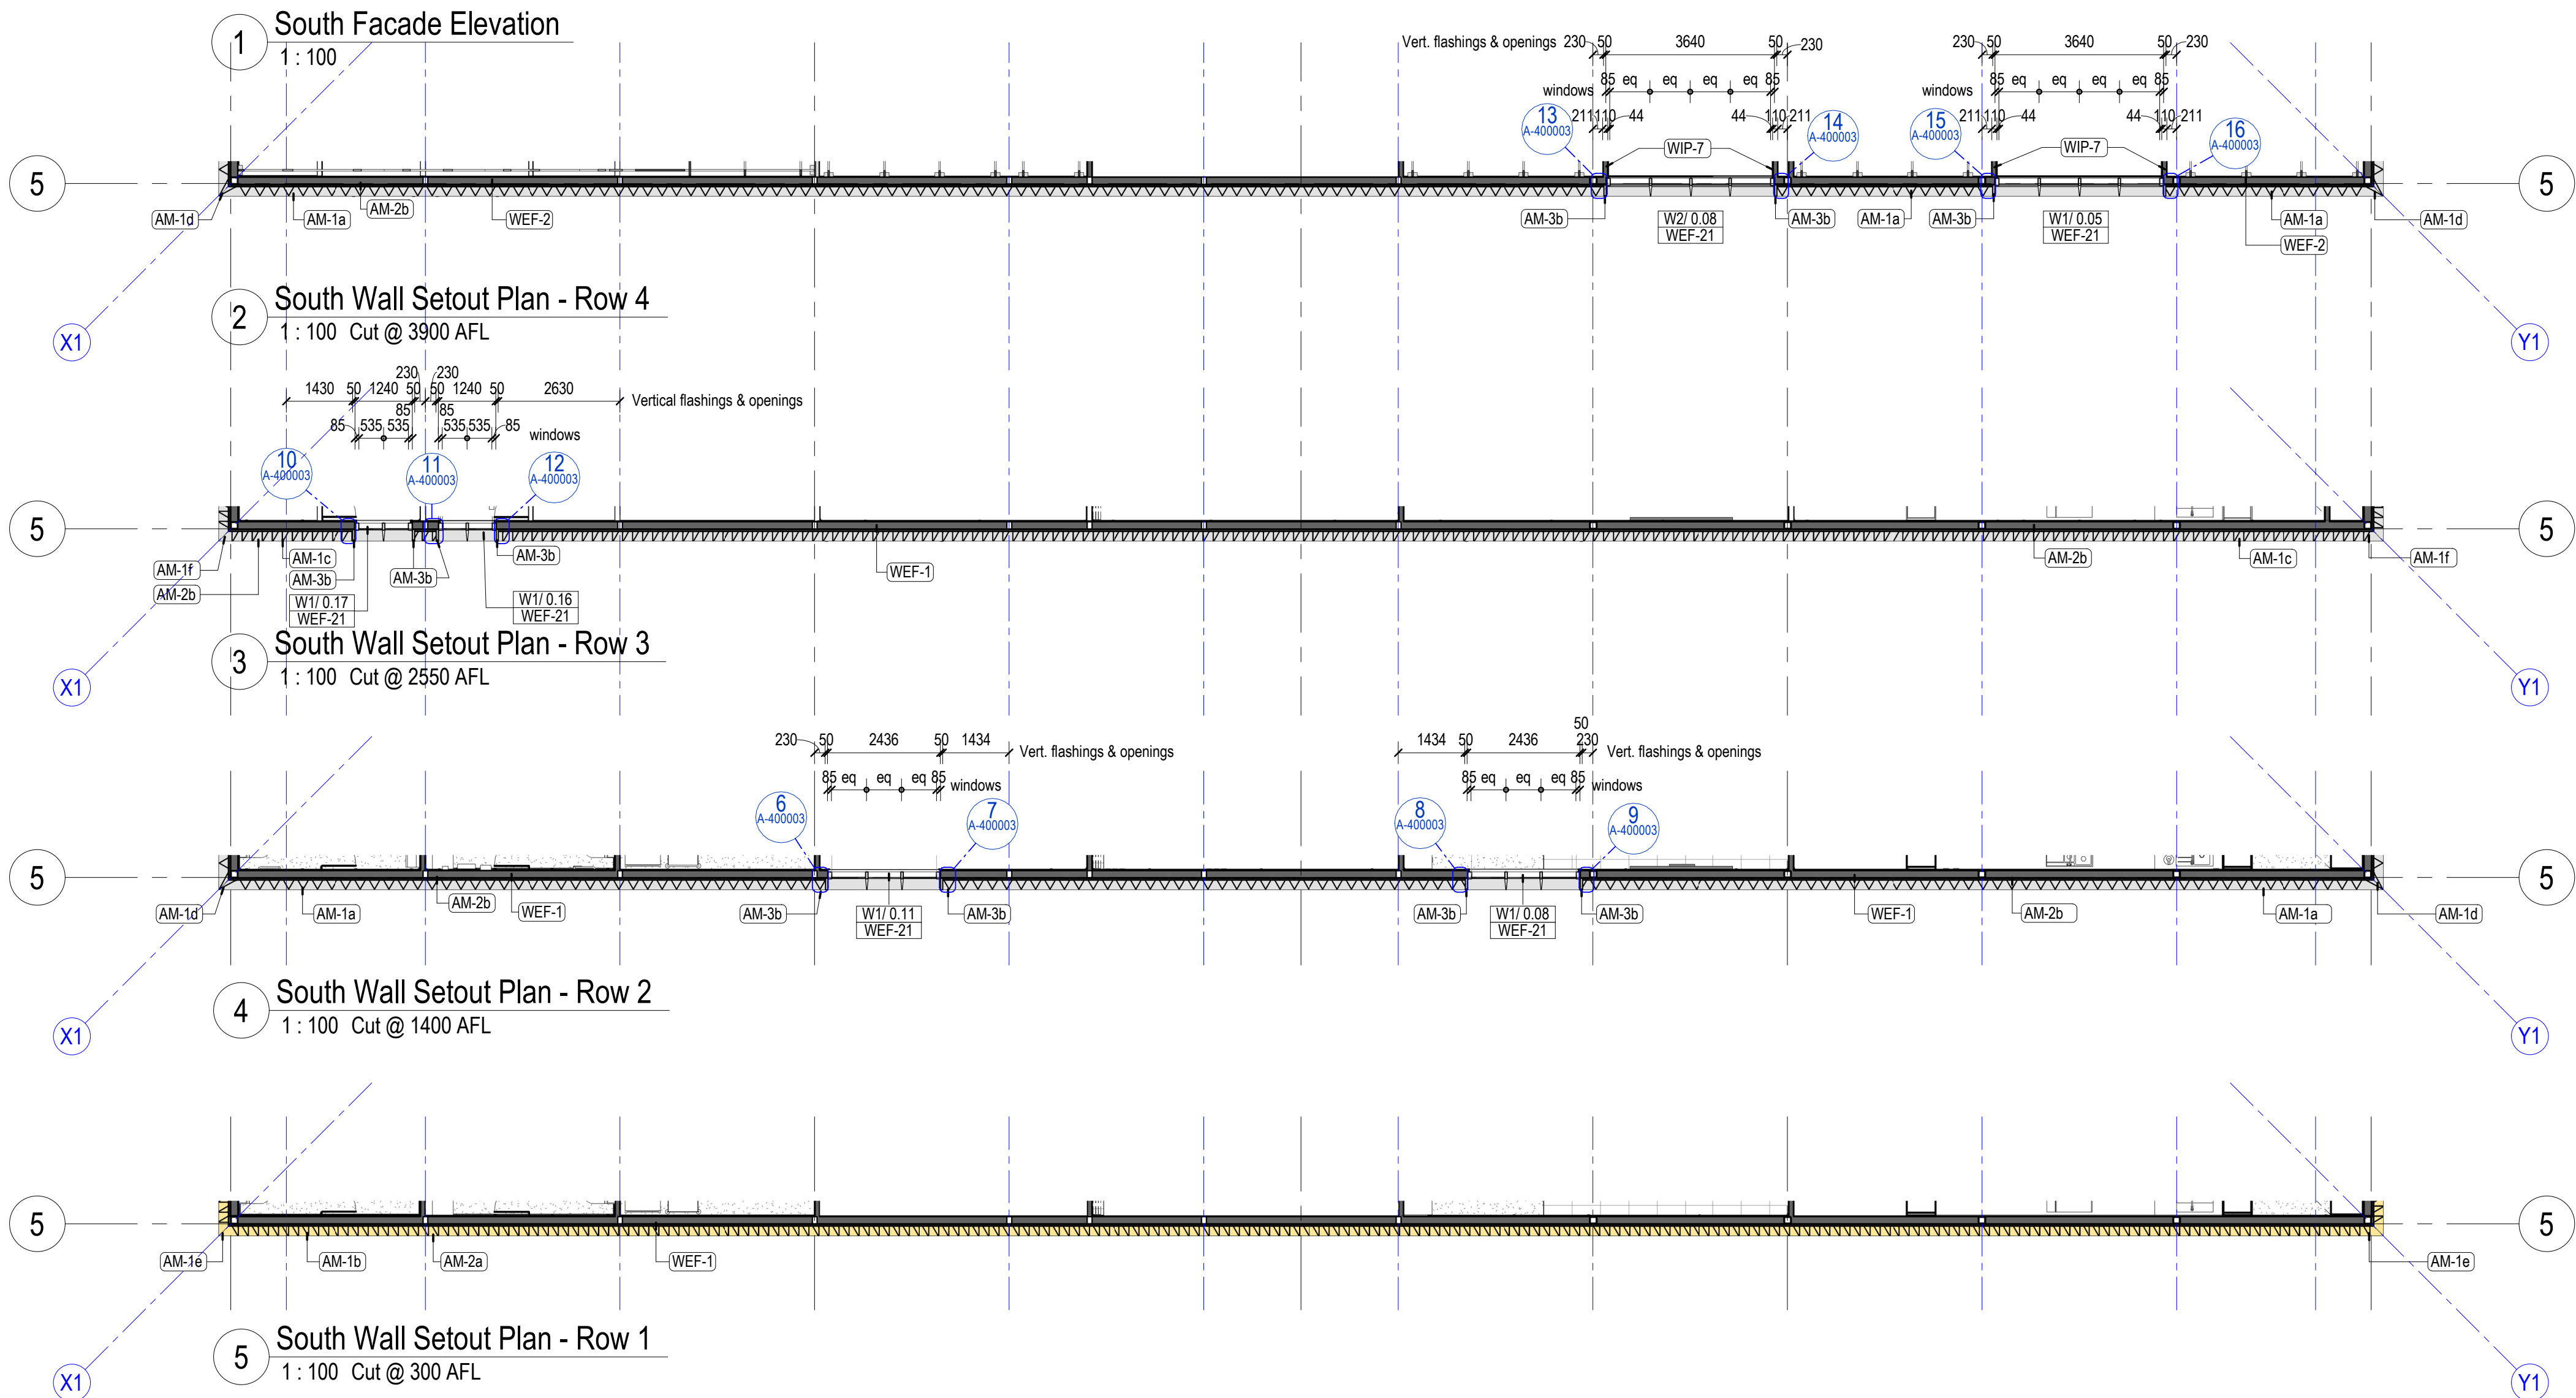

Drawings include colour information. A black & white copy may not have all the information. This background is coloured blue.

brian hooperarchitect
m3architecture
ph: +61 7 3831 4644
11 saint james street petrie tce q 4000
info@m3architecture.com
www.m3architecture.com

client **stanwell**

project **Stanwell New Projects Office**
Switchyard Road,
Stanwell, QLD, 4702

title **Facade Plans & Elevation - South**

drawn bg
checked jb
date March 2026
scale As indicated at A1
drawing 25010 / cd A-400003 / T1

copyright ©
These designs, plans, specifications and the copyright herein are the property of the architect and must not be used, reproduced, or copied wholly or in part without the written permission of m3architecture Pty Ltd abn 23 079 044 545. Use figured dimensions in preference to scale. If there are any questions contact the architect.

1:100 at A1