




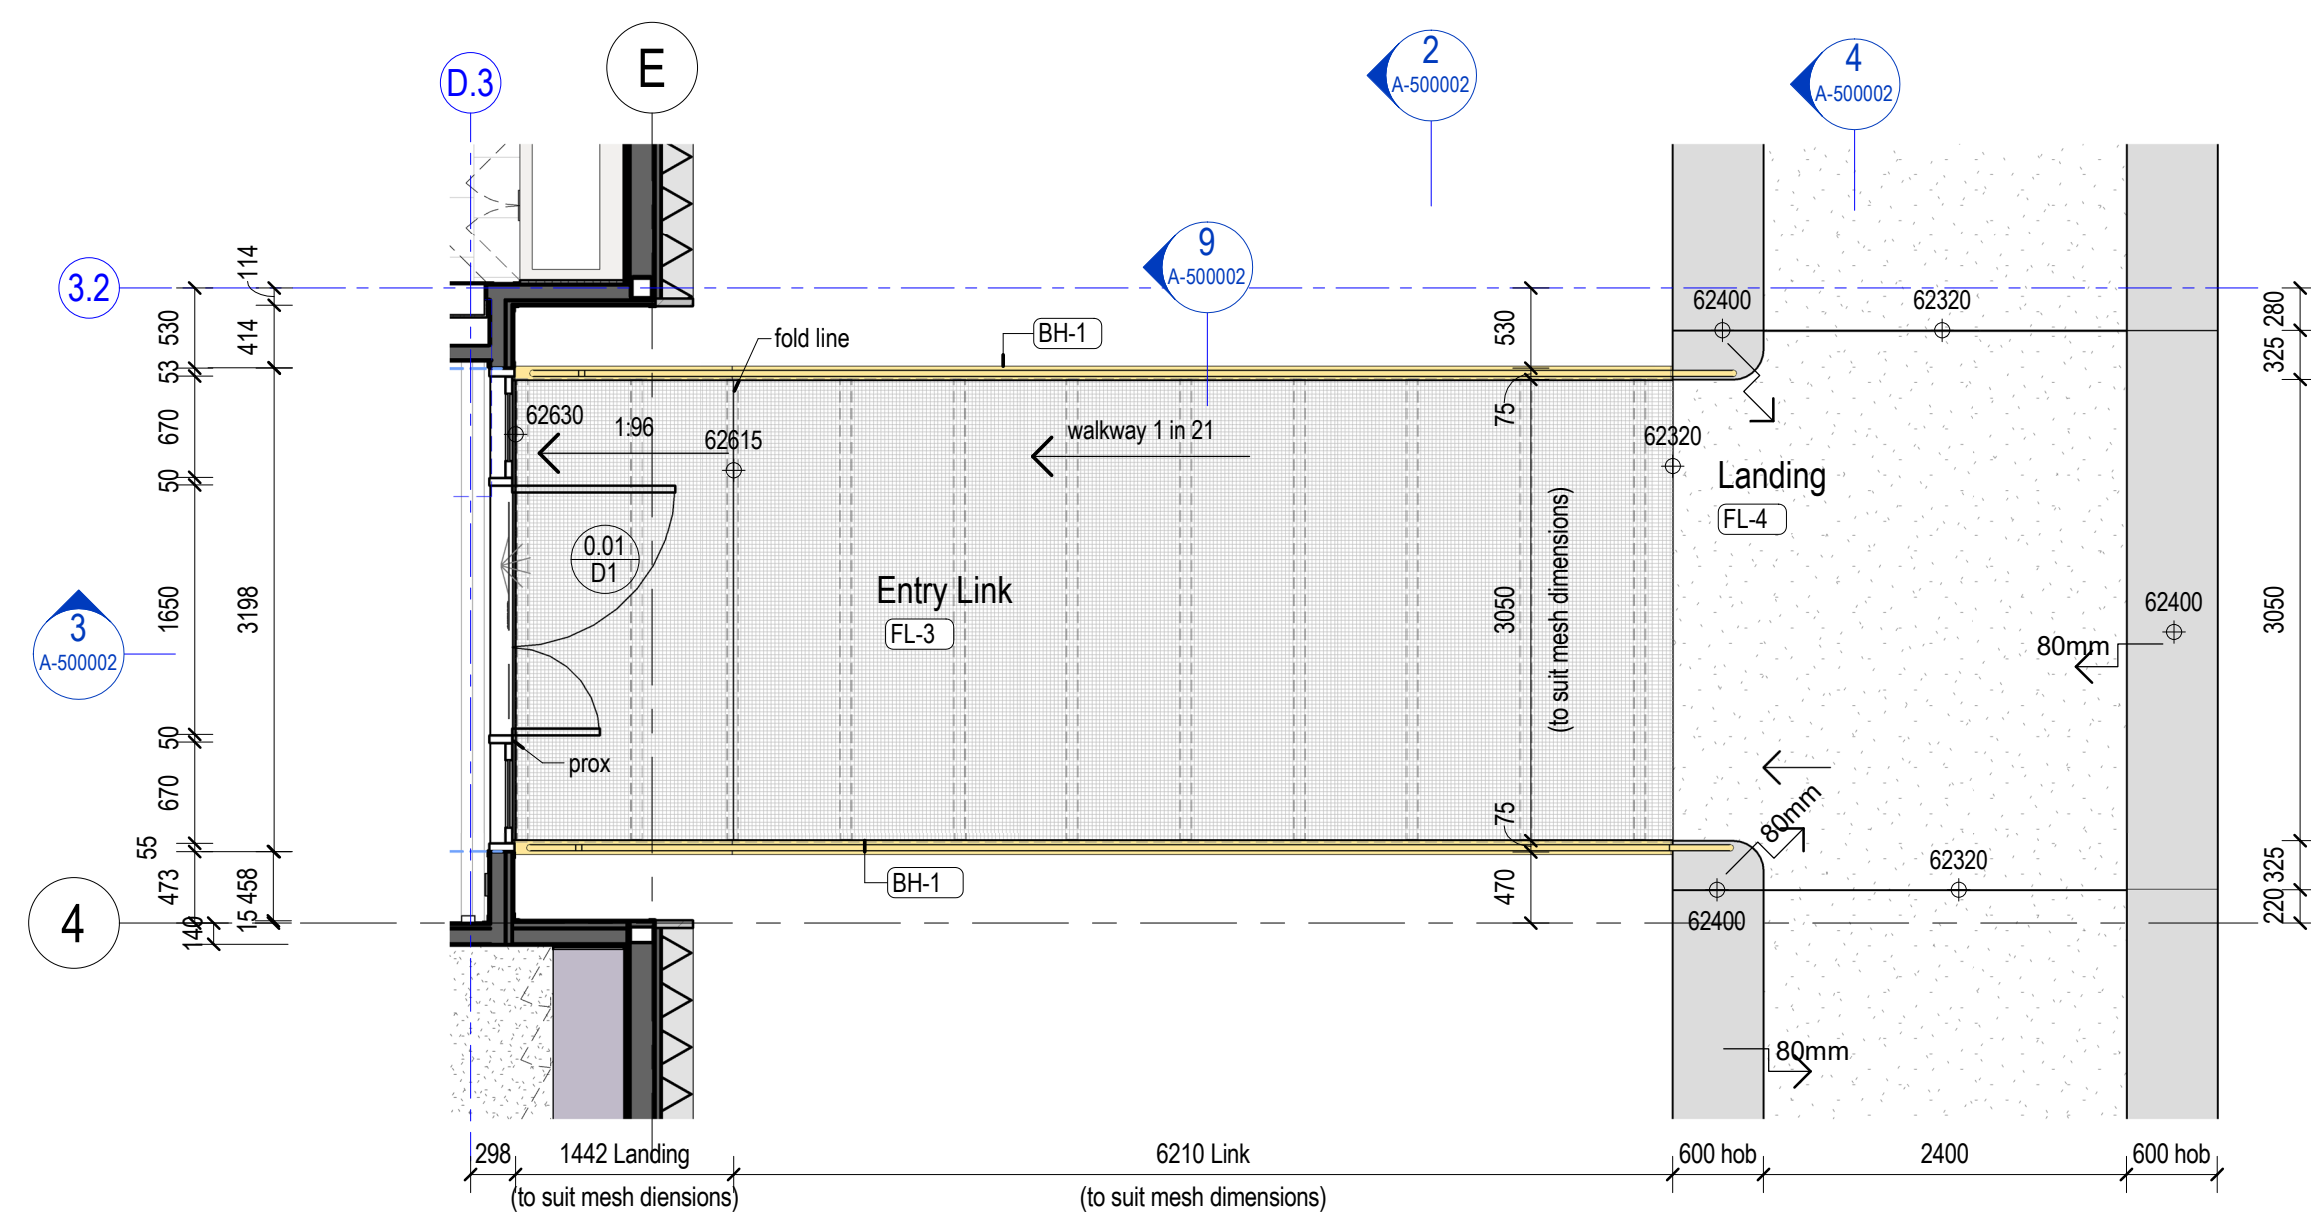


1 East Entry Walkway Link
1:50

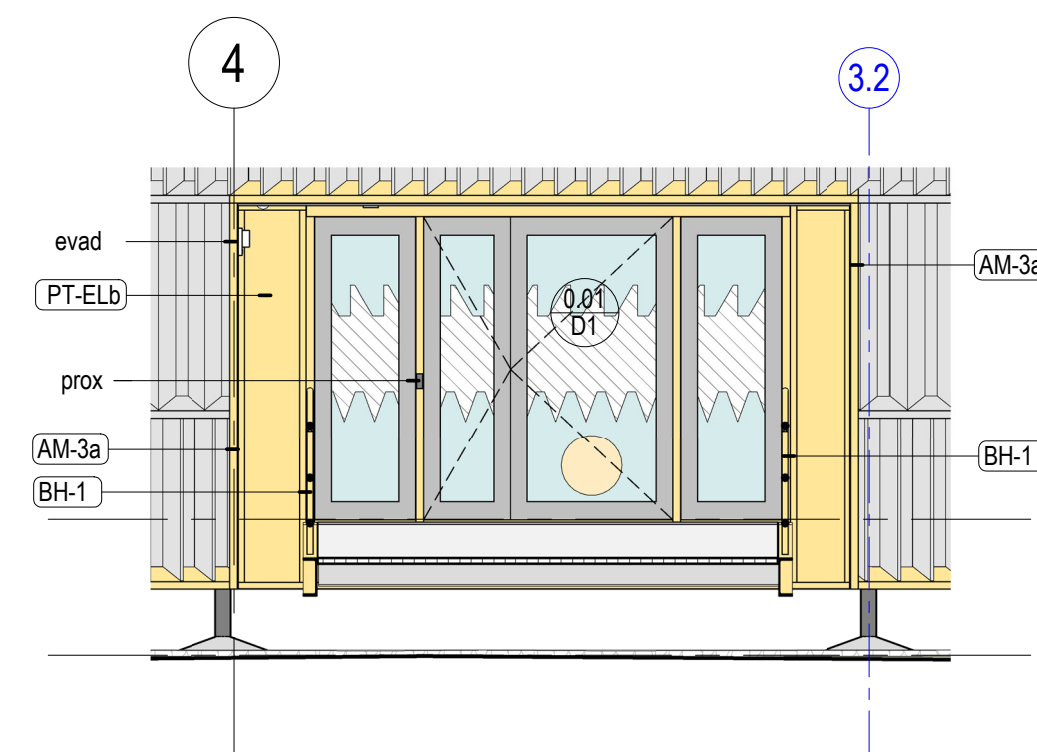


2 East Entry Walkway - Section 1
1:50

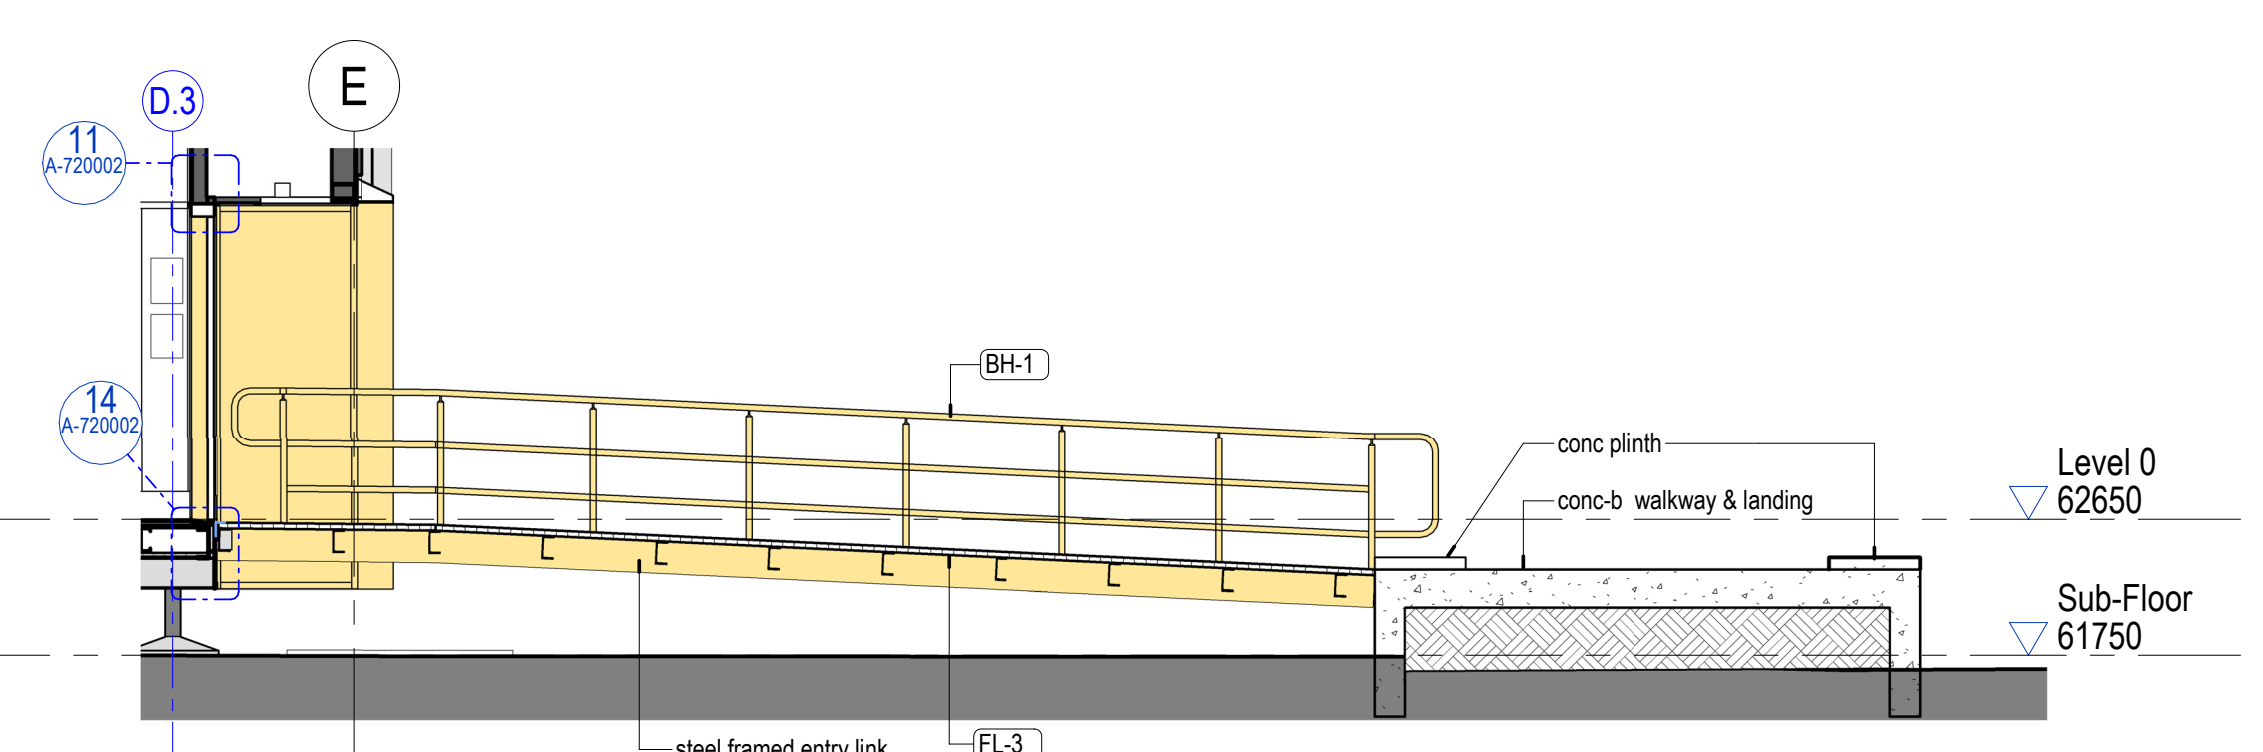


3 East Entry Walkway - Section 2
1 : 50

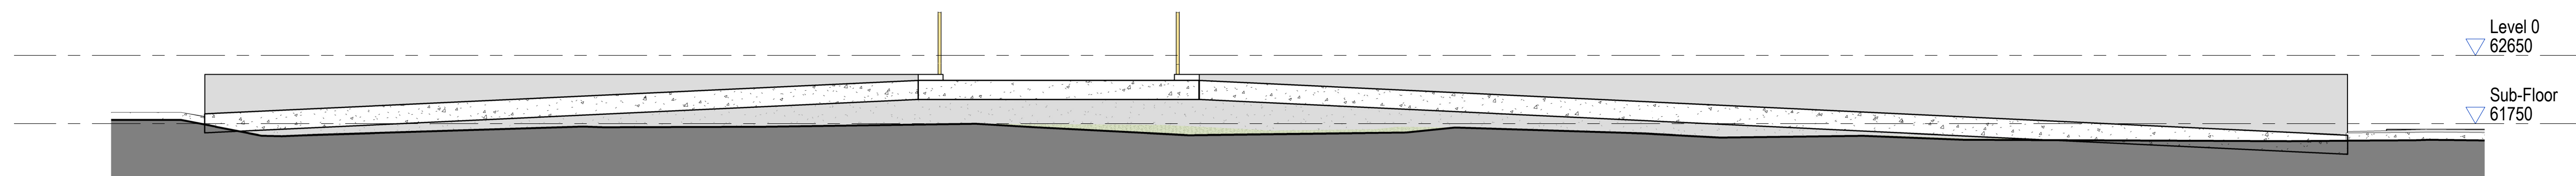


4 East Entry Walkway - Section 3
1:50

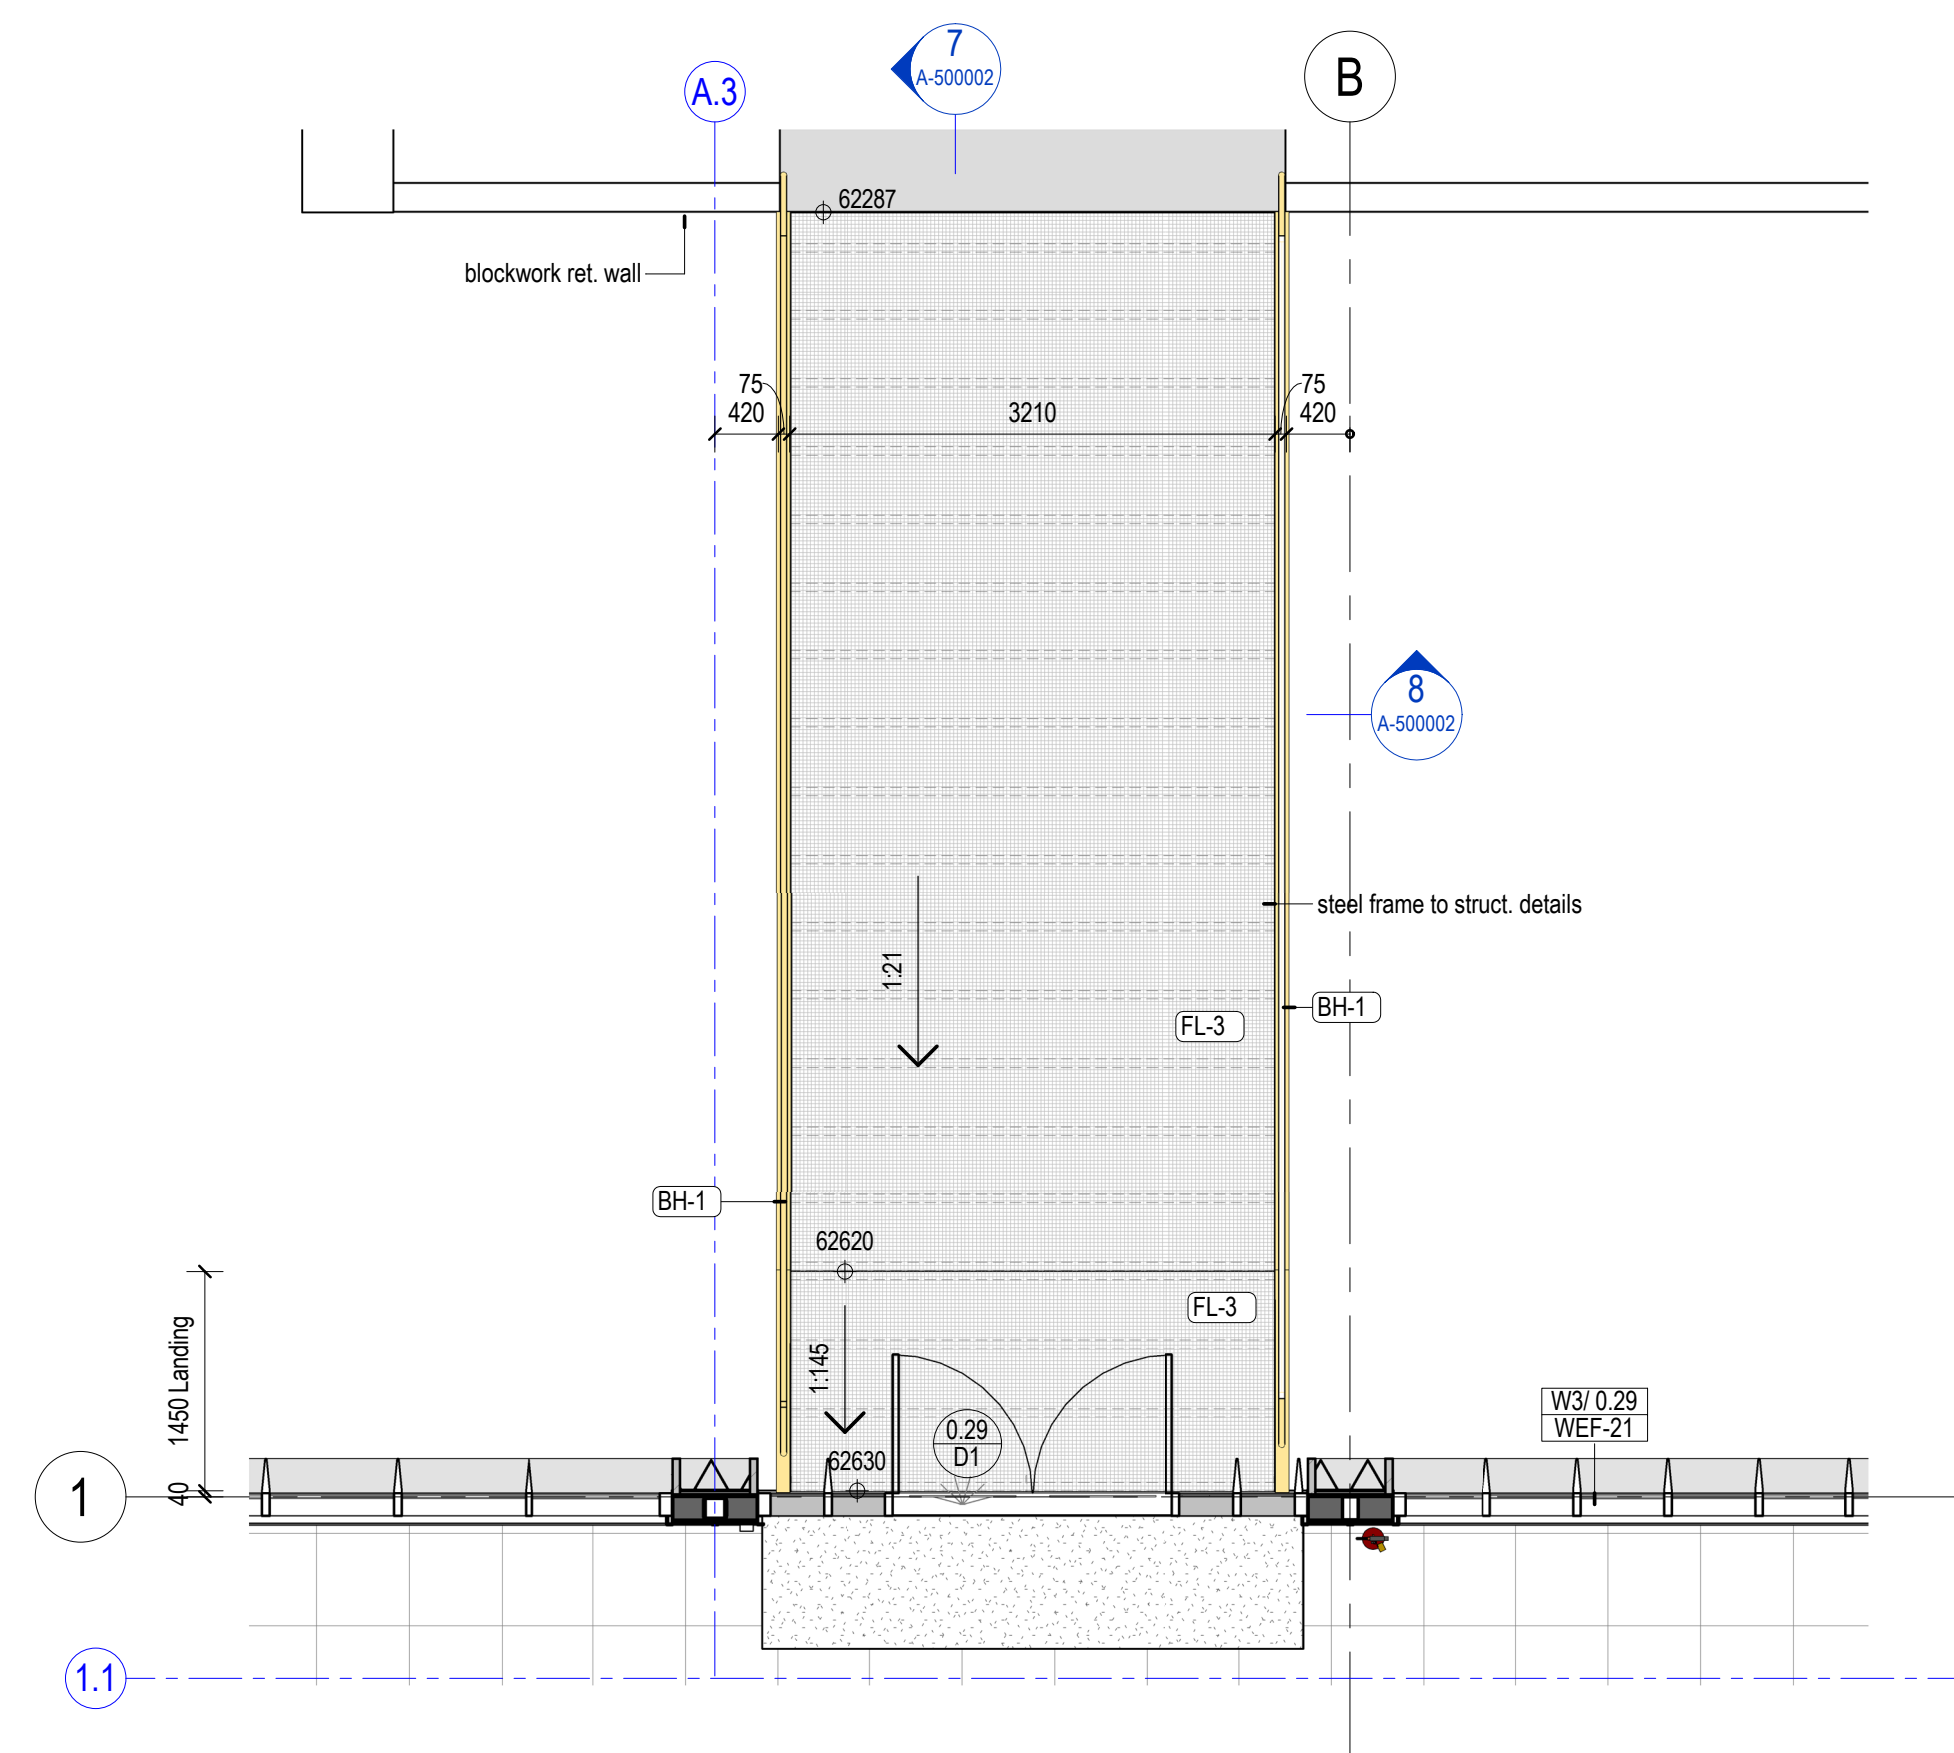


6 North Entry Link
1 : 50

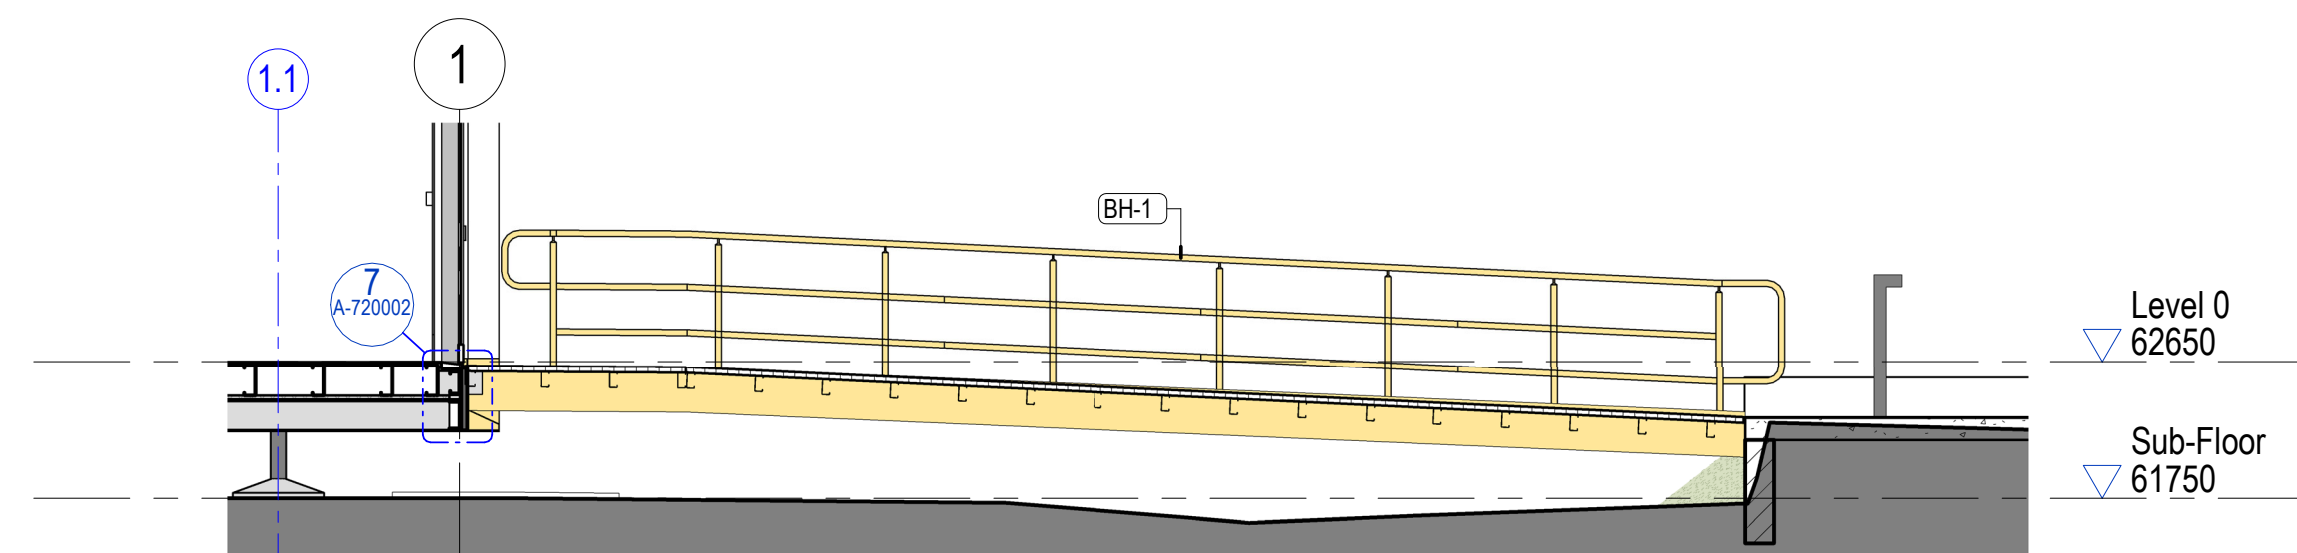

7 North Entry Link - Section 1
1 : 50

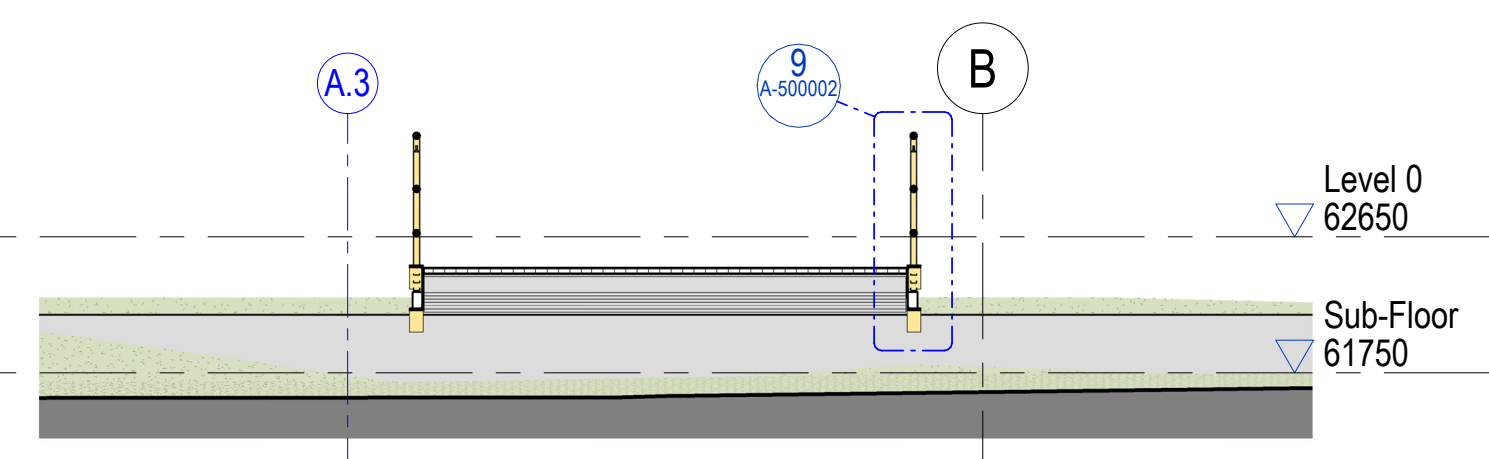

8 North Entry Link - Section 2
1 : 50

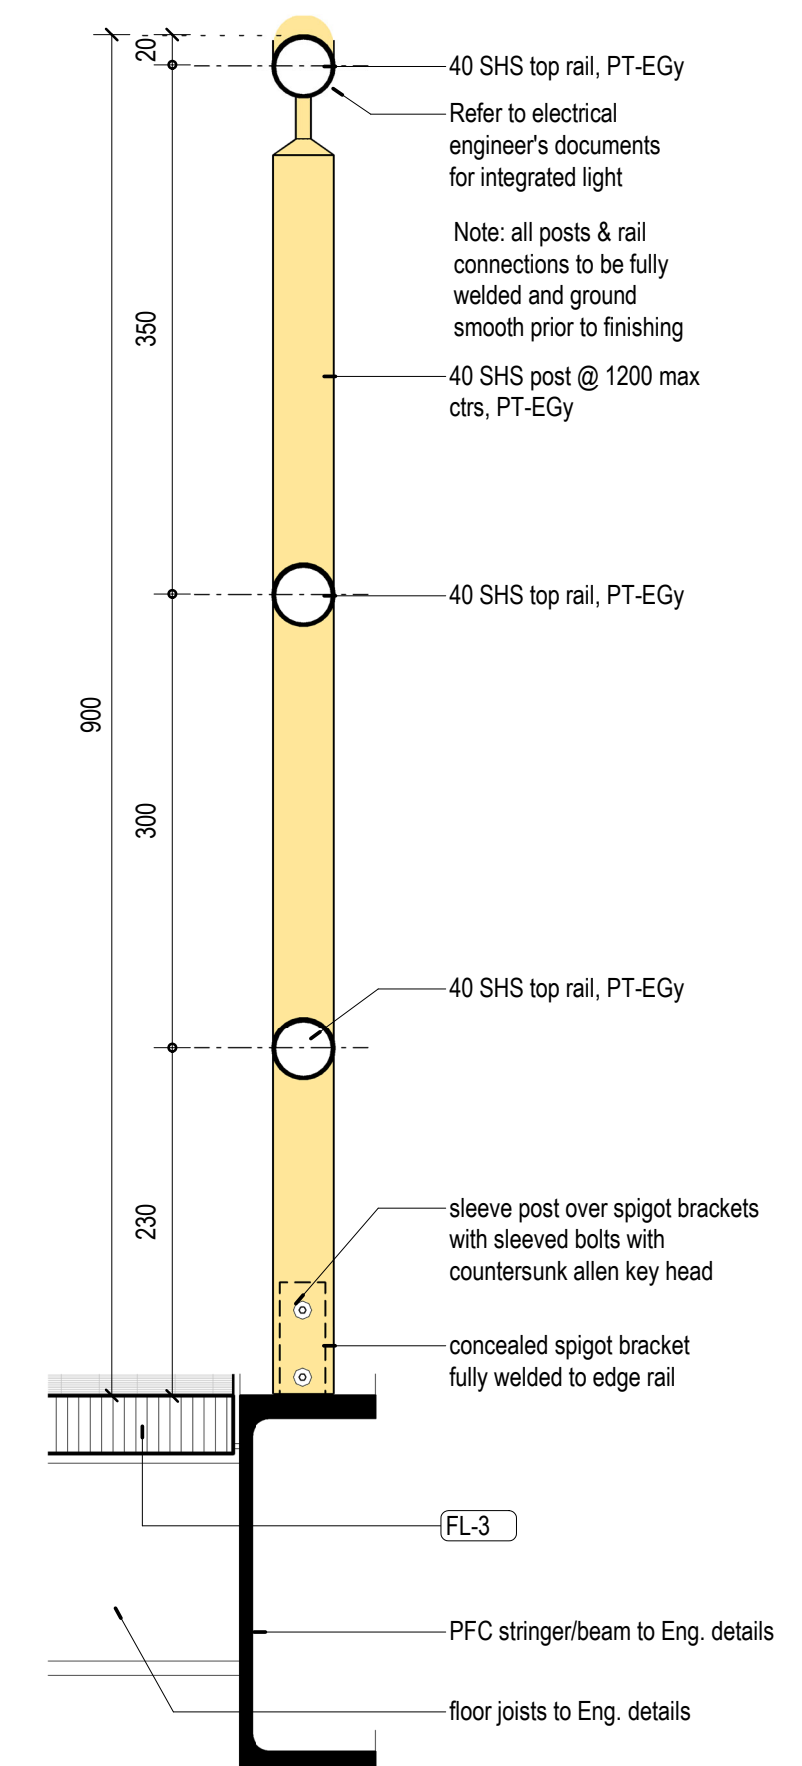

9 Entry Walkway - Section 1
1:5

WALKWAY & LINK NOTES

1. AS 1428.1(2021) compliance required
2. TGSi: required??
3. Co-ordinate steel structure with FL-3 sheet sizes to facilitate a full perimeter support & edge to each panel. Note grid on under side of mesh has bars @ 40mm centres and the bars are typically ~7mm wide. Internal dimensions for perimeter frames to be a multiple of 40mm plus 10mm.

rev	date	description
T1	11/03/2026	For Tender

JB

PRELIMINARY
NOT FOR CONSTRUCTION

Drawings include colour information. A black & white copy may not have all the information. This background is coloured blue.

brian hooperarchitect
m3architecture
ph: +61 7 3831 4644
11 saint james street petrie tce q 4000
info@m3architecture.com
www.m3architecture.com



stanwell

project Stanwell New Projects Office
Switchyard Road,
Stanwell, QLD, 4702

title	Walkways
-------	----------

drawn bg
checked jb
date March 2026
scale As indicated at A1
drawing 25010 / cd A-500002 / T1

copyright ©
These designs, plans, specifications and the
copyright herein are the property of the architect
and must not be used, reproduced, or copied
wholly or in part without the written permission of
m3architecture pty ltd abn 23 079 044 545.
Use figured dimensions in preference to scale.
If there are any questions contact the architect.

1 at A1

A horizontal scale bar with markings at 10, 20, 30, 40, and 50mm.