




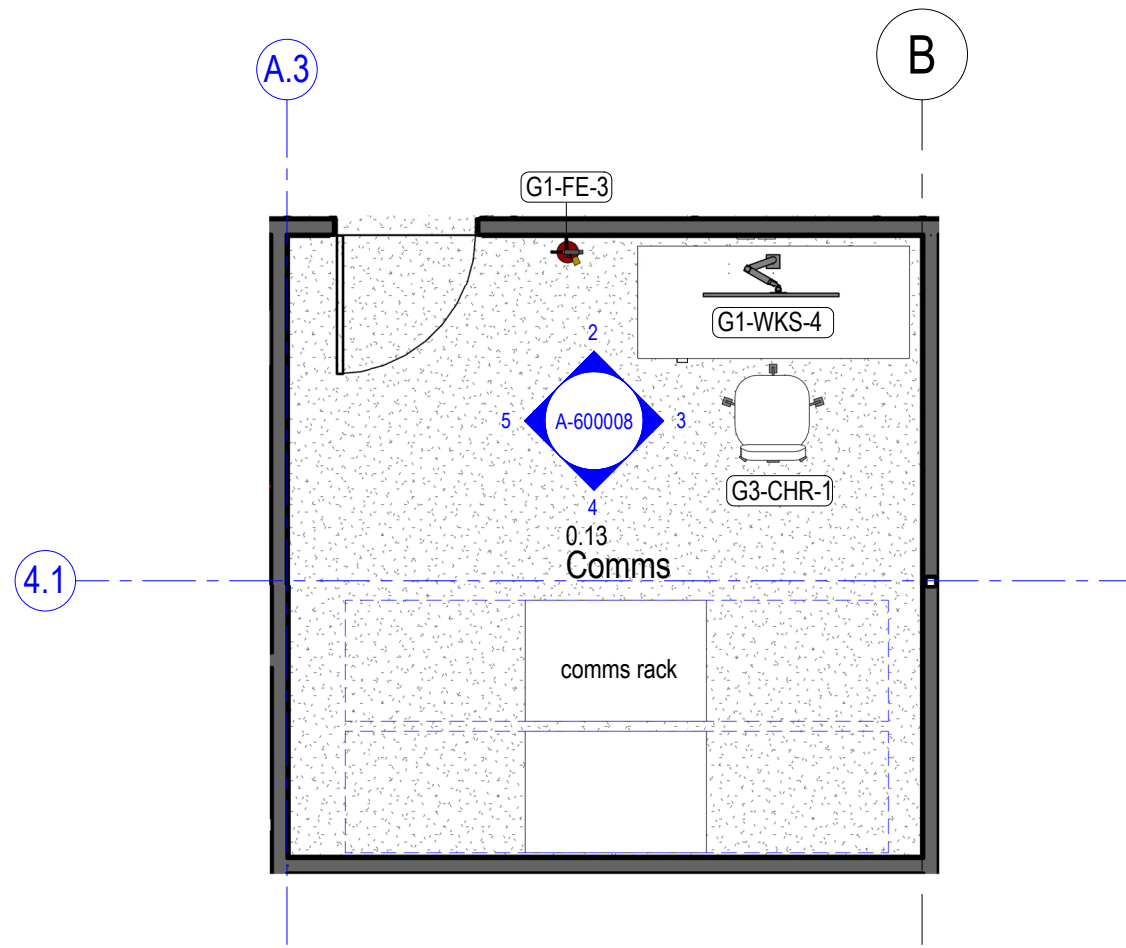


1 0.13 - Comms - Plan
1 : 50

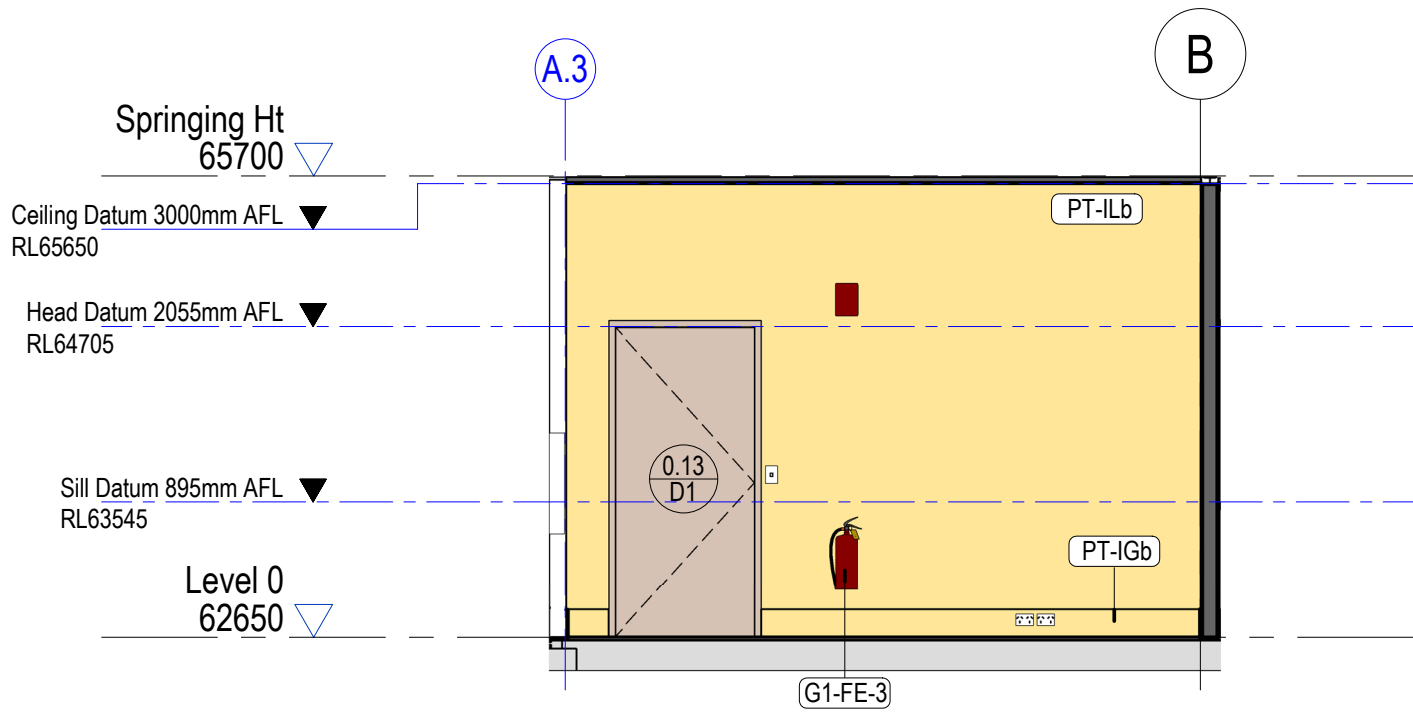


2 0.13 - Comms - North Elevation
1 : 50

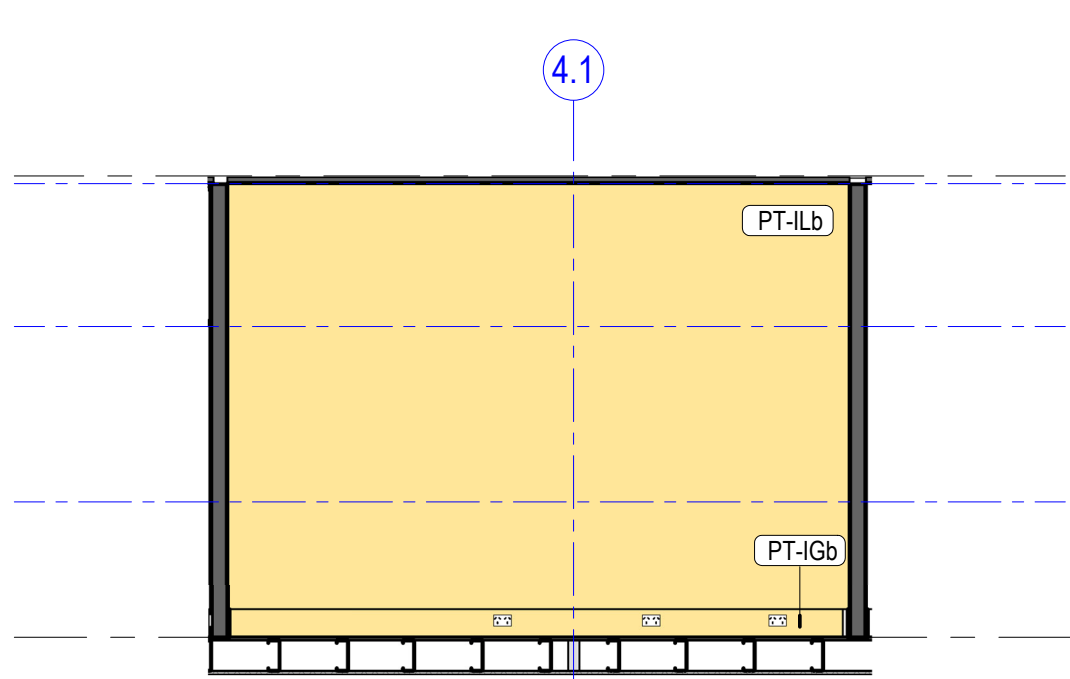


3 0.13 - Comms - East Elevation
1 : 50

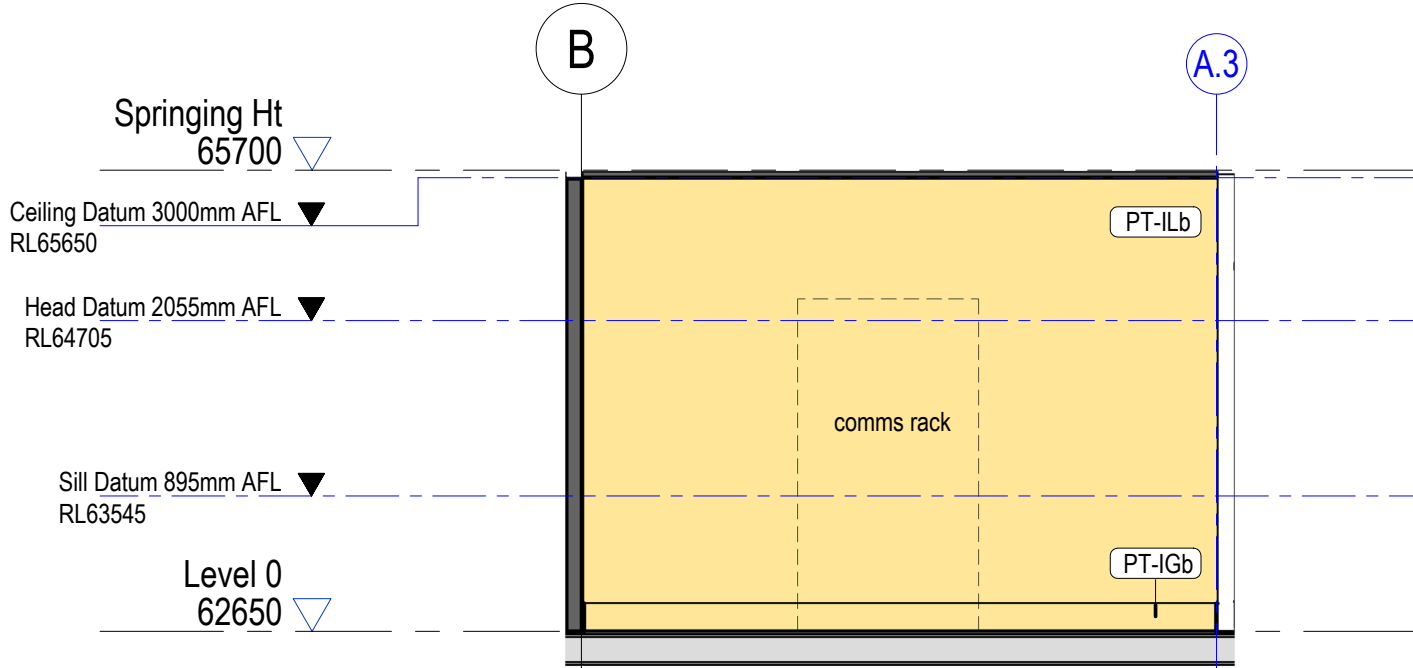


4 0.13 - Comms - South Elevation
1 : 50

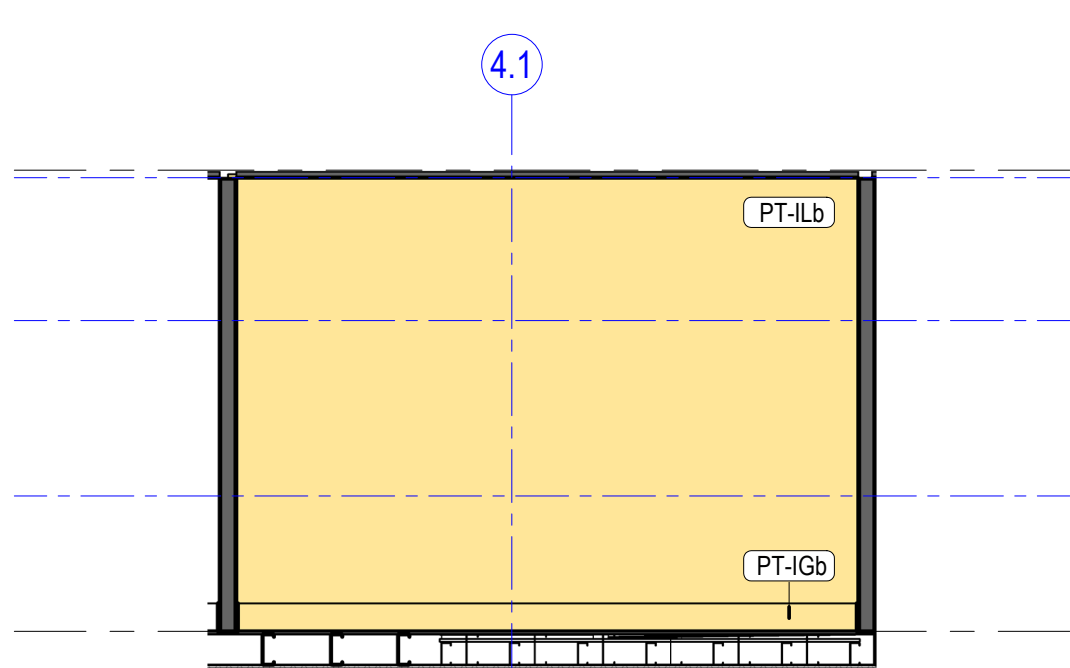


5 0.13 - Comms - West Elevation
1 : 50

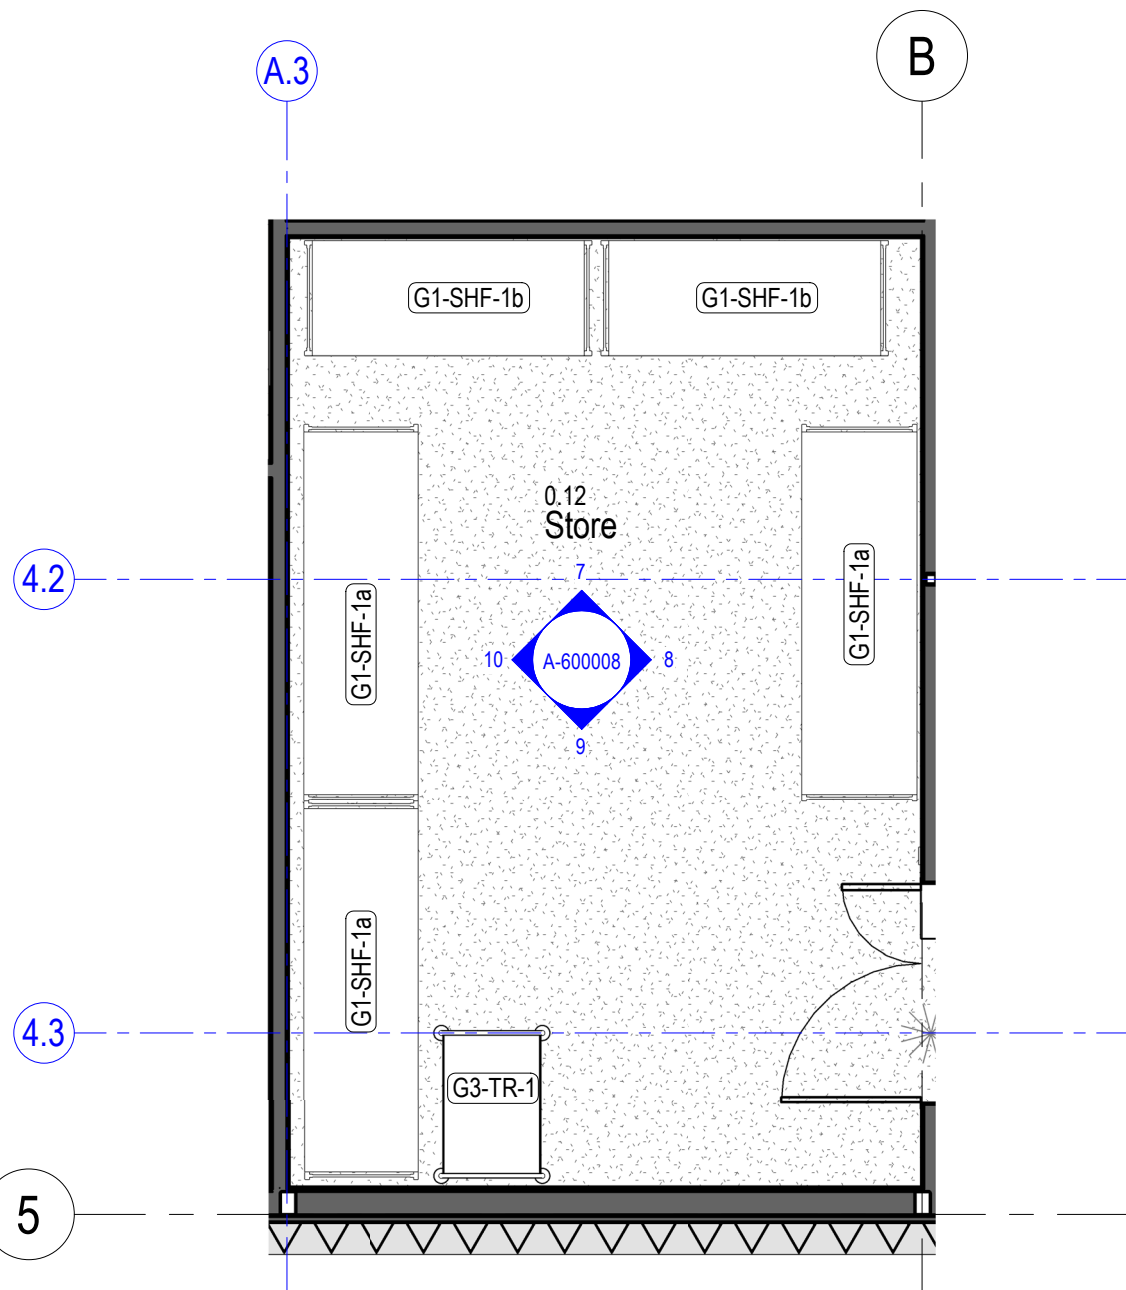


6 0.12 - Store - Plan
1 : 50

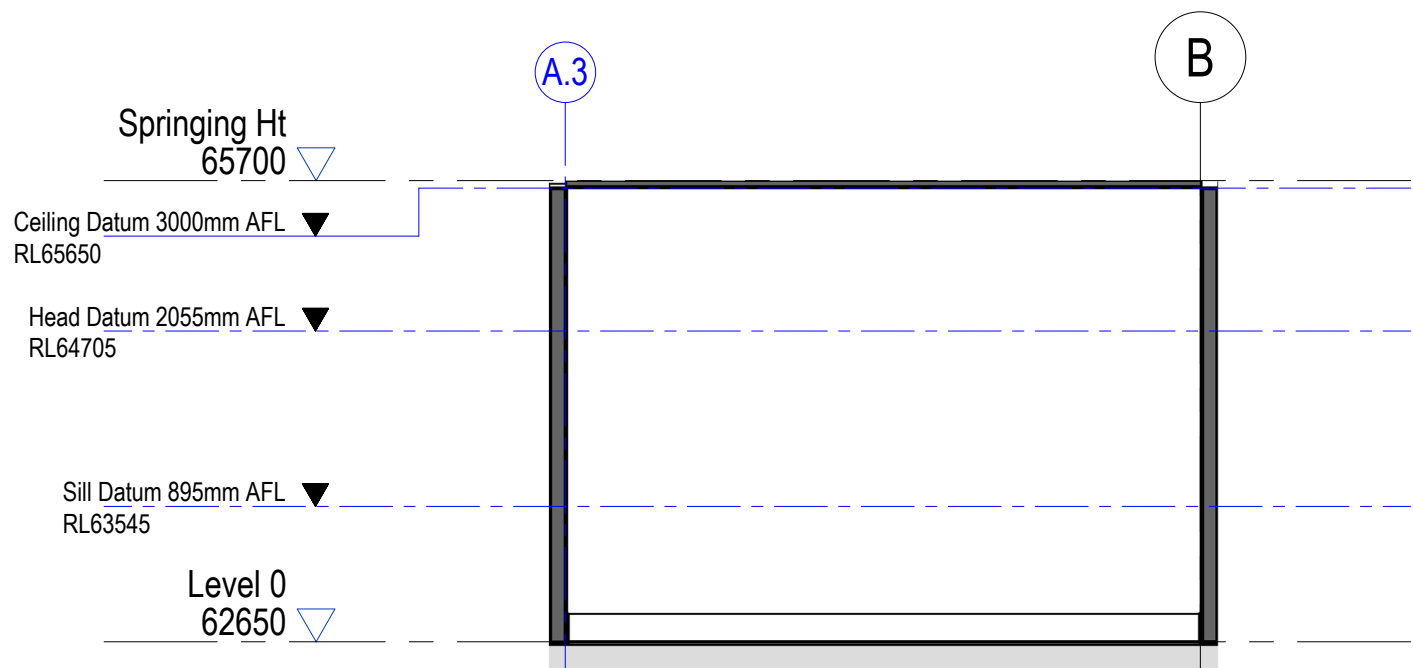


7 0.12 - Store - North Elevation
1 : 50

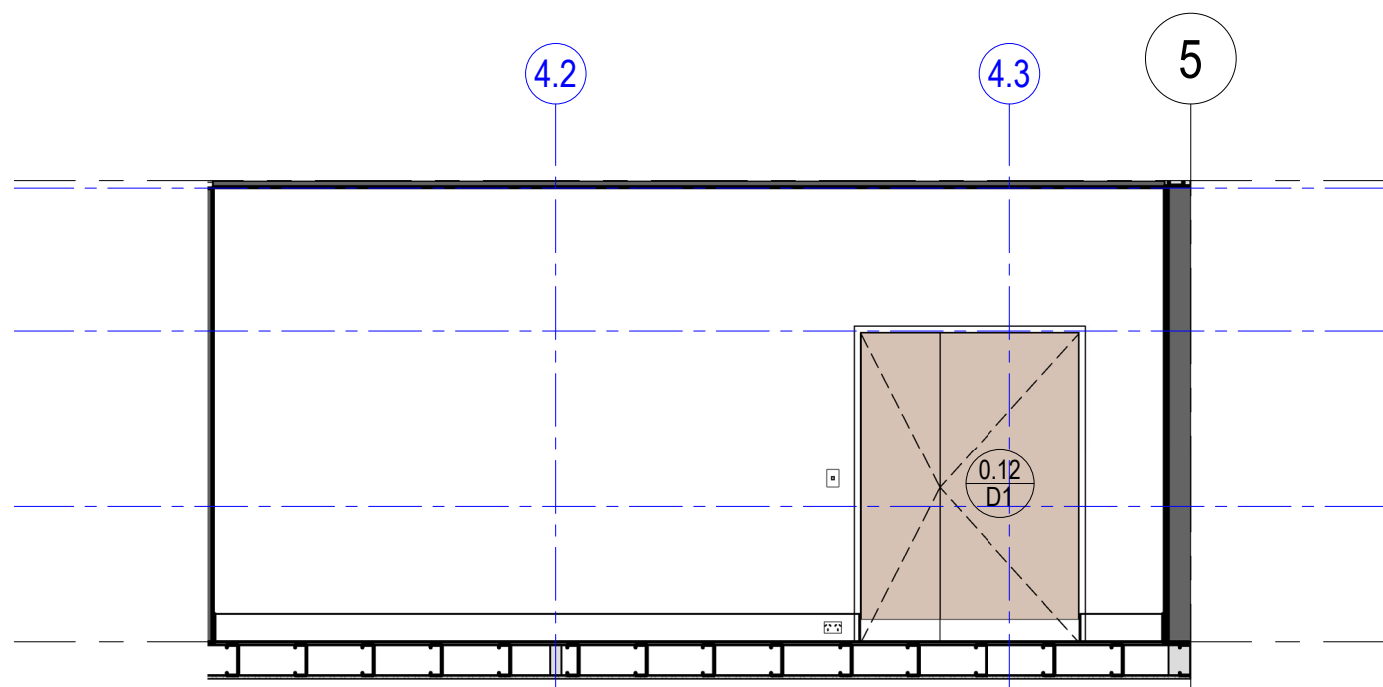

8 0.12 - Store - East Elevation
1 : 50

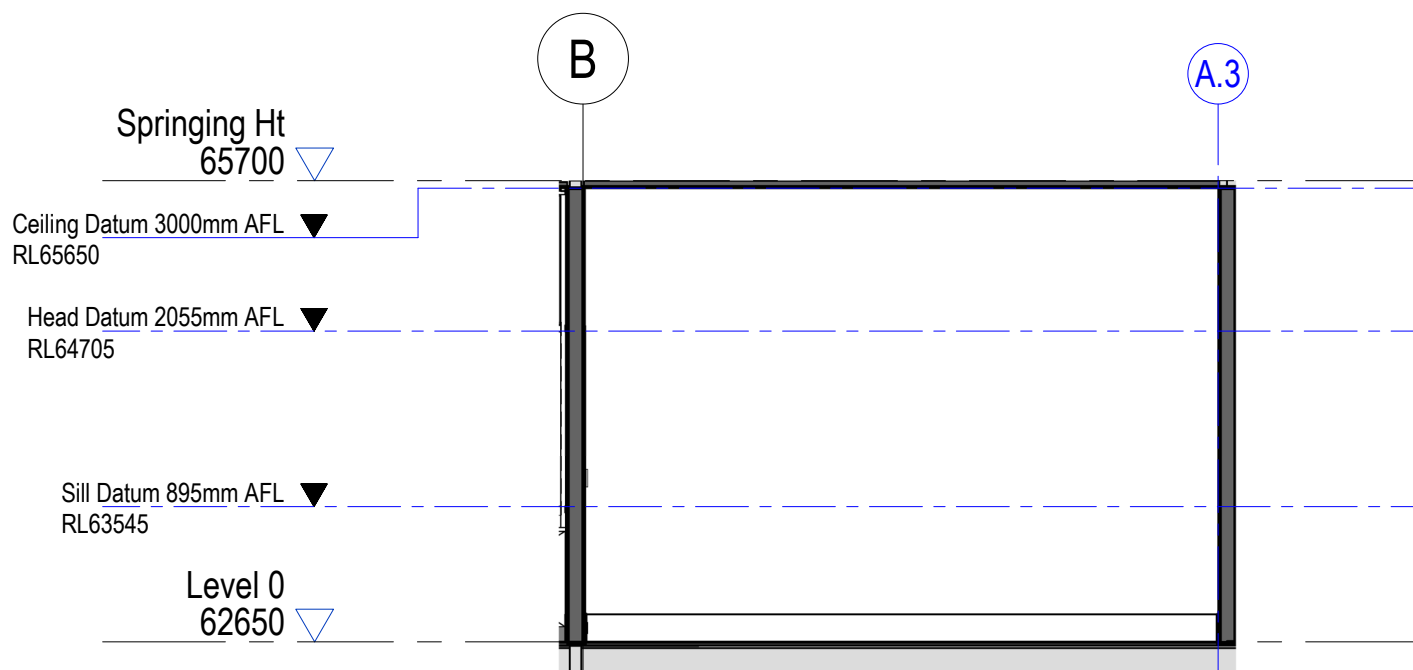

9 0.12 - Store - South Elevation
1 : 50

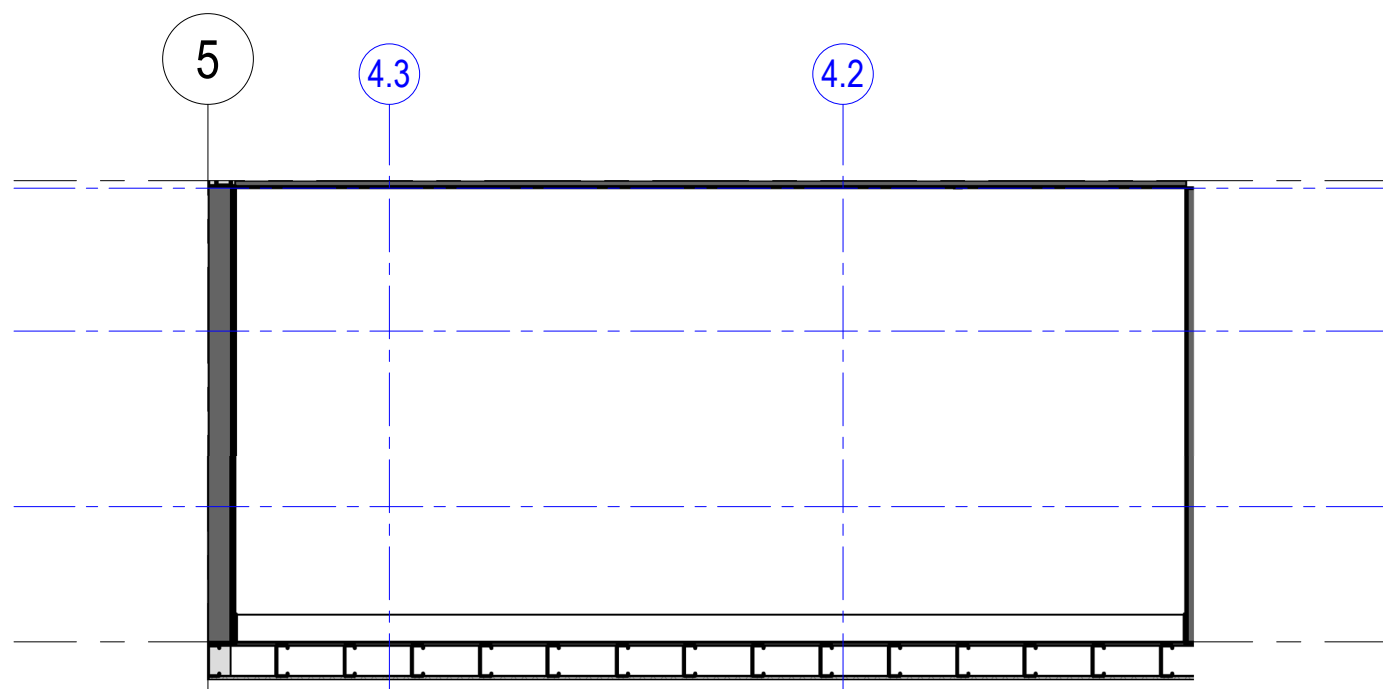

10 0.12 - Store - West Elevation
1 : 50

WALL NOTES:

- Walls are painted typically. Refer to Colour Scheme below for paint system & colour.
- Tags are used for materials other than painted walls.
- Decals shown where required on glazing, MDE-1.
- Install FC wall lining sheets to match cover batten setout, and install cover battens to conceal joints.
- GPOs on architectural drawings are for setout purposes only. For selections refer to Electrical Engineer's documents.

Typical
Wall Battens: MTR-1a UNO
Skirting: MTR-d UNO

ROOM COLOUR
SCHEME WHITE (UNO):

Walls	PT-ILa
Walls skirtings and battens	PT-IGa
Ceiling	PT-IMa
Ceiling battens	PT-IGa

PRELIMINARY
NOT FOR CONSTRUCTION

Drawings include colour information. A black & white copy may not have all the information. This background is coloured blue.

brian hooper**architect**
m3architecture

ph: +61 7 3831 4644
11 saint james street petrie tce q 4000
info@m3architecture.com
www.m3architecture.com



project **Stanwell New Projects Office**
Switchyard Road,
Stanwell, QLD, 4702

title **Interior Plan and Elevations -**
0.12-0.13 - Store and Comms

drawn ZW
checked JB
date March 2026
scale As indicated at A1
drawing 25010 / cd A-600008 / T1

copyright ©
These designs, plans, specifications and the
copyright herein are the property of the architect
and must not be used, reproduced, or copied
wholly or in part without the written permission of
m3architecture Pty Ltd abn 23 079 044 545.
Use figured dimensions in preference to scale.
If there are any questions contact the architect.

1:50 at A1
0 0.5 1.0 1.5 2.0 2.5m