




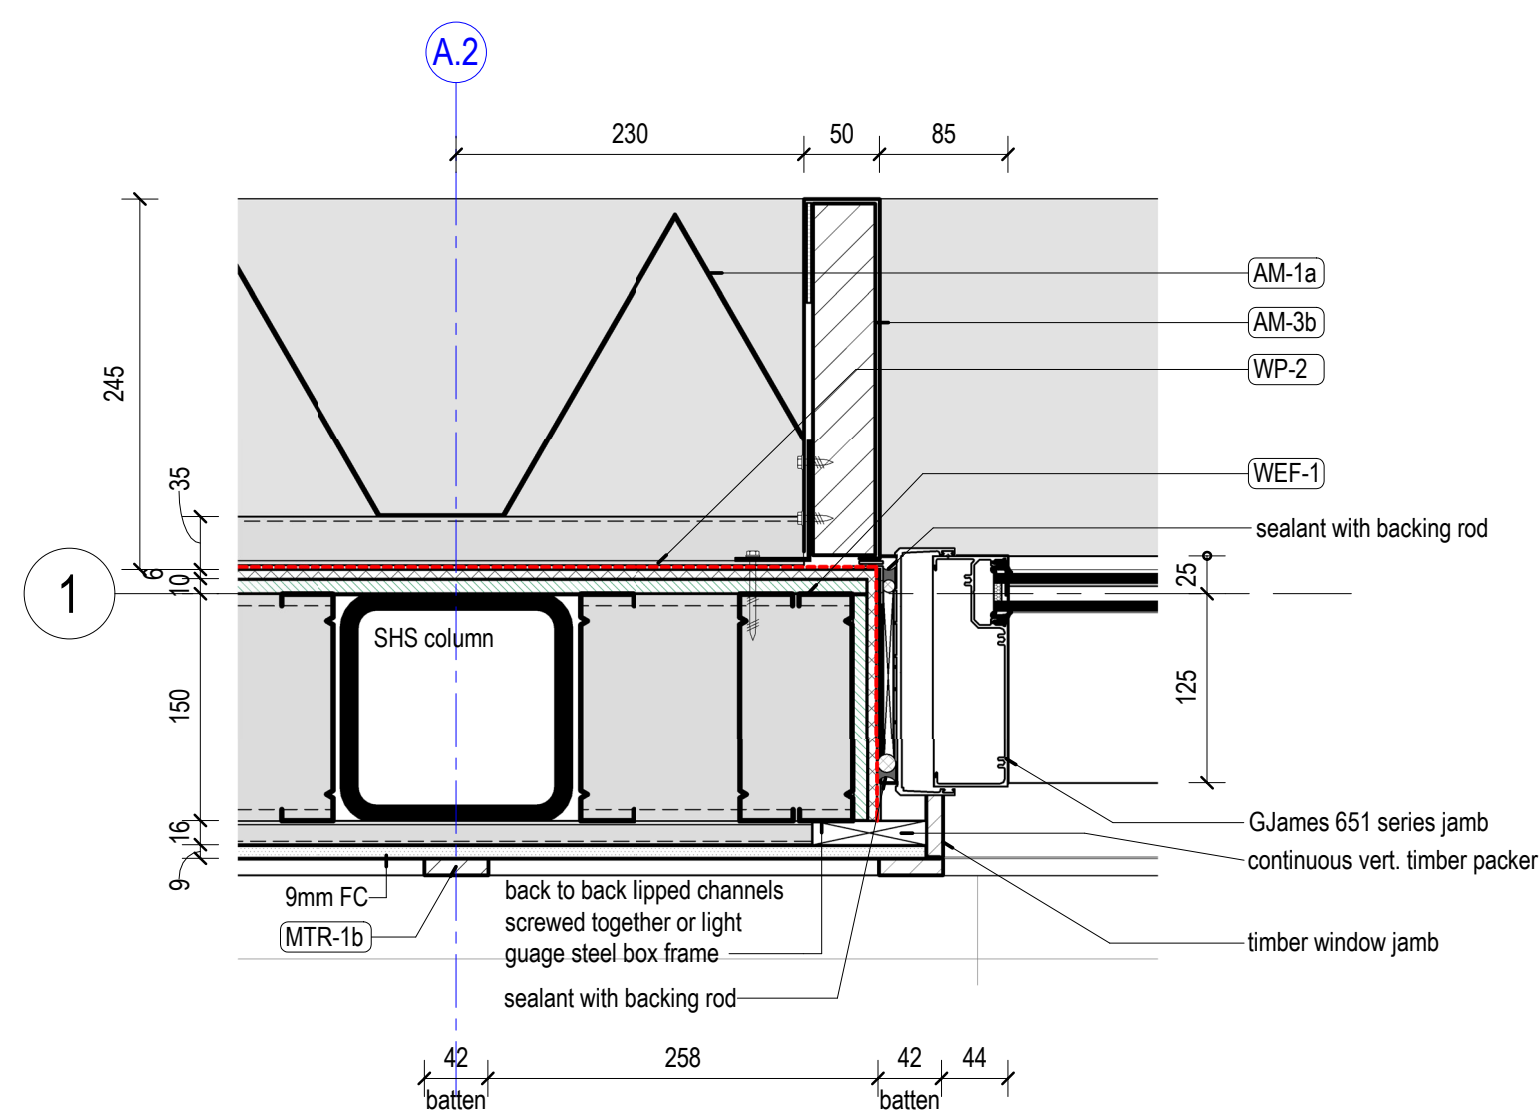


1 WEF-21 Window Jamb
1 : 5 Typical Window Jamb

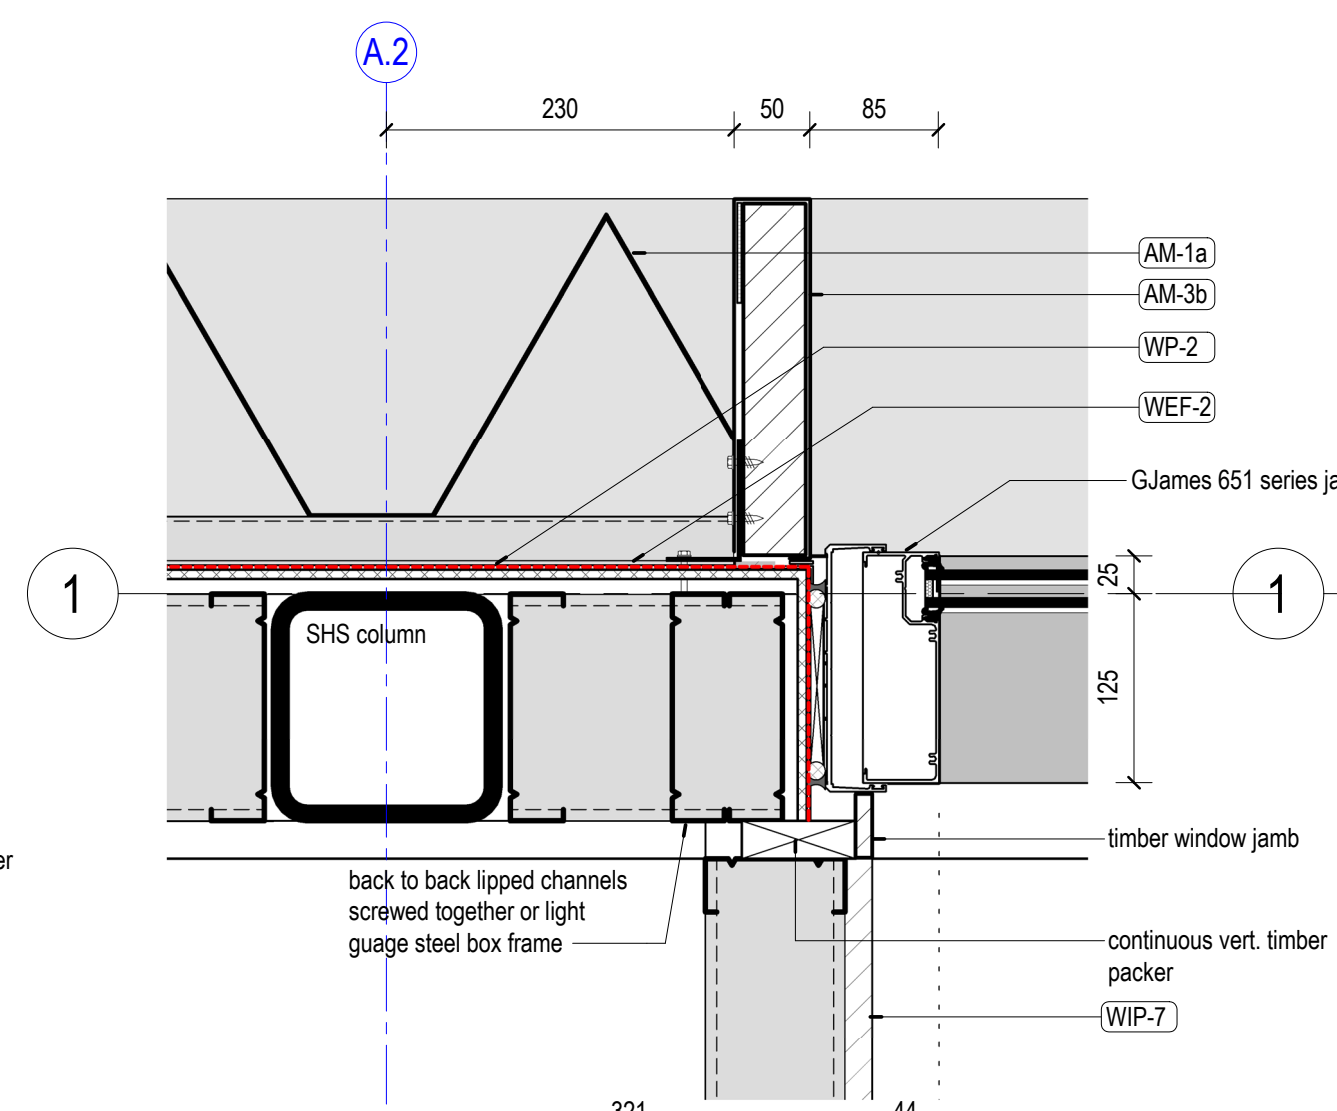

2 WEF-21 Window Jamb @ High Level
1:5

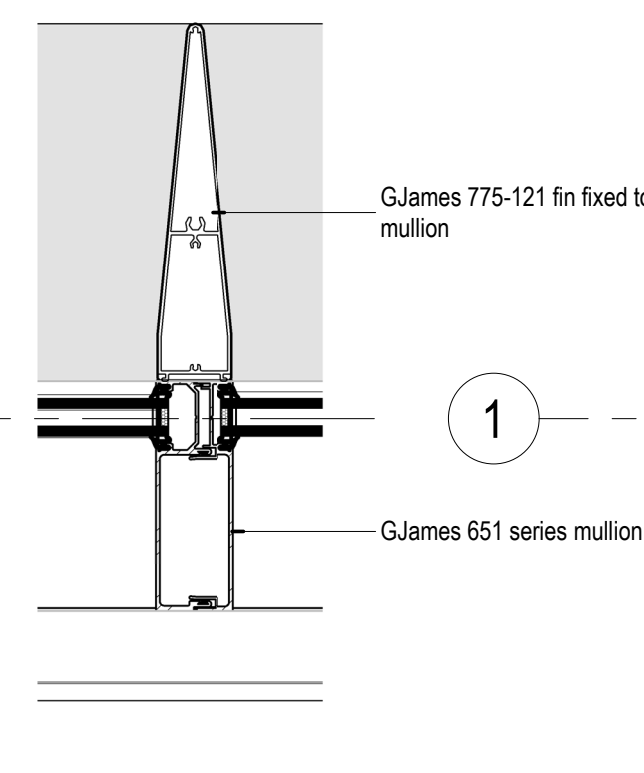

3 WEF-21 Window Fin
1 : 5 Typical

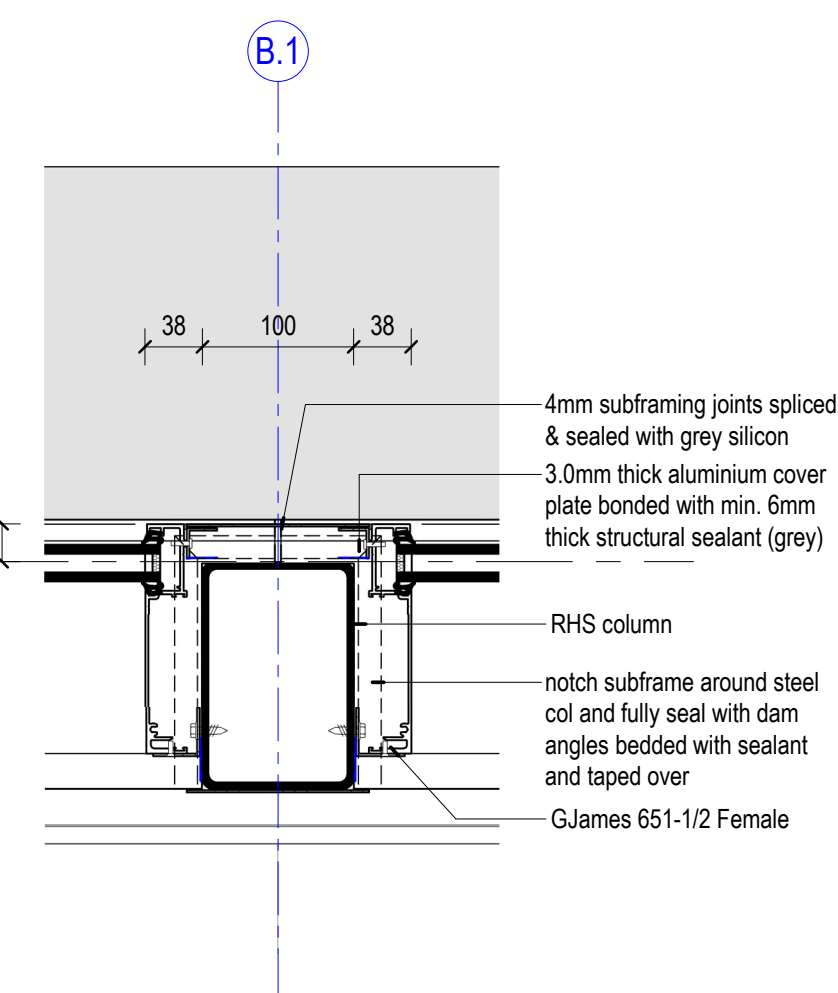

4 WEF-21 Window Column
1 : 5 Typical

DETAILS NOTES

1. All aluminium flashings @ floor level to be min. 1.6 thick. Flashings to be installed with end clamps at each end and fully sealed at the corners and vertical framing junctions. Flashings must be continuous and wrap around steel columns where they exist. Water hose test required for weathertesting validation and flood test required for sub-sill after installation of sub-jamb & sub-sill.
2. For all screw fixings between timber or aluminium framed cladding and the substrate, apply a blob of sealant before installation and seal screw heads after. Use stainless steel screws/screws only.
3. Install separation plate between dissimilar materials to prevent corrosion.

FACADE LEGEND

-
- The diagram illustrates a cross-section of a roof waterproofing system. From top to bottom, the layers are:
- WP-2** Ext. bonded membrane
 - Folded aluminium flashing
 - WP-1 or 3** Floor Waterproof Membrane
 - WP-4** Ext. non-bonded membrane
 - Roof sarking

Drawings include colour information. A black & white copy may not have all the information
This background is coloured blue.

brian hooperarchitect
m3architecture

ph: +61 7 3831 4644
11 saint james street petrie tce q 4000
info@m3architecture.com
www.m3architecture.com

client  stanwell

project Stanwell New Projects Office
Switchyard Road,
Stanwell, QLD, 4702

title	Plan Details - Facade
-------	-----------------------

drawn bg
checked jb
date March 2026
scale 1 : 5 at A1
drawing 25010 / cd A-710001 / T1

copyright ©
These designs, plans, specifications and the
copyright herein are the property of the architect
and must not be used, reproduced, or copied
wholly or in part without the written permission of
m3architecture pty ltd abn 23 079 044 545.
Use figured dimensions in preference to scale.
If there are any questions contact the architect

1:1 at A1