




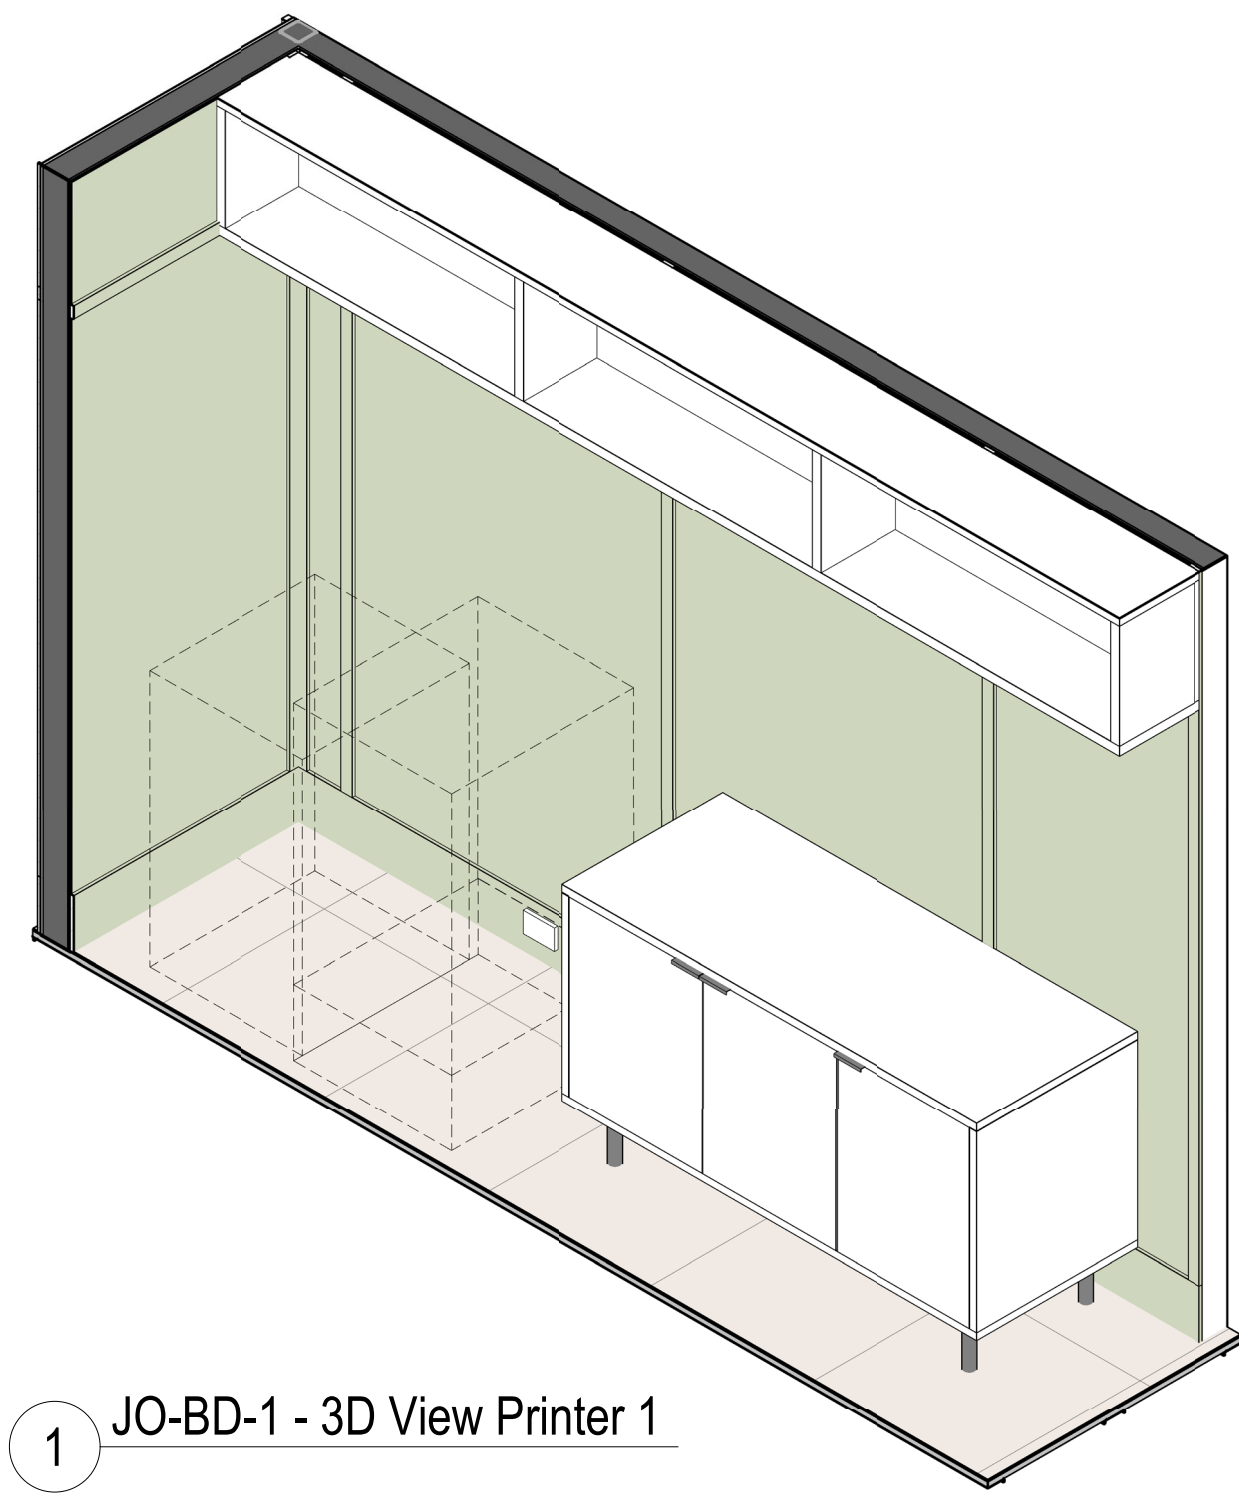

1 JO-BD-1 - 3D View Printer 1

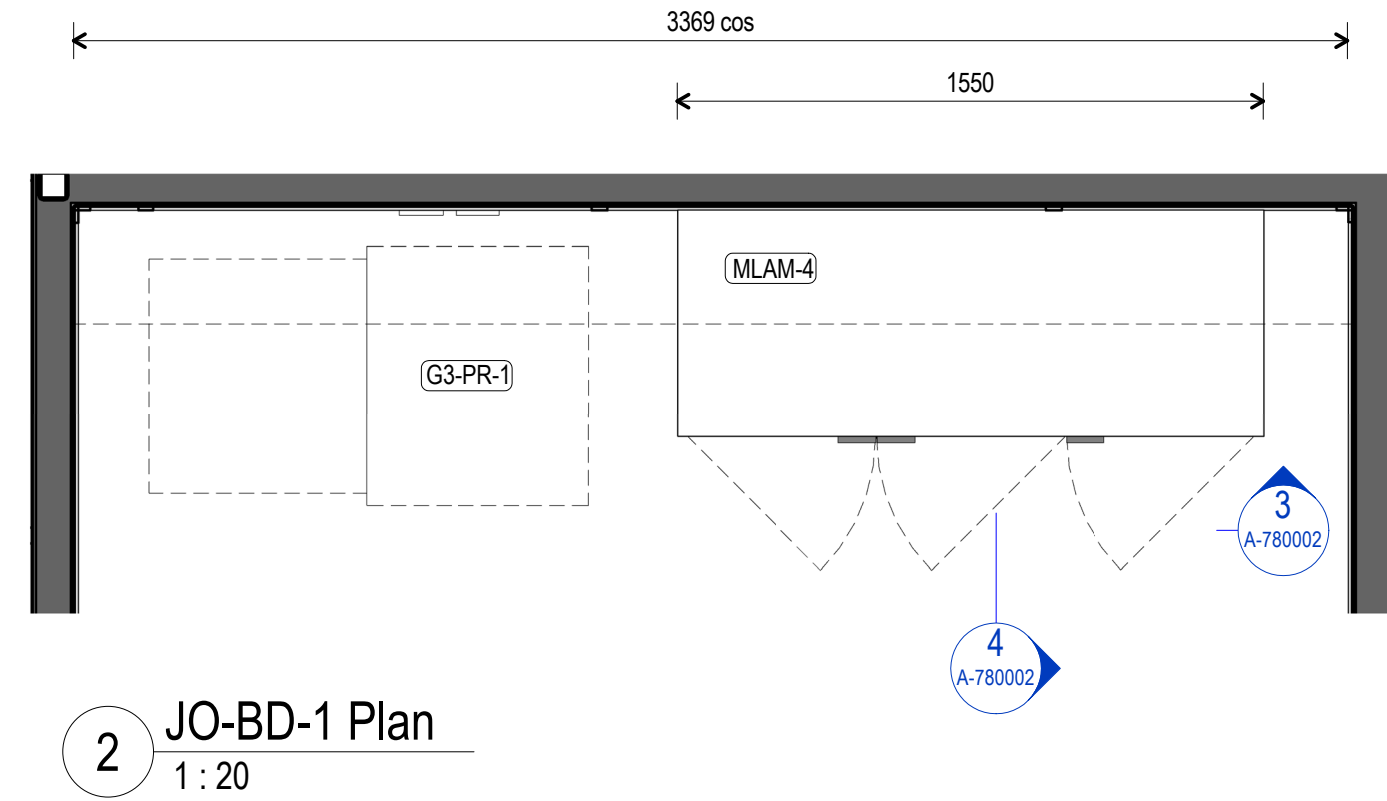


2 JO-BD-1 Plan
1:20

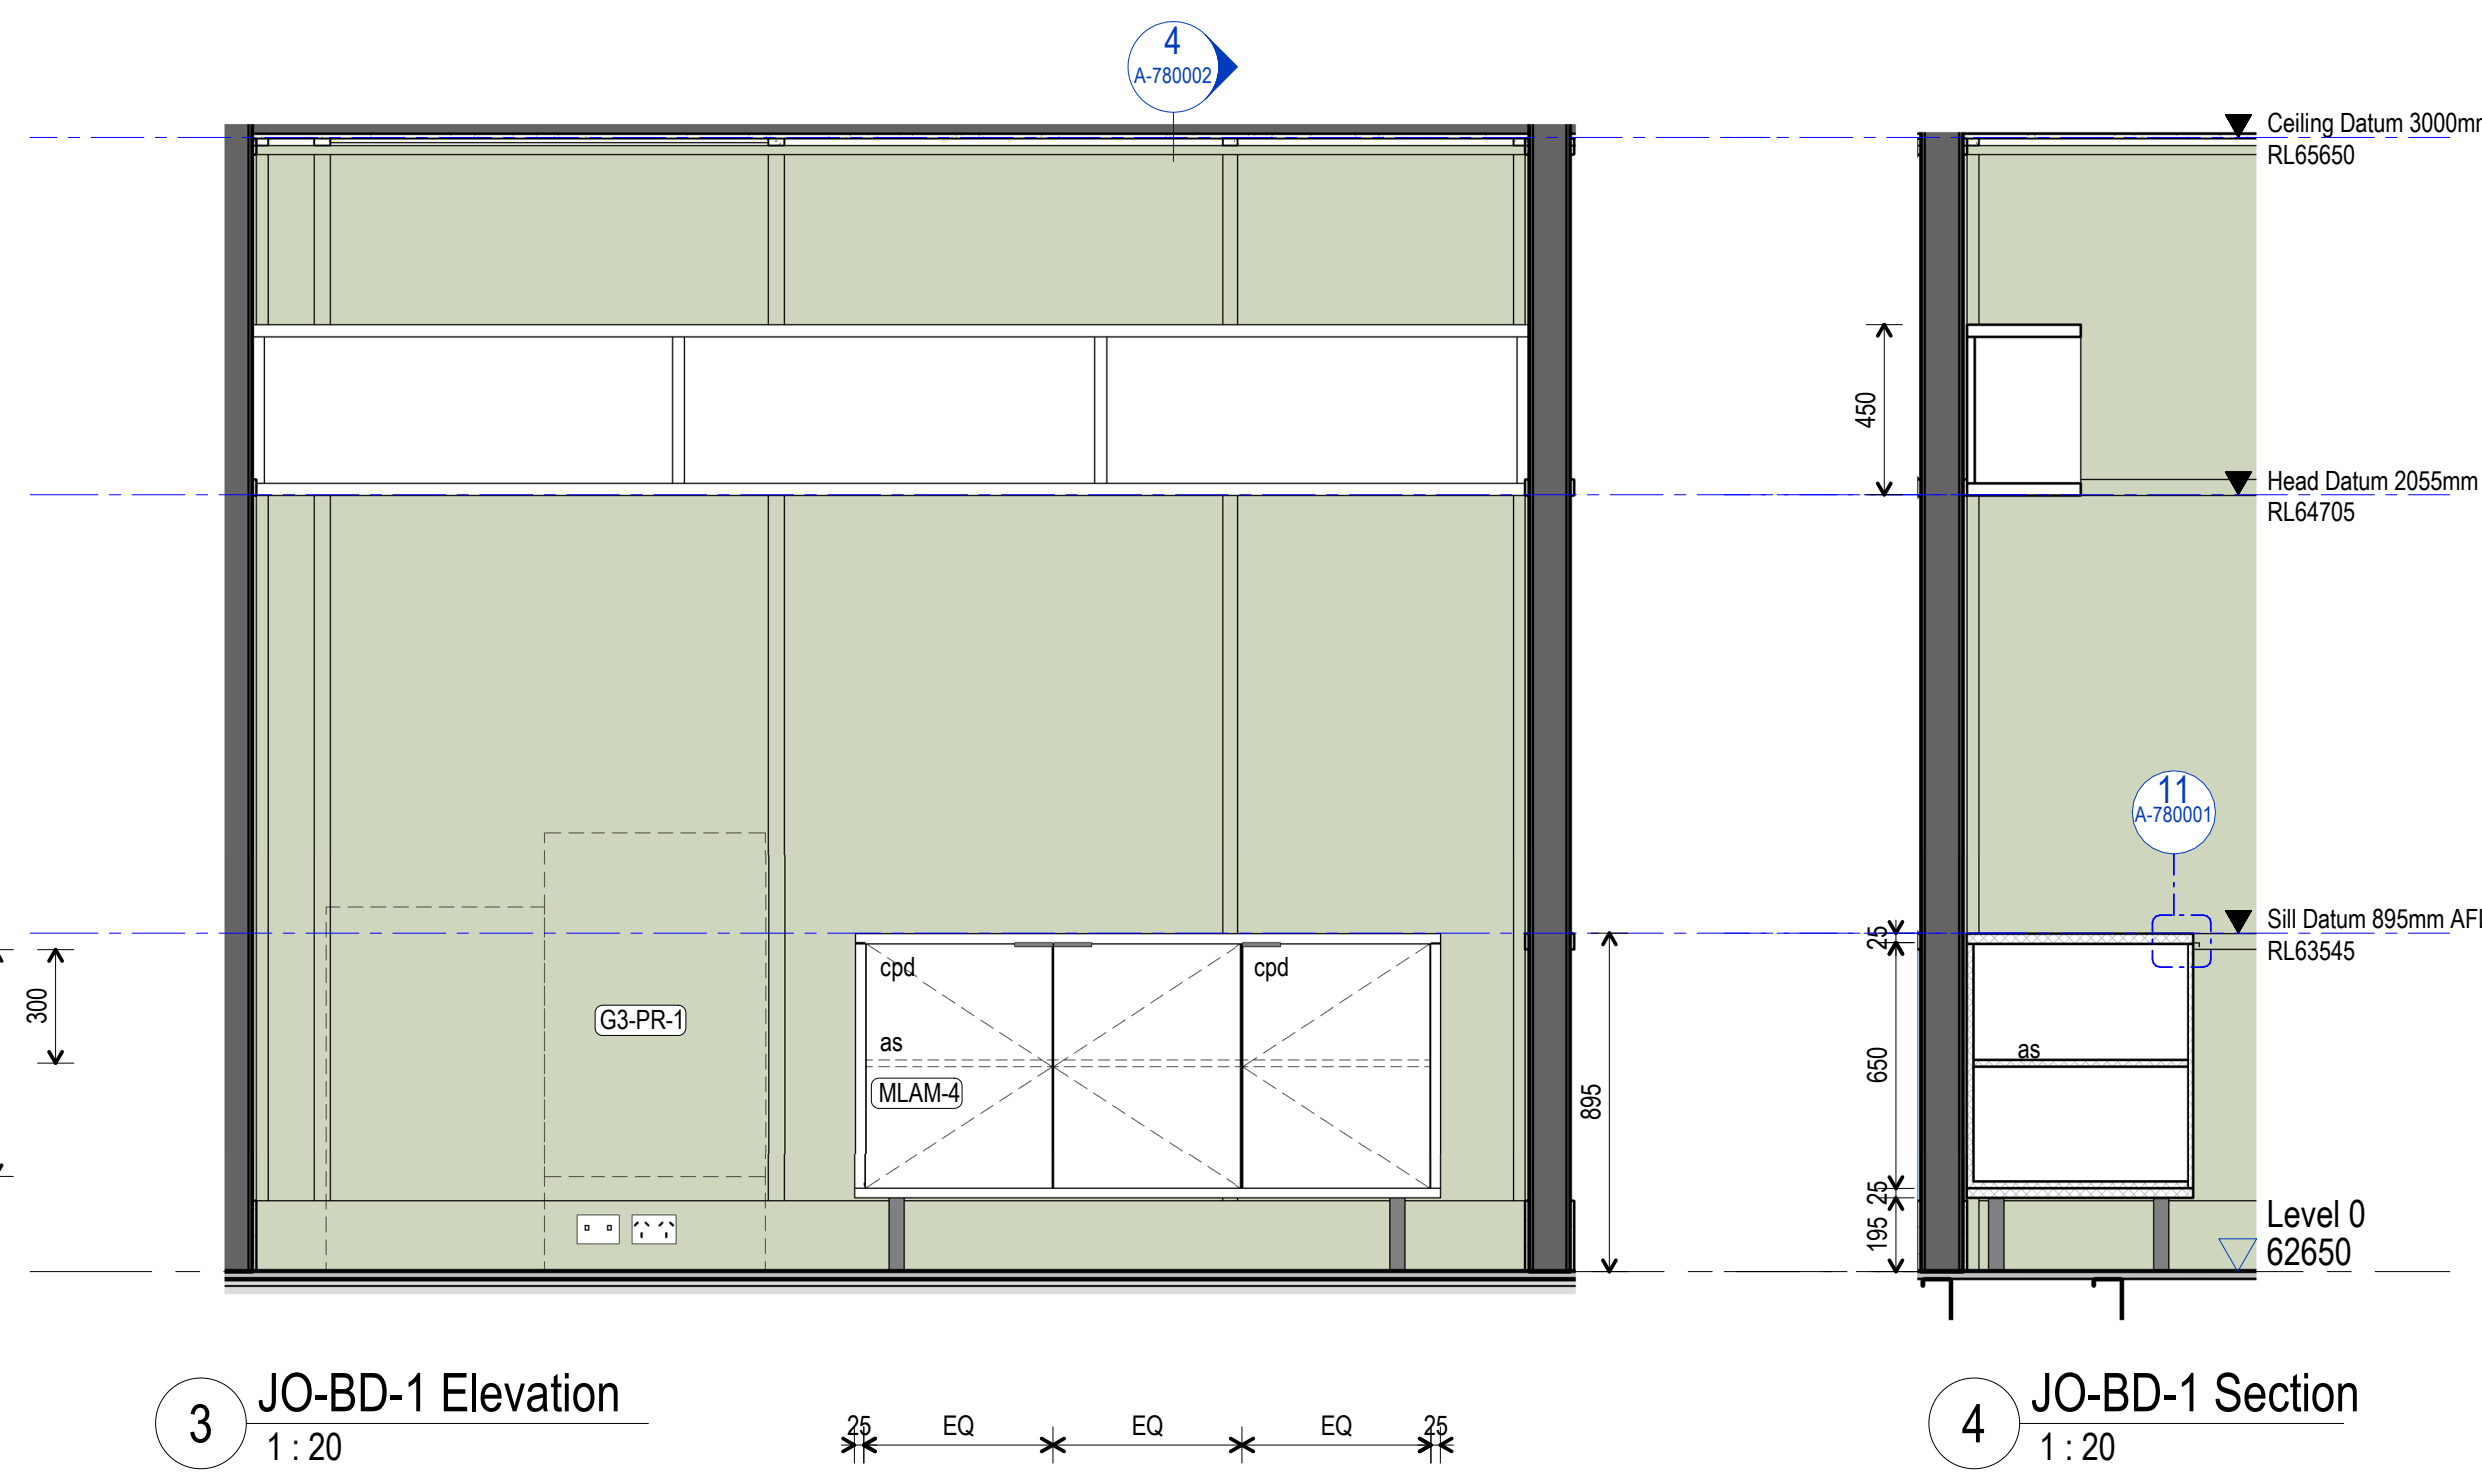


3 JO-BD-1 Elevation
1:20


4 JO-BD-1 Section
1:20

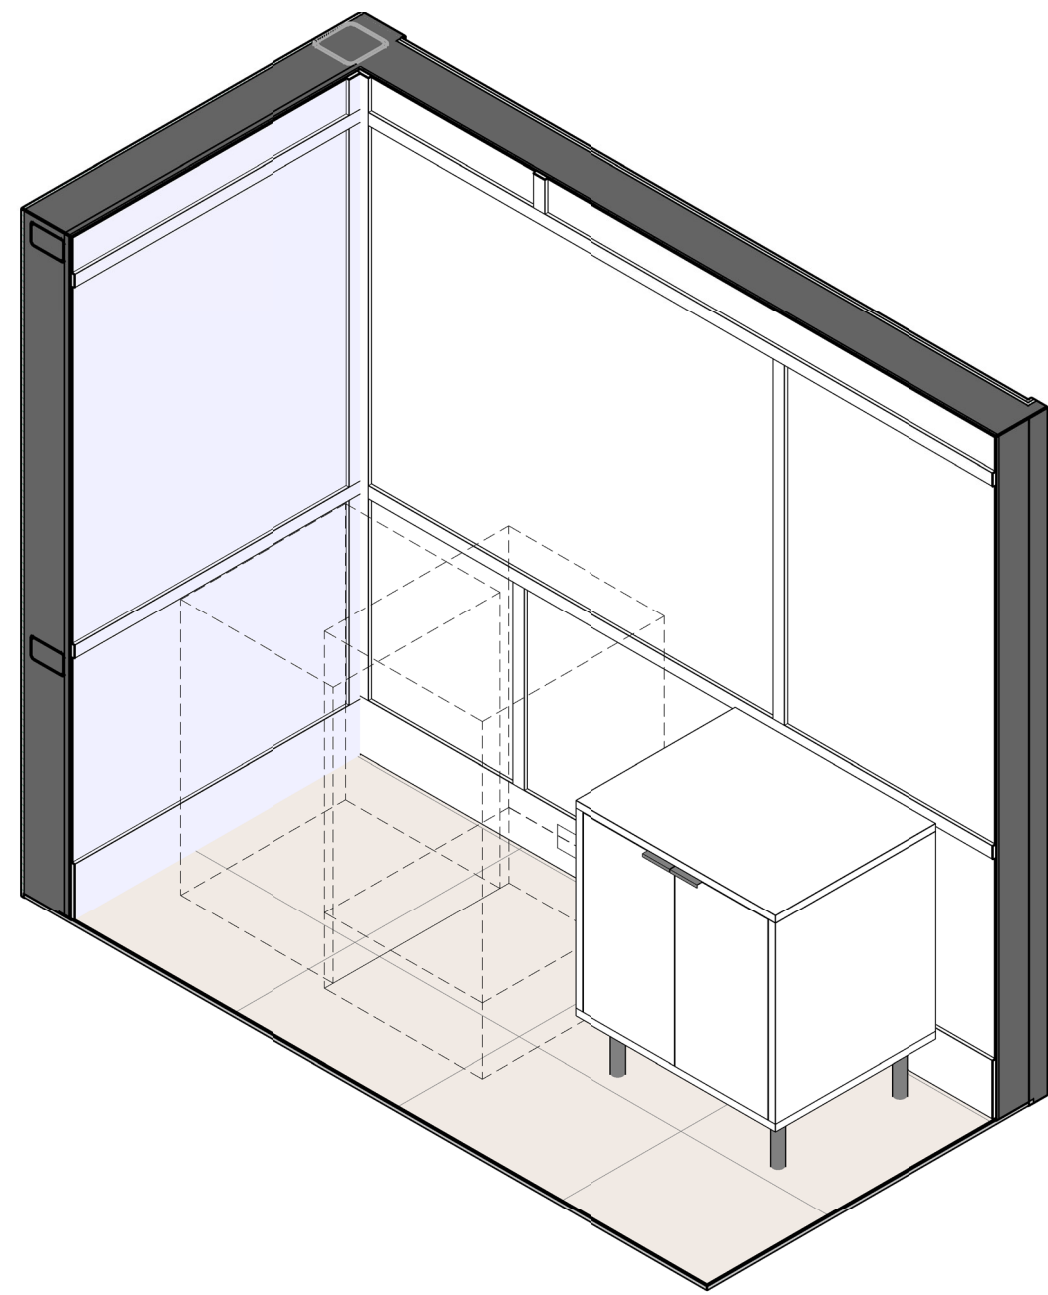

5 JO-BD-2 - 3D View Printer 2

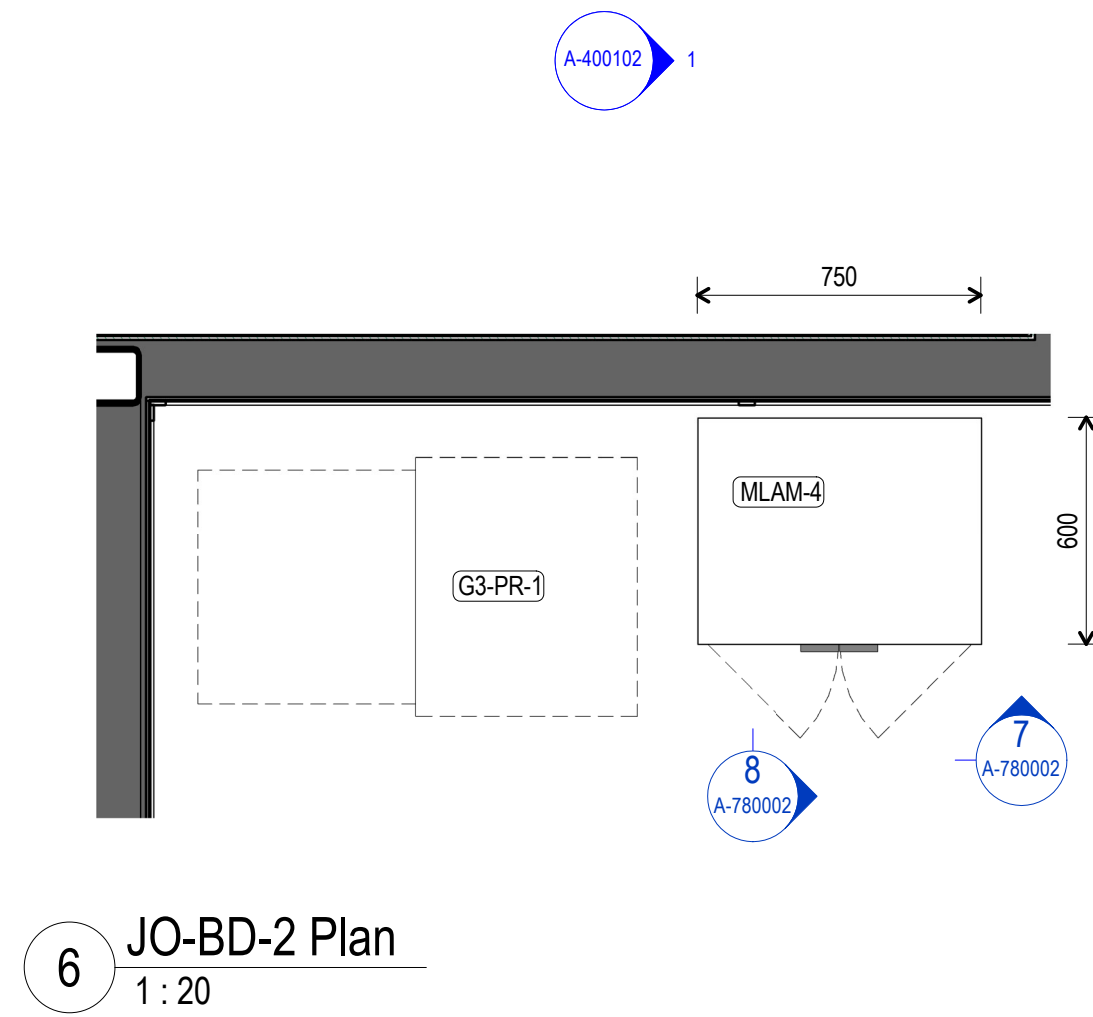


6 JO-BD-2 Plan
1:20

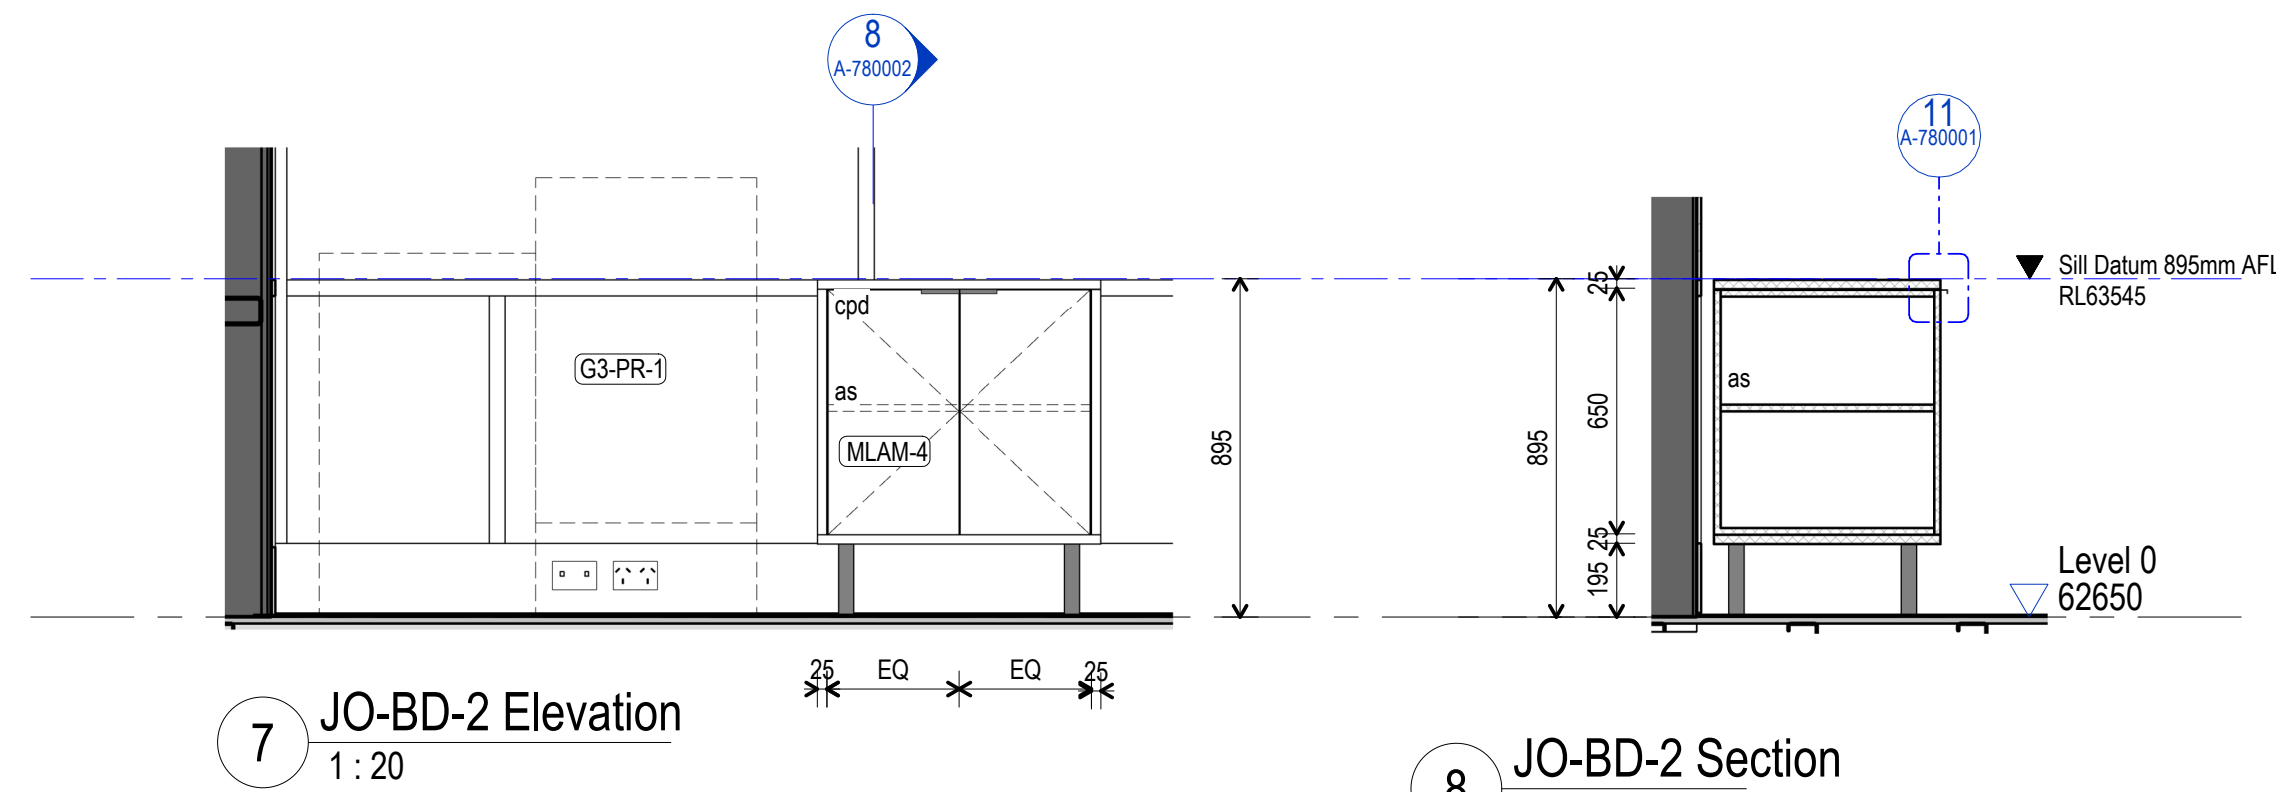


7 JO-BD-2 Elevation
1:20


8 JO-BD-2 Section
1:20

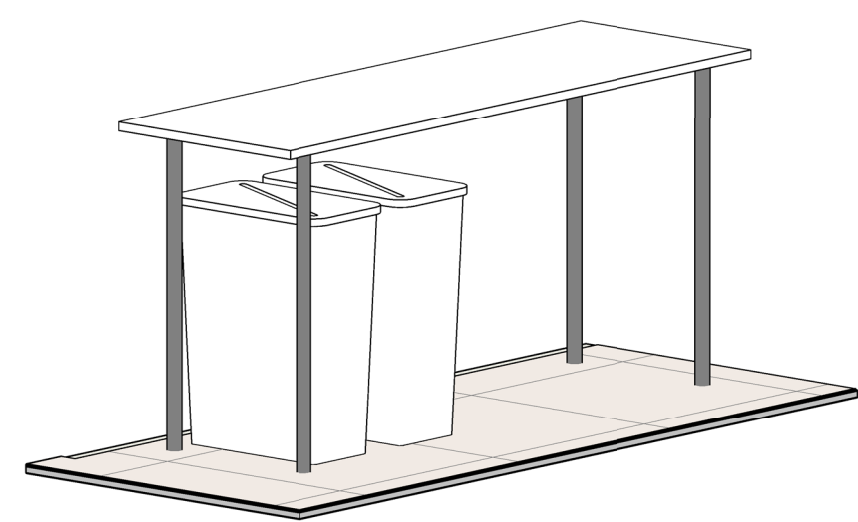


9 JO-BD-3 - 3D View Printer 3

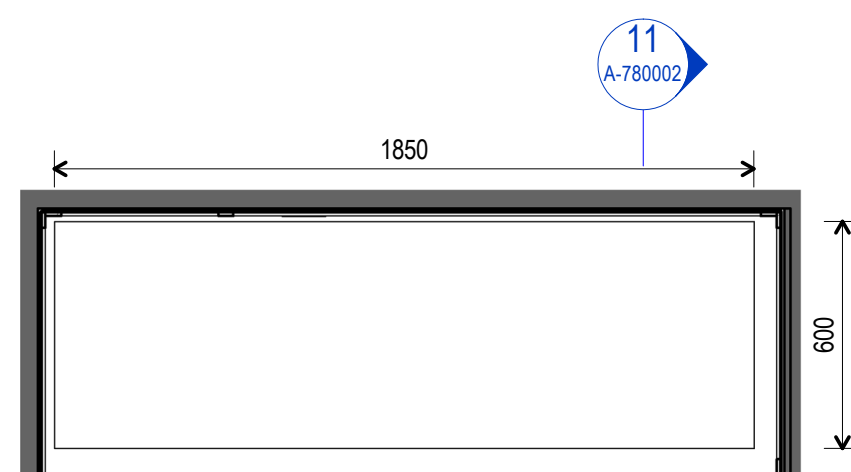


10 JO-BD-3 Plan
1:20

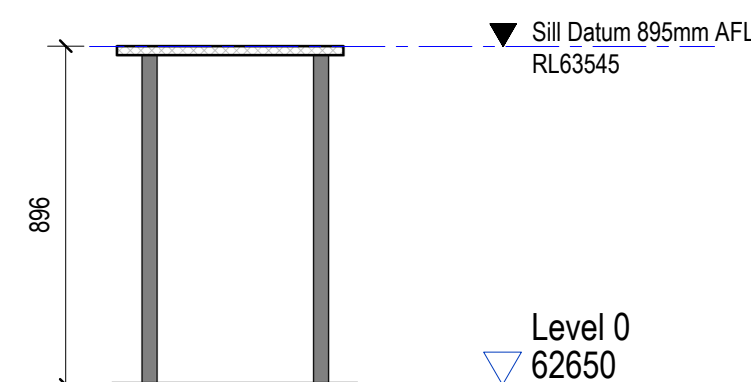

11 JO-BD-3 Section
1:20

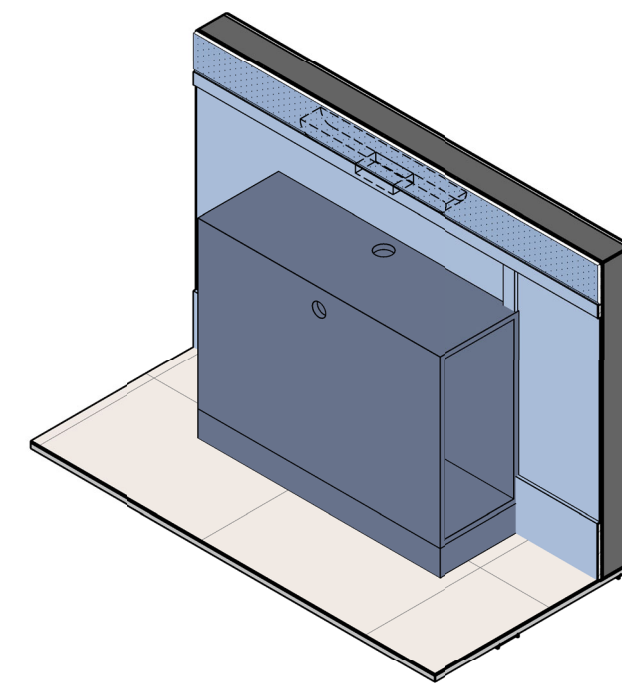

12 JO-BD-4 - 3D View - Meeting Rooms

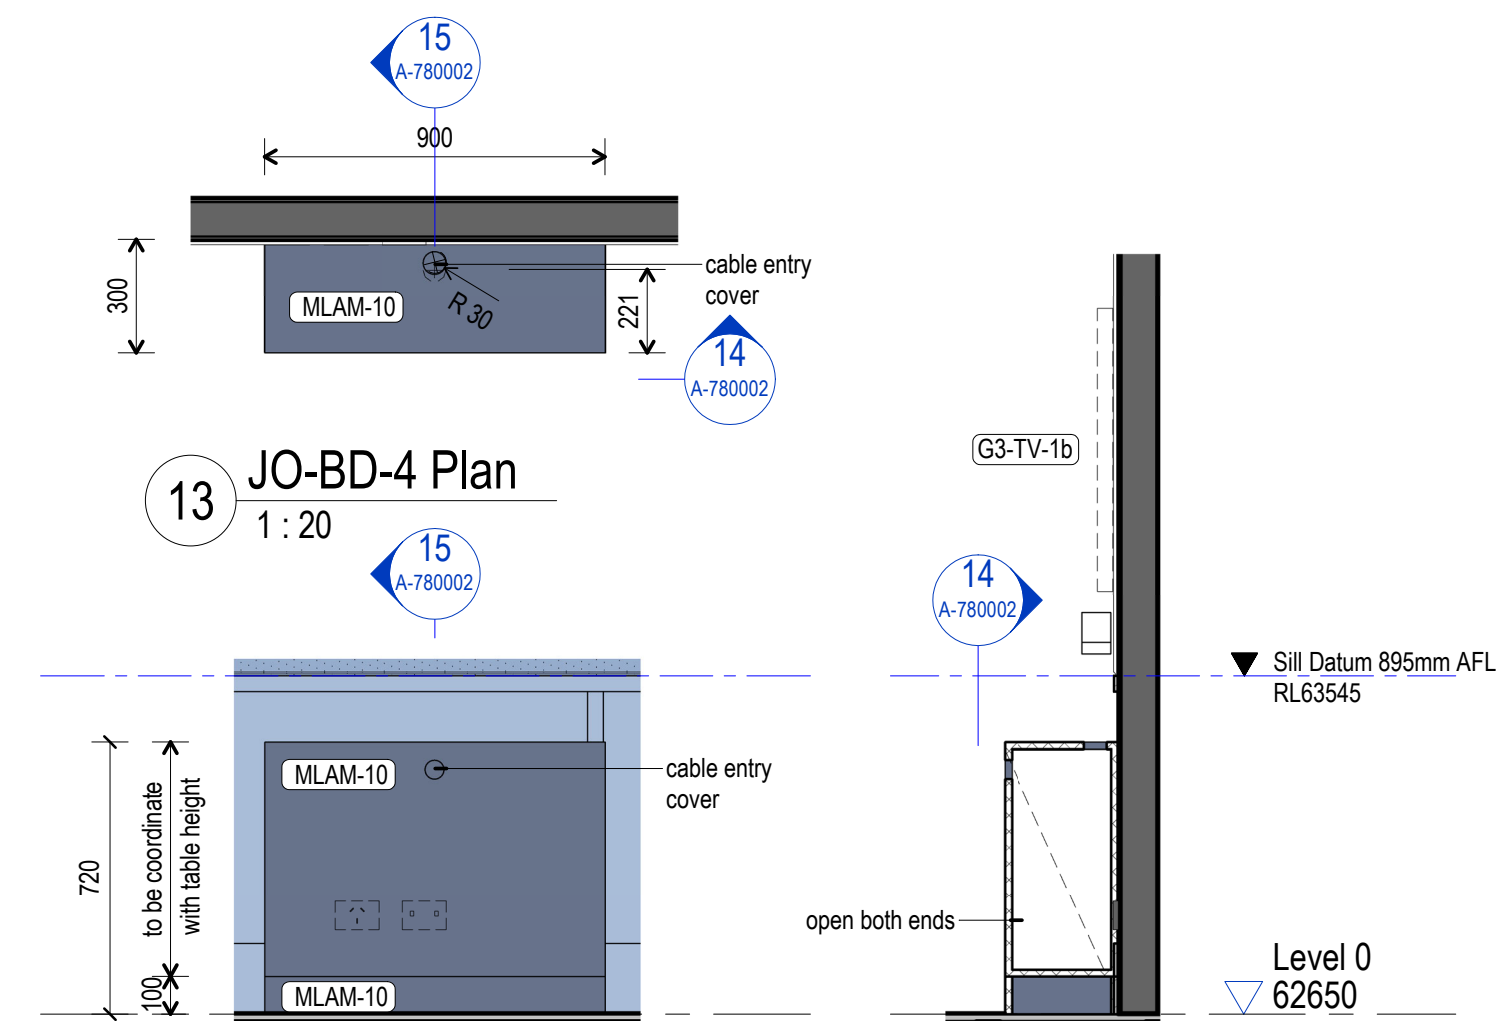

13 JO-BD-4 Plan
1:20

14 JO-BD-4 Elevation
1:20

15 JO-BD-4 Section
1:20

PRELIMINARY
NOT FOR CONSTRUCTION

Drawings include colour information. A black & white copy may not have all the information. This background is coloured blue.

brian hooperarchitect
m3architecture
ph: +61 7 3831 4644
11 saint james street petrie tce q 4000
info@m3architecture.com
www.m3architecture.com

client **stanwell**

project **Stanwell New Projects Office
Switchyard Road,
Stanwell, QLD, 4702**

title **Joinery Details JO-BD-1, 2, 3 & 4**

drawn mk
checked jb
date March 2026
scale 1:20 at A1
drawing 25010 / cd A-780002 / T1

copyright ©
These designs, plans, specifications and the copyright herein are the property of the architect and must not be used, reproduced, or copied wholly or in part without the written permission of m3architecture Pty Ltd abn 23 079 044 545. Use figured dimensions in preference to scale. If there are any questions contact the architect.

1:1 at A1
0 10 20 30 40 50mm