


REFER TO SITE PLAN & CONSULTANT
DRAWINGS FOR EXTERNAL SERVICES

REVISIONS		
Rev	Description	Date
T1	TENDER ISSUE	12.03.2026

DO NOT SCALE THIS DRAWINGS


CONFIRM HEIGHTS AND LEVELS
ON SITE

CONFIRM UNDERGROUND
SERVICES ON SITE

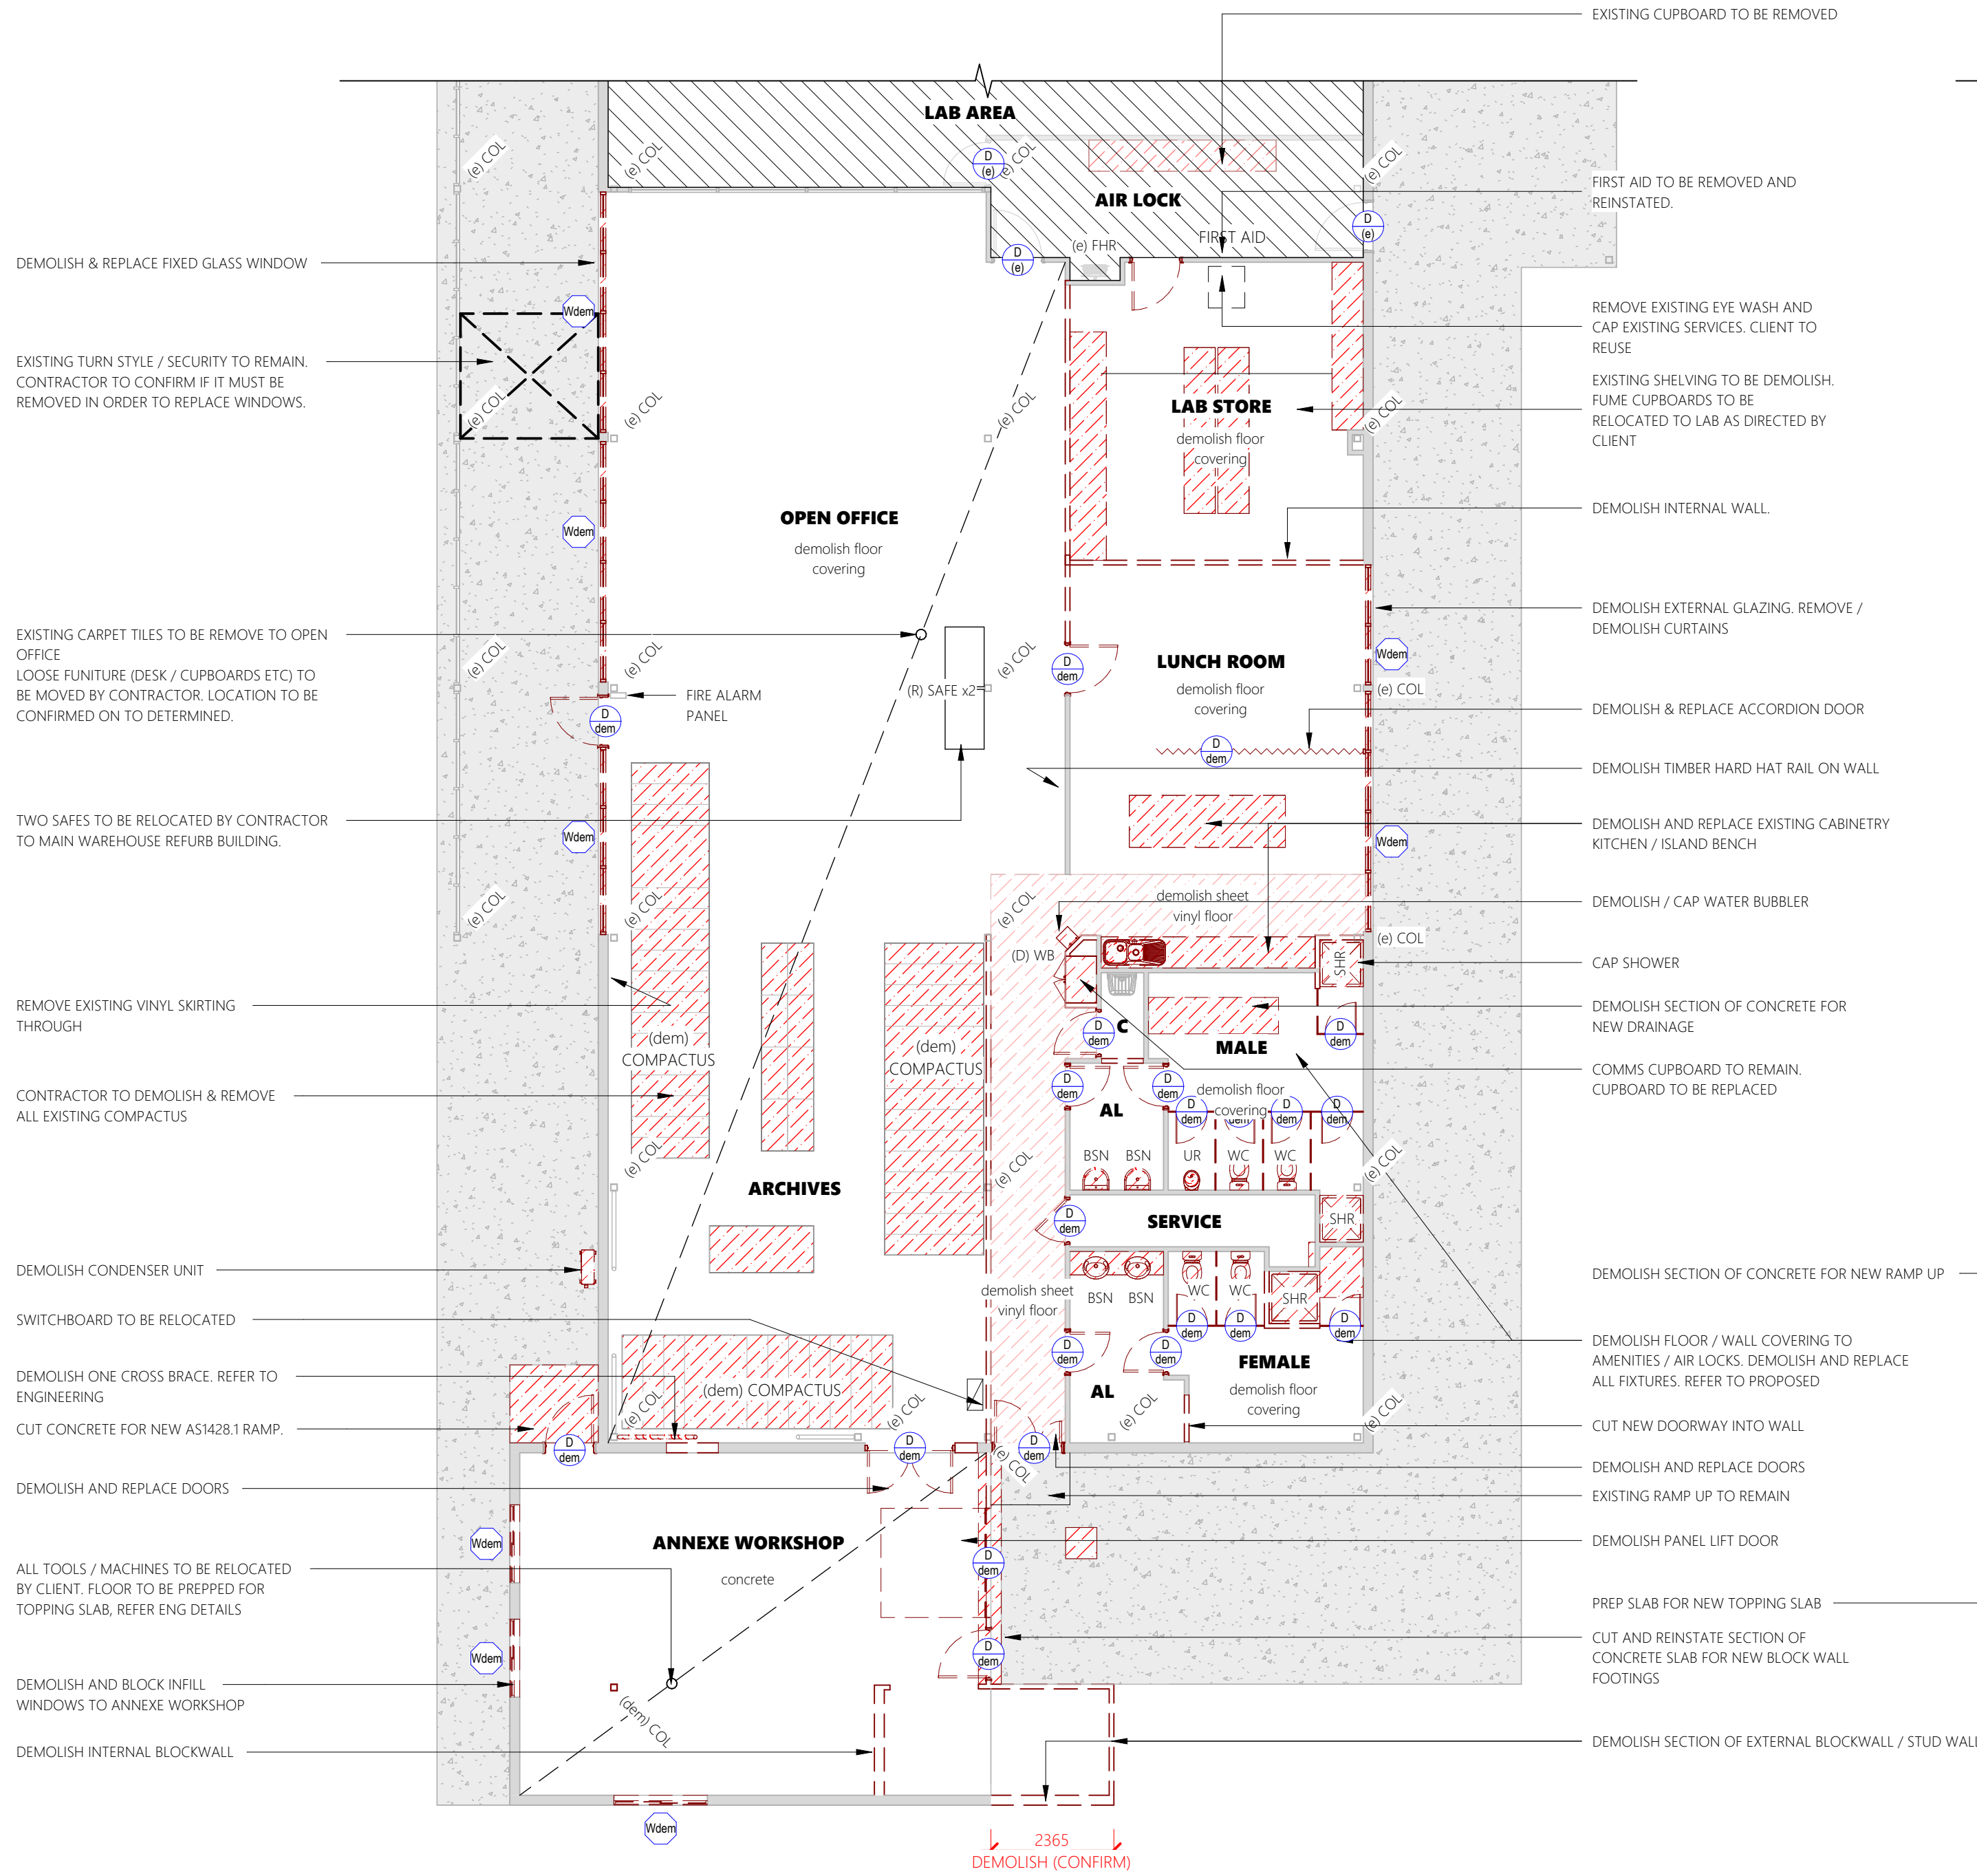



Existing Registry Floor Plan

1 : 100

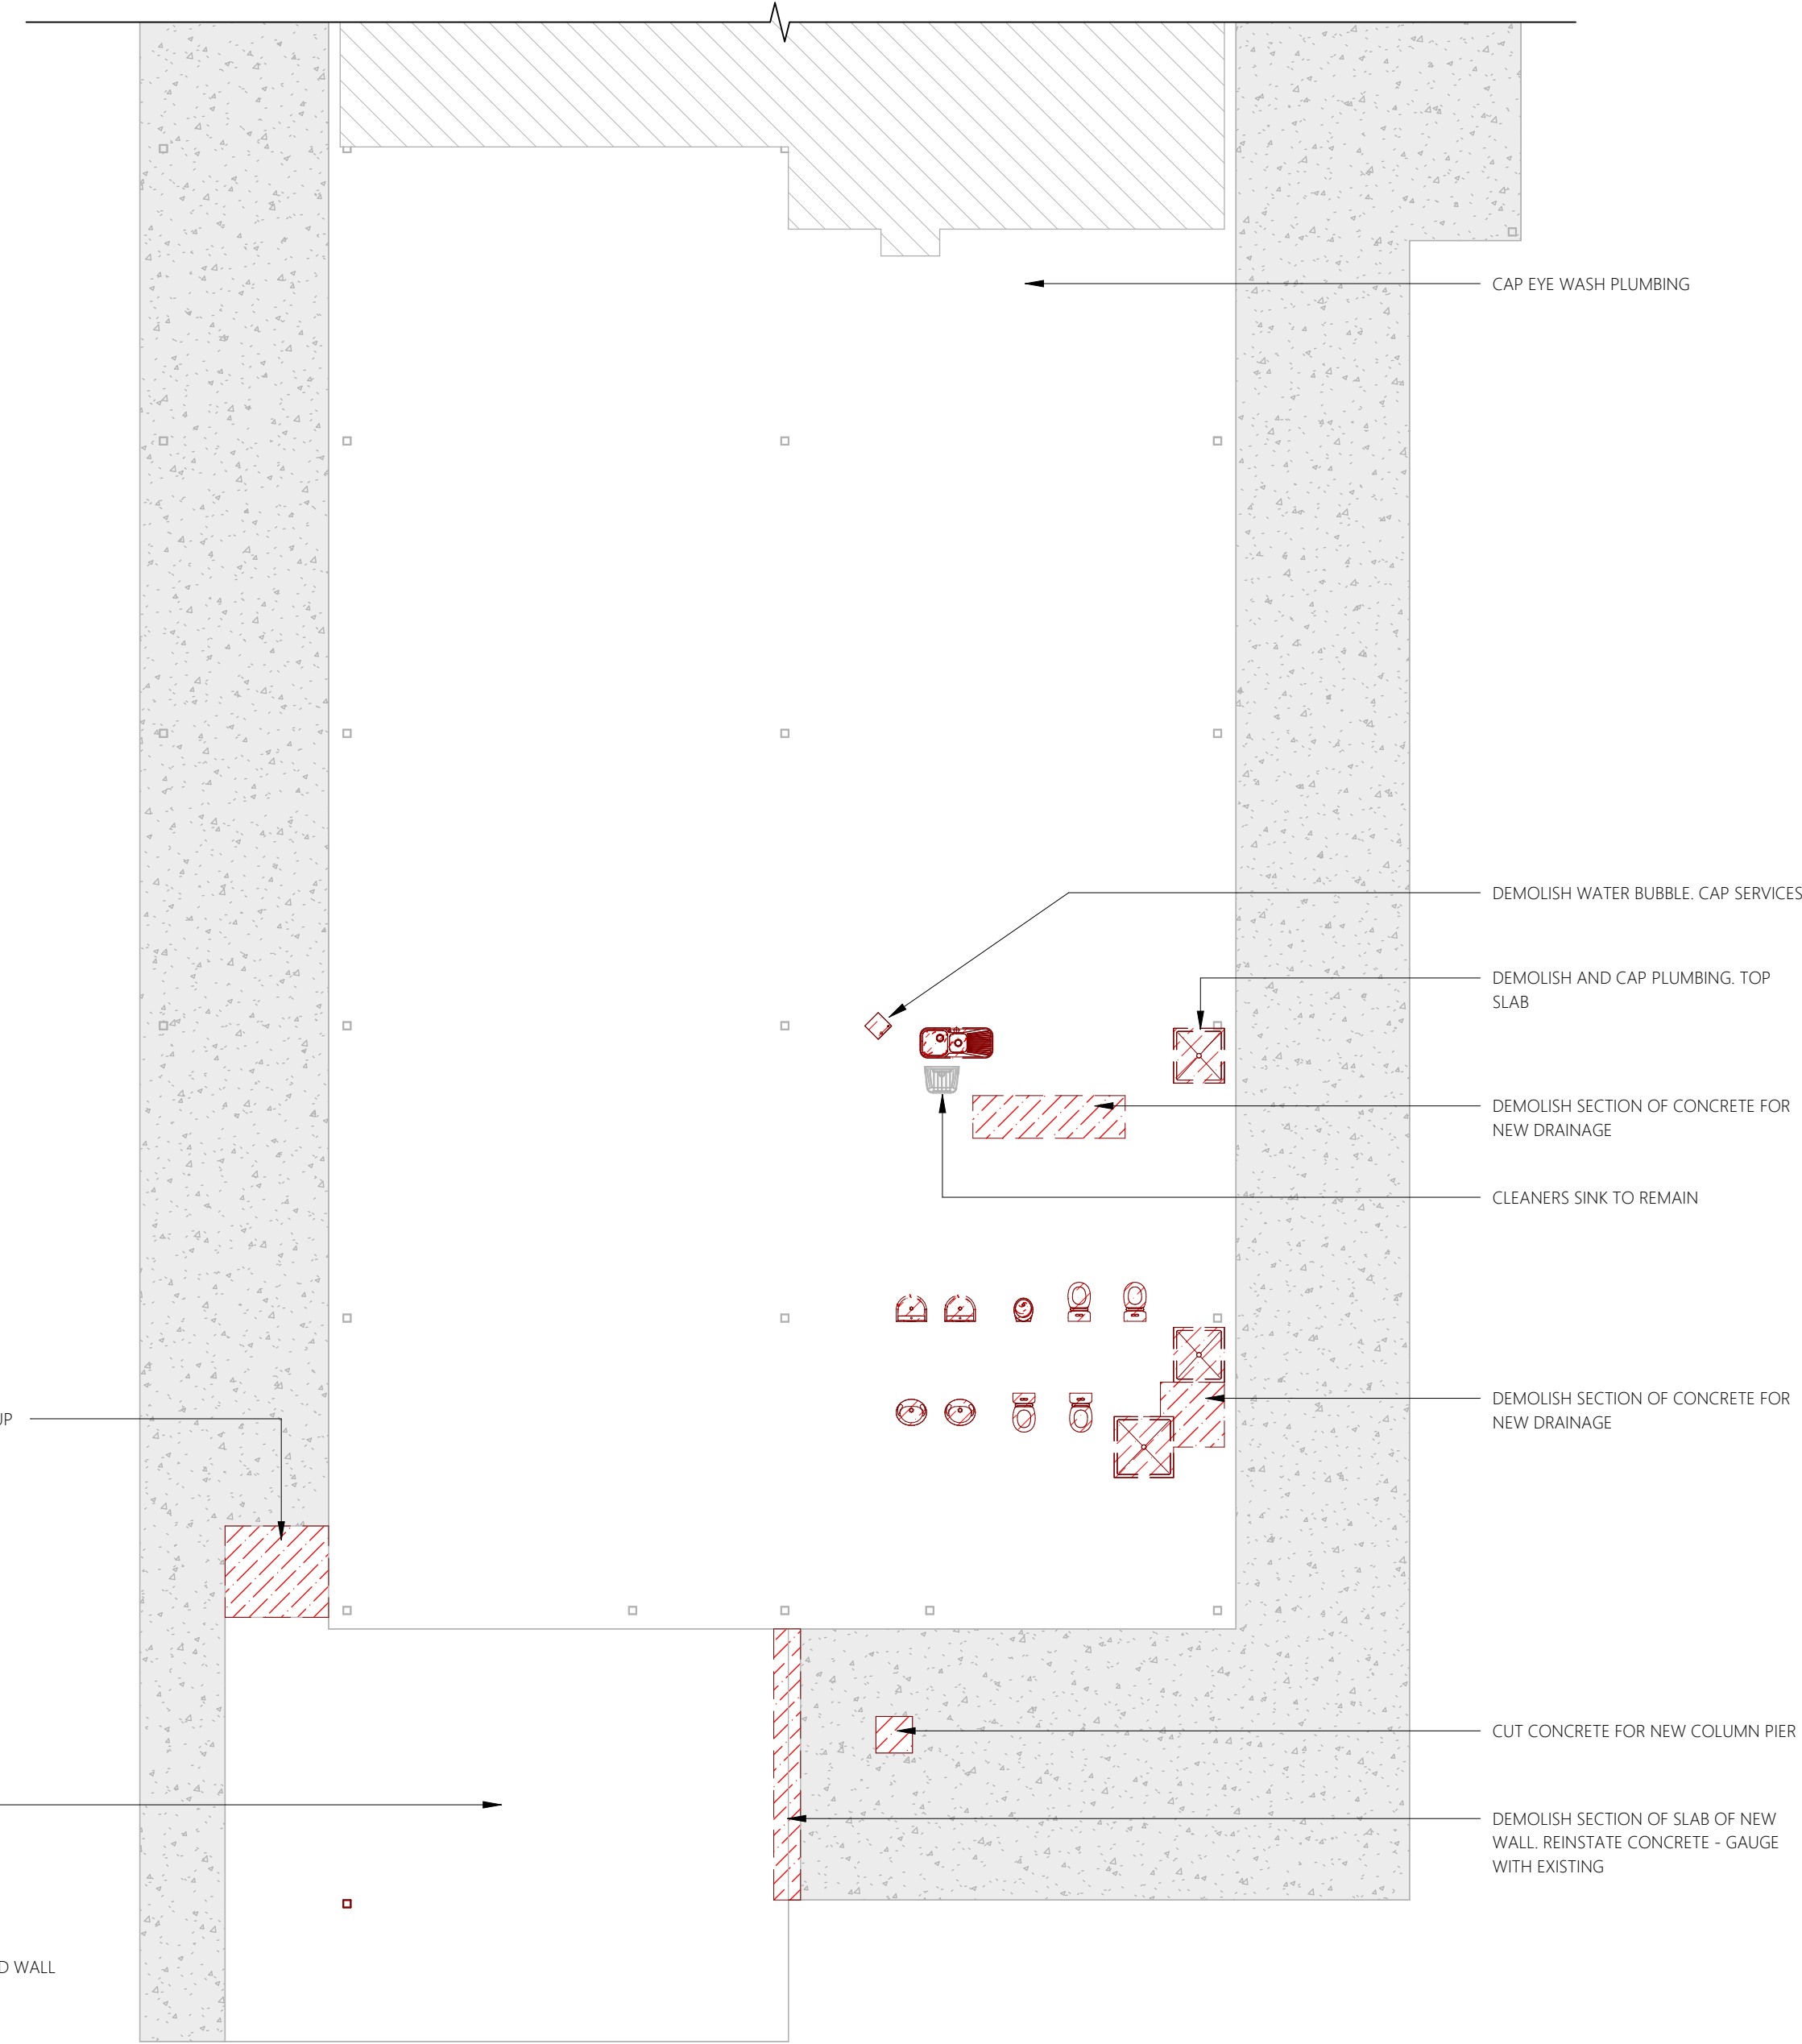

Existing Slab Plan

1 : 100

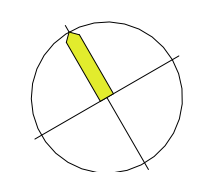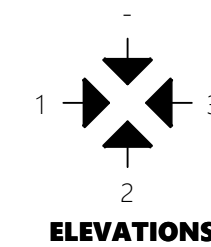

TENDER ISSUE



Project Details
REGISTRY REFURBISHMENT

Address
**STANWELL POWER
STATION**

Drawing Title
**EXISTING FLOOR & SLAB
PLAN**



0483 988 655
info@designelements.com.au

QBCC No: 1247120 BDAQ No: 0001677

Scale: 1 : 100 Rev:

Date: MARCH 2026

Drawn: NJB

Project No: Drawing No:


25_003 A1-200

12/03/2026 6:31:42 PM

LIGHTS AND AC FIXTURES SHOWN FOR INDICATION ONLY. CONFIRM ON SITE AND READ IN CONJUNCTION WITH CONSULTANT DRAWINGS

REVISIONS		
Rev	Description	Date
T1	TENDER ISSUE	12.03.2026

DO NOT SCALE THIS DRAWINGS

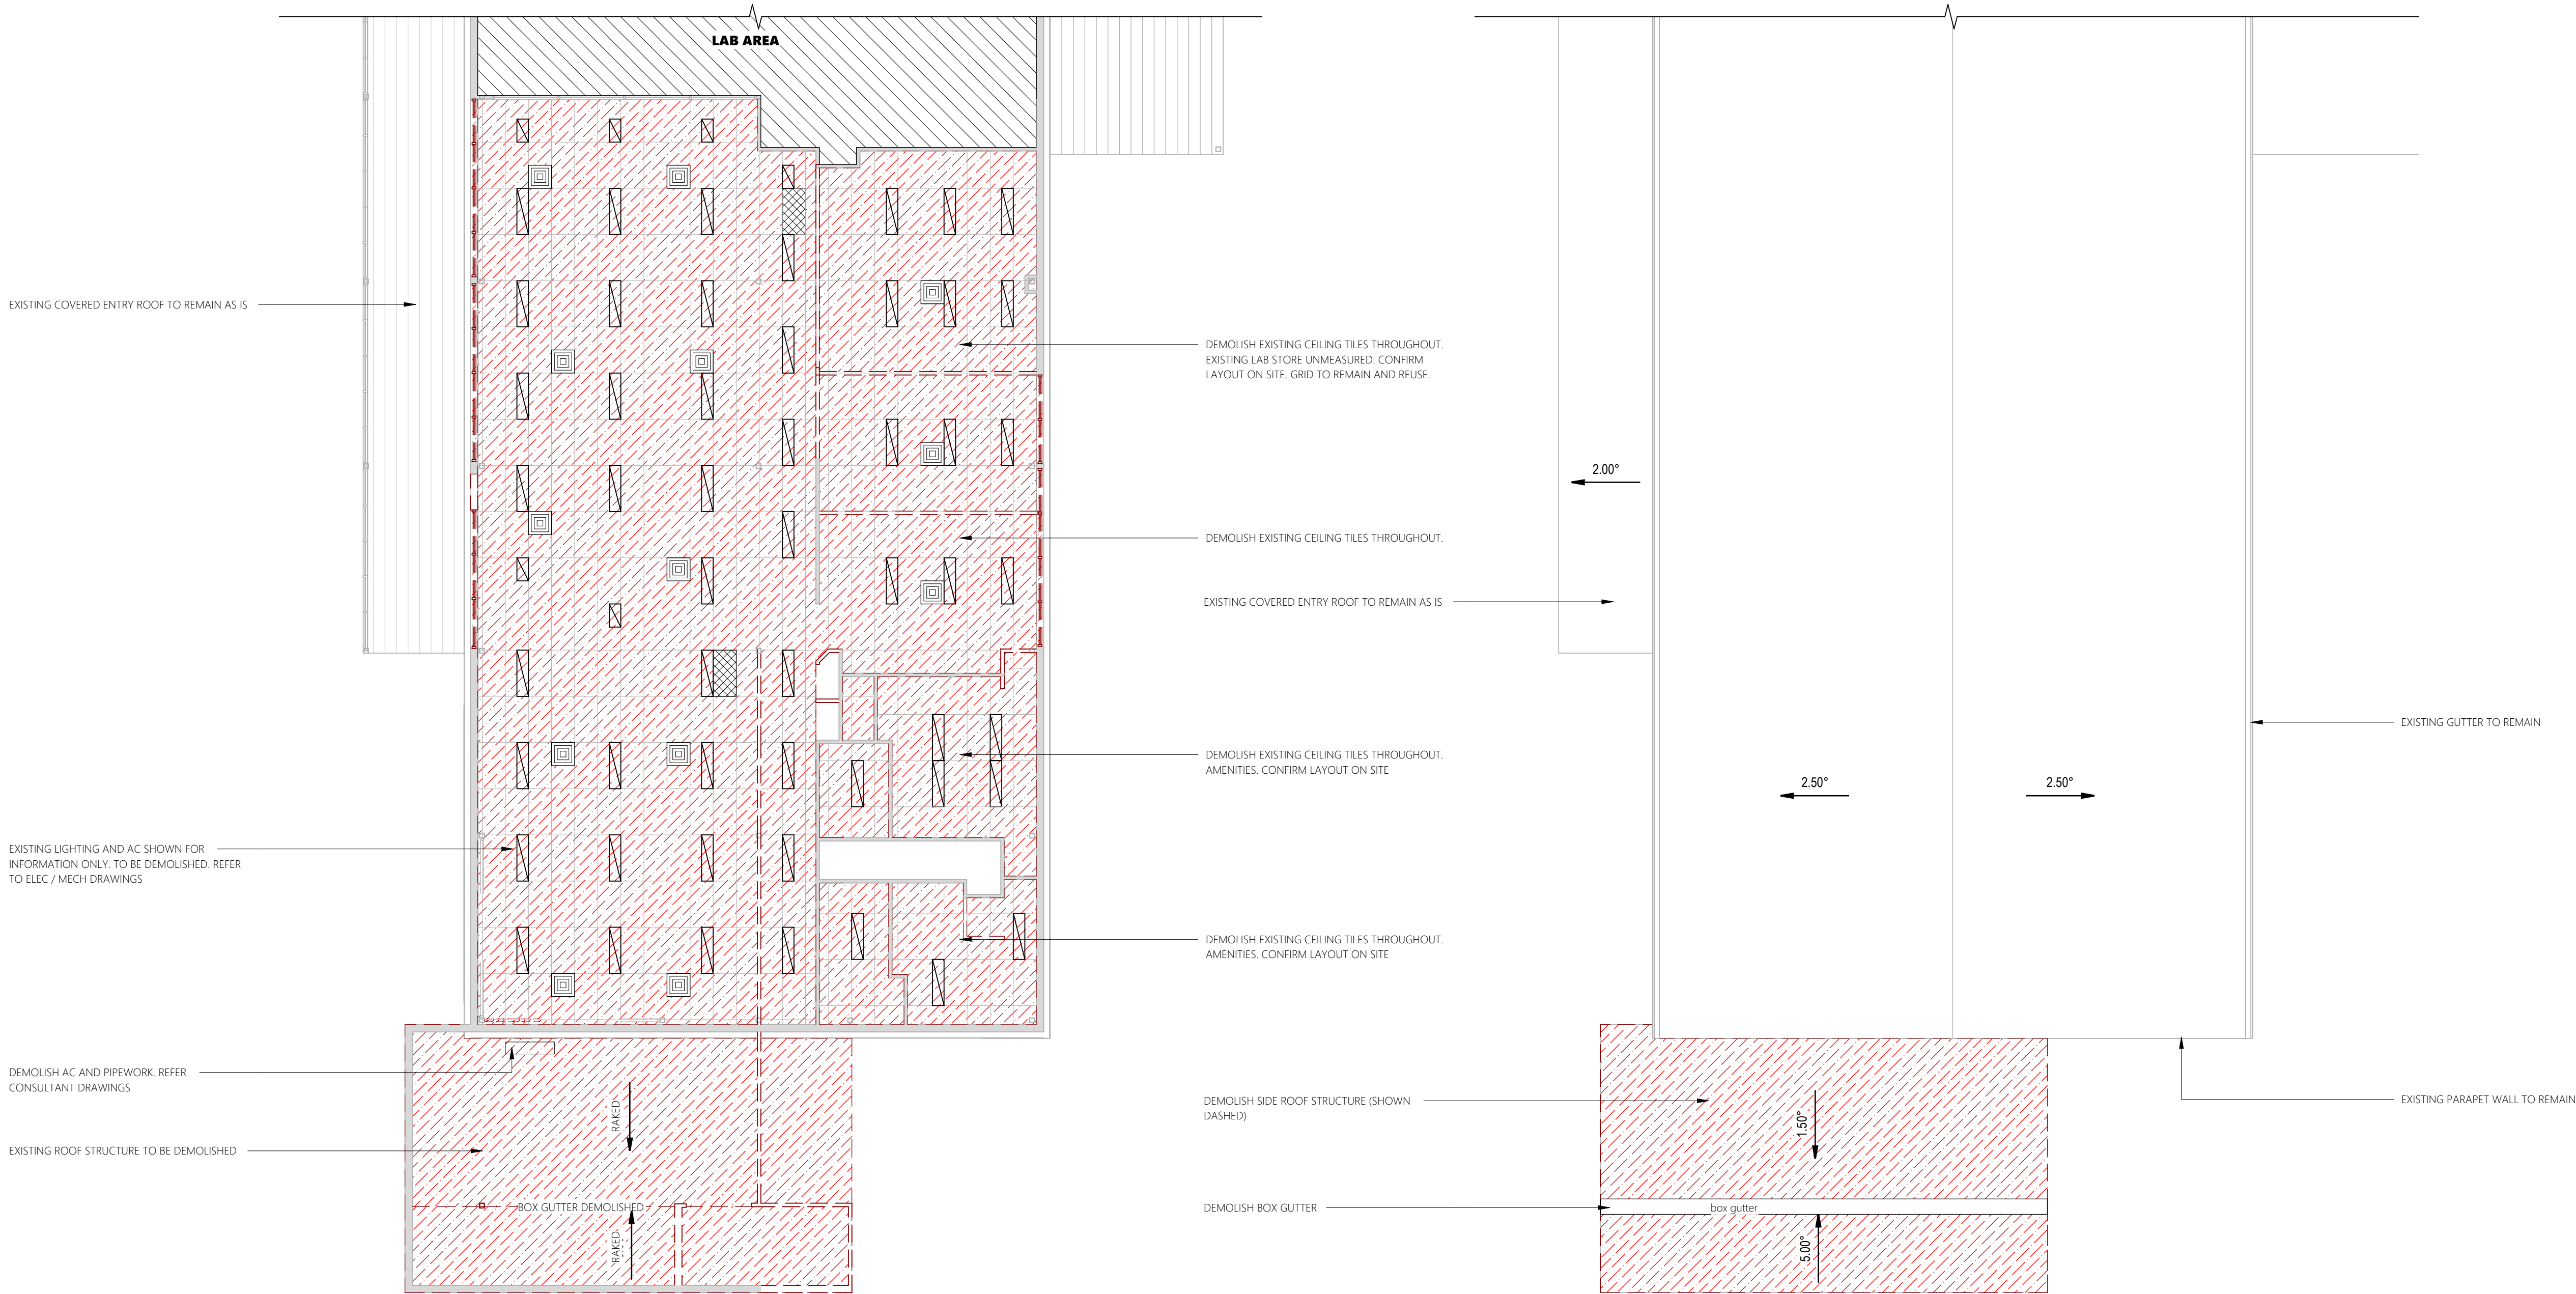

TENDER ISSUE

Client

 **stanwell**

Project Details

REGISTRY REFURBISHMENT

Address

STANWELL POWER STATION

Drawing Title

EXISTING CEILING & ROOF PLAN

Client

 **stanwell**

Project Details

REGISTRY REFURBISHMENT

Address

STANWELL POWER STATION

Drawing Title

EXISTING CEILING & ROOF PLAN


 **designelements**
BUILDING DESIGNERS

0483 988 655 **M**
info@designelements.com.au **E**

QBCC No: 1247120 BDAQ No: 0001677

Scale: 1 : 100 Rev: **T1**
Date: MARCH 2026
Drawn: NJB

Project No: Drawing No:
25_003 A1-201

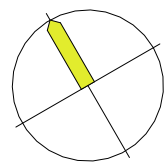

REVISIONS		
Rev	Description	Date
T1	TENDER ISSUE	12.03.2026

DO NOT SCALE THIS DRAWINGS



TENDER ISSUE

Client



Project Details

REGISTRY REFURBISHMENT

Address

STANWELL POWER STATION

Drawing Title

EXISTING ELEVATIONS



0483 988 655 
info@dezi elements.com.au 
QBCC No: 1247120 BDAQ No: 0001677

Scale: 1 : 100


Date: MARCH 2026

Drawn: NJB


Rev: T1

Project No: 25_003


Drawing No: A1-202

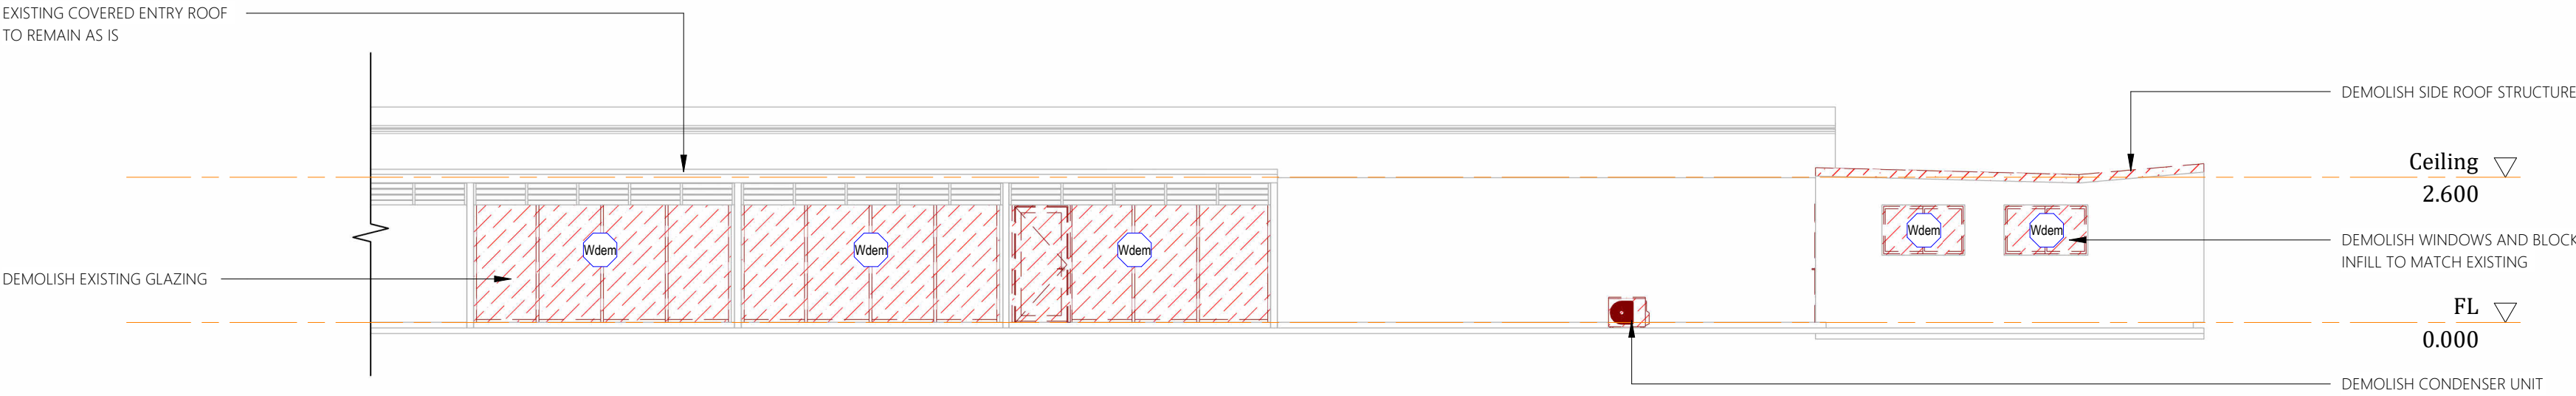

Existing Elevation 1
1 : 100

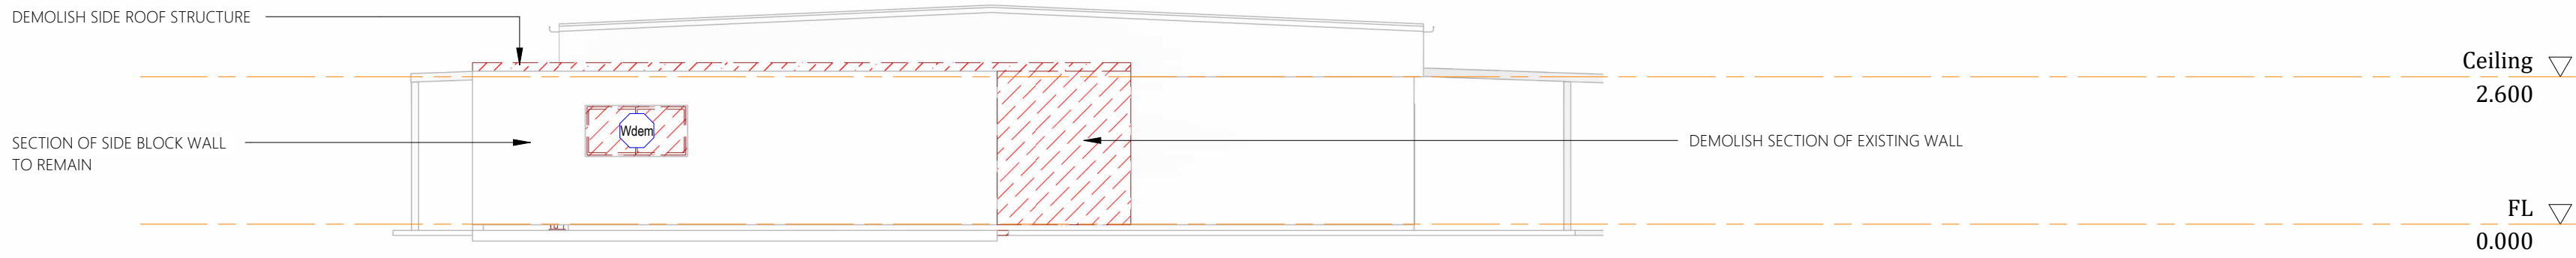

Existing Elevation 2
1 : 100

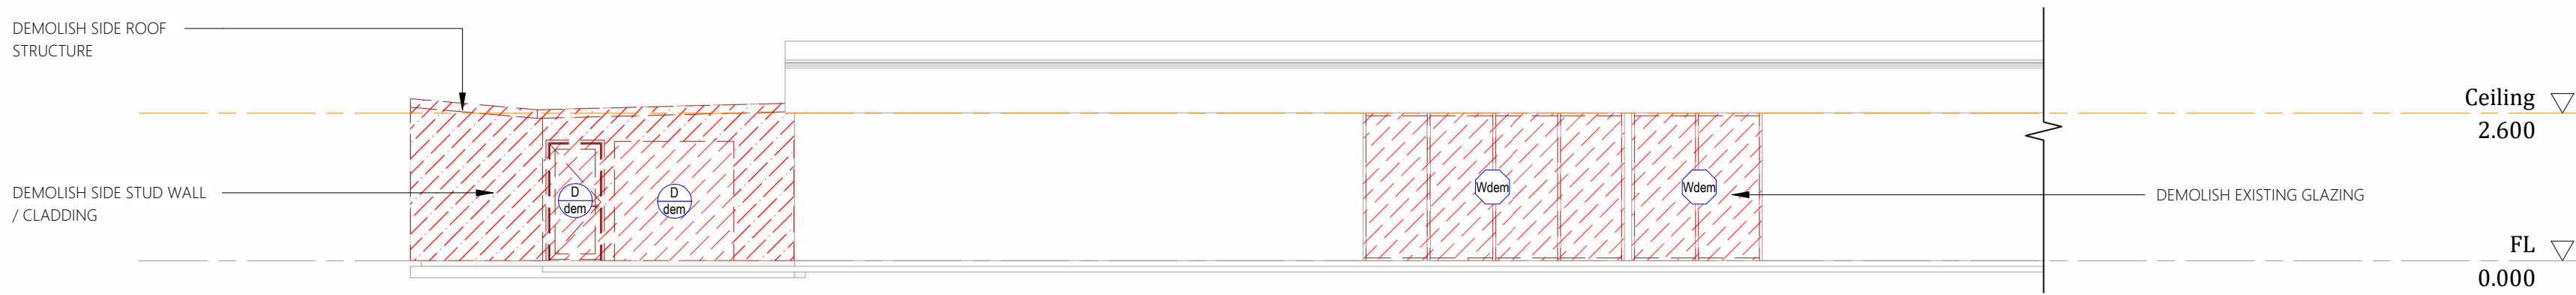

Existing Elevation 3
1 : 100

REVISIONS		
Rev	Description	Date
T1	TENDER ISSUE	12.03.2026

DO NOT SCALE THIS DRAWINGS

KEYNOTE LEGEND

- (e) Existing
- dem Demolish
- (R) Remove / Reinstate

- BSN Basin
- COL Column
- CON Condenser
- CPD Cupboard
- CS Cleaners Sink
- CT Cooktop
- DP Downpipe
- DW Dish Washer
- FAP Fire Alarm Panel
- FHR Fire Hose Reel
- FR Fridge (By Client)
- HD Hand Driver (Air Blade)
- L Locker
- OV Oven
- RH Range Hood
- DW Dish Washer
- SK Sink
- SB Switch Board
- UR Urinal

TENDER ISSUE

Client



Project Details
REGISTRY REFURBISHMENT

Address
STANWELL POWER STATION

Drawing Title
PROPOSED FLOOR & SLAB PLAN



BUILDING DESIGNERS

0483 988 655 **M**
info@dezi nelements.com.au **E**



QBCC No: 1247120 BDAQ No: 0001677

Scale: 1 : 100 Rev:
Date: MARCH 2026 **T1**
Drawn: NJB

Project No: Drawing No:

25_003 A1-300


12/03/2026 6:31:51 PM

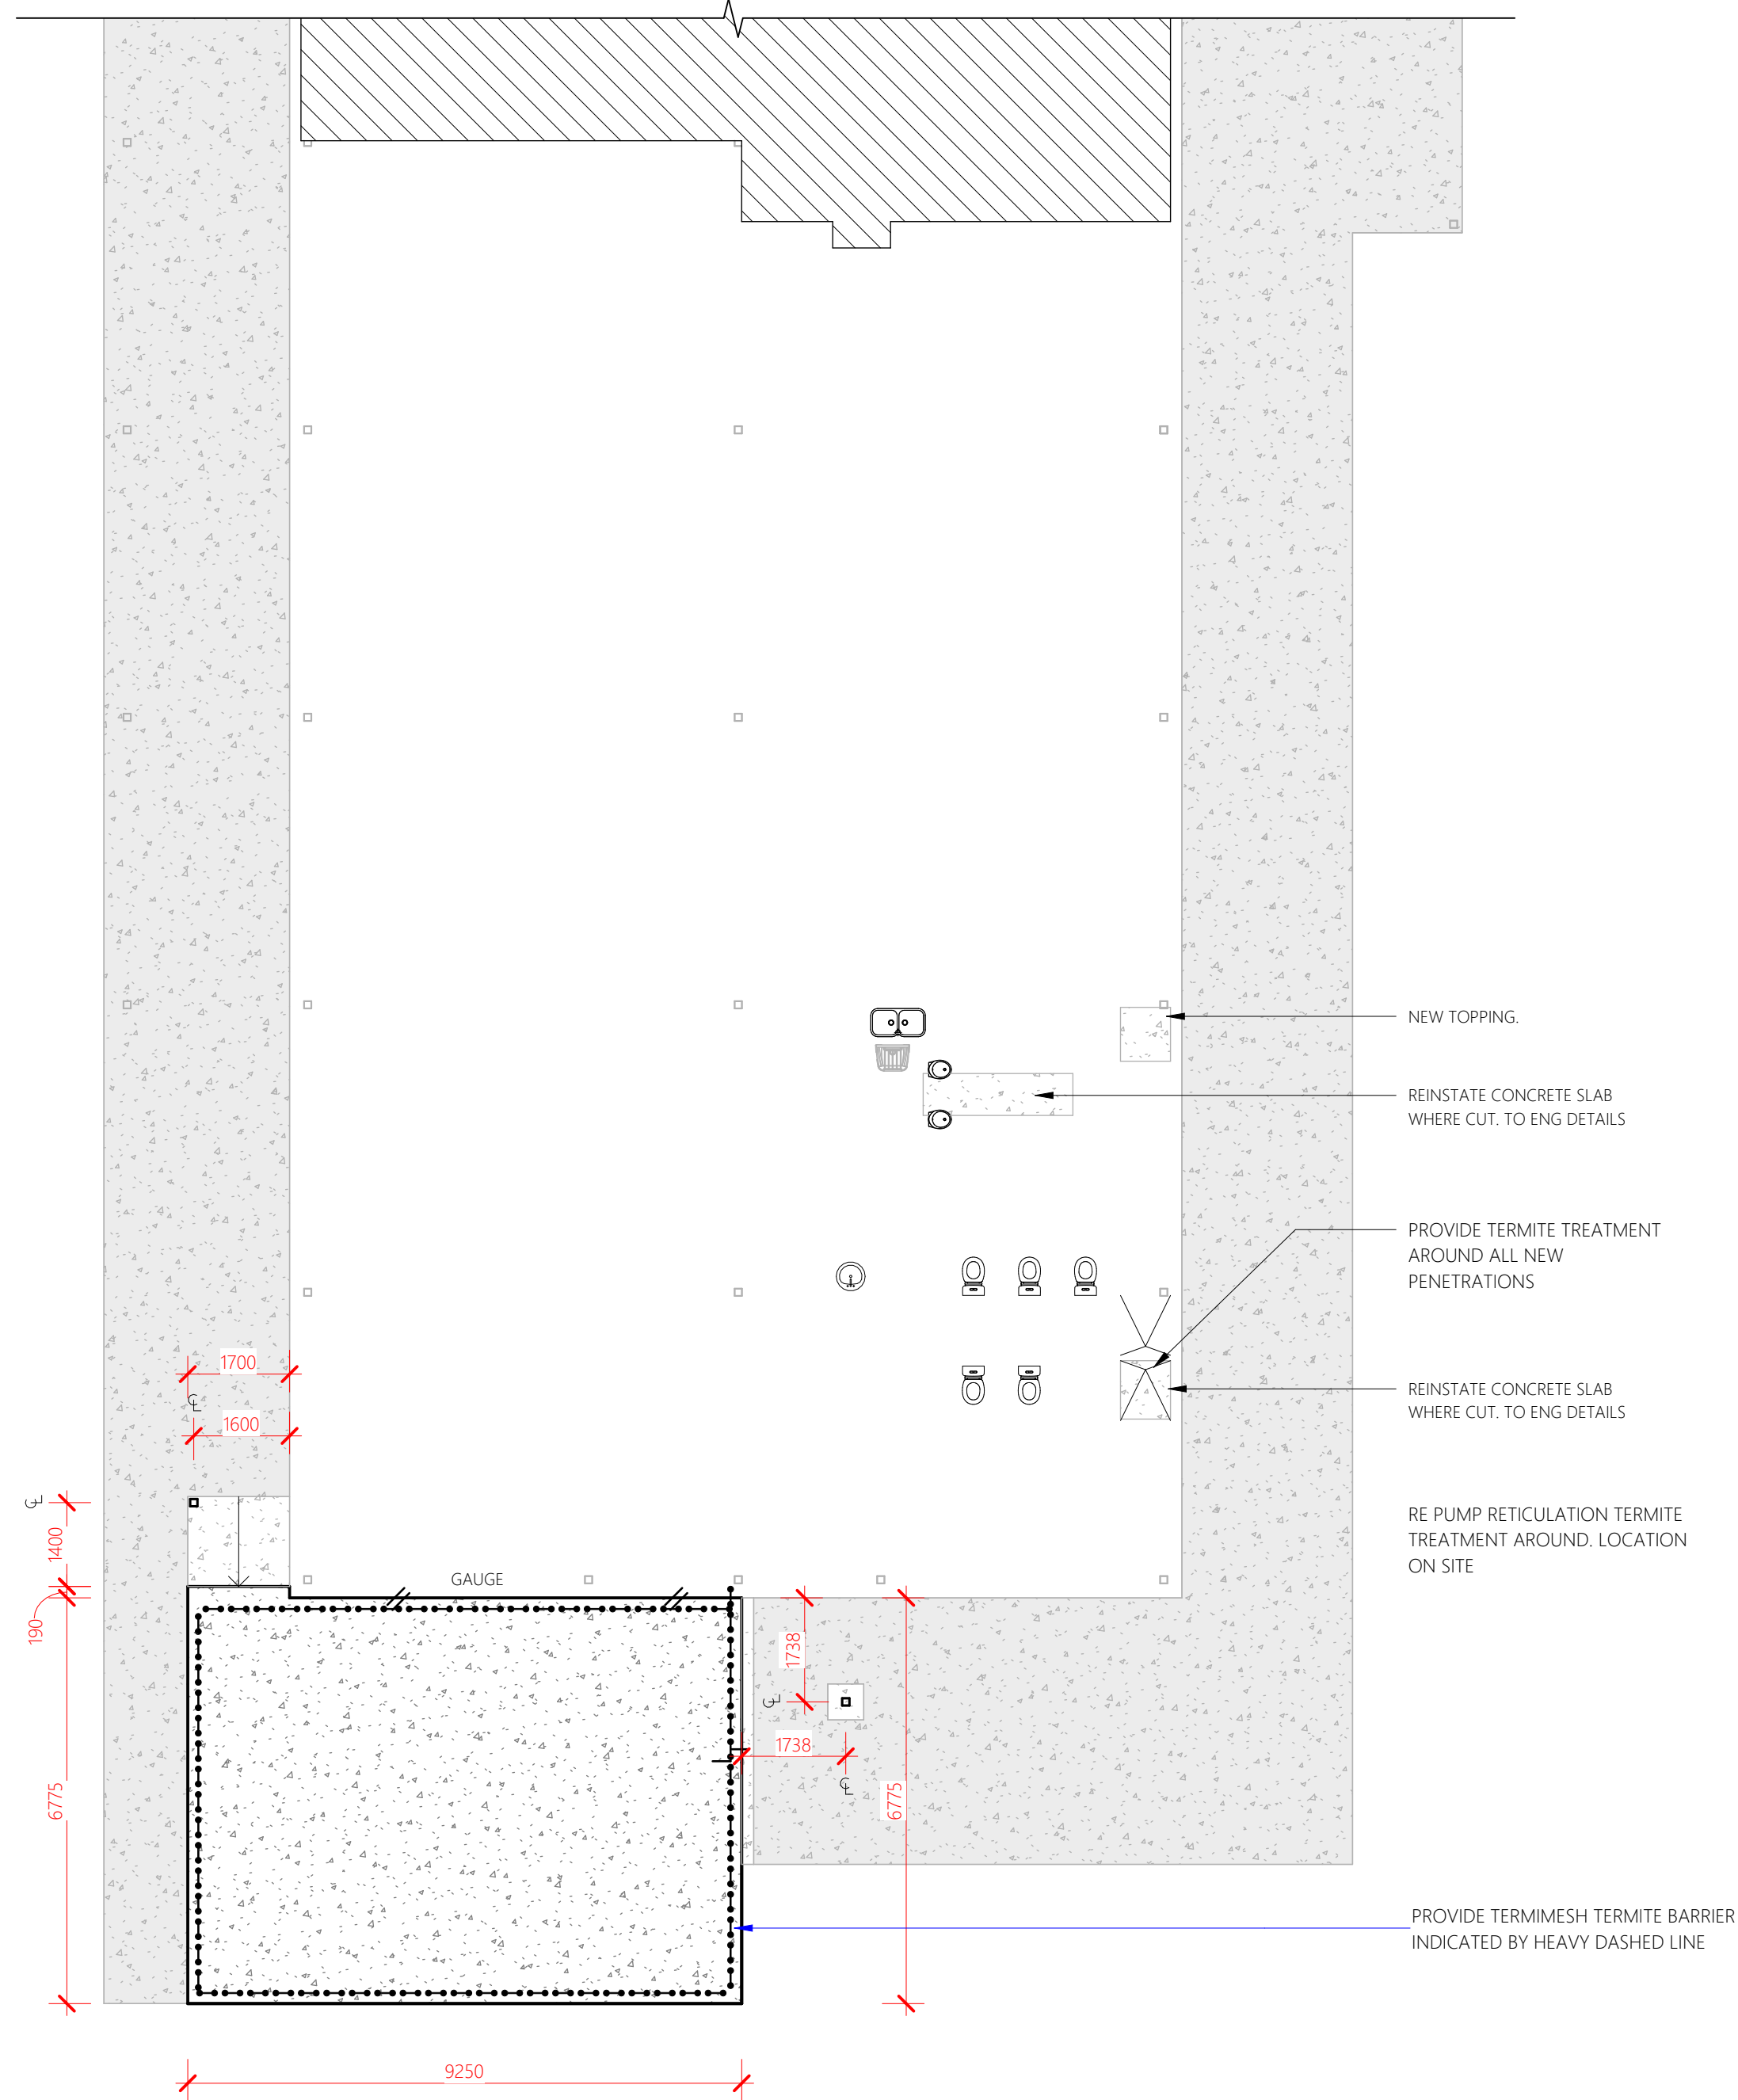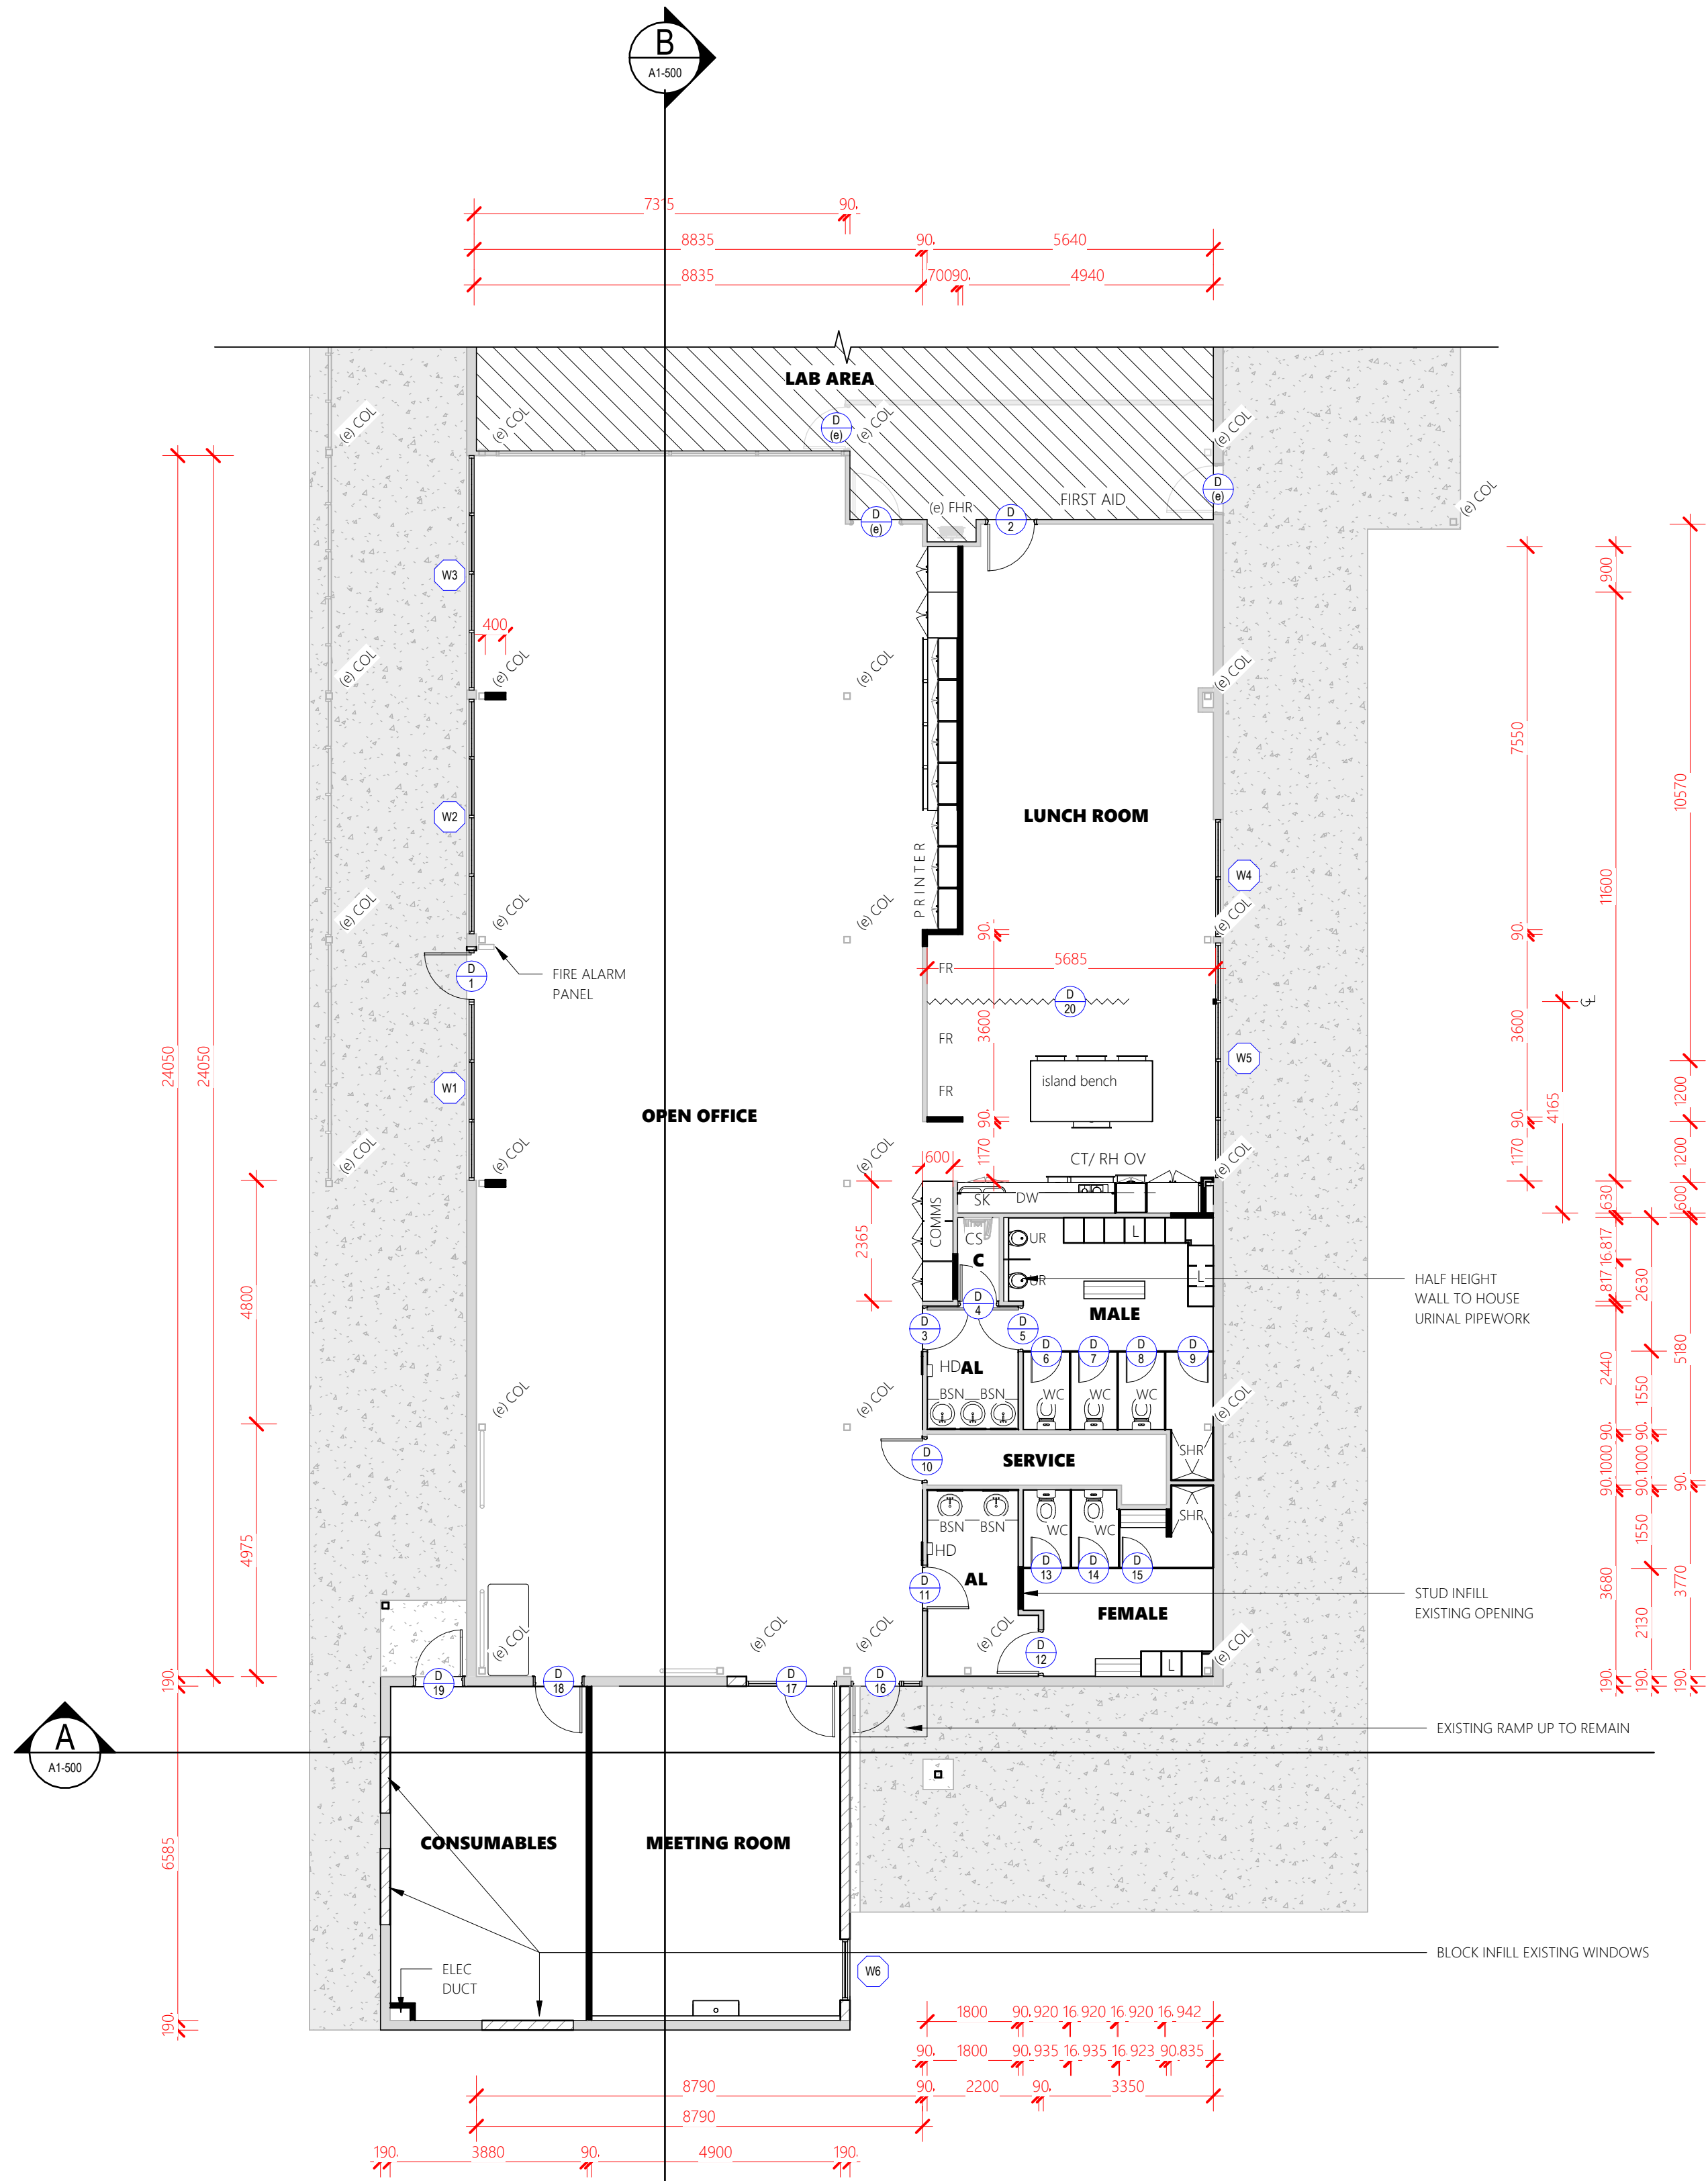


CONFIRM EXISTING GRID SETOUT ON SITE

NEW CEILING INSULATION THROUGHOUT
SHADED AREA - REFER SPEC


- CEILING LEGEND
- 1200 x 600 APEX ACOUSTIC CEILING TILES (OR APPROVED EQUAL. NEW TILES THROUGH RENOVATED AREA)
 - PROVIDE CONCEALED FIX RIBBEDTRIMDEK SOFFIT SHEETING (TO MATCH EXISTING)
 - INSULATION ABOVE CEILING TILES

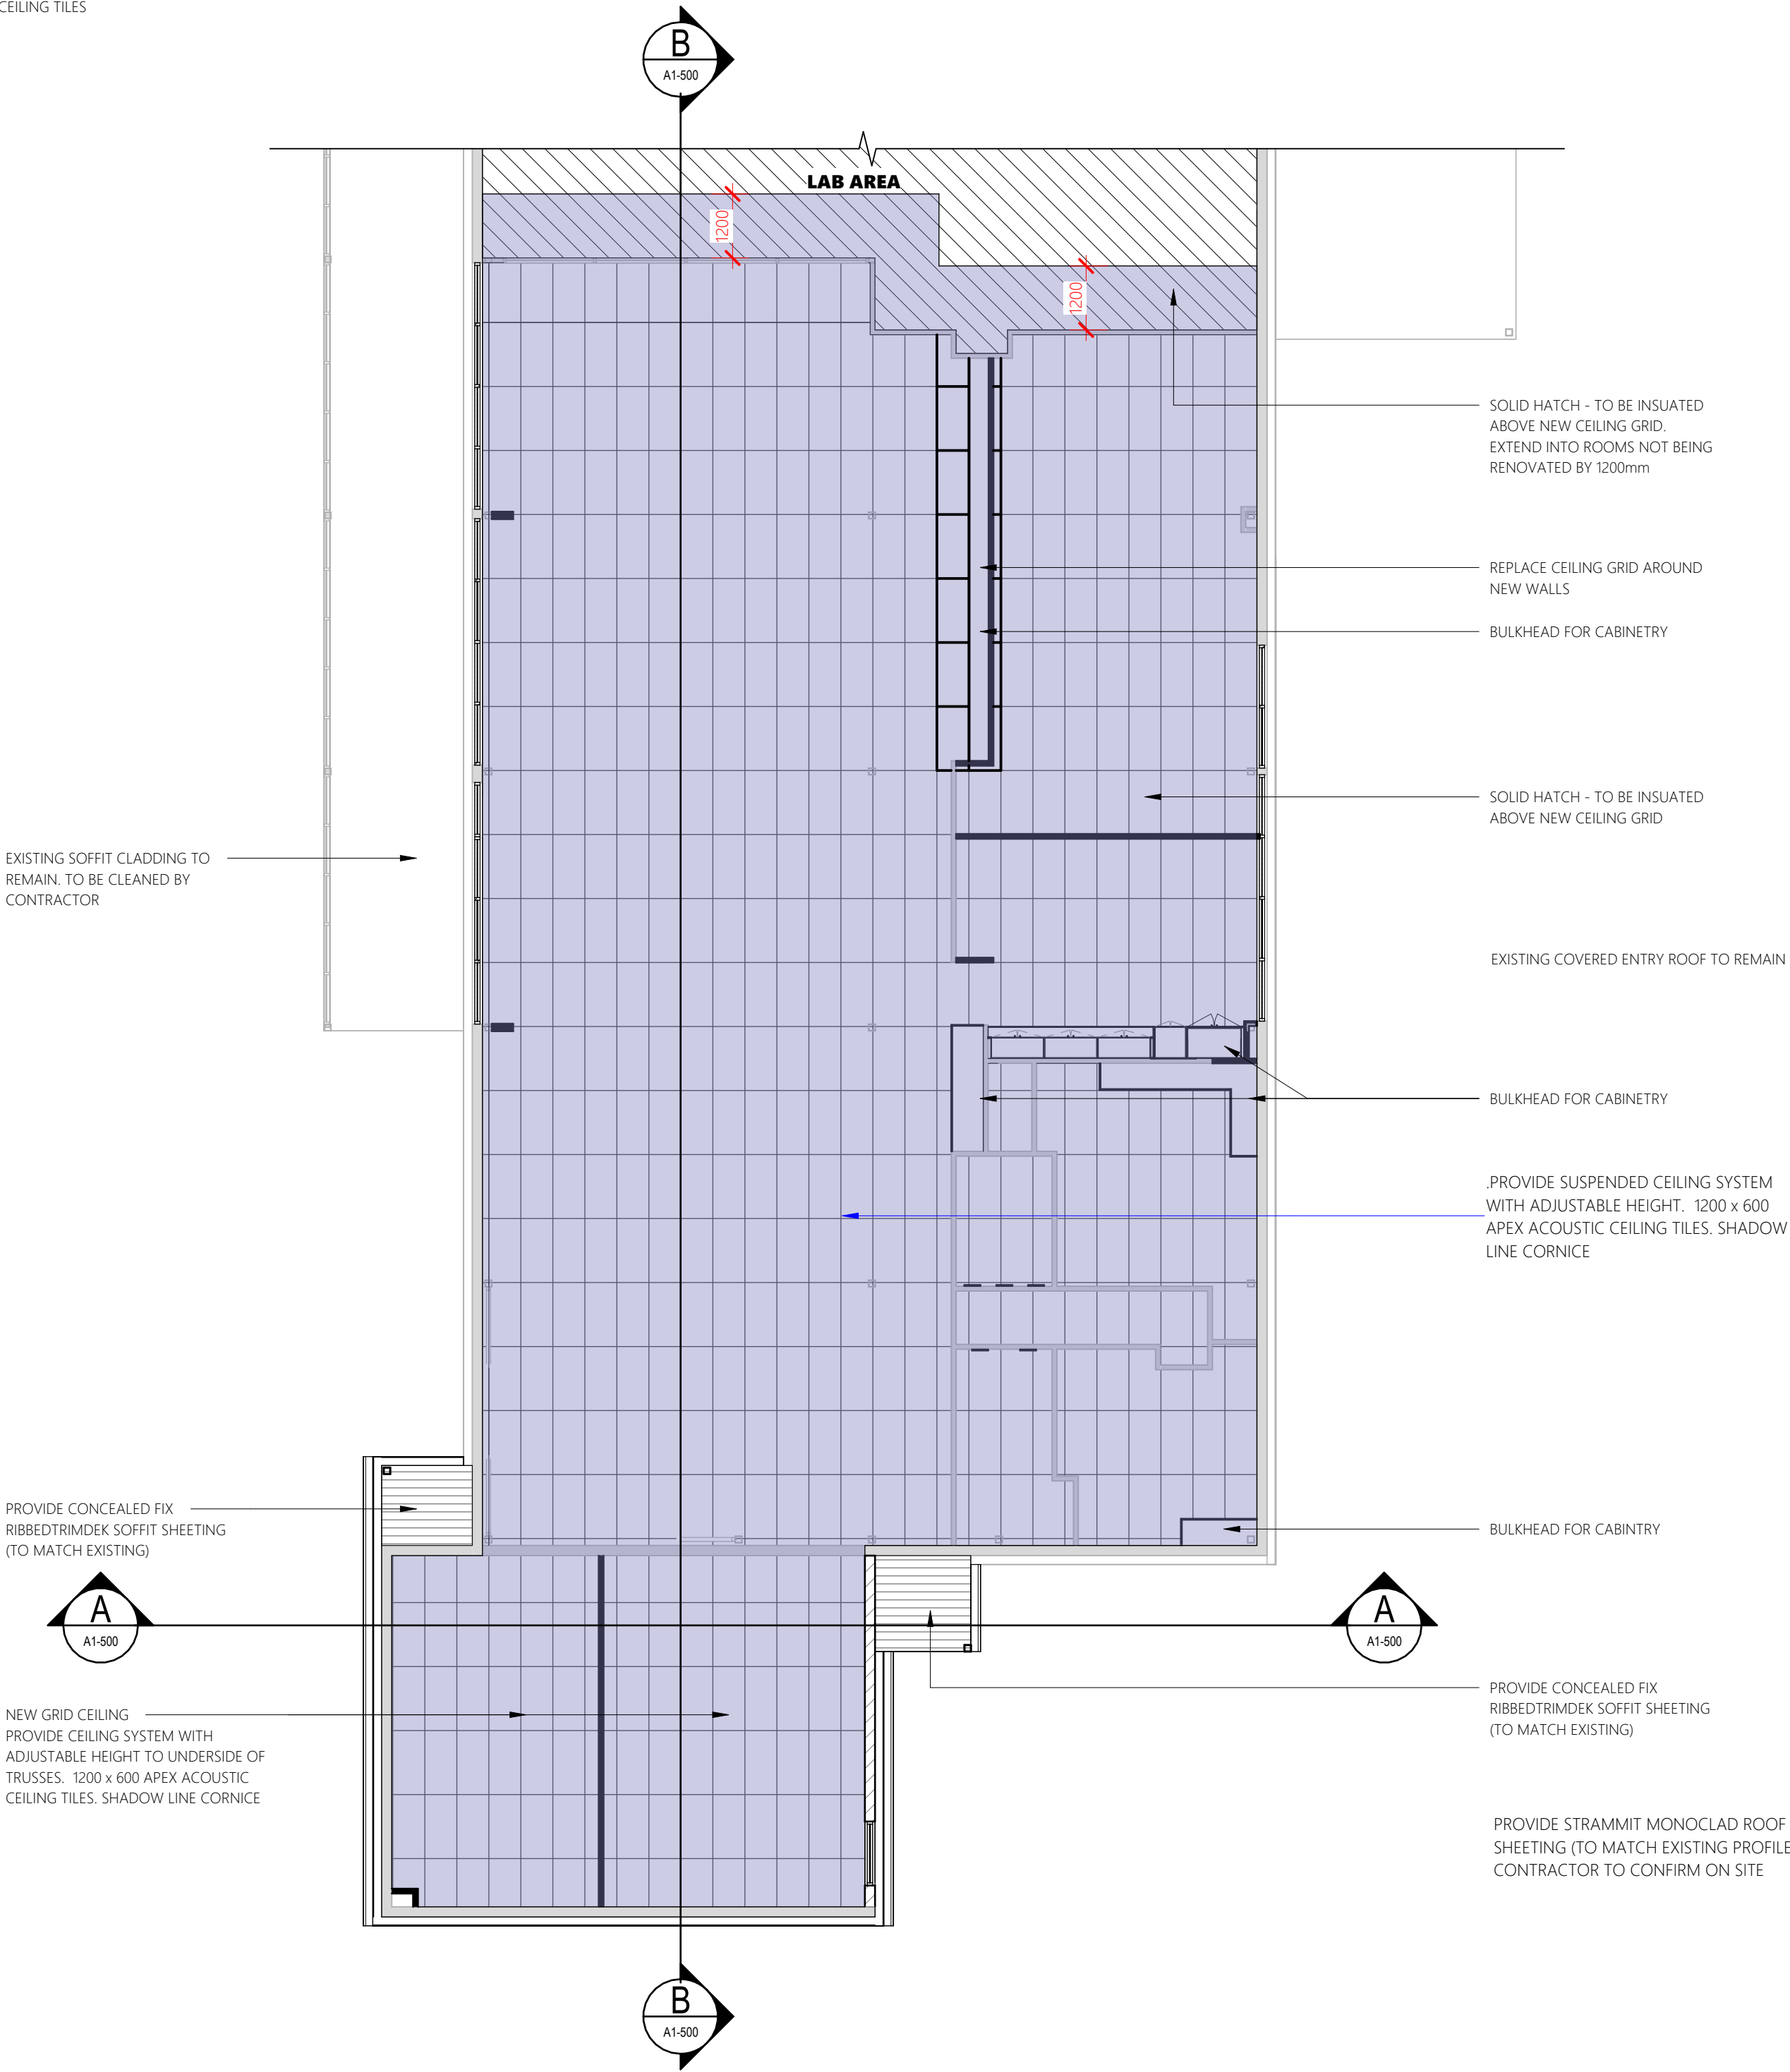


Proposed Ceiling Plan

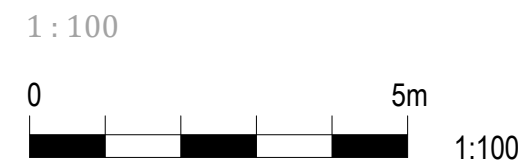

CONFIRM EXISTING ROOF PITCH ON SITE

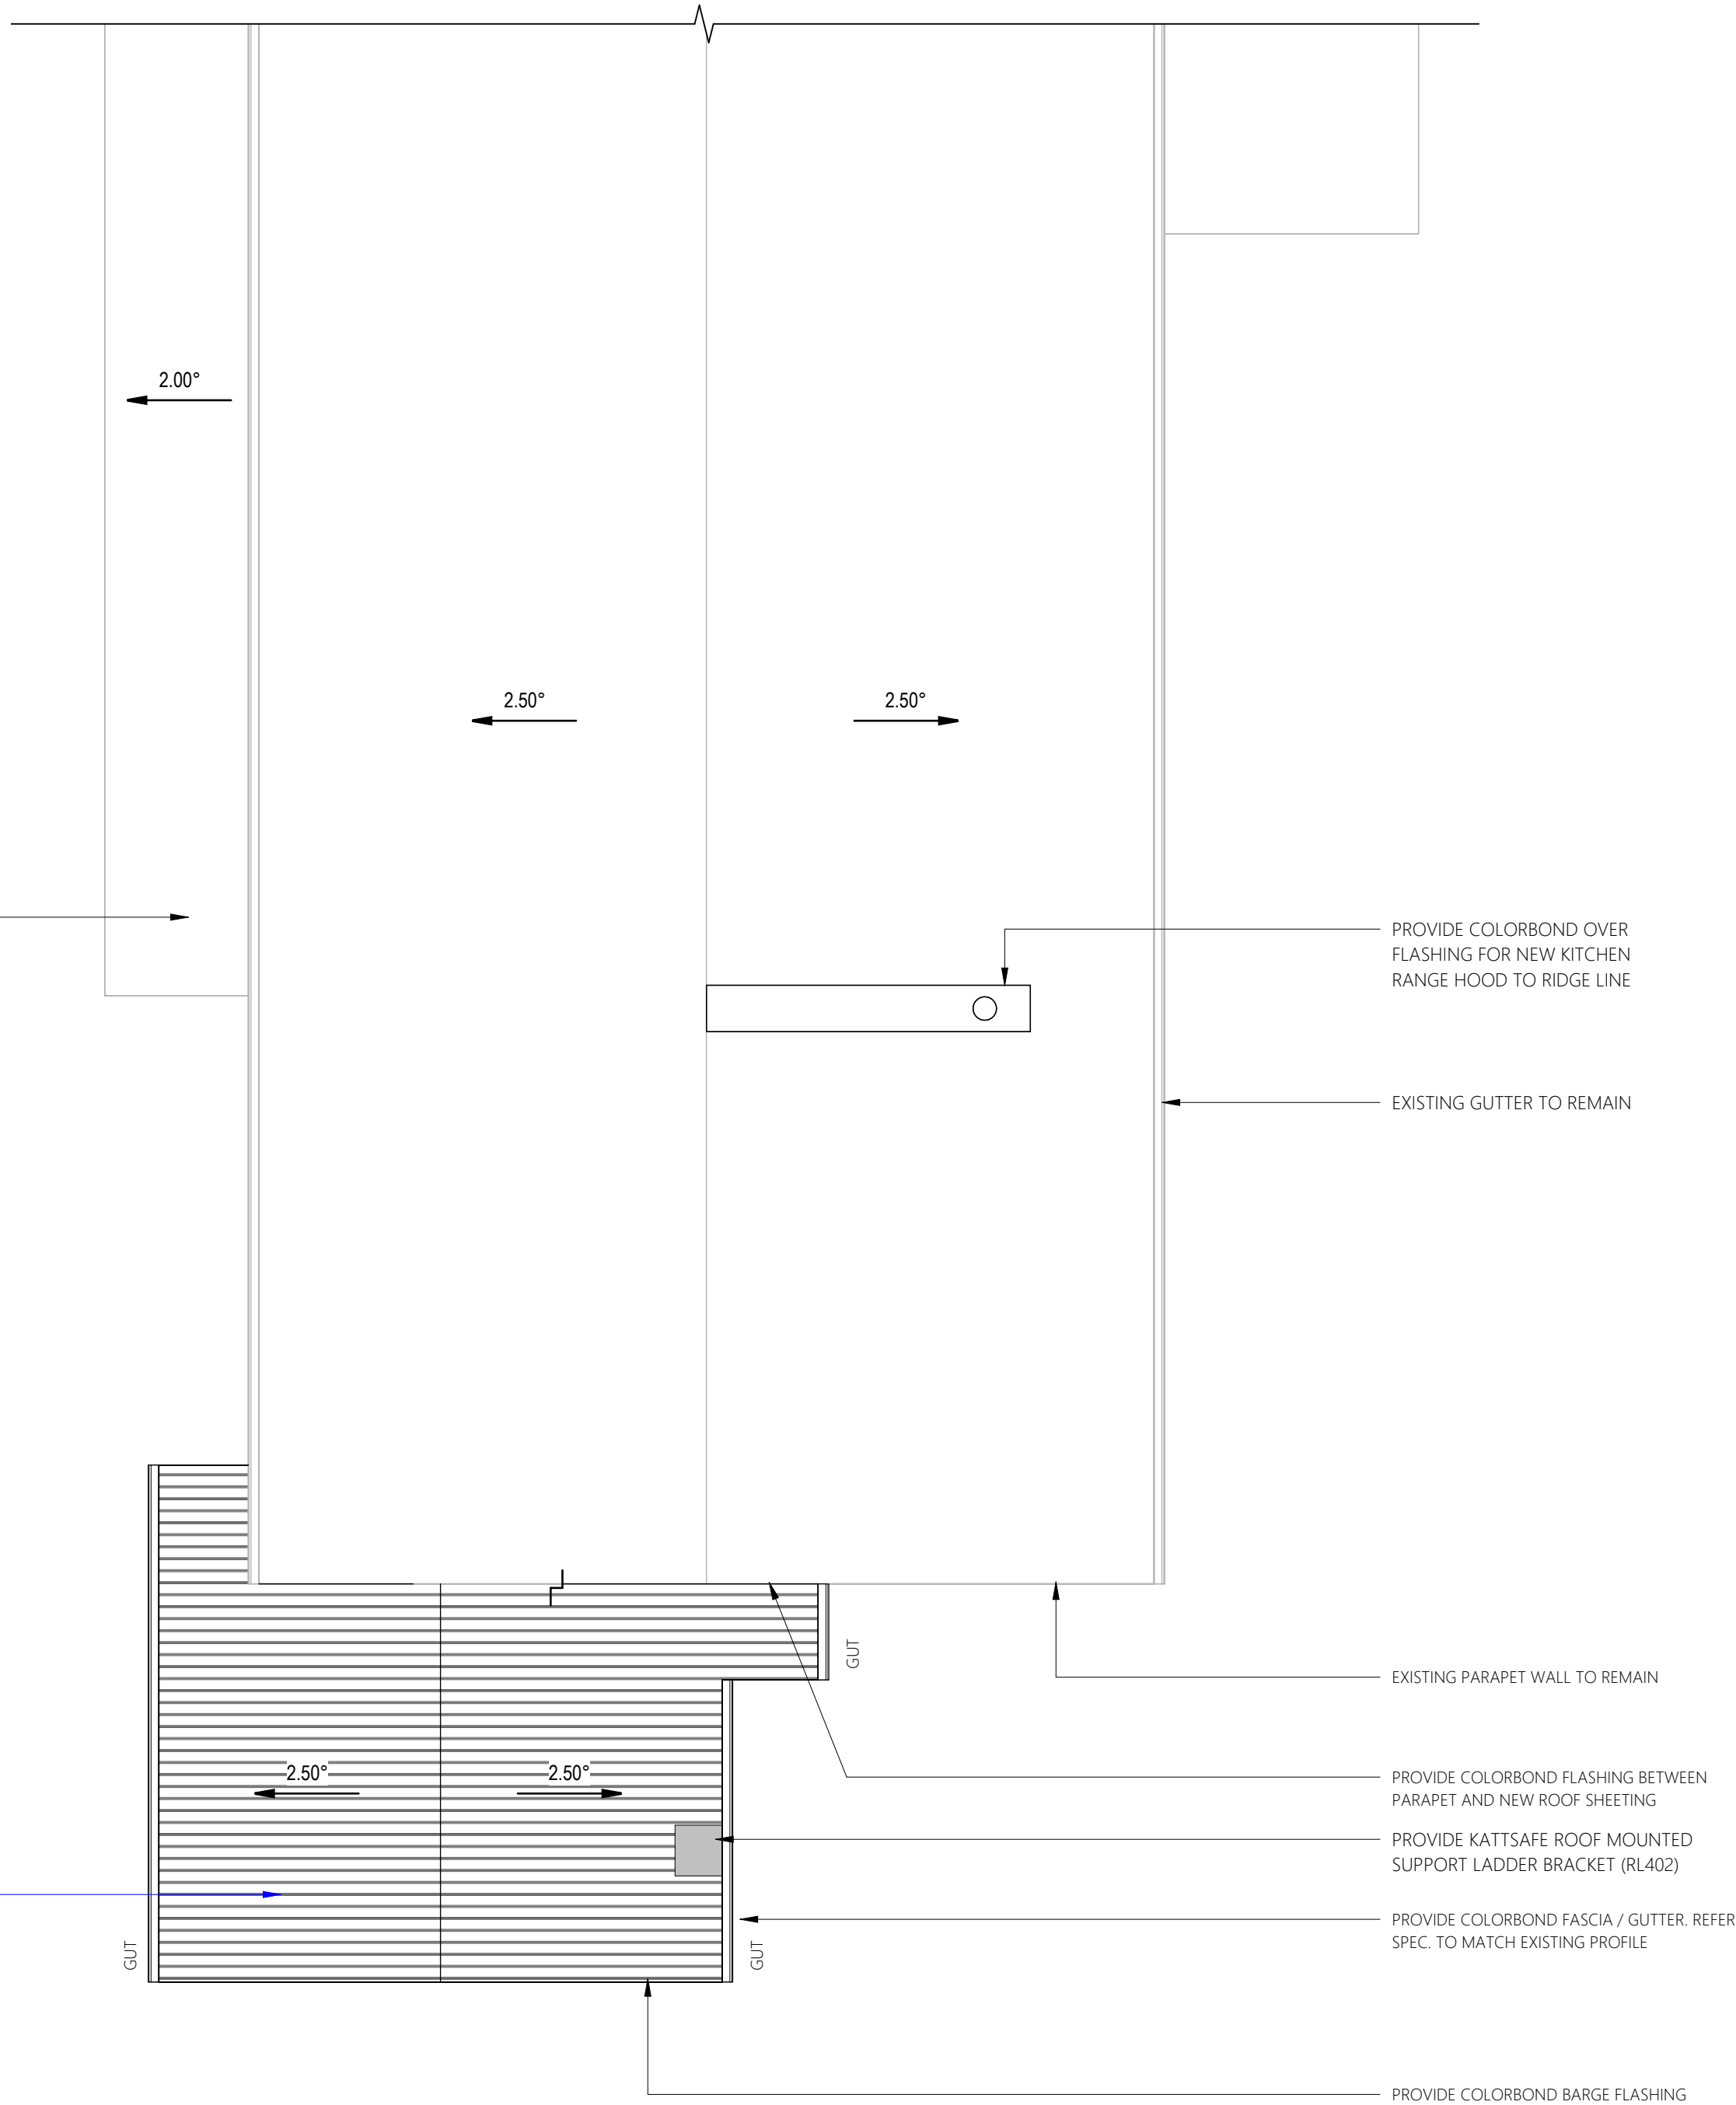

Proposed Roof Plan

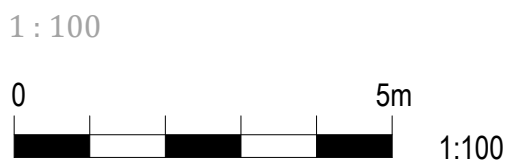

REVISIONS		
Rev	Description	Date
T1	TENDER ISSUE	12.03.2026

DO NOT SCALE THIS DRAWINGS



TENDER ISSUE

Client

Project Details

REGISTRY REFURBISHMENT

Address

STANWELL POWER STATION

Drawing Title

PROPOSED CEILING & ROOF

0483 988 655 **M**

info@designelements.com.au **E**

QBCC No: 1247120 BDAQ No: 0001677


Scale: 1 : 100 Rev: **T1**


Date: MARCH 2026

Drawn: NJB


Project No: Drawing No:

25_003 A1-301

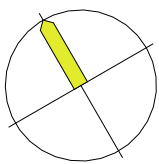


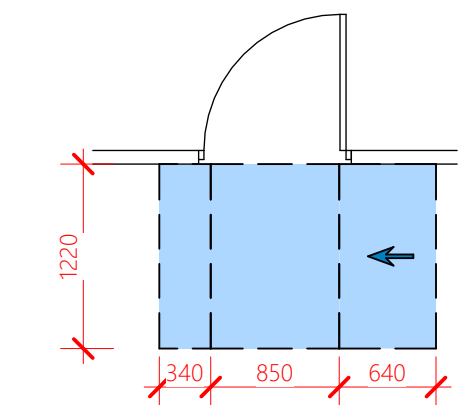


HINGE-SIDE APPROACH
DOOR OPENS AWAY FROM USER

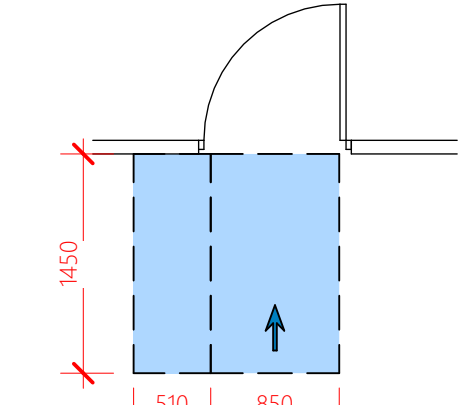


FRONT APPROACH
DOOR OPENS AWAY FROM USER

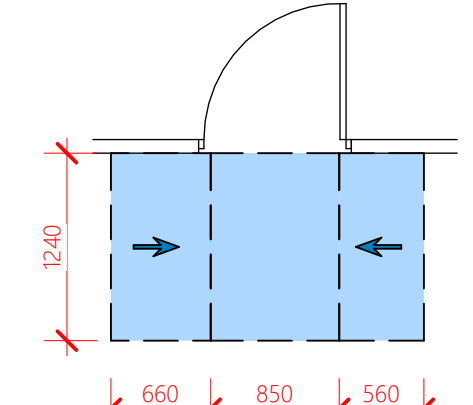


EITHER SIDE APPROACH
DOOR OPENS AWAY FROM USER

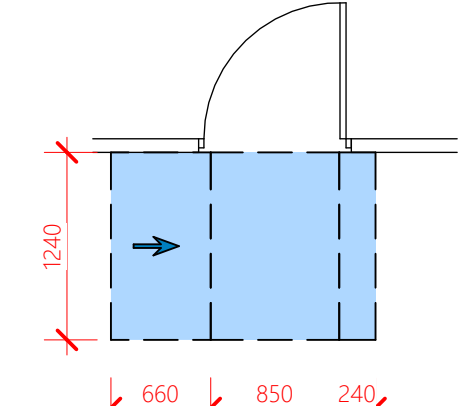


LATCH APPROACH
DOOR OPENS AWAY FROM USER

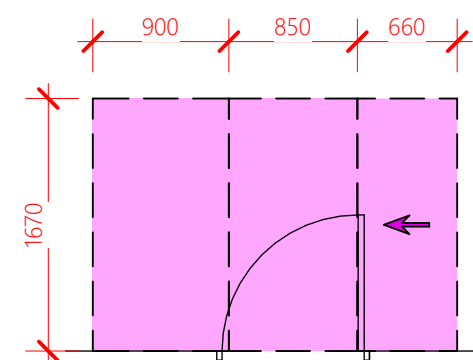


HINGE-SIDE APPROACH
DOOR OPENS TOWARDS USER

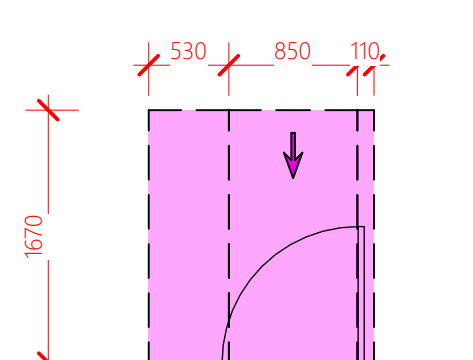


FRONT APPROACH
DOOR OPENS TOWARDS USER

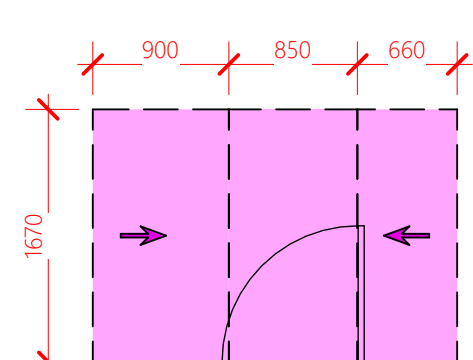

EITHER-SIDE APPROACH
DOOR OPENS TOWARDS USER

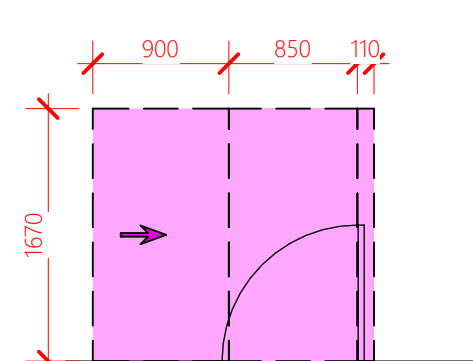


LATCH-SIDE APPROACH
DOOR OPENS TOWARDS USER

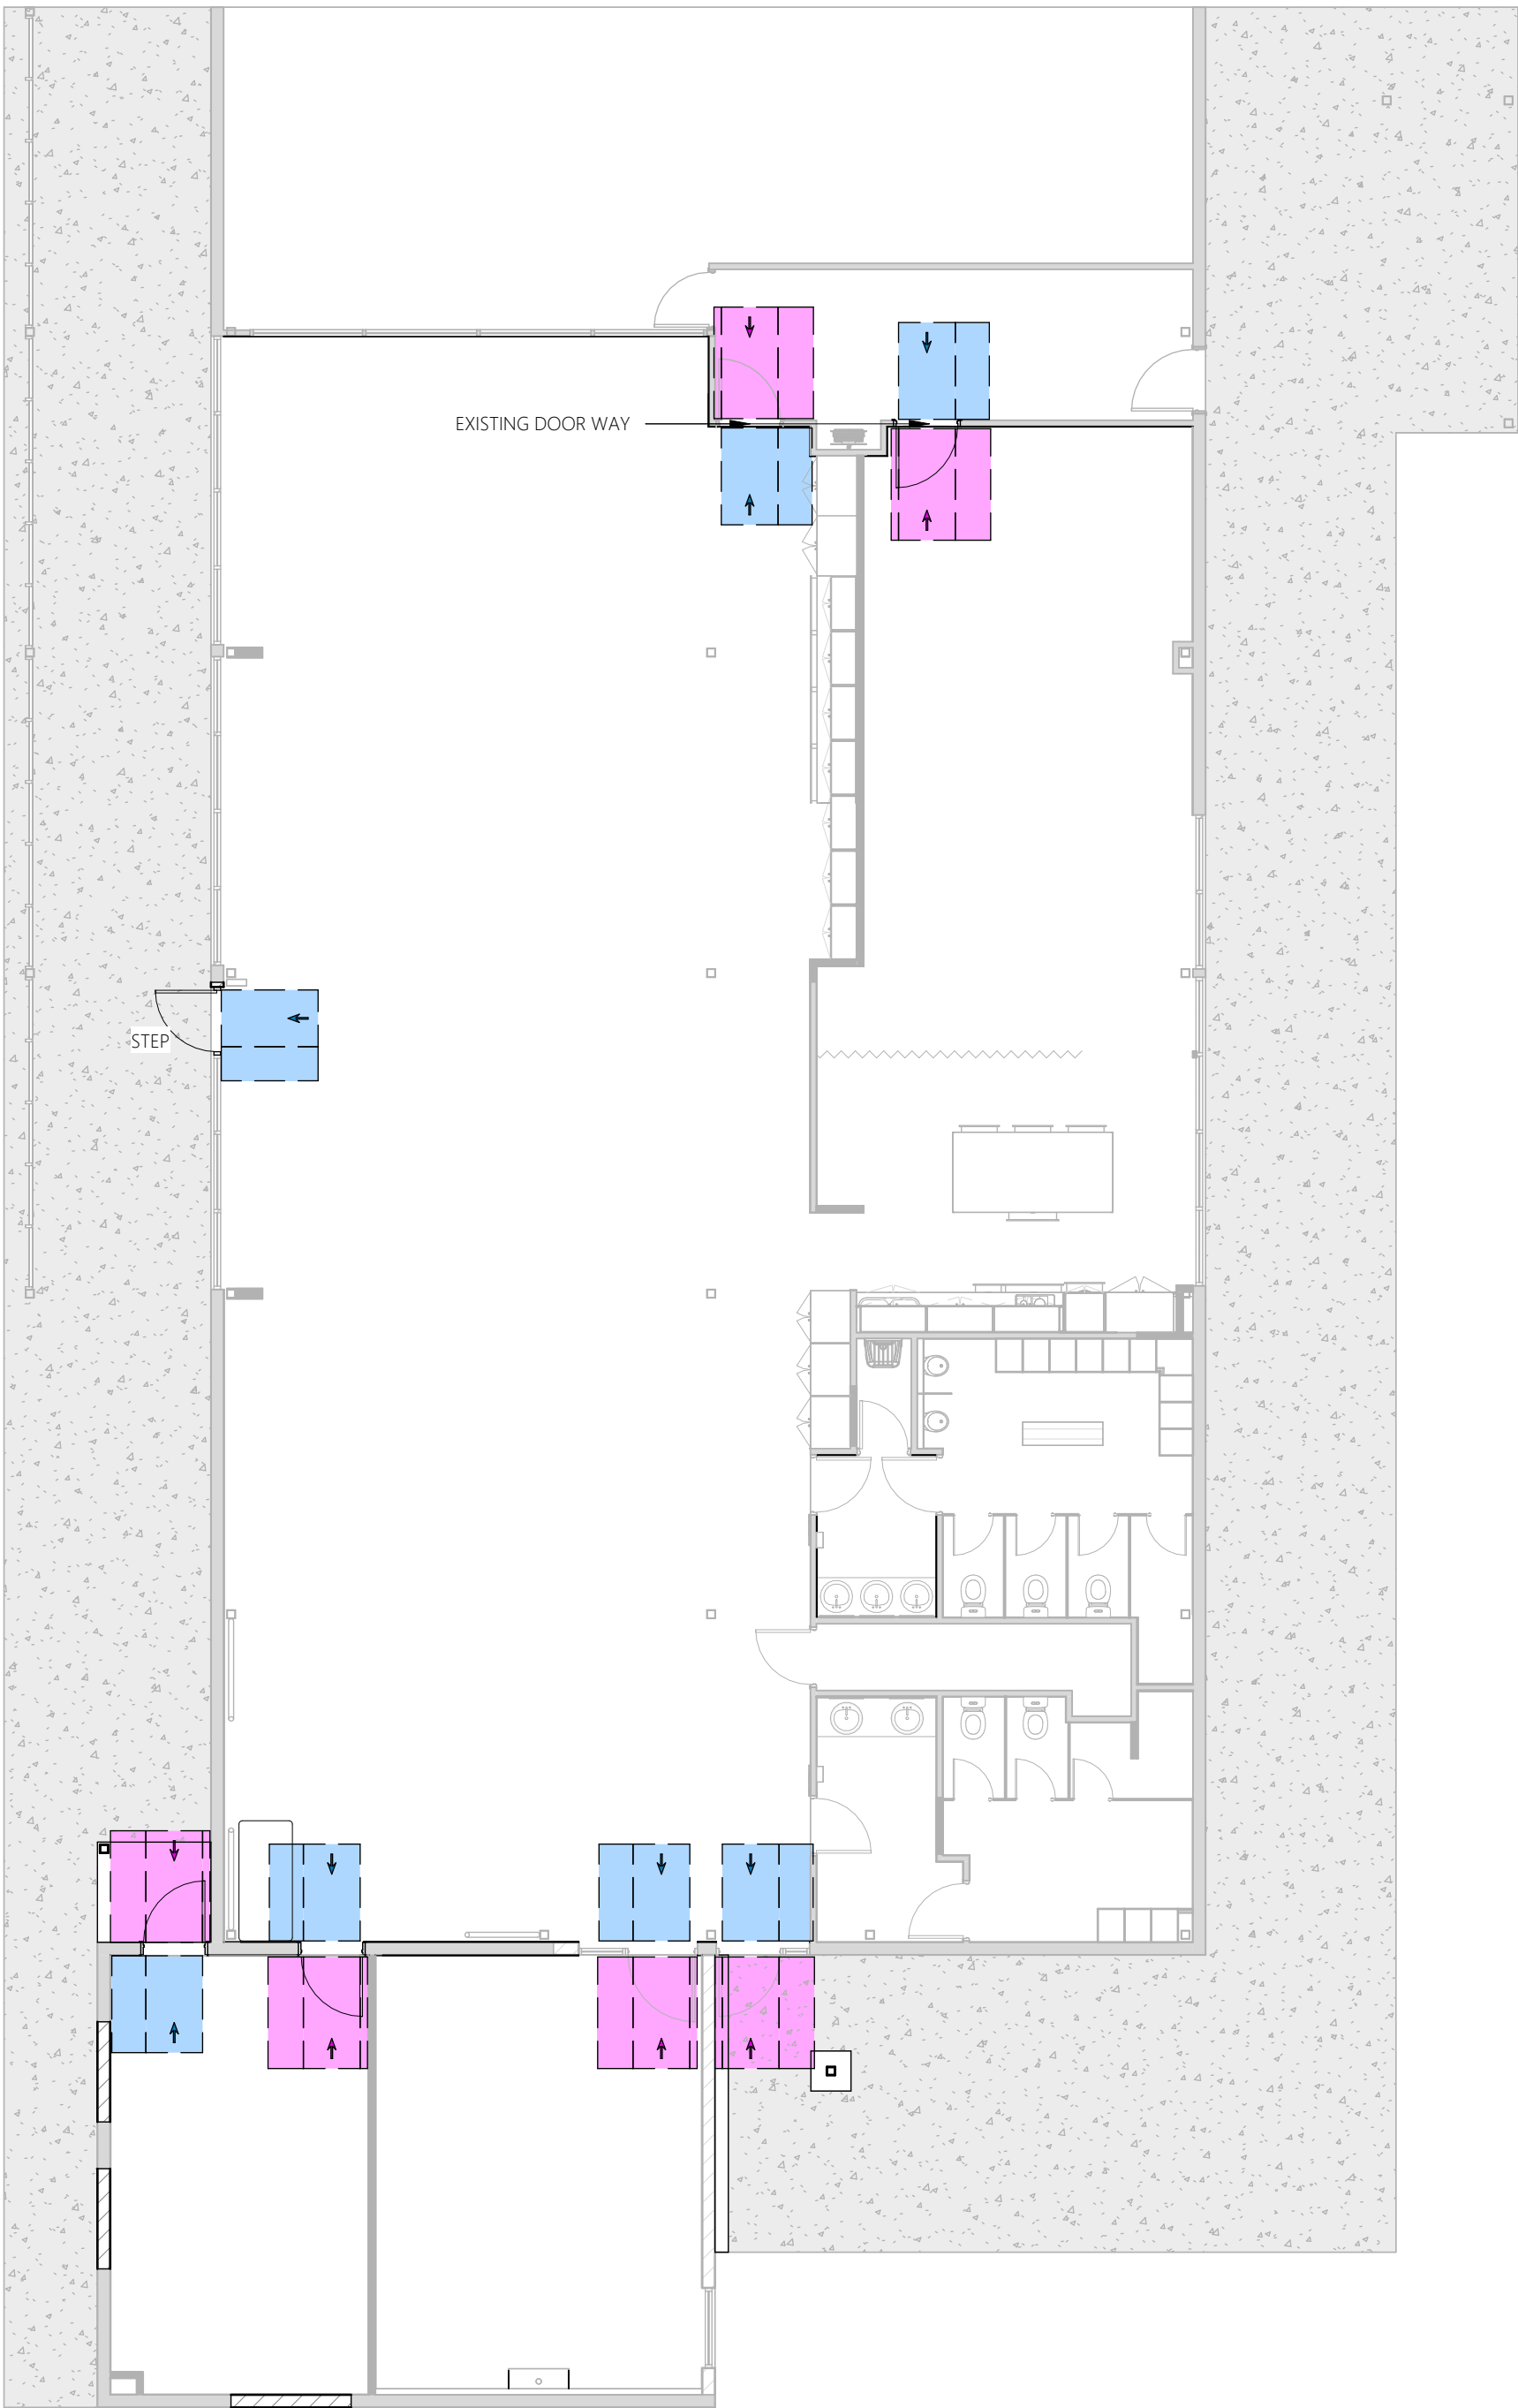

AS1428.1 - Clearance Plan

1 : 100

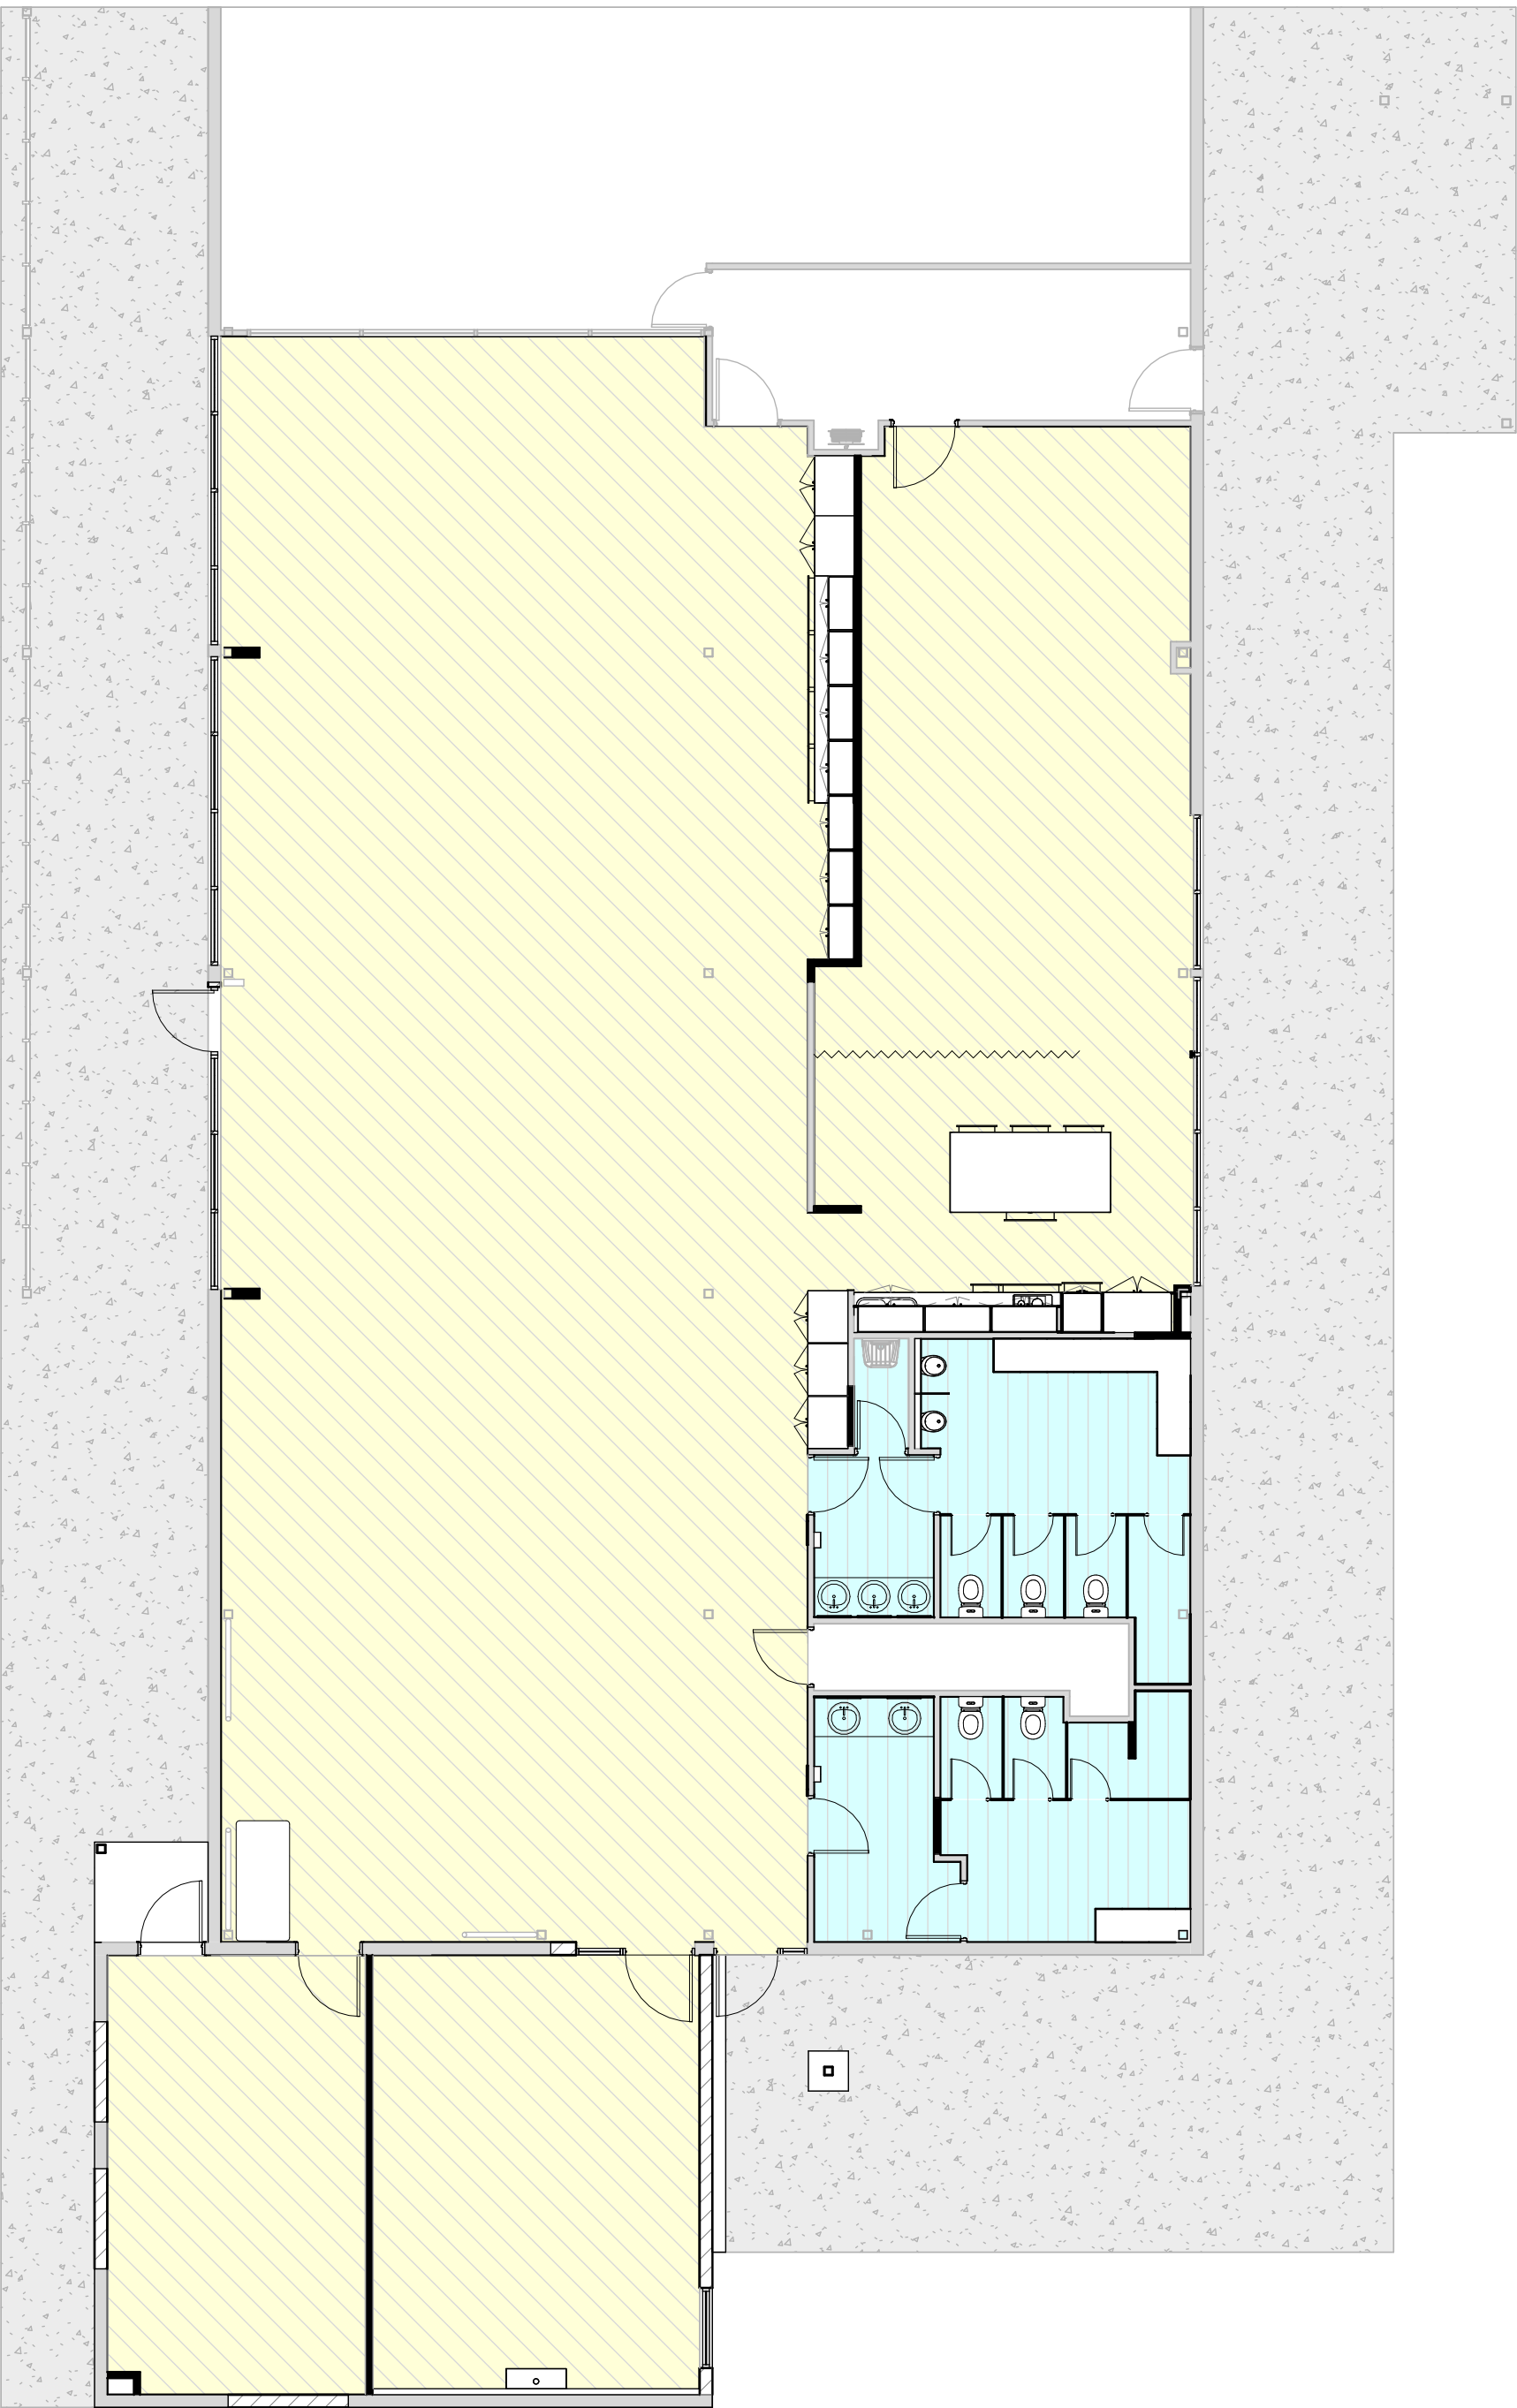

Floor Covering Plan

1 : 100

REVISIONS

Rev	Description	Date
T1	TENDER ISSUE	12.03.2026

DO NOT SCALE THIS DRAWINGS

FLOOR COVERING PLAN

- SHEET VINYL - TYPE 1
100mm FEATHER EDGE SKIRTING - BLACK
- SHEET VINYL - TYPE 2
100mm COVERED UP SKIRTING
- SHEET VINYL - TYPE 3
100mm FEATHER EDGE SKIRTING - BLACK

TENDER ISSUE

Client

Project Details
REGISTRY REFURBISHMENT

Address
STANWELL POWER STATION

Drawing Title
AS1428.1 - CLEARANCE & FLOOR COVERING PLAN

dezi nelements
BUILDING DESIGNERS

0483 988 655

info@dezi nelements.com.au


QBCC No: 1247120 BDAQ No: 0001677

Scale: As indicated Rev: **T1**

Date: MARCH 2026


Drawn: NJB

Project No: **25_003** Drawing No: **A1-302**

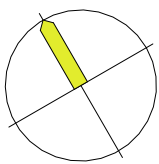


REVISIONS		
Rev	Description	Date
T1	TENDER ISSUE	12.03.2026

DO NOT SCALE THIS DRAWINGS

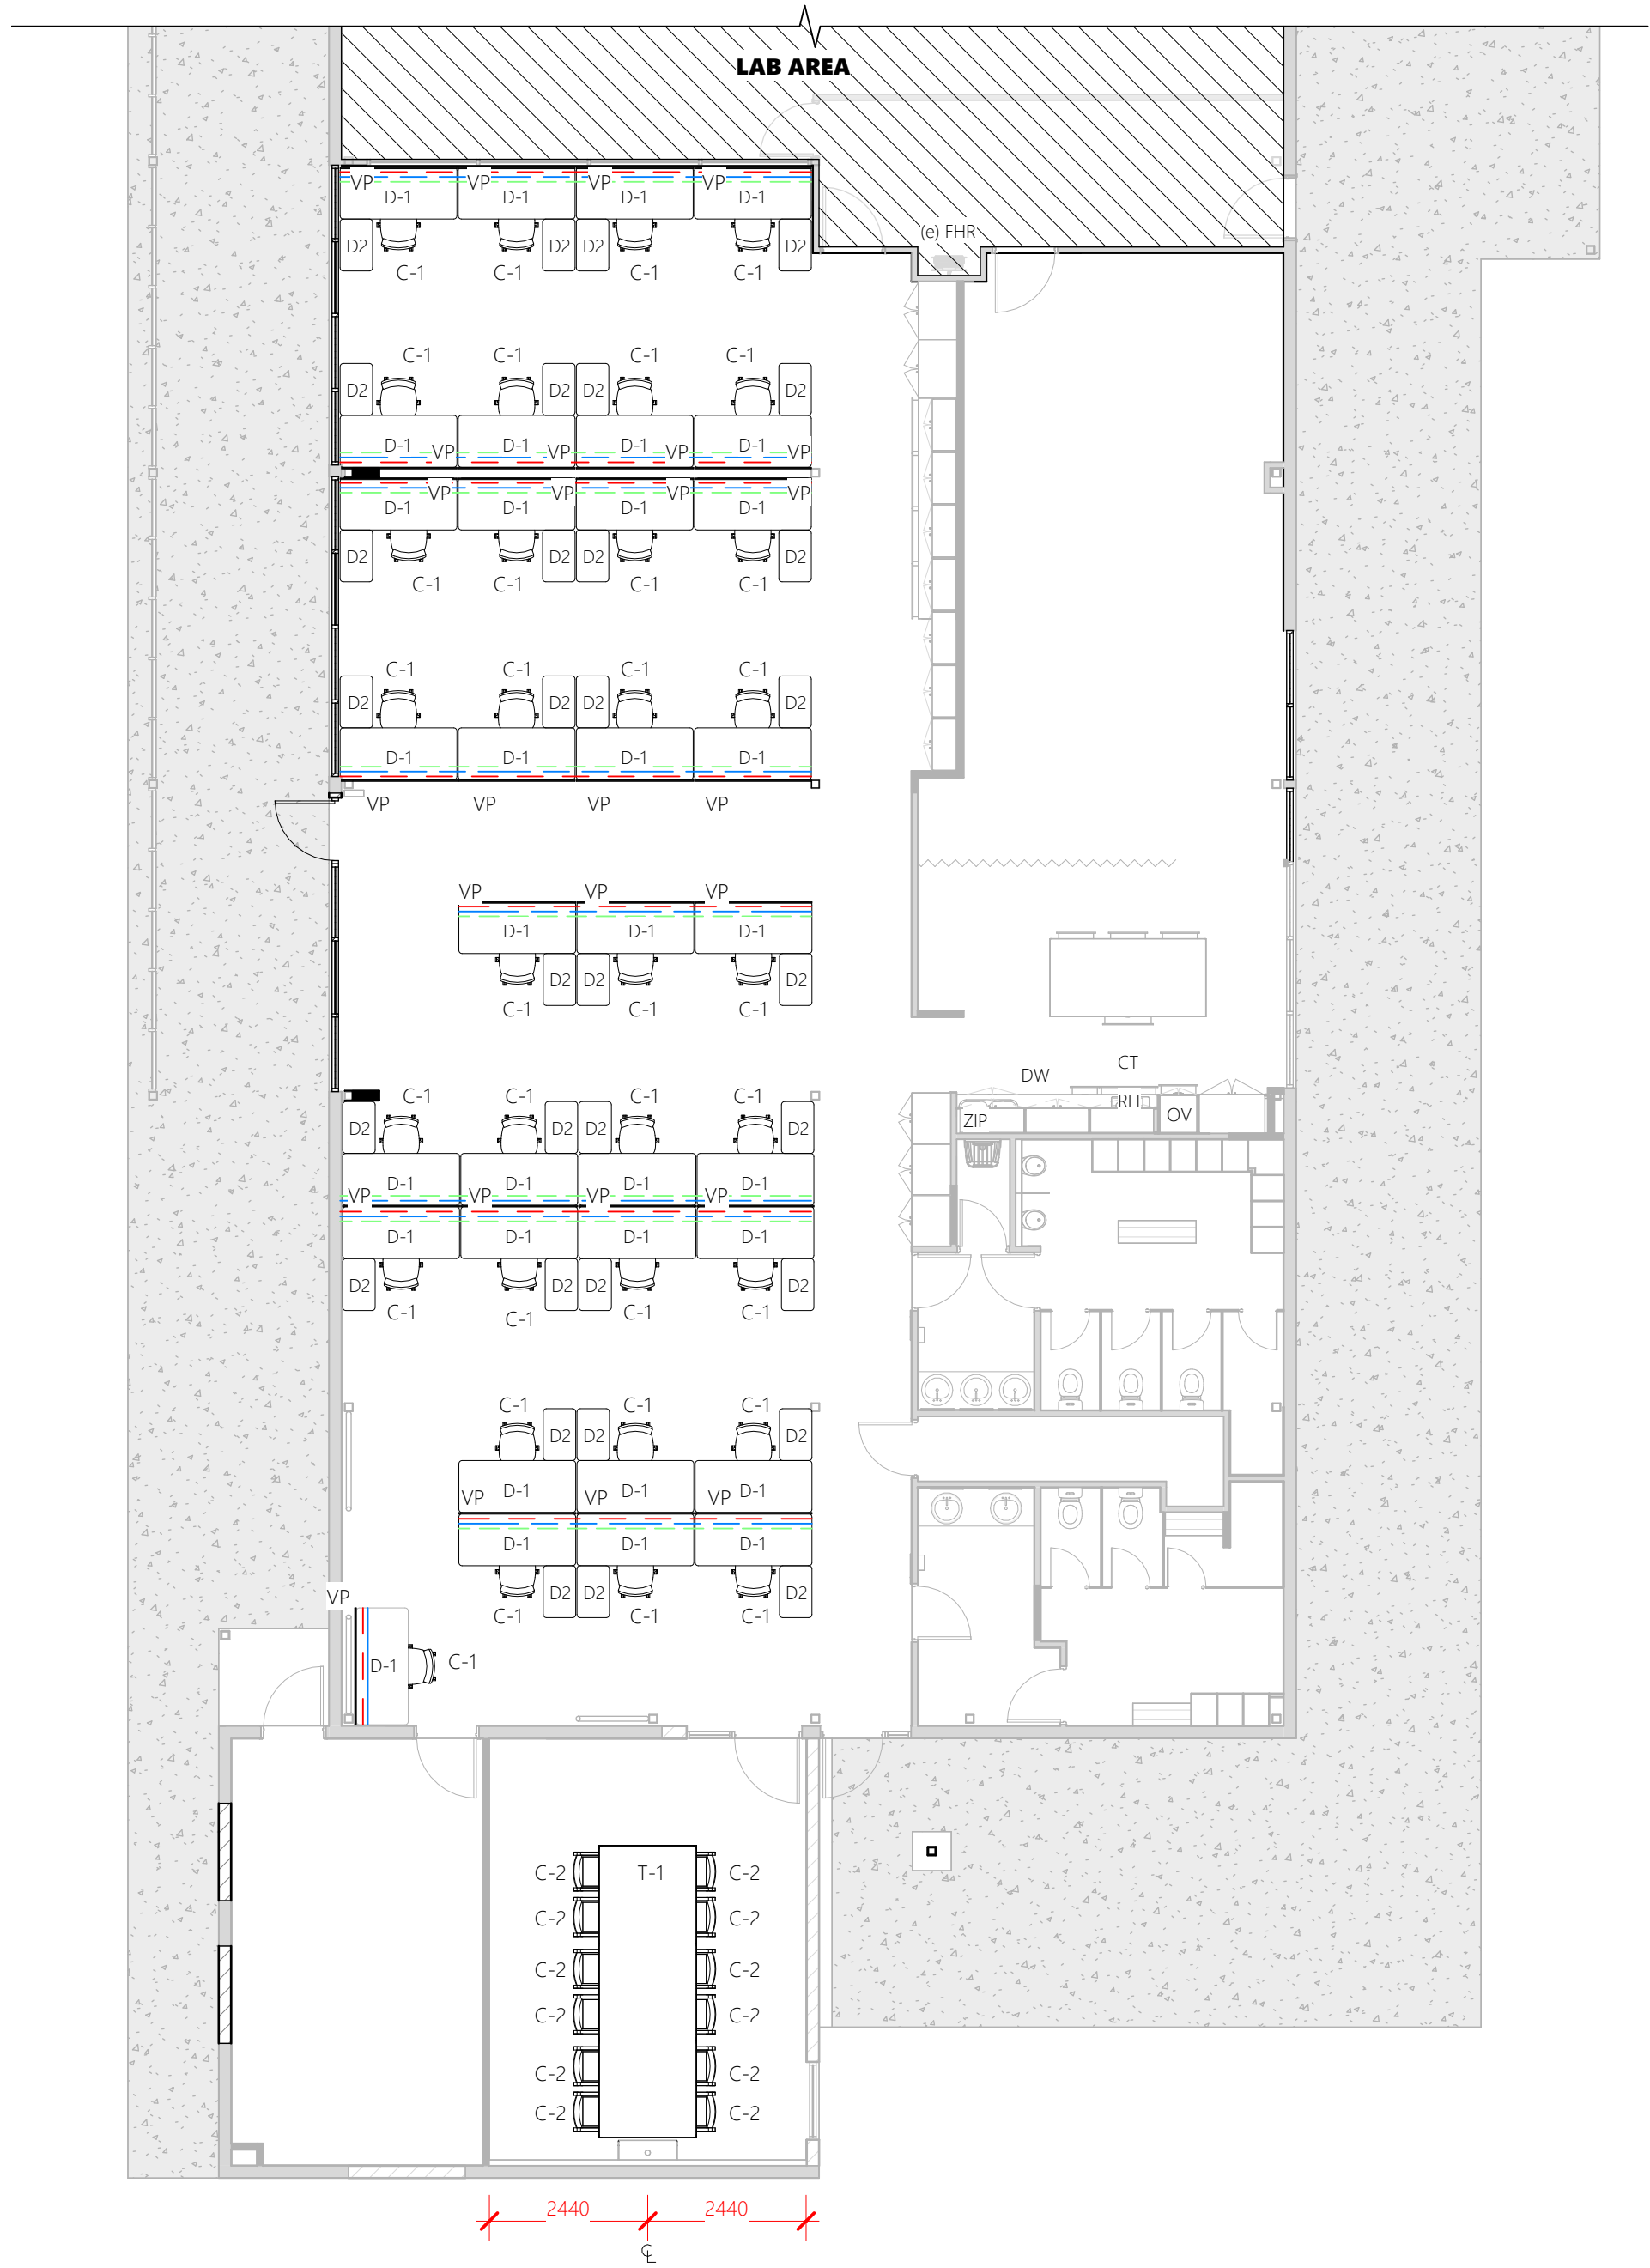

Proposed Furniture Layout

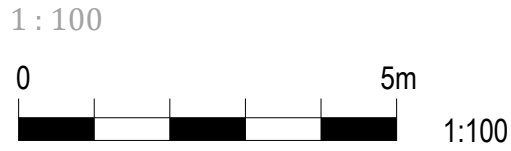

FURNITURE & APPLIANCE SCHEDULE

CODE	TYPE	SIZE	QTY	SUPPLIER
D-1	DESK	1800 x 800	34	SCHIAVELLA CLIMATE RECTANGLE WORK STATION
D-2	DESK	800 x 500	33	SCHIAVELLA CLIMATE RECTANGLE WORK STATION RETURN
C-1	CHAIR (workstation)	-	34	SCHIAVELLA HIGH BACK CHAIR BY OKAMURA, BLACK BODY, BLACK MESH BLACK AND UPHOLSTERED SEAT
C-2	CHAIR (meeting)	-	12	SHIBUSA HIGH BACK BY OKAMURA (BLACK)
T-1	TABLE	1400 x 4400	1	MEETING TABLE EONA - 25mm LAMINEX CHARCOAL NATURAL FINISH WITH ABS EDGING
—	CABLE CATCHER	AS REQUIRED	-	SCHIAVELLA
- -	CABLE ARTICULATOR	AS REQUIRED	-	SCHIAVELLA
- - -	CABLE CHANNEL	AS REQUIRED	-	SCHIAVELLA
VP	VIDE SUSP. PANEL	1800 (600mm ABOVE DESK)	27	SCHIAVELLA - PROVIDE SUSPENDEED BRACKETS TO EACH DESK
OV	OVEN	598 x 596	1	FISHER & PAYKEL 60CM SERIES 7 CONTEMPORARY PYROLYTIC OVEN 9 FUNCTION - BLACK
DW	DISHWASHER	597 x 600	1	FISHER & PAYKEL SERIES 7 CONTEMPORARY DISHWASHER - BLACK STEEL
CT	COOK TOP	600	1	FISHER & PAYKEL 60CM SERIES 7 4 ZONE INDUCTION COOKTOP 2 SMARTZONES - BLACK
RH	RANGE HOOD	600	1	FISHER & PAYKEL 60CM SERIES 7 INTEGRATED INSERT WALL RANGEHOOD EXTERNAL MOTOR - STEEL GLASS
ZIP	ZIP UNIT	-	1	HYDROTAP G5 BCSHA100 5-IN-1 CLASSIC TAP WITH CLASSIC MIXER BLACK

TENDER ISSUE




Project Details
REGISTRY REFURBISHMENT
Address
STANWELL POWER STATION
Drawing Title
FURNITURE LAYOUT



0483 988 655 M
info@dezignelements.com.au E
QBCC No: 1247120 BDAQ No: 0001677

Scale: 1 : 100	Rev:
Date: MARCH 2026	T1
Drawn: NJB	
Project No: 25_003	Drawing No: A1-303

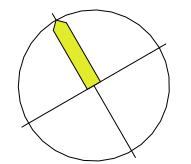

REVISIONS		
Rev	Description	Date
T1	TENDER ISSUE	12.03.2026

DO NOT SCALE THIS DRAWINGS



TENDER ISSUE

Client



Project Details

REGISTRY REFURBISHMENT

Address

STANWELL POWER STATION


Drawing Title

PROPOSED ELEVATION




0483 988 655 
info@dezi elements.com.au 
QBCC No: 1247120 BDAQ No: 0001677


Scale: 1 : 100 Rev: **T1**
Date: MARCH 2026
Drawn: NJB
Project No: Drawing No:
25_003 A1-400

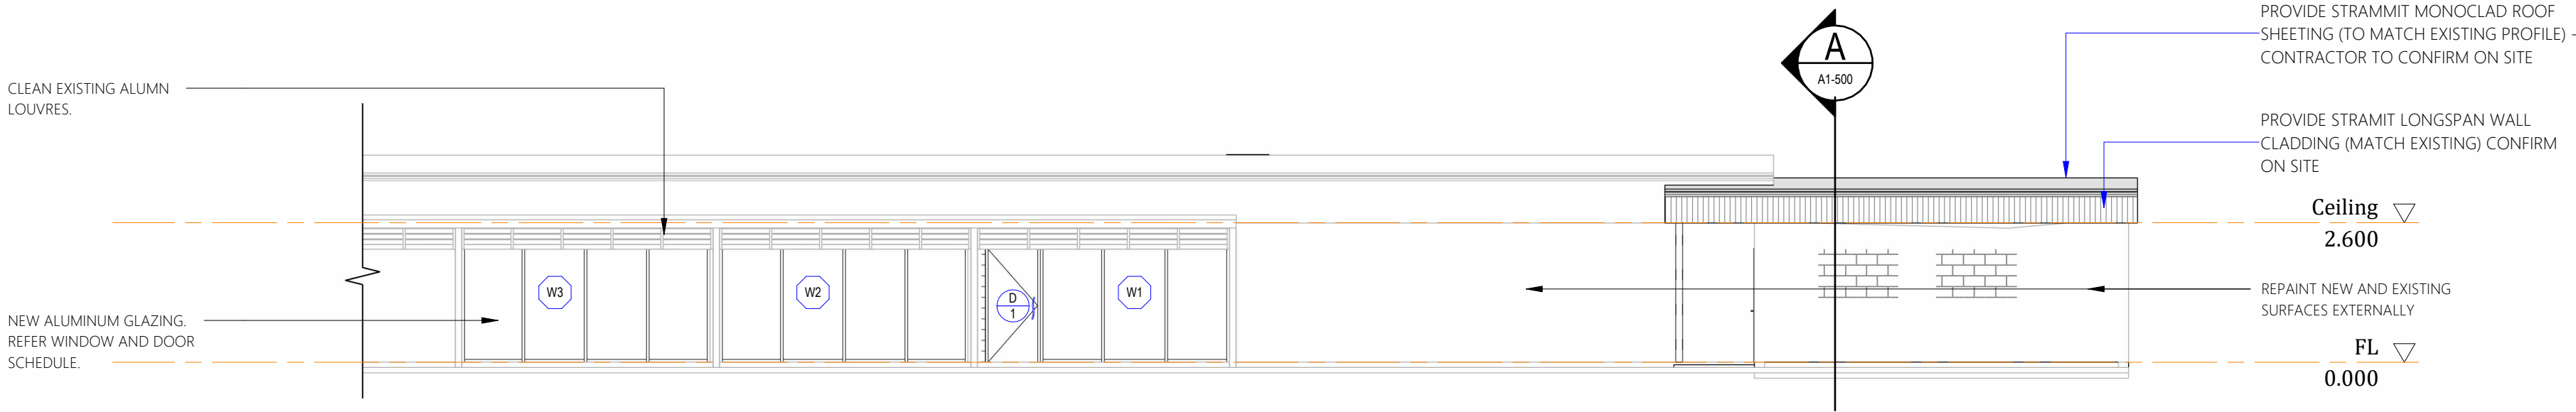


Proposed Elevation 1
1 : 100

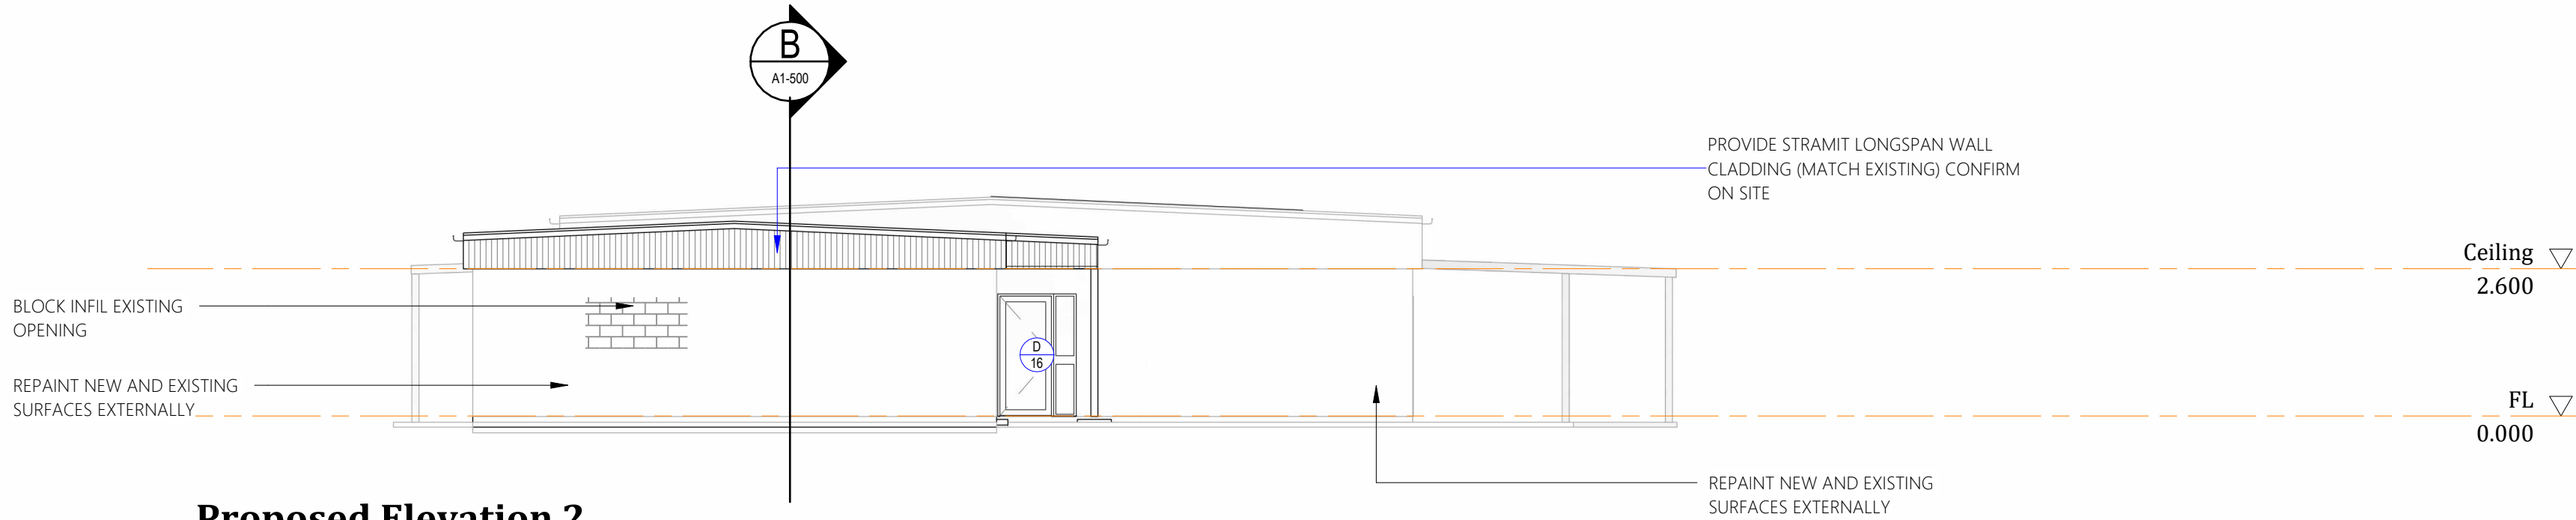


Proposed Elevation 2
1 : 100

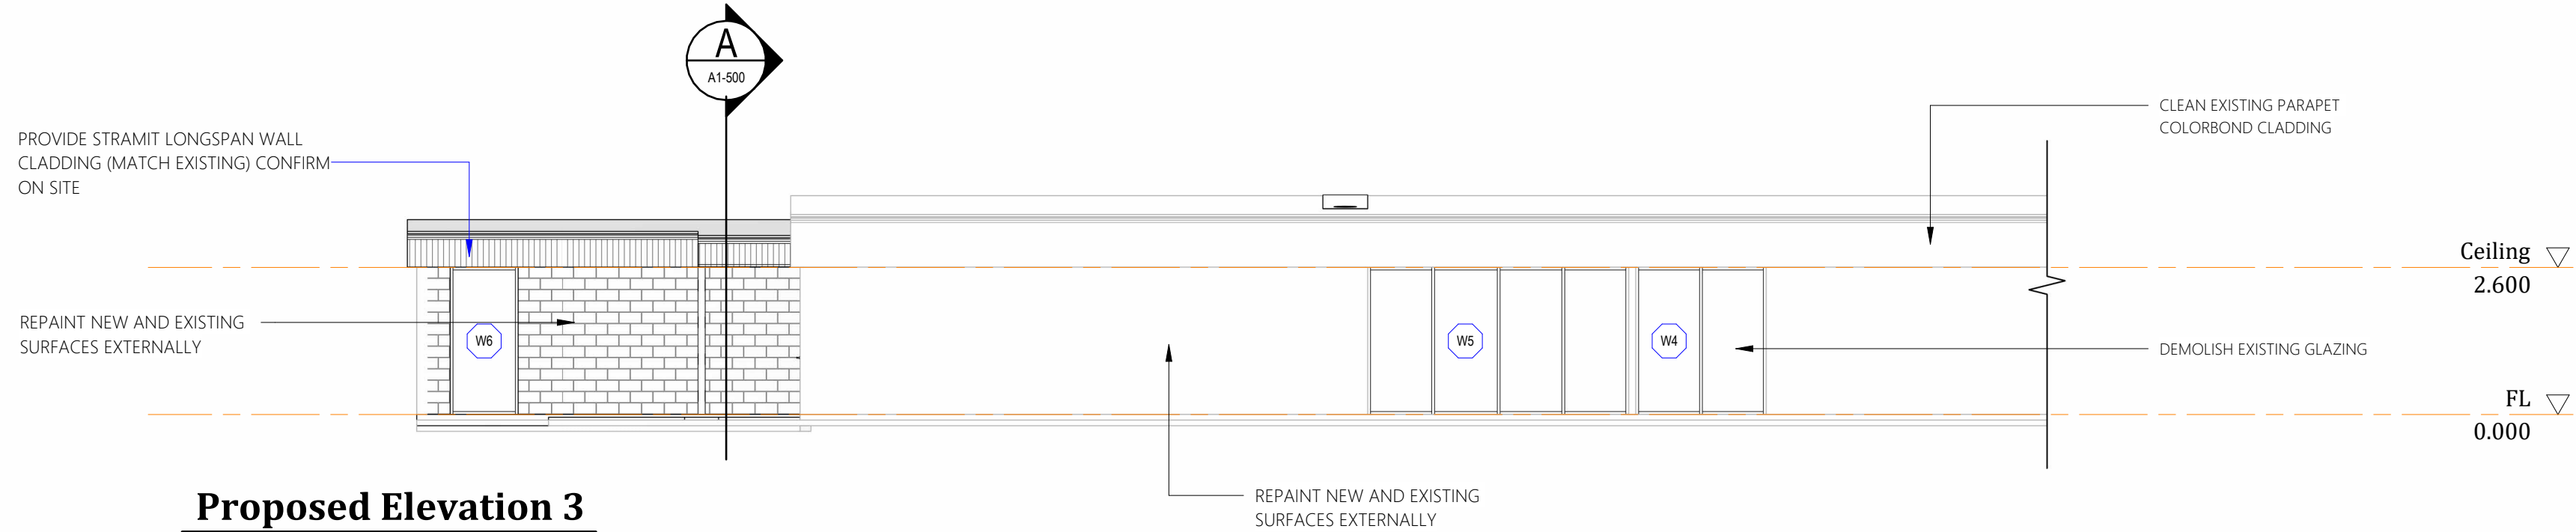

Proposed Elevation 3
1 : 100

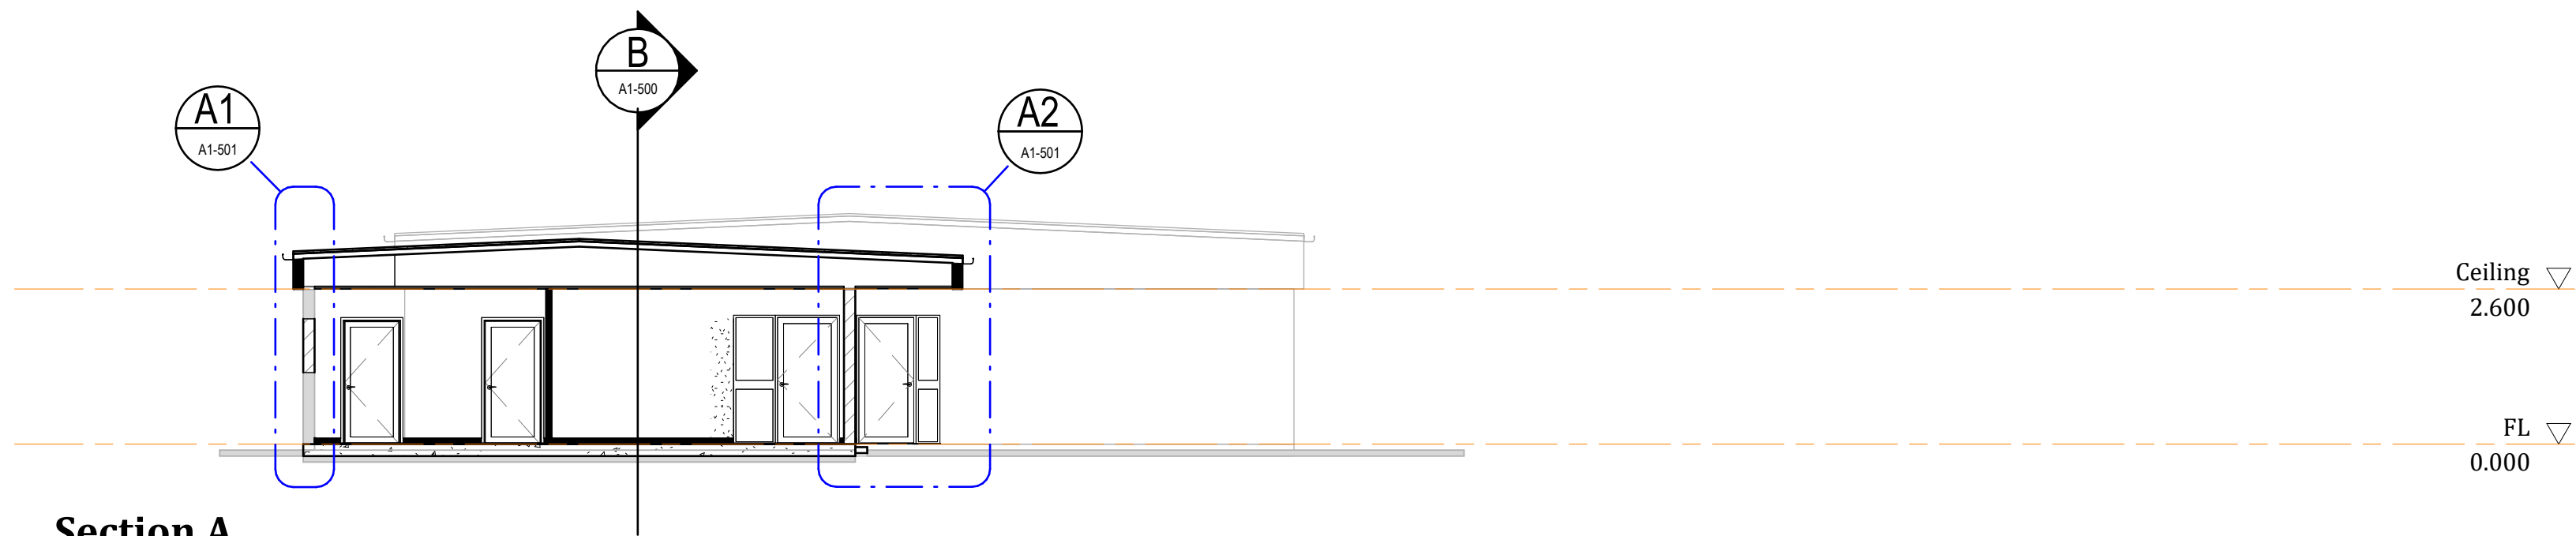

Section A
1 : 100

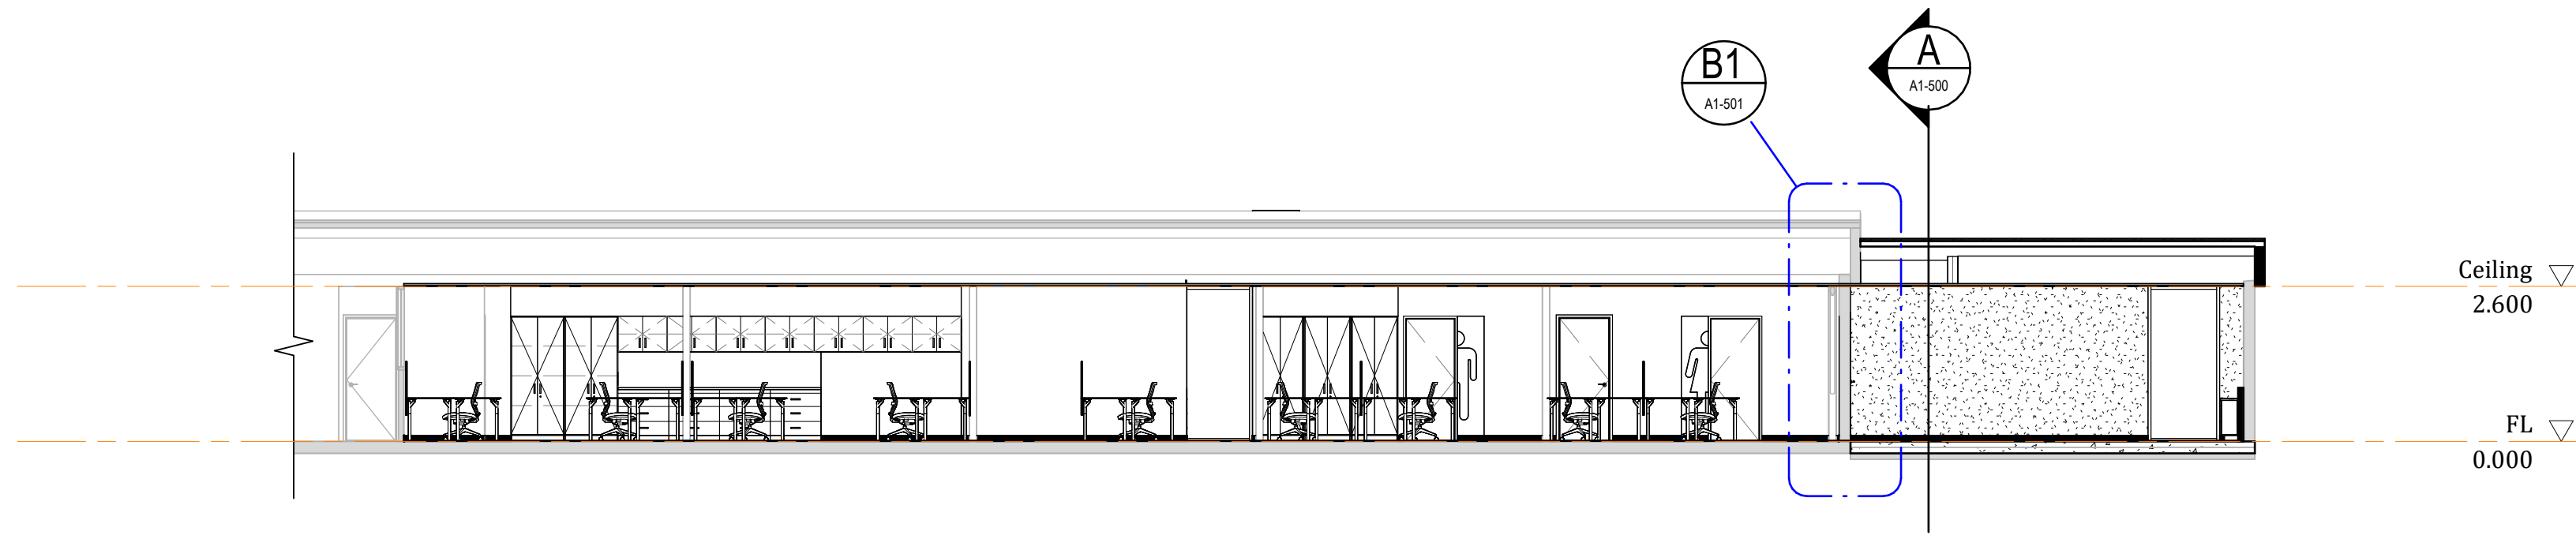

Section B
1 : 100

REVISIONS		
Rev	Description	Date
T1	TENDER ISSUE	12.03.2026

DO NOT SCALE THIS DRAWINGS



TENDER ISSUE



Project Details
REGISTRY REFURBISHMENT
Address
STANWELL POWER STATION
Drawing Title
PROPOSED SECTION




0483 988 655 
info@dezi elements.com.au 
QBCC No: 1247120 BDAQ No: 0001677

Scale:	1 : 100	Rev:
Date:	MARCH 2026	T1
Drawn:	NJB	
Project No:		Drawing No:
25_003		A1-500


12/03/2026 6:32:13 PM

REVISIONS		
Rev	Description	Date
T1	TENDER ISSUE	12.03.2026


DO NOT SCALE THIS DRAWINGS

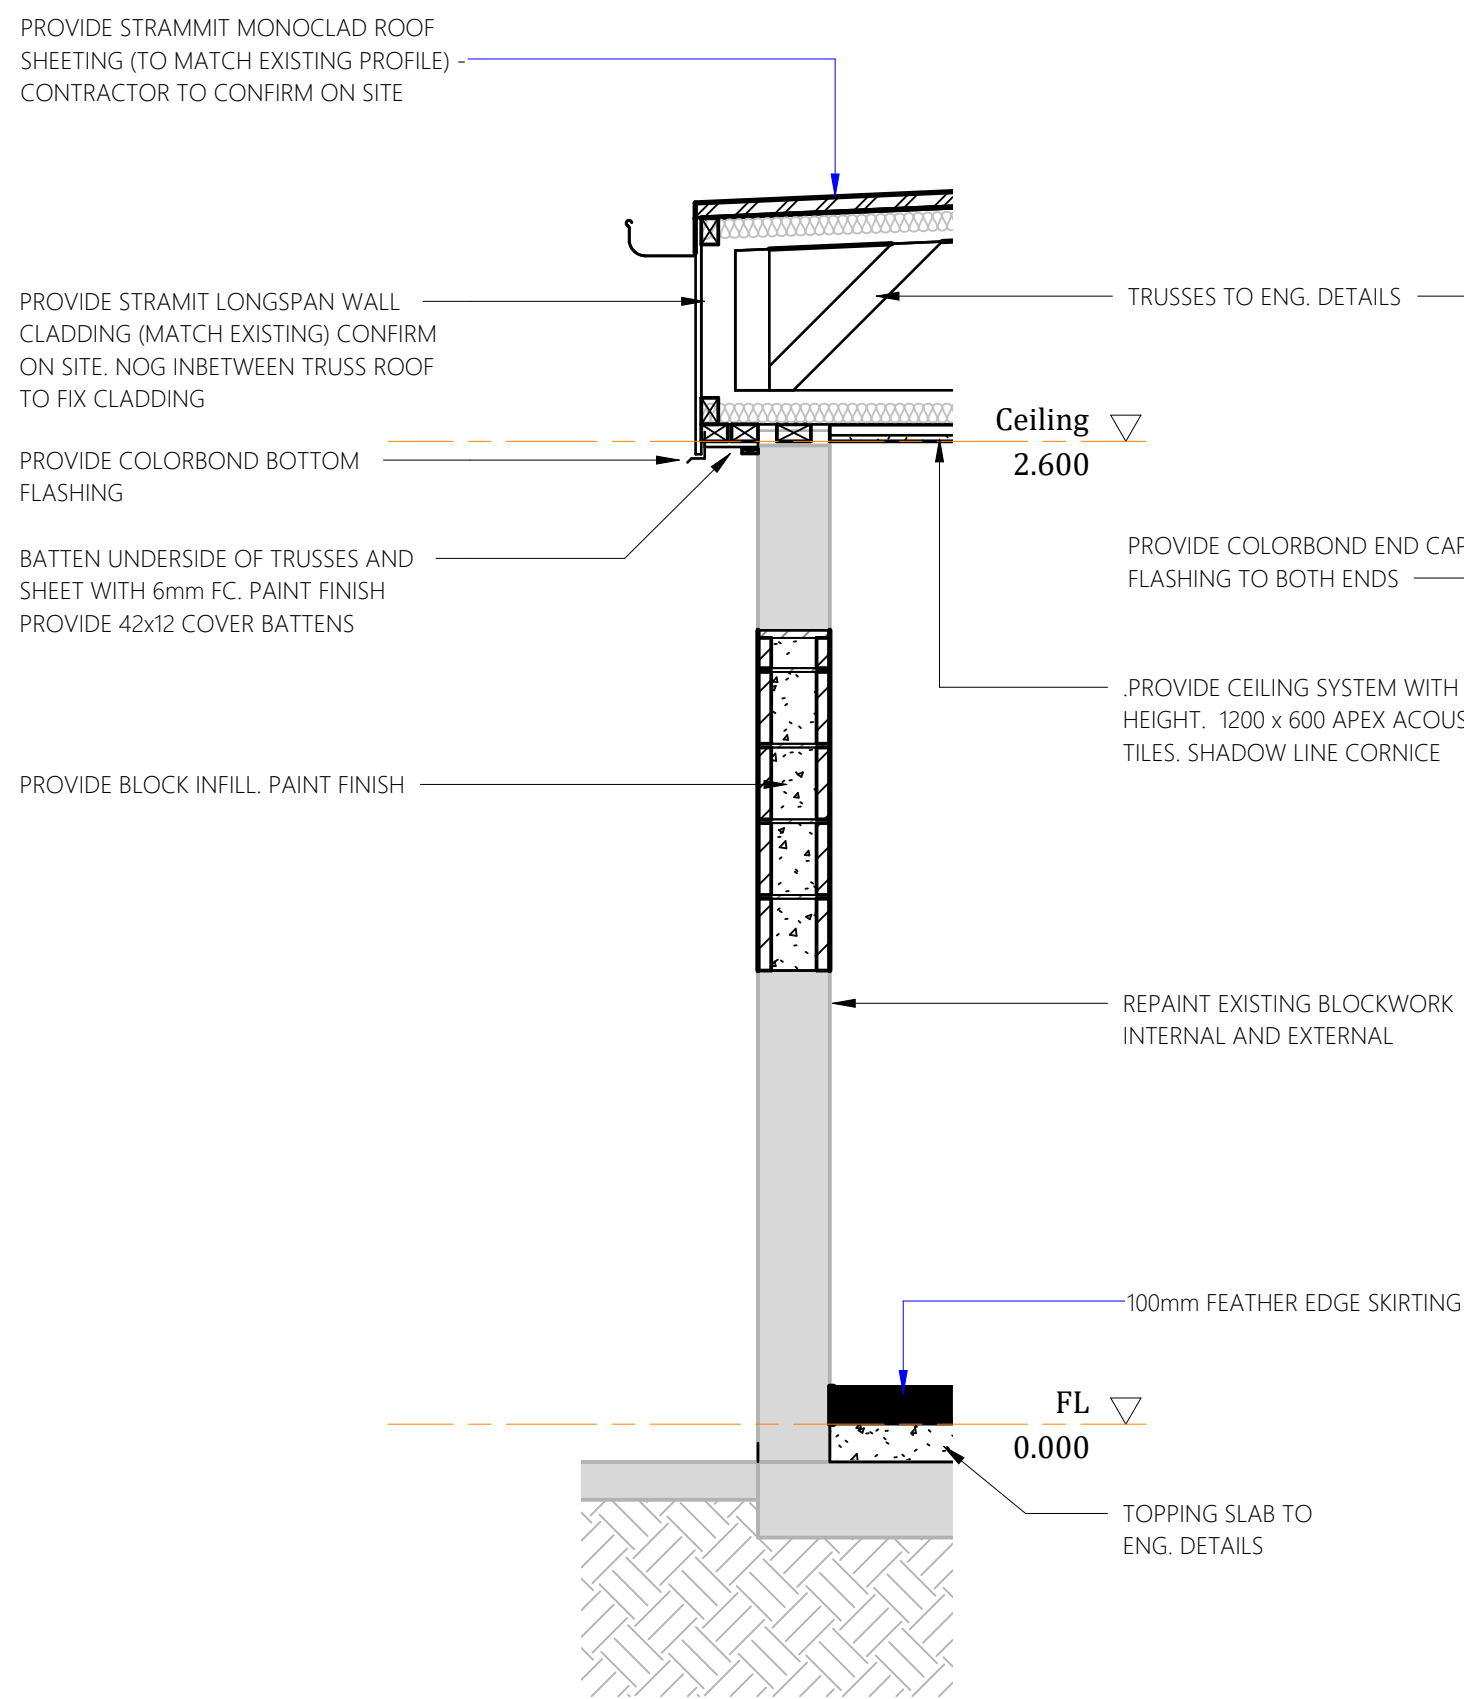

Section Detail A1
1 : 20

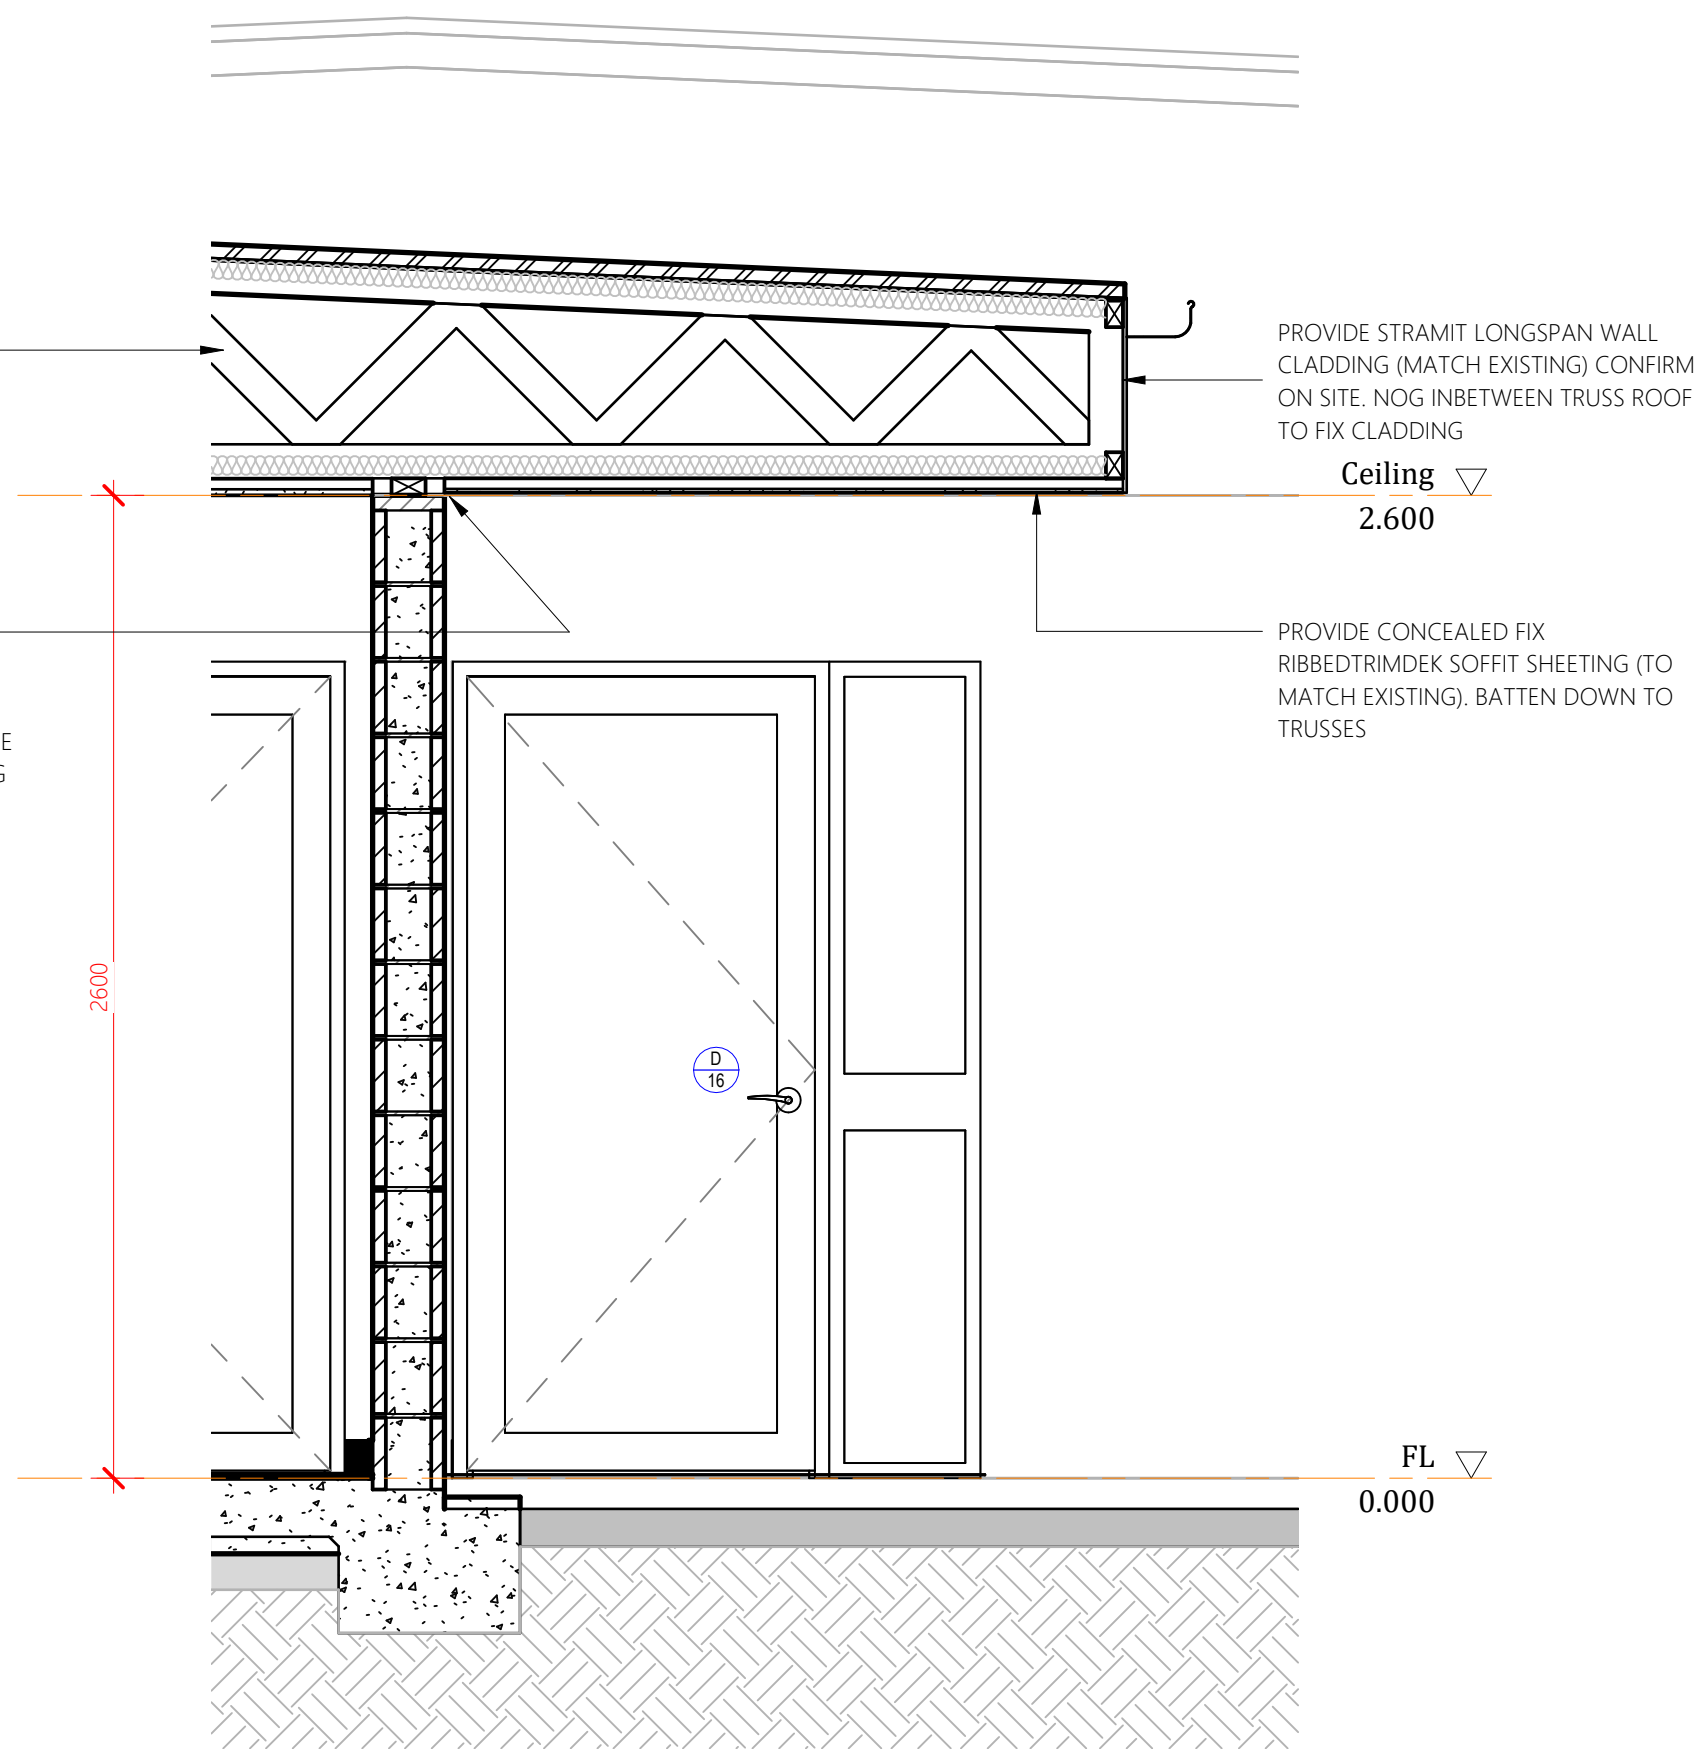

Section Detail A2
1 : 20

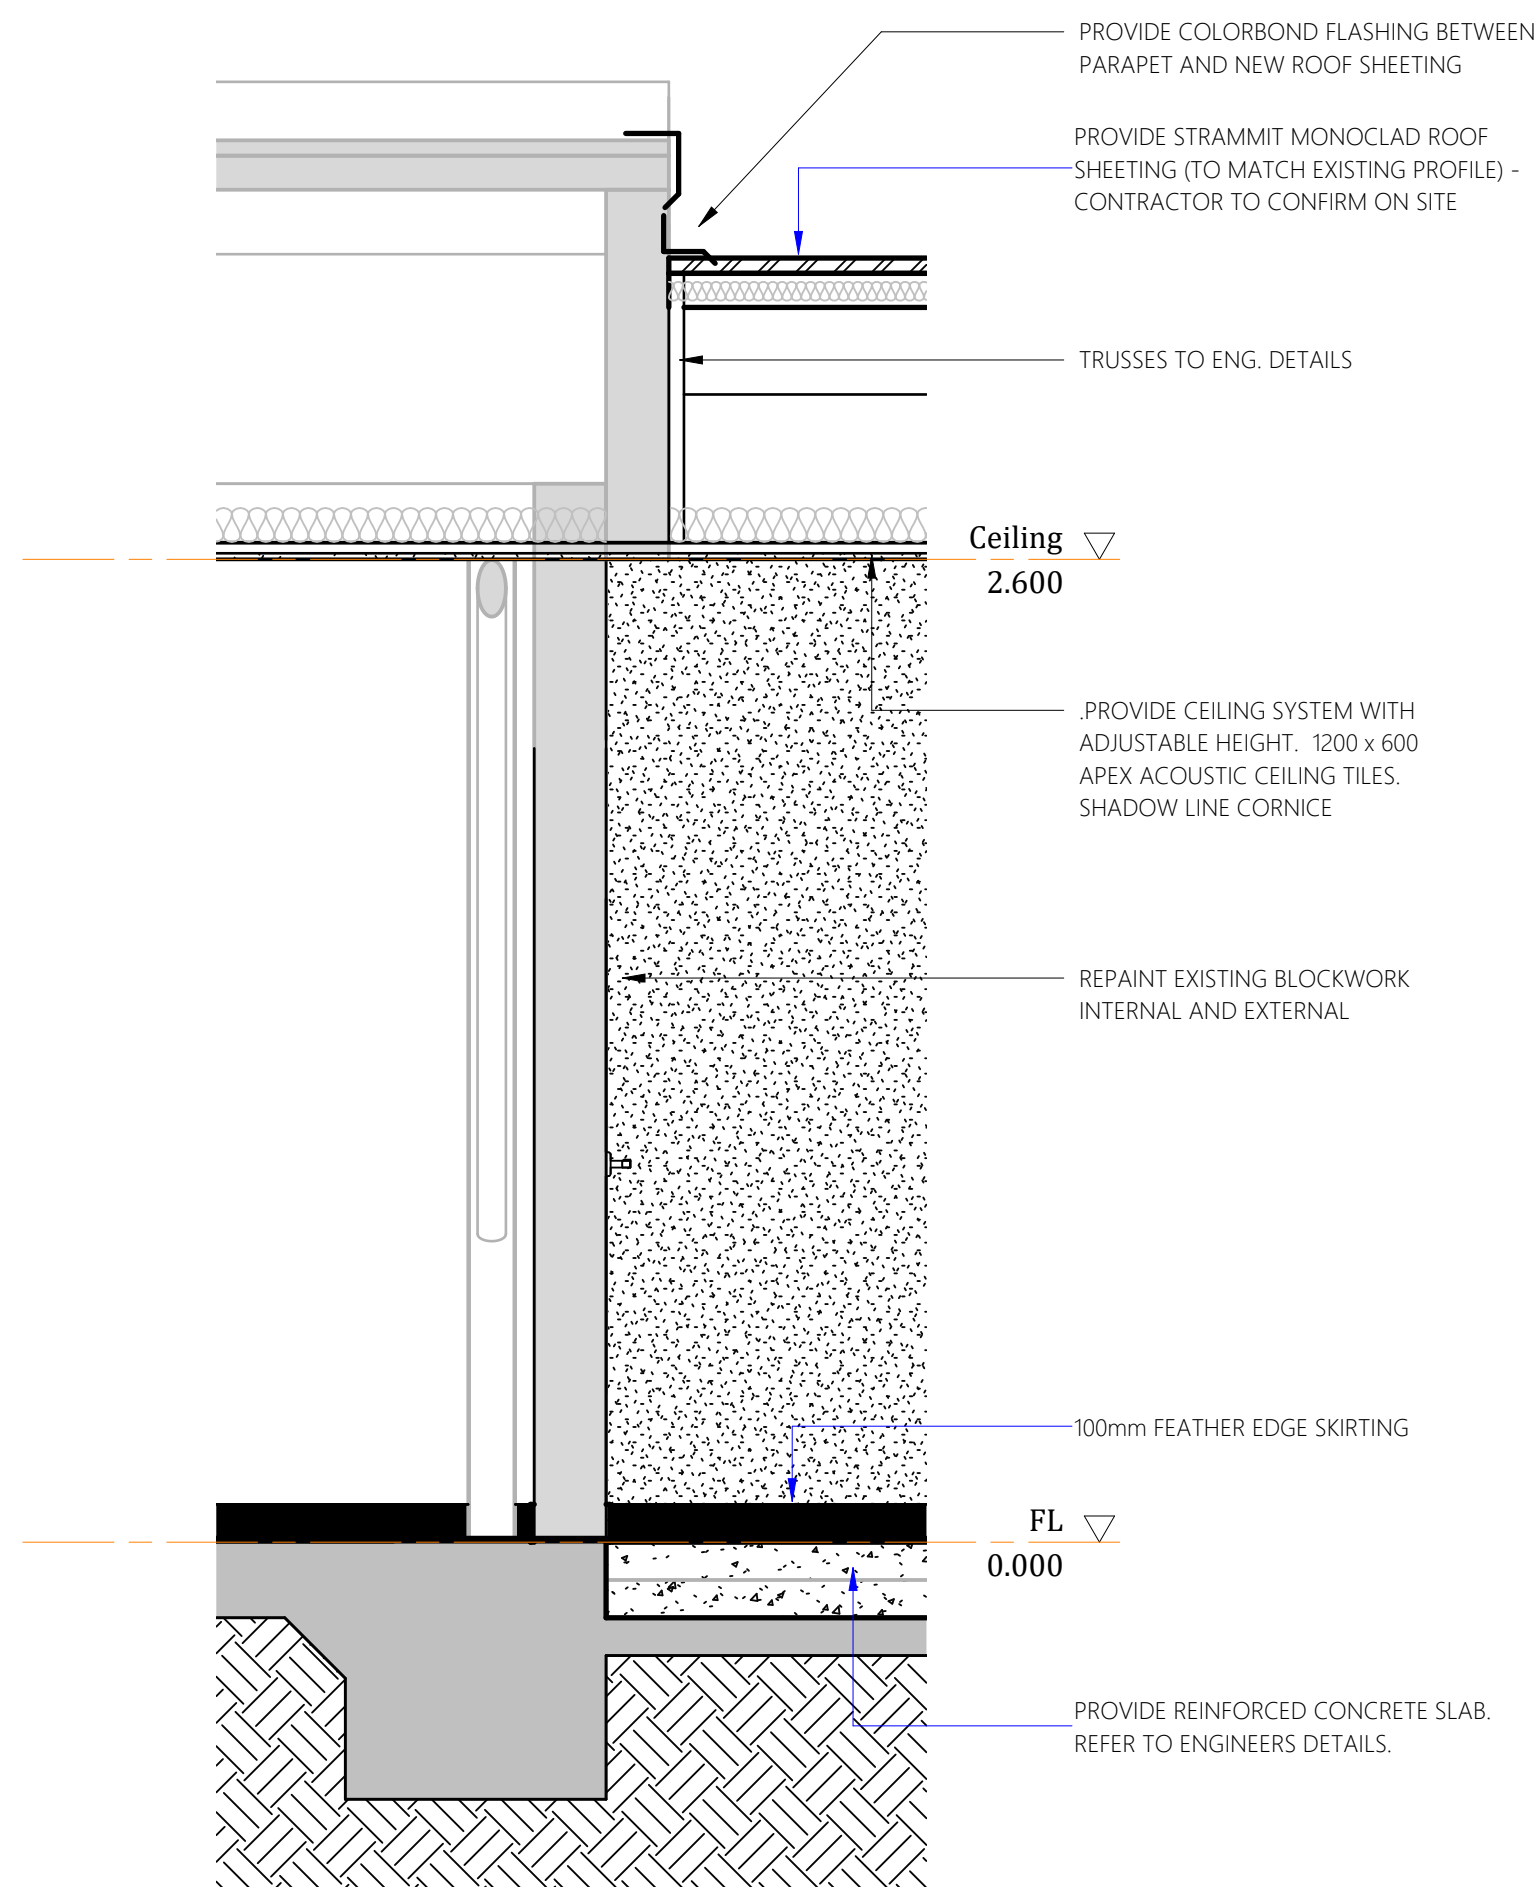

Section Detail B1
1 : 20

TENDER ISSUE



Project Details
REGISTRY REFURBISHMENT

Address
STANWELL POWER STATION

Drawing Title
SECTION DETAILS











0483 988 655 **M**
info@designelements.com.au **E**
QBCC No: 1247120 BDAQ No: 0001677

Scale: 1 : 20 Rev:
Date: MARCH 2026 **T1**
Drawn: NJB

Project No: Drawing No:
25_003 A1-501


DO NOT SCALE THIS DRAWINGS

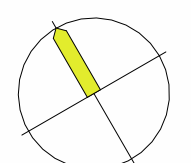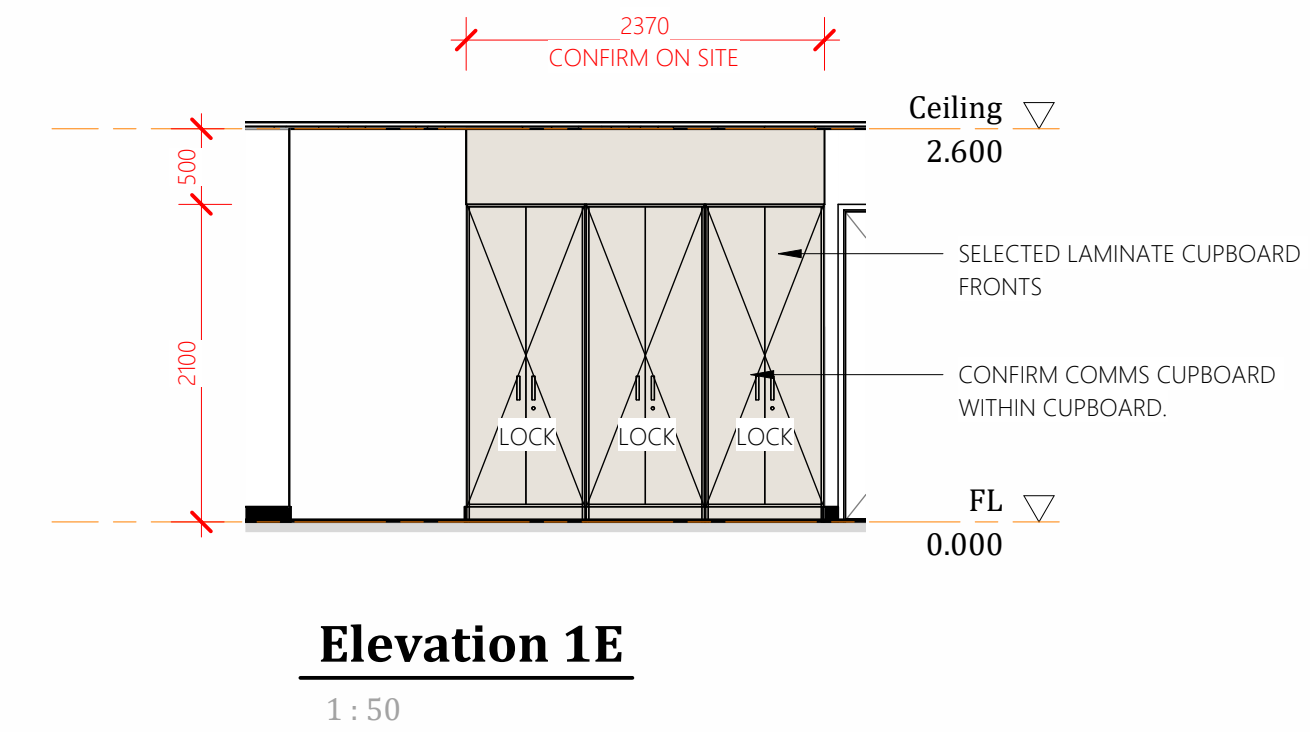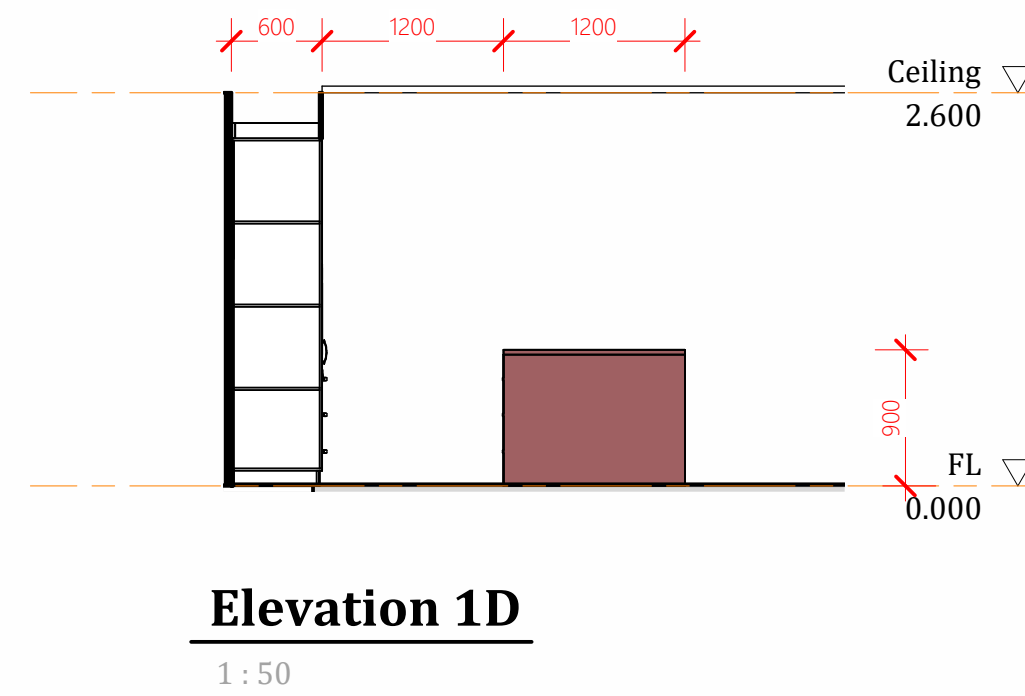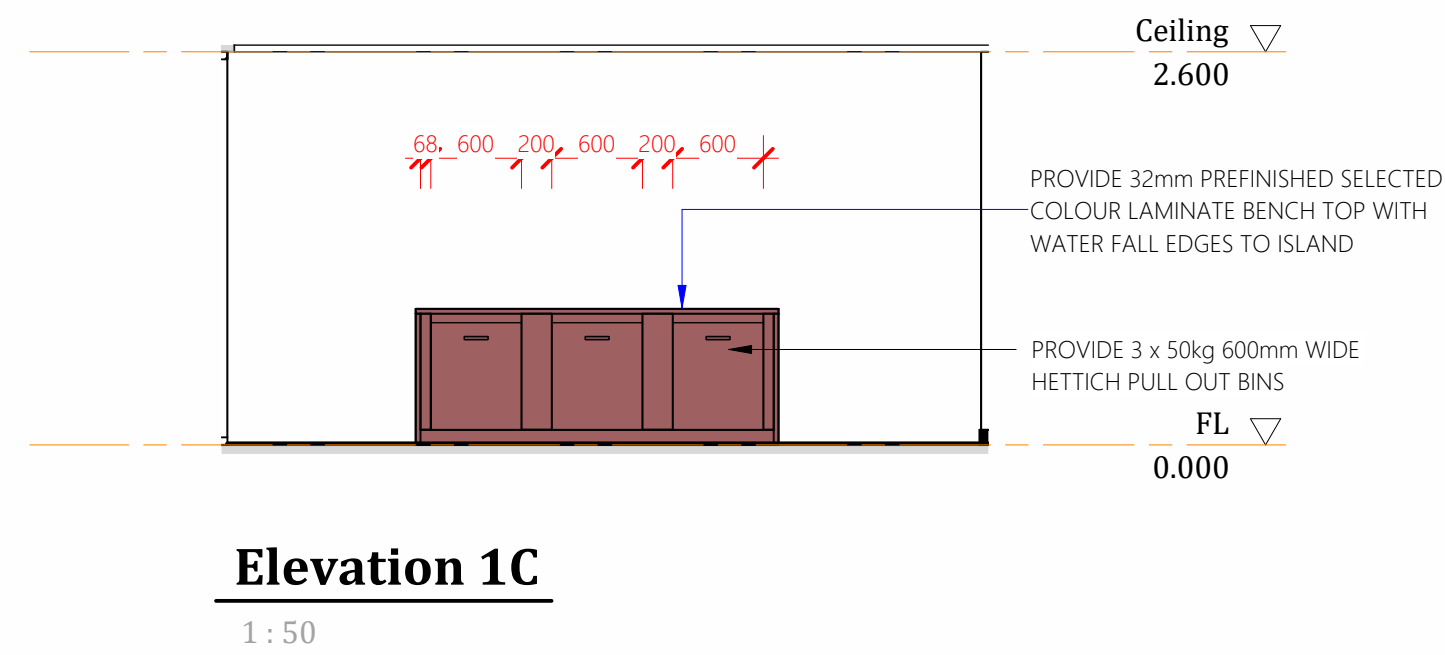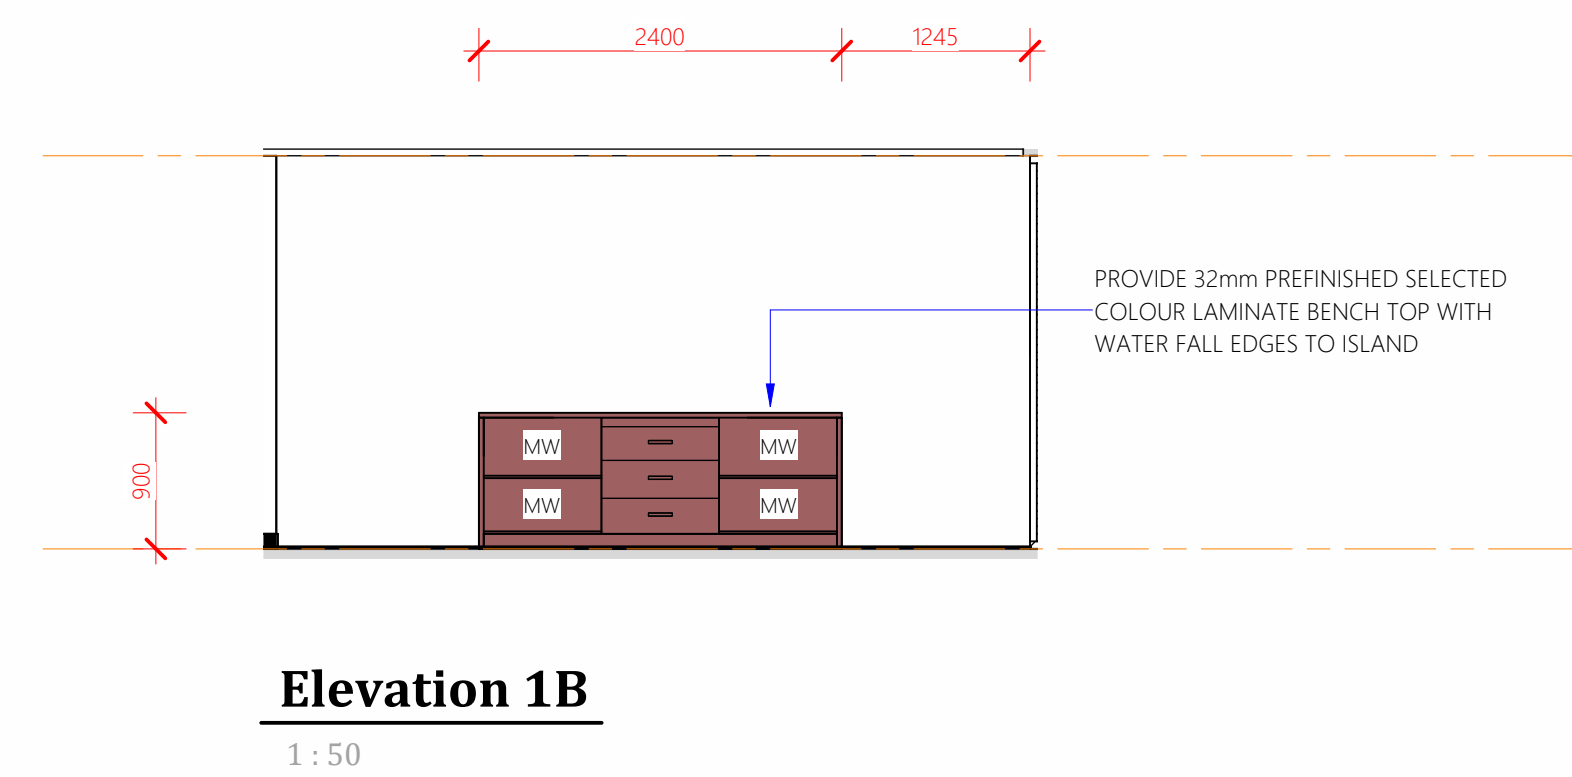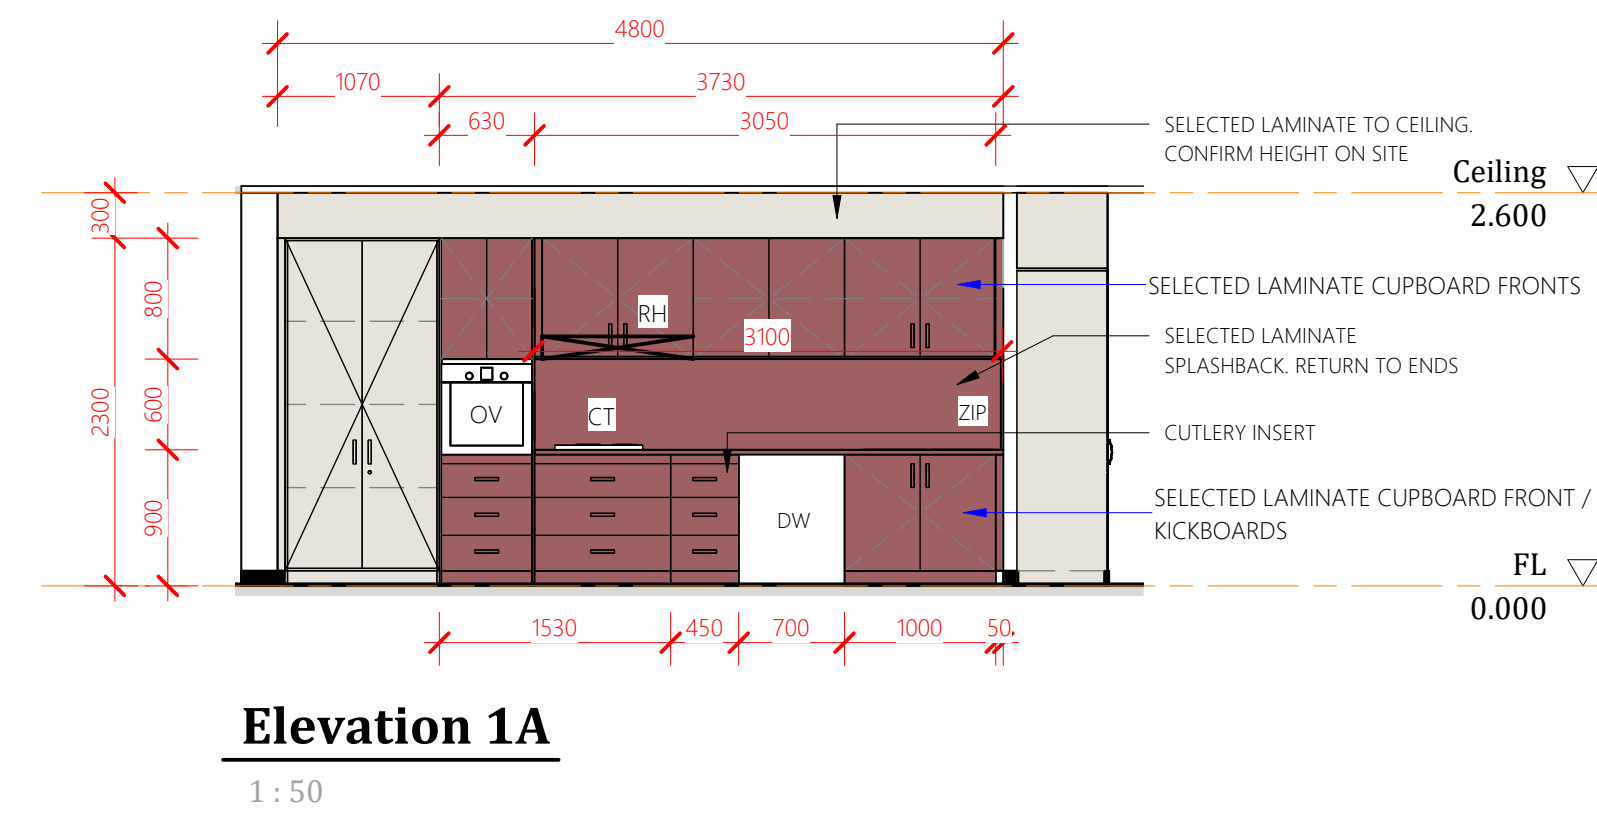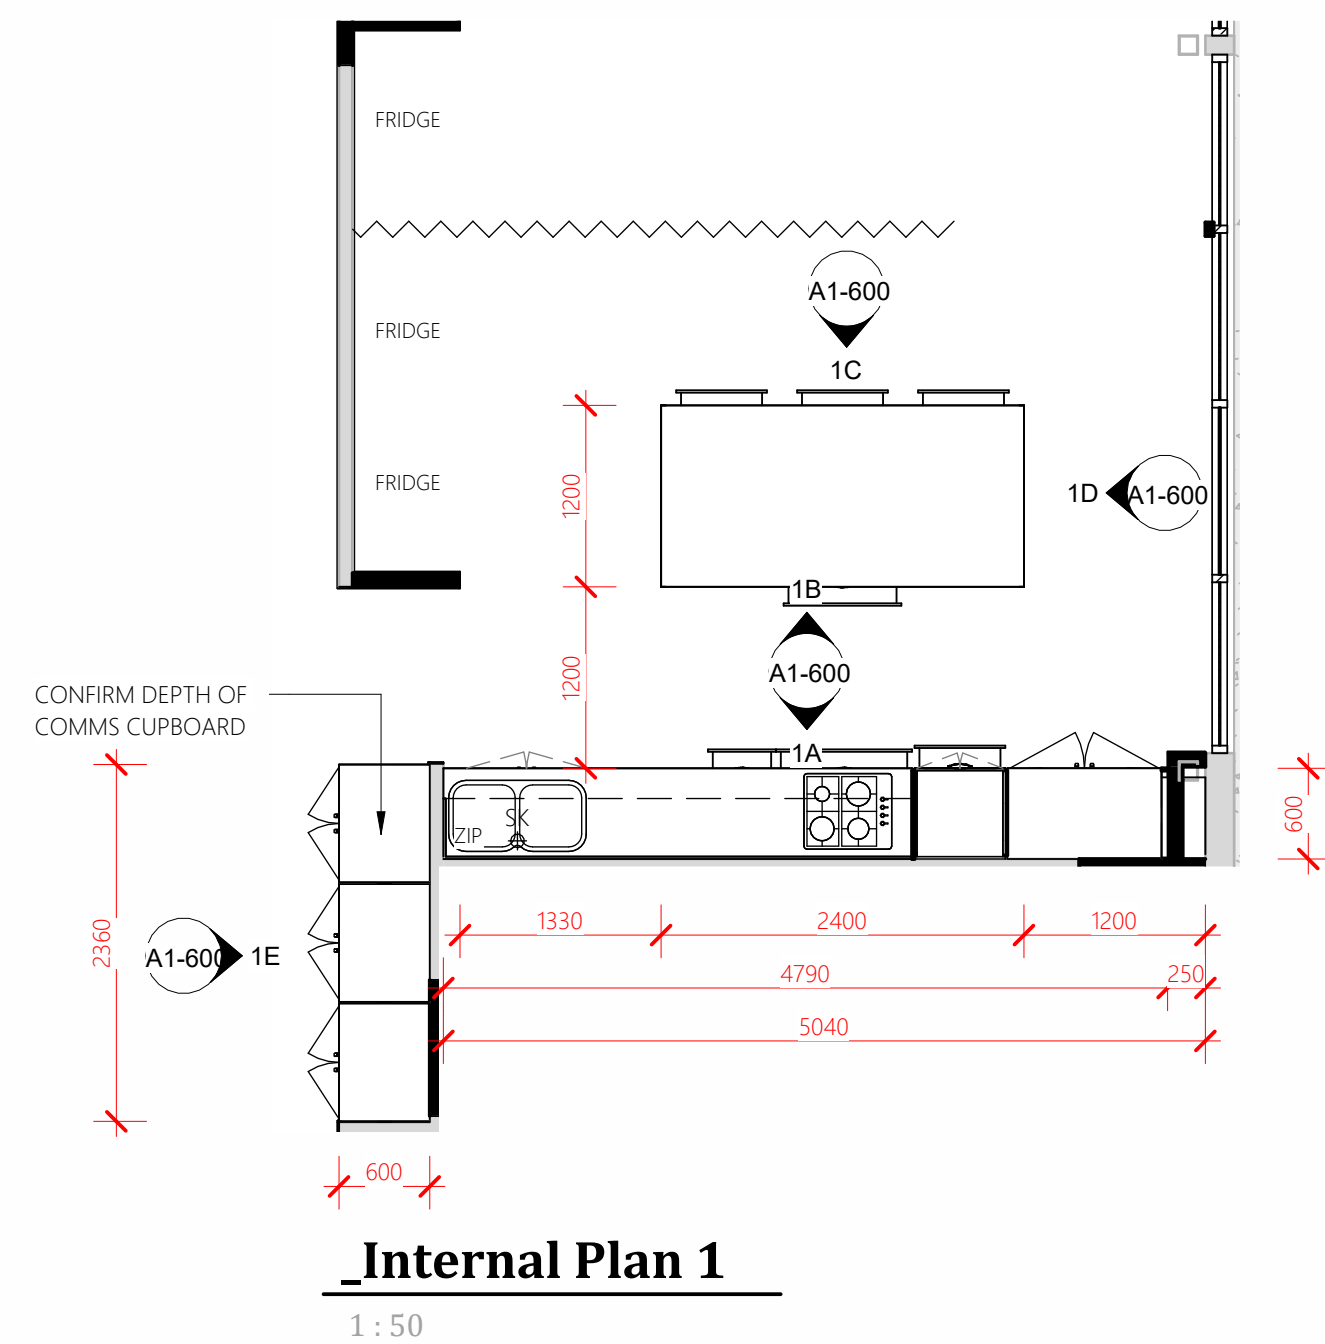

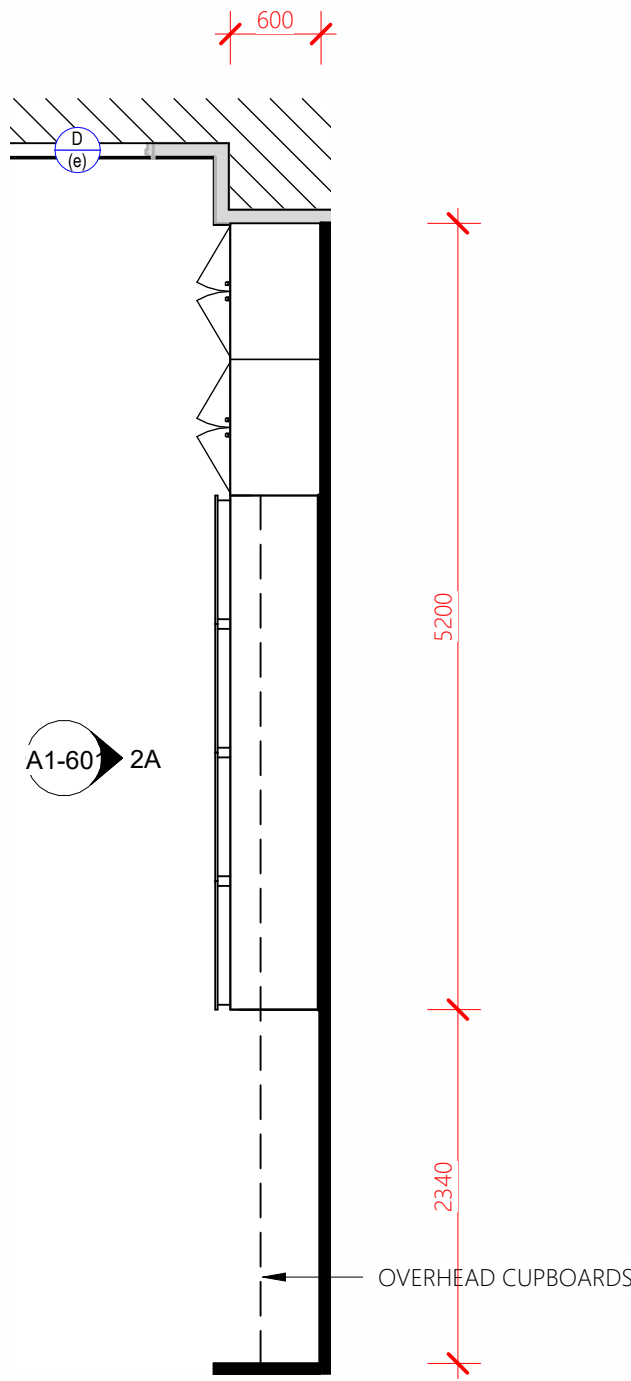

Internal Plan 2

1 : 50

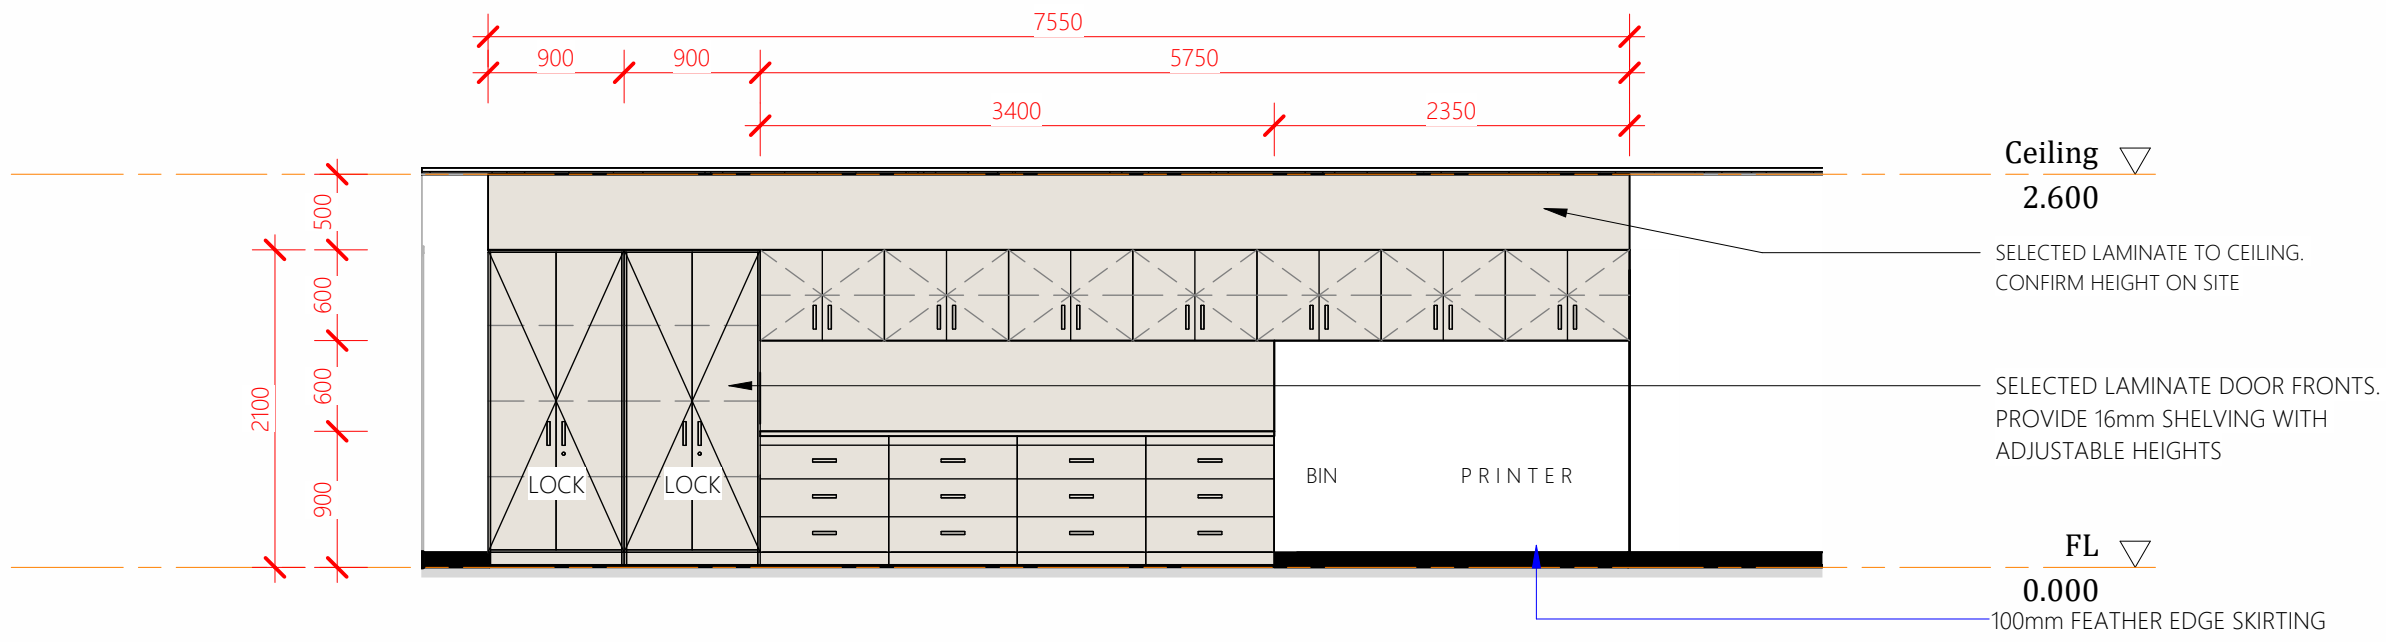

Elevation 2A

1 : 50



REVISIONS		
Rev	Description	Date
T1	TENDER ISSUE	12.03.2026

DO NOT SCALE THIS DRAWINGS



TENDER ISSUE

Client



Project Details

REGISTRY REFURBISHMENT

Address

STANWELL POWER STATION


Drawing Title


INTERNAL ELEVATIONS 2 - OPEN OFFICE



0483 988 655 **M**
info@designelements.com.au **E**
QBCC No: 1247120 BDAQ No: 0001677


Scale: 1 : 50 Rev: **T1**
Date: MARCH 2026
Drawn: NJB
Project No: 25_003 Drawing No: **A1-601**

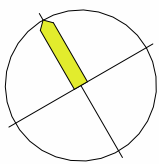

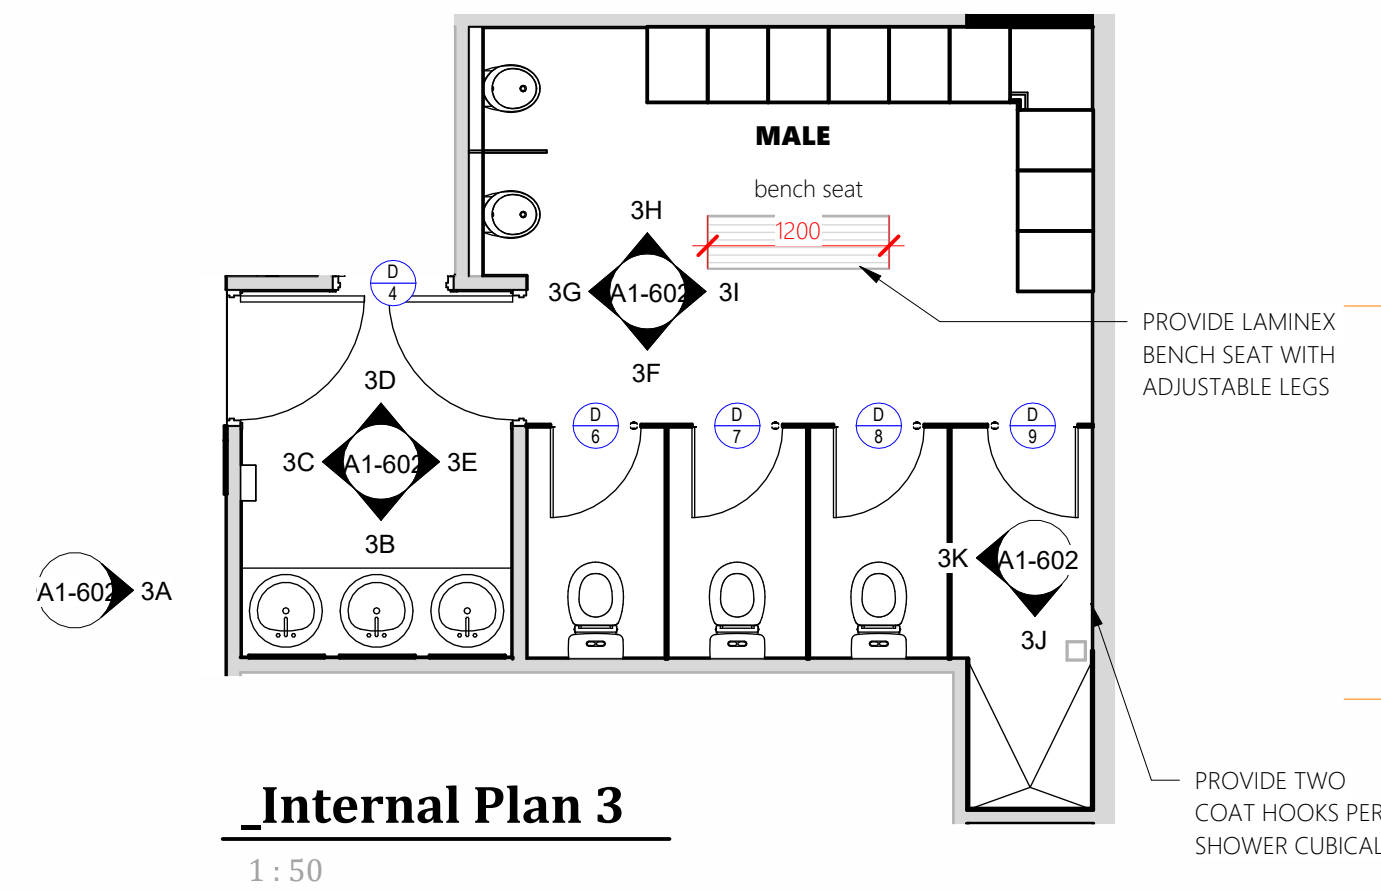


Internal Plan 3

1 : 50

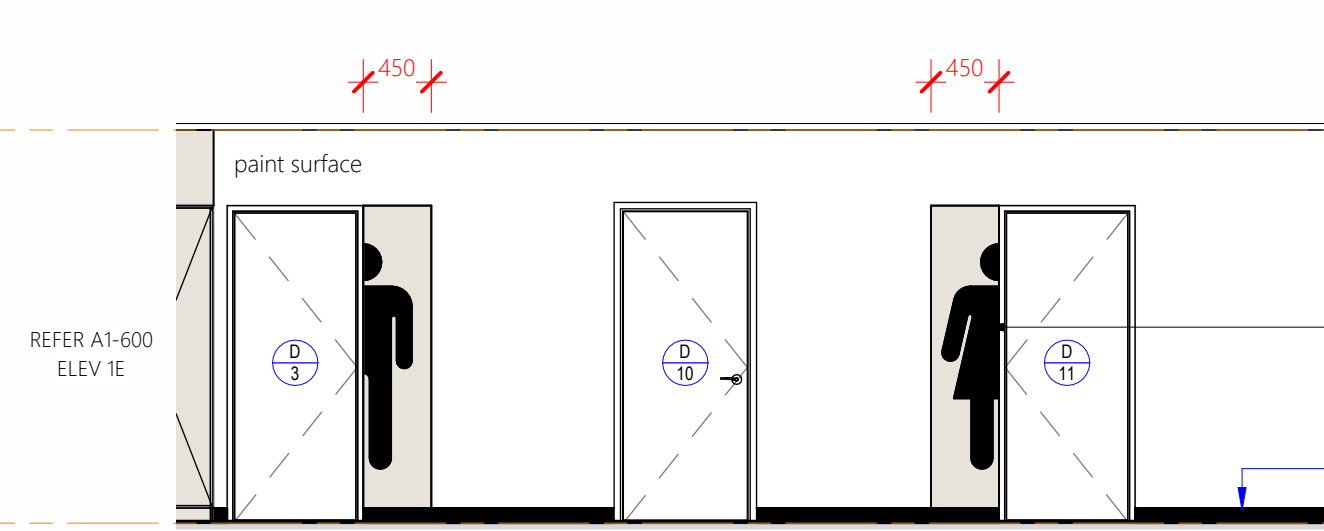


Elevation 3A

1 : 50

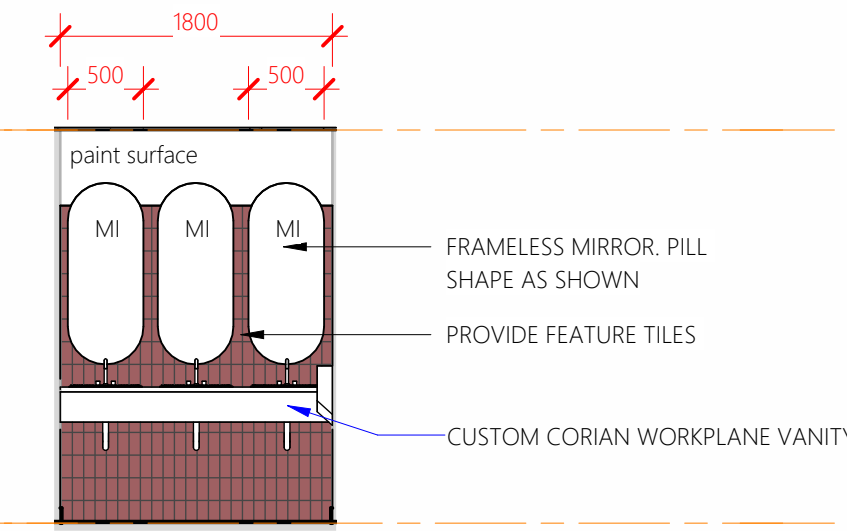


Elevation 3B

1 : 50

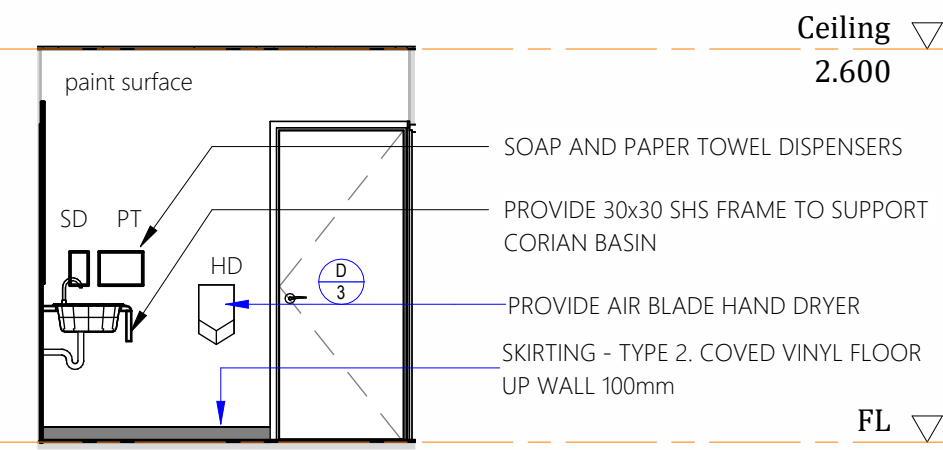


Elevation 3C

1 : 50

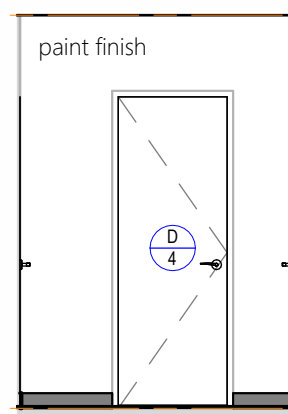


Elevation 3D

1 : 50

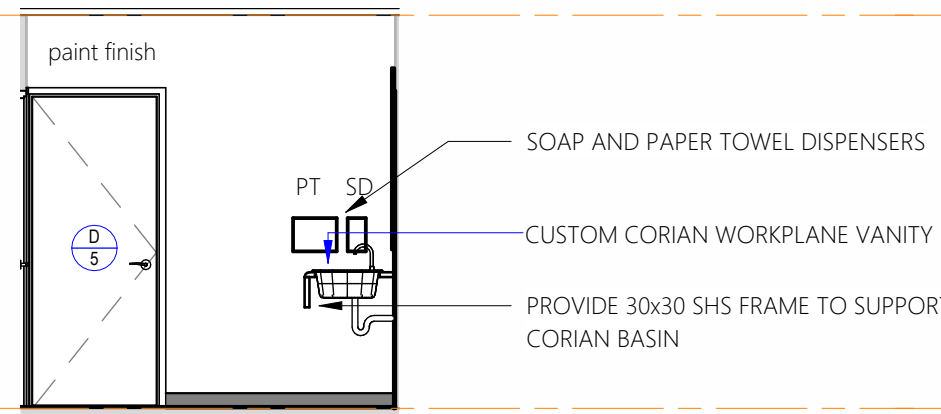


Elevation 3E

1 : 50

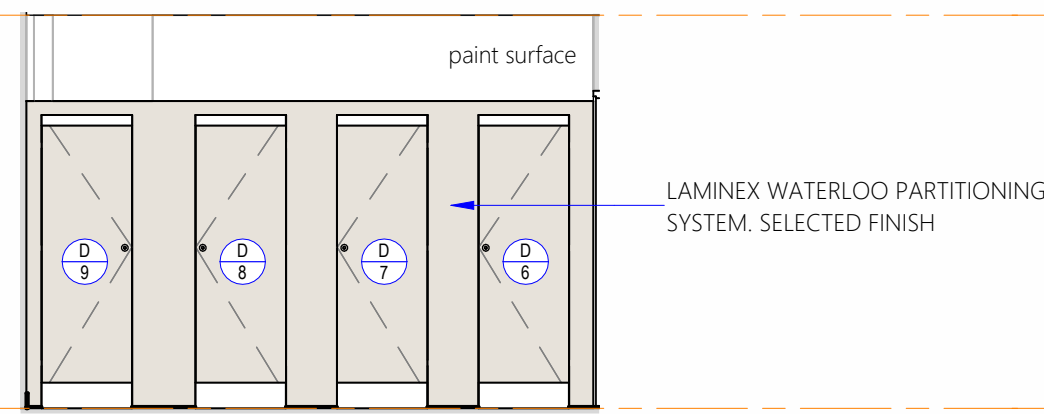


Elevation 3F

1 : 50

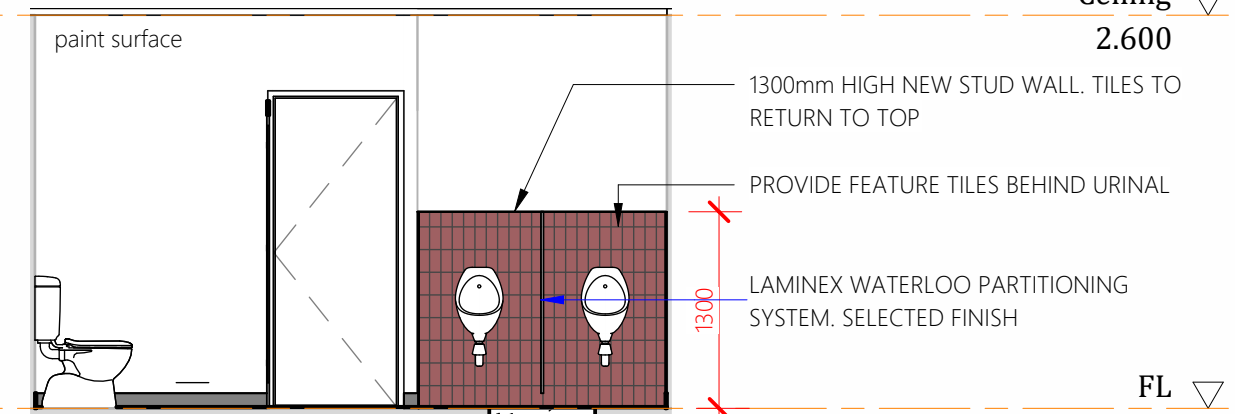


Elevation 3G

1 : 50

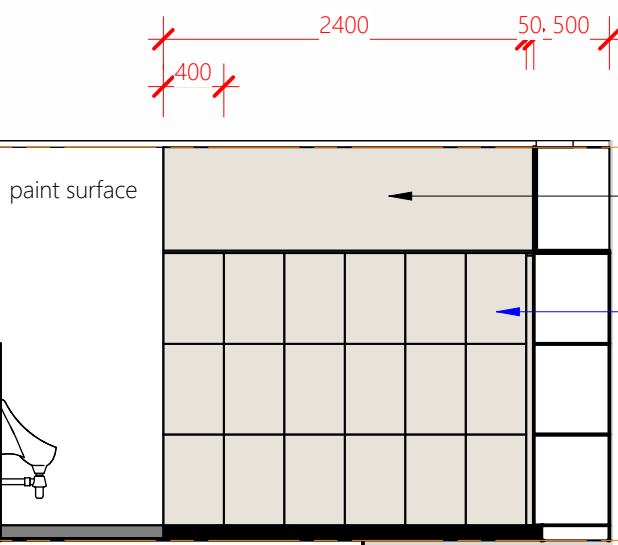


Elevation 3H

1 : 50

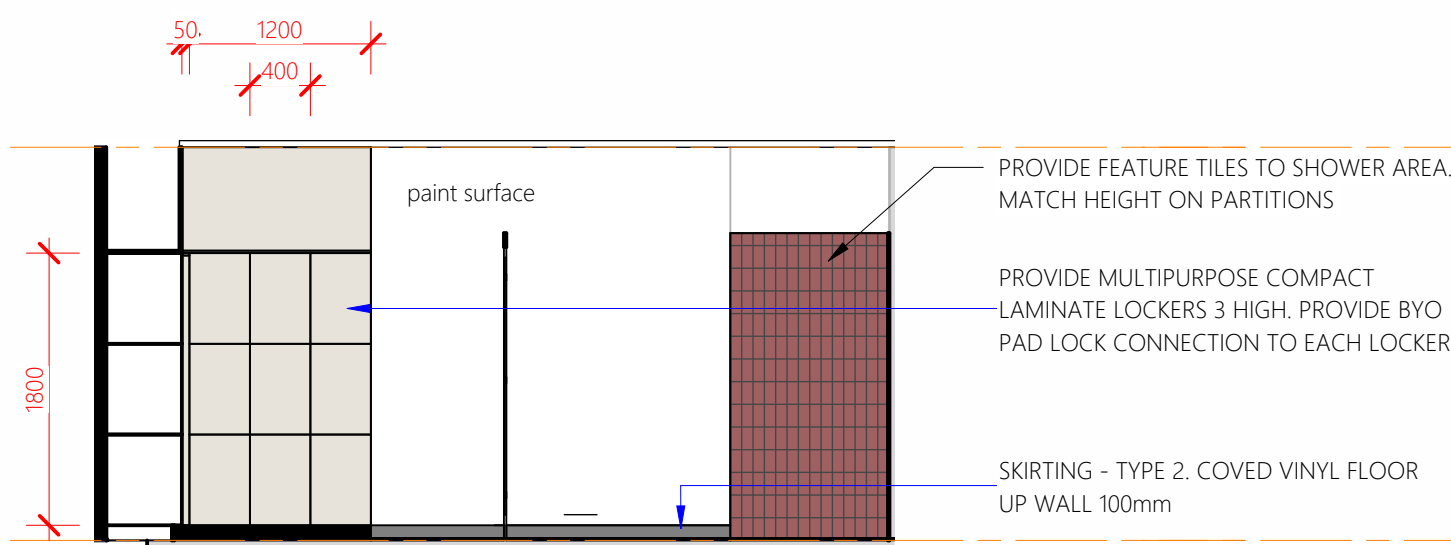


Elevation 3I

1 : 50

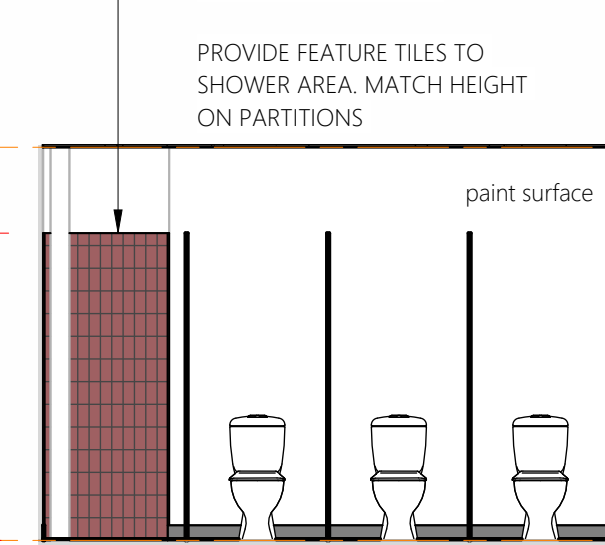


Elevation 3J

1 : 50

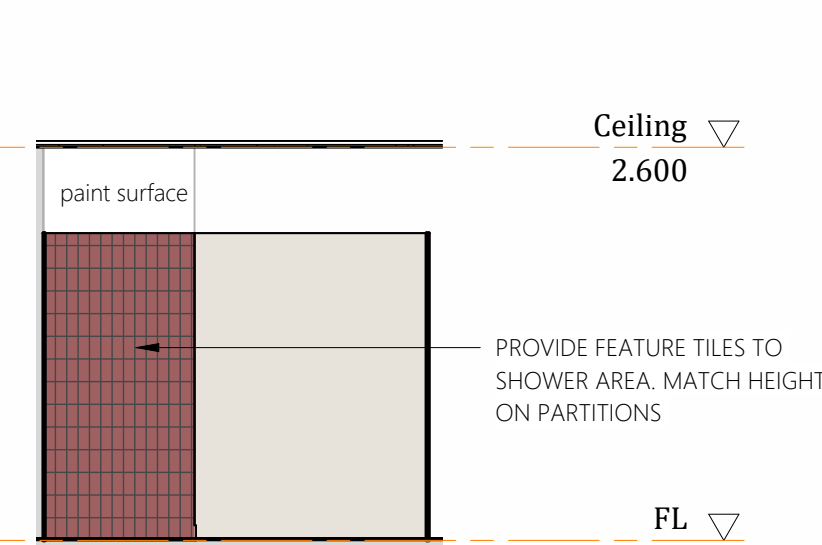


Elevation 3K

1 : 50

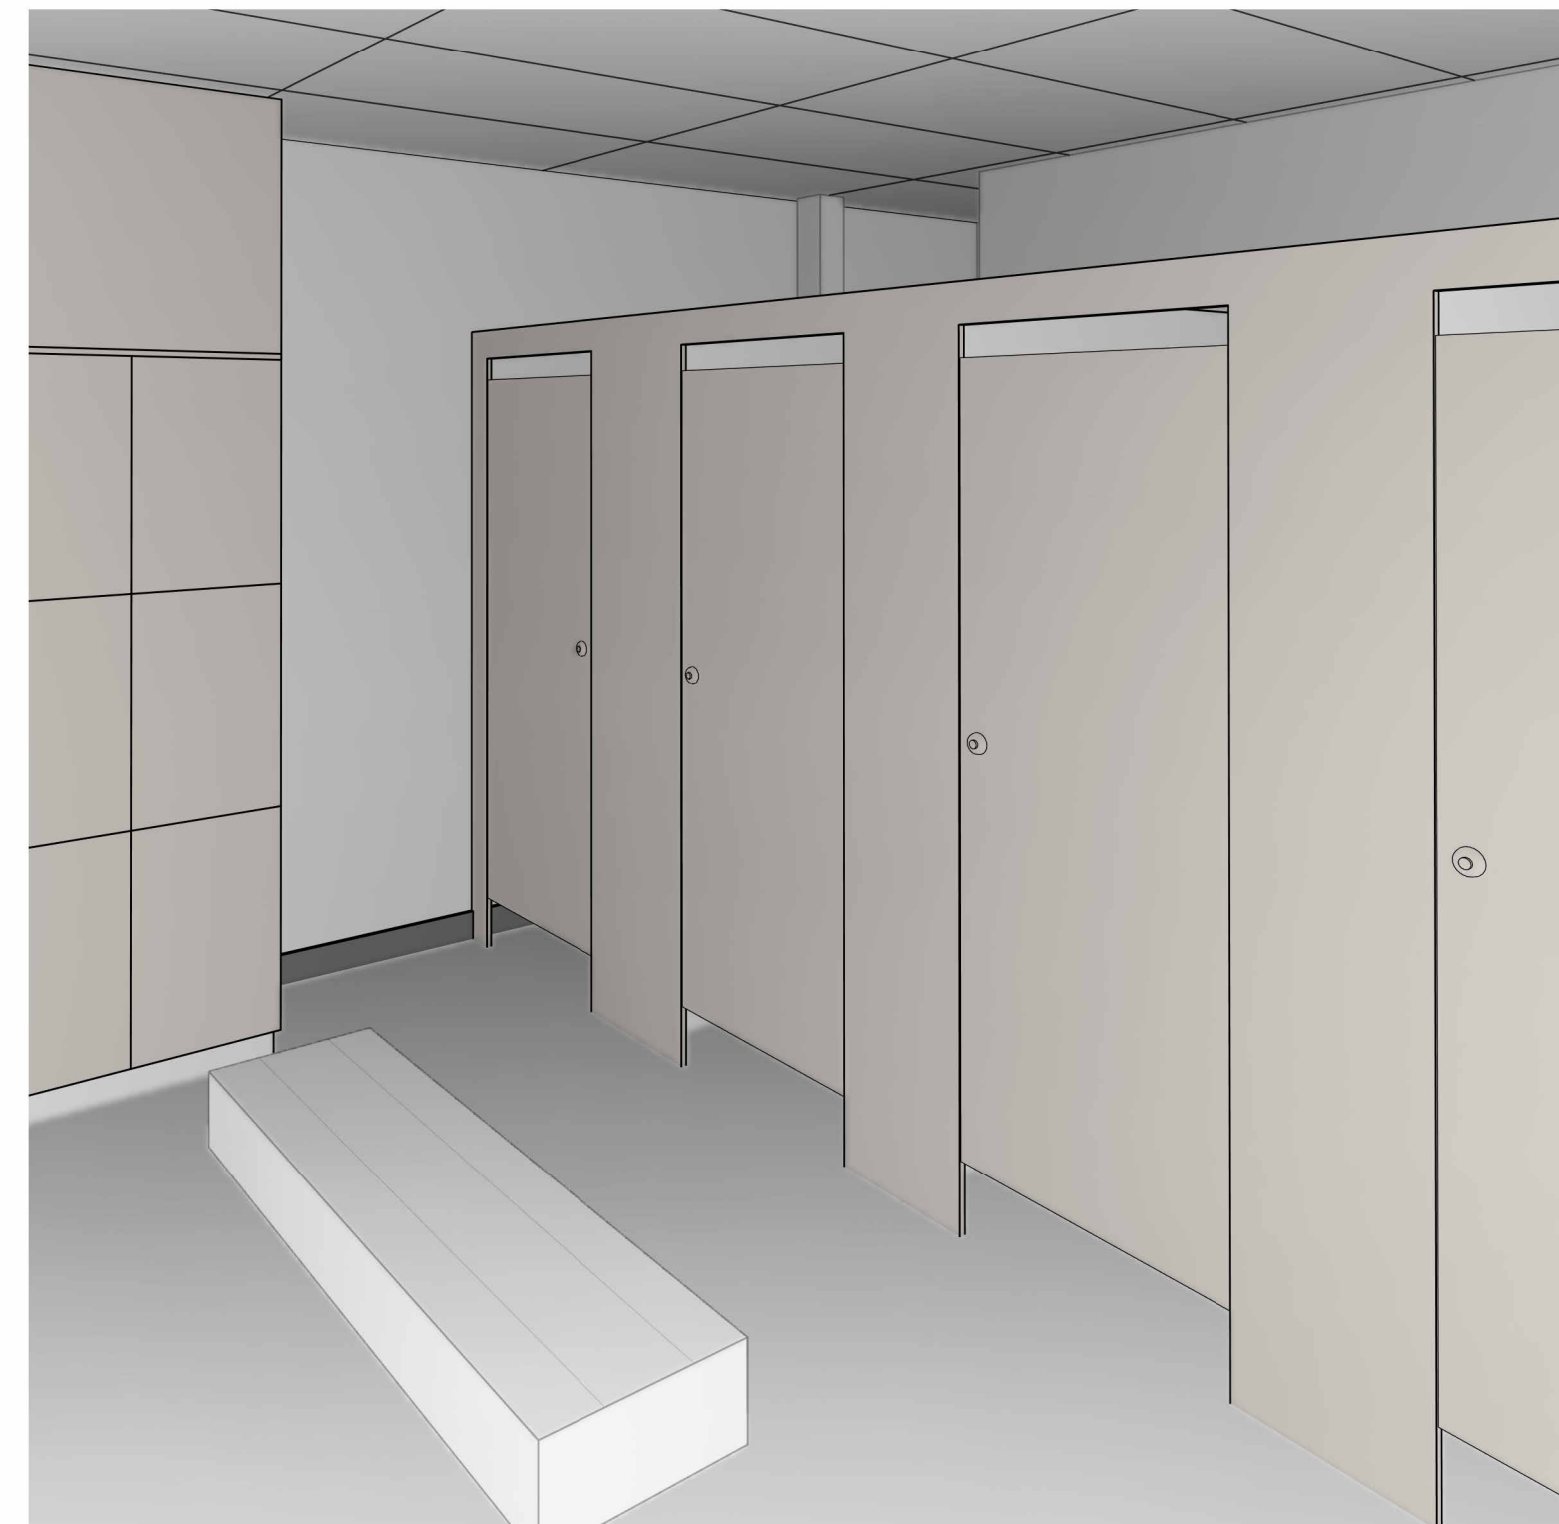

REVISIONS		
Rev	Description	Date
T1	TENDER ISSUE	12.03.2026

DO NOT SCALE THIS DRAWINGS

 


TENDER ISSUE



Project Details
REGISTRY REFURBISHMENT
Address
STANWELL POWER STATION
Drawing Title
INTERNAL ELEVATIONS 3 - MALE AMENITIES


dezi nelements BUILDING DESIGNERS
0483 988 655 M
info@dezi
QBCC No: 1247120 BDAQ No: 0001677
Scale: 1 : 50
Date: MARCH 2026
Drawn: NJB
Project No: Drawing No:
25_003 A1-602

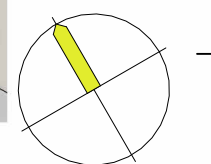


REVISIONS

Rev	Description	Date
T1	TENDER ISSUE	12.03.2026


DO NOT SCALE THIS DRAWINGS

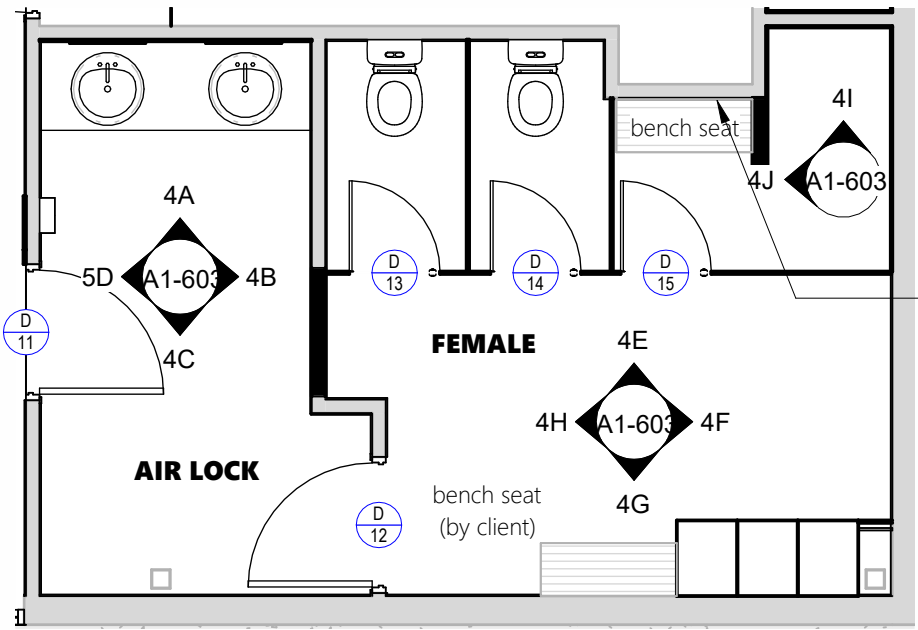


Internal Plan 4
1 : 50

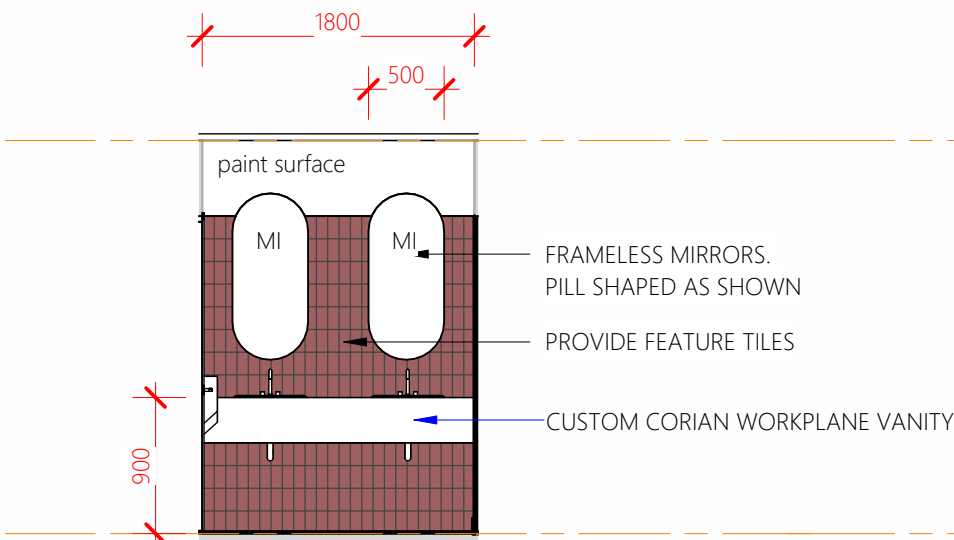


Elevation 4A
1 : 50

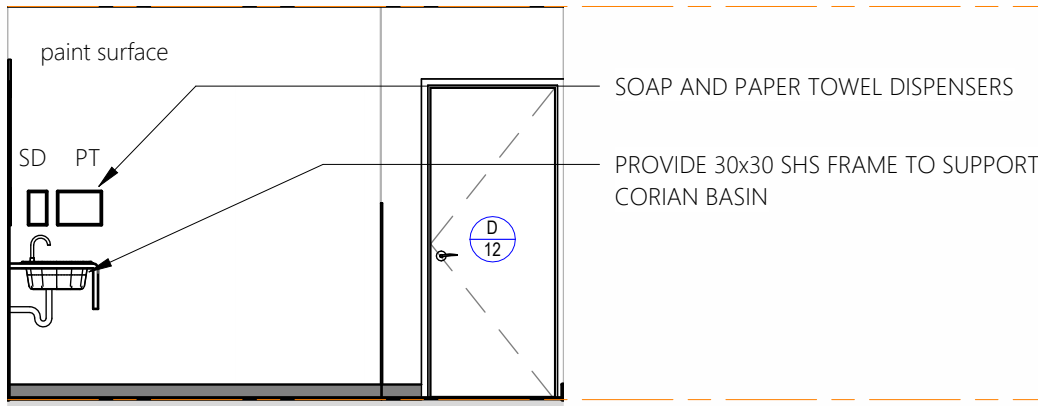


Elevation 4B
1 : 50

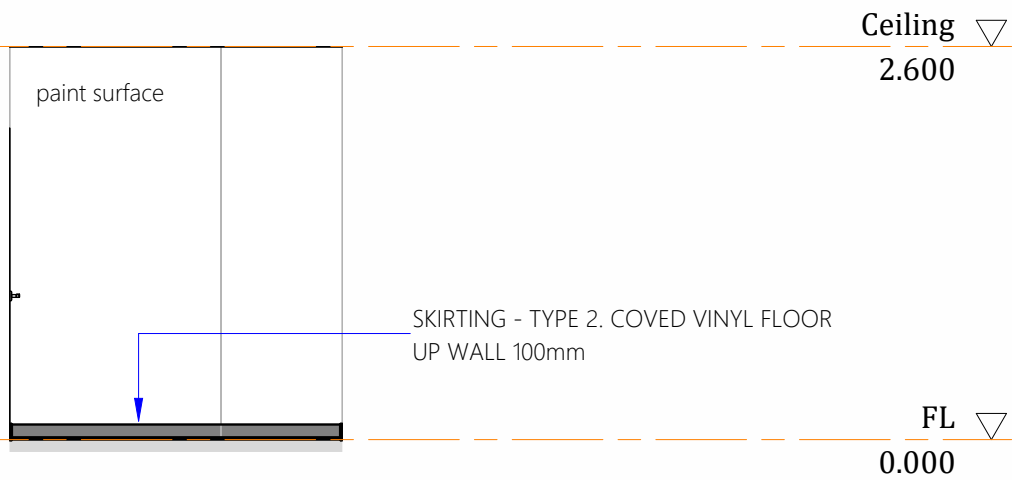


Elevation 4C
1 : 50

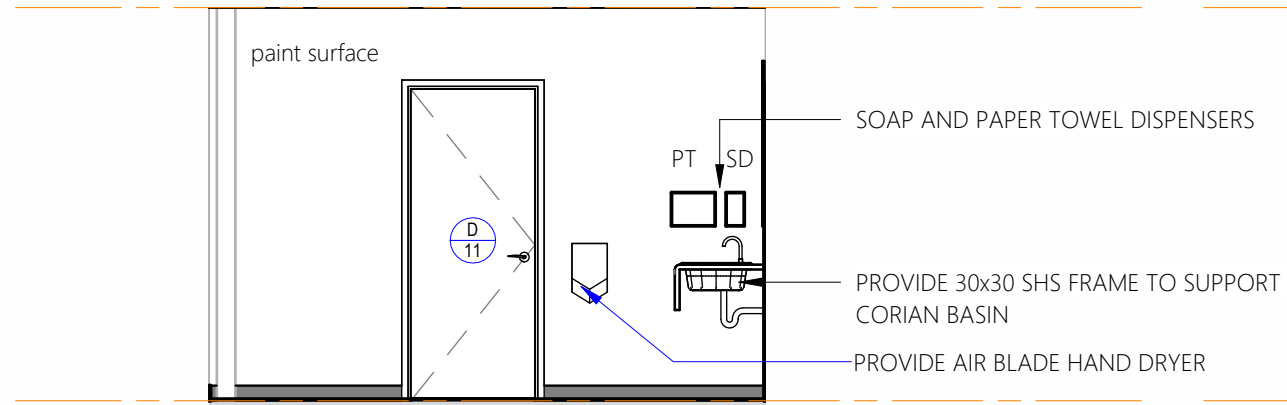


Elevation 4D
1 : 50

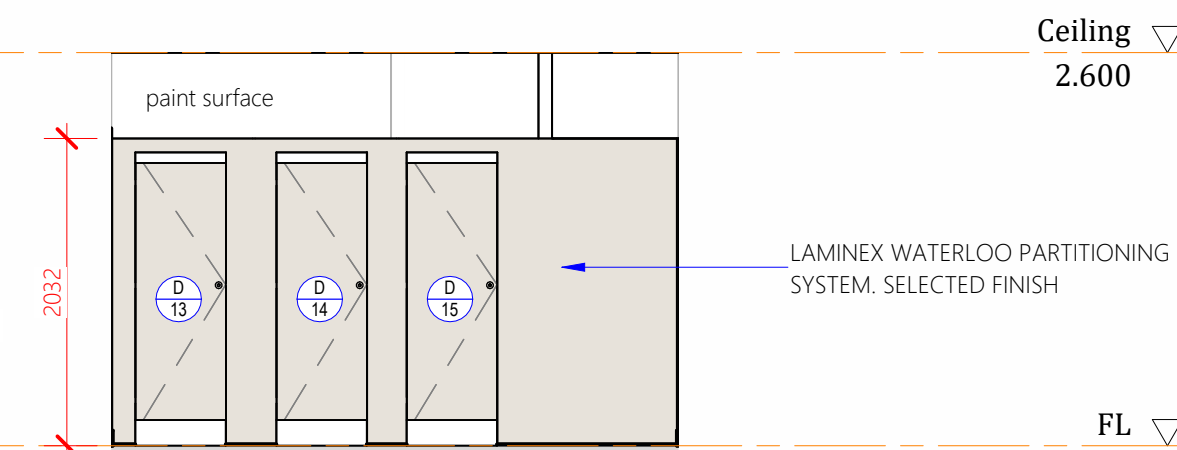


Elevation 4E
1 : 50

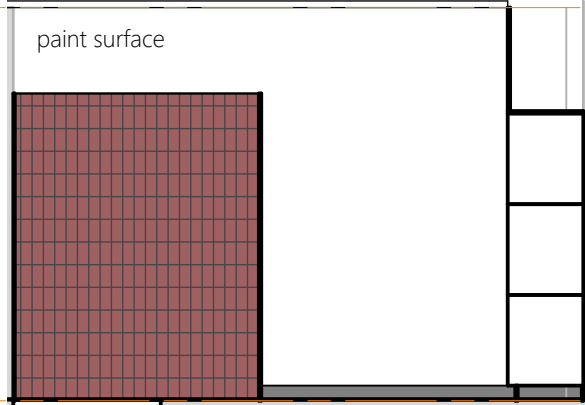


Elevation 4F
1 : 50

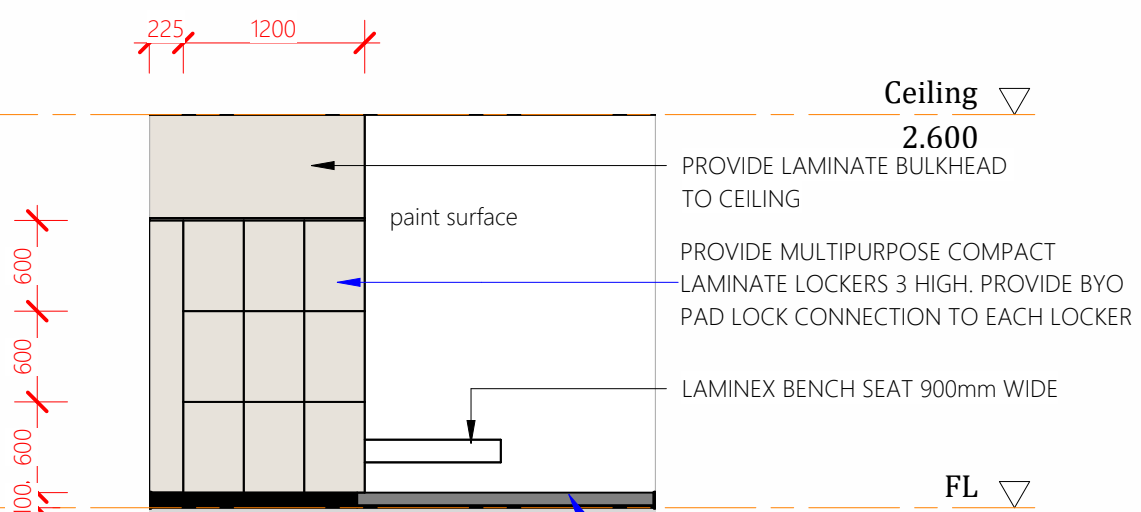


Elevation 4G
1 : 50

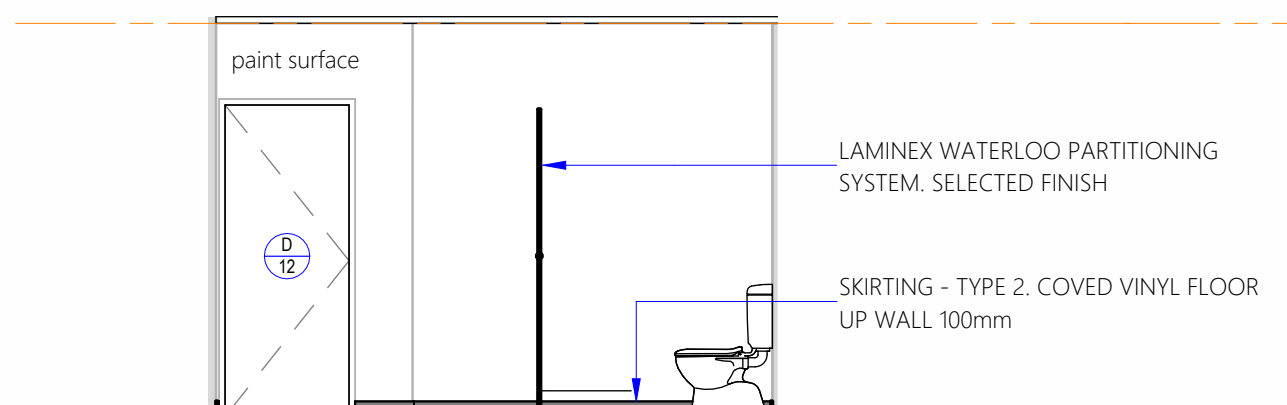


Elevation 4H
1 : 50

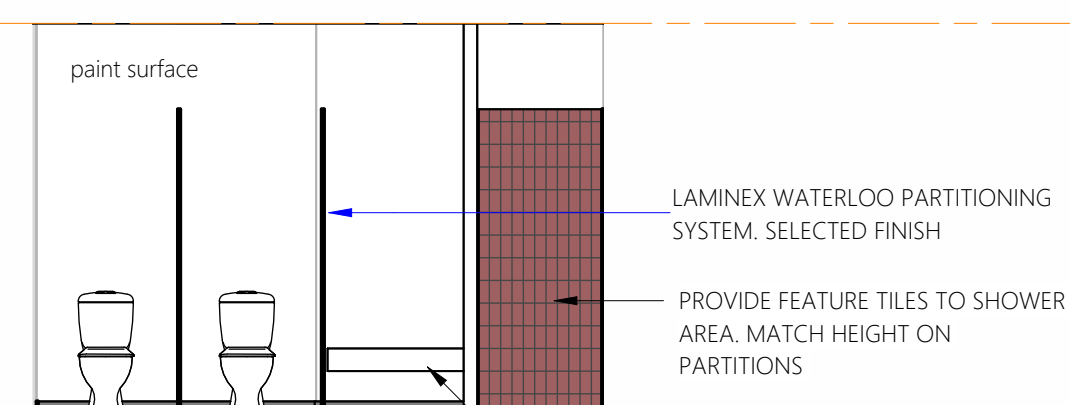

Elevation 4I
1 : 50

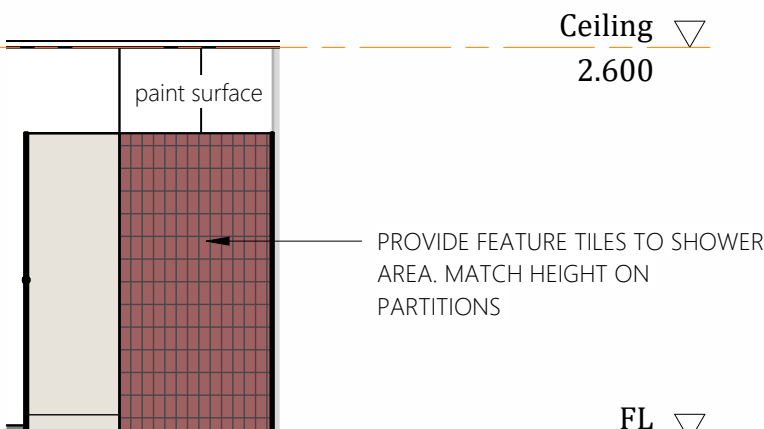

Elevation 4J
1 : 50

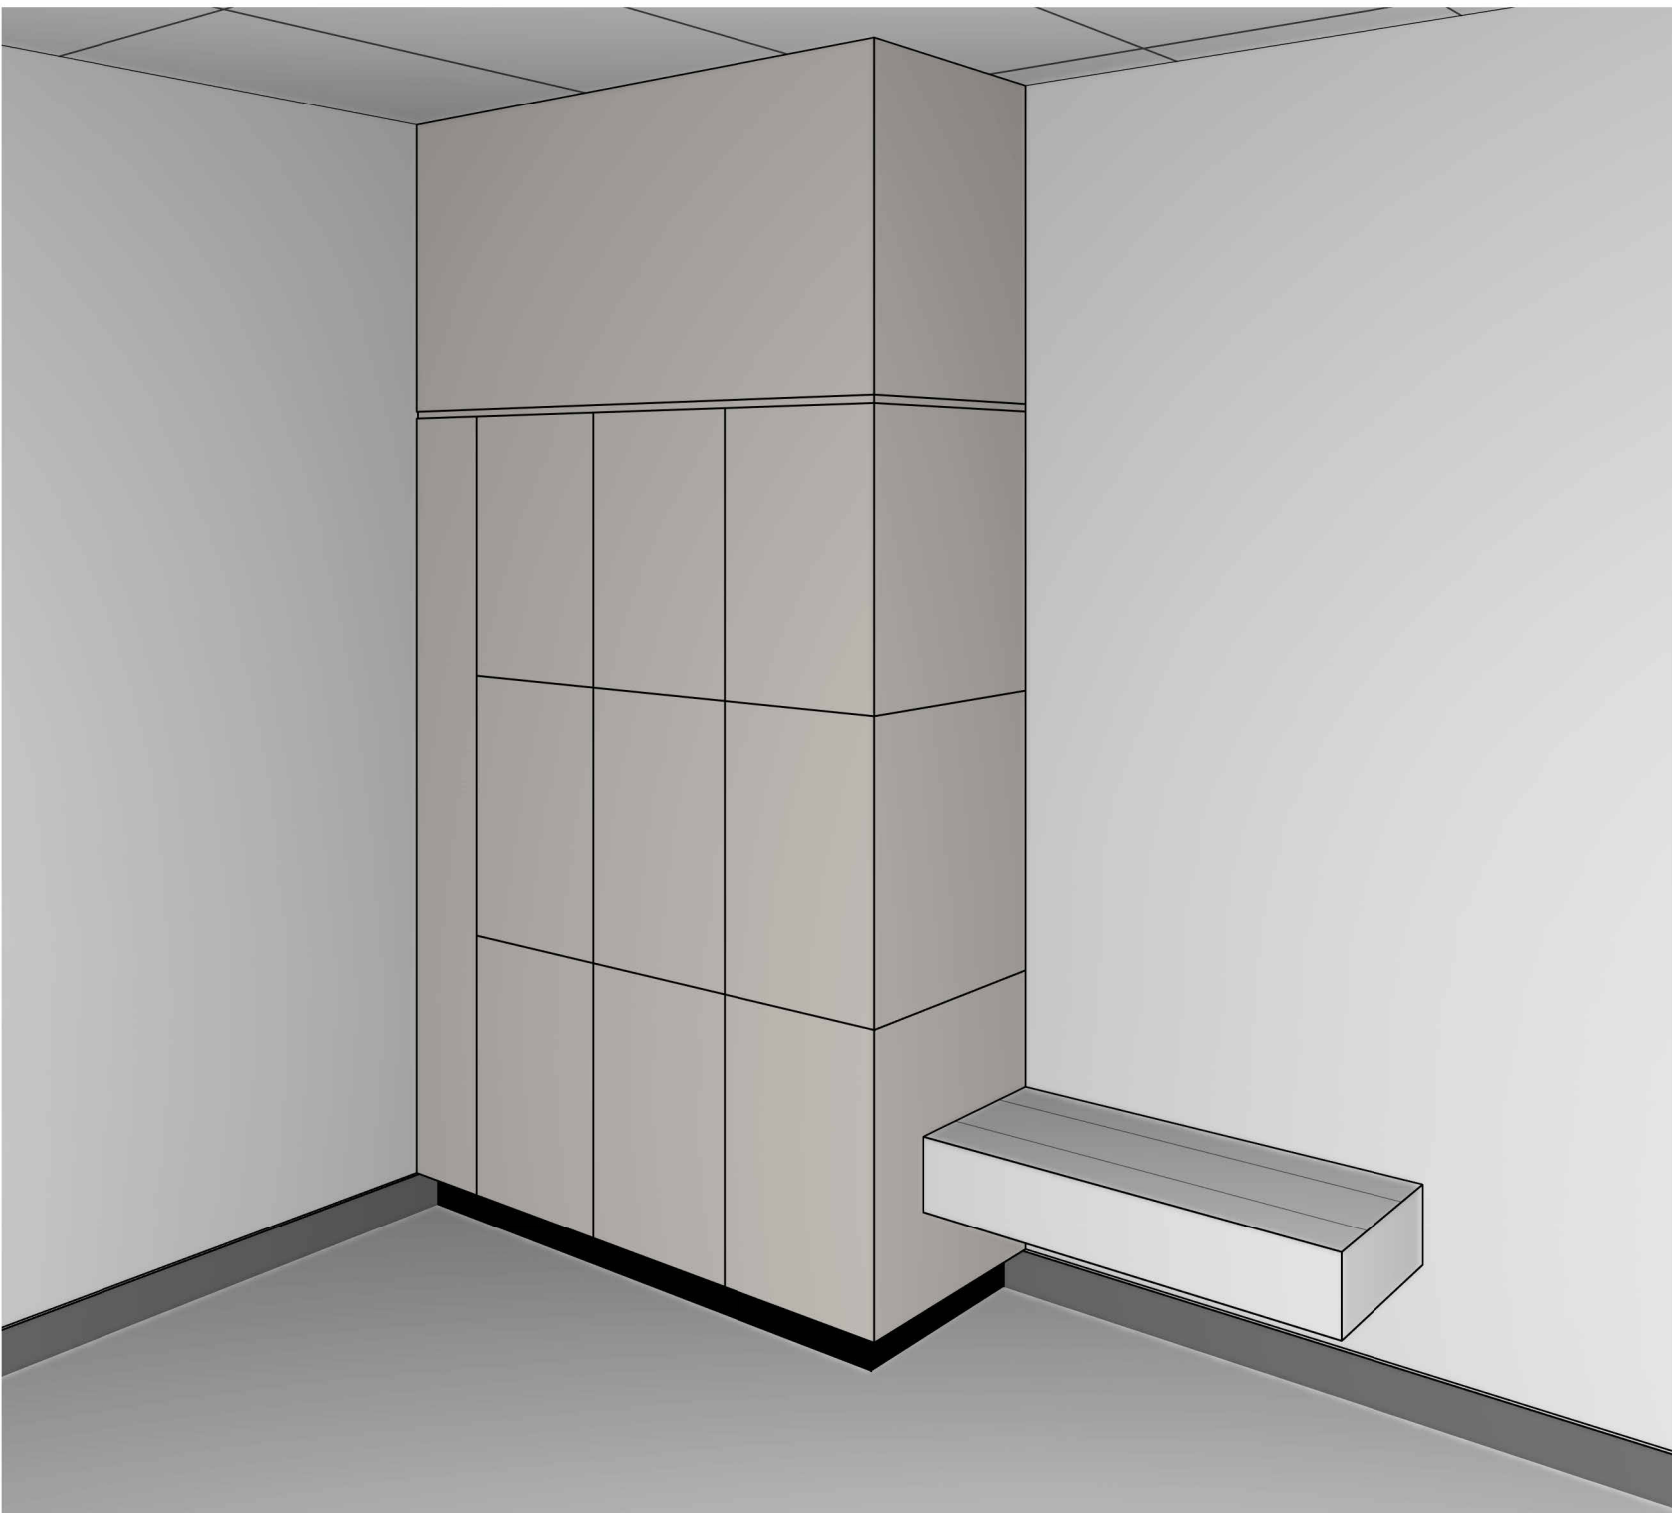

TENDER ISSUE



Project Details
REGISTRY REFURBISHMENT

Address
STANWELL POWER STATION

Drawing Title
INTERNAL ELEVATIONS 4 - FEMALE AMENITIES





0483 988 655 M
info@designelements.com.au E
QBCC No: 1247120 BDAQ No: 0001677

Scale: 1 : 50 Rev:
Date: MARCH 2026 **T1**
Drawn: NJB


Project No: Drawing No:

25_003 A1-603

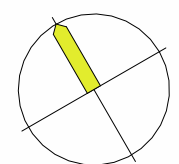

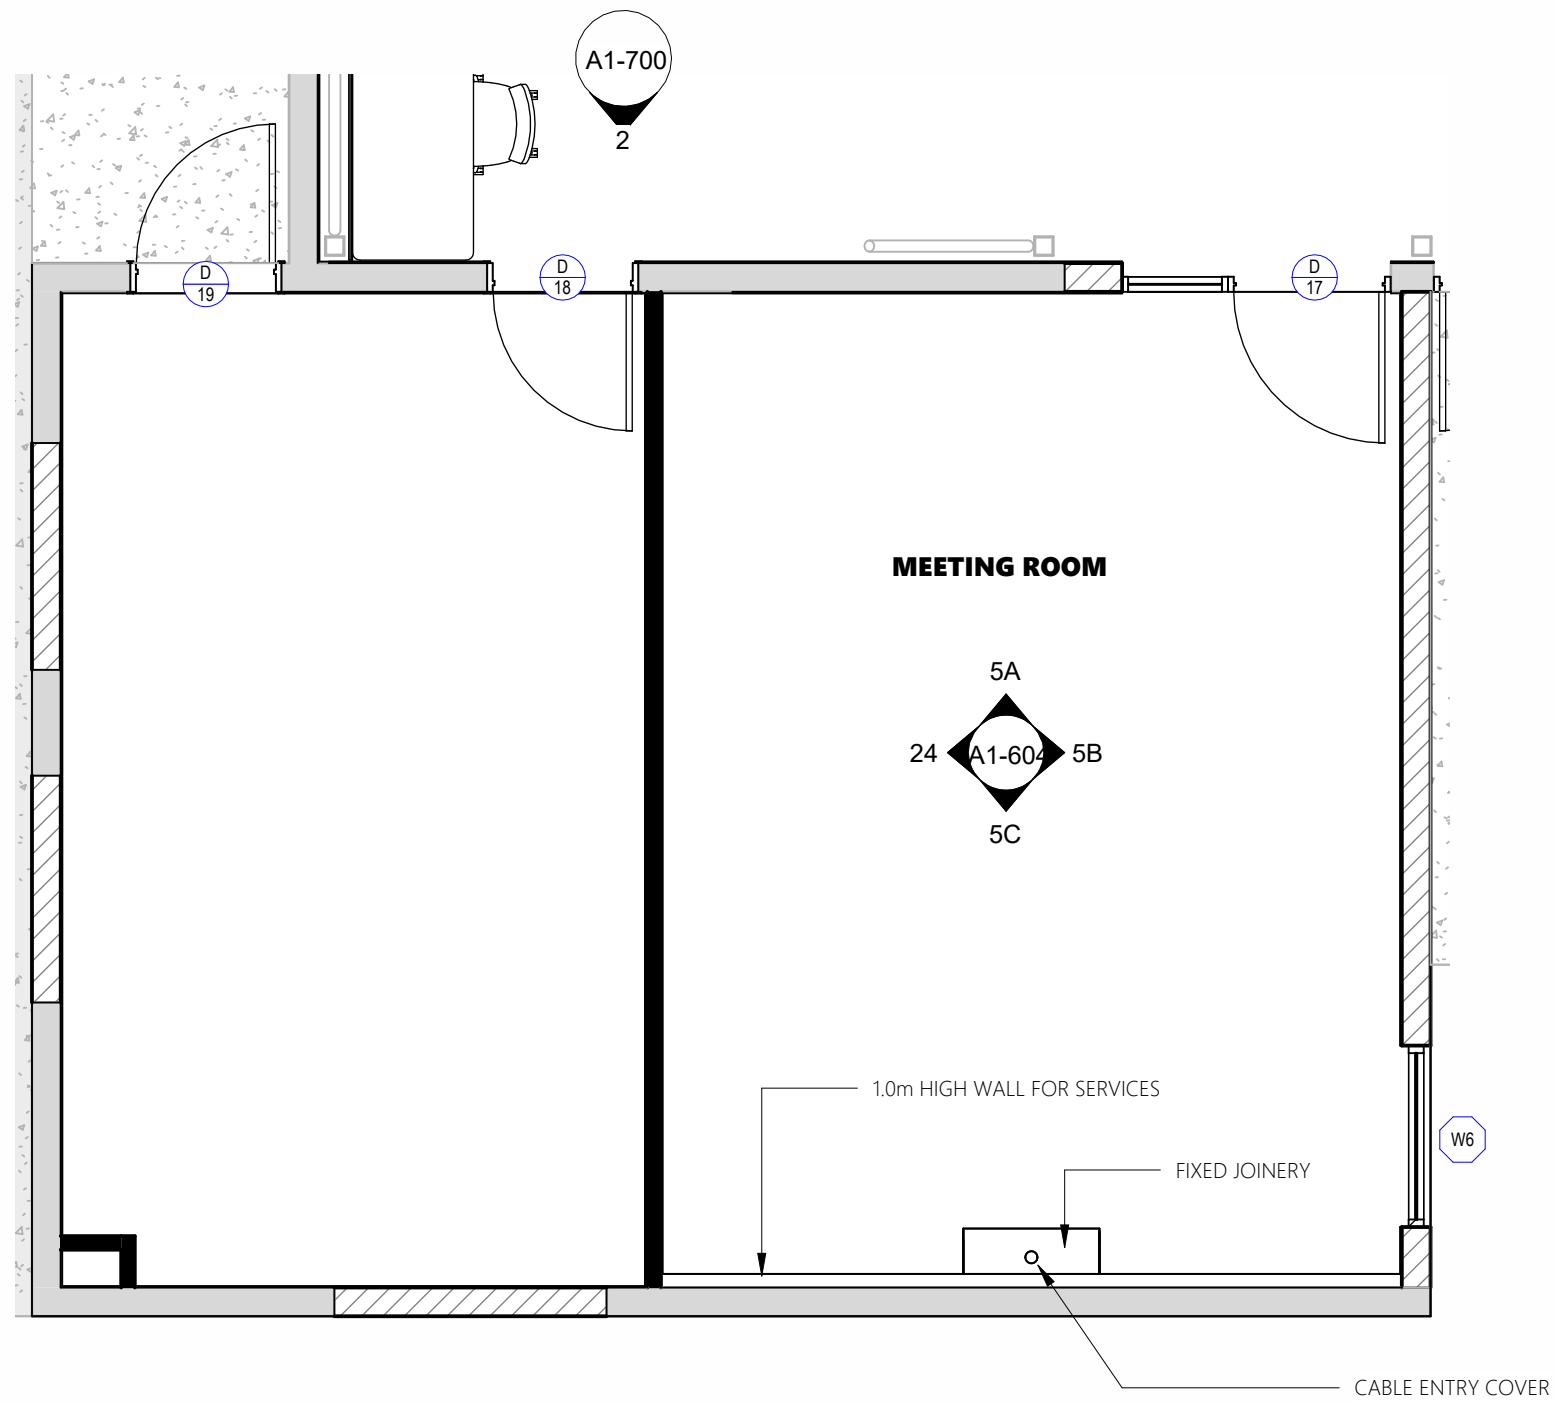


Internal Plan 5
1 : 50

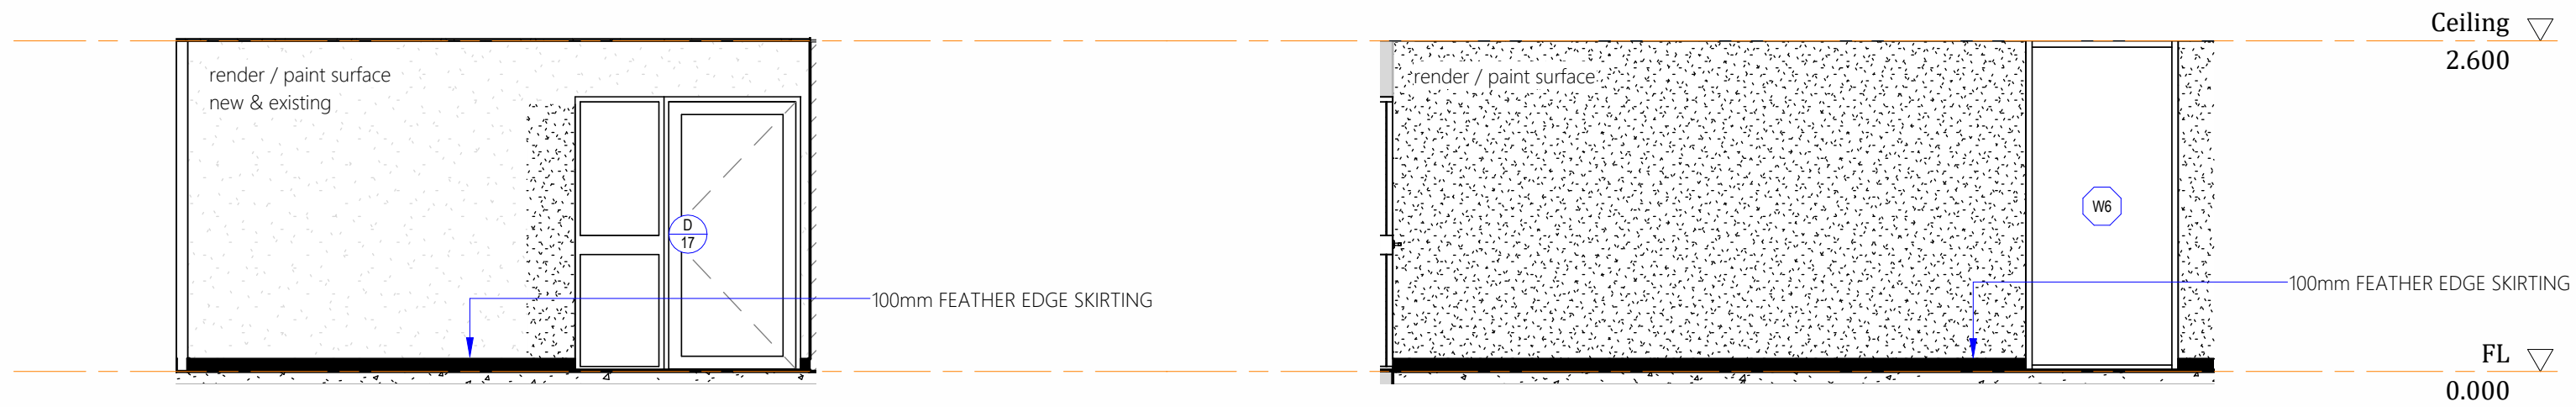


Elevation 5A
1 : 50

Elevation 5B
1 : 50

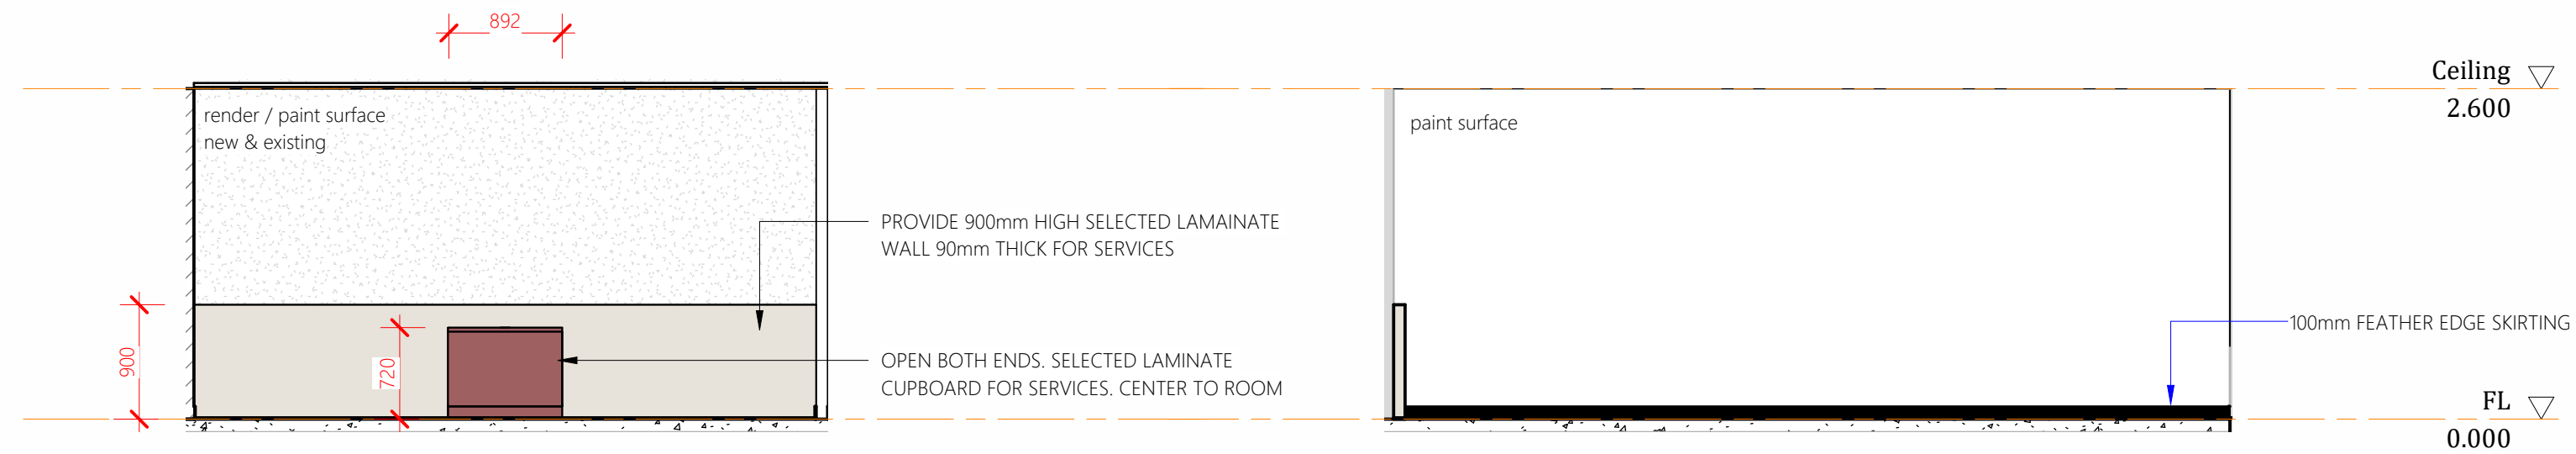

Elevation 5C
1 : 50

Elevation 5D
1 : 50

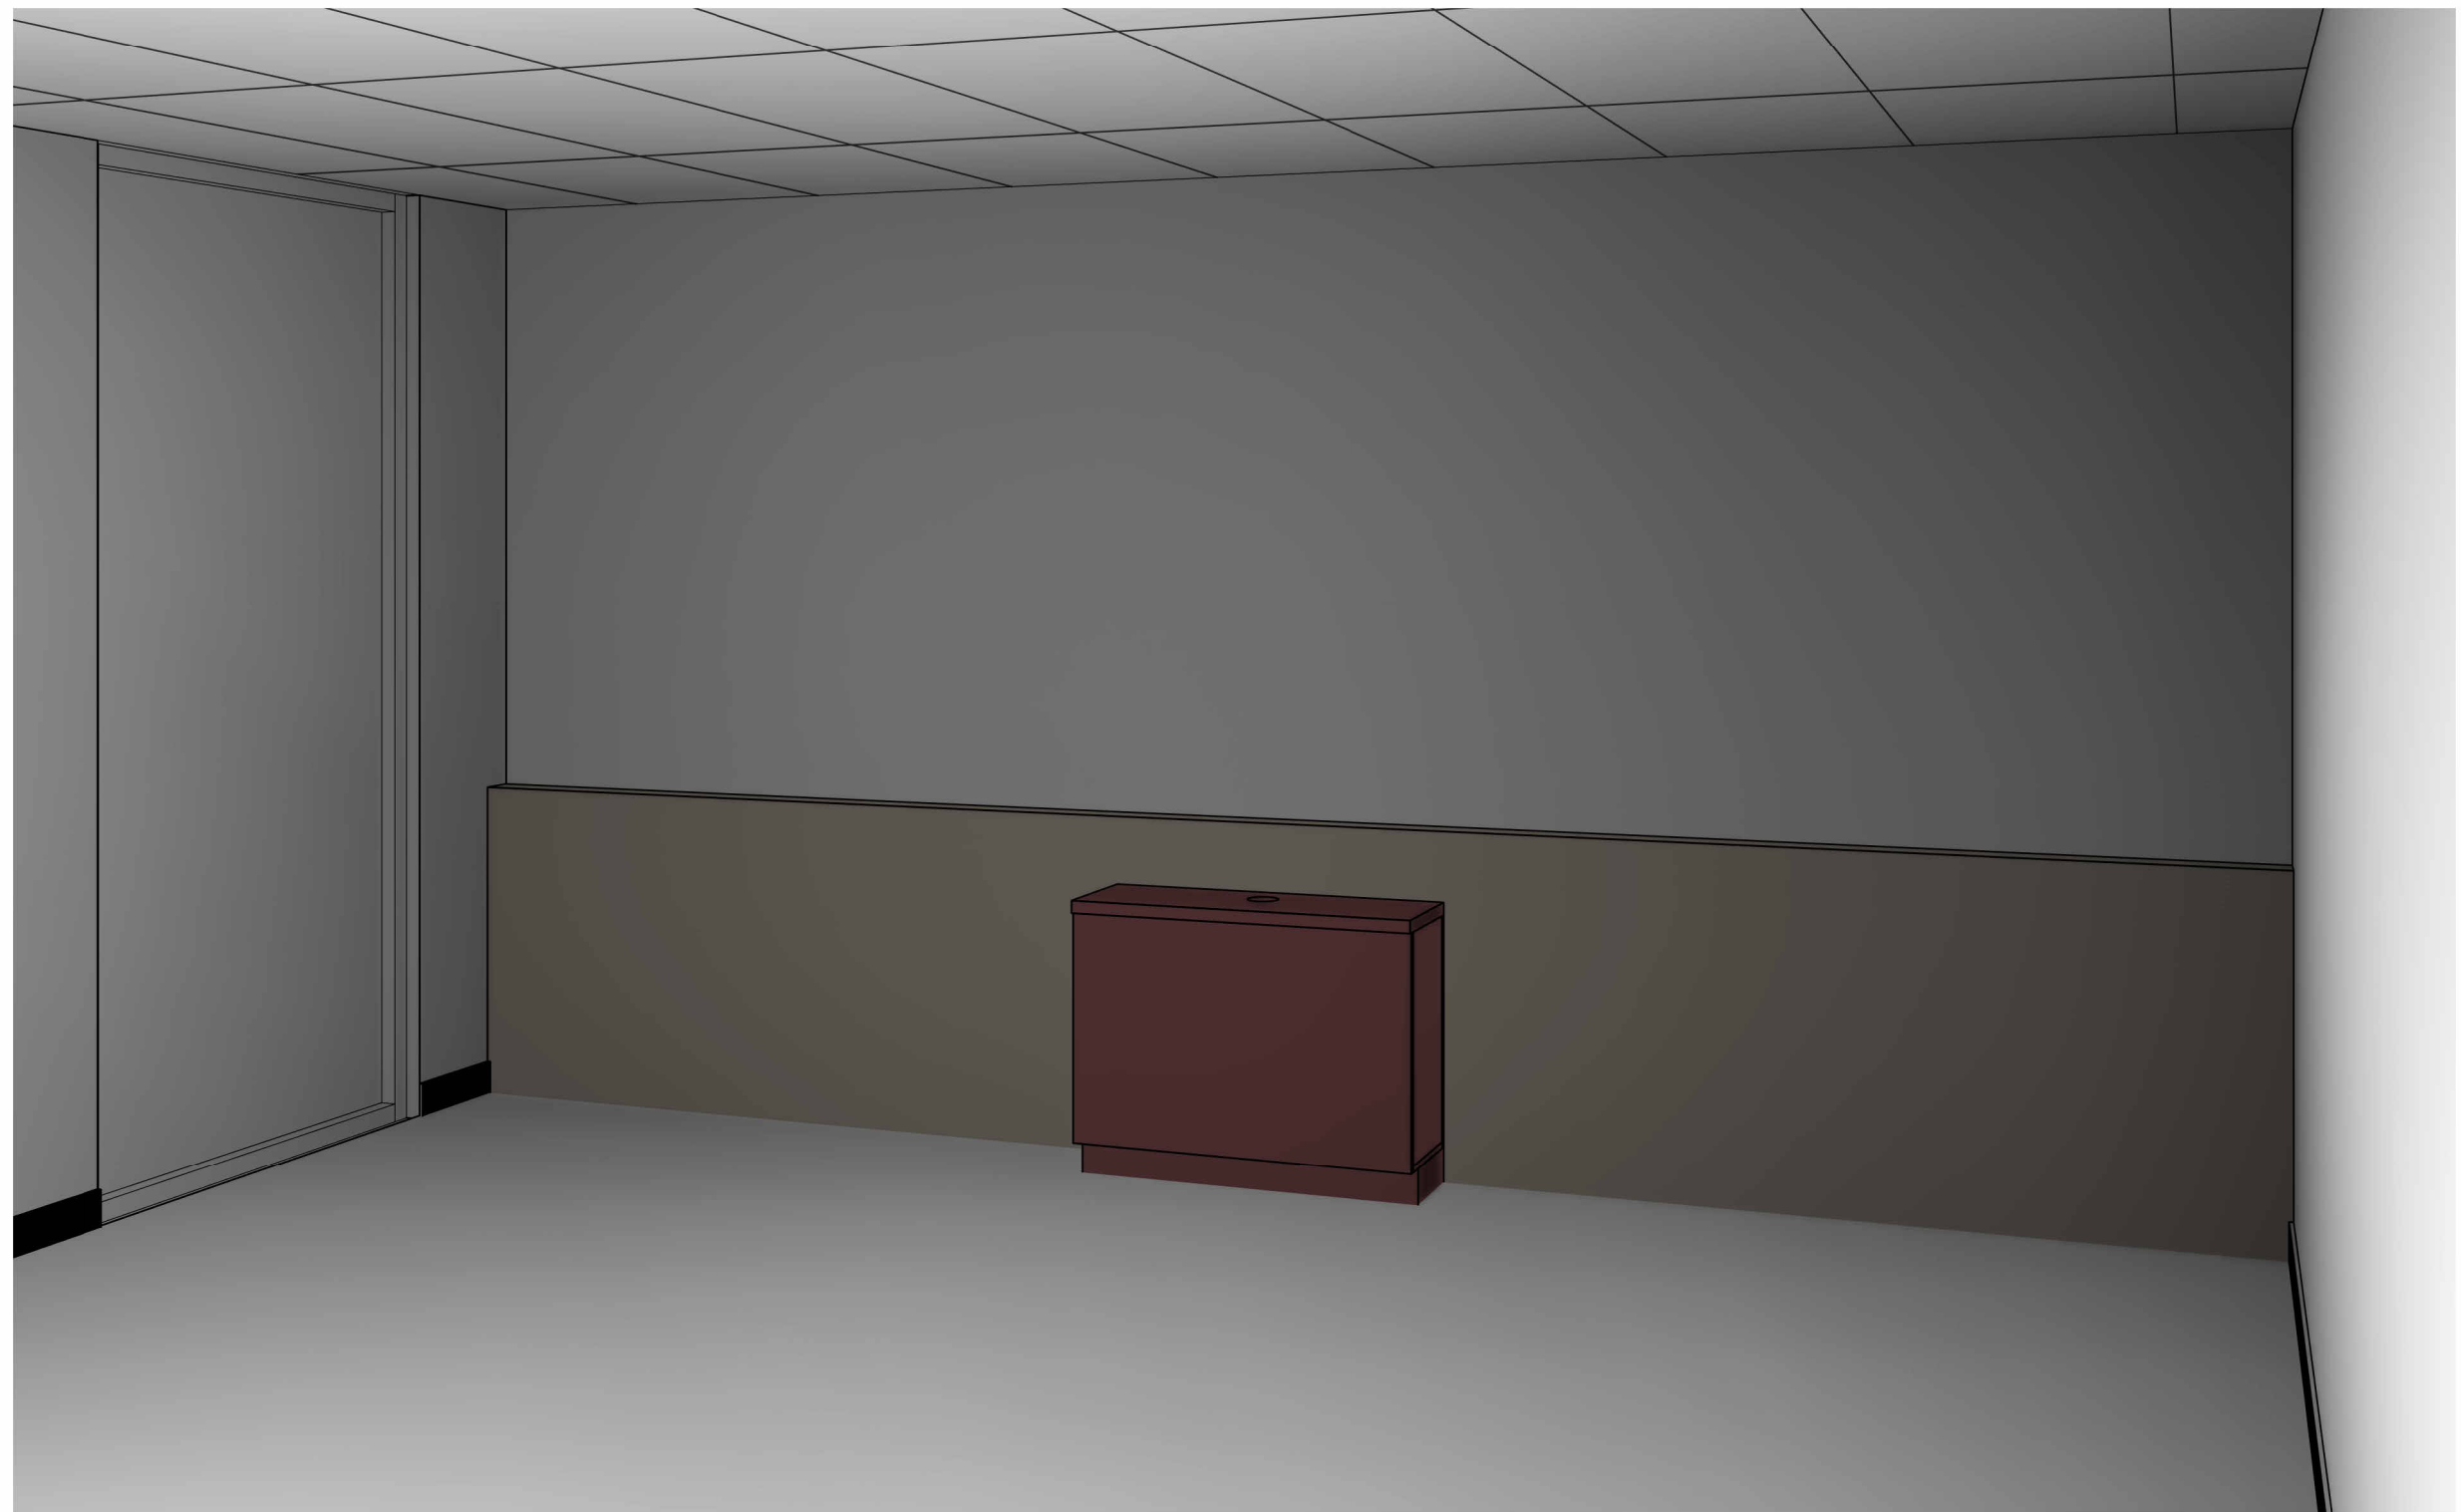

REVISIONS		
Rev	Description	Date
T1	TENDER ISSUE	12.03.2026

DO NOT SCALE THIS DRAWINGS



TENDER ISSUE




Project Details
REGISTRY REFURBISHMENT
Address
STANWELL POWER STATION
Drawing Title
INTERNAL ELEVATIONS 5 - MEETING ROOM

dezinelements
BUILDING DESIGNERS


0483 988 655 **M**
info@dezi nelements.com.au **E**

QBCC No: 1247120 BDAQ No: 0001677

Scale: 1 : 50	Rev: T1
Date: MARCH 2026	
Drawn: NJB	
Project No: 25_003	Drawing No: A1-604

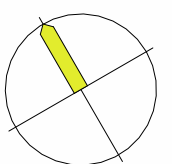


DOOR SCHEDULE	
DOOR NO.	DOOR TYPE
1	TYPE A
2	TYPE B
3	TYPE C
4	TYPE D
5	TYPE C
6	TYPE E
7	TYPE E
8	TYPE E
9	TYPE E
10	TYPE C
11	TYPE C
12	TYPE C
13	TYPE E
14	TYPE E
15	TYPE E
16	TYPE F
17	TYPE G
18	TYPE B
19	TYPE H

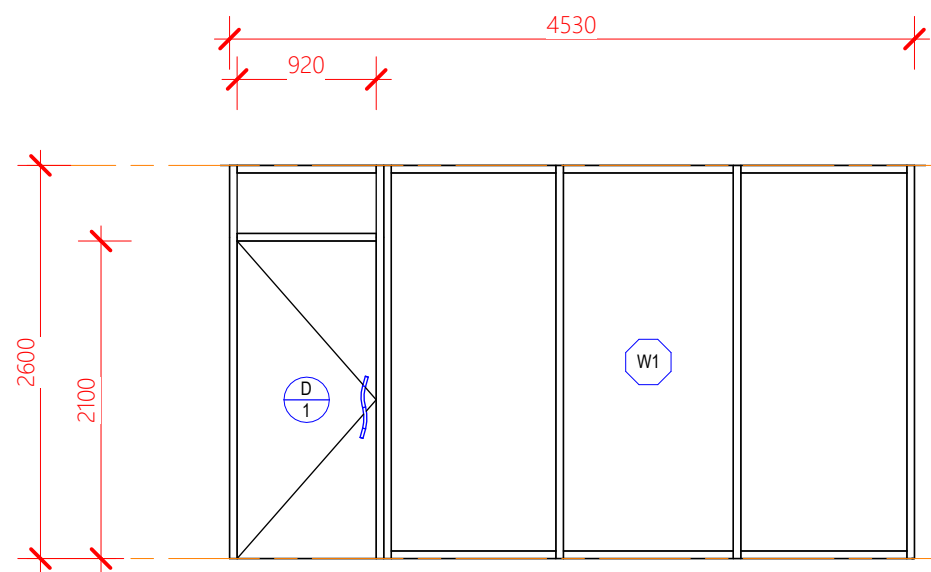


DOOR TYPE A

LOCATION: EXTERNAL
DOOR TYPE: HINGED ALUMINIUM FRAMED SINGLE DOOR
FRAME TYPE: G.JAMES 475 SERIES
FRAME FINISH: SELECTED POWDERCOAT
DOOR FINISH: SELECTED POWDERCOAT
INFILL: GREY SAFETY GLASS
THRESHOLD:
SEALS:
LOCK: REFER HARDWARE SCHEDULE
HARDWARE: DOOR CLOSER, DOOR STOP

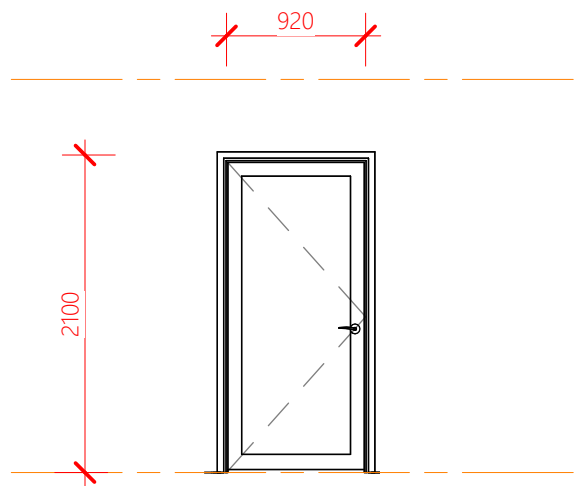


DOOR TYPE B

LOCATION: INTERNAL
DOOR TYPE: HINGED ALUMINIUM FRAMED SINGLE DOOR
FRAME TYPE: G.JAMES 475 SERIES
FRAME FINISH: SELECTED POWDERCOAT
DOOR FINISH: SELECTED POWDERCOAT
INFILL: GREY SAFETY GLASS
SEALS: NONE
LOCK: REFER HARDWARE SCHEDULE
HARDWARE: DOOR CLOSER, DOOR STOP

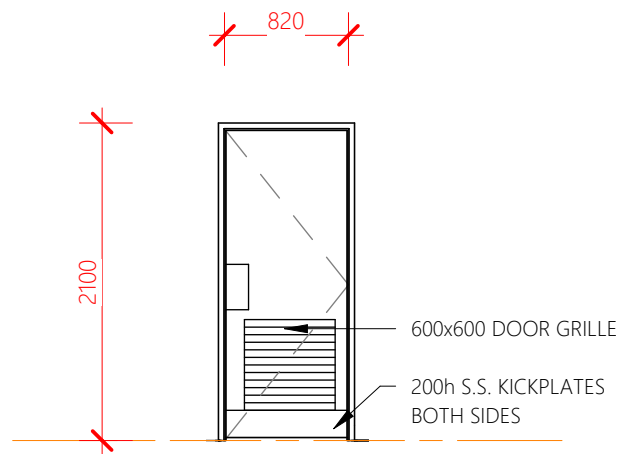


DOOR TYPE C

LOCATION: MALE & FEMALE AMENITIES
DOOR TYPE: 40mm HINGED SOLID CORE SINGLE DOOR
FRAME TYPE: TIMBER
FRAME FINISH: PAINT
DOOR FINISH: PAINT
SEALS: NONE
LOCK: PUSH PULL PLATES (NO LOCKING)
HARDWARE: KICK PLATES, DOOR CLOSER, DOOR STOP

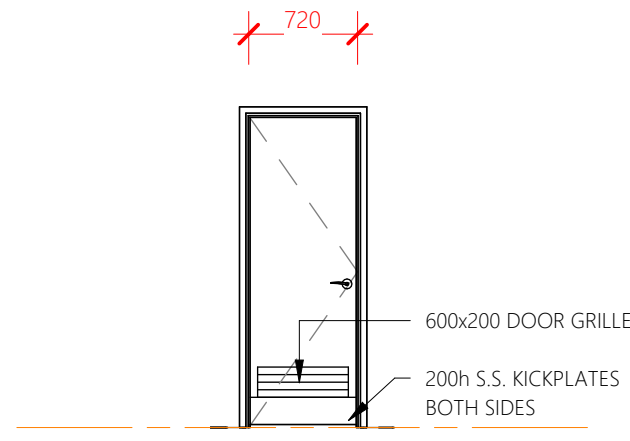


DOOR TYPE D

LOCATION: CLEANER
DOOR TYPE: 40mm HINGED SOLID CORE SINGLE DOOR
FRAME TYPE: TIMBER
FRAME FINISH: PAINT
DOOR FINISH: PAINT
SEALS: NONE
LOCK: REFER HARDWARE SCHEDULE
HARDWARE: KICK PLATES, DOOR CLOSER, DOOR STOP

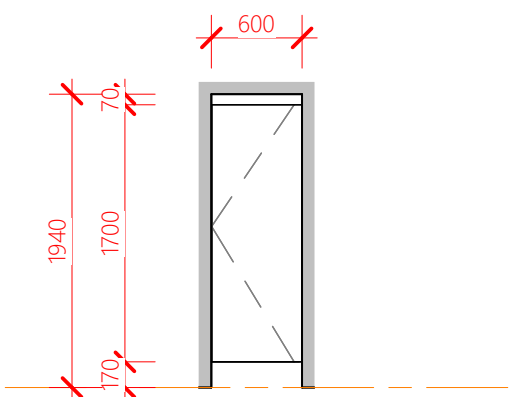


DOOR TYPE E

LOCATION: AMENITIES
DOOR TYPE: 13mm COMPACT LAMINATE PARTITION DOOR
FRAME TYPE: PROVIDE 30° PRIVACY BEVEL
DOOR FINISH: SELECTED LAMINATE
SEALS: NONE
LOCK: METLAM XCEL SLIDE LOCK & INDICATOR.
HARDWARE:

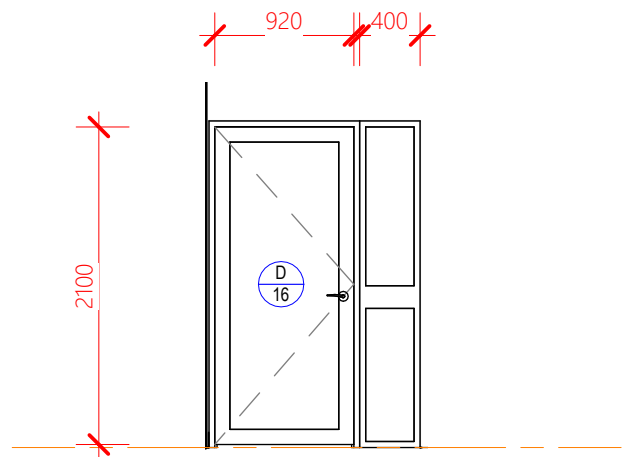


DOOR TYPE F

LOCATION: EXTERNAL
DOOR TYPE: HINGED ALUMINIUM FRAMED SINGLE DOOR
FRAME TYPE: G.JAMES 475 SERIES
FRAME FINISH: SELECTED POWDERCOAT
DOOR FINISH: SELECTED POWDERCOAT
INFILL: GREY SAFETY GLASS
THRESHOLD:
SEALS:
LOCK: REFER HARDWARE SCHEDULE
HARDWARE: DOOR CLOSER, DOOR STOP

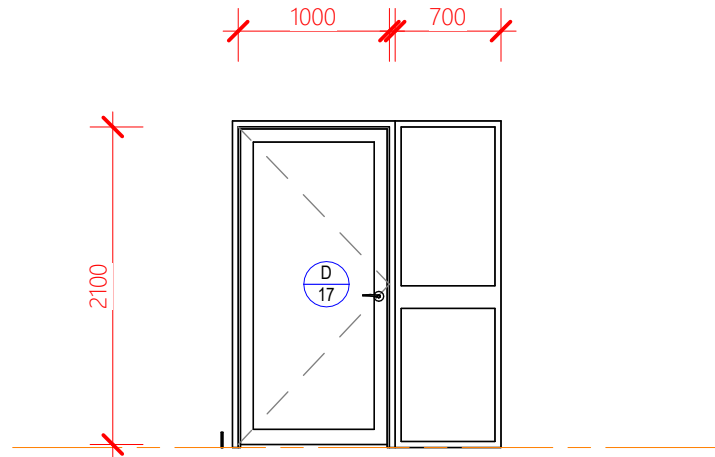

DOOR TYPE G


LOCATION: INTERNAL
DOOR TYPE: HINGED ALUMINIUM FRAMED SINGLE DOOR
FRAME TYPE: G.JAMES 475 SERIES
FRAME FINISH: SELECTED POWDERCOAT
DOOR FINISH: SELECTED POWDERCOAT
INFILL: GREY SAFETY GLASS
SEALS: NONE
LOCK: REFER HARDWARE SCHEDULE
HARDWARE: DOOR CLOSER, DOOR STOP

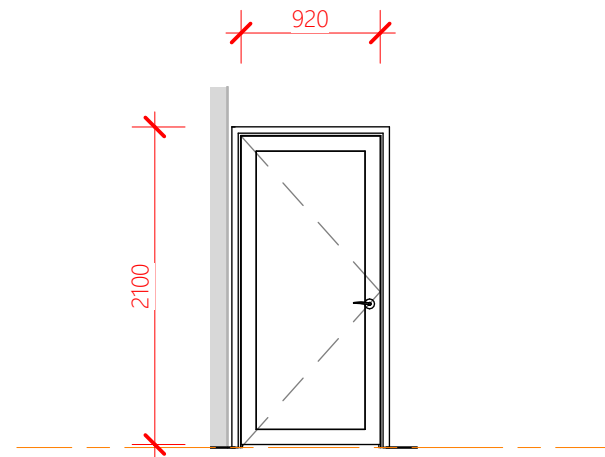

DOOR TYPE H


LOCATION: EXTERNAL
DOOR TYPE: HINGED ALUMINIUM FRAMED SINGLE DOOR
FRAME TYPE: G.JAMES 475 SERIES
FRAME FINISH: SELECTED POWDERCOAT
DOOR FINISH: SELECTED POWDERCOAT
INFILL: GREY SAFETY GLASS
THRESHOLD:
SEALS:
LOCK: REFER HARDWARE SCHEDULE
HARDWARE: DOOR CLOSER, DOOR STOP

WINDOW SCHEDULE	
WINDOW NO.	WINDOW TYPE
1	TYPE A
2	TYPE B
3	TYPE B
4	TYPE C
5	TYPE B
6	TYPE C

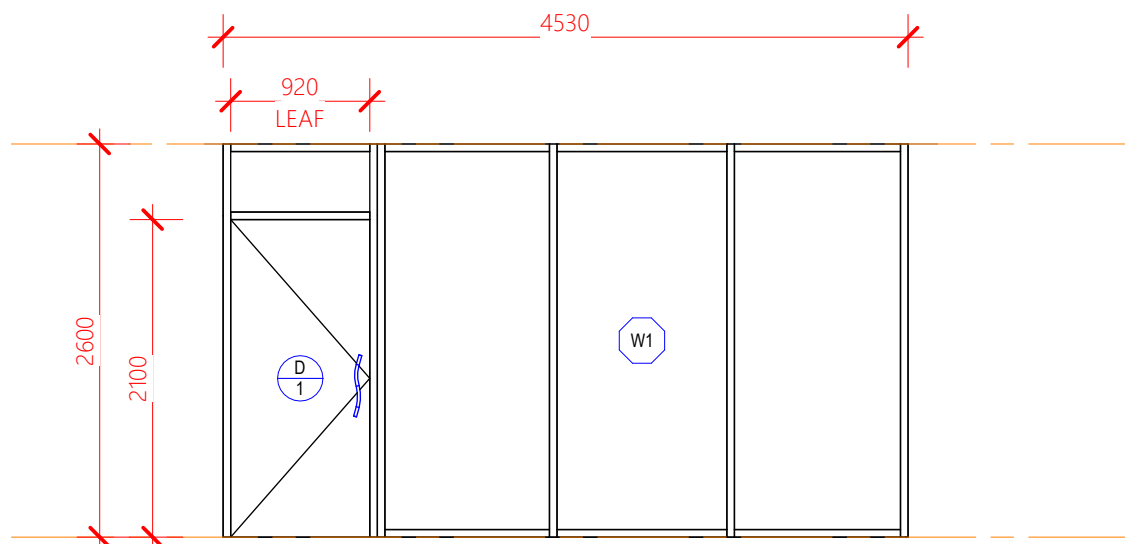


WINDOW TYPE A

LOCATION: EXTERNAL
FRAME TYPE: G.JAMES 475 SERIES
FRAME FINISH: SELECTED POWDERCOAT
WINDOW: FIXED GLASS
GLASS: SAFETY GLASS

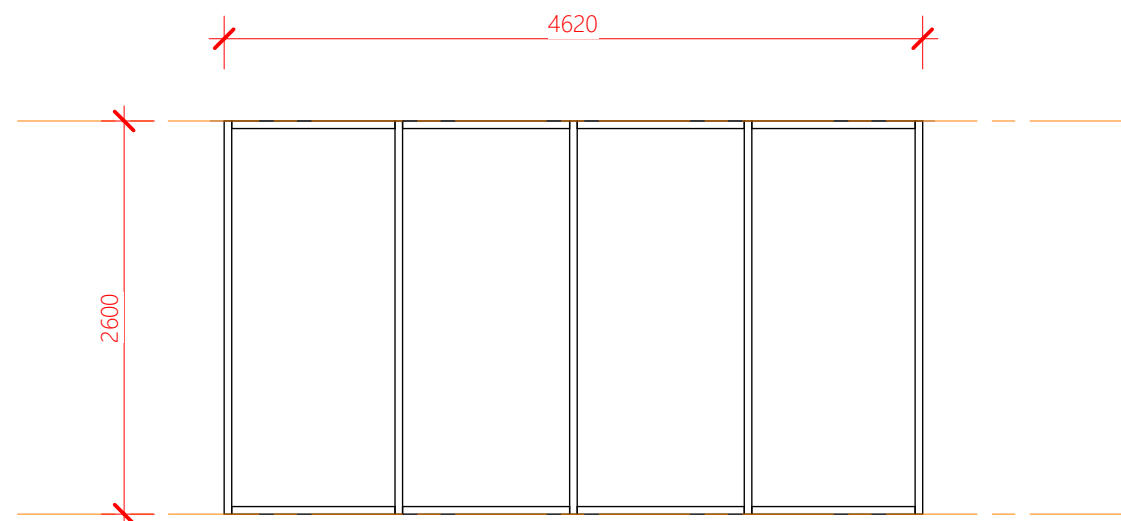


WINDOW TYPE B

LOCATION: EXTERNAL
FRAME TYPE: G.JAMES 475 SERIES
FRAME FINISH: SELECTED POWDERCOAT
WINDOW: FIXED GLASS
GLASS: SAFETY GLASS

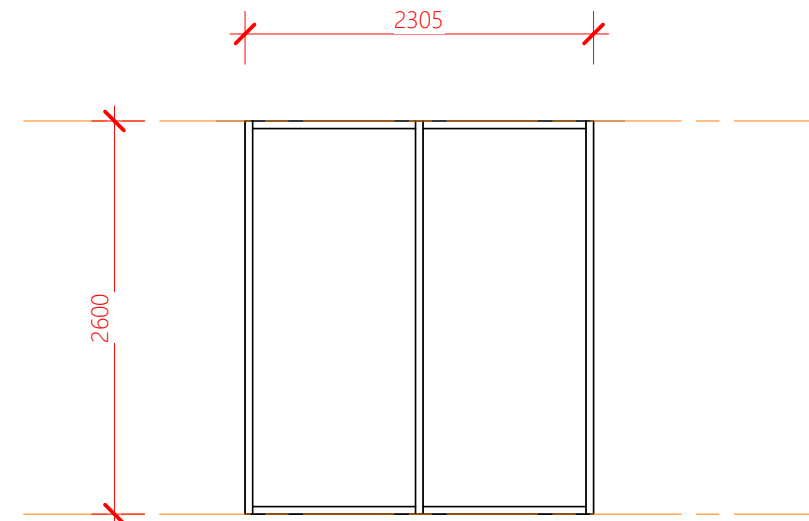

WINDOW TYPE C

LOCATION: EXTERNAL
FRAME TYPE: G.JAMES 475 SERIES
FRAME FINISH: SELECTED POWDERCOAT
WINDOW: FIXED GLASS
GLASS: SAFETY GLASS

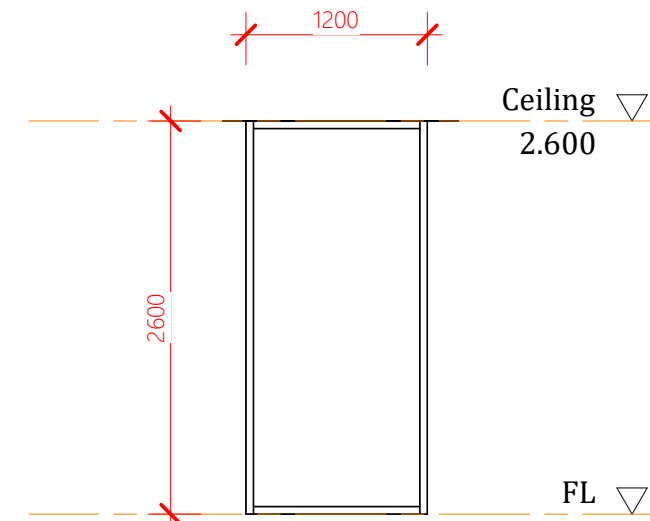

WINDOW TYPE C

LOCATION: EXTERNAL
FRAME TYPE: G.JAMES 475 SERIES
FRAME FINISH: SELECTED POWDERCOAT
WINDOW: FIXED GLASS
GLASS: SAFETY GLASS

REVISIONS

Rev	Description	Date
T1	TENDER ISSUE	12.03.2026

DO NOT SCALE THIS DRAWINGS



TENDER ISSUE

Client

Project Details

REGISTRY REFURBISHMENT

Address

STANWELL POWER STATION

Drawing Title

WINDOW AND DOOR SCHEDULES

0483 988 655 **M**
info@dezi nelements.com.au **E**
QBCC No: 1247120 BDAQ No: 0001677

Scale: 1 : 50

Date: MARCH 2026

Drawn: NJB

Rev: **T1**

Project No: Drawing No:

25_003 A1-700

12/03/2026 6:32:38 PM

