


**REFER TO SITE PLAN & CONSULTANT
DRAWINGS FOR EXTERNAL SERVICES**

REVISIONS		
Rev	Description	Date
T1	TENDER ISSUE	12.03.2026

DO NOT SCALE THIS DRAWINGS


**CONFIRM HEIGHTS AND LEVELS
ON SITE**

**CONFIRM UNDERGROUND
SERVICES ON SITE**

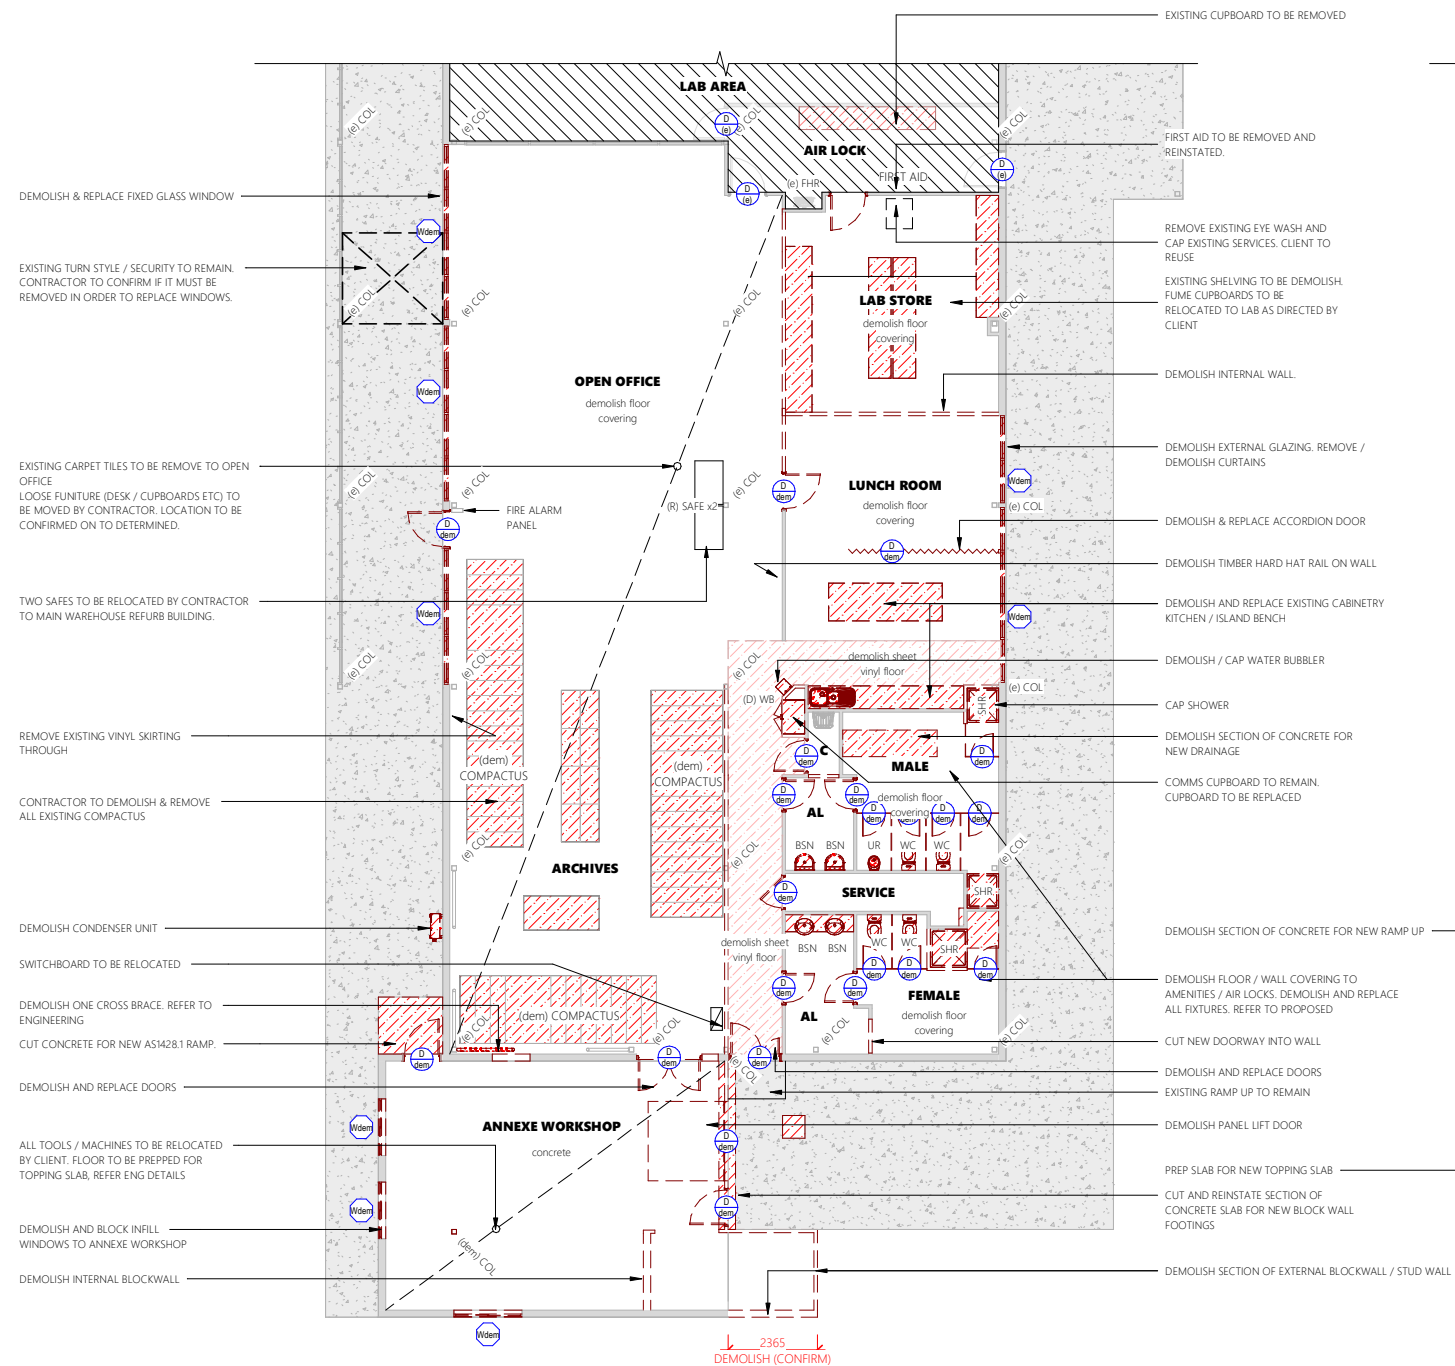


Existing Registry Floor Plan

1 : 100

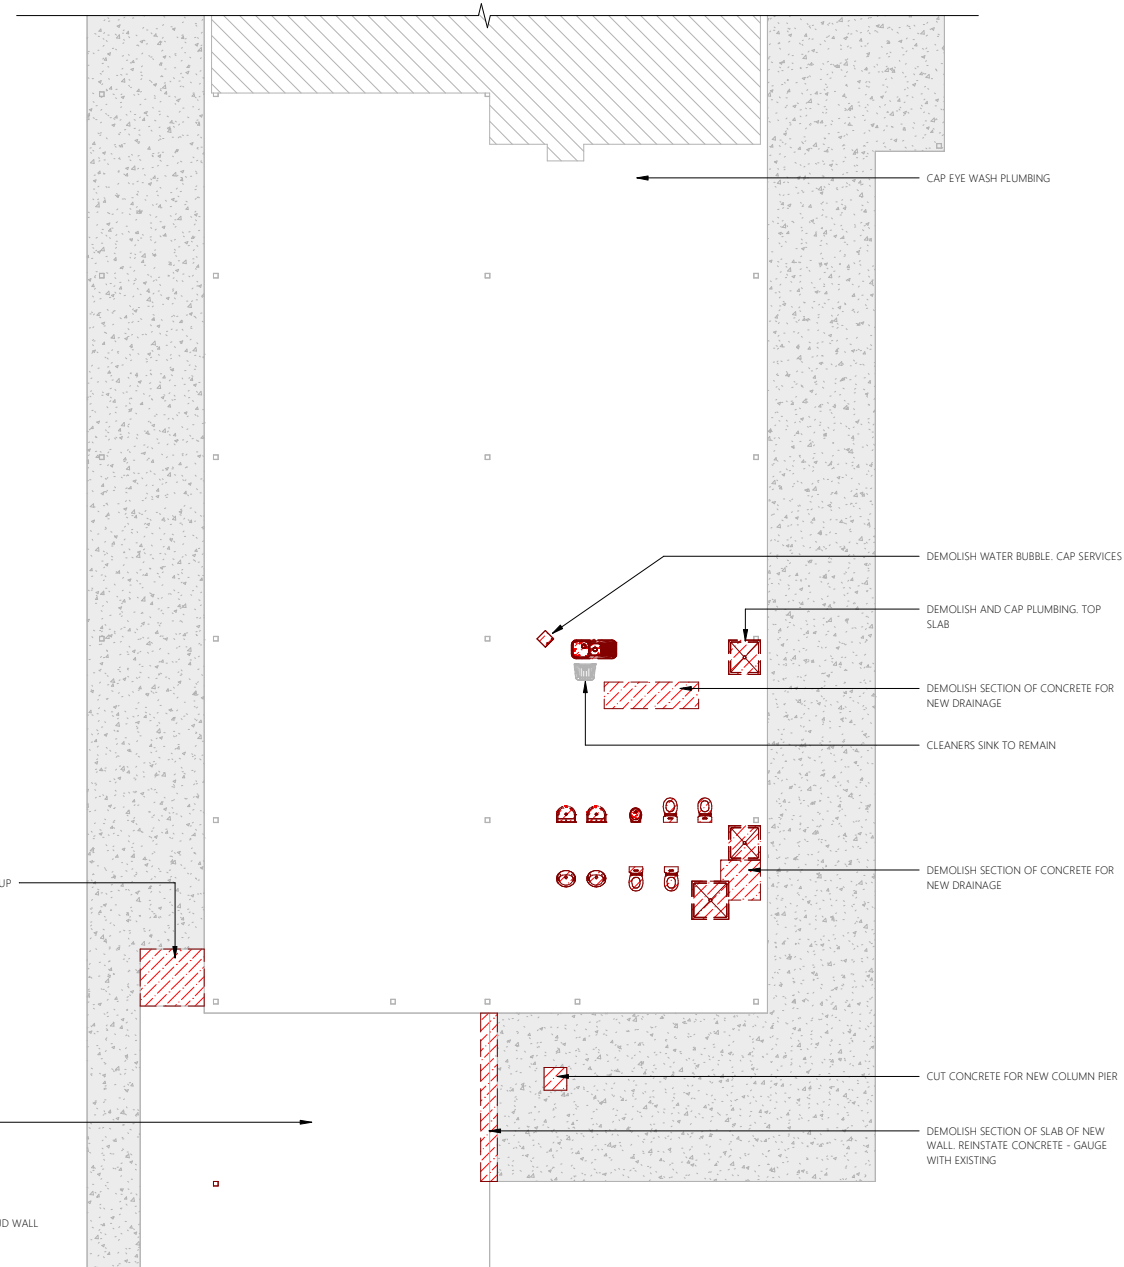

Existing Slab Plan

1 : 100

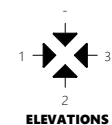

TENDER ISSUE

Client



Project Details

REGISTRY REFURBISHMENT

Address

STANWELL POWER STATION

Drawing Title

**EXISTING FLOOR & SLAB
PLAN**



0483 988 655 **M**

info@dezignelements.com.au 

QBCC No: 1247120 BDAQ No: 0001677

Scale: 1 : 100 Rev:

Scale: 1:100 Rev:
 Date: MARCH 2026

Date: MARCH 2020 **T1**
Drawn: NJB 30:22

Project No: _____ Drawing No: _____

Project No: Drawing No: 03/20


25_003 A1-200 12/0

2/03/2026 6:30:22 PM

LIGHTS AND AC FIXTURES SHOWN FOR INDICATION ONLY. CONFIRM ON SITE AND READ IN CONJUNCTION WITH CONSULTANT DRAWINGS

REVISIONS		
Rev	Description	Date
T1	TENDER ISSUE	12.03.2026


DO NOT SCALE THIS DRAWINGS

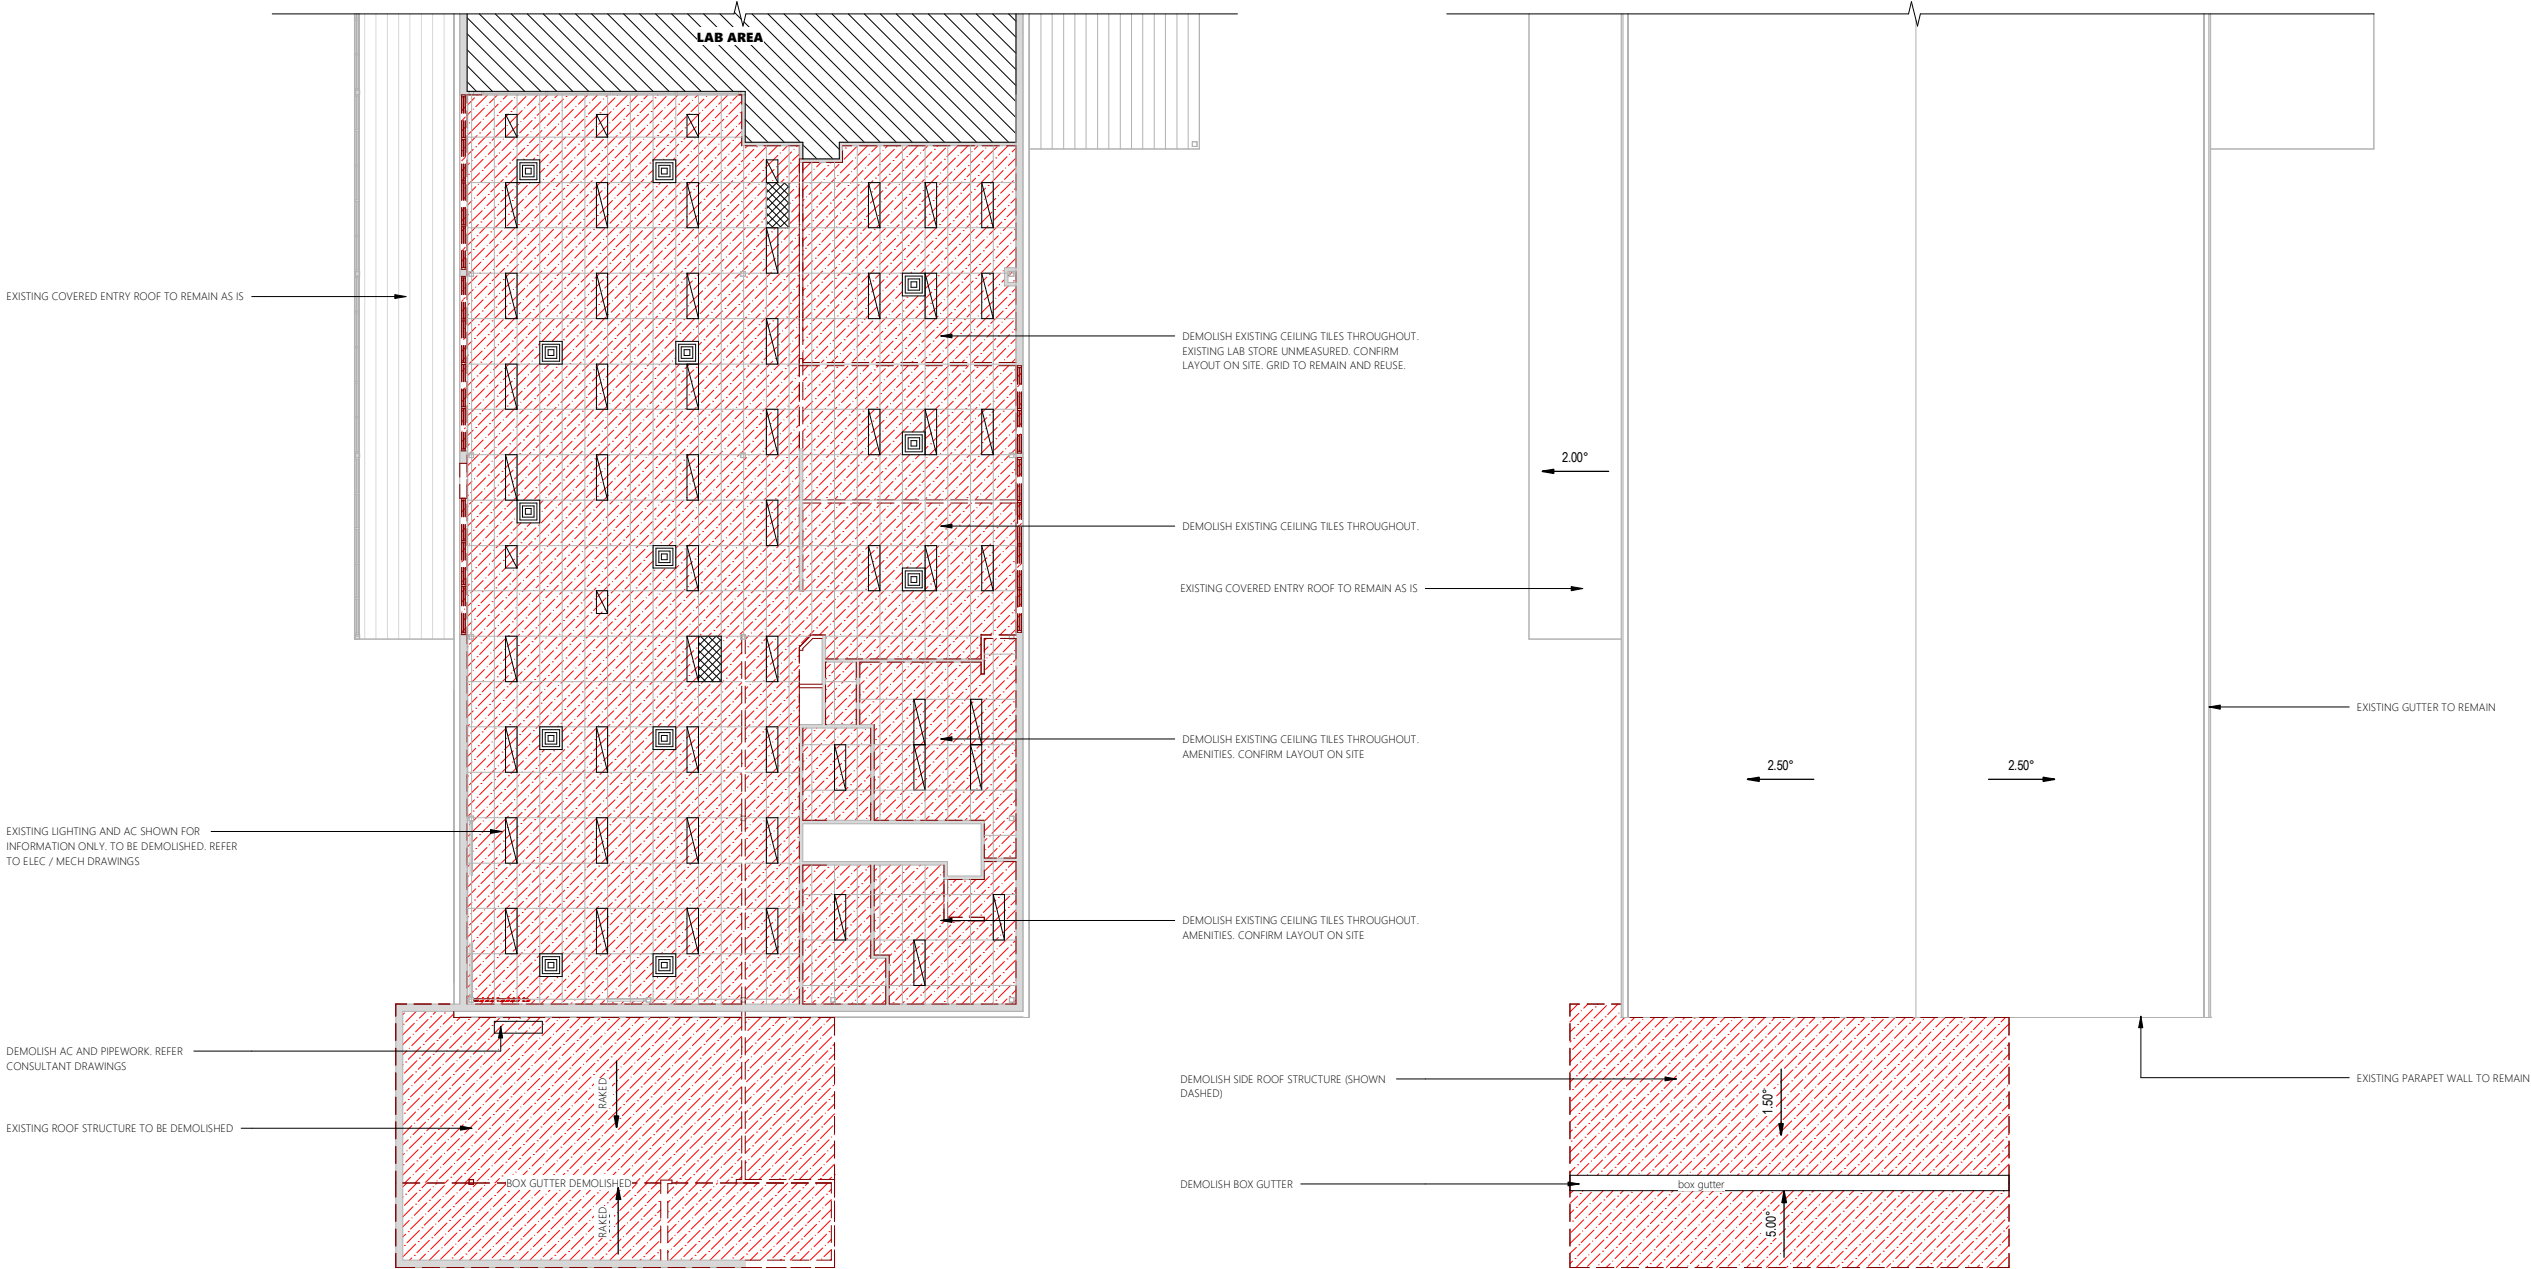

Existing Ceiling Plan



Existing Roof Plan

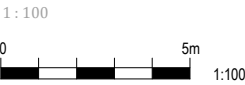

TENDER ISSUE



Project Details
REGISTRY REFURBISHMENT

Address
STANWELL POWER STATION

Drawing Title
EXISTING CEILING & ROOF PLAN

dezi^{ne}elements
BUILDING DESIGNERS
0483 988 655 M
info@dezi^{ne}elements.com.au E
QBCC No: 1247120 BDAQ No: 0001677

Scale: 1 : 100 Rev: T1
Date: MARCH 2026
Drawn: NJB
Project No: 25_003 Drawing No: A1-201



REVISIONS		
Rev	Description	Date
T1	TENDER ISSUE	12.03.2026

DO NOT SCALE THIS DRAWINGS



TENDER ISSUE

Client



Project Details

REGISTRY REFURBISHMENT

Address

STANWELL POWER STATION


Drawing Title

EXISTING ELEVATIONS



BUILDING DESIGNERS
0483 988 655 M
info@deziignelements.com.au E
QBCC No: 1247120 BDAQ No: 0001677

Scale: 1 : 100
Date: MARCH 2026
Drawn: NJB


Rev: T1
Project No: 25_003
Drawing No: A1-202

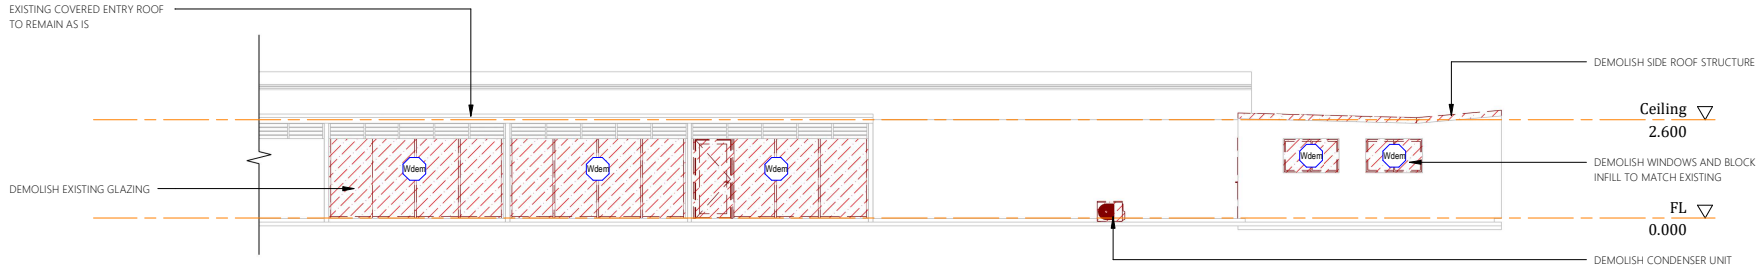

Existing Elevation 1
1 : 100

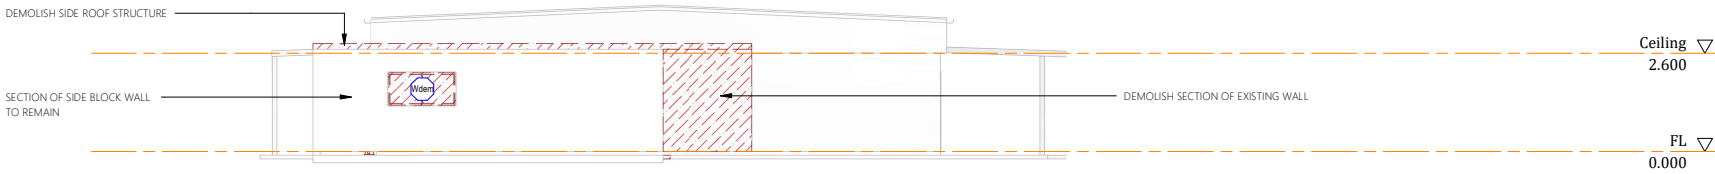

Existing Elevation 2
1 : 100

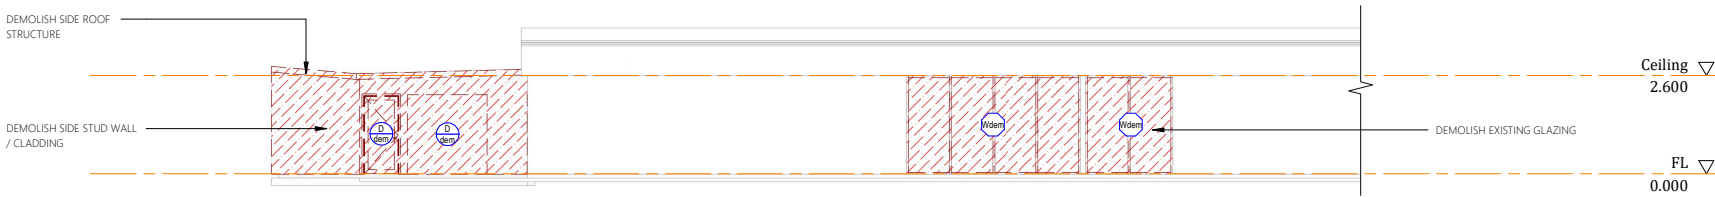

Existing Elevation 3
1 : 100

REVISIONS

Rev	Description	Date
T1	TENDER ISSUE	12.03.2026

DO NOT SCALE THIS DRAWINGS

KEYNOTE LEGEND

(e)	Existing
dem	Demolish
(R)	Remove / Reinstate

BSN	Basin
COL	Column
CON	Condenser
CPD	Cupboard
CS	Cleaners Sink
CT	Cooktop
DP	Downpipe
DW	Dish Washer
FAP	Fire Alarm Panel
FHR	Fire Hose Reel
FR	Fridge (By Client)
HD	Hand Driver (Air Blade)
L	Locker
OV	Oven
RH	Range Hood
DW	Dish Washer
SK	Sink
SB	Switch Board
UR	Urinal

TENDER ISSUE



Project Details
REGISTRY REFURBISHMENT


Address
STANWELL POWER STATION

Drawing Title
PROPOSED FLOOR & SLAB PLAN





0483 988 655 M
info@dezignelements.com.au E
QBCC No: 1247120 BDAQ No: 0001677


Scale:	1 : 100	Rev:	T1
Date:	MARCH 2026	Drawn:	NJB
Project No:	25_003	Drawing No:	A1-300

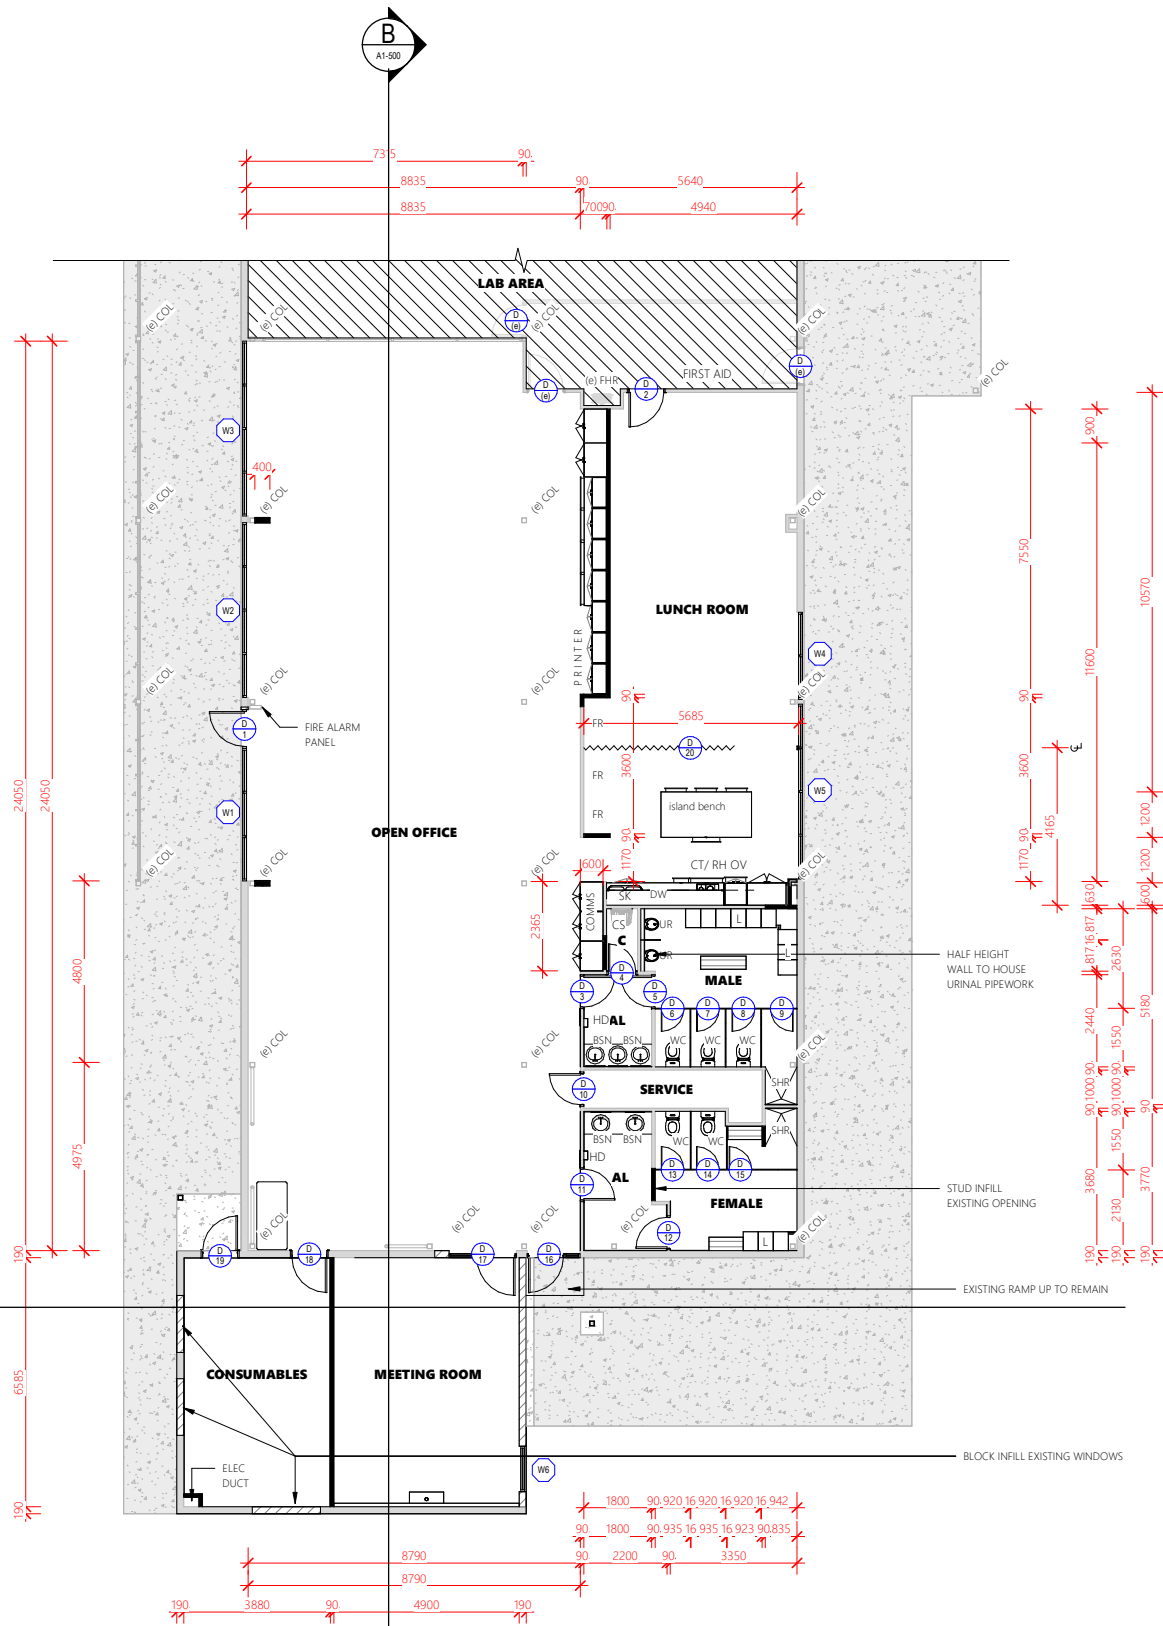

Proposed Registry Floor Plan

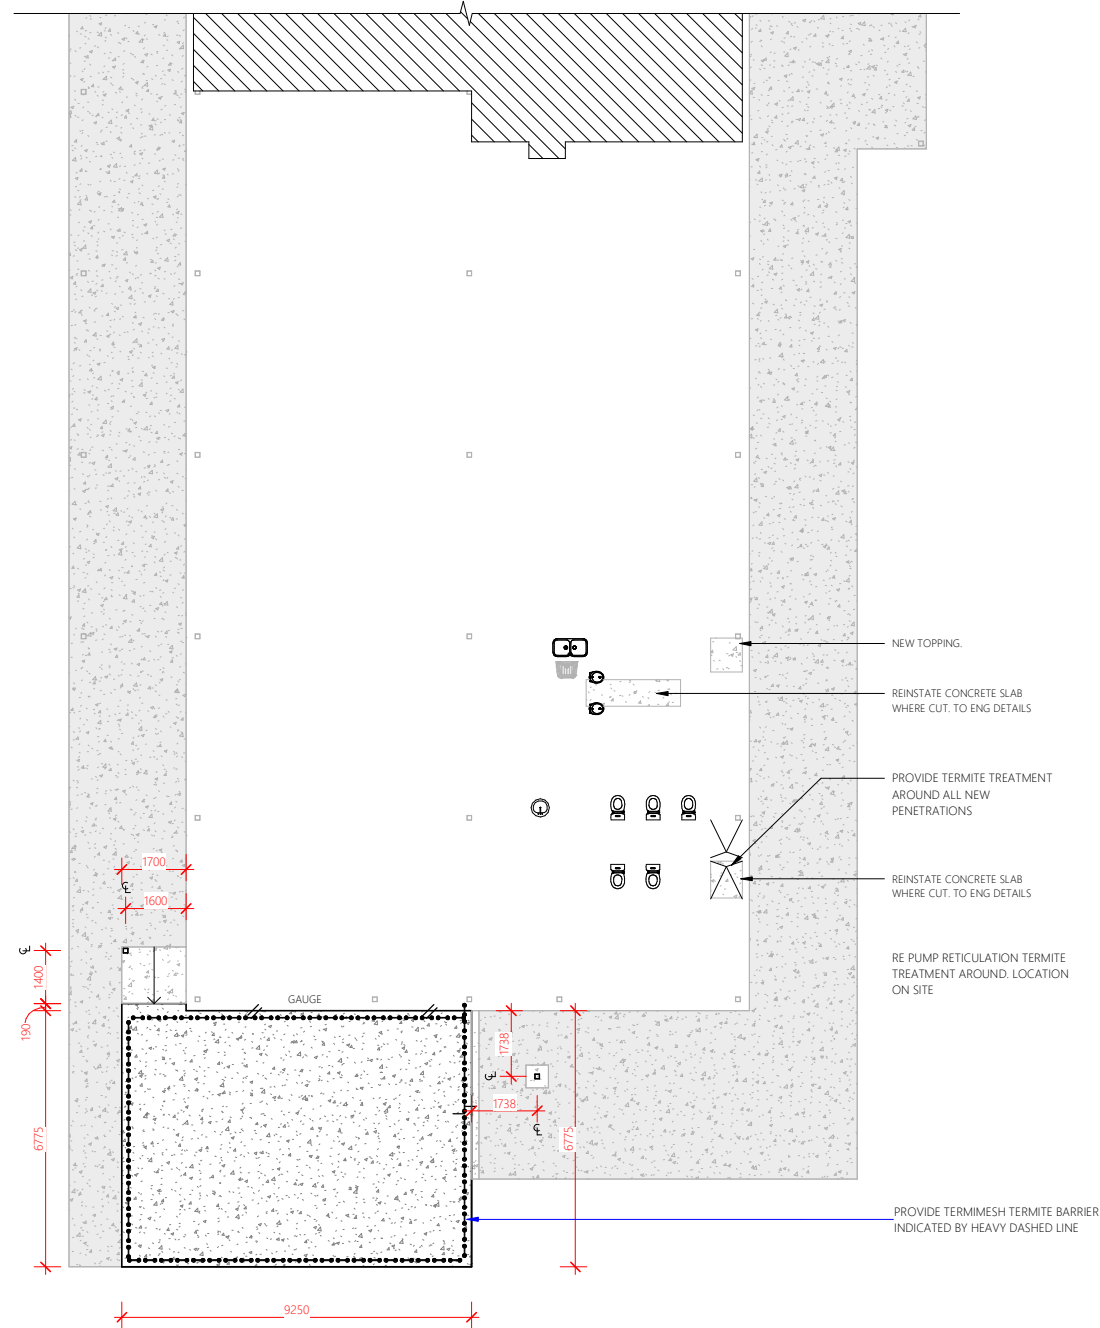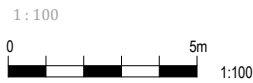


Proposed Slab Plan

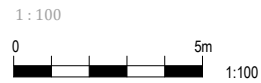


CONFIRM EXISTING GRID SETOUT ON SITE

NEW CEILING INSULATION THROUGHOUT
SHADED AREA - REFER SPEC


- CEILING LEGEND**
- 1200 x 600 APEX ACOUSTIC CEILING TILES (OR APPROVED EQUAL. NEW TILES THROUGH RENOVATED AREA)
 - PROVIDE CONCEALED FIX RIBBEDTRIMDEK SOFFIT SHEETING (TO MATCH EXISTING)
 - INSULATION ABOVE CEILING TILES

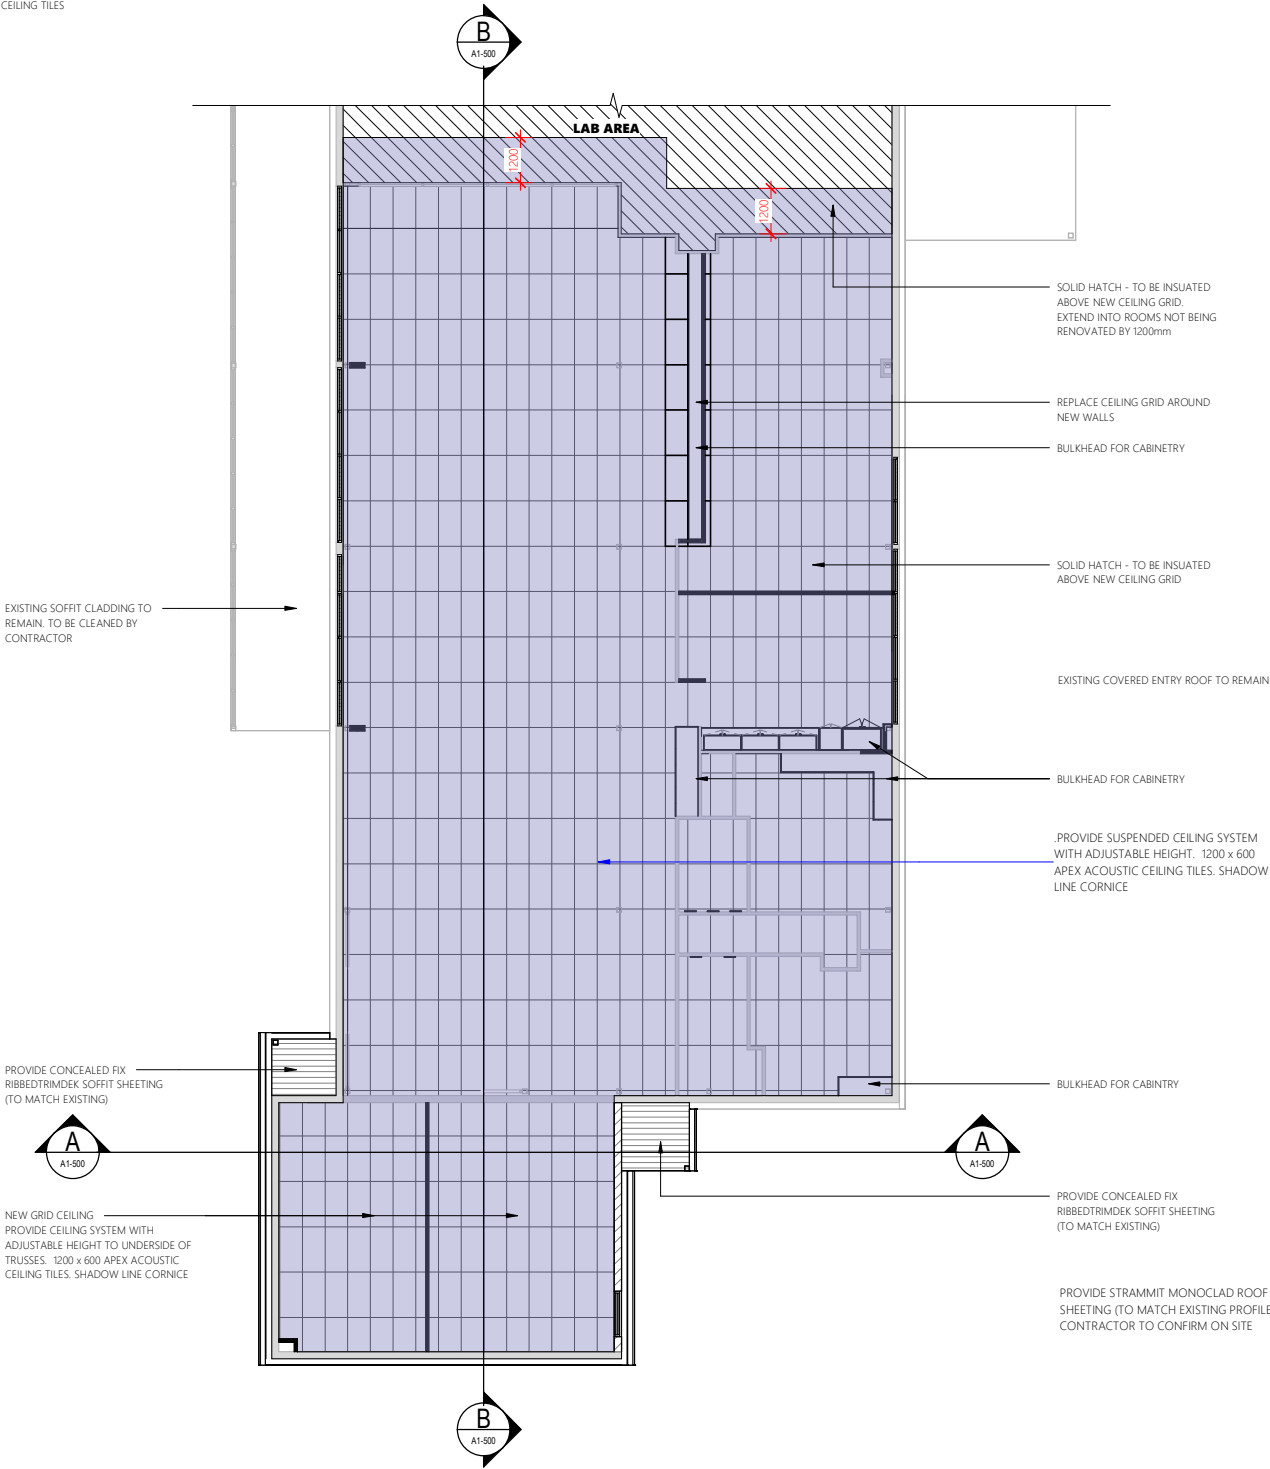


Proposed Ceiling Plan

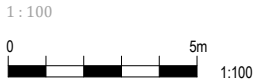

CONFIRM EXISTING ROOF PITCH ON SITE

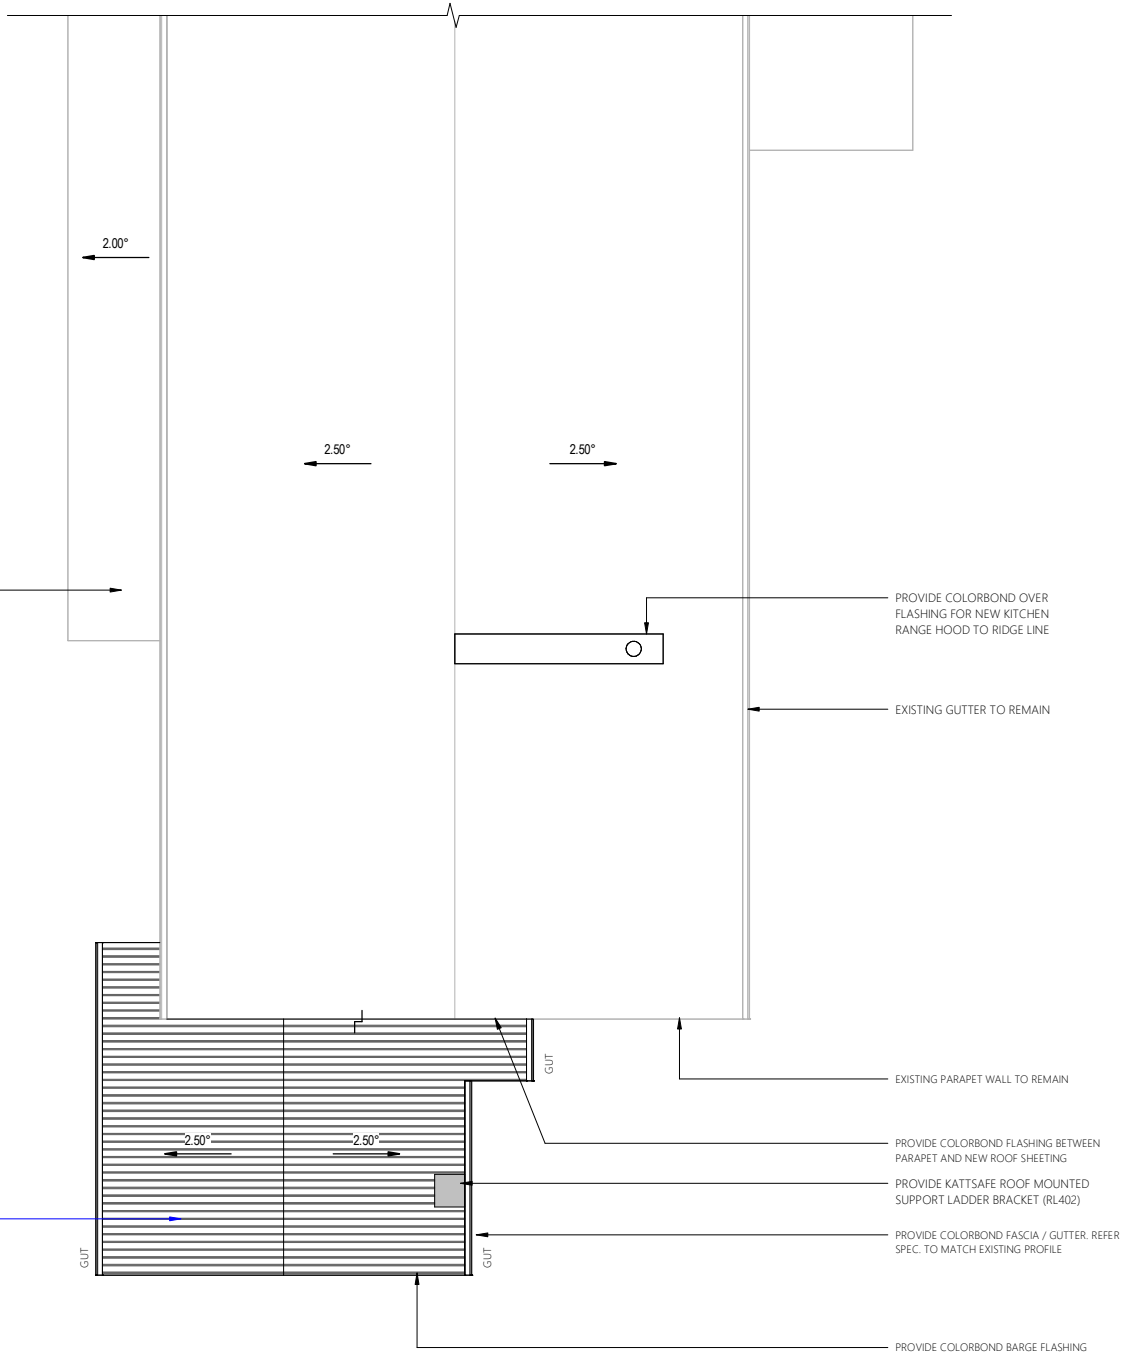

Proposed Roof Plan

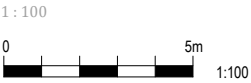

REVISIONS		
Rev	Description	Date
T1	TENDER ISSUE	12.03.2026

DO NOT SCALE THIS DRAWINGS



TENDER ISSUE

Client

Project Details

REGISTRY REFURBISHMENT

Address

STANWELL POWER STATION


Drawing Title

PROPOSED CEILING & ROOF


0483 988 655 M
info@deziignelements.com.au E
QBCC No: 1247120 BDAQ No: 0001677

Scale: 1 : 100 Rev: T1
Date: MARCH 2026
Drawn: NJB
Project No: 25_003 Drawing No: A1-301




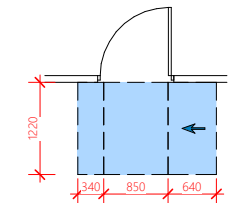


HINGE-SIDE APPROACH
DOOR OPENS AWAY FROM USER

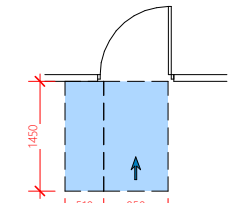


FRONT APPROACH
DOOR OPENS AWAY FROM USER

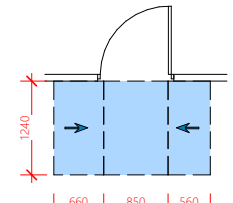


EITHER SIDE APPROACH
DOOR OPENS AWAY FROM USER

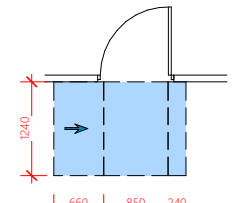


LATCH APPROACH
DOOR OPENS AWAY FROM USER

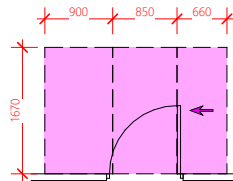


HINGE-SIDE APPROACH
DOOR OPENS TOWARDS USER

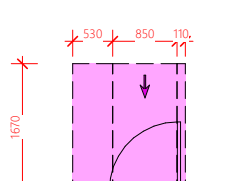


FRONT APPROACH
DOOR OPENS TOWARDS USER

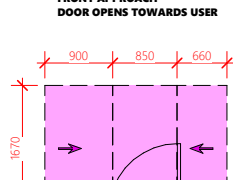

EITHER-SIDE APPROACH
DOOR OPENS TOWARDS USER

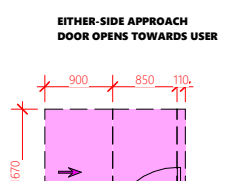


LATCH-SIDE APPROACH
DOOR OPENS TOWARDS USER

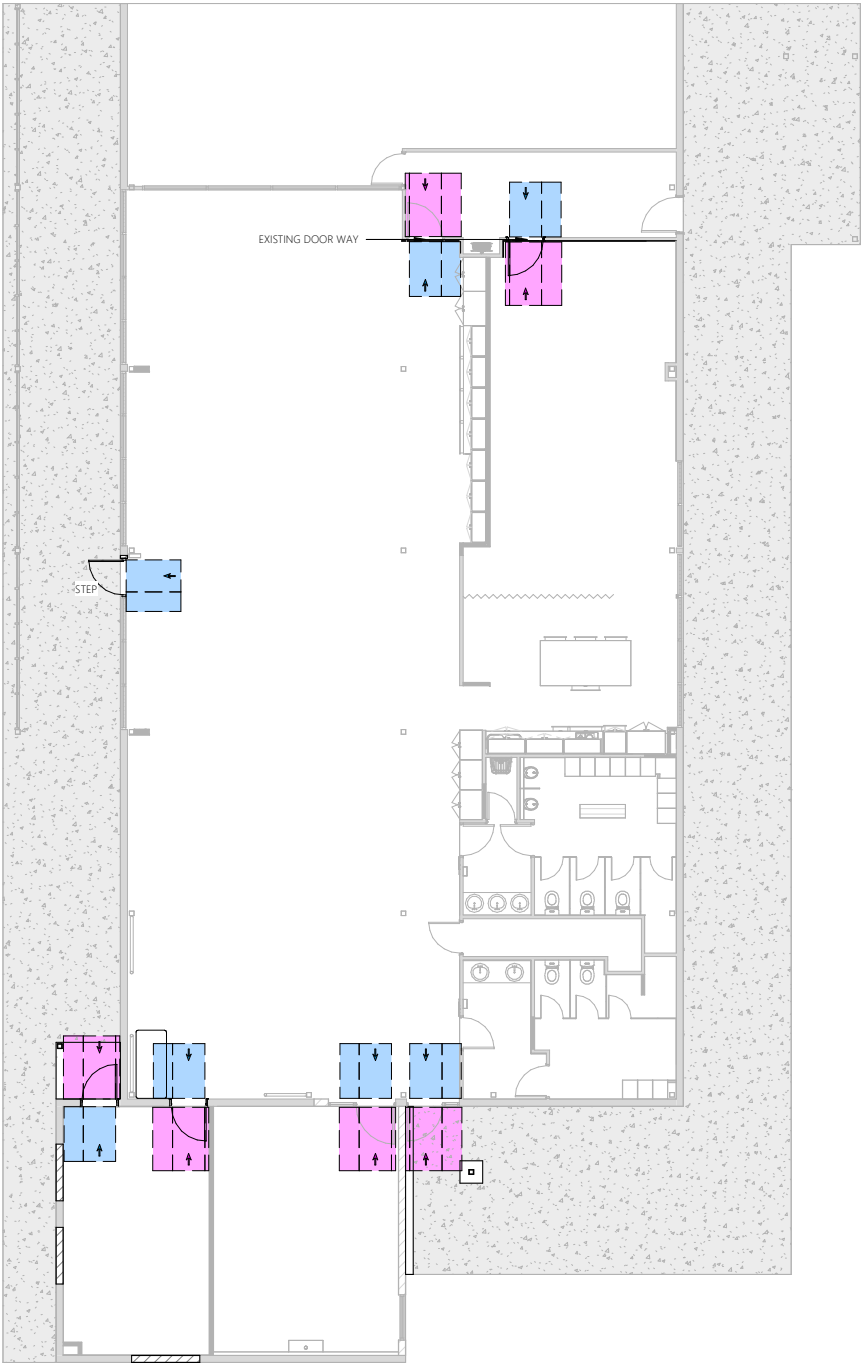

AS1428.1 - Clearance Plan

1 : 100

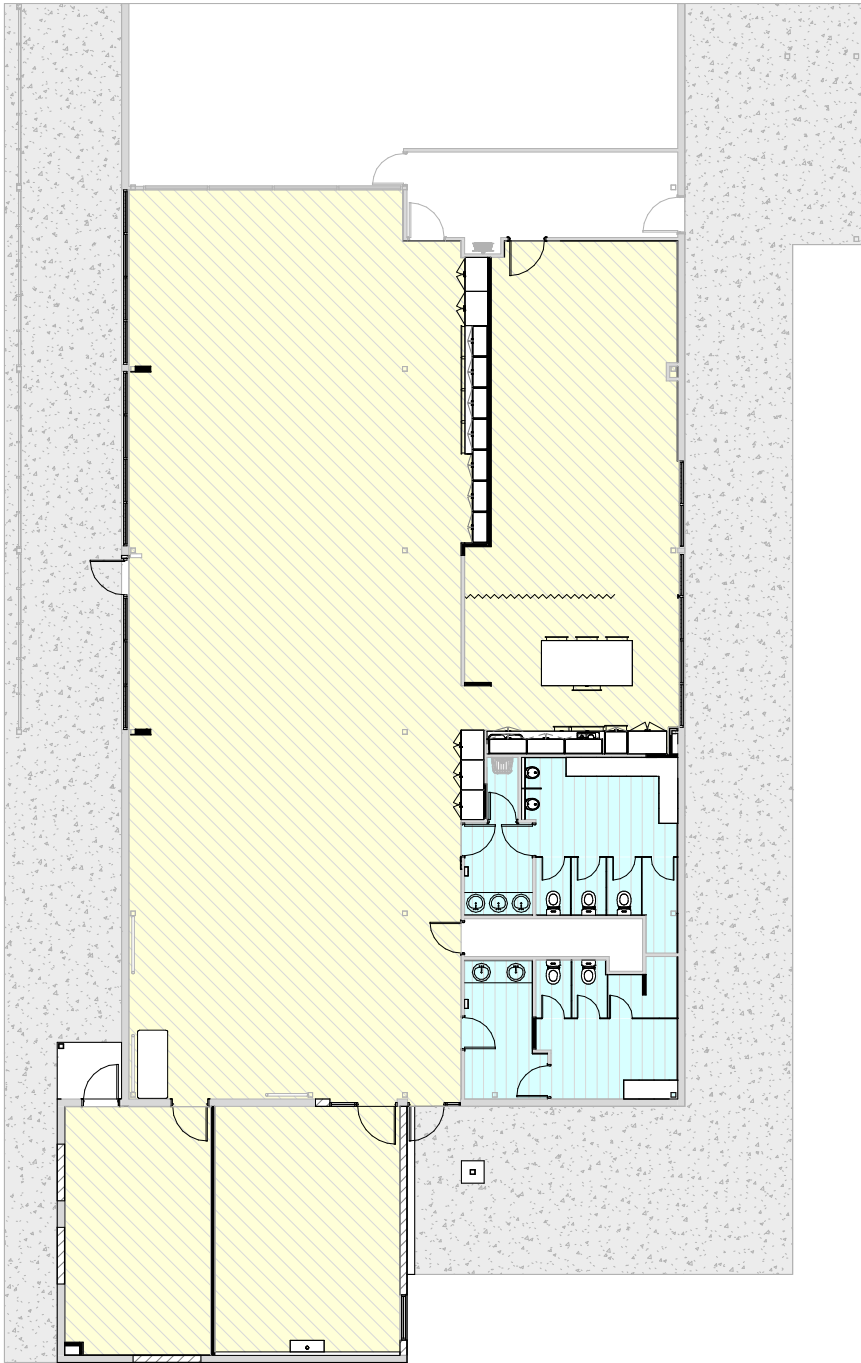

Floor Covering Plan

1 : 100

REVISIONS

Rev	Description	Date
T1	TENDER ISSUE	12.03.2026

DO NOT SCALE THIS DRAWINGS

FLOOR COVERING PLAN

	SHEET VINYL - TYPE 1 100mm FEATHER EDGE SKIRTING - BLACK
	SHEET VINYL - TYPE 2 100mm COVERED UP SKIRTING
	SHEET VINYL - TYPE 3 100mm FEATHER EDGE SKIRTING - BLACK

TENDER ISSUE

Client

Project Details
REGISTRY REFURBISHMENT

Address
**STANWELL POWER
STATION**

Drawing Title
**AS1428.1 - CLEARANCE &
FLOOR COVERING PLAN**


0483 988 655 M
info@designelements.com.au E
QBCC No: 1247120 BDAQ No: 0001677

Scale: As indicated	Rev: T1
Date: MARCH 2026	
Drawn: NJB	
Project No: 25_003	Drawing No: A1-302




REVISIONS		
Rev	Description	Date
T1	TENDER ISSUE	12.03.2026

DO NOT SCALE THIS DRAWINGS

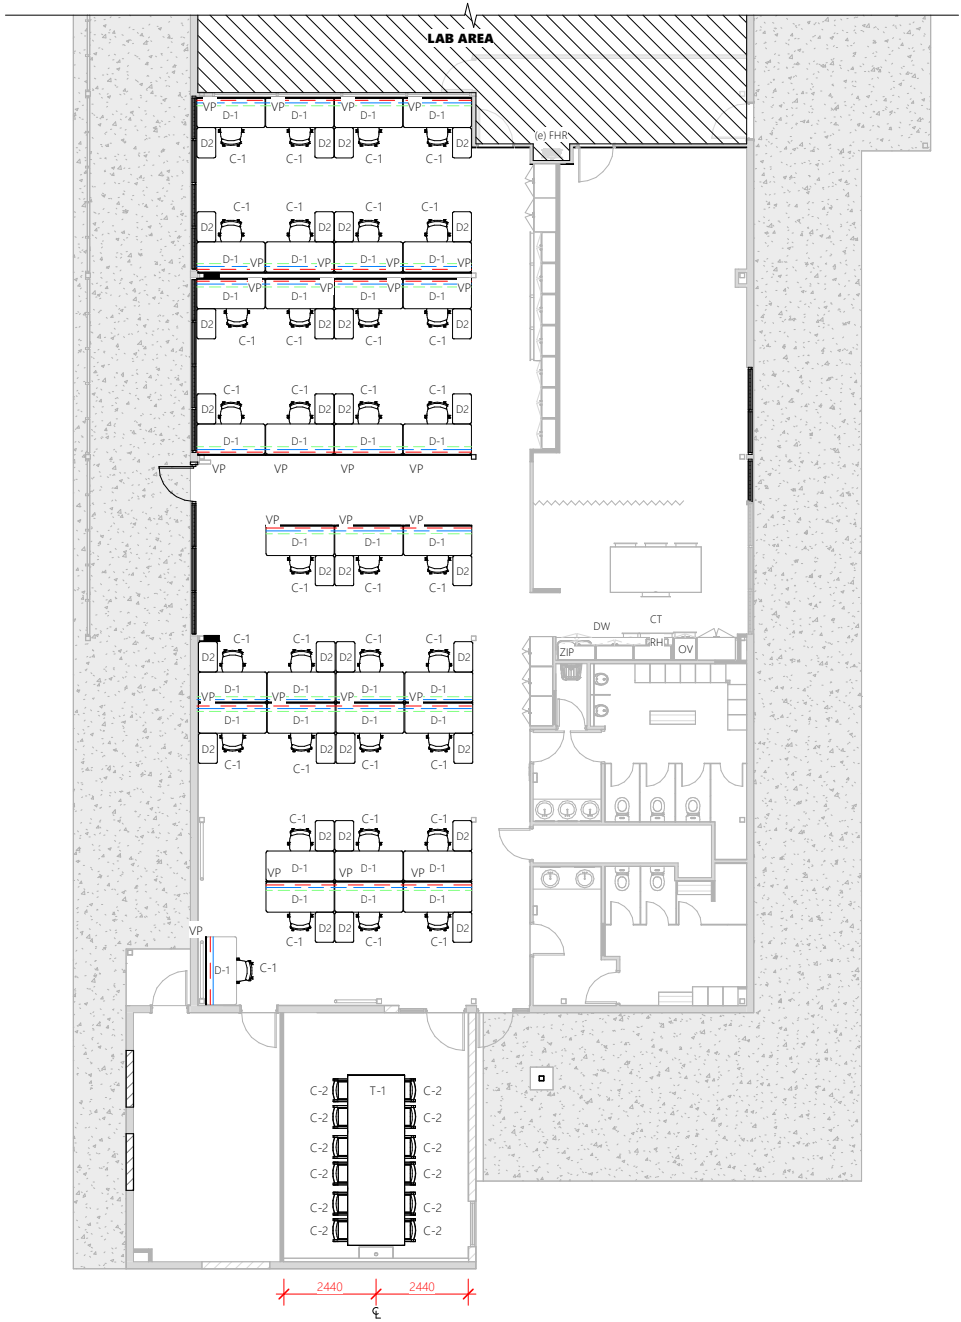

Proposed Furniture Layout

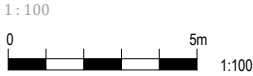

FURNITURE & APPLIANCE SCHEDULE

CODE	TYPE	SIZE	QTY	SUPPLIER
D-1	DESK	1800 x 800	34	SCHIAVELLA CLIMATE RECTANGLE WORK STATION
D-2	DESK	800 x 500	33	SCHIAVELLA CLIMATE RECTANGLE WORK STATION RETURN
C-1	CHAIR (workstation)	-	34	SCHIAVELLA HIGH BACK CHAIR BY OKAMURA, BLACK BODY, BLACK MESH BLACK AND UPHOLSTERED SEAT
C-2	CHAIR (meeting)	-	12	SHIBUSA HIGH BACK BY OKAMURA (BLACK)
T-1	TABLE	1400 x 4400	1	MEETING TABLE EONA - 25mm LAMINEX CHARCOAL NATURAL FINISH WITH ABS EDGING
—	CABLE CATCHER	AS REQUIRED	-	SCHIAVELLA
- - -	CABLE ARTICULATOR	AS REQUIRED	-	SCHIAVELLA
- - -	CABLE CHANNEL	AS REQUIRED	-	SCHIAVELLA
VP	VIDE SUSP. PANEL	1800 (600mm ABOVE DESK)	27	SCHIAVELLA - PROVIDE SUSPENDE BRACKETS TO EACH DESK
OV	OVEN	598 x 596	1	FISHER & PAYKEL 60CM SERIES 7 CONTEMPORARY PYROLYTIC OVEN 9 FUNCTION - BLACK
DW	DISHWASHER	597 x 600	1	FISHER & PAYKEL SERIES 7 CONTEMPORARY DISHWASHER - BLACK STEEL
CT	COOK TOP	600	1	FISHER & PAYKEL 60CM SERIES 7 4 ZONE INDUCTION COOKTOP 2 SMARTZONES - BLACK
RH	RANGE HOOD	600	1	FISHER & PAYKEL 60CM SERIES 7 INTEGRATED INSERT WALL RANGEHOOD EXTERNAL MOTOR - STEEL GLASS
ZIP	ZIP UNIT	-	1	HYDROTAP G5 BC5HA100 5-IN-1 CLASSIC TAP WITH CLASSIC MIXER BLACK

TENDER ISSUE

Client

Project Details

REGISTRY REFURBISHMENT

Address

STANWELL POWER STATION

Drawing Title

FURNITURE LAYOUT

0483 988 655 M

info@dezignelements.com.au E

QBCC No: 1247120 BDAQ No: 0001677

Scale: 1 : 100	Rev: T1
Date: MARCH 2026	
Drawn: NJB	
Project No: 25_003	Drawing No: A1-303



REVISIONS		
Rev	Description	Date
T1	TENDER ISSUE	12.03.2026

DO NOT SCALE THIS DRAWINGS



TENDER ISSUE

Client



Project Details

REGISTRY REFURBISHMENT

Address

STANWELL POWER STATION

Drawing Title


PROPOSED ELEVATION




0483 988 655 M
info@deziignelements.com.au E
QBCC No: 1247120 BDAQ No: 0001677

Scale: 1 : 100
Date: MARCH 2026
Drawn: NJB


Rev: T1
Project No: 25_003
Drawing No: A1-400

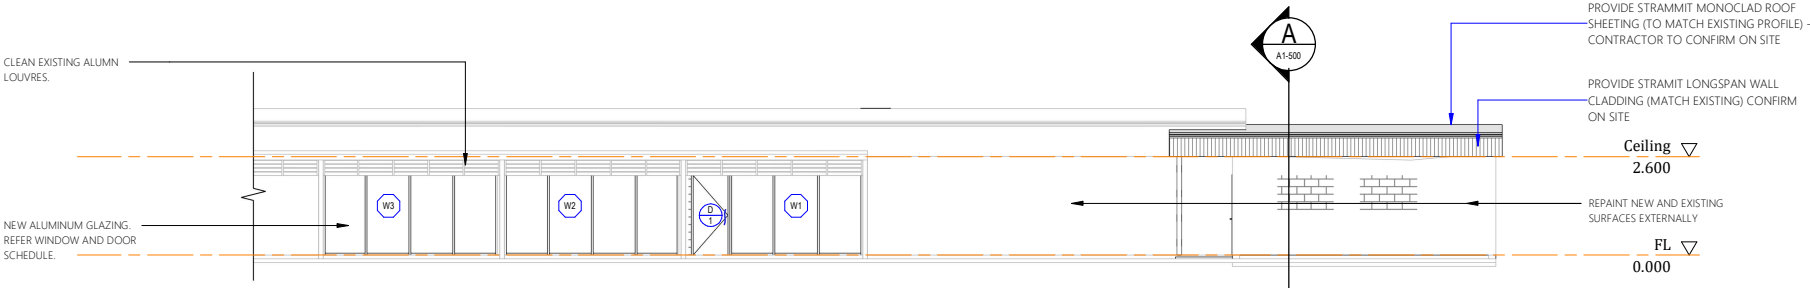


Proposed Elevation 1
1 : 100

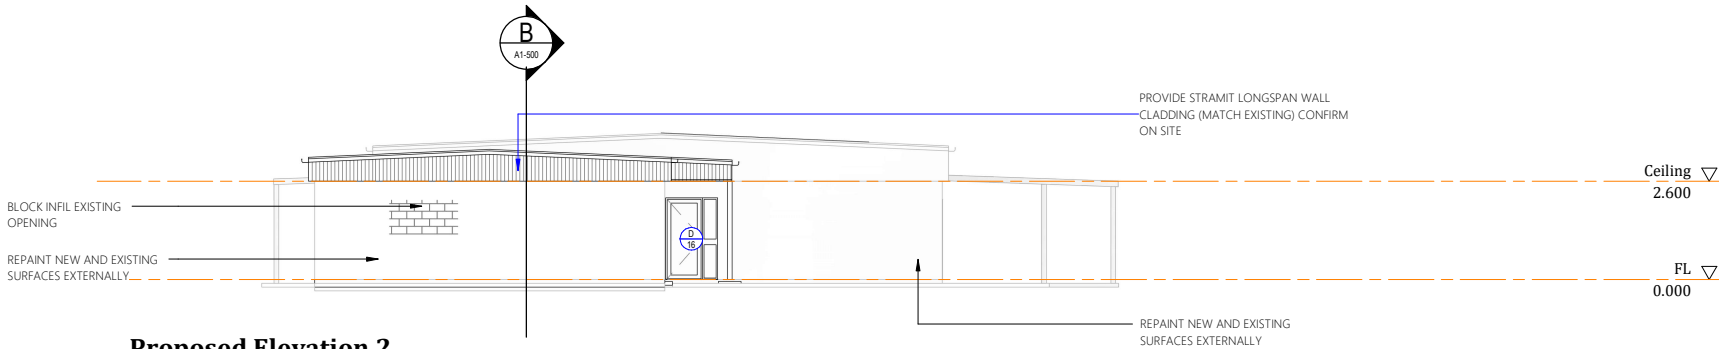


Proposed Elevation 2
1 : 100

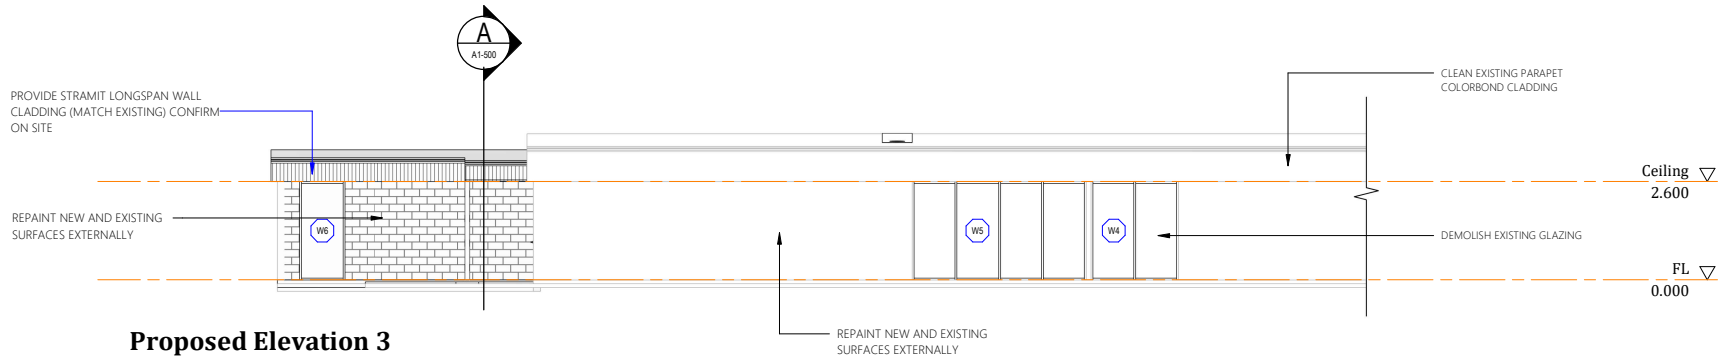

Proposed Elevation 3
1 : 100

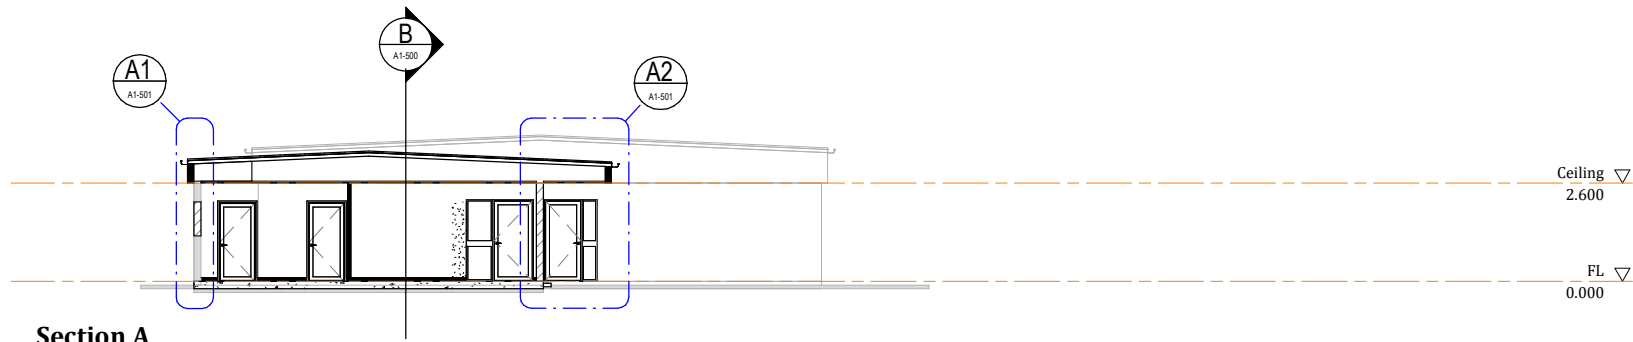

Section A
1 : 100

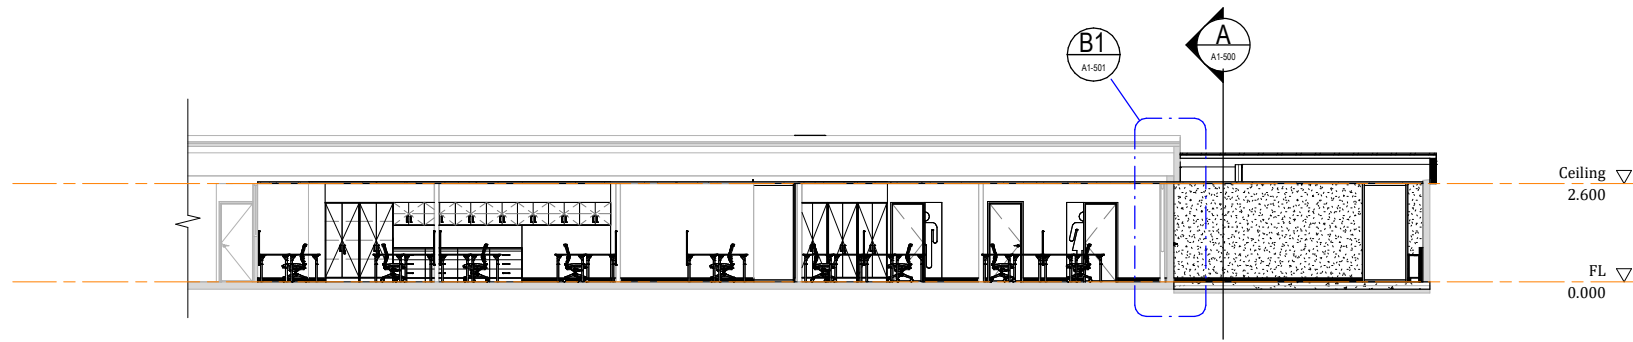

Section B
1 : 100

REVISIONS		
Rev	Description	Date
T1	TENDER ISSUE	12.03.2026

DO NOT SCALE THIS DRAWINGS



TENDER ISSUE

Client



Project Details

REGISTRY REFURBISHMENT

Address

STANWELL POWER STATION

Drawing Title

PROPOSED SECTION


BUILDING DESIGNERS
0483 988 655 M
info@deziignelements.com.au E
QBCC No: 1247120 BDAQ No: 0001677

Scale: 1 : 100
Date: MARCH 2026
Drawn: NJB

Rev: T1

Project No: 25_003
Drawing No: A1-500

REVISIONS		
Rev	Description	Date
T1	TENDER ISSUE	12.03.2026

DO NOT SCALE THIS DRAWINGS

PROVIDE STRAMMIT MONOCLAD ROOF SHEETING (TO MATCH EXISTING PROFILE) - CONTRACTOR TO CONFIRM ON SITE

PROVIDE STRAMMIT LONGSPAN WALL CLADDING (MATCH EXISTING) CONFIRM ON SITE. NOG INBETWEEN TRUSS ROOF TO FIX CLADDING

PROVIDE COLORBOND BOTTOM FLASHING

BATTEN UNDERSIDE OF TRUSSES AND SHEET WITH 6mm FC. PAINT FINISH
PROVIDE 42x12 COVER BATTENS

PROVIDE BLOCK INFILL. PAINT FINISH

TRUSSES TO ENG. DETAILS

PROVIDE COLORBOND END CAP FLASHING TO BOTH ENDS

PROVIDE CEILING SYSTEM WITH ADJUSTABLE HEIGHT. 1200 x 600 APEX ACOUSTIC CEILING TILES. SHADOW LINE CORNICE

REPAINT EXISTING BLOCKWORK INTERNAL AND EXTERNAL

100mm FEATHER EDGE SKIRTING

TOPPING SLAB TO ENG. DETAILS

PROVIDE STRAMMIT LONGSPAN WALL CLADDING (MATCH EXISTING) CONFIRM ON SITE. NOG INBETWEEN TRUSS ROOF TO FIX CLADDING

PROVIDE CONCEALED FIX RIBBEDTRIMDEK SOFFIT SHEETING (TO MATCH EXISTING). BATTEN DOWN TO TRUSSES

PROVIDE COLORBOND FLASHING BETWEEN PARAPET AND NEW ROOF SHEETING

PROVIDE STRAMMIT MONOCLAD ROOF SHEETING (TO MATCH EXISTING PROFILE) - CONTRACTOR TO CONFIRM ON SITE

TRUSSES TO ENG. DETAILS

PROVIDE CEILING SYSTEM WITH ADJUSTABLE HEIGHT. 1200 x 600 APEX ACOUSTIC CEILING TILES. SHADOW LINE CORNICE

REPAINT EXISTING BLOCKWORK INTERNAL AND EXTERNAL

100mm FEATHER EDGE SKIRTING

PROVIDE REINFORCED CONCRETE SLAB. REFER TO ENGINEERS DETAILS.

Section Detail A1

1 : 20

Section Detail A2


1 : 20

Section Detail B1

1 : 20


DO NOT SCALE THIS DRAWINGS



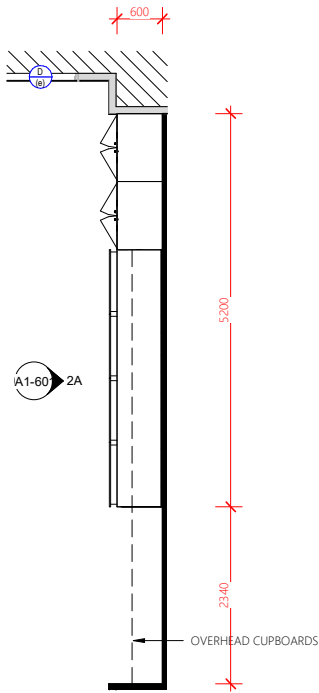

Internal Plan 2

1 : 50

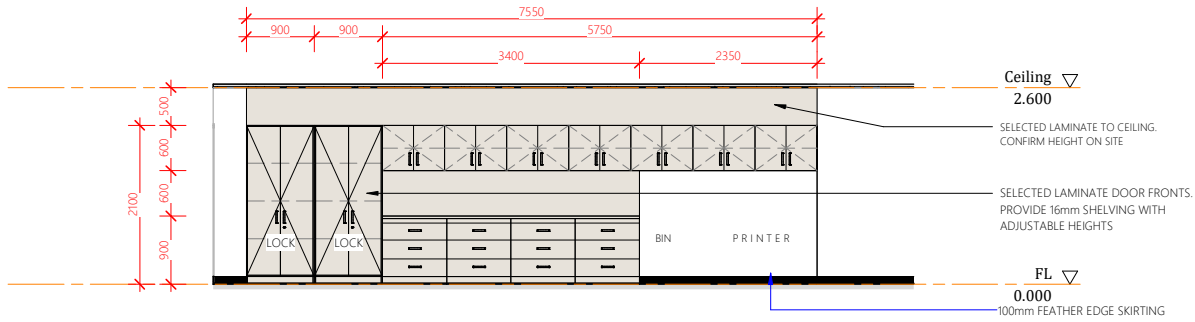

Elevation 2A

1 : 50



REVISIONS

Rev	Description	Date
T1	TENDER ISSUE	12.03.2026

DO NOT SCALE THIS DRAWINGS



TENDER ISSUE

Client



Project Details

REGISTRY REFURBISHMENT

Address

STANWELL POWER STATION

Drawing Title

INTERNAL ELEVATIONS 2 - OPEN OFFICE



dezynelements
BUILDING DESIGNERS

0483 988 655 M
info@dezynelements.com.au E

QBCC No: 1247120 BDAQ No: 0001677





Scale: 1 : 50 Rev: T1

Date: MARCH 2026

Drawn: NJB


Project No: 25_003 Drawing No: A1-601



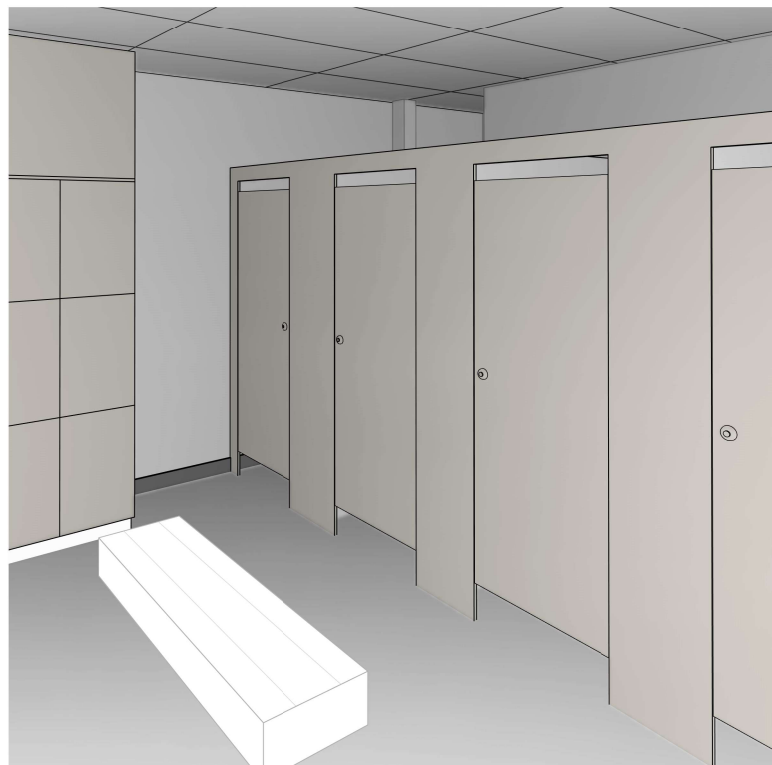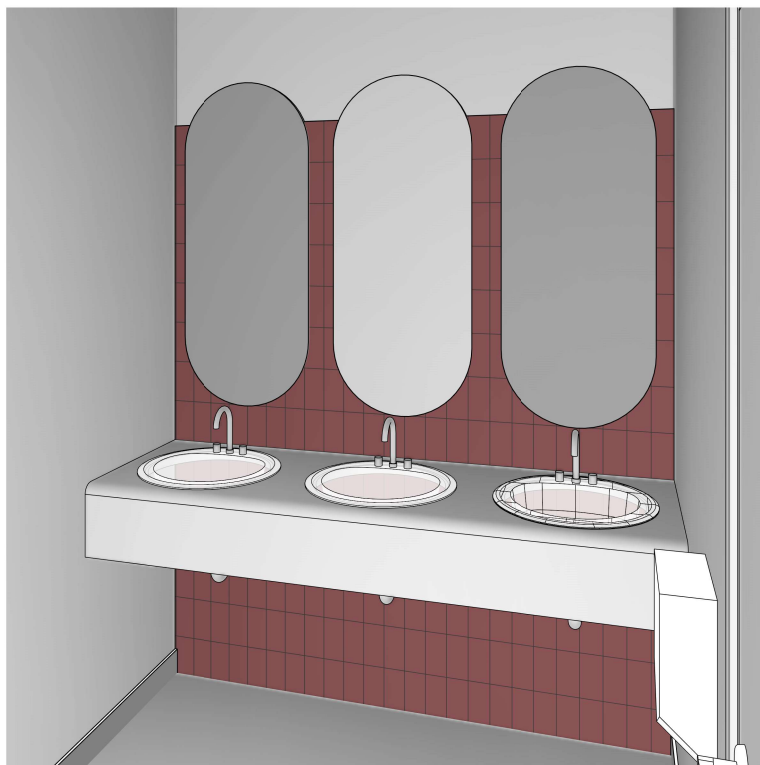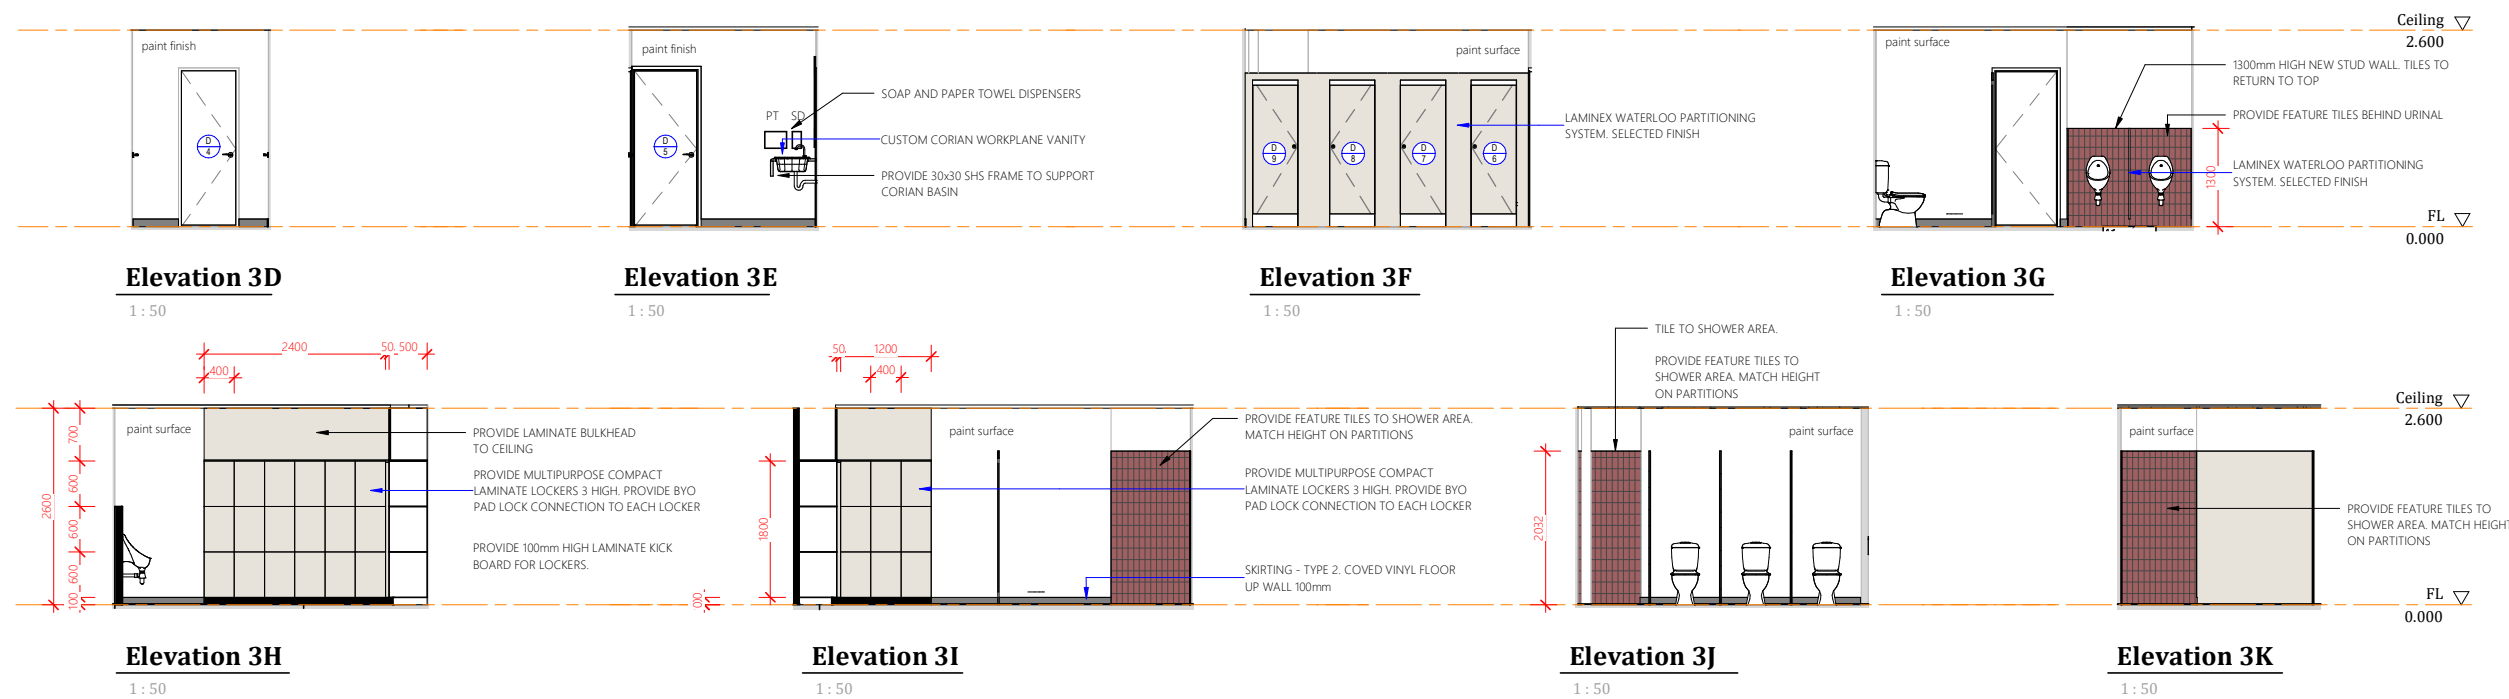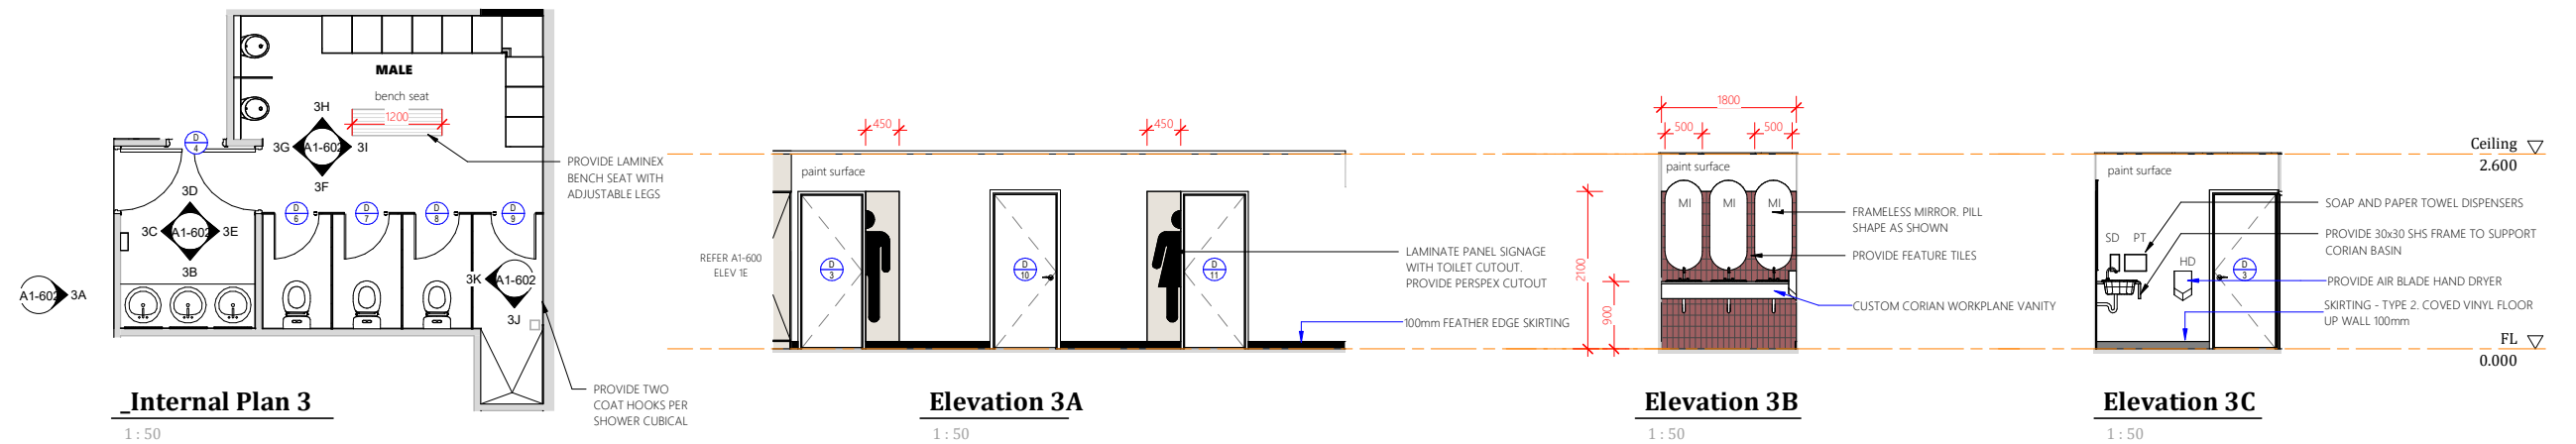

REVISIONS		
Rev	Description	Date
T1	TENDER ISSUE	12.03.2026

DO NOT SCALE THIS DRAWINGS

 

TENDER ISSUE



Project Details
REGISTRY REFURBISHMENT
Address
STANWELL POWER STATION
Drawing Title
INTERNAL ELEVATIONS 3 - MALE AMENITIES




Scale: 1 : 50	Rev: T1
Date: MARCH 2026	
Drawn: NJB	
Project No: 25_003	Drawing No: A1-602



REVISIONS


Rev	Description	Date
T1	TENDER ISSUE	12.03.2026

DO NOT SCALE THIS DRAWINGS

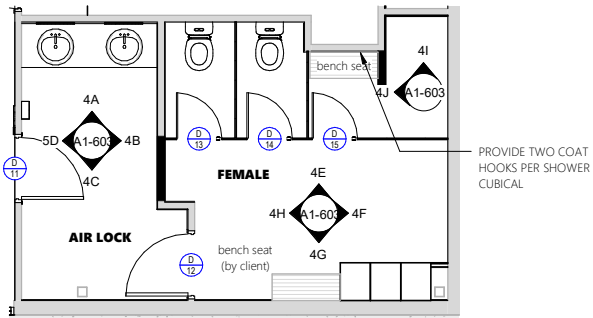


Internal Plan 4

1 : 50

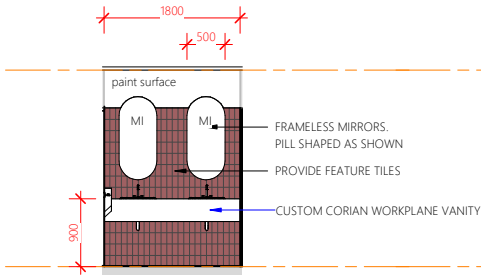


Elevation 4A

1 : 50

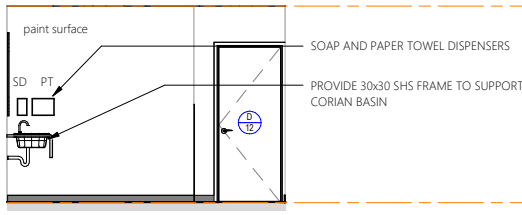


Elevation 4B

1 : 50

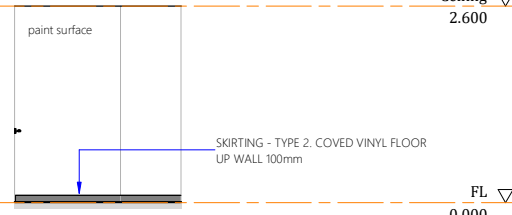


Elevation 4C

1 : 50

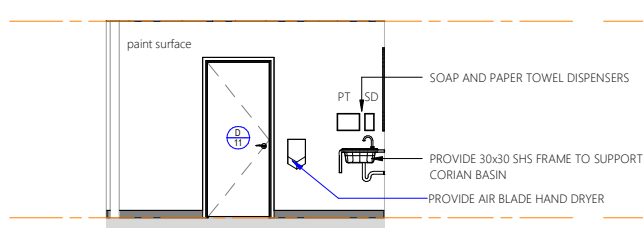


Elevation 4D

1 : 50

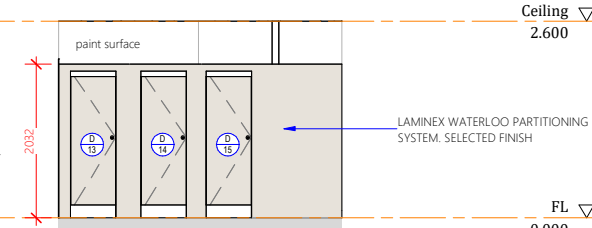


Elevation 4E

1 : 50

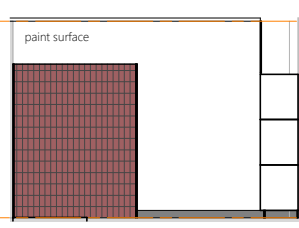


Elevation 4F

1 : 50

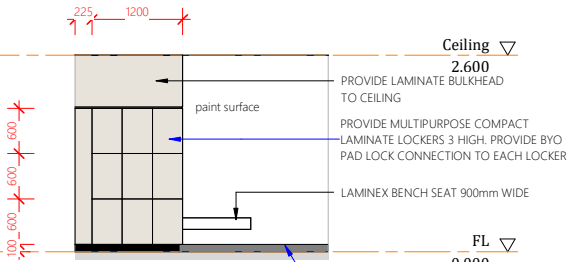


Elevation 4G

1 : 50

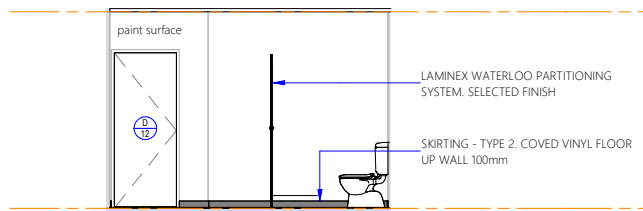


Elevation 4H

1 : 50

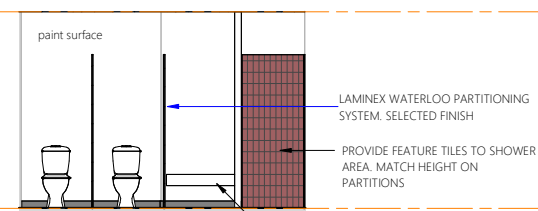



Elevation 4I

1 : 50

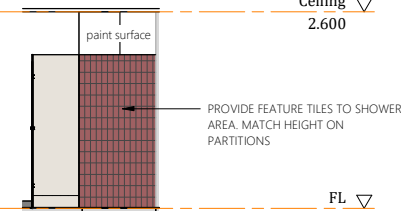

Elevation 4J

1 : 50

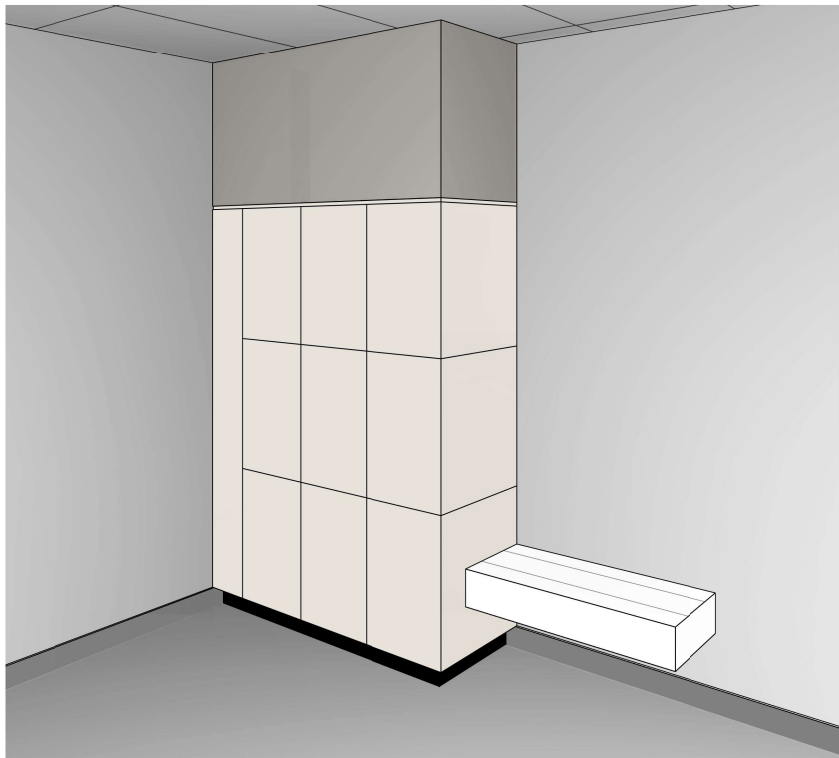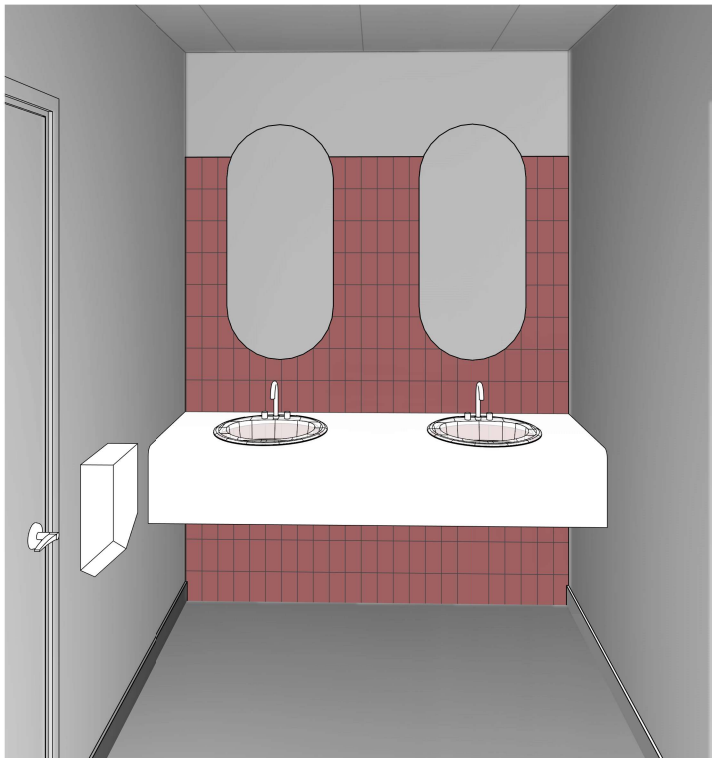

TENDER ISSUE



Project Details
REGISTRY REFURBISHMENT

Address
STANWELL POWER STATION


Drawing Title
INTERNAL ELEVATIONS 4 - FEMALE AMENITIES

dezinelements
BUILDING DESIGNERS
0483 988 655 M
info@dezi


Scale: 1 : 50
Date: MARCH 2026
Drawn: NJB

Rev: T1
Project No: 25_003
Drawing No: A1-603



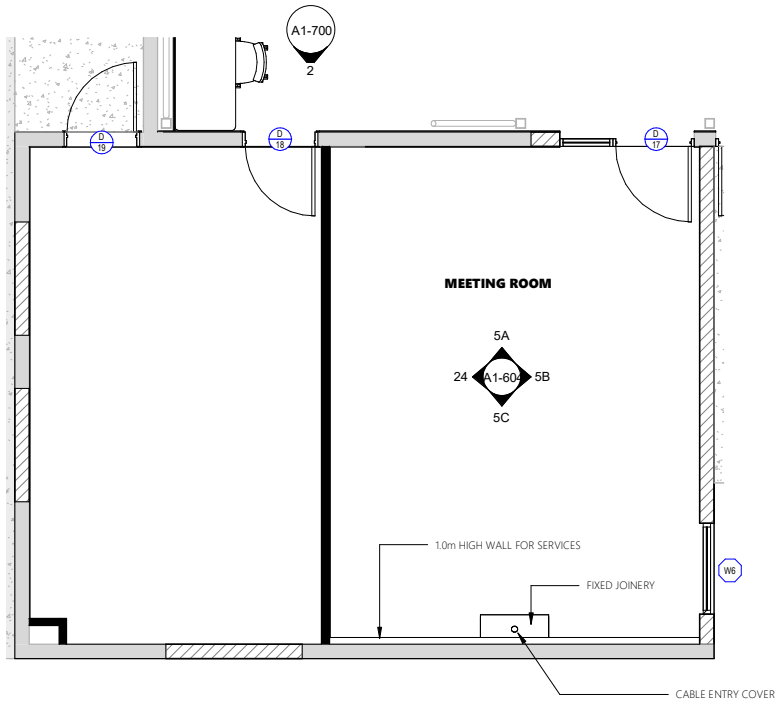


Internal Plan 5
1 : 50

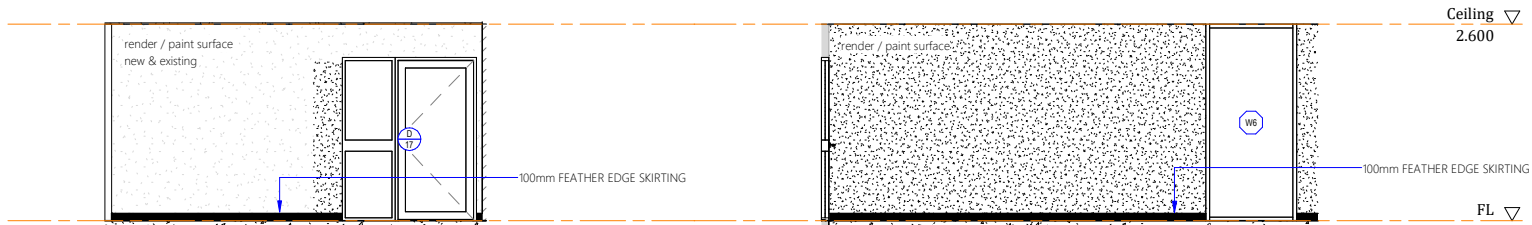


Elevation 5A
1 : 50

Elevation 5B
1 : 50

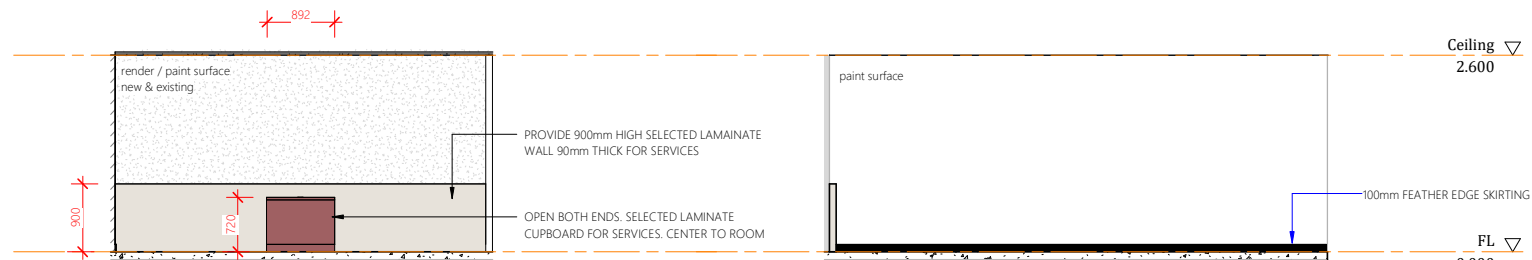

Elevation 5C
1 : 50

Elevation 5D
1 : 50

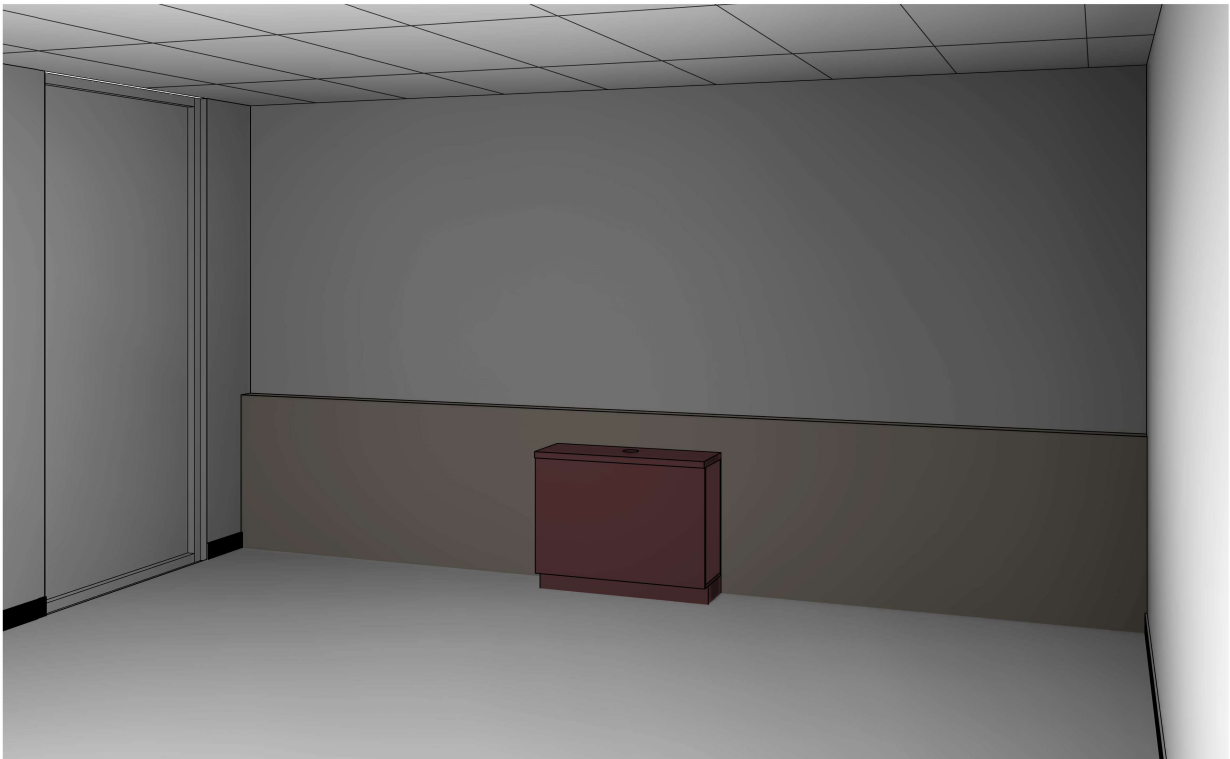

REVISIONS		
Rev	Description	Date
T1	TENDER ISSUE	12.03.2026

DO NOT SCALE THIS DRAWINGS



TENDER ISSUE

Client

 stanwell

Project Details

REGISTRY REFURBISHMENT

Address

STANWELL POWER STATION

Drawing Title

INTERNAL ELEVATIONS 5 - MEETING ROOM


 **designelements**
BUILDING DESIGNERS

0483 988 655 **M**
info@designelements.com.au **E**
QBCC No: 1247120 BDAQ No: 0001677

Scale: **1 : 50** Rev: **T1**
Date: **MARCH 2026**
Drawn: **NJB**
Project No: **25_003** Drawing No: **A1-604**




DOOR SCHEDULE	
DOOR NO.	DOOR TYPE
1	TYPE A
2	TYPE B
3	TYPE C
4	TYPE D
5	TYPE C
6	TYPE E
7	TYPE E
8	TYPE E
9	TYPE E
10	TYPE C
11	TYPE C
12	TYPE C
13	TYPE E
14	TYPE E
15	TYPE E
16	TYPE F
17	TYPE G
18	TYPE B
19	TYPE H

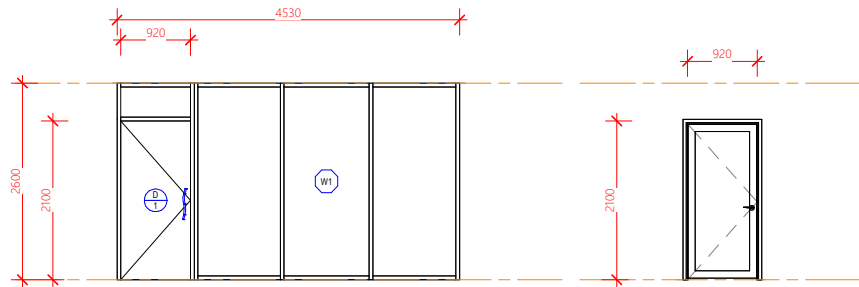


DOOR TYPE A

LOCATION: EXTERNAL
DOOR TYPE: HINGED ALUMINIUM FRAMED SINGLE DOOR
FRAME TYPE: G.JAMES 475 SERIES
FRAME FINISH: SELECTED POWDERCOAT
DOOR FINISH: SELECTED POWDERCOAT
INFILL: GREY SAFETY GLASS
THRESHOLD:
SEALS:
LOCK: REFER HARDWARE SCHEDULE
HARDWARE: DOOR CLOSER, DOOR STOP

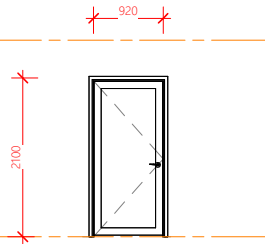


DOOR TYPE B

LOCATION: INTERNAL
DOOR TYPE: HINGED ALUMINIUM FRAMED SINGLE DOOR
FRAME TYPE: G.JAMES 475 SERIES
FRAME FINISH: SELECTED POWDERCOAT
DOOR FINISH: SELECTED POWDERCOAT
INFILL: GREY SAFETY GLASS
SEALS: NONE
LOCK: REFER HARDWARE SCHEDULE
HARDWARE: DOOR CLOSER, DOOR STOP

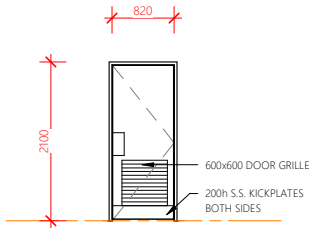


DOOR TYPE C

LOCATION: MALE & FEMALE AMENITIES
DOOR TYPE: 40mm HINGED SOLID CORE SINGLE DOOR
FRAME TYPE: TIMBER
FRAME FINISH: PAINT
DOOR FINISH: PAINT
SEALS: NONE
LOCK: PUSH PULL PLATES (NO LOCKING)
HARDWARE: KICK PLATES, DOOR CLOSER, DOOR STOP

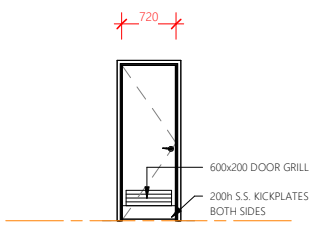


DOOR TYPE D

LOCATION: CLEANER
DOOR TYPE: 40mm HINGED SOLID CORE SINGLE DOOR
FRAME TYPE: TIMBER
FRAME FINISH: PAINT
DOOR FINISH: PAINT
SEALS: NONE
LOCK: REFER HARDWARE SCHEDULE
HARDWARE: KICK PLATES, DOOR CLOSER, DOOR STOP

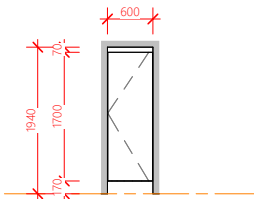


DOOR TYPE E

LOCATION: AMENITIES
DOOR TYPE: 13mm COMPACT LAMINATE PARTITION DOOR
FRAME TYPE: PROVIDE 30° PRIVACY BEVEL
DOOR FINISH: SELECTED LAMINATE
SEALS: NONE
LOCK: METLAM XCEL SLIDE LOCK & INDICATOR.
HARDWARE:

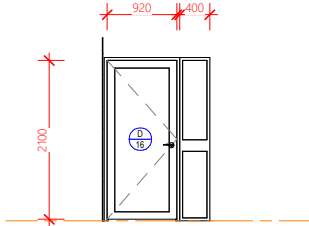


DOOR TYPE F

LOCATION: EXTERNAL
DOOR TYPE: HINGED ALUMINIUM FRAMED SINGLE DOOR
FRAME TYPE: G.JAMES 475 SERIES
FRAME FINISH: SELECTED POWDERCOAT
DOOR FINISH: SELECTED POWDERCOAT
INFILL: GREY SAFETY GLASS
THRESHOLD:
SEALS:
LOCK: REFER HARDWARE SCHEDULE
HARDWARE: DOOR CLOSER, DOOR STOP

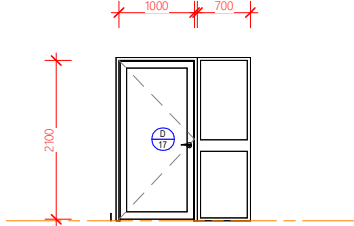

DOOR TYPE G


LOCATION: INTERNAL
DOOR TYPE: HINGED ALUMINIUM FRAMED SINGLE DOOR
FRAME TYPE: G.JAMES 475 SERIES
FRAME FINISH: SELECTED POWDERCOAT
DOOR FINISH: SELECTED POWDERCOAT
INFILL: GREY SAFETY GLASS
SEALS: NONE
LOCK: REFER HARDWARE SCHEDULE
HARDWARE: DOOR CLOSER, DOOR STOP

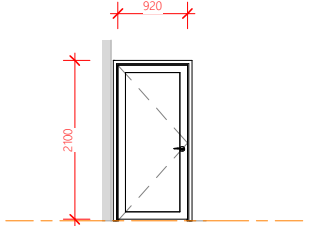

DOOR TYPE H


LOCATION: EXTERNAL
DOOR TYPE: HINGED ALUMINIUM FRAMED SINGLE DOOR
FRAME TYPE: G.JAMES 475 SERIES
FRAME FINISH: SELECTED POWDERCOAT
DOOR FINISH: SELECTED POWDERCOAT
INFILL: GREY SAFETY GLASS
THRESHOLD:
SEALS:
LOCK: REFER HARDWARE SCHEDULE
HARDWARE: DOOR CLOSER, DOOR STOP

WINDOW SCHEDULE	
WINDOW NO.	WINDOW TYPE
1	TYPE A
2	TYPE B
3	TYPE B
4	TYPE C
5	TYPE B
6	TYPE C

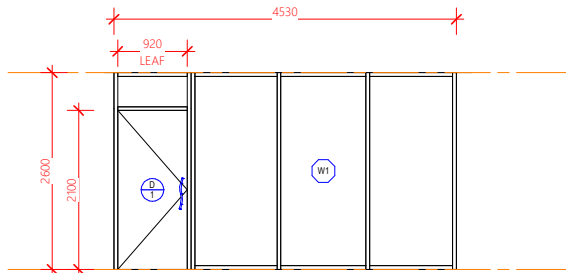


WINDOW TYPE A

LOCATION: EXTERNAL
FRAME TYPE: G.JAMES 475 SERIES
FRAME FINISH: SELECTED POWDERCOAT
WINDOW: FIXED GLASS
GLASS: SAFETY GLASS

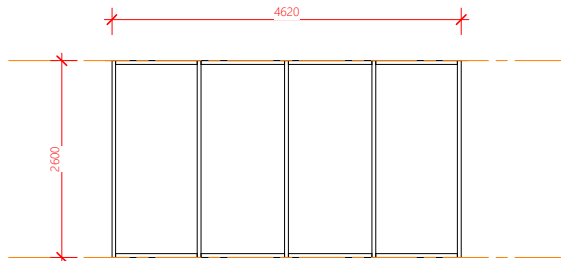


WINDOW TYPE B

LOCATION: EXTERNAL
FRAME TYPE: G.JAMES 475 SERIES
FRAME FINISH: SELECTED POWDERCOAT
WINDOW: FIXED GLASS
GLASS: SAFETY GLASS

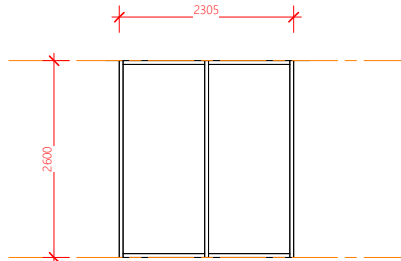

WINDOW TYPE C

LOCATION: EXTERNAL
FRAME TYPE: G.JAMES 475 SERIES
FRAME FINISH: SELECTED POWDERCOAT
WINDOW: FIXED GLASS
GLASS: SAFETY GLASS

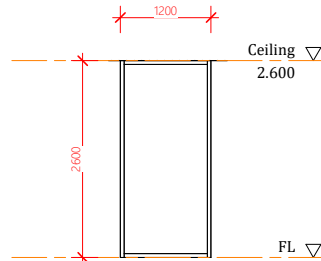

WINDOW TYPE C

LOCATION: EXTERNAL
FRAME TYPE: G.JAMES 475 SERIES
FRAME FINISH: SELECTED POWDERCOAT
WINDOW: FIXED GLASS
GLASS: SAFETY GLASS

REVISIONS

Rev	Description	Date
T1	TENDER ISSUE	12.03.2026

DO NOT SCALE THIS DRAWINGS



TENDER ISSUE



Project Details
REGISTRY REFURBISHMENT
Address
STANWELL POWER STATION
Drawing Title
WINDOW AND DOOR SCHEDULES



0483 988 655 M
info@designelements.com.au E
QBCC No: 1247120 BDAQ No: 0001677

Scale: 1 : 50	Rev:
Date: MARCH 2026	T1
Drawn: NJB	
Project No: 25_003	Drawing No: A1-700

