


REFER TO SITE PLAN & CONSULTANT
DRAWINGS FOR EXTERNAL SERVICES

REVISIONS		
Rev	Description	Date
T1	TENDER ISSUE	12.03.2026

DO NOT SCALE THIS DRAWINGS

 

TENDER ISSUE

Client



Project Details

WAREHOUSE REFURB

Address

STANWELL POWER
STATION

Drawing Title


EXISTING FLOOR PLAN


BUILDING DESIGNERS


0483 988 655 
info@designelements.com.au 

QBCC No: 1247120 BDAQ No: 0001677


Scale: 1 : 100 Rev: **T1**
Date: MARCH 2026
Drawn: NJB
Project No: Drawing No:
25_003 A2-200

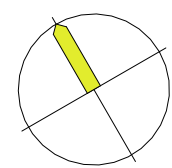

13/03/2026 11:27:04 AM

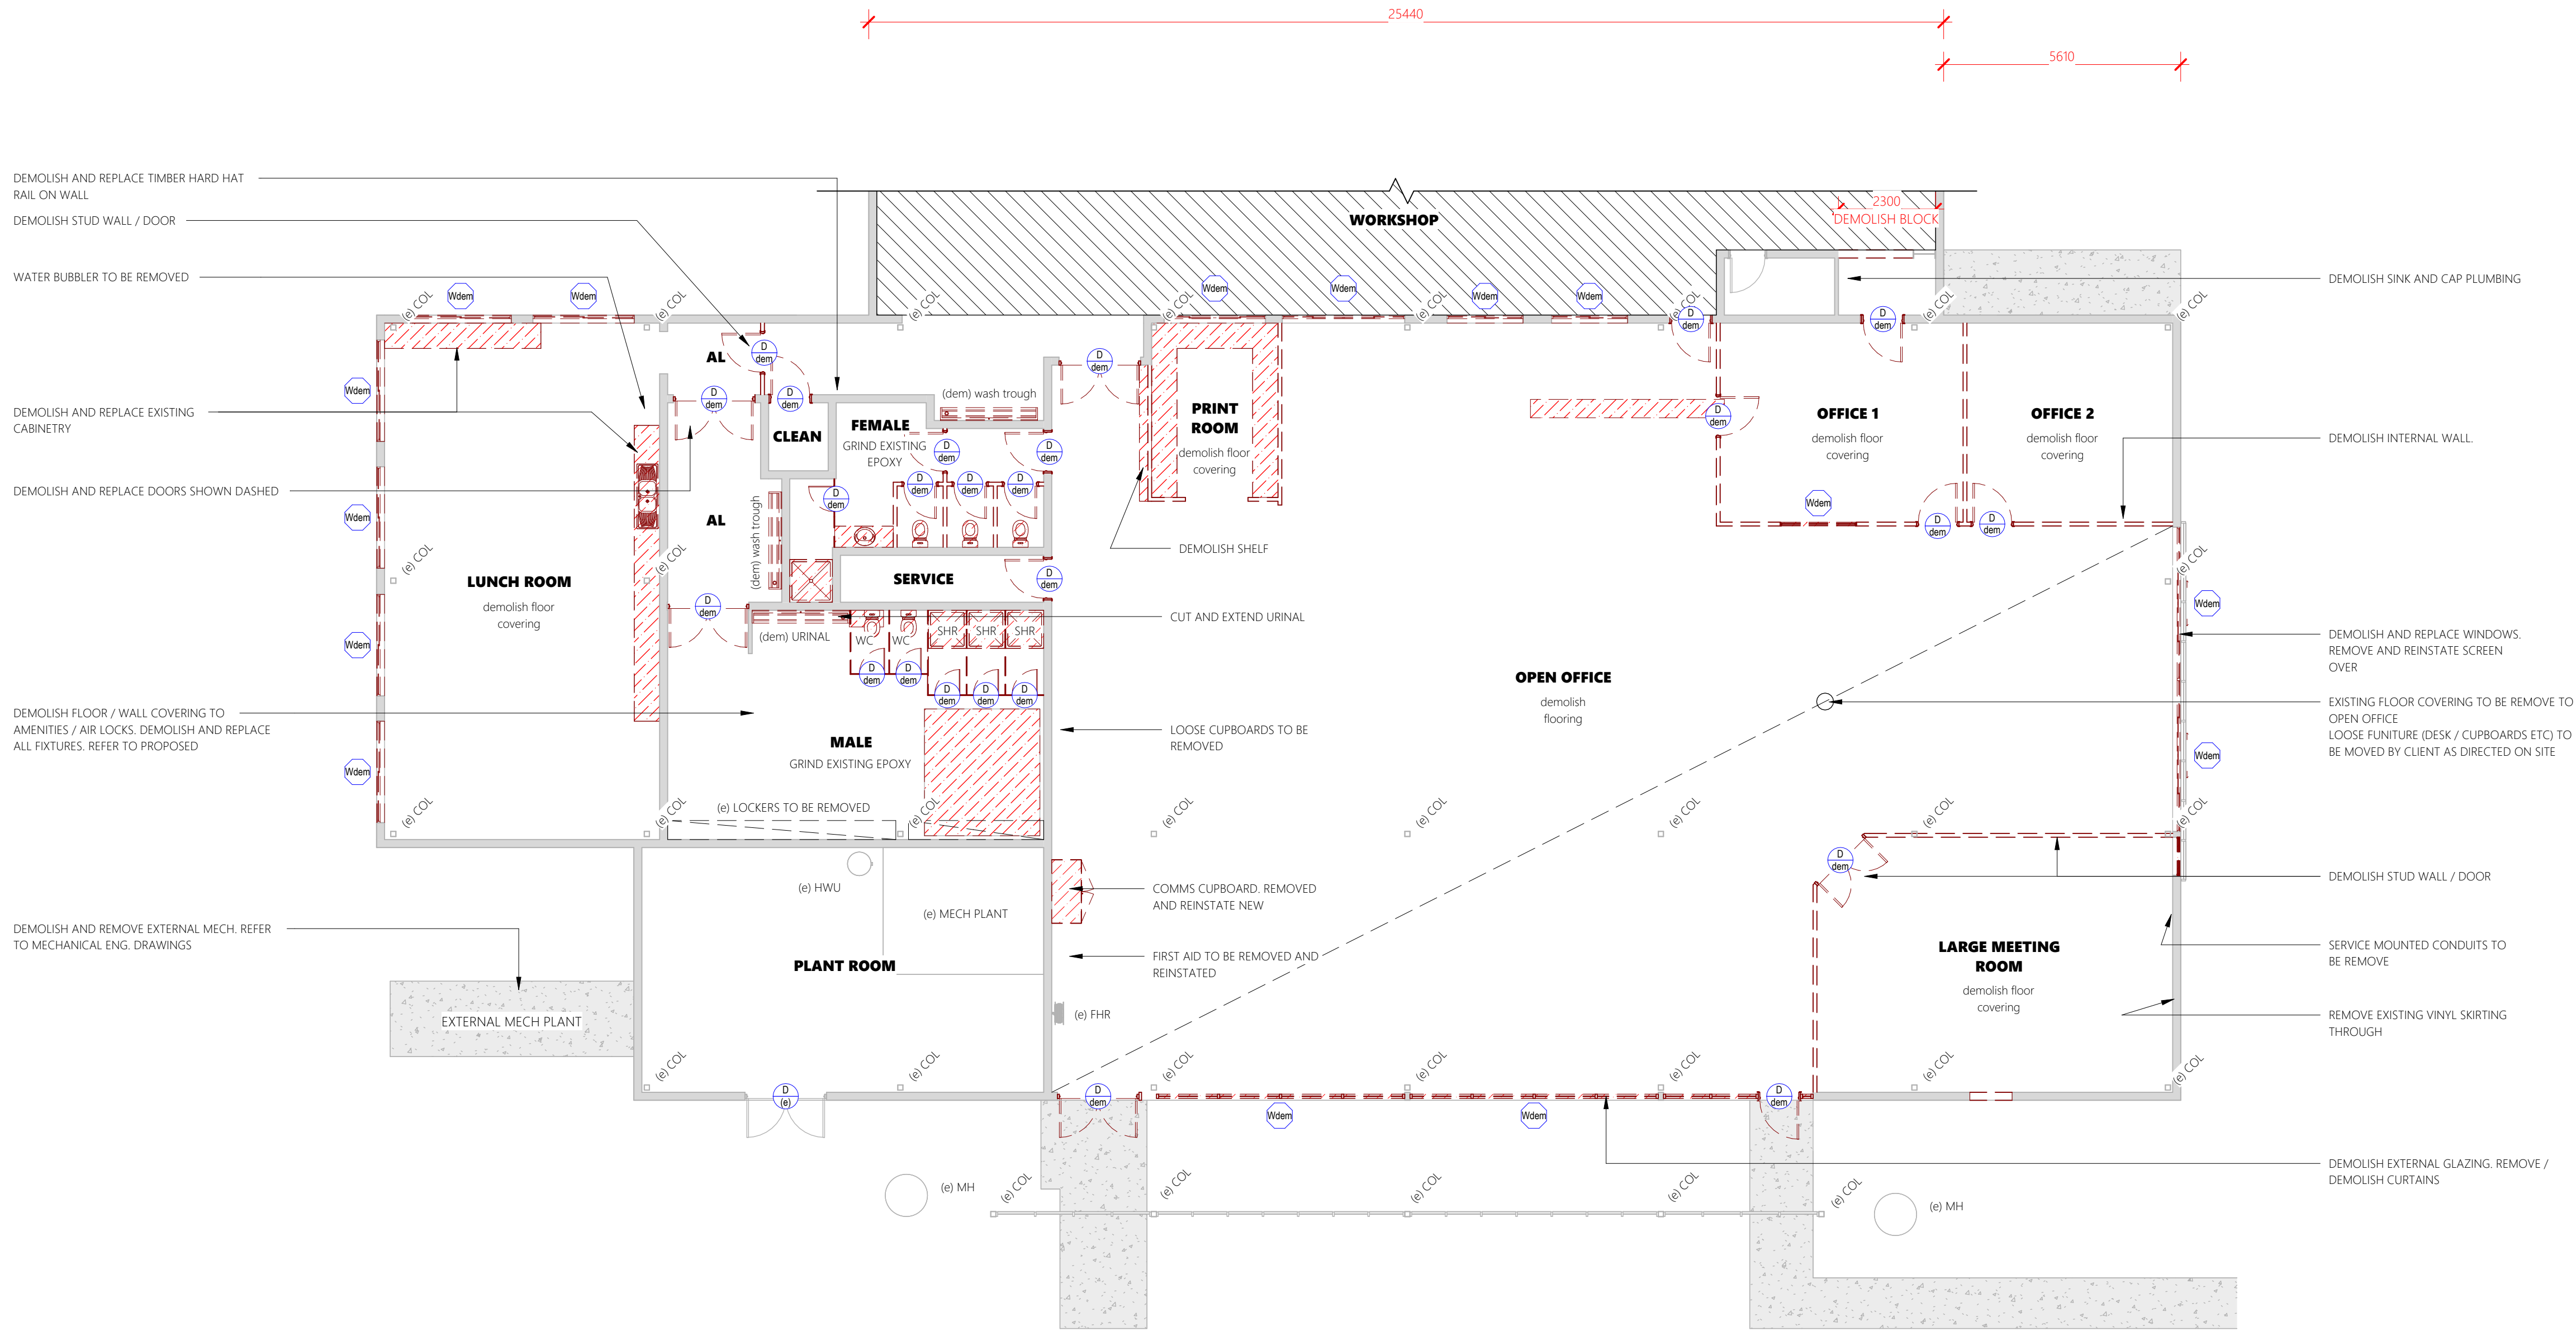


Existing Main Workshop Floor
Plan

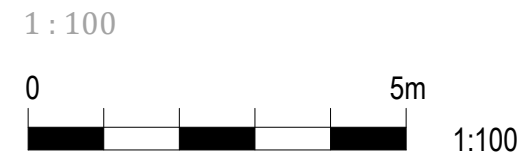


REFER TO SITE PLAN & CONSULTANT
DRAWINGS FOR EXTERNAL SERVICES

REVISIONS		
Rev	Description	Date
T1	TENDER ISSUE	12.03.2026

DO NOT SCALE THIS DRAWINGS

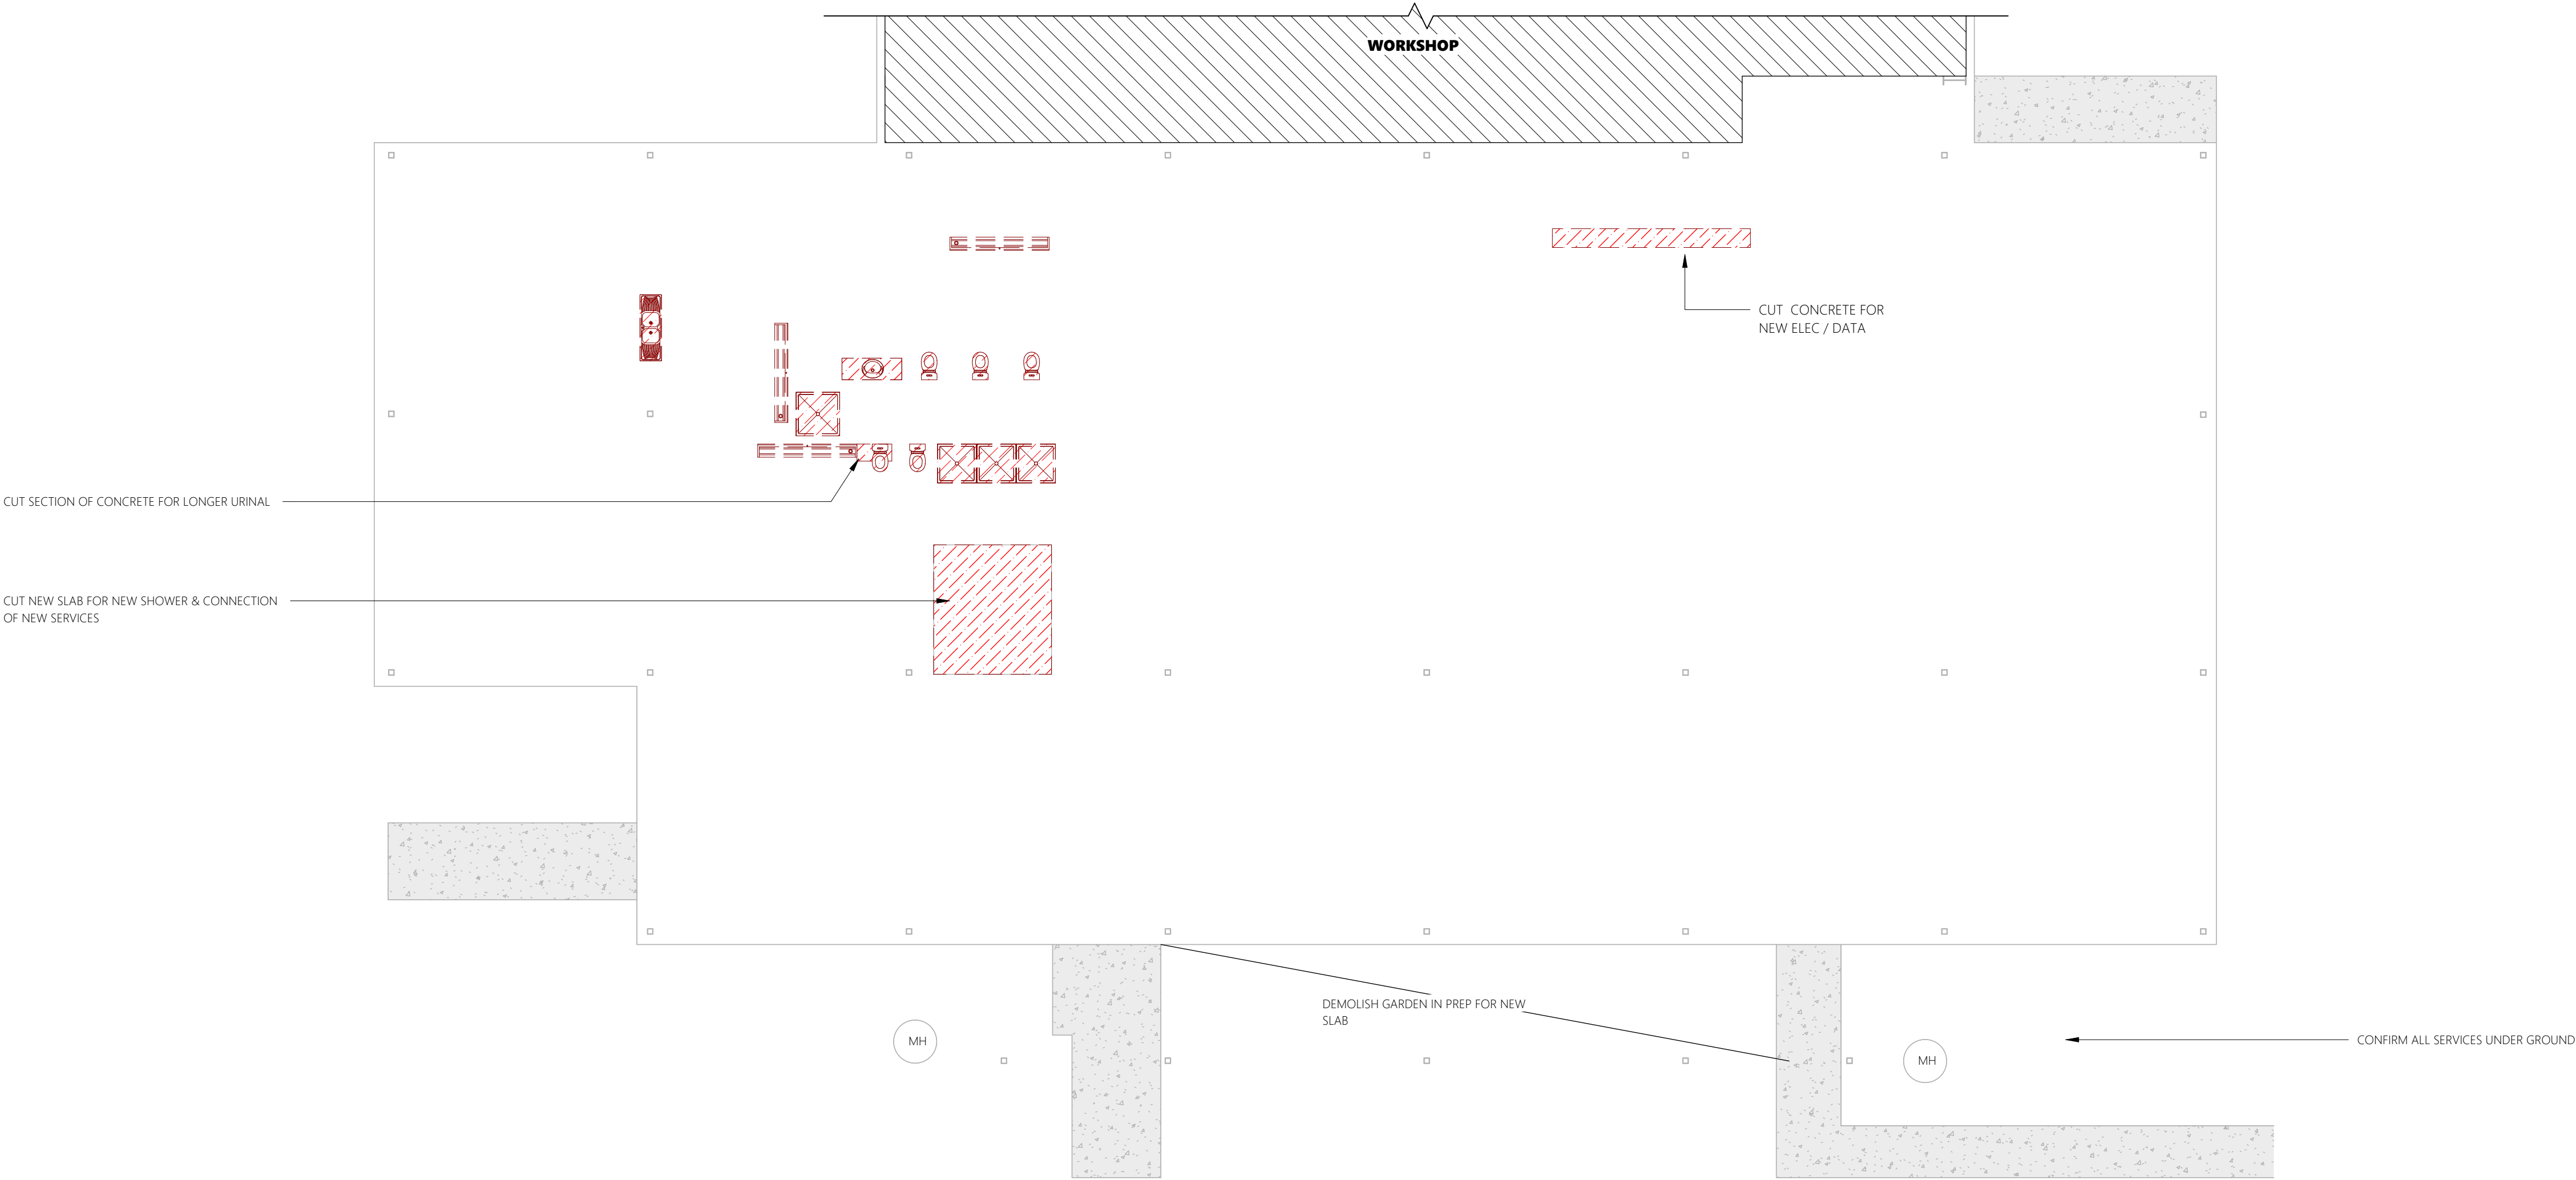

Existing Slab Plan

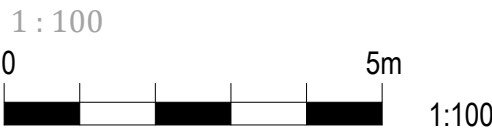

TENDER ISSUE

Client



Project Details

WAREHOUSE REFURB

Address

STANWELL POWER STATION

Drawing Title

EXISTING SLAB PLAN




0483 988 655 **M**
info@dezignelements.com.au **E**
QBCC No: 1247120 BDAQ No: 0001677

Scale: 1 : 100
Date: MARCH 2026
Drawn: Author

Rev: **T1**

Project No: 25_003
Drawing No: A2-201


13/03/2026 11:27:04 AM

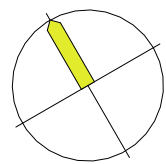

LIGHTS AND AC FIXTURES SHOWN FOR INDICATION ONLY. CONFIRM ON SITE AND READ IN CONJUNCTION WITH CONSULTANT DRAWINGS

REVISIONS		
Rev	Description	Date
T1	TENDER ISSUE	12.03.2026

DO NOT SCALE THIS DRAWINGS

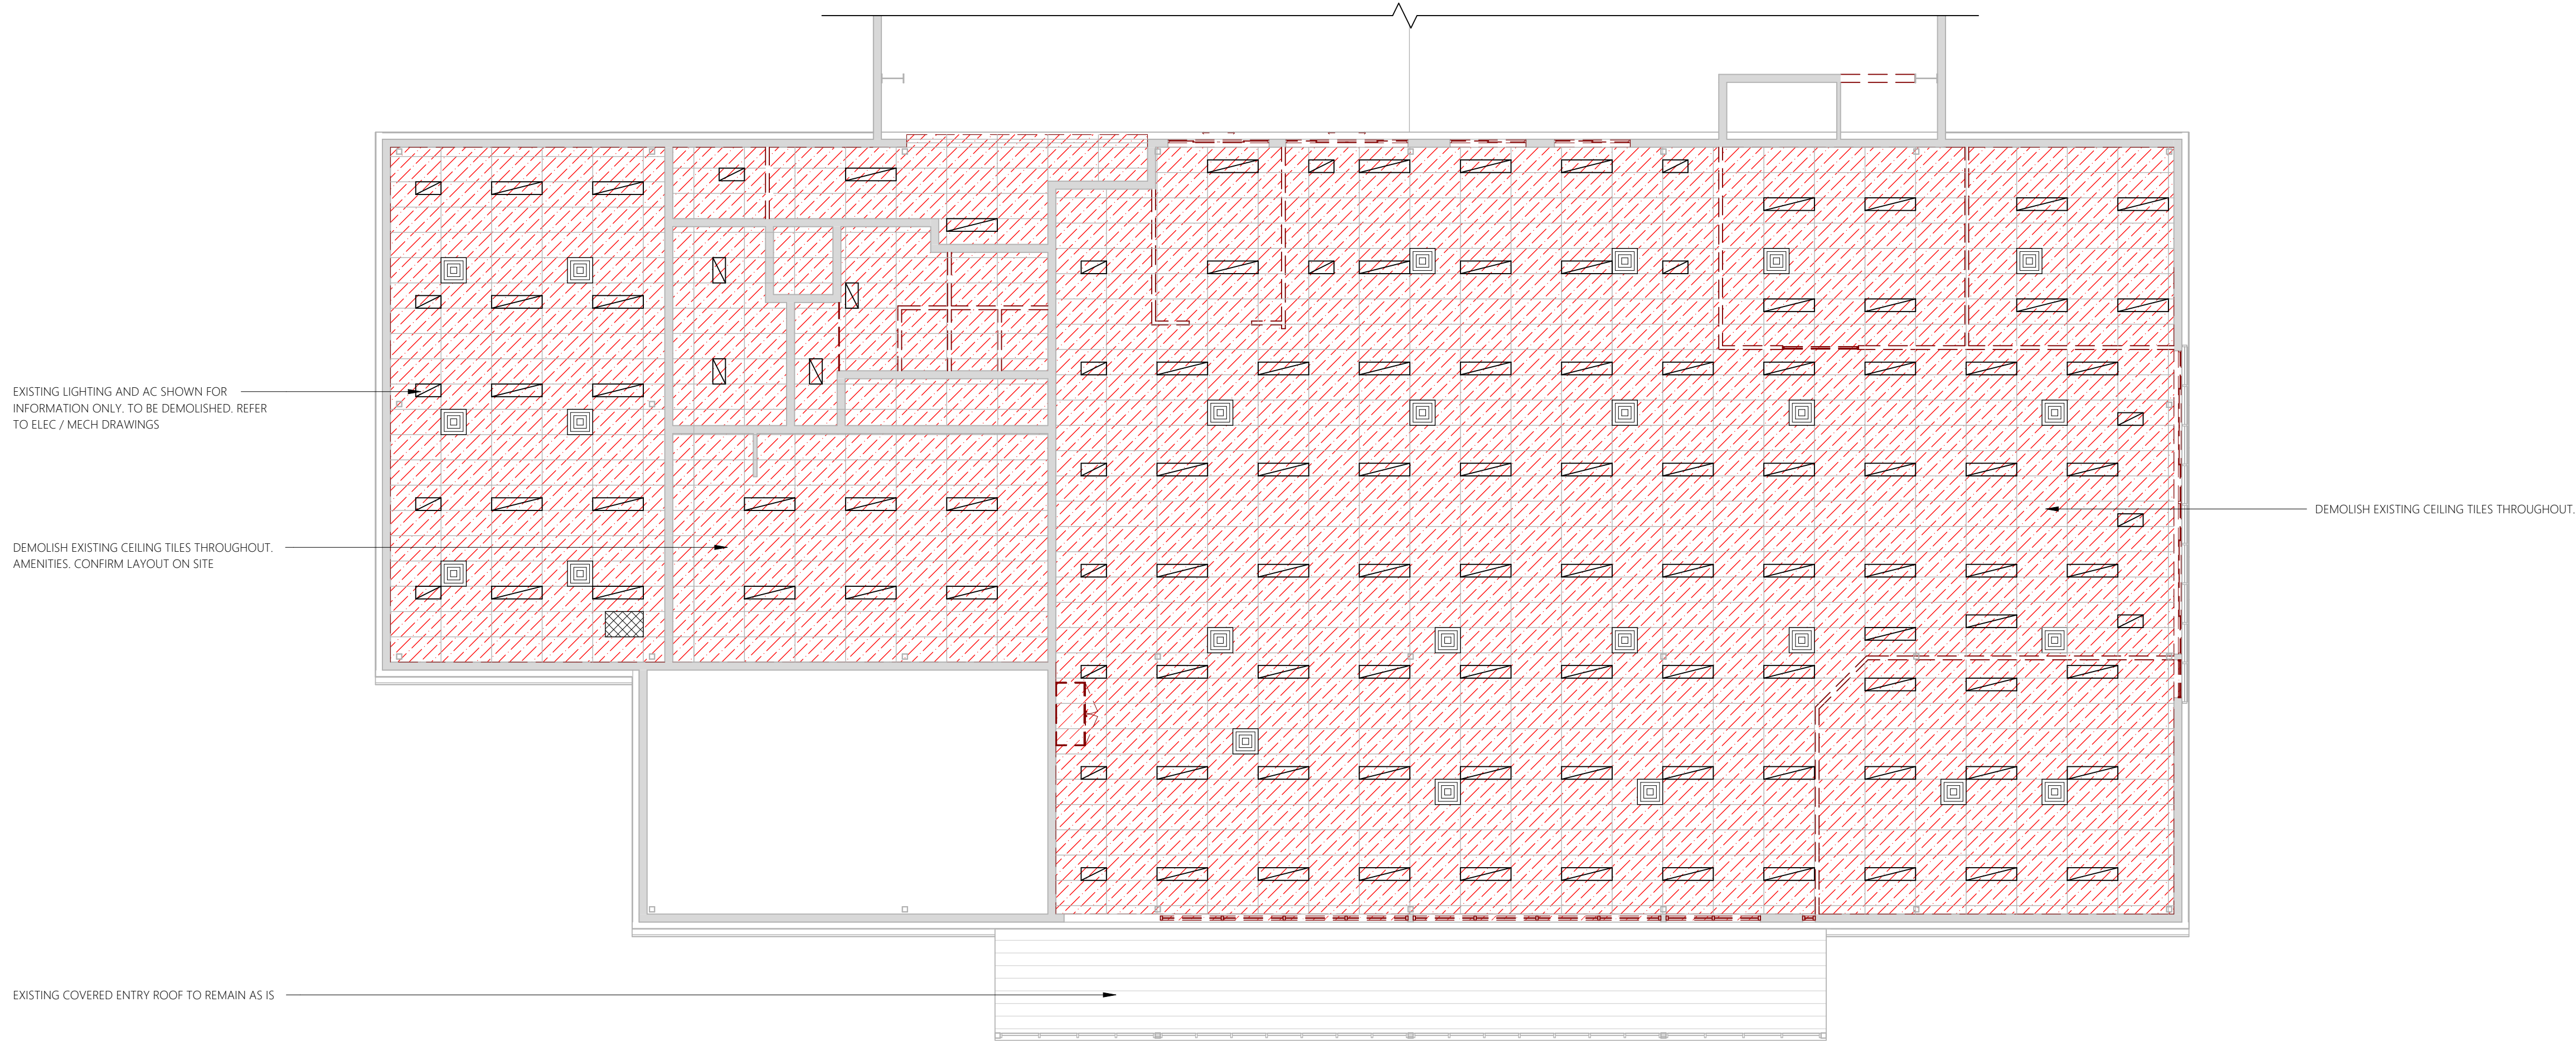

Existing Ceiling Plan



TENDER ISSUE

Client

Project Details

WAREHOUSE REFURB

Address

STANWELL POWER STATION

Drawing Title

EXISTING CEILING PLAN

0483 988 655 **M**
info@dezignelements.com.au **E**
QBCC No: 1247120 BDAQ No: 0001677

Scale: 1 : 100 Rev: **T1**
Date: MARCH 2026
Drawn: Author

Project No: 25_003 Drawing No: A2-202

REVISIONS		
Rev	Description	Date
T1	TENDER ISSUE	12.03.2026

DO NOT SCALE THIS DRAWINGS

TENDER ISSUE

Client



Project Details

WAREHOUSE REFURB

Address

STANWELL POWER STATION

Drawing Title

EXISTING ROOF PLAN



0483 988 655 
info@dezi elements.com.au 
QBCC No: 1247120 BDAQ No: 0001677



Scale: 1 : 100 Rev:

T1

Date: MARCH 2026

Drawn: Author

Project No: 25_003 Drawing No: A2-203

 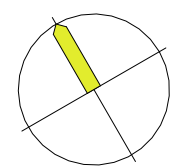


Existing Roof Plan




REVISIONS		
Rev	Description	Date
T1	TENDER ISSUE	12.03.2026

DO NOT SCALE THIS DRAWINGS

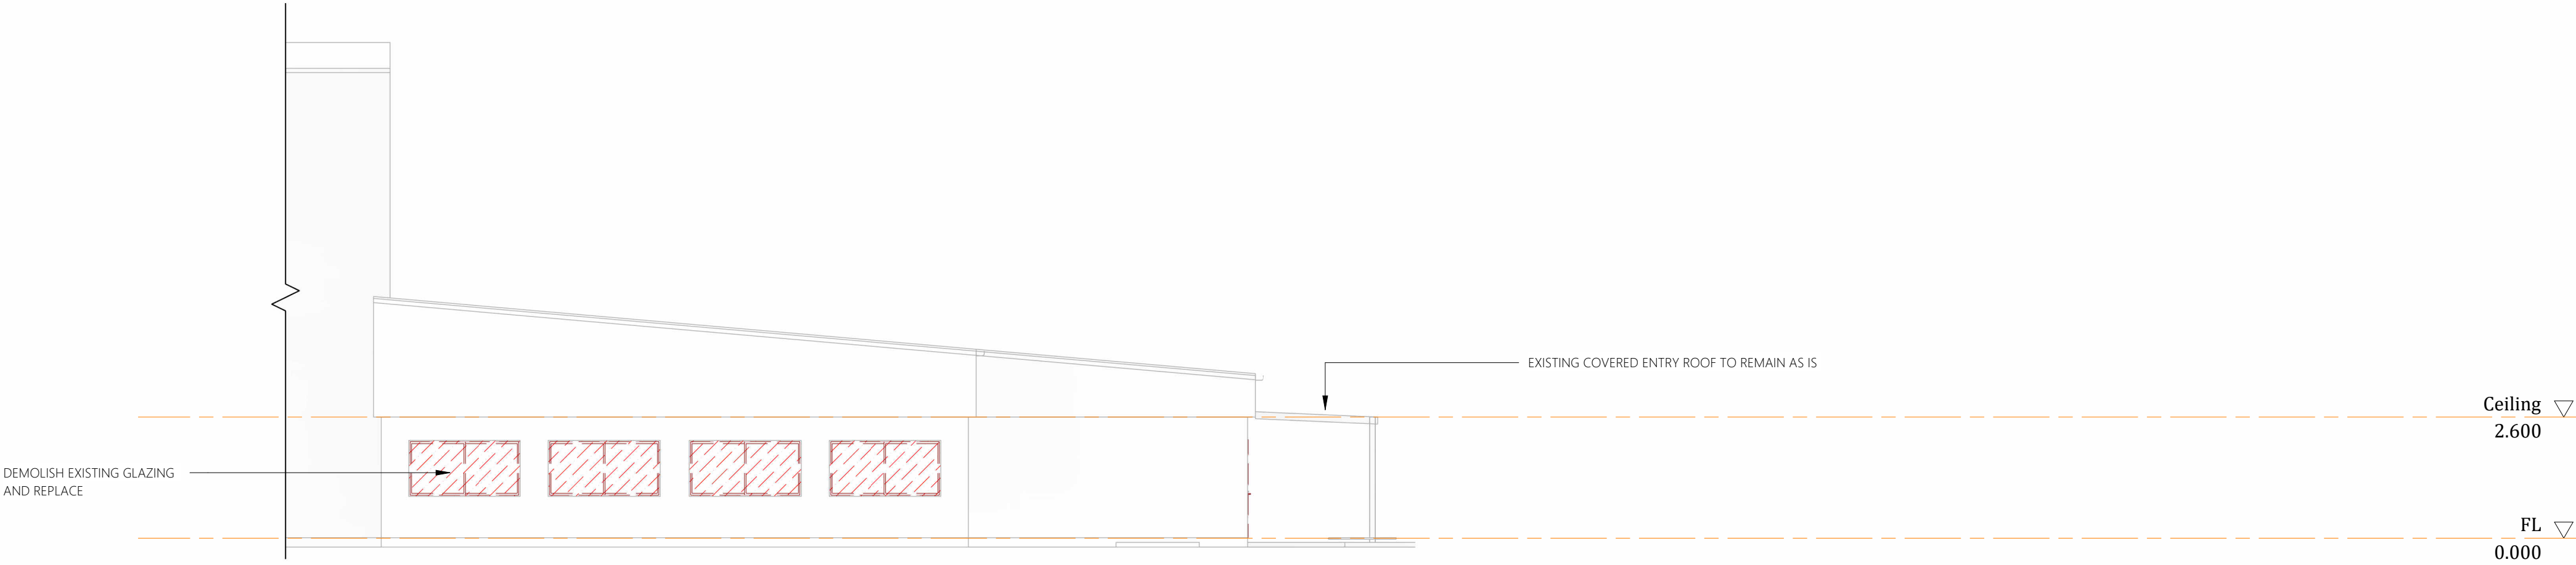


Existing Elevation 1

1 : 100

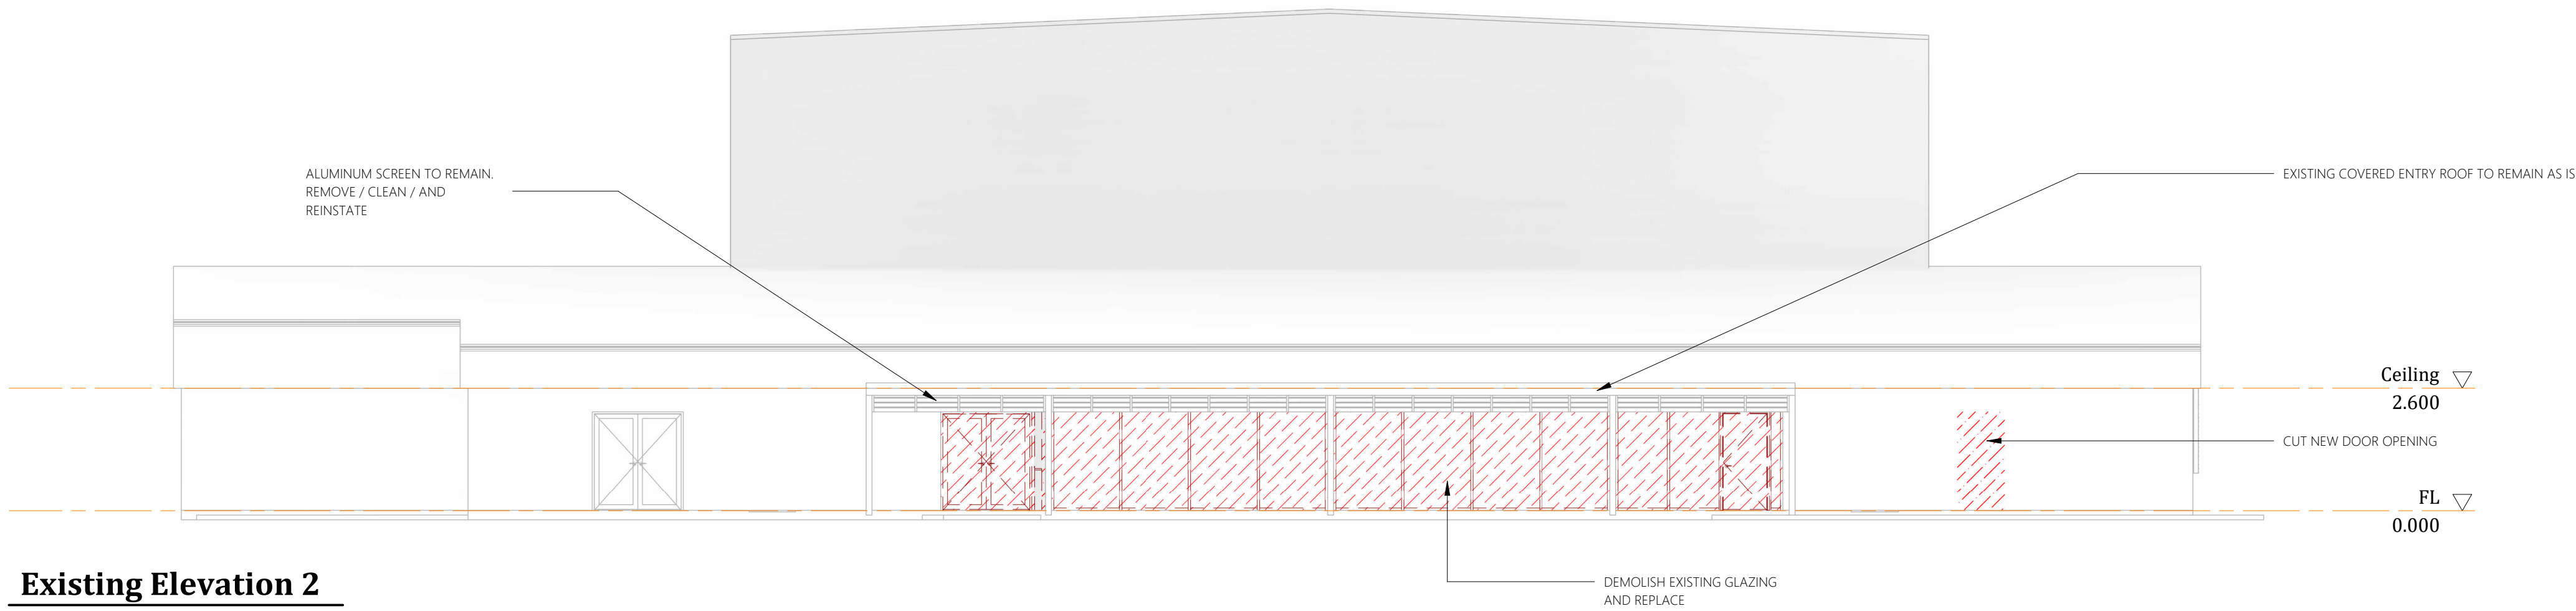

Existing Elevation 2

1 : 100

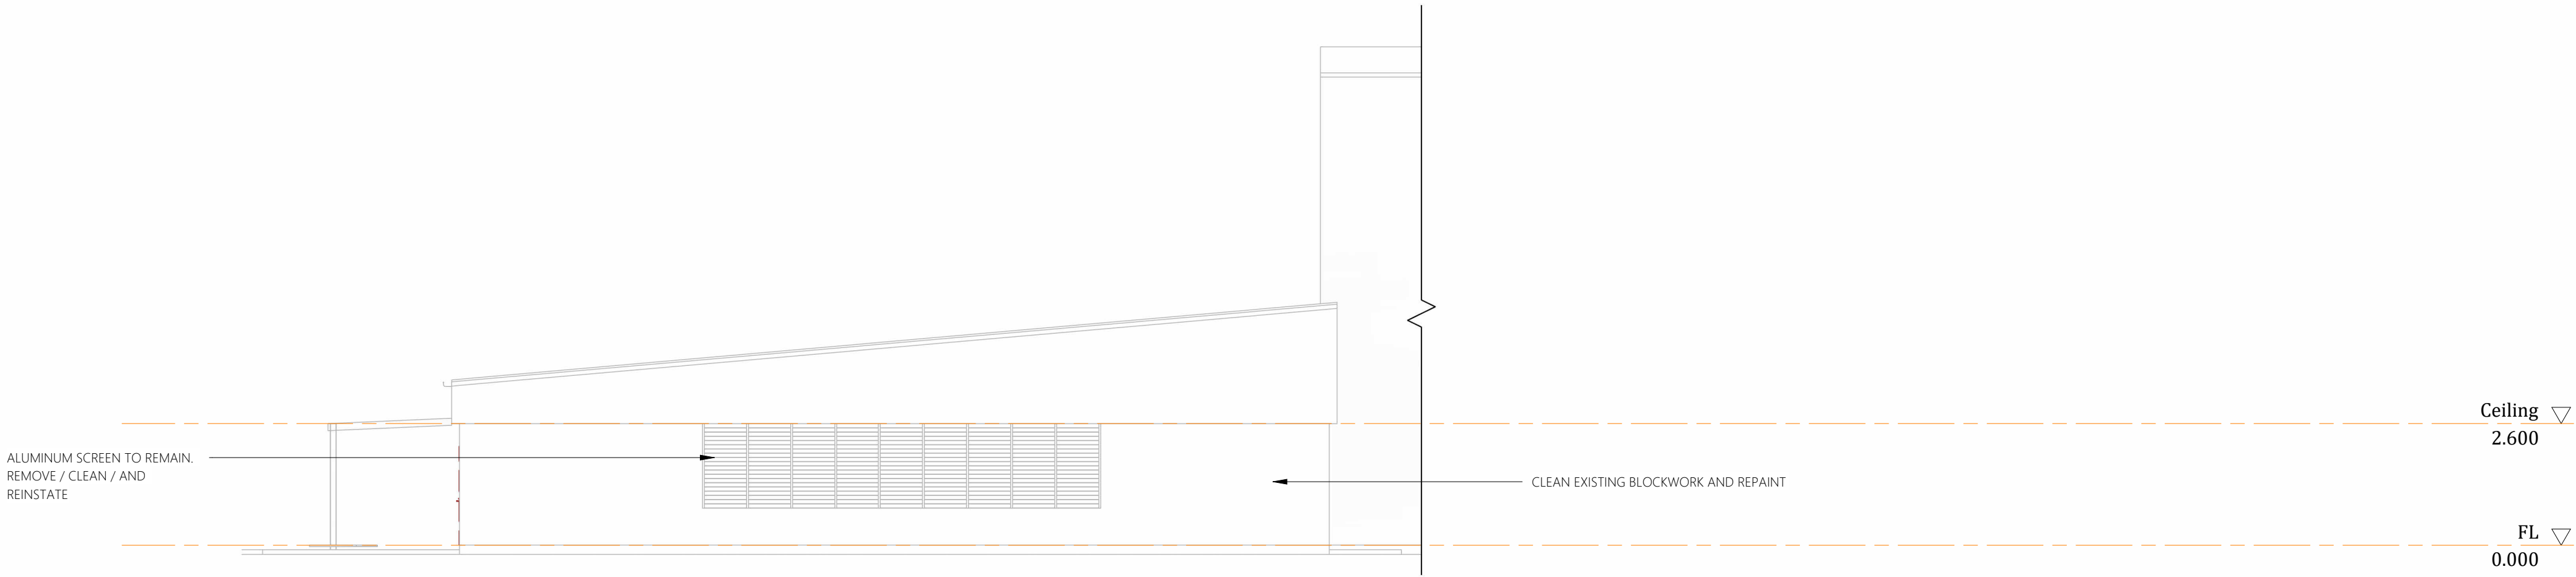

Existing Elevation 3

1 : 100

TENDER ISSUE



Project Details
WAREHOUSE REFURB
Address
STANWELL POWER STATION
Drawing Title
EXISTING ELEVATIONS





0483 988 655 **M**
info@dezi elements.com.au **E**
QBCC No: 1247120 BDAQ No: 0001677

Scale: 1 : 100	Rev: T1
Date: MARCH 2026	
Drawn: Author	
Project No: 25_003	Drawing No: A2-204

13/03/2026 11:27:10 AM

_Proposed Main Workshop Floor Plan

1 : 100

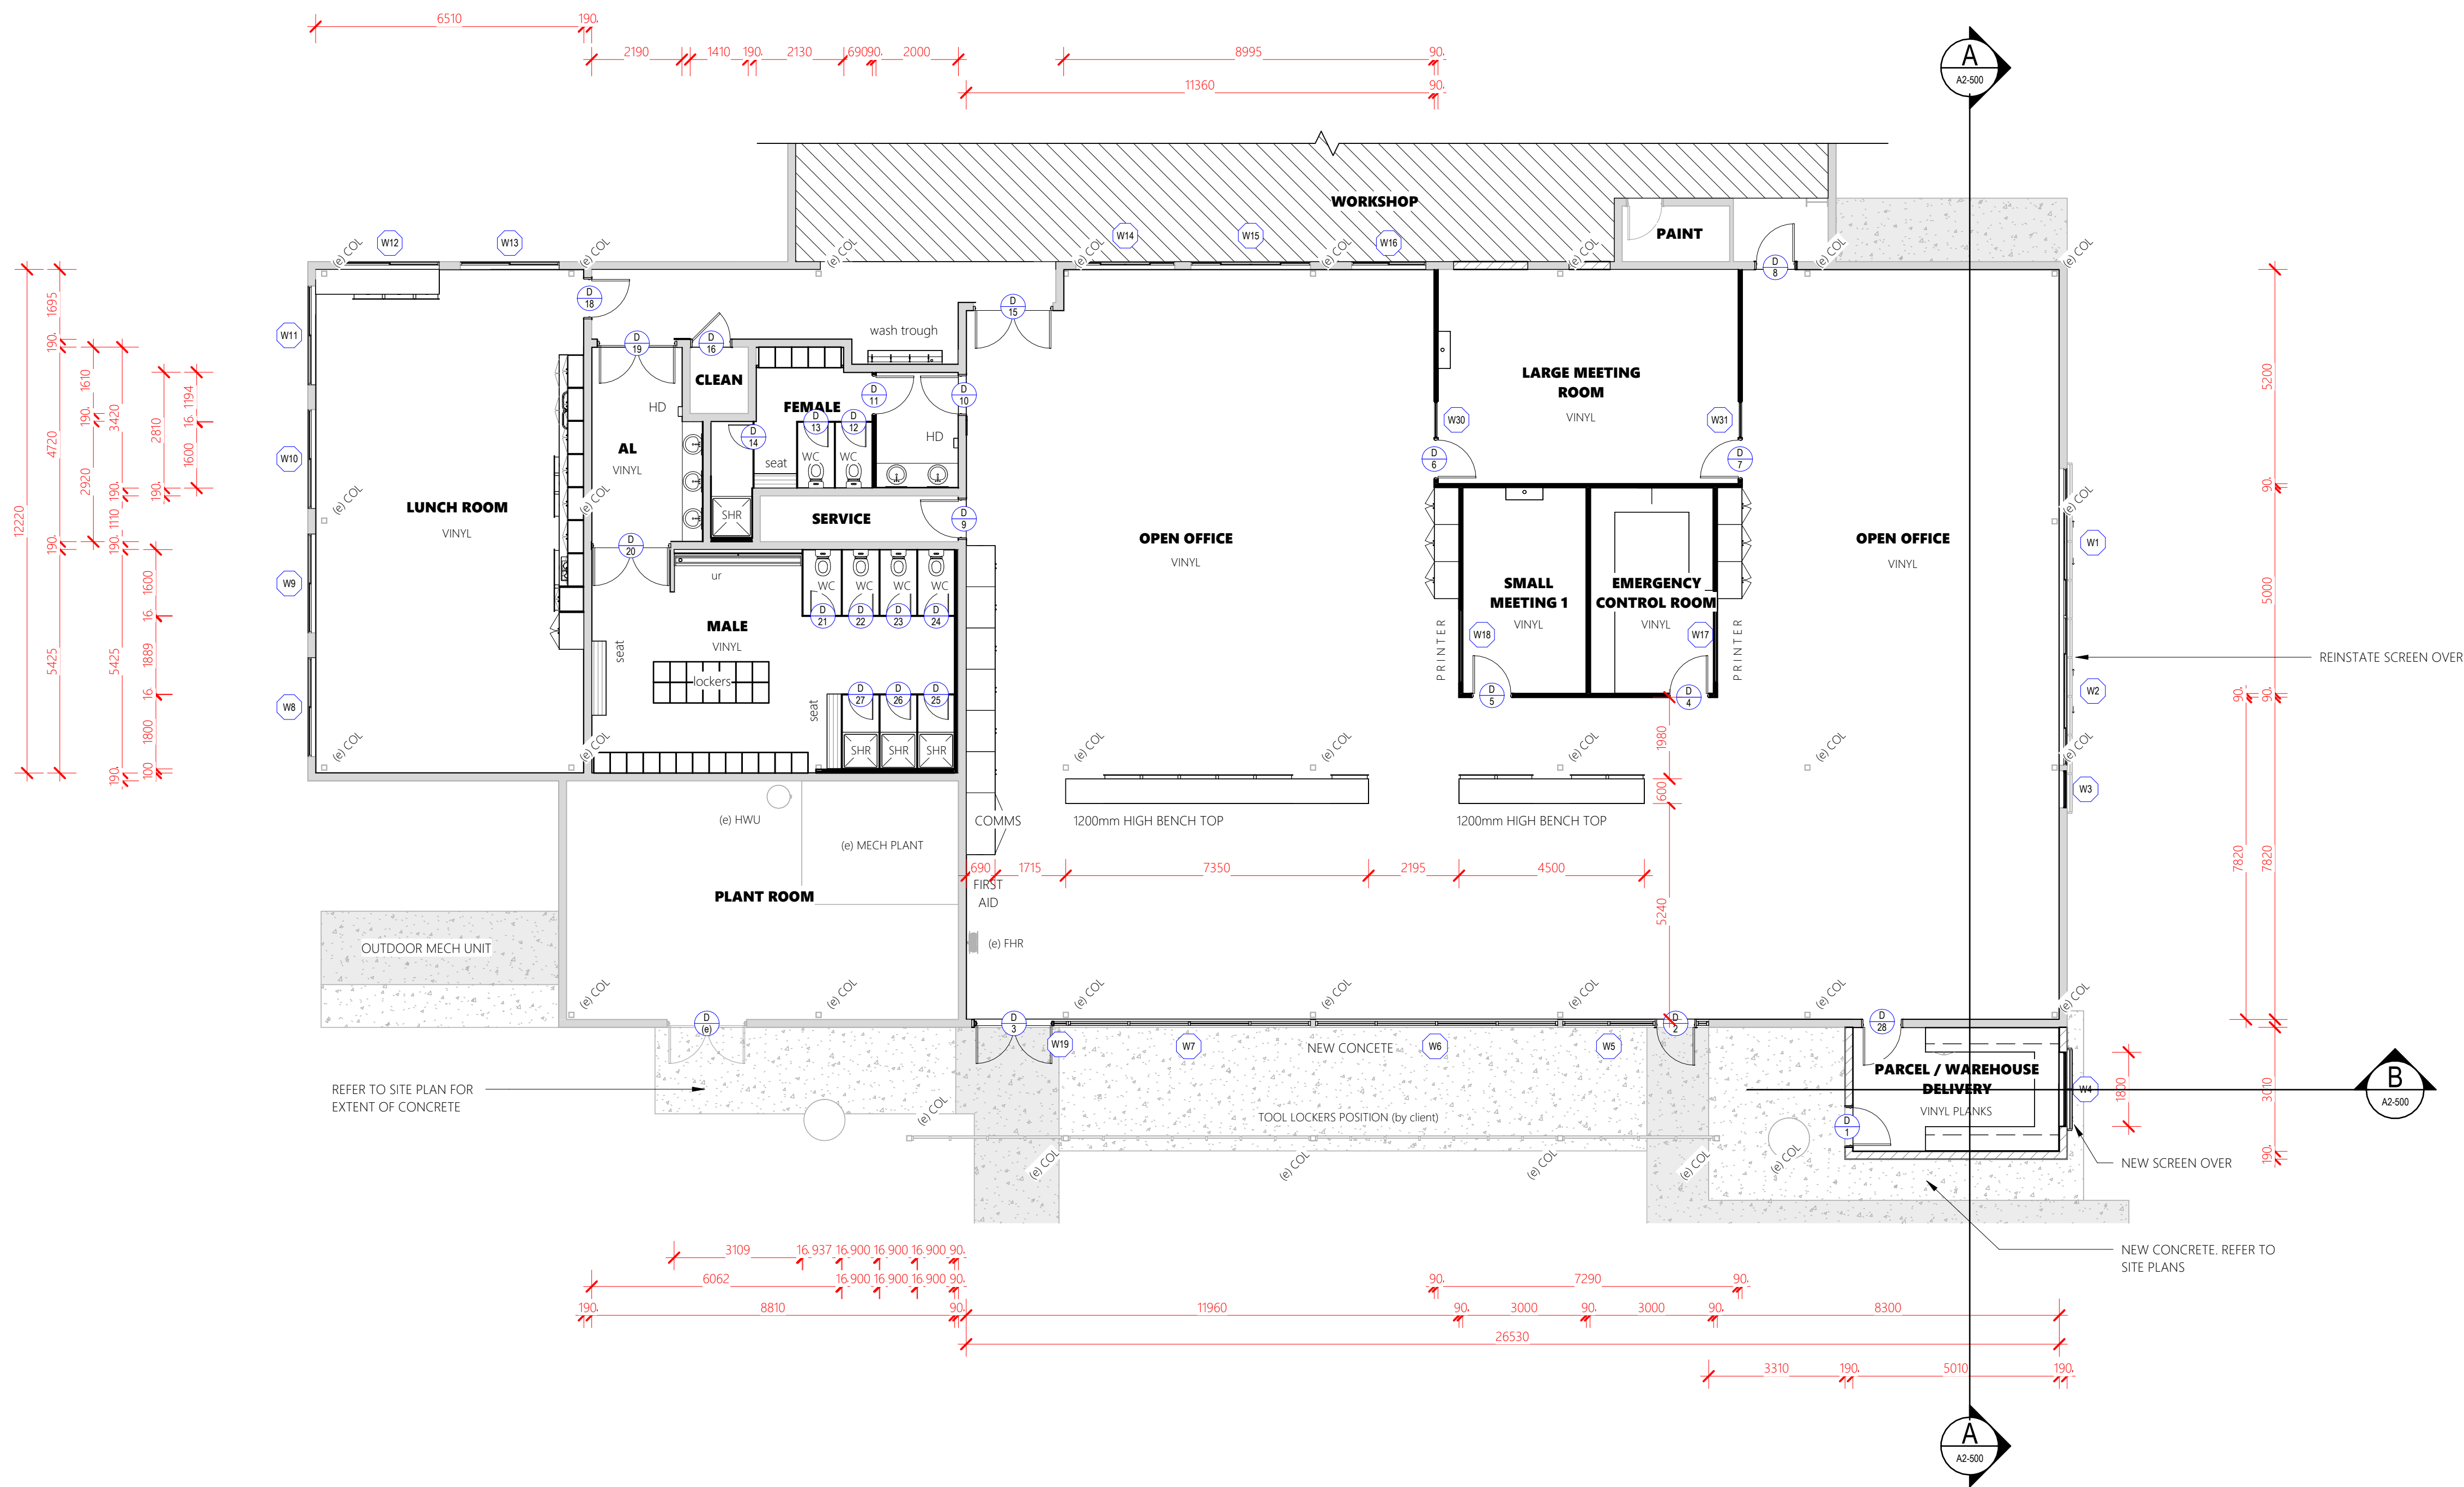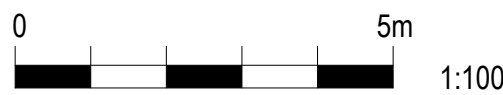

REVISIONS

Rev	Description	Date
T1	TENDER ISSUE	12.03.2026

DO NOT SCALE THIS DRAWINGS

KEYNOTE LEGEND

(e)	Existing
dem	Demolish
(R)	Remove / Reinstate

BSN	Basin
COL	Column
CON	Condenser
CPD	Cupboard
CS	Cleaners Sink
CT	Cooktop
DP	Downpipe
DW	Dish Washer
FAP	Fire Alarm Panel
FHR	Fire Hose Reel
FR	Fridge (By Client)
L	Locker
HD	Hand Driver (Air Blade)
OV	Oven
RH	Range Hood
DW	Dish Washer
SK	Sink
SB	Switch Board
UR	Urinal

TENDER ISSUE



Project Details
WAREHOUSE REFURB

Address
STANWELL POWER STATION

Drawing Title
PROPOSED FLOOR PLAN



0483 988 655
info@designelements.com.au

QBCC No: 1247120 BDAQ No: 0001677


Scale: 1 : 100 Rev:

Date: MARCH 2026 **T1**

Drawn: Author

Project No: Drawing No:

25_003 A2-300

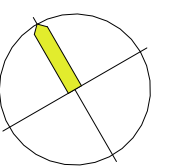


CONFIRM LOCATION OF UNDERGROUND SERVICES
PRIOR TO CUTTING OR EXCAVATION.


REFER TO CONSULTANT DRAWINGS

REVISIONS		
Rev	Description	Date
T1	TENDER ISSUE	12.03.2026

DO NOT SCALE THIS DRAWINGS

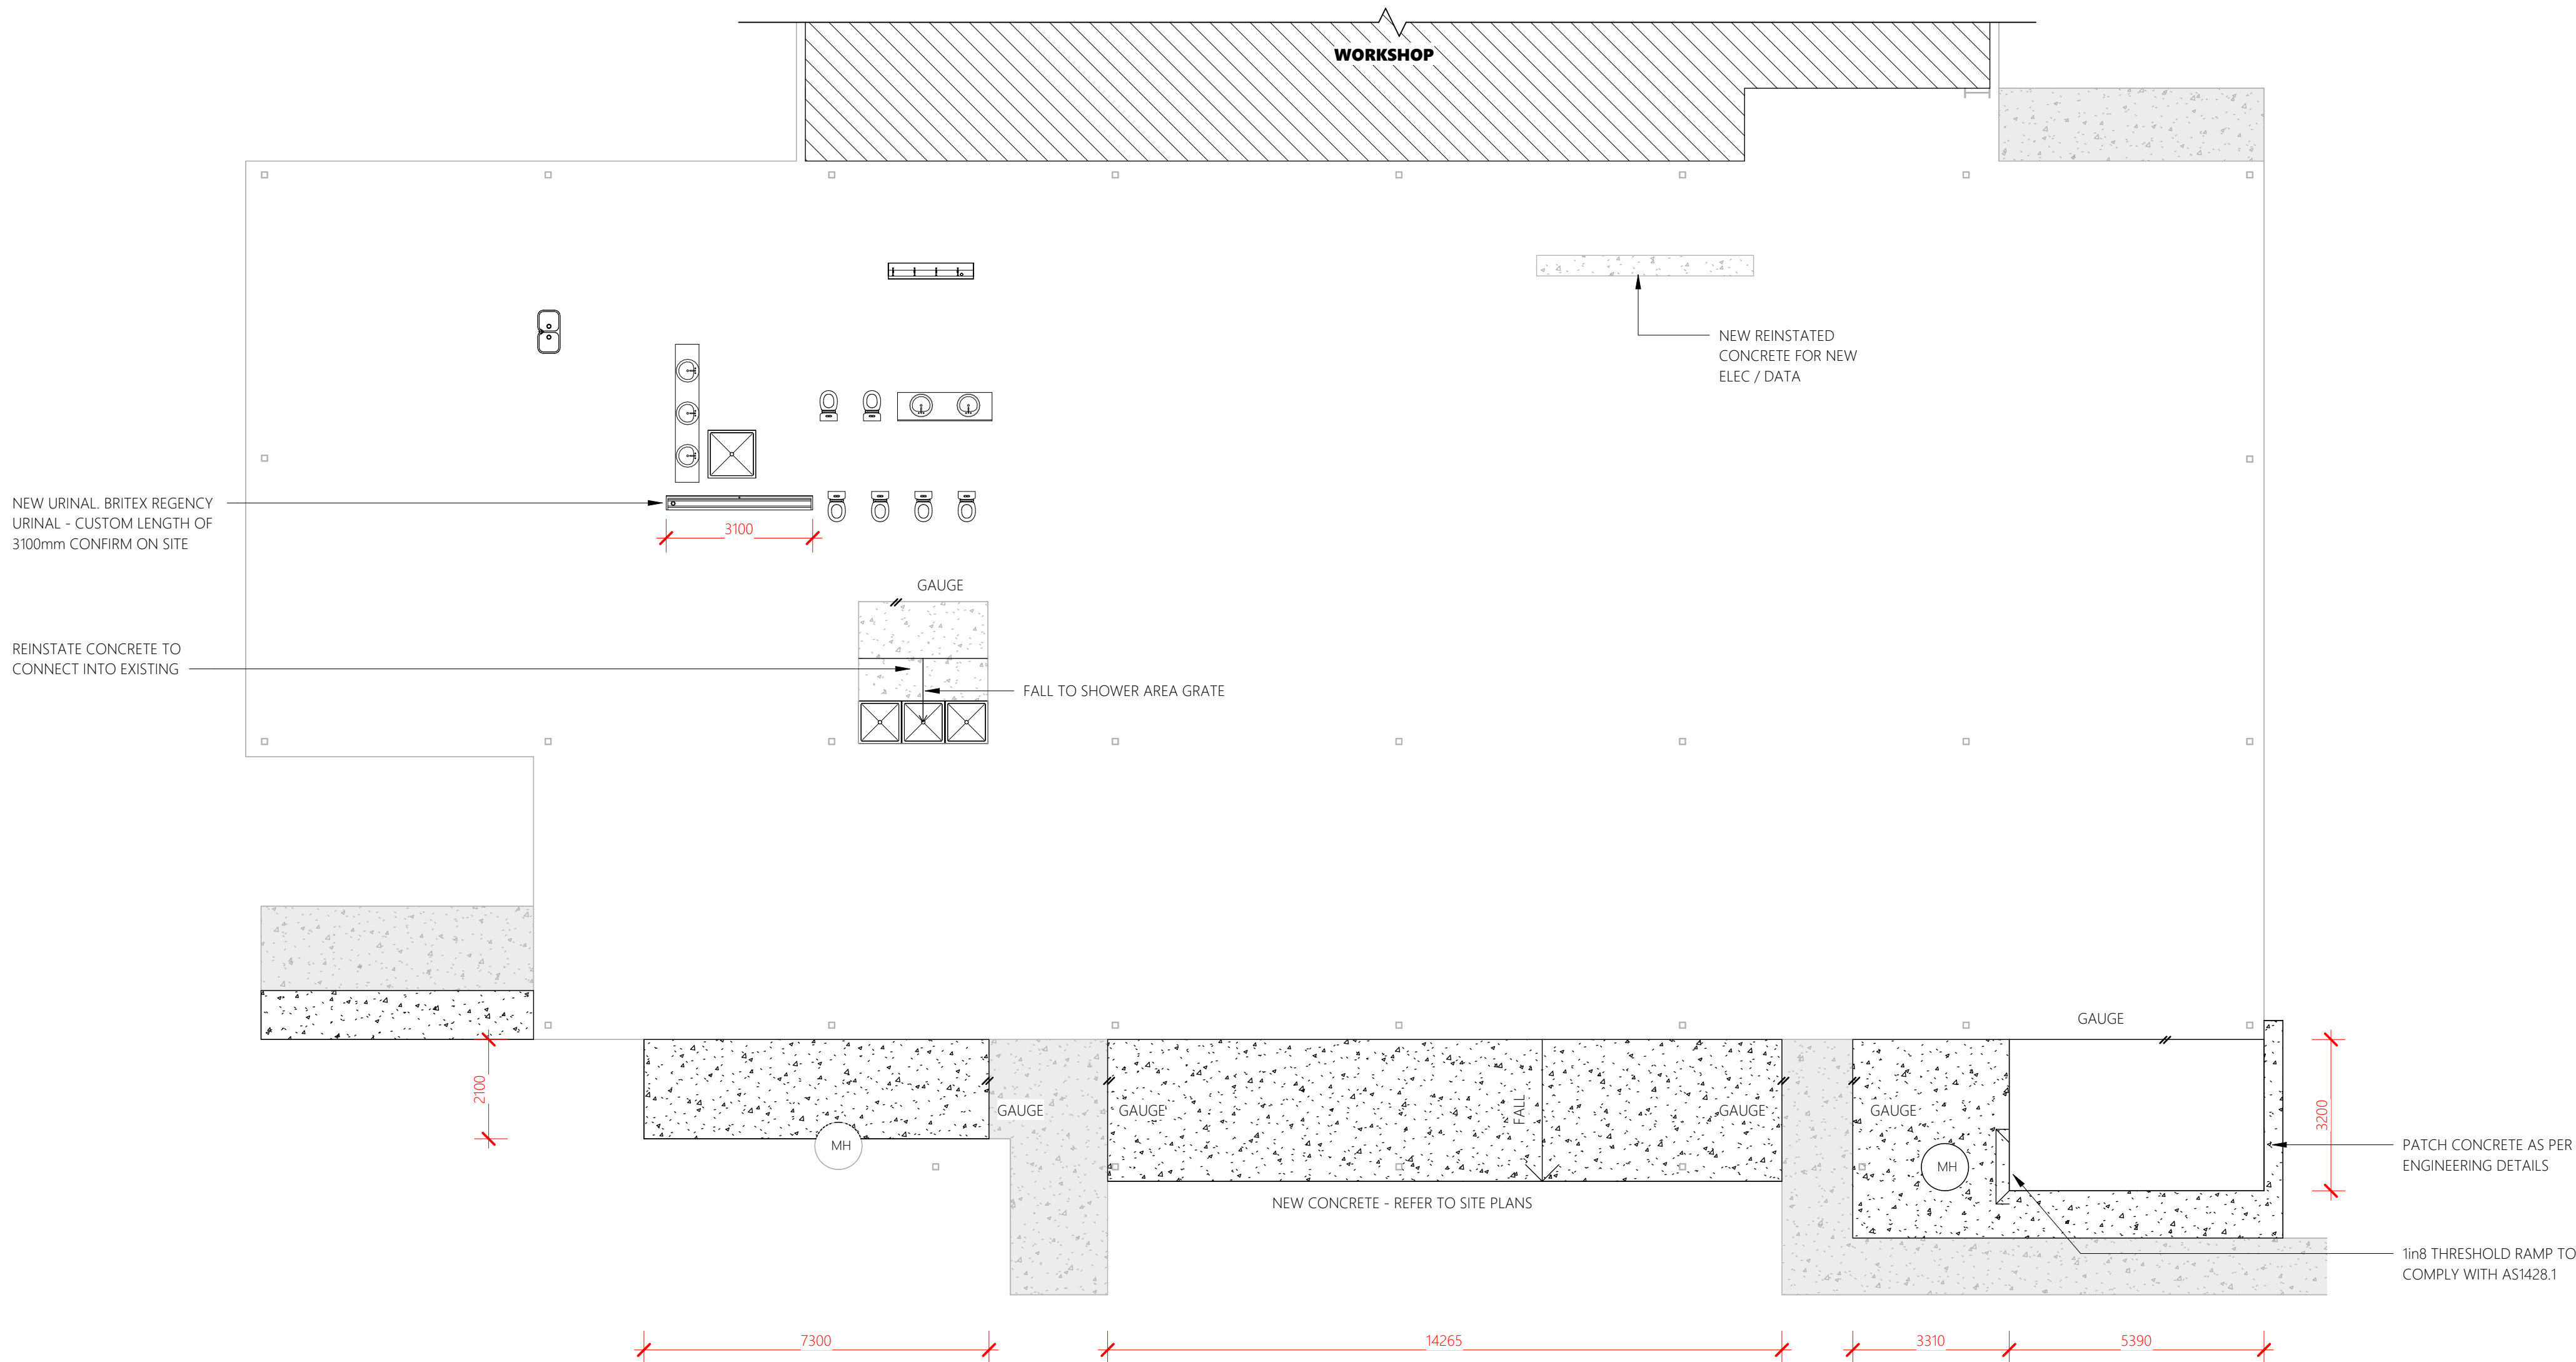

Proposed Slab Plan

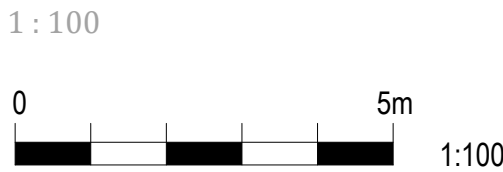

TENDER ISSUE

Client

 stanwell

Project Details

WAREHOUSE REFURB

Address

STANWELL POWER STATION

Drawing Title

PROPOSED SLAB PLAN

 **designelements**
BUILDING DESIGNERS


0483 988 655 **M**
info@designelements.com.au **E**

QBCC No: 1247120 BDAQ No: 0001677

Scale: 1 : 100 Rev: **T1**
Date: MARCH 2026
Drawn: Author

Project No: Drawing No:
25_003 A2-301

13/03/2026 11:27:13 AM

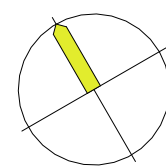


CONFIRM EXISTING GRID SETOUT ON SITE

NEW CEILING INSULATION THROUGHOUT
SHADED AREA - REFER SPEC


CEILING LEGEND

- 1200 x 600 APEX ACOUSTIC CEILING
TILES (OR APPROVED EQUAL NEW
TILES THROUGH RENOVATED AREA)
- PROVIDE CONCEALED FIX RIBBEDTRIMDEX
SOFFIT SHEETING (TO MATCH EXISTING)
- INSULATION ABOVE CEILING TILES

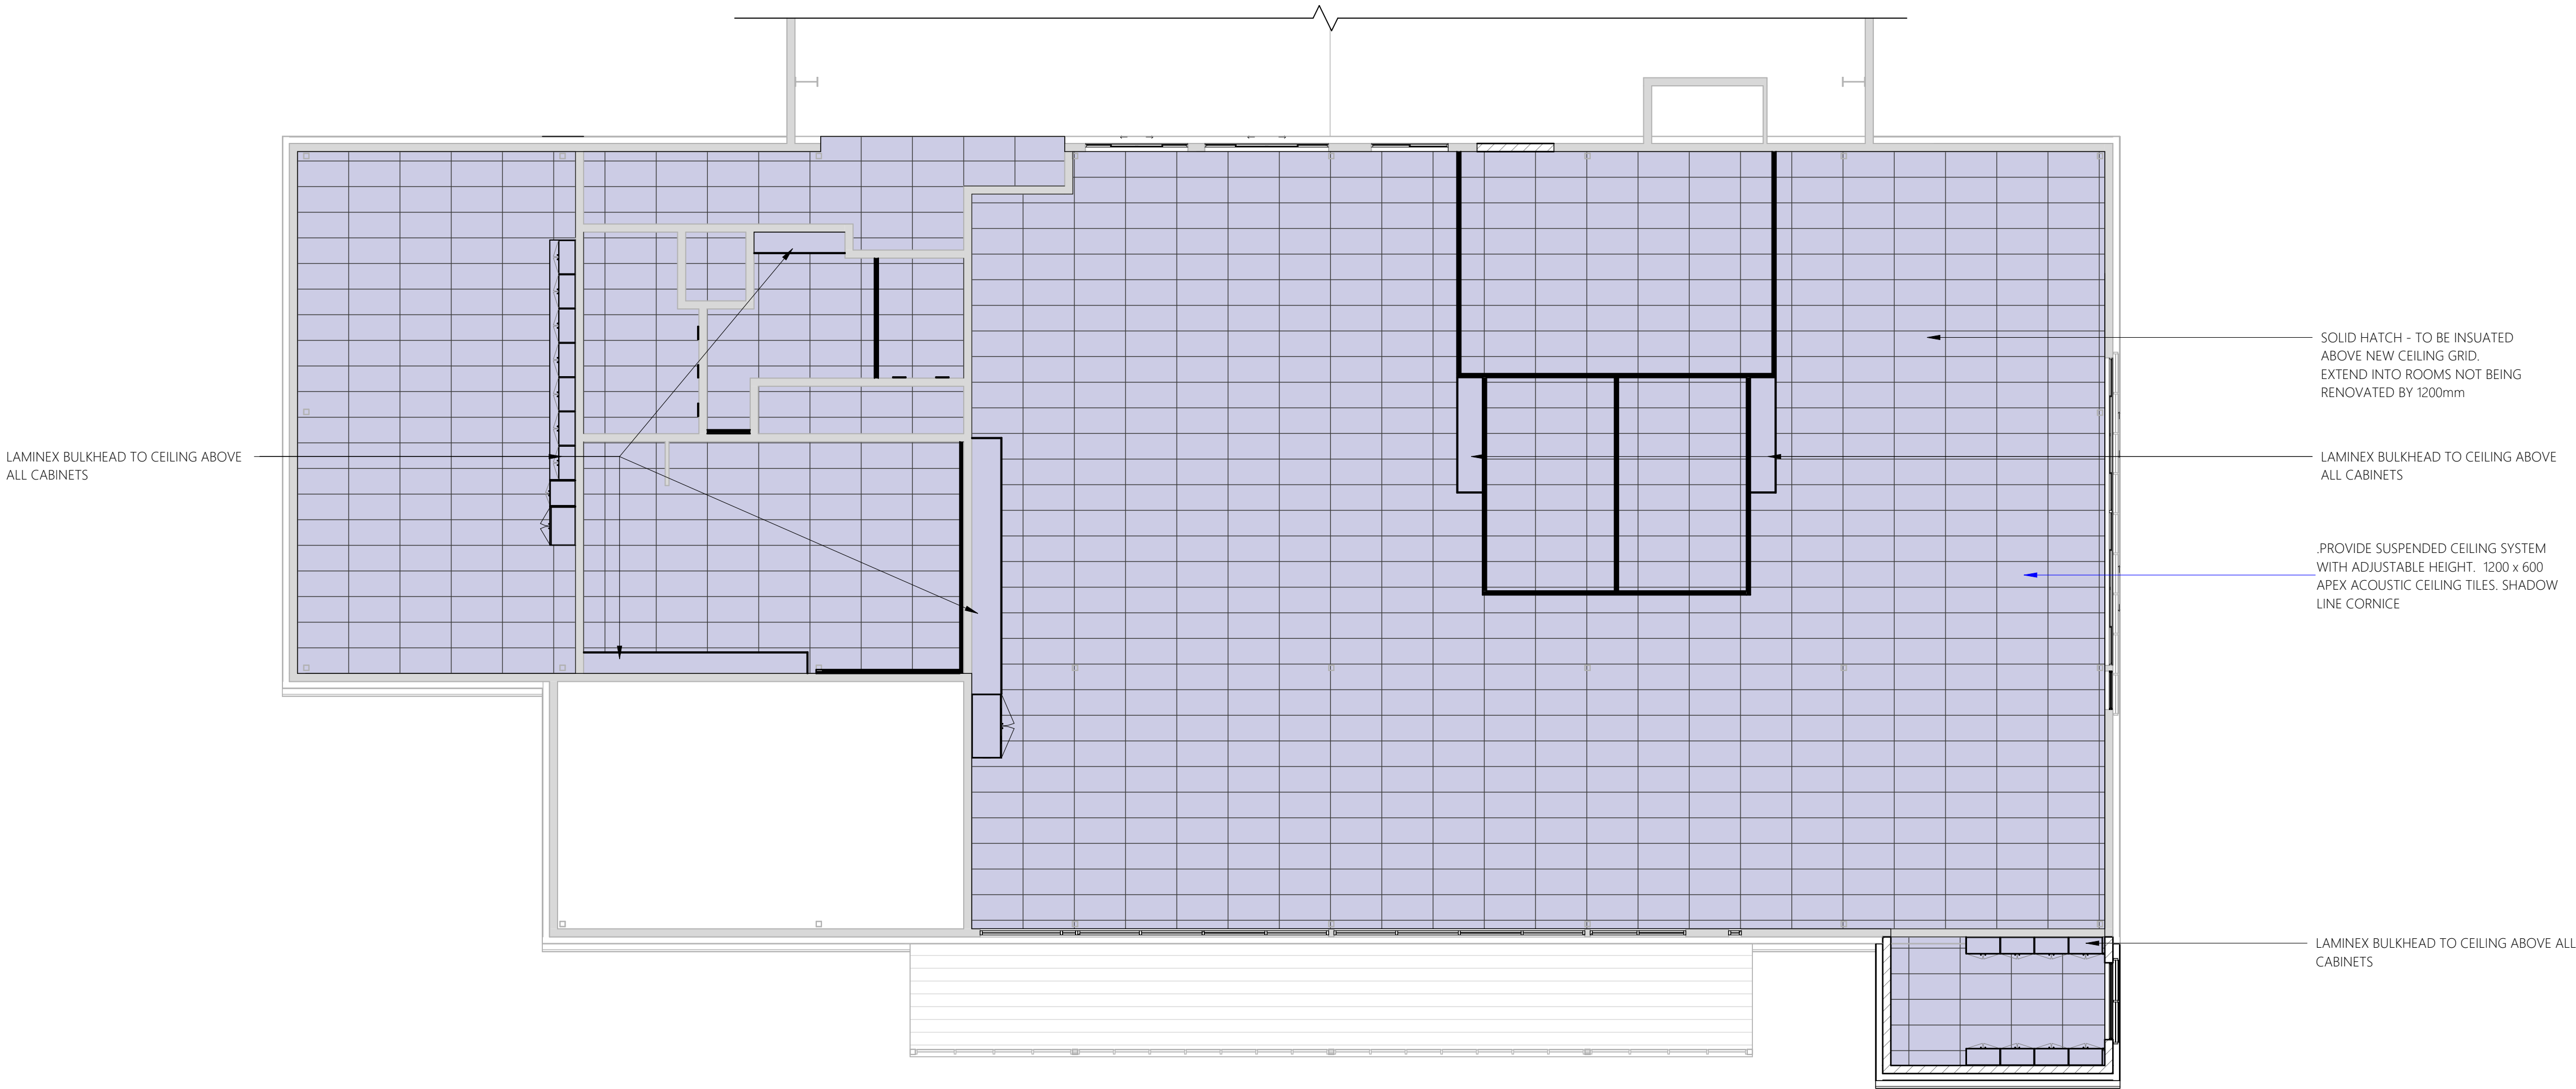

Proposed Ceiling Plan

1 : 100

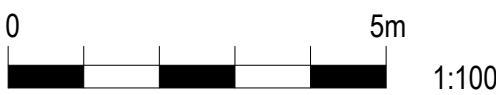

REVISIONS

Rev	Description	Date
T1	TENDER ISSUE	12.03.2026

DO NOT SCALE THIS DRAWINGS



TENDER ISSUE

Client

Project Details

WAREHOUSE REFURB

Address

STANWELL POWER STATION

Drawing Title

PROPOSED CEILING PLAN

0483 988 655

info@deziignelements.com.au

QBCC No: 1247120 BDAQ No: 0001677


Scale: 1 : 100 Rev:

Date: MARCH 2026 **T1**

Drawn: Author

Project No: Drawing No:

25_003 A2-302

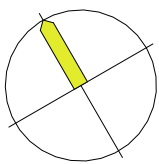

CONFIRM EXISTING ROOF PITCH ON SITE

REVISIONS		
Rev	Description	Date
T1	TENDER ISSUE	12.03.2026

DO NOT SCALE THIS DRAWINGS

PROVIDE COLORBOND OVER FLASHING FOR NEW KITCHEN RANGE HOOD TO RIDGE LINE

5.00°

EXISTING PARAPET WALL TO REMAIN

PROVIDE COLORBOND FLASHING BETWEEN PARAPET AND NEW ROOF SHEETING
PROVIDE STRAMMIT MONOCLAD ROOF SHEETING (TO MATCH EXISTING PROFILE) - CONTRACTOR TO CONFIRM ON SITE


PROVIDE COLORBOND FASCIA / GUTTER. REFER SPEC. TO MATCH EXISTING PROFILE

PROVIDE KATTSAFE ROOF MOUNTED SUPPORT LADDER BRACKET (RL402)

5.00°

Proposed Roof Plan

1 : 100

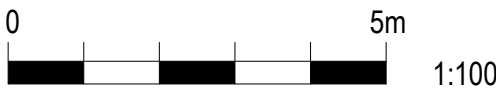

TENDER ISSUE

Client

 **stanwell**

Project Details

WAREHOUSE REFURB

Address

STANWELL POWER STATION


Drawing Title

PROPOSED ROOF PLAN


 **dezin**
BUILDING DESIGNERS

0483 988 655 **M**
info@dezinements.com.au **E**
QBCC No: 1247120 BDAQ No: 0001677


Scale: 1 : 100 Rev: **T1**
Date: MARCH 2026
Drawn: Author
Project No: Drawing No:
25_003 A2-303

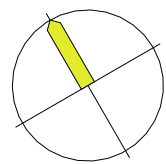


13/03/2026 11:27:14 AM

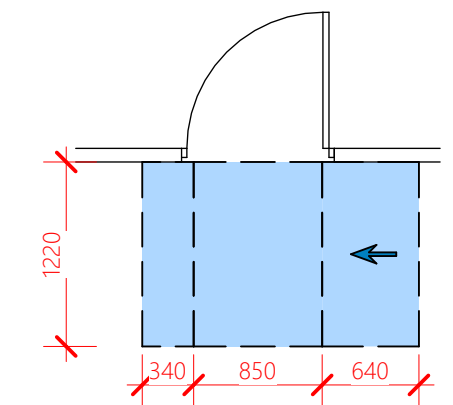


HINGE-SIDE APPROACH
DOOR OPENS AWAY FROM USER

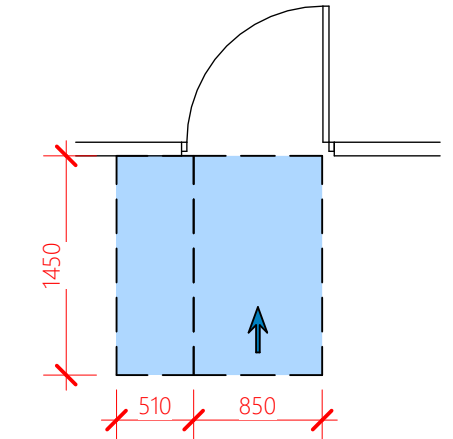


FRONT APPROACH
DOOR OPENS AWAY FROM USER

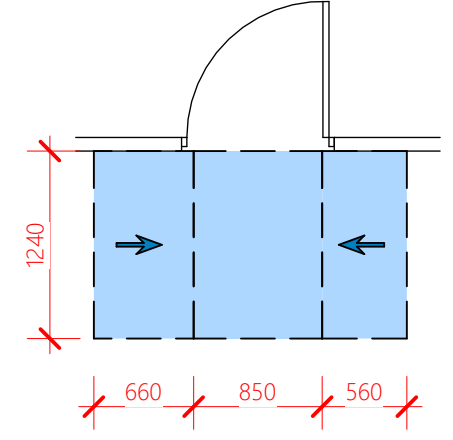


EITHER SIDE APPROACH
DOOR OPENS AWAY FROM USER

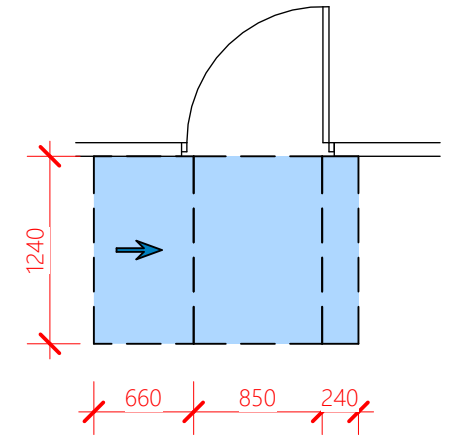


LATCH APPROACH
DOOR OPENS AWAY FROM USER

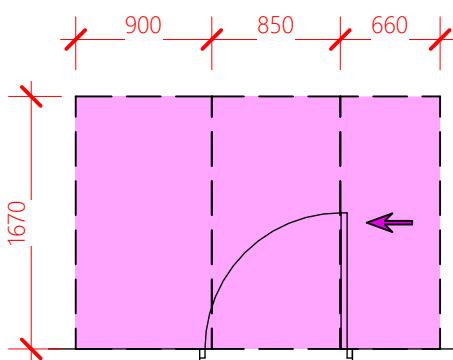


HINGE-SIDE APPROACH
DOOR OPENS TOWARDS USER

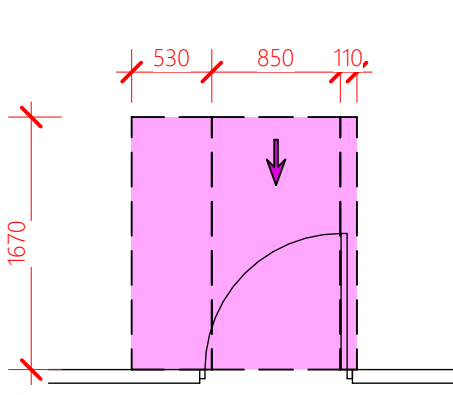


FRONT APPROACH
DOOR OPENS TOWARDS USER

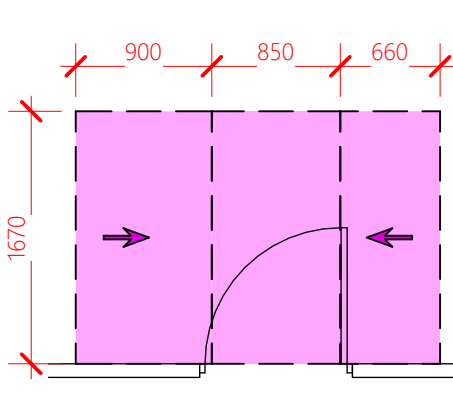

EITHER-SIDE APPROACH
DOOR OPENS TOWARDS USER

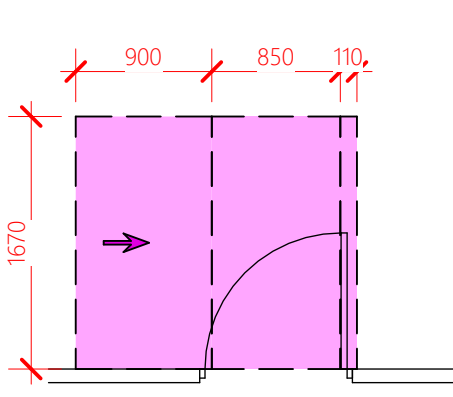


LATCH-SIDE APPROACH
DOOR OPENS TOWARDS USER

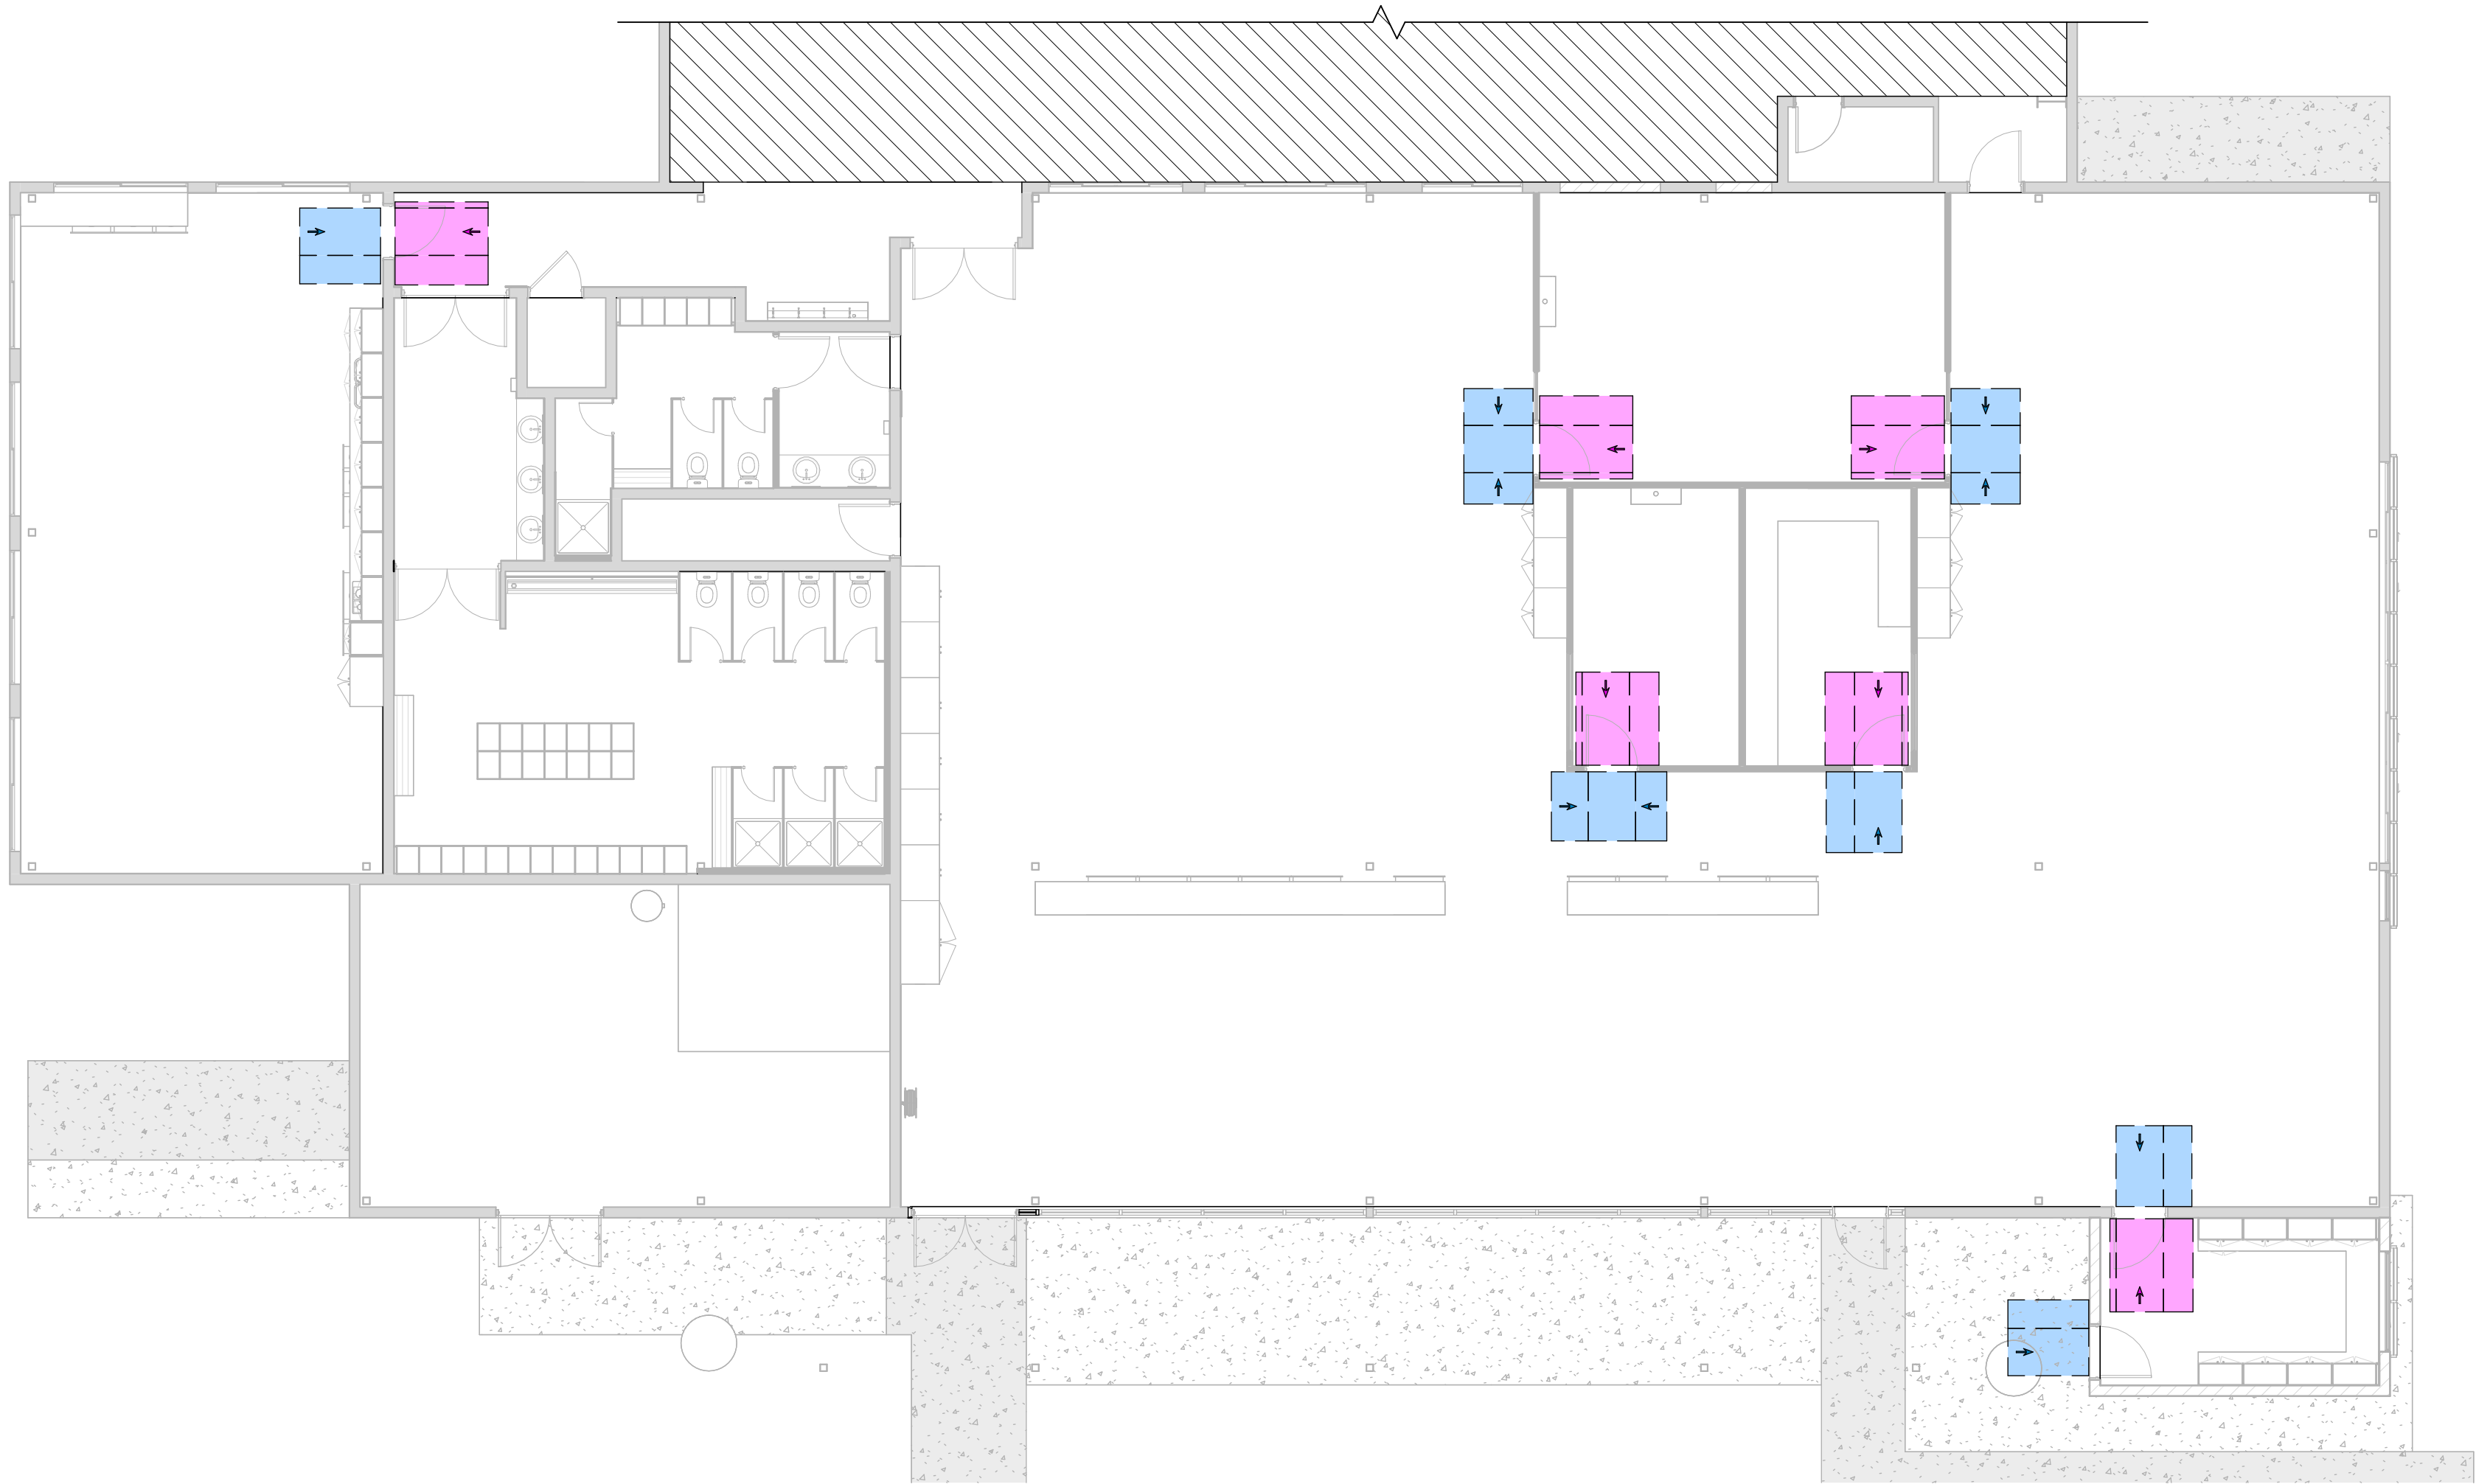

AS1428.1 - Clearance Plan

1 : 100

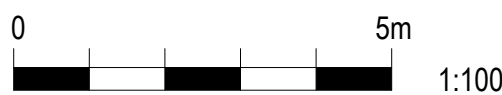

REVISIONS		
Rev	Description	Date
T1	TENDER ISSUE	12.03.2026

DO NOT SCALE THIS DRAWINGS



TENDER ISSUE

Client



Project Details

WAREHOUSE REFURB

Address

STANWELL POWER STATION


Drawing Title

AS1428.1 - CLEARANCE




0483 988 655 
info@designelements.com.au 
QBCC No: 1247120 BDAQ No: 0001677

Scale: As indicated Rev: 
Date: MARCH 2026 **T1**
Drawn: Author
Project No: Drawing No:
25_003 A2-304

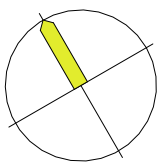


REVISIONS		
Rev	Description	Date
T1	TENDER ISSUE	12.03.2026

DO NOT SCALE THIS DRAWINGS

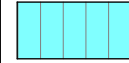FLOOR COVERING PLAN	
	SHEET VINYL - TYPE 1 100mm FEATHER EDGE SKIRTING - BLACK
	SHEET VINYL - TYPE 2 100mm COVED UP SKIRTING
	SHEET VINYL - TYPE 3 100mm FEATHER EDGE SKIRTING - BLACK



Floor Covering Plan

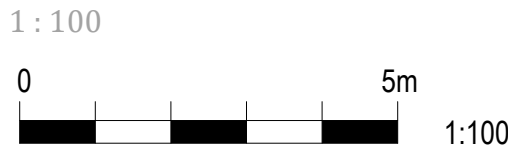

TENDER ISSUE

Client



Project Details

WAREHOUSE REFURB

Address

STANWELL POWER STATION

Drawing Title


FLOOR COVERING PLAN



0483 988 655 **M**
info@designelements.com.au **E**
QBCC No: 1247120 BDAQ No: 0001677


Scale:	1 : 100	Rev:	
Date:	MARCH 2026		T1
Drawn:	Author		
Project No:	25_003	Drawing No:	A2-305

13/03/2026 11:27:15 AM

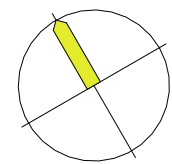

REVISIONS		
Rev	Description	Date
T1	TENDER ISSUE	12.03.2026

DO NOT SCALE THIS DRAWINGS

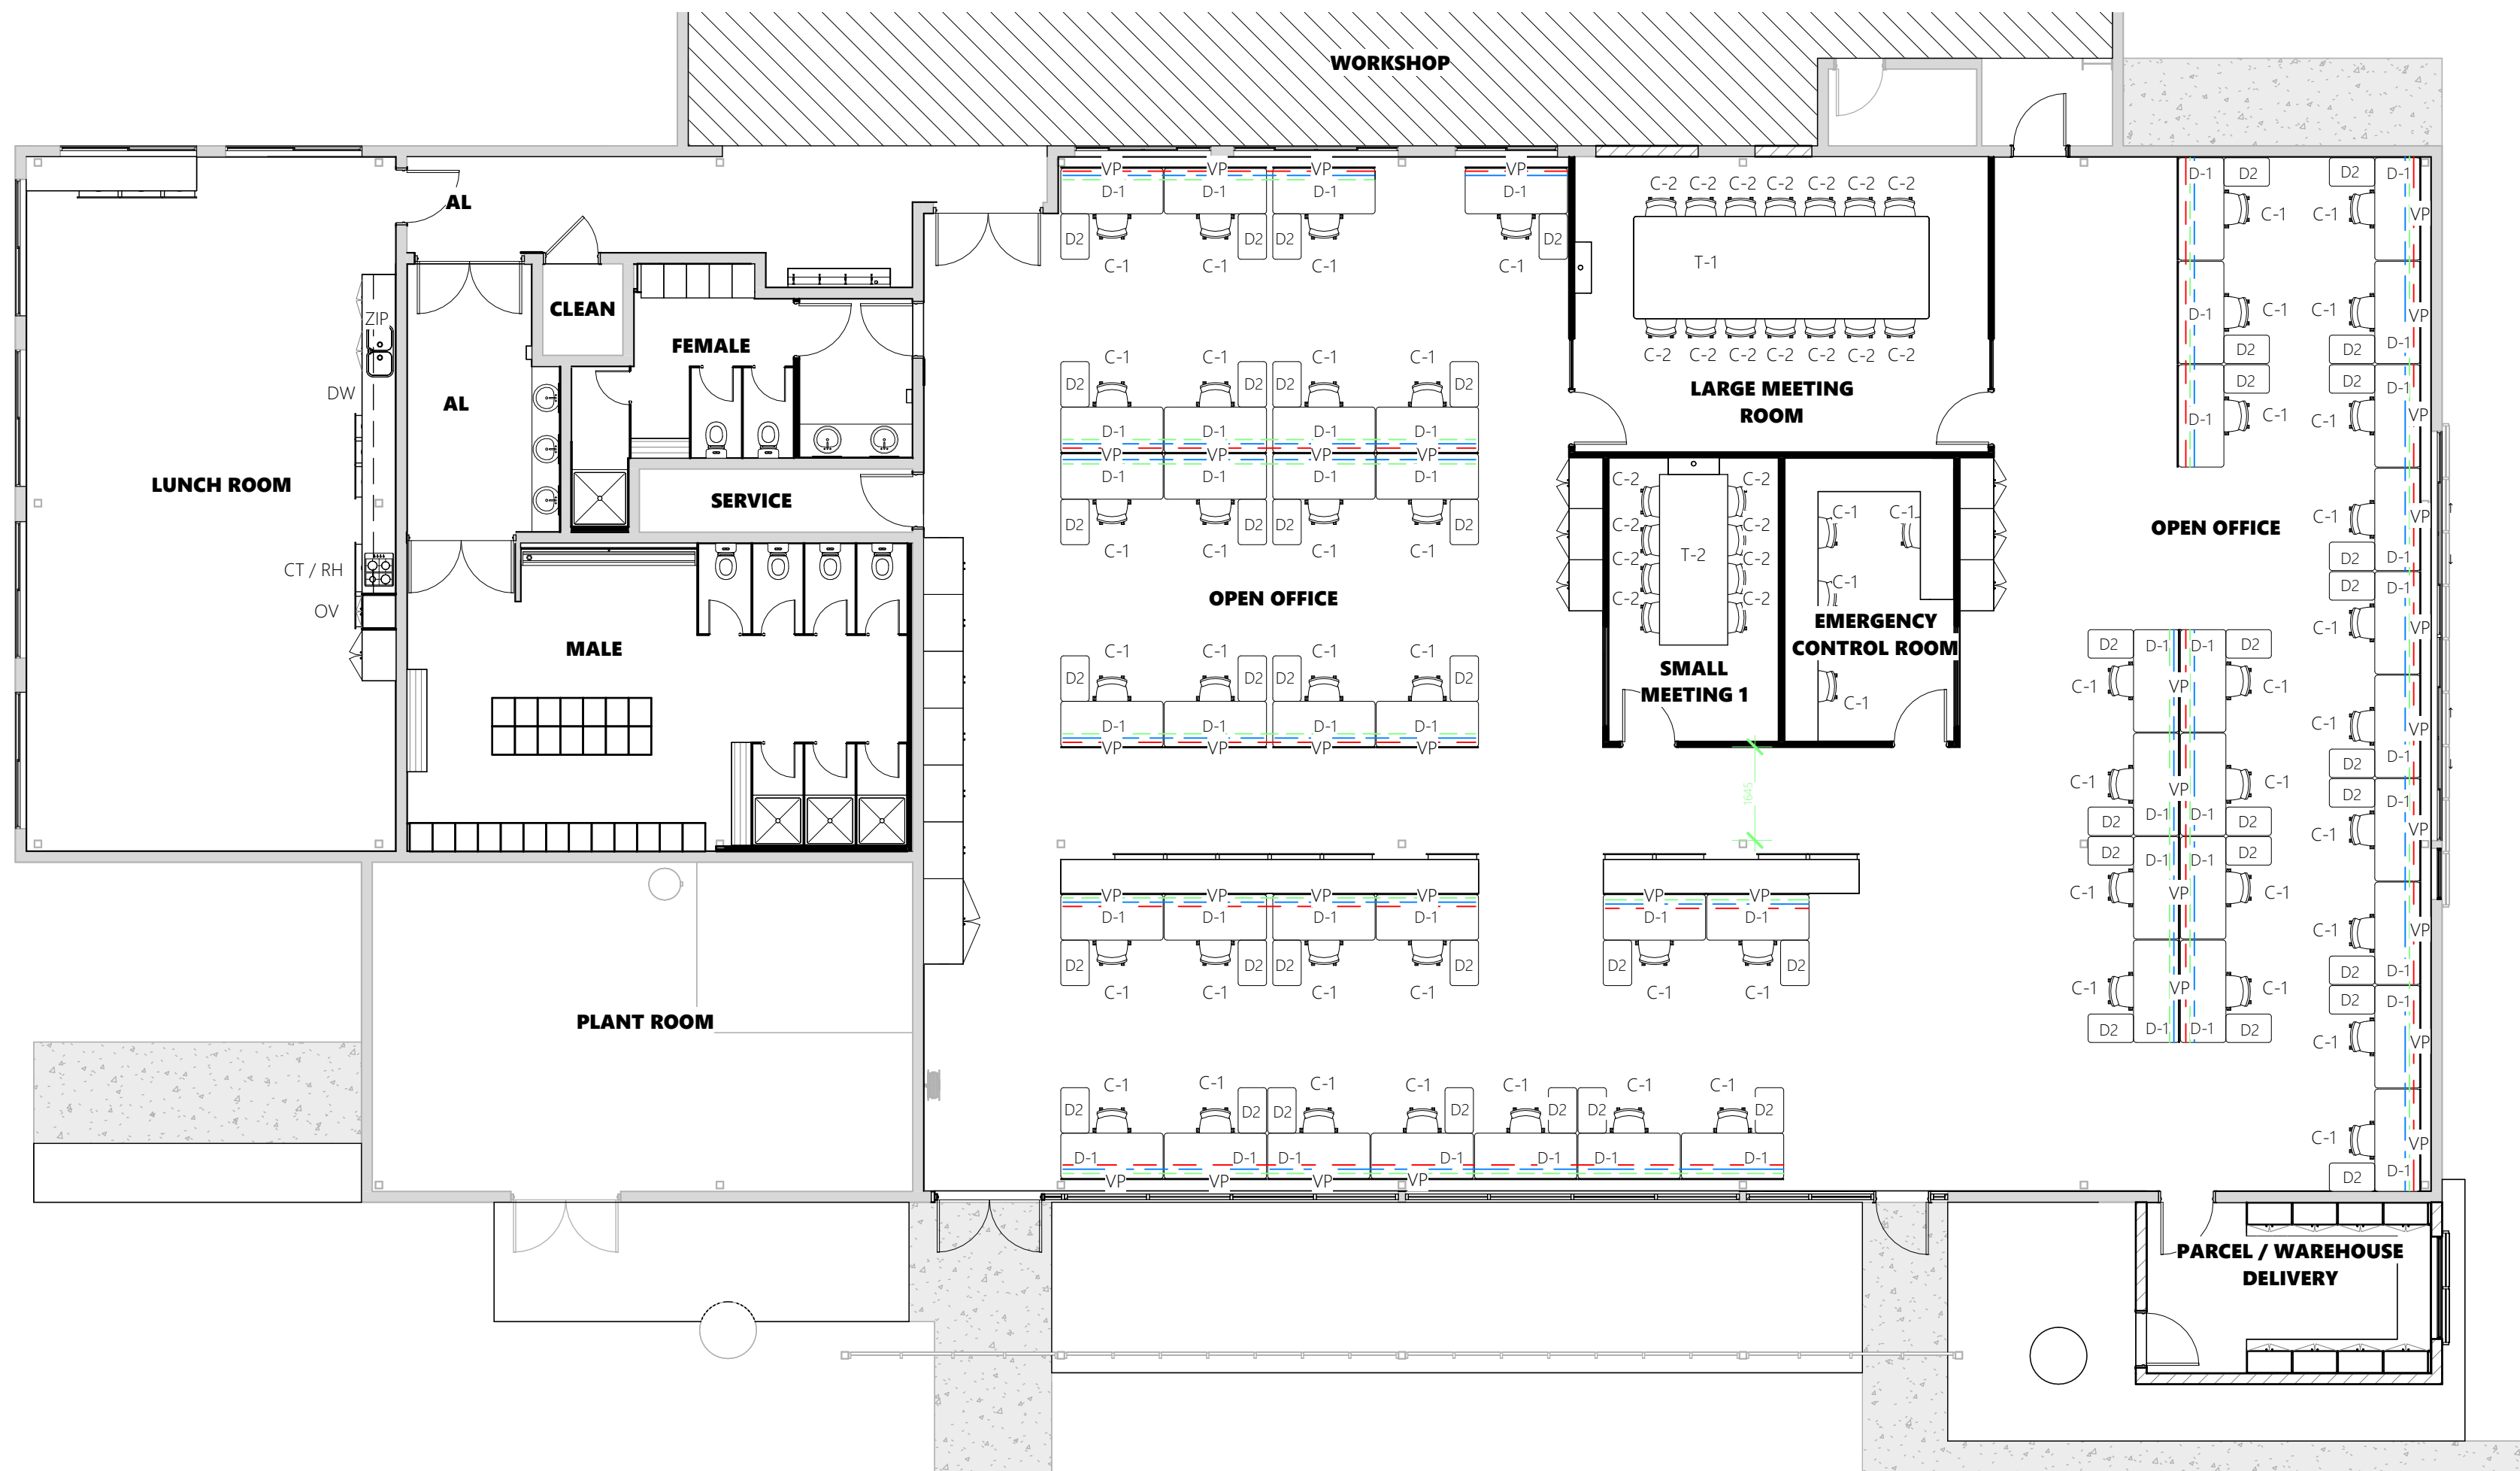


FURNITURE & APPLIANCE SCHEDULE

CODE	TYPE	SIZE	QTY	SUPPLIER
D-1	DESK	1800 x 800	50	SCHIAVELLA CLIMATE RECTANGLE WORK STATION
D-2	DESK	800 x 500	50	SCHIAVELLA CLIMATE RECTANGLE WORK STATION RETURN
C-1	CHAIR (workstation)	-	54	SCHIAVELLA HIGH BACK CHAIR BY OKAMURA, BLACK BODY, BLACK MESH BLACK AND UPHOLSTERED SEAT
C-2	CHAIR (meeting)	-	22	SHIBUSA HIGH BACK BY OKAMURA (BLACK)
T-1	LARGE TABLE	1800 x 5200	1	MEETING TABLE EONA - 25mm LAMINEX CHARCOAL NATURAL FINISH WITH ABS EDGING
T-2	SMALL TABLE	1250 x 3000	1	MEETING TABLE EONA - 25mm LAMINEX CHARCOAL NATURAL FINISH WITH ABS EDGING
	CABLE CATCHER	AS REQUIRED	-	SCHIAVELLA
	CABLE ARTICULATOR	AS REQUIRED	-	SCHIAVELLA
	CABLE CHANNEL	AS REQUIRED	-	SCHIAVELLA
VP	VIDE SUSP. PANEL	1800 (600mm ABOVE DESK)	42	SCHIAVELLA - PROVIDE SUSPENDED BRACKETS TO EACH DESK
OV	OVEN	598 x 596	1	FISHER & PAYKEL 60CM SERIES 7 CONTEMPORARY PYROLYTIC OVEN 9 FUNCTION - BLACK
DW	DISHWASHER	597 x 600	1	FISHER & PAYKEL SERIES 7 CONTEMPORARY DISHWASHER - BLACK STEEL
CT	COOK TOP	600	1	FISHER & PAYKEL 60CM SERIES 7 4 ZONE INDUCTION COOKTOP 2 SMARTZONES - BLACK
RH	RANGE HOOD	600	1	FISHER & PAYKEL 60CM SERIES 7 INTEGRATED INSERT WALL RANGEHOOD EXTERNAL MOTOR - STEEL GLASS
ZIP	ZIP UNIT	-	1	HYDROTAP G5 BCSHA100 5-IN-1 CLASSIC TAP WITH CLASSIC MIXER BLACK

Proposed Furniture Layout

1 : 100

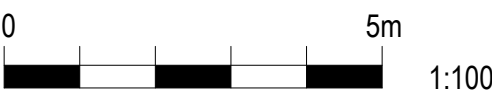

TENDER ISSUE




Project Details
WAREHOUSE REFURB
Address
STANWELL POWER STATION
Drawing Title
FUNITURE LAYOUT

dezinelements
BUILDING DESIGNERS

0483 988 655 **M**
info@dezinelements.com.au **E**


QBCC No: 1247120 BDAQ No: 0001677

Scale: 1 : 100 Rev:
Date: MARCH 2026 **T1**
Drawn: Author
Project No: Drawing No:
25_003 A2-306

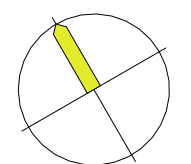


REVISIONS		
Rev	Description	Date
T1	TENDER ISSUE	12.03.2026

DO NOT SCALE THIS DRAWINGS

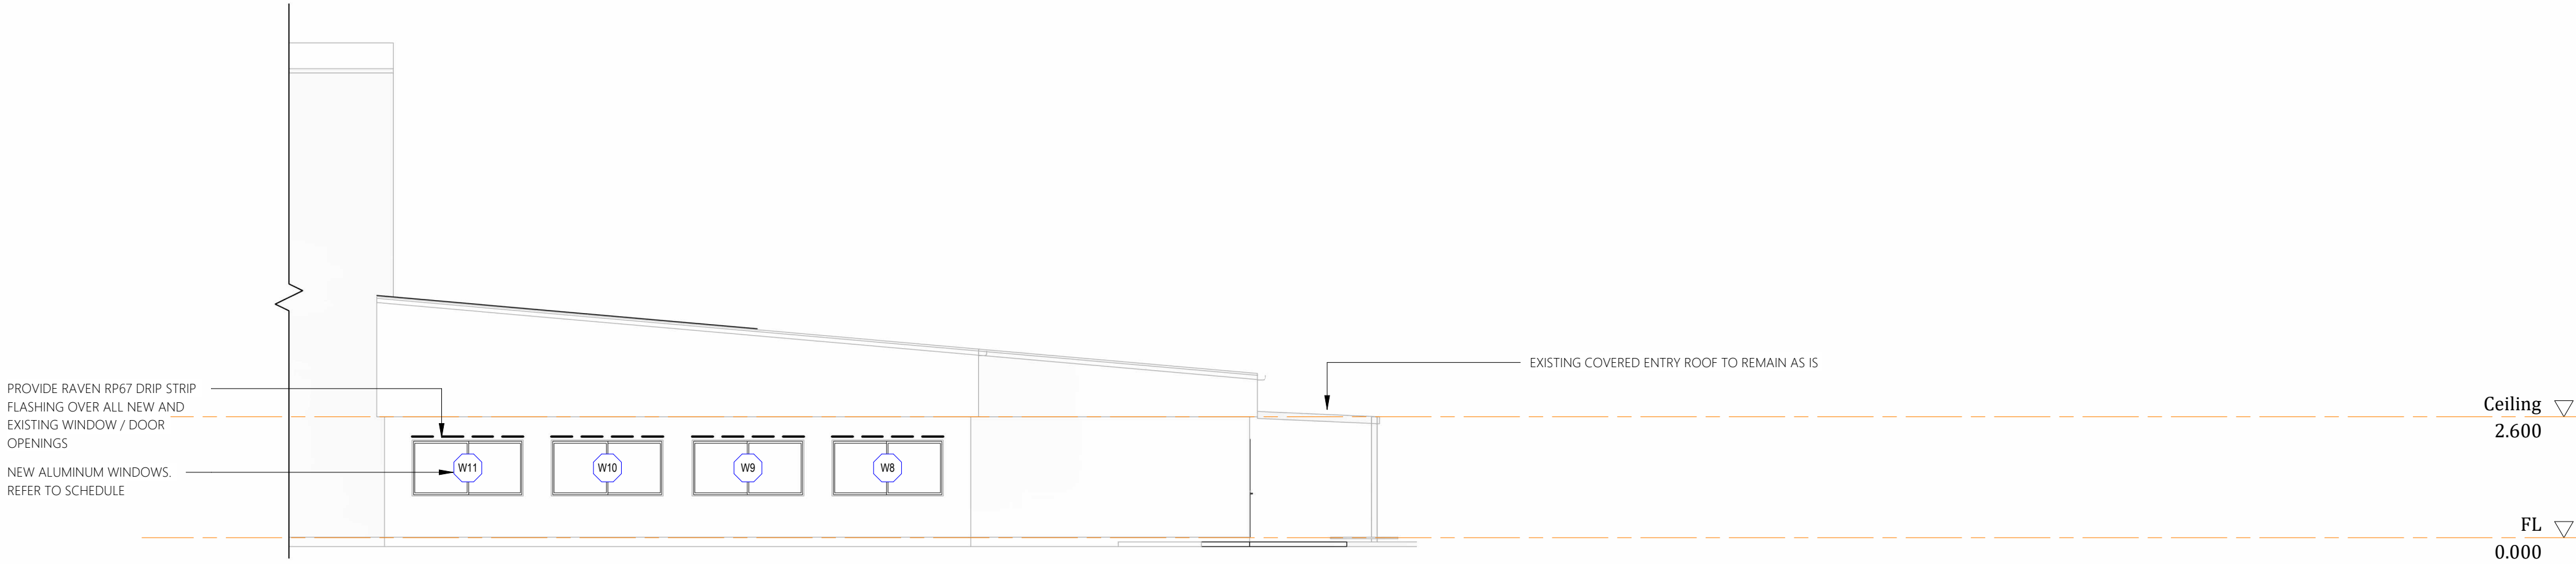


Proposed Elevation 1

1 : 100

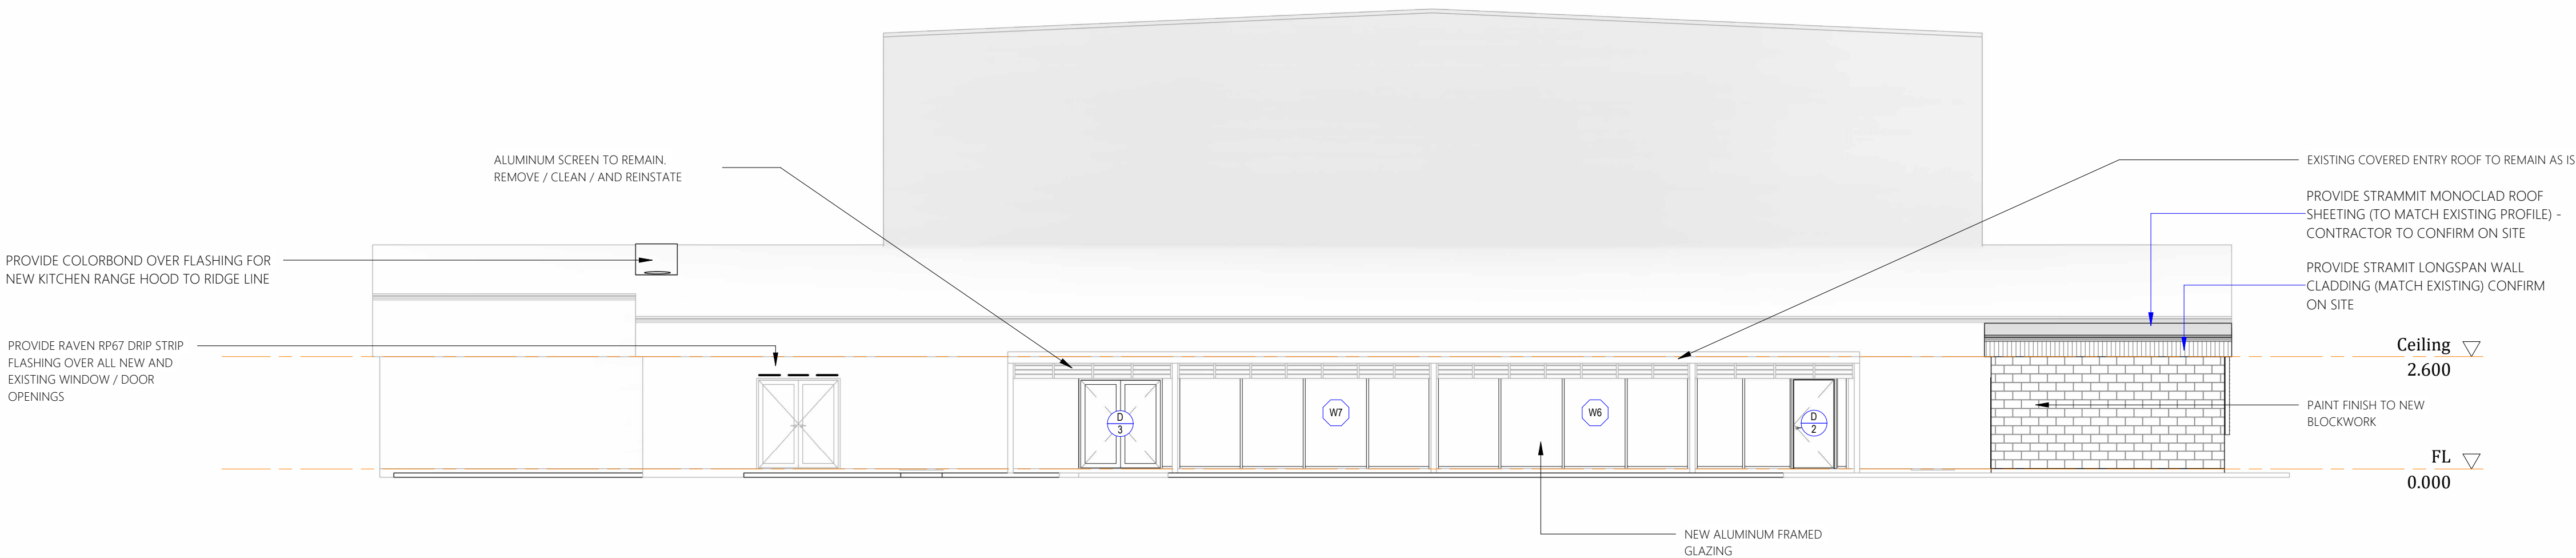

Proposed Elevation 2

1 : 100

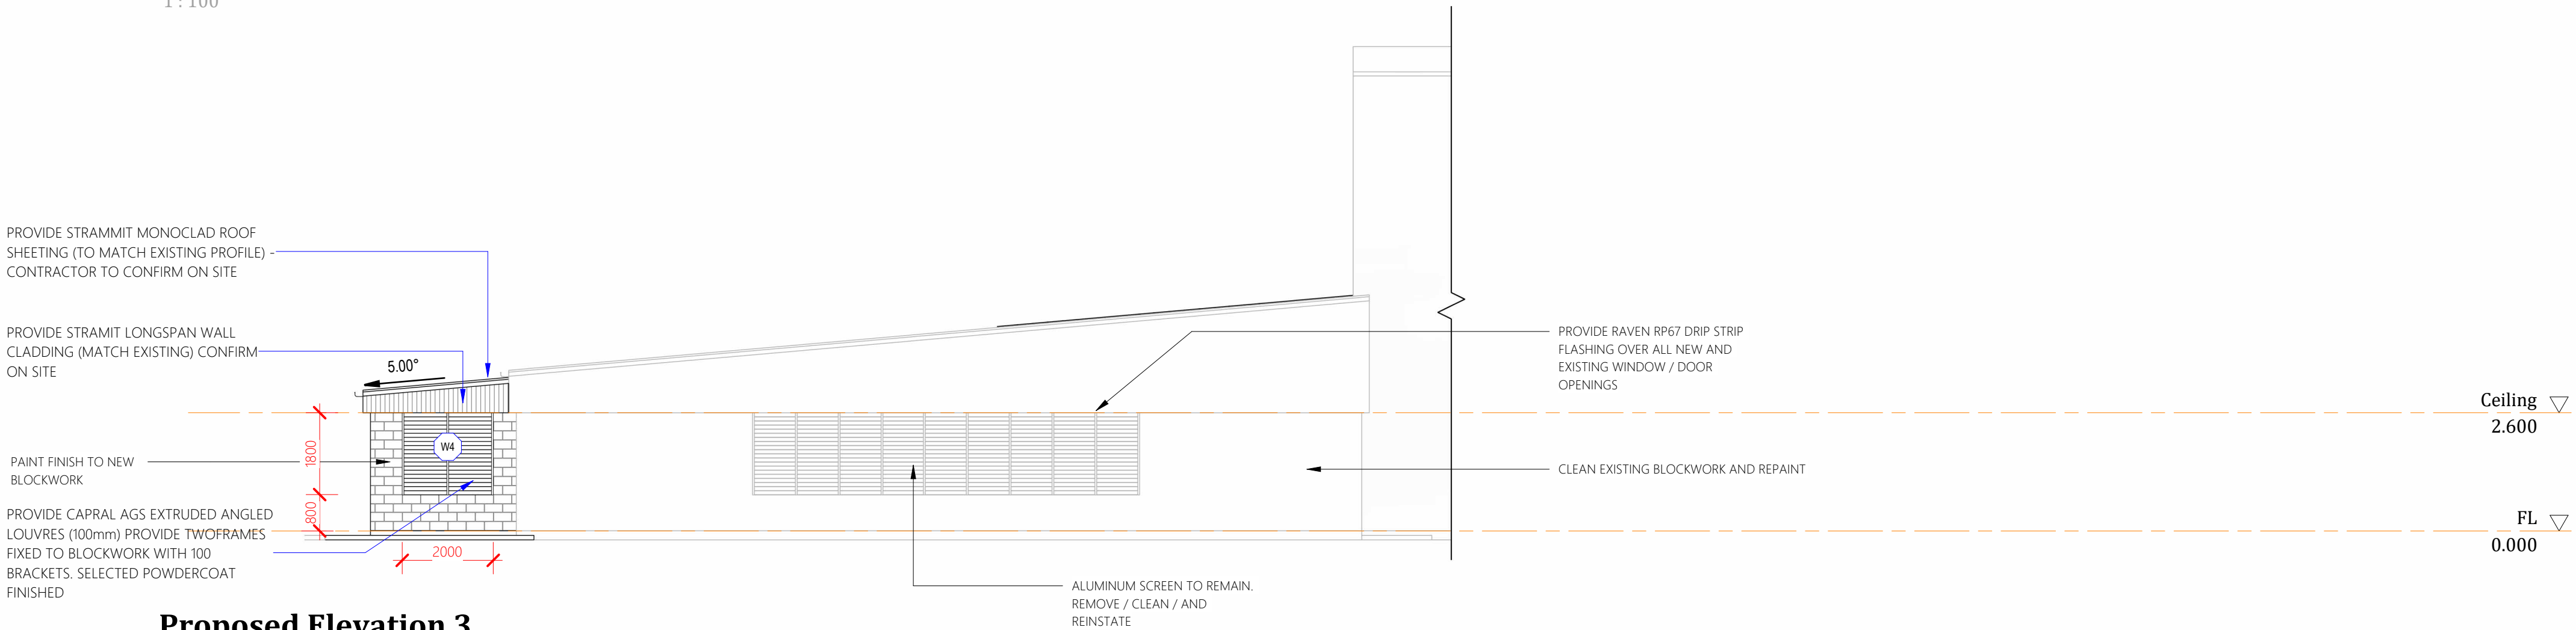

Proposed Elevation 3

1 : 100

TENDER ISSUE



Project Details
WAREHOUSE REFURB
Address
STANWELL POWER STATION
Drawing Title
PROPOSED ELEVATIONS

dezinelements
BUILDING DESIGNERS

0483 988 655 **M**
info@dezi nelements.com.au **E**


QBCC No: 1247120 BDAQ No: 0001677

Scale: 1 : 100	Rev:
Date: MARCH 2026	T1
Drawn: Author	
Project No:	Drawing No:
25_003	A2-400


13/03/2026 11:27:34 AM

REVISIONS		
Rev	Description	Date
T1	TENDER ISSUE	12.03.2026

DO NOT SCALE THIS DRAWINGS

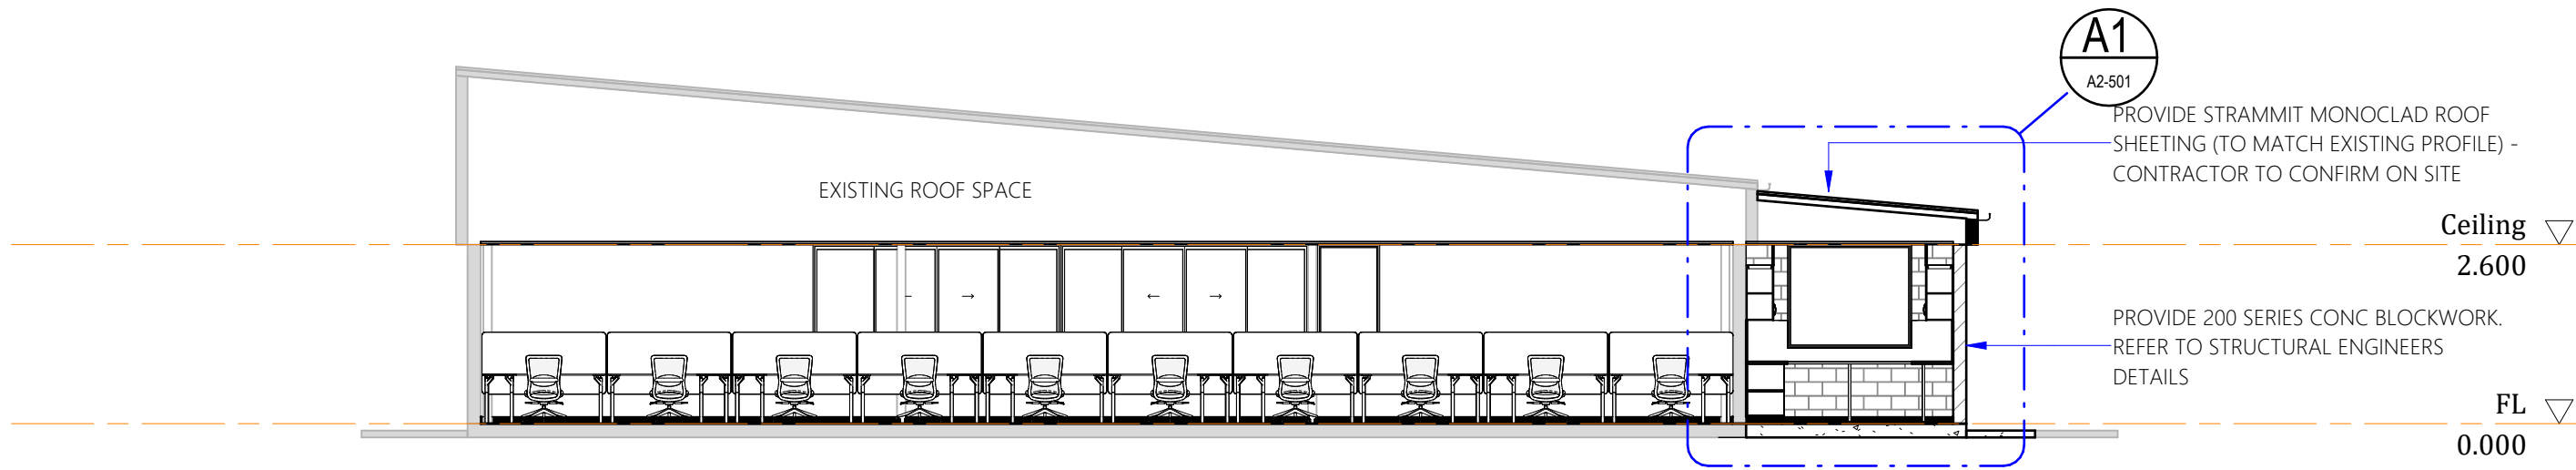

Section A
1 : 100

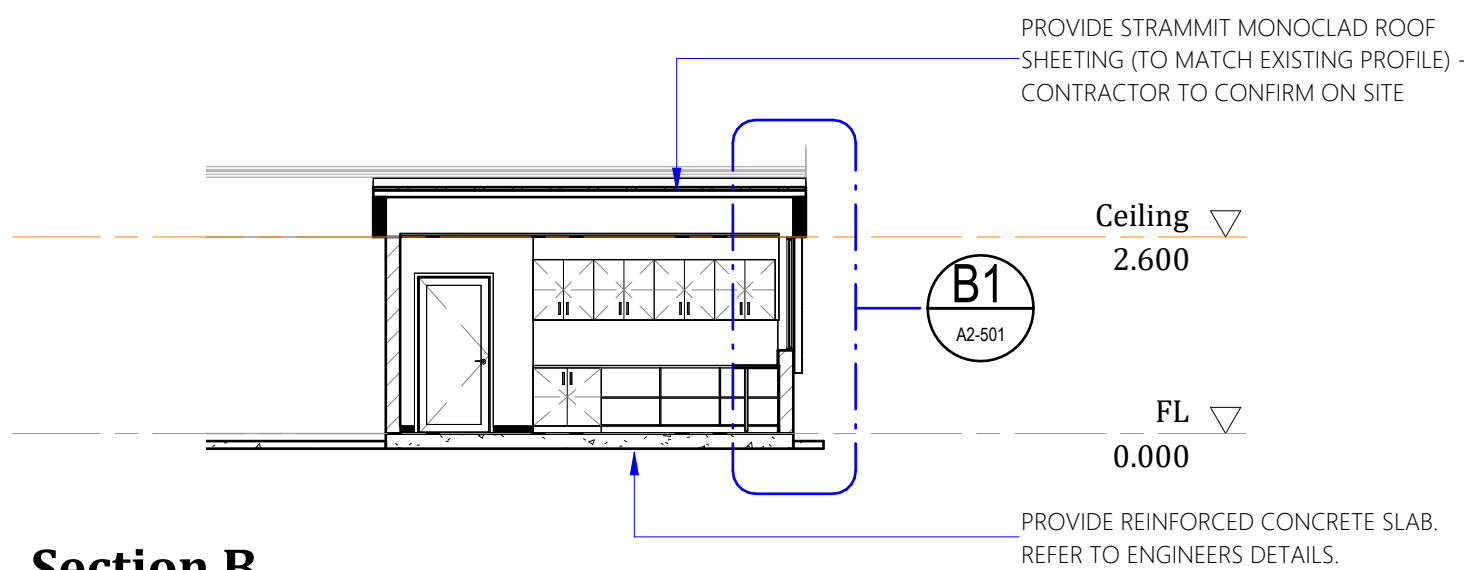

Section B
1 : 100

TENDER ISSUE




Project Details
WAREHOUSE REFURB
Address
STANWELL POWER STATION
Drawing Title
PROPOSED SECTION




0483 988 655 **M**
info@designelements.com.au **E**
QBCC No: 1247120 BDAQ No: 0001677

Scale: 1 : 100	Rev: T1
Date: MARCH 2026	
Drawn: Author	
Project No: 25_003	Drawing No: A2-500

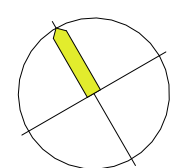


REVISIONS		
Rev	Description	Date
T1	TENDER ISSUE	12.03.2026

DO NOT SCALE THIS DRAWINGS

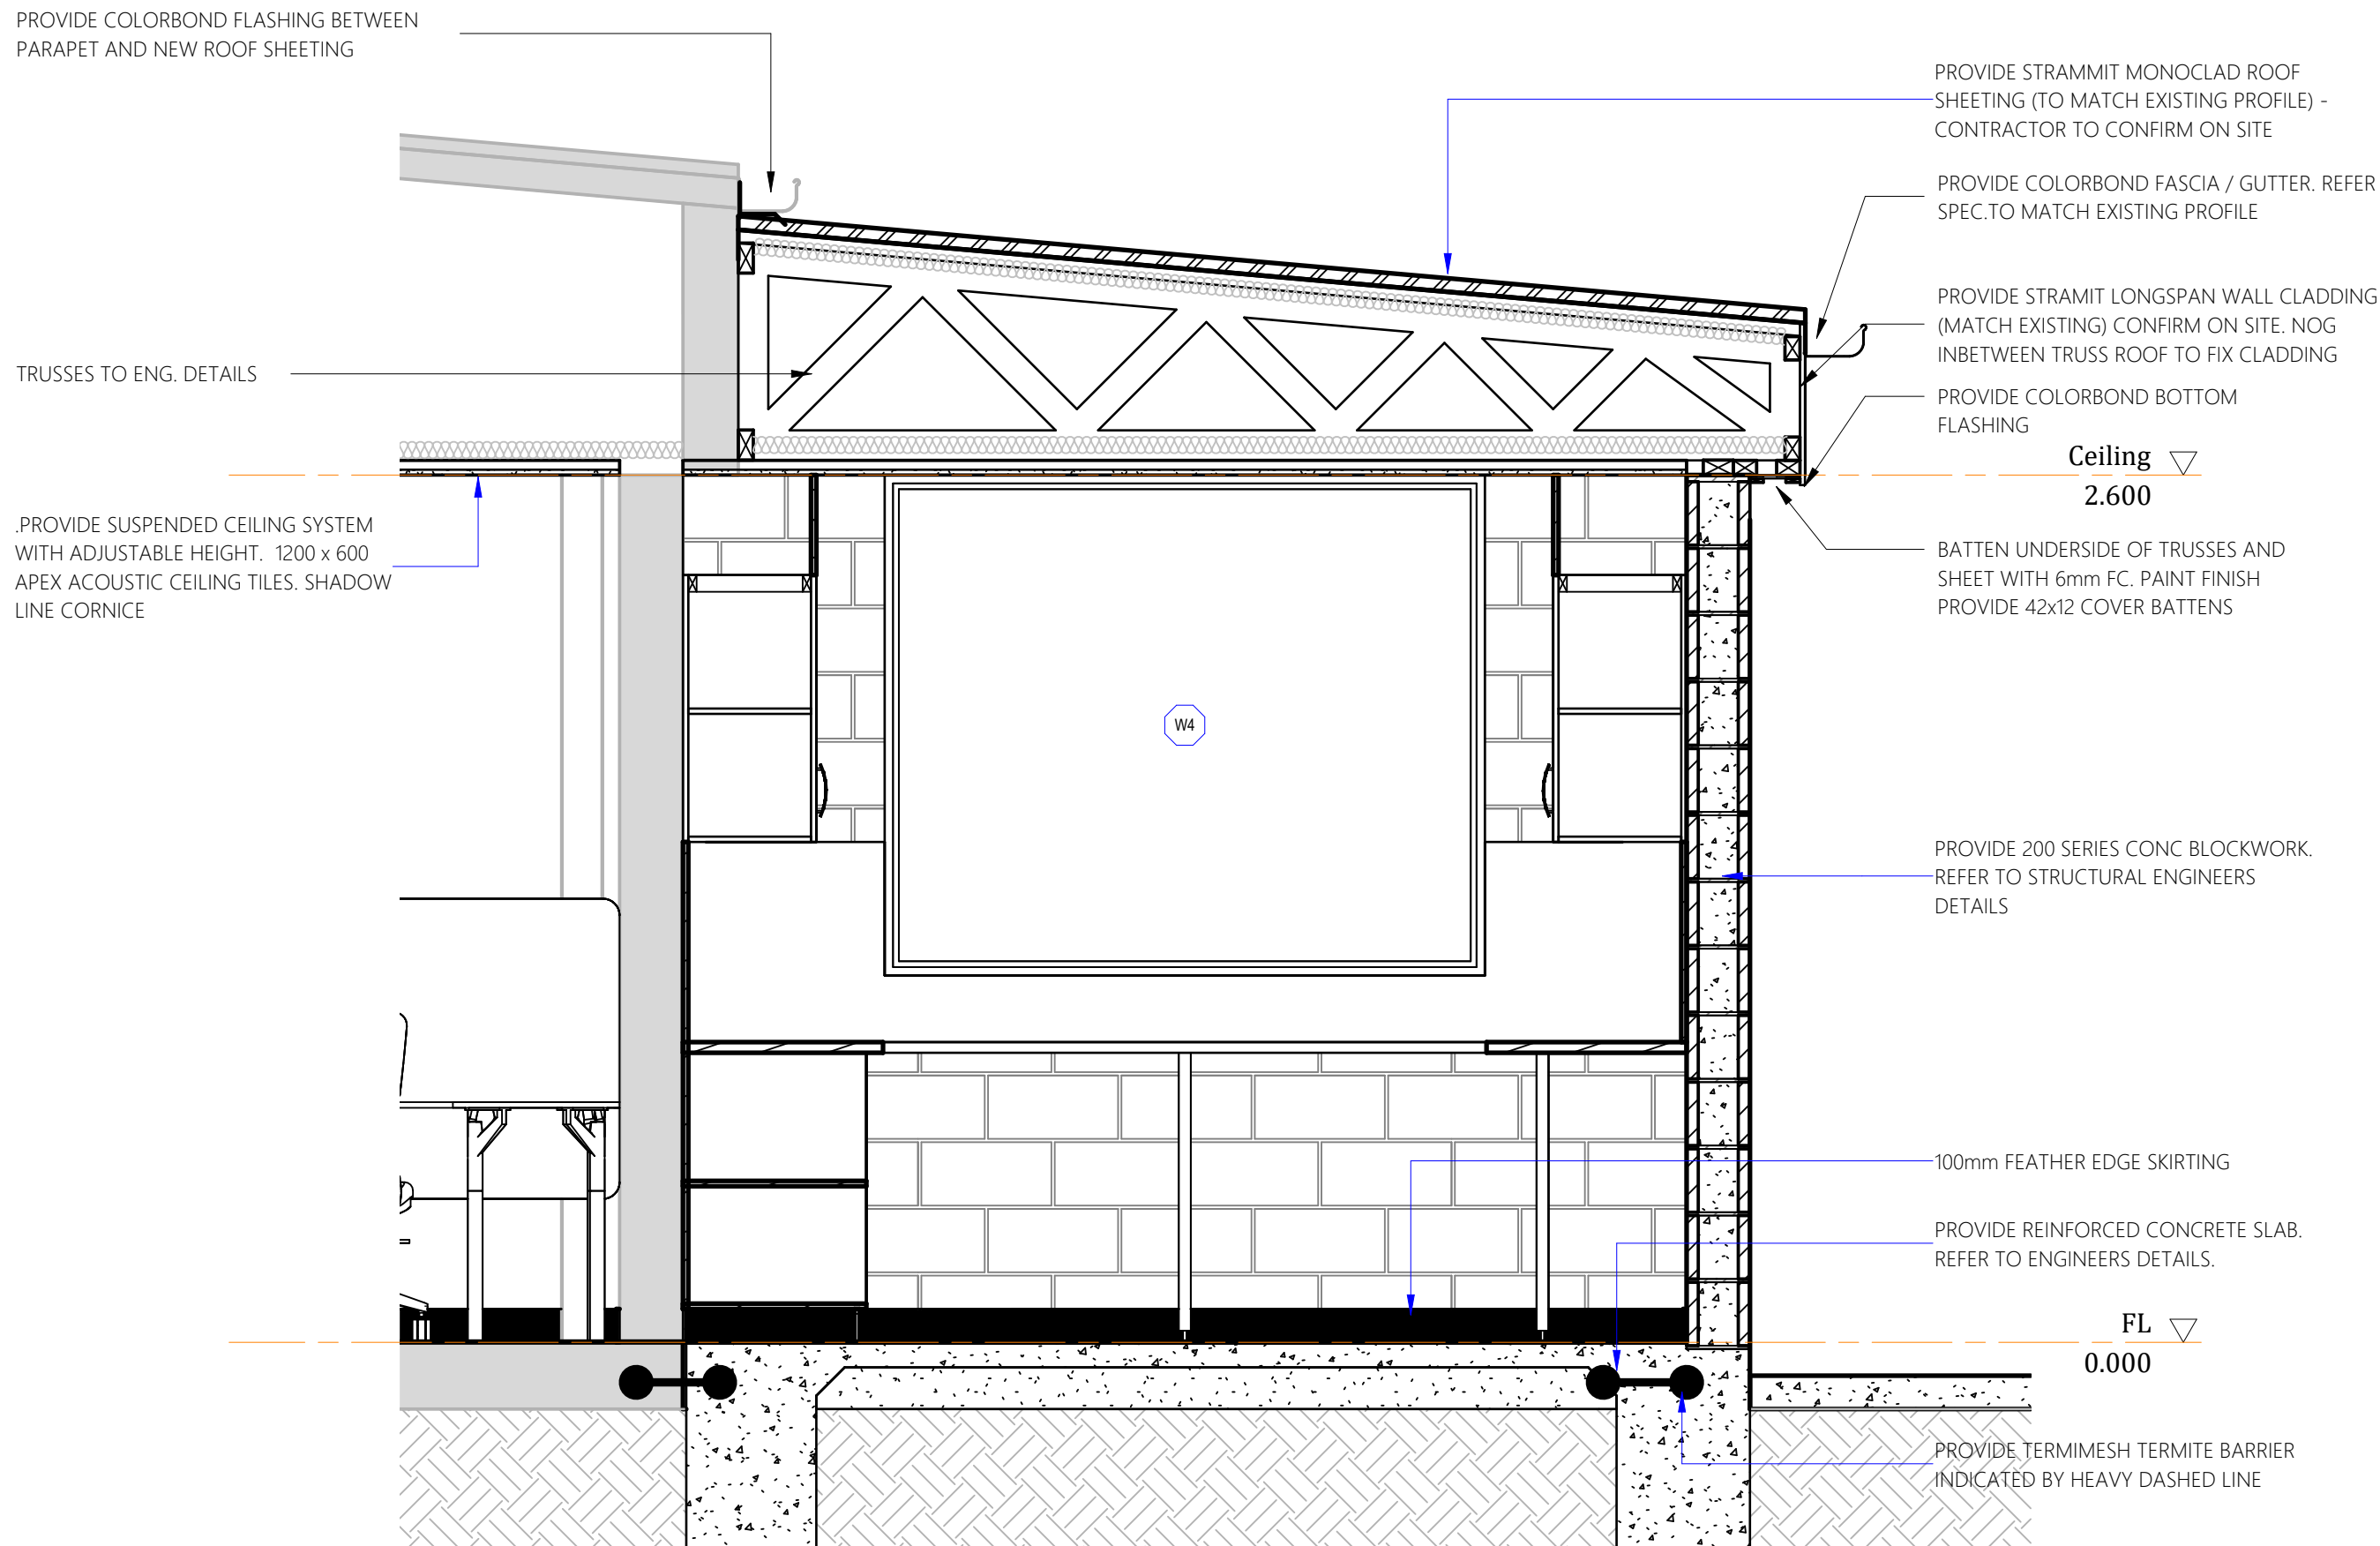

Section A1

1 : 20

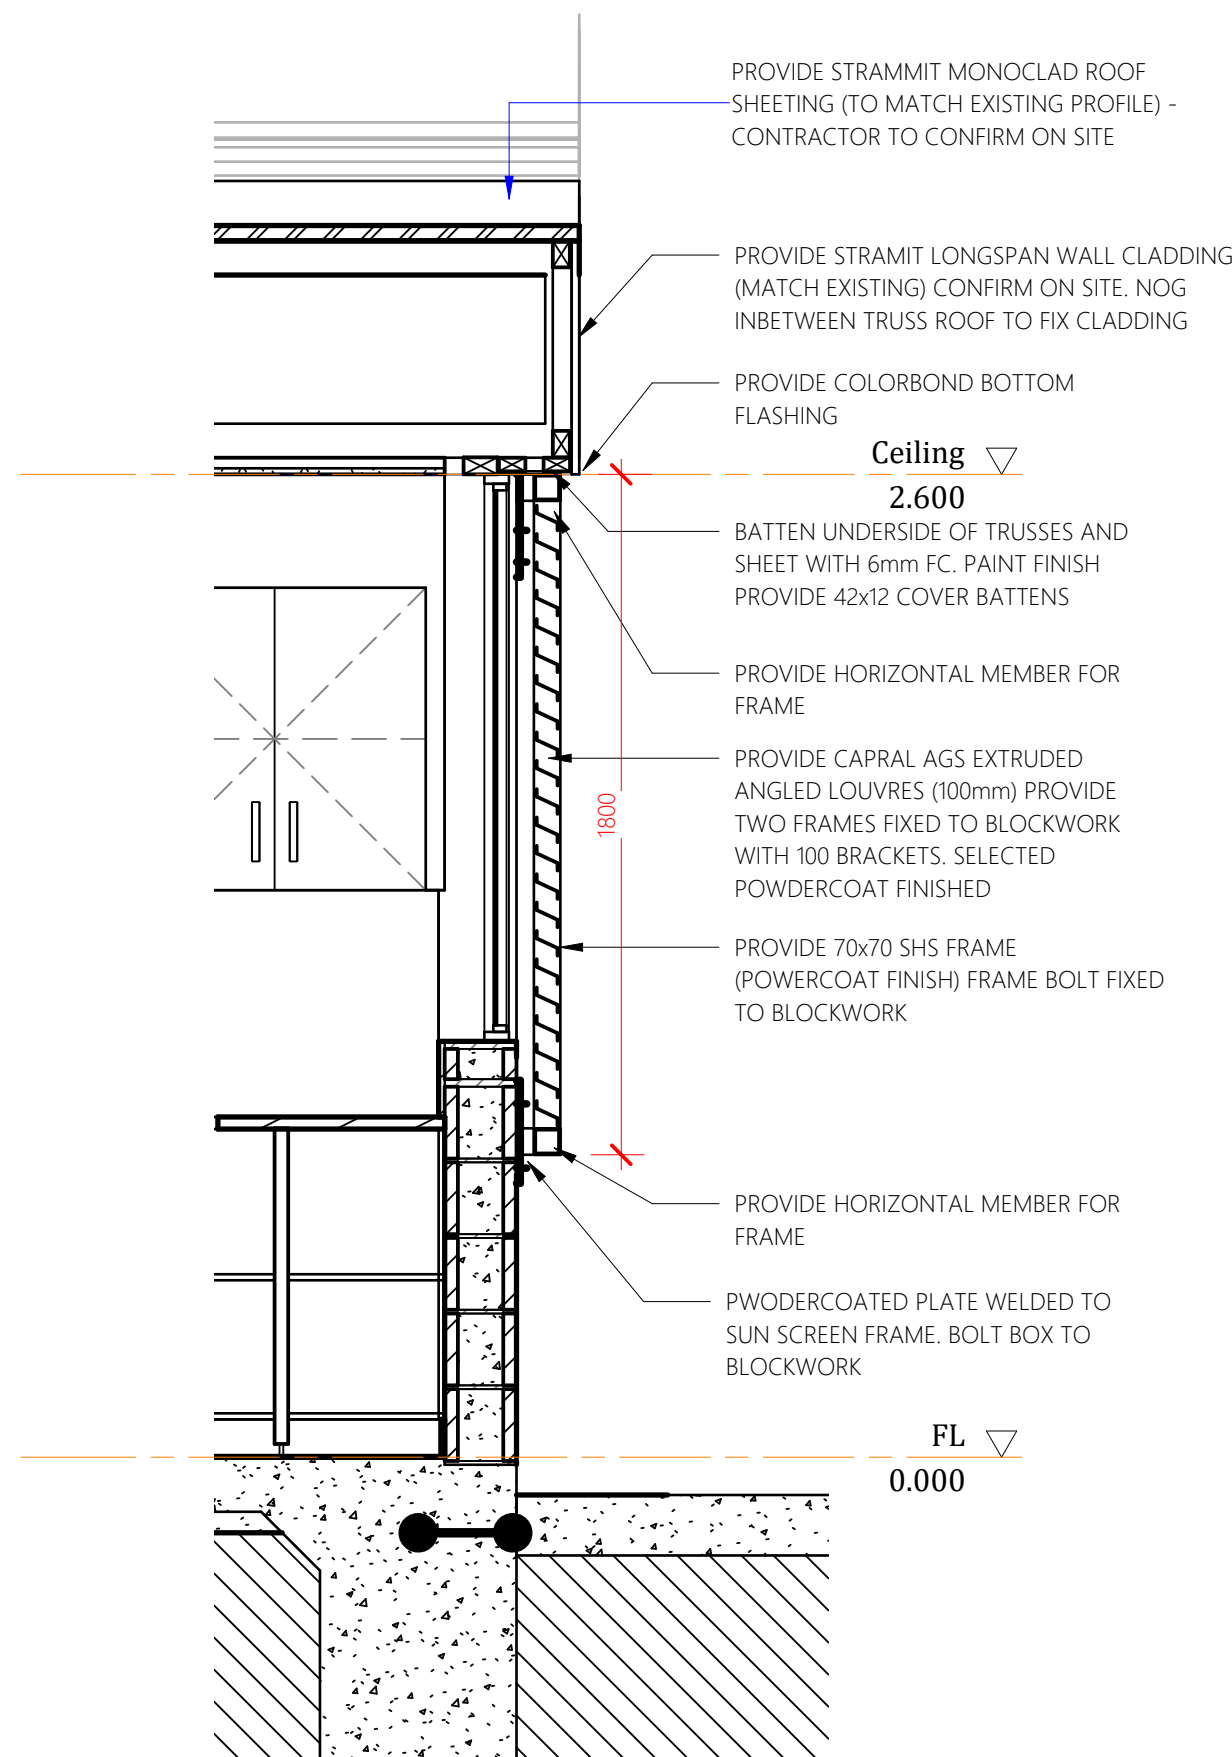

Section B1

1 : 20

TENDER ISSUE





Project Details
WAREHOUSE REFURB
Address
STANWELL POWER STATION
Drawing Title
SECTION DETAILS



0483 988 655 M
info@designelements.com.au E
QBCC No: 1247120 BDAQ No: 0001677


Scale: 1 : 20	Rev:
Date: MARCH 2026	T1
Drawn: Author	
Project No: 25_003	Drawing No: A2-501

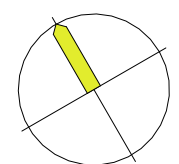

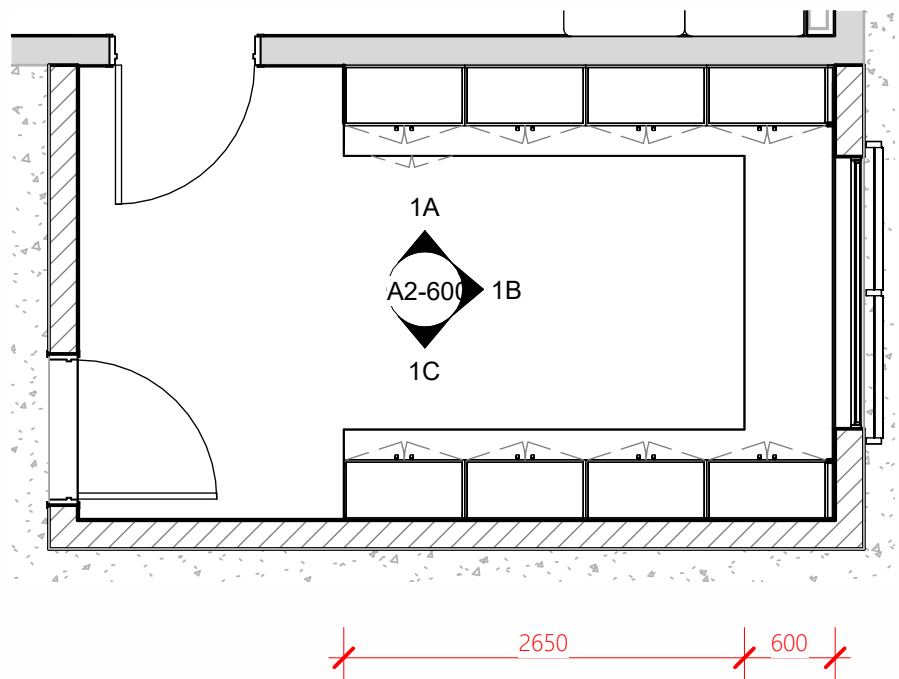


Internal Plan 1

1 : 50

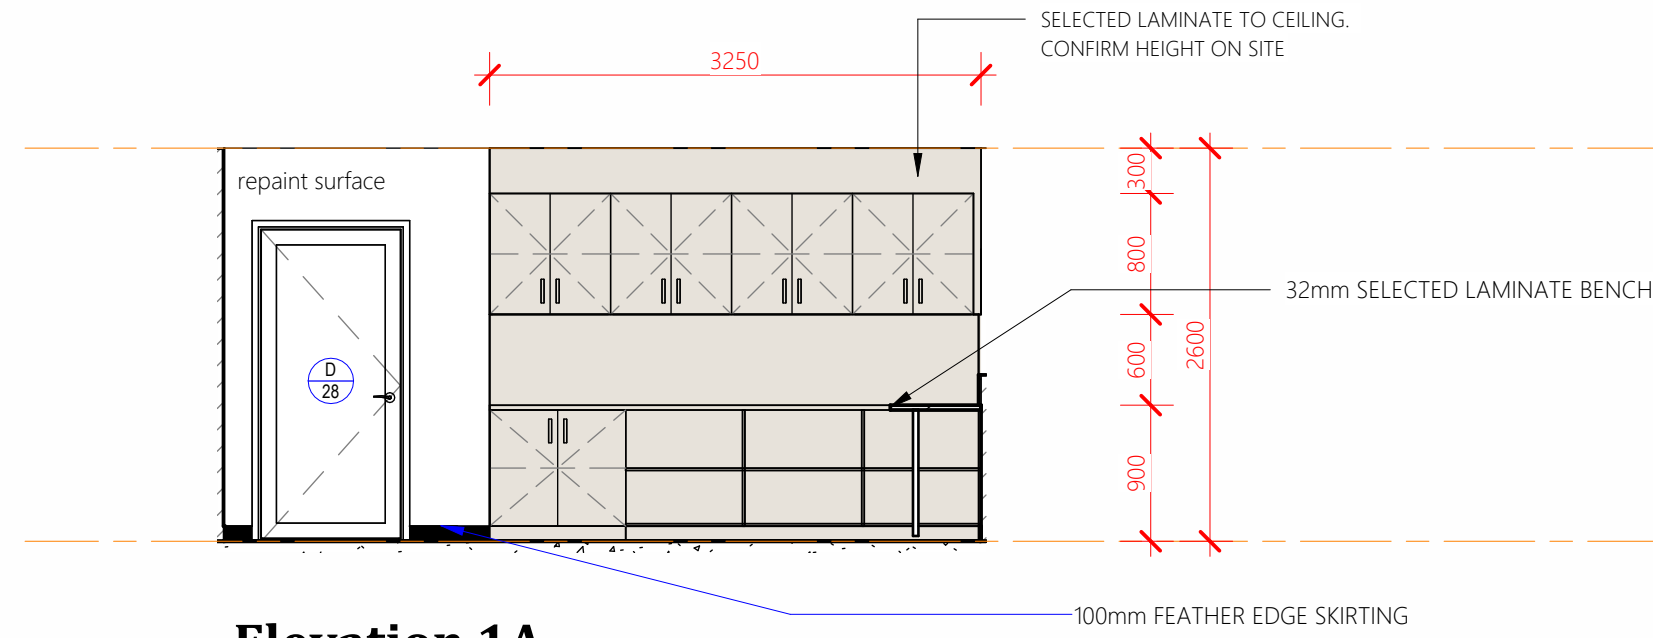


Elevation 1A

1 : 50

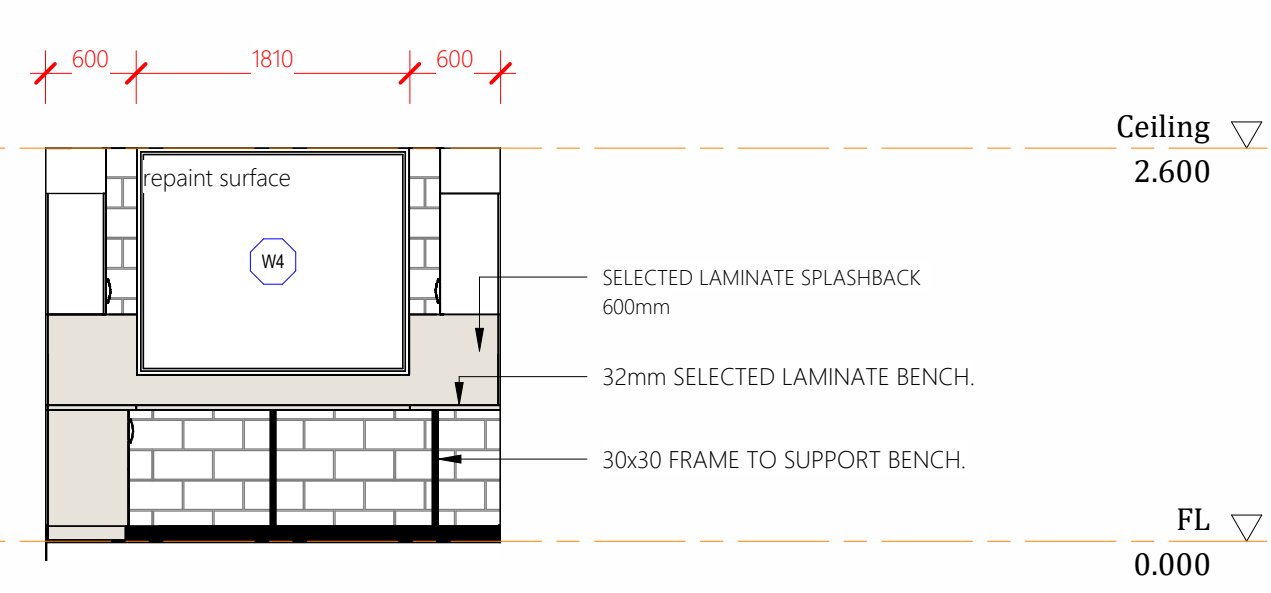

Elevation 1B

1 : 50

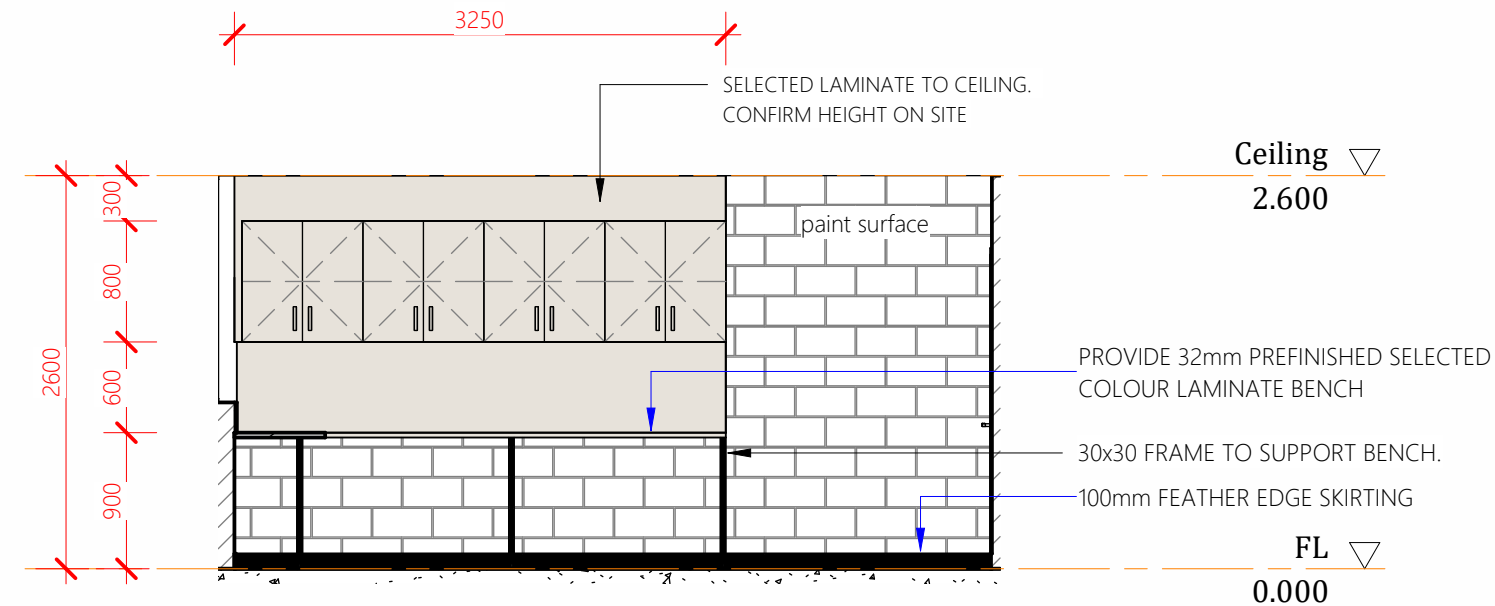

Elevation 1C


1 : 50



REVISIONS

Rev	Description	Date
T1	TENDER ISSUE	12.03.2026

DO NOT SCALE THIS DRAWINGS

 

TENDER ISSUE



Project Details
WAREHOUSE REFURB

Address
STANWELL POWER STATION


Drawing Title
INTERNAL ELEVATIONS 1 - PARCEL ROOM




0483 988 655 **M**
info@designelements.com.au **E**
QBCC No: 1247120 BDAQ No: 0001677

Scale: 1 : 50 Rev:
Date: MARCH 2026 **T1**
Drawn: Author


Project No: Drawing No:
25_003 A2-600

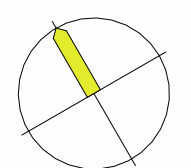

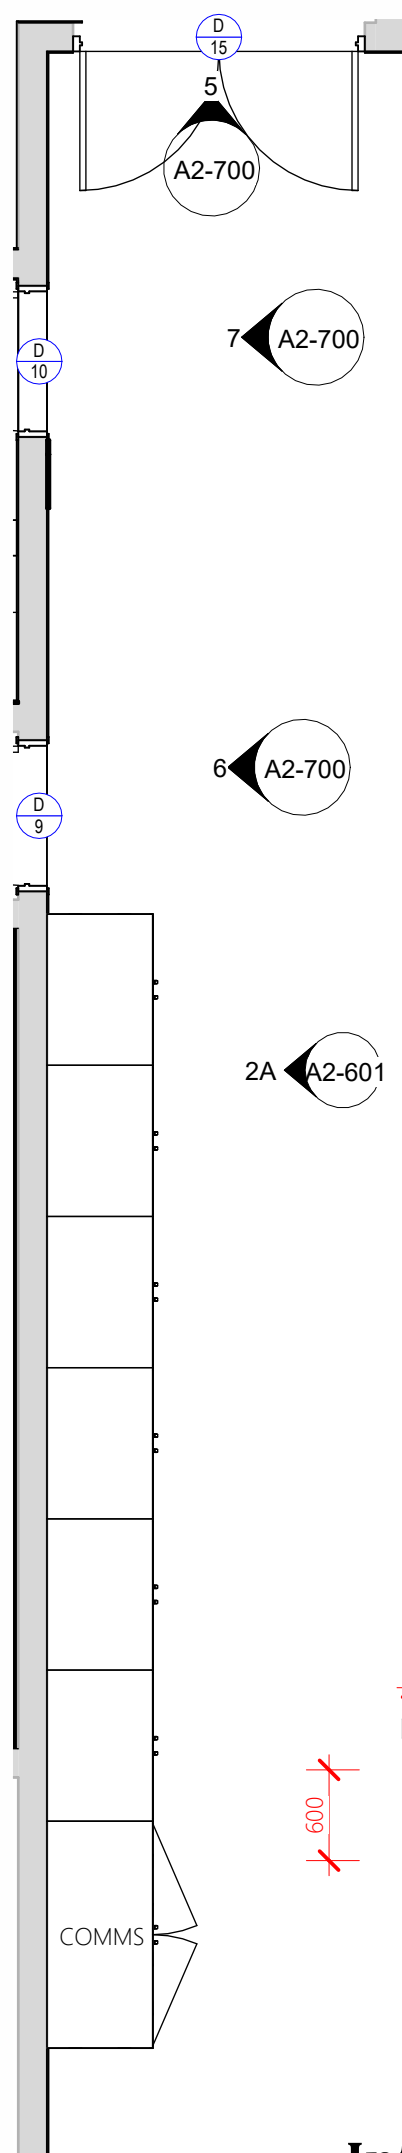


Internal Plan 2

1 : 50

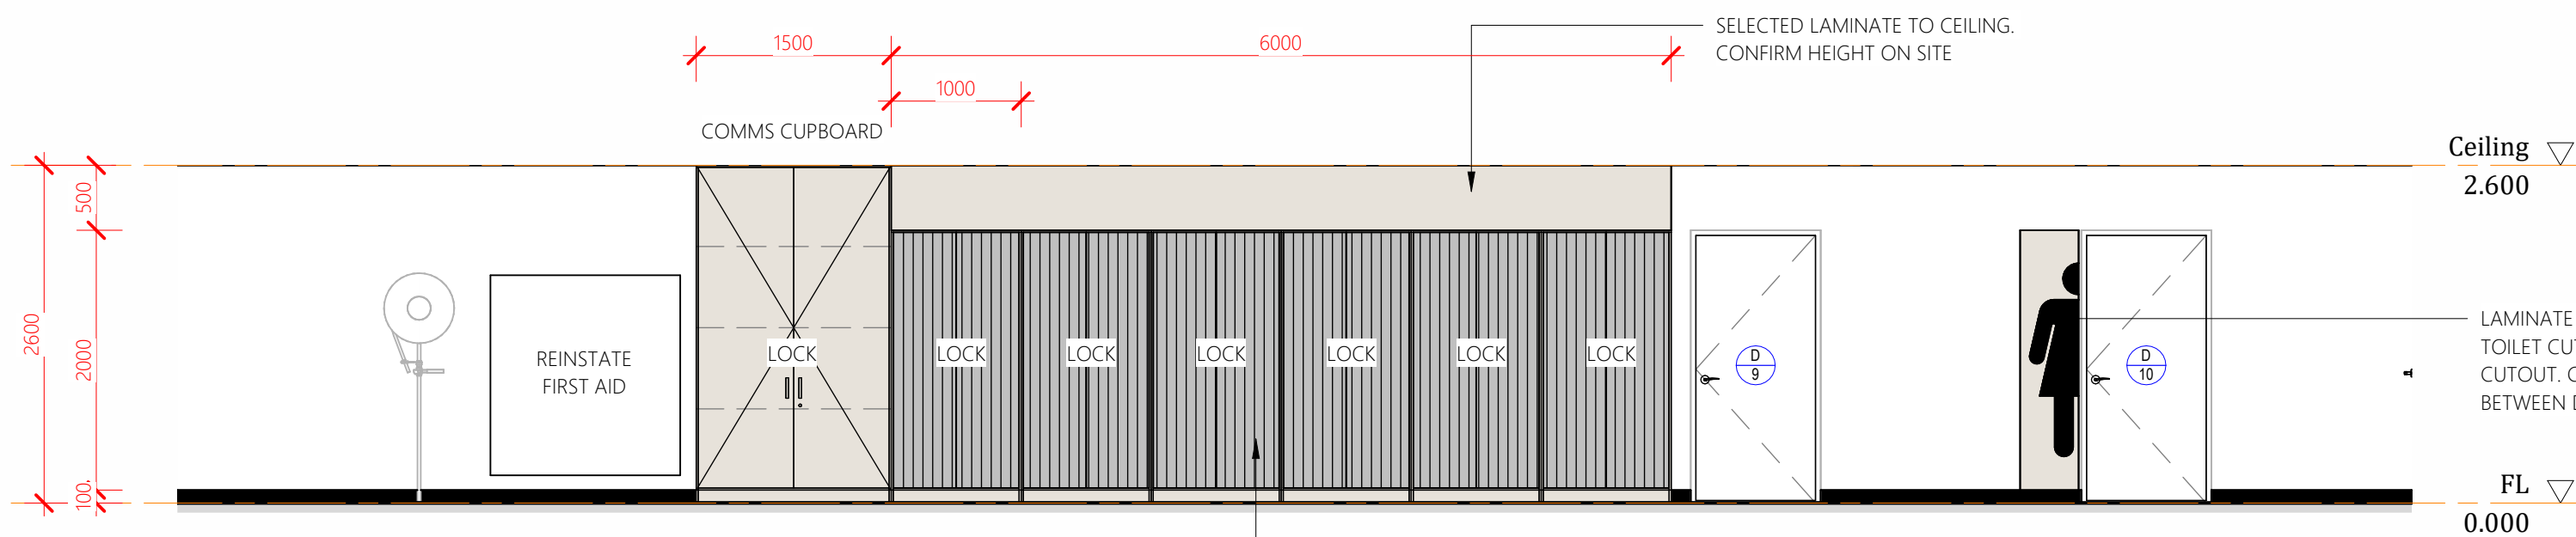


Elevation 2A

1 : 50

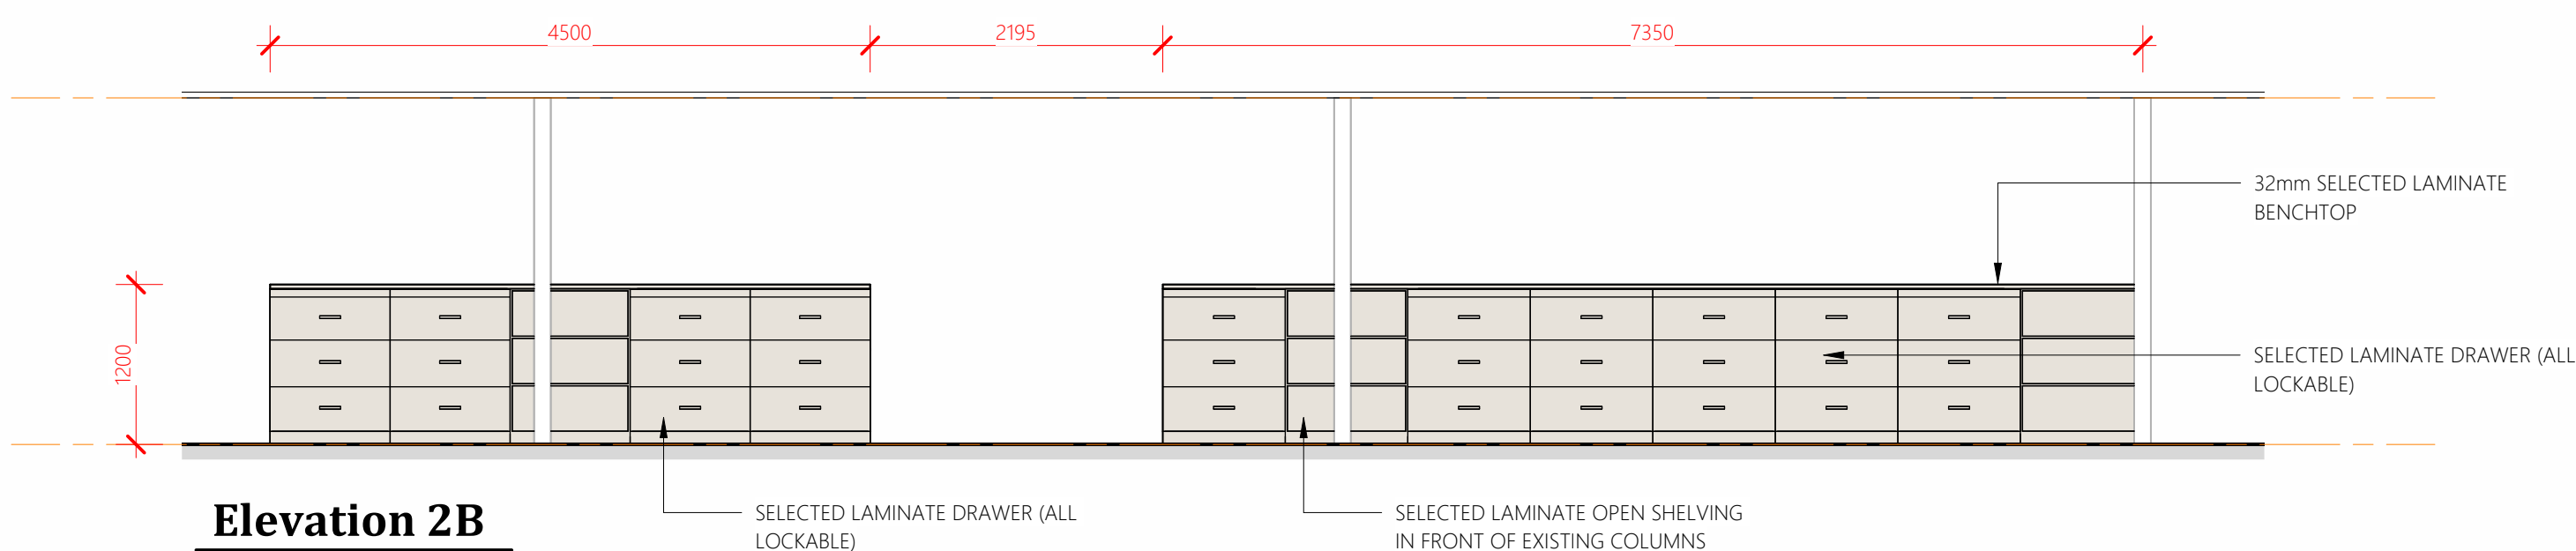

Elevation 2B

1 : 50

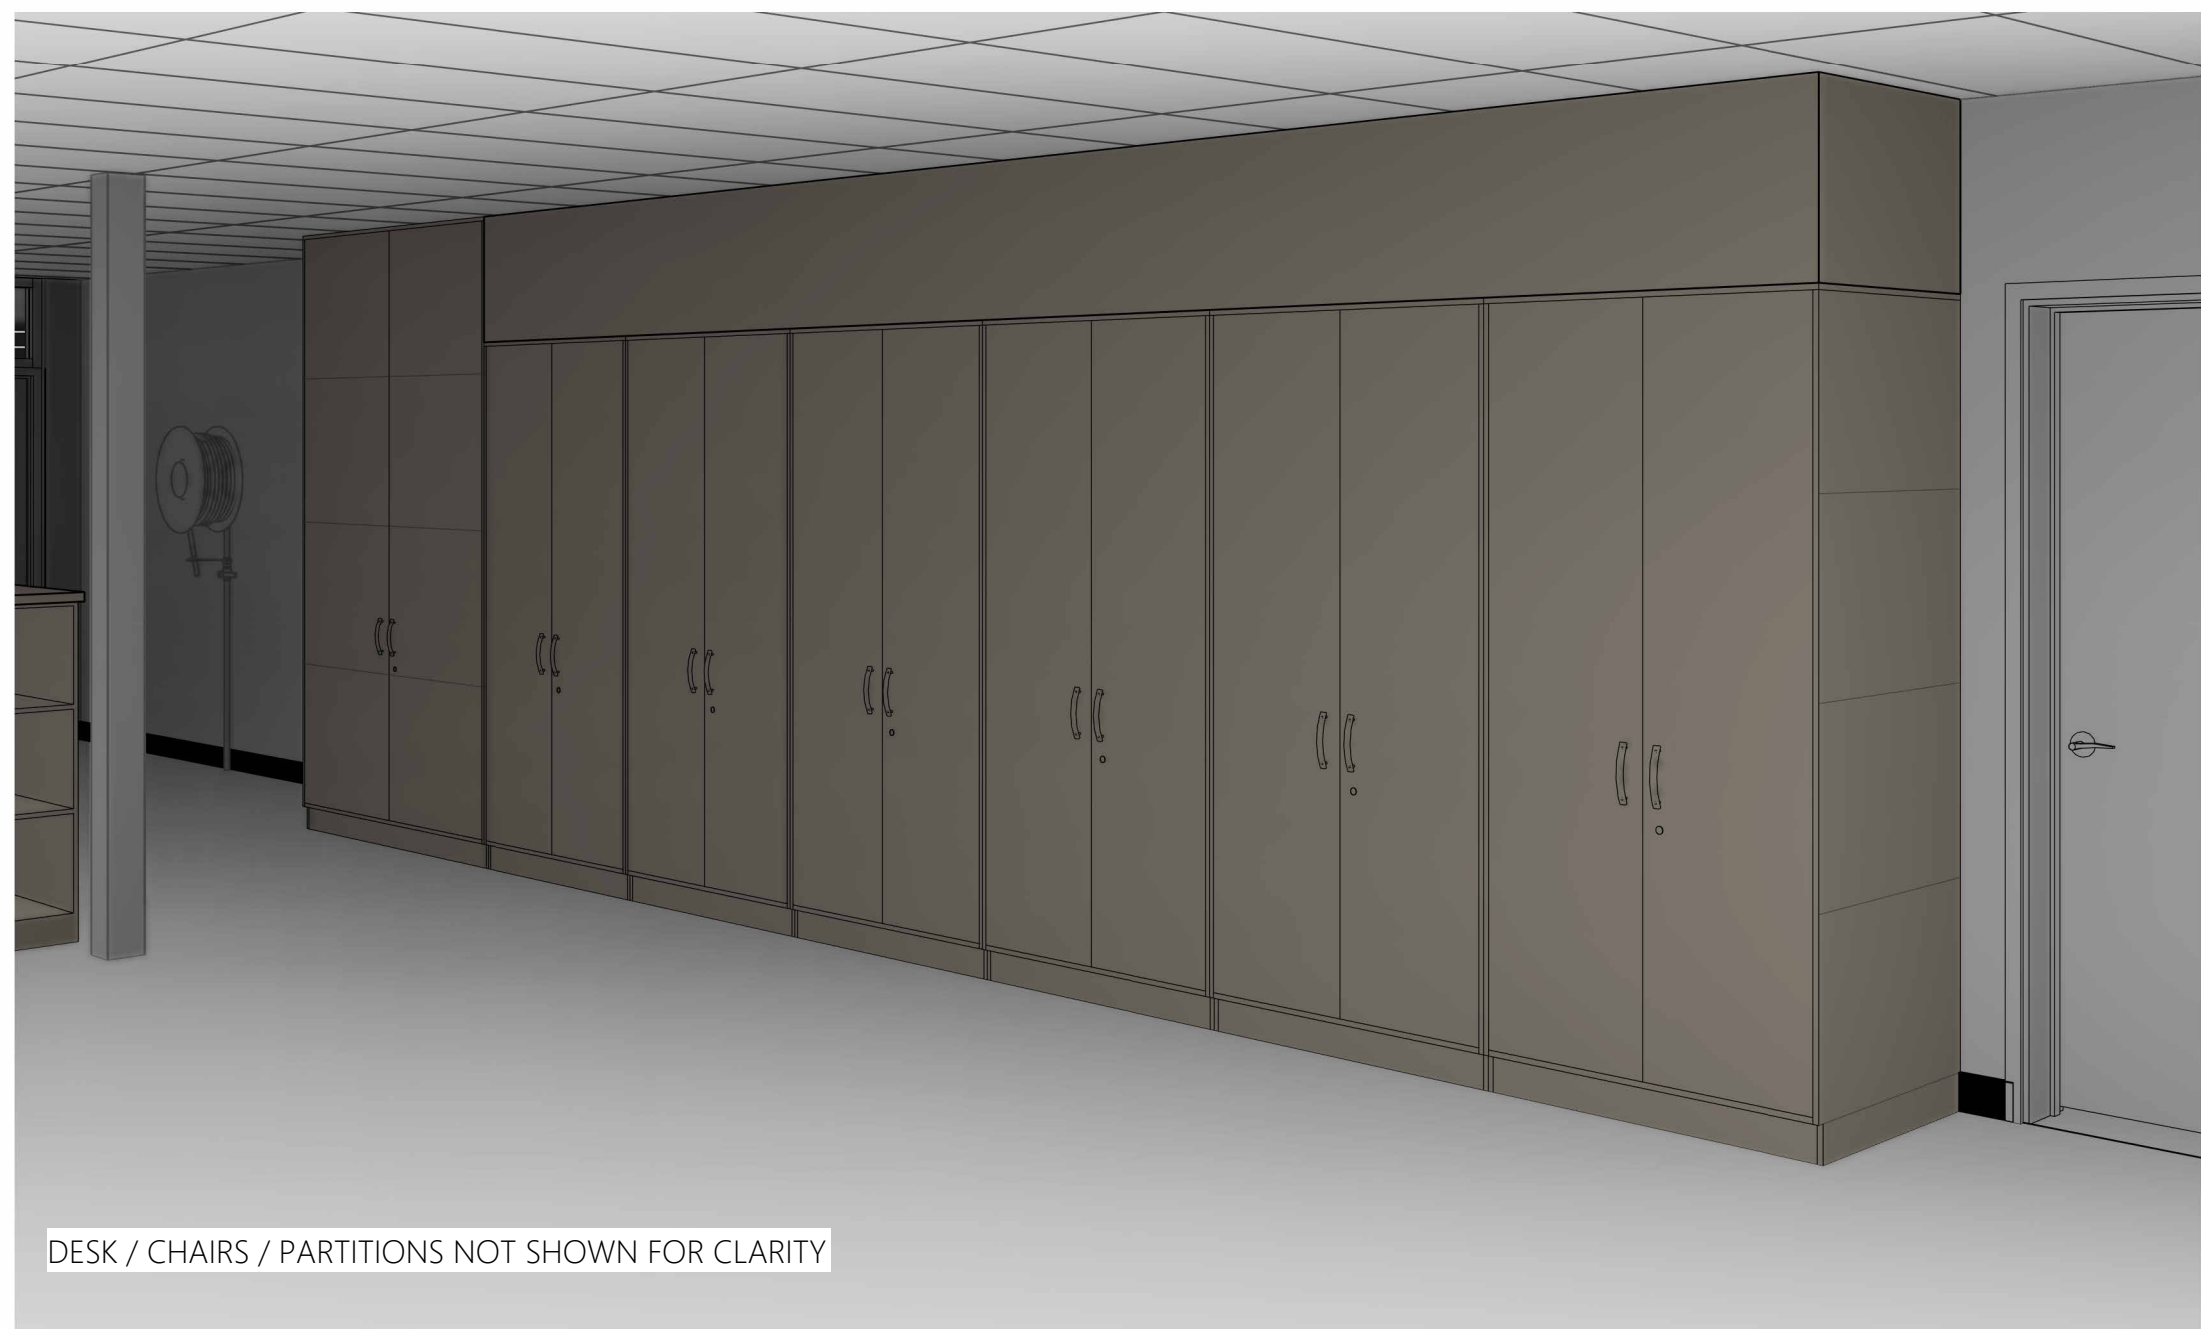

REVISIONS

Rev	Description	Date
T1	TENDER ISSUE	12.03.2026

DO NOT SCALE THIS DRAWINGS

TENDER ISSUE



Project Details
WAREHOUSE REFURB

Address
STANWELL POWER STATION


Drawing Title
INTERNAL ELEVATIONS 2 - OPEN OFFICE



0483 988 655 M
info@designelements.com.au E
QBCC No: 1247120 BDAQ No: 0001677

Scale: 1 : 50 Rev:
Date: MARCH 2026 **T1**
Drawn: Author

Project No: Drawing No:
25_003 A2-601

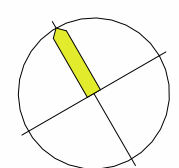

REVISIONS		
Rev	Description	Date
T1	TENDER ISSUE	12.03.2026

DO NOT SCALE THIS DRAWINGS



TENDER ISSUE

Client



Project Details

WAREHOUSE REFURB

Address

STANWELL POWER STATION



Drawing Title

INTERNAL ELEVATIONS 3 - CENTRAL MEETING ROOMS




0483 988 655 
info@designelements.com.au 
QBCC No: 1247120 BDAQ No: 0001677

Scale: 1 : 50 Rev: **T1**
Date: MARCH 2026
Drawn: Author
Project No: Drawing No:
25_003 A2-602

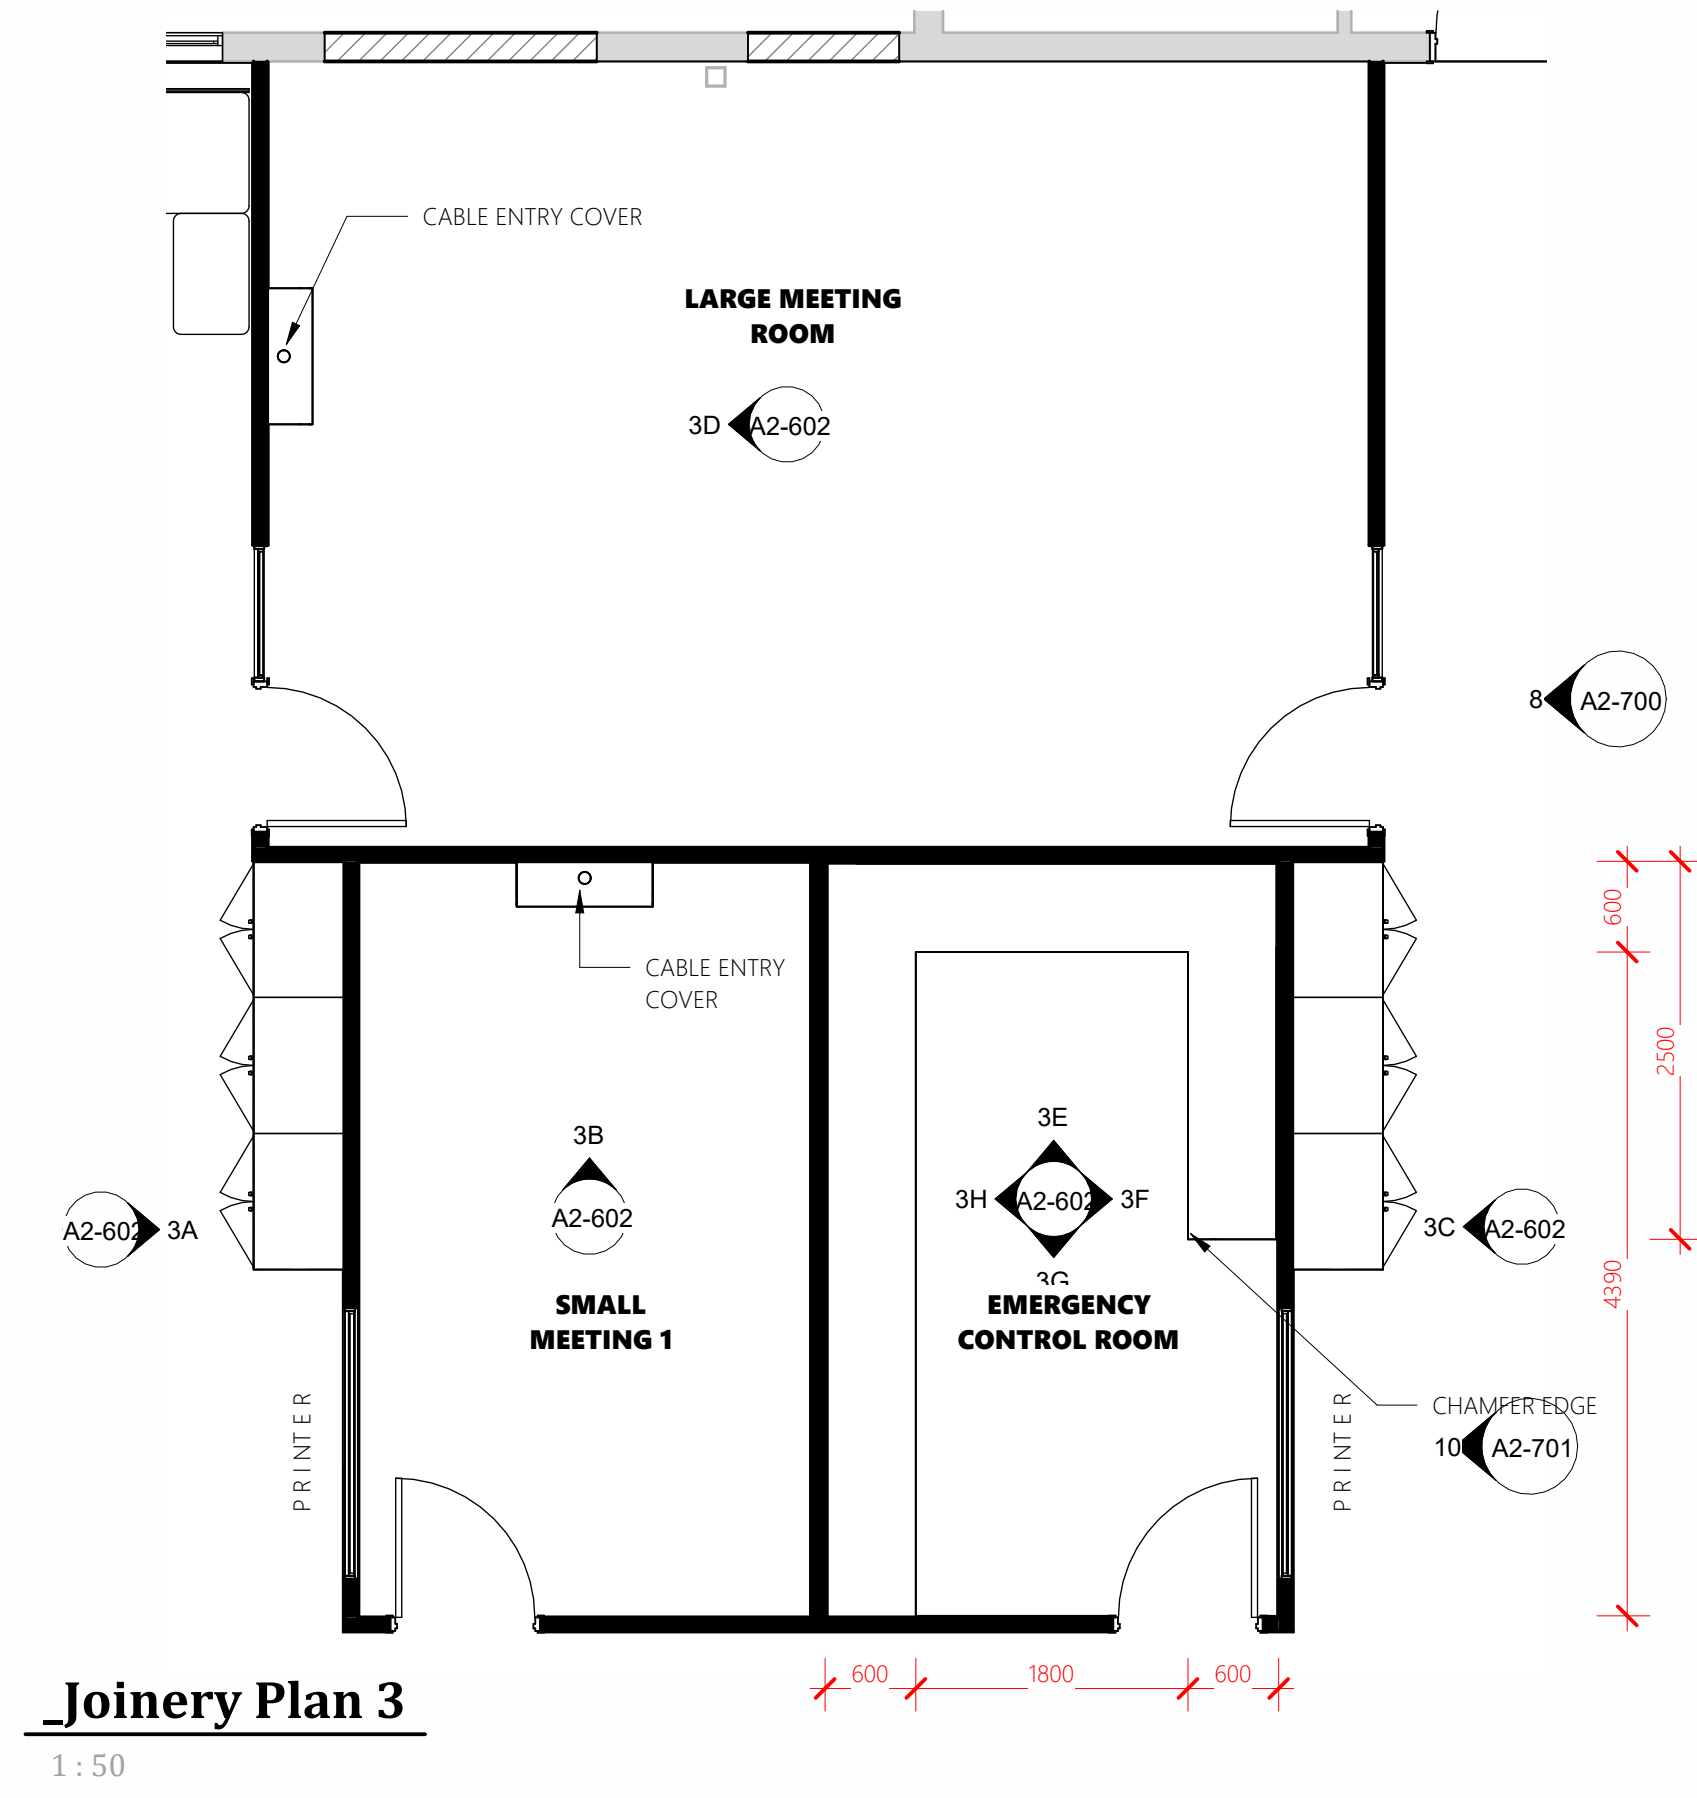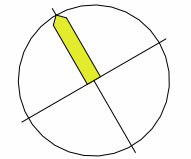


Joinery Plan 3
1:50

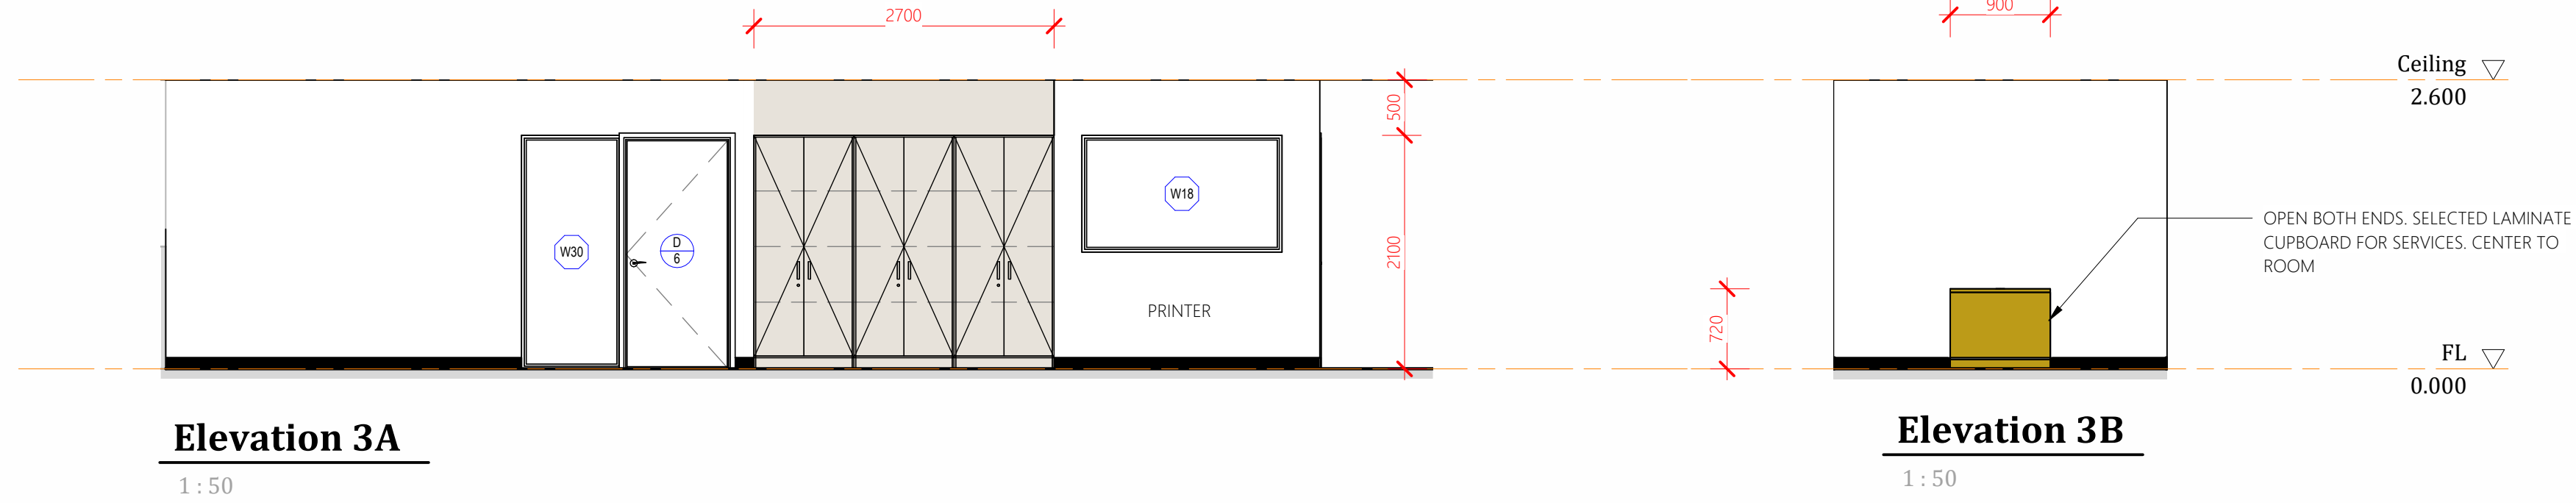


Elevation 3A
1:50

Elevation 3B
1:50

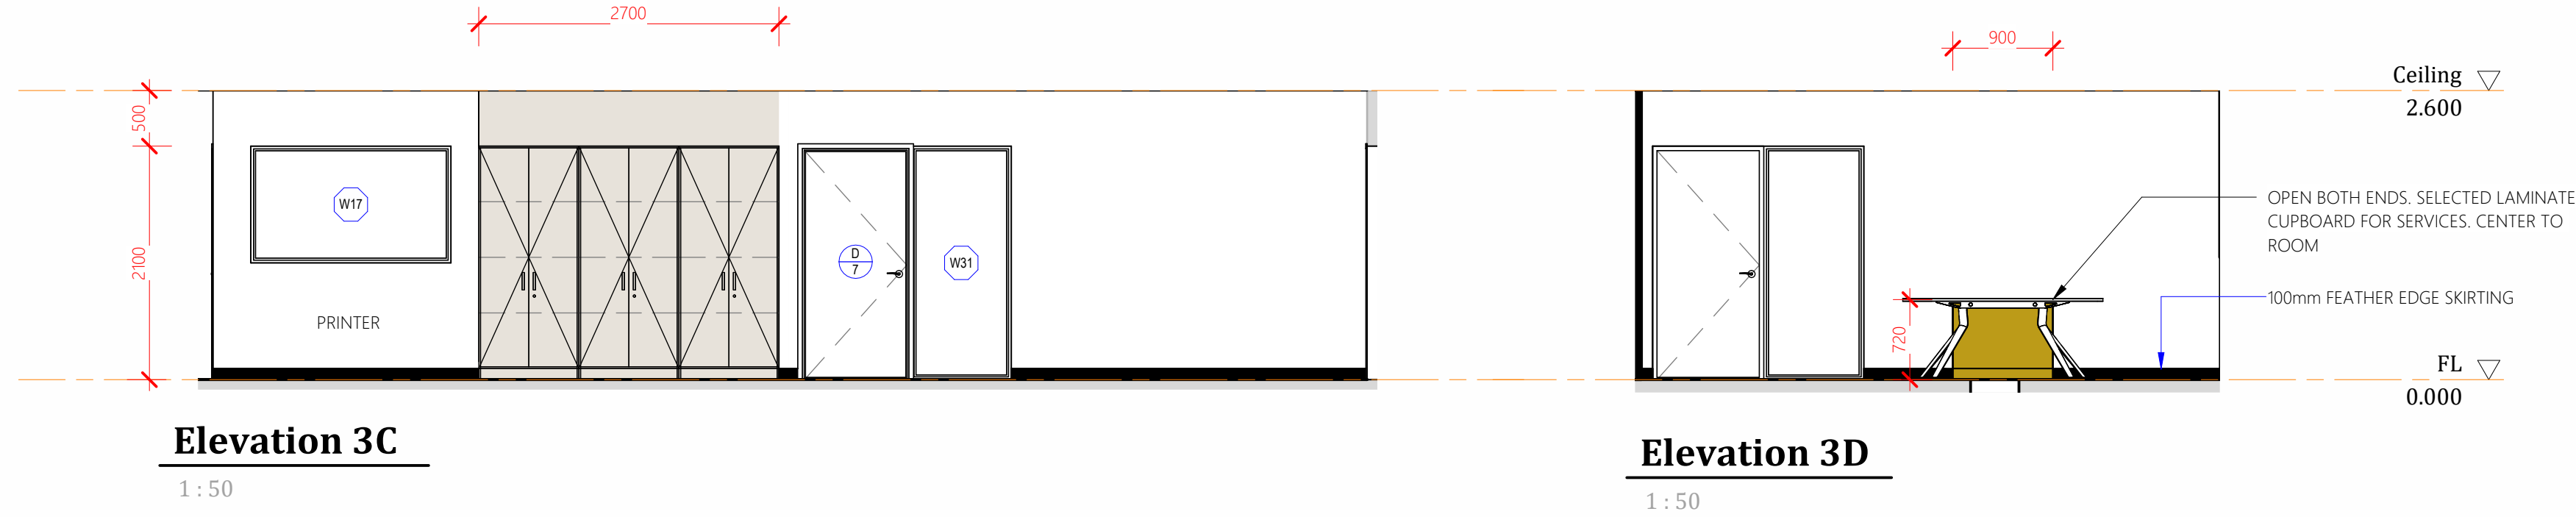


Elevation 3C
1:50

Elevation 3D
1:50

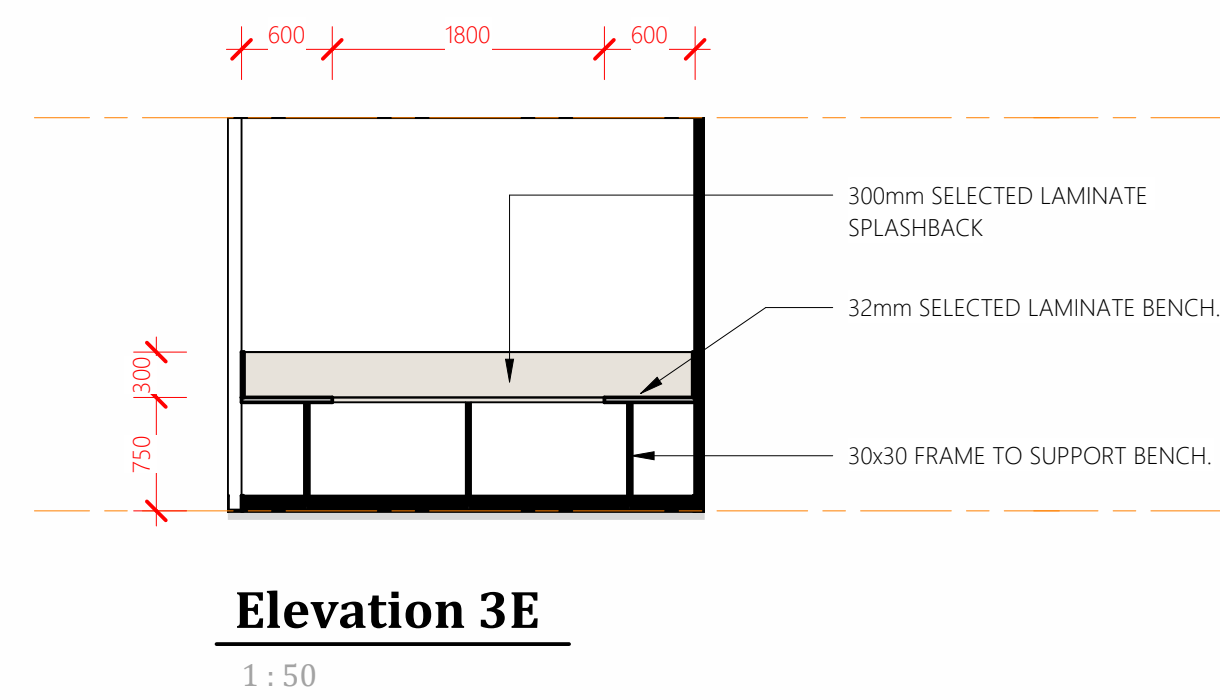


Elevation 3E
1:50


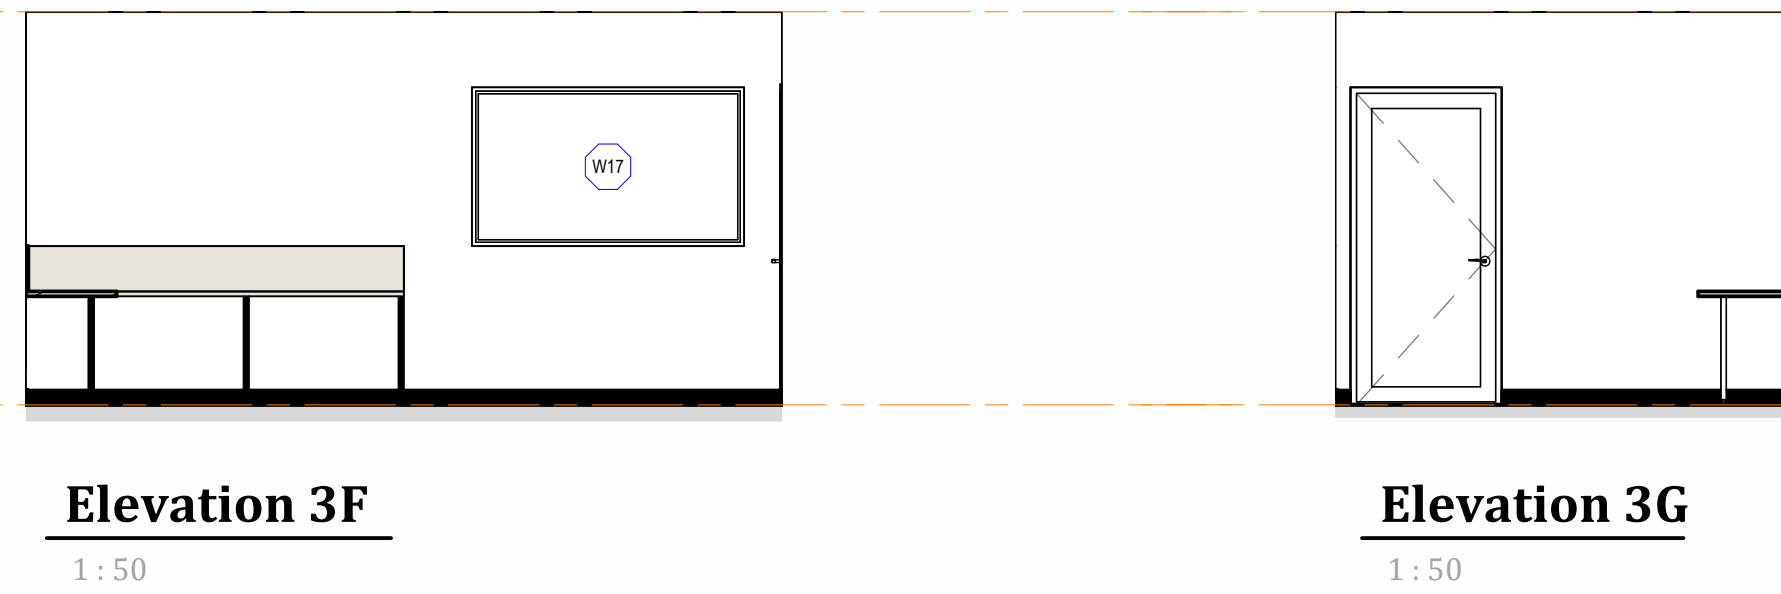



Elevation 3F
1:50

Elevation 3G
1:50

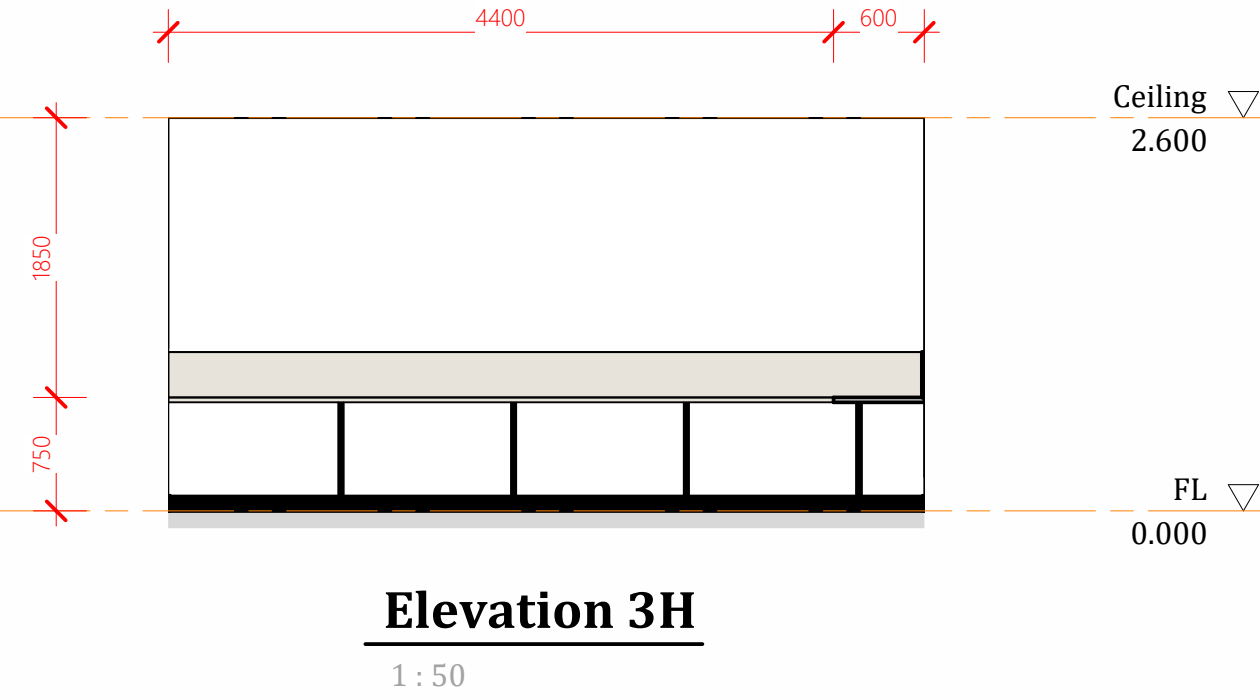


Elevation 3H
1:50

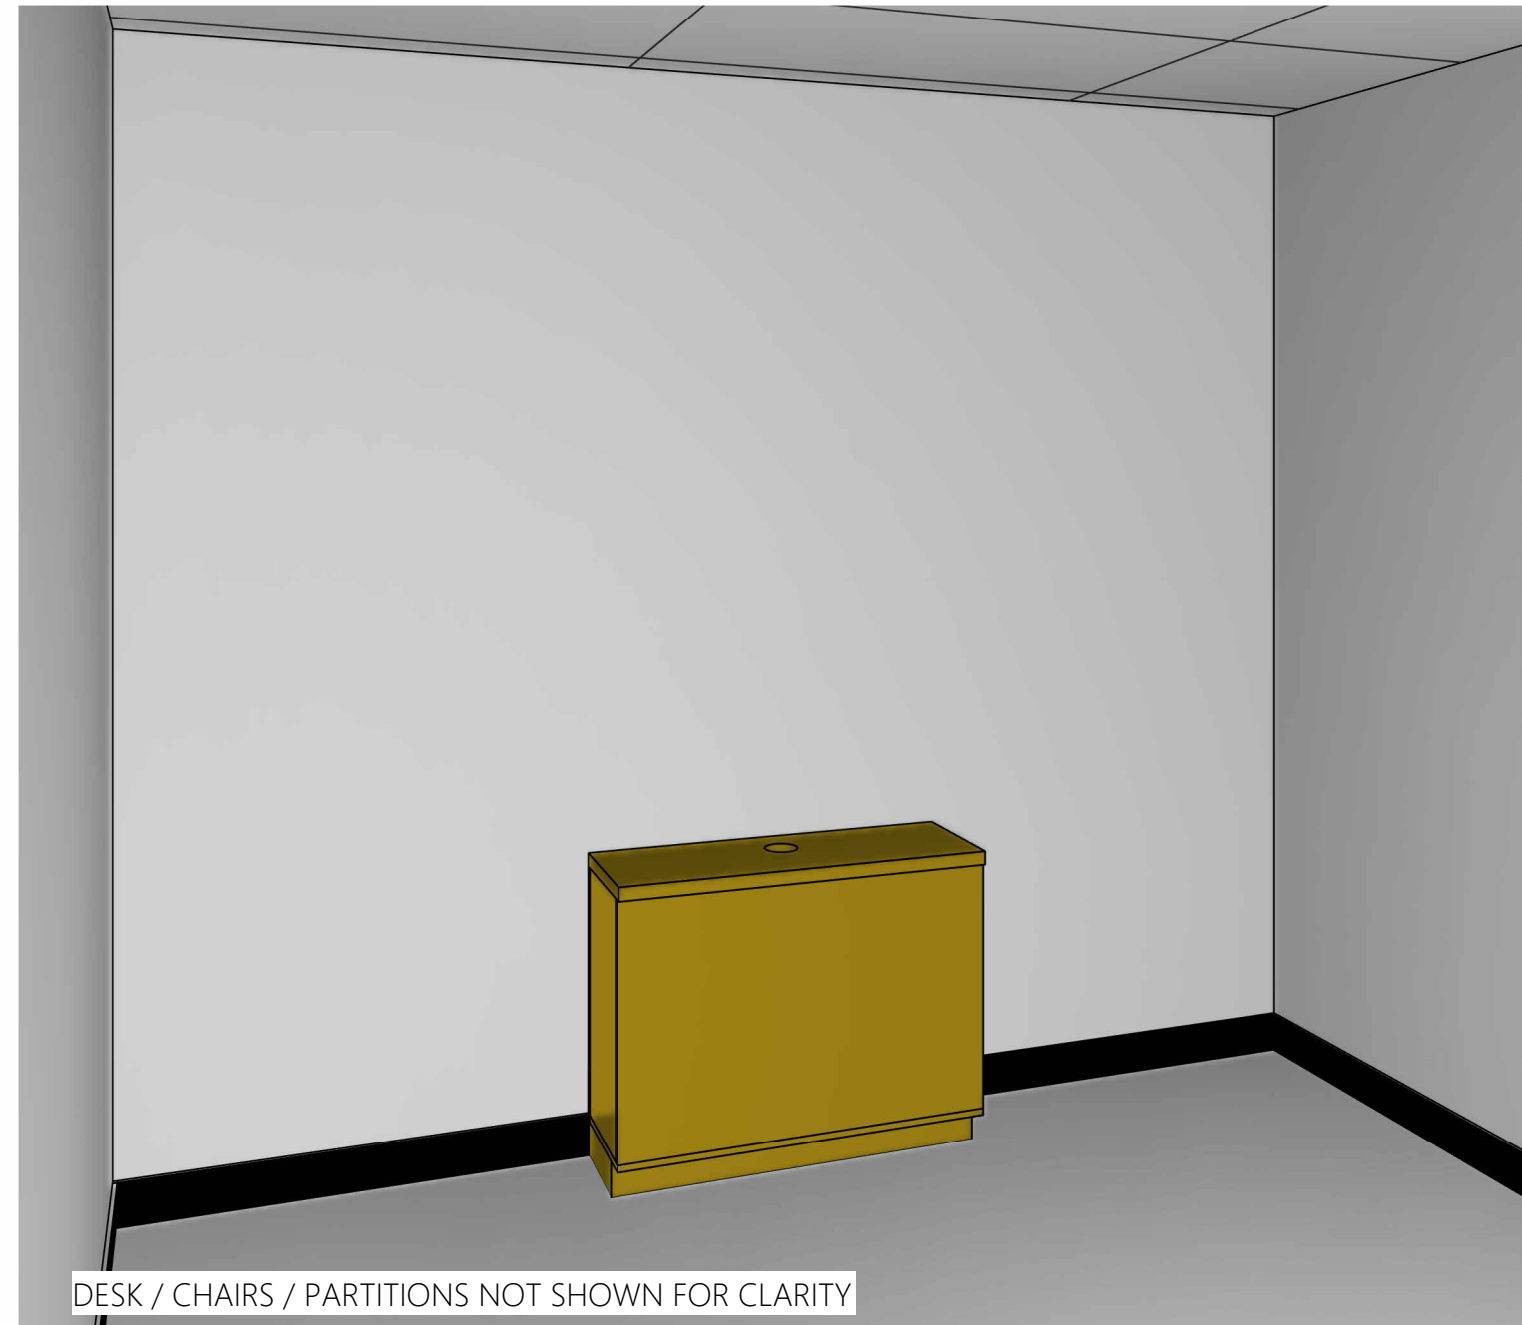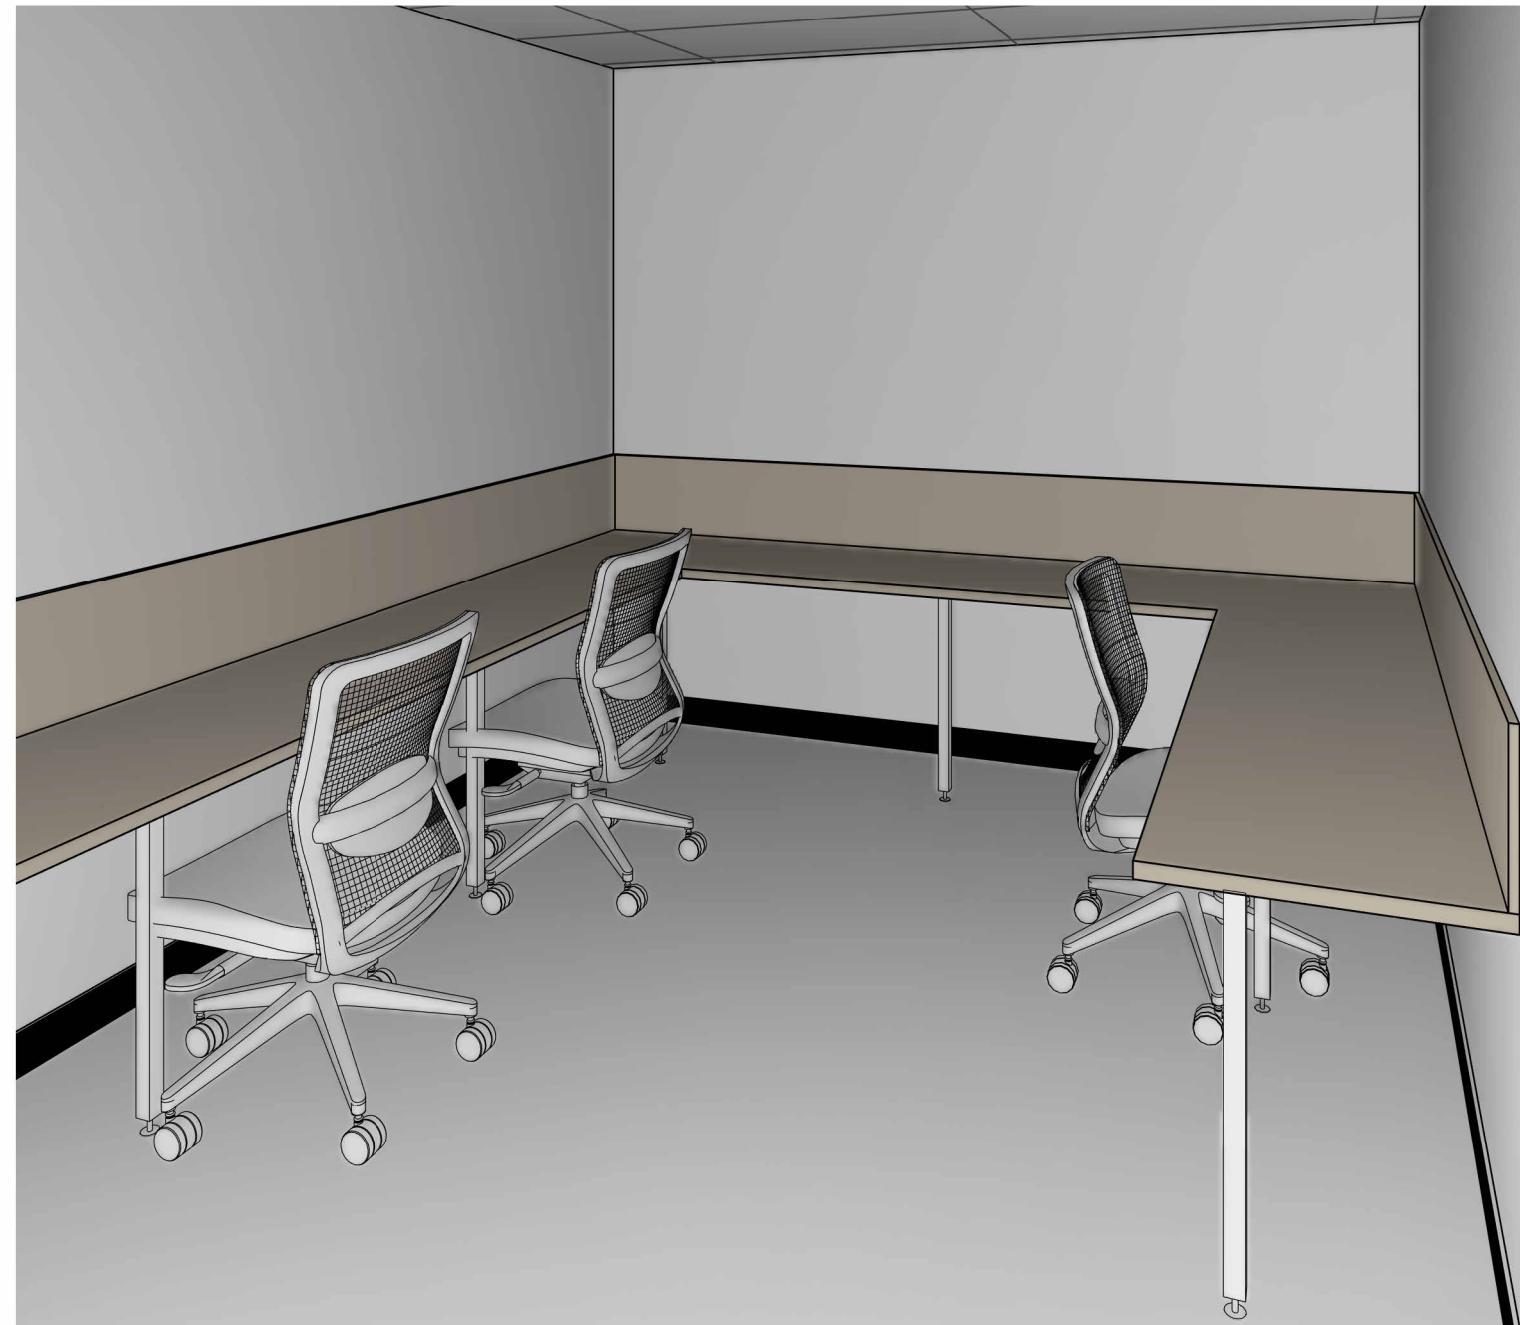

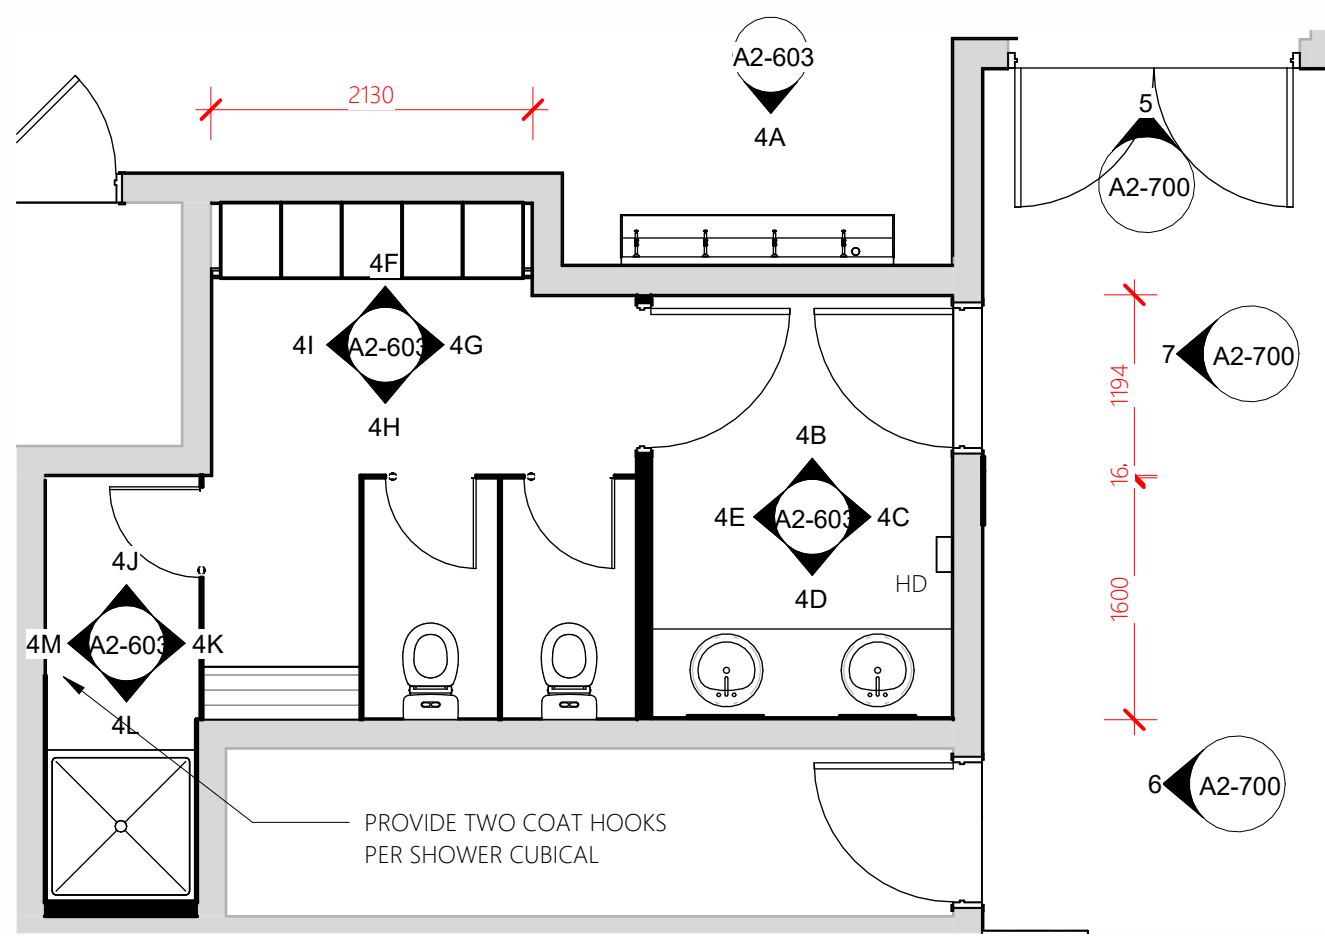

Joinery Plan 4

1 : 50

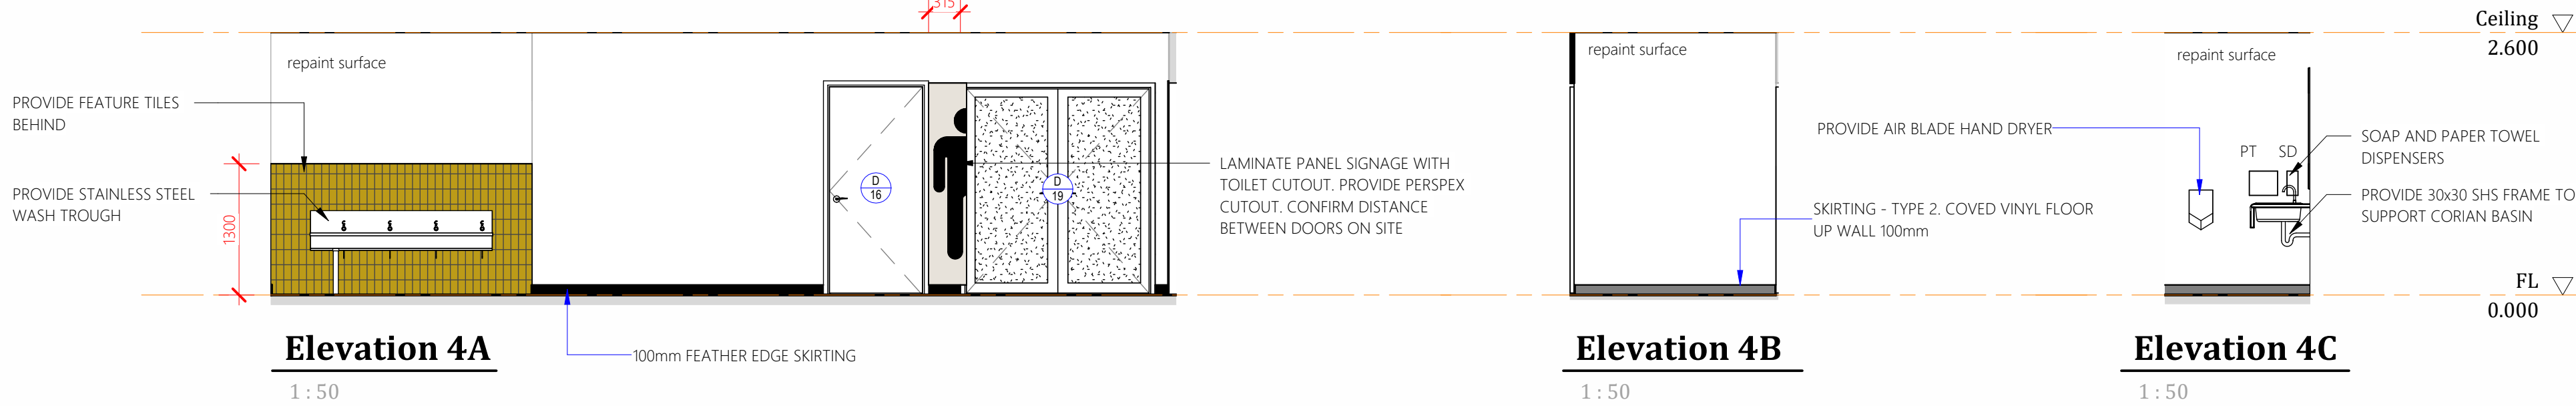

Elevation 4A


1 : 50

Elevation 4B

1 : 50

Elevation 4C

1 : 50

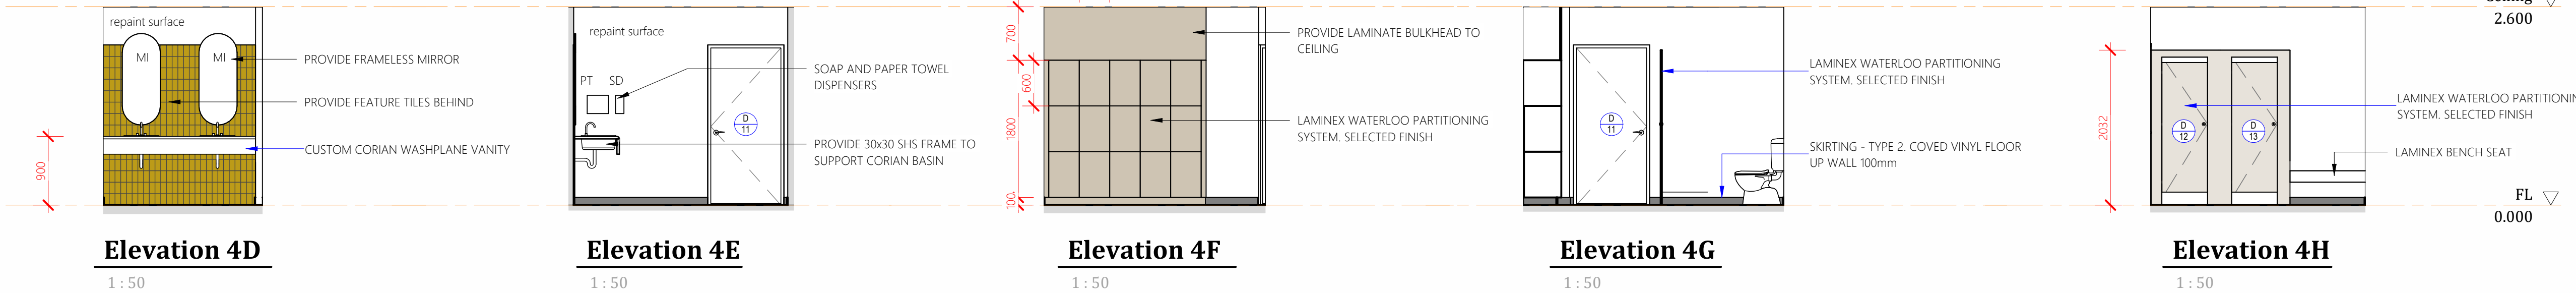

Elevation 4D

1 : 50

Elevation 4E

1 : 50

Elevation 4F


1 : 50

Elevation 4G

1 : 50

Elevation 4H

1 : 50

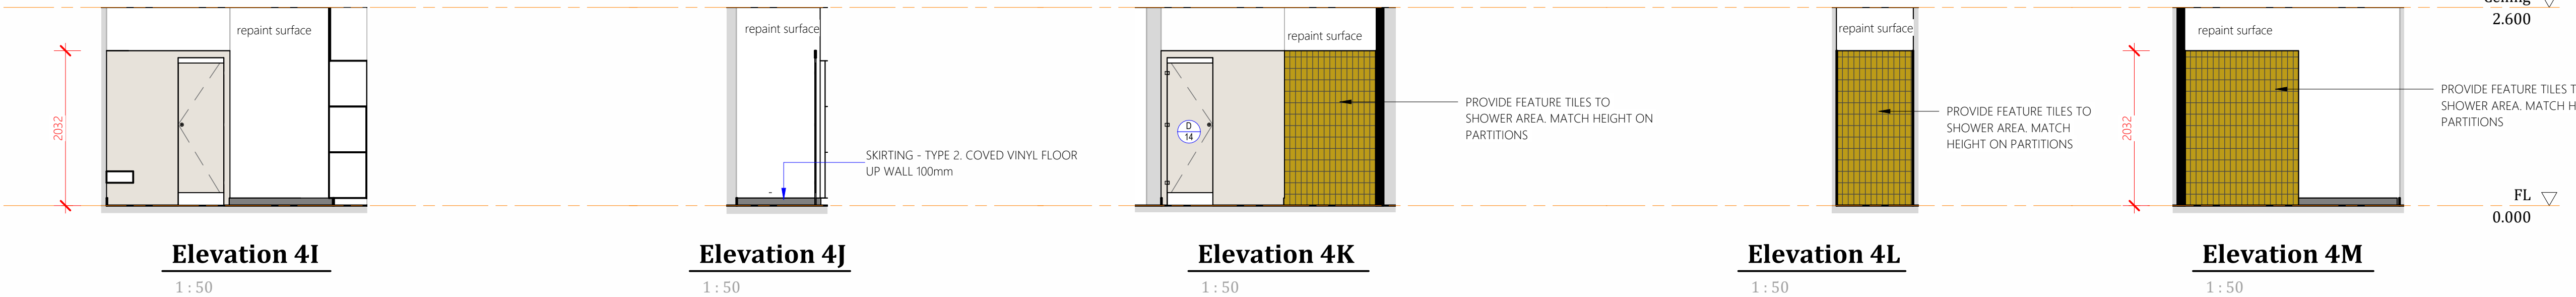

Elevation 4I

1 : 50

Elevation 4J

1 : 50

Elevation 4K


1 : 50

Elevation 4L

1 : 50

Elevation 4M

1 : 50

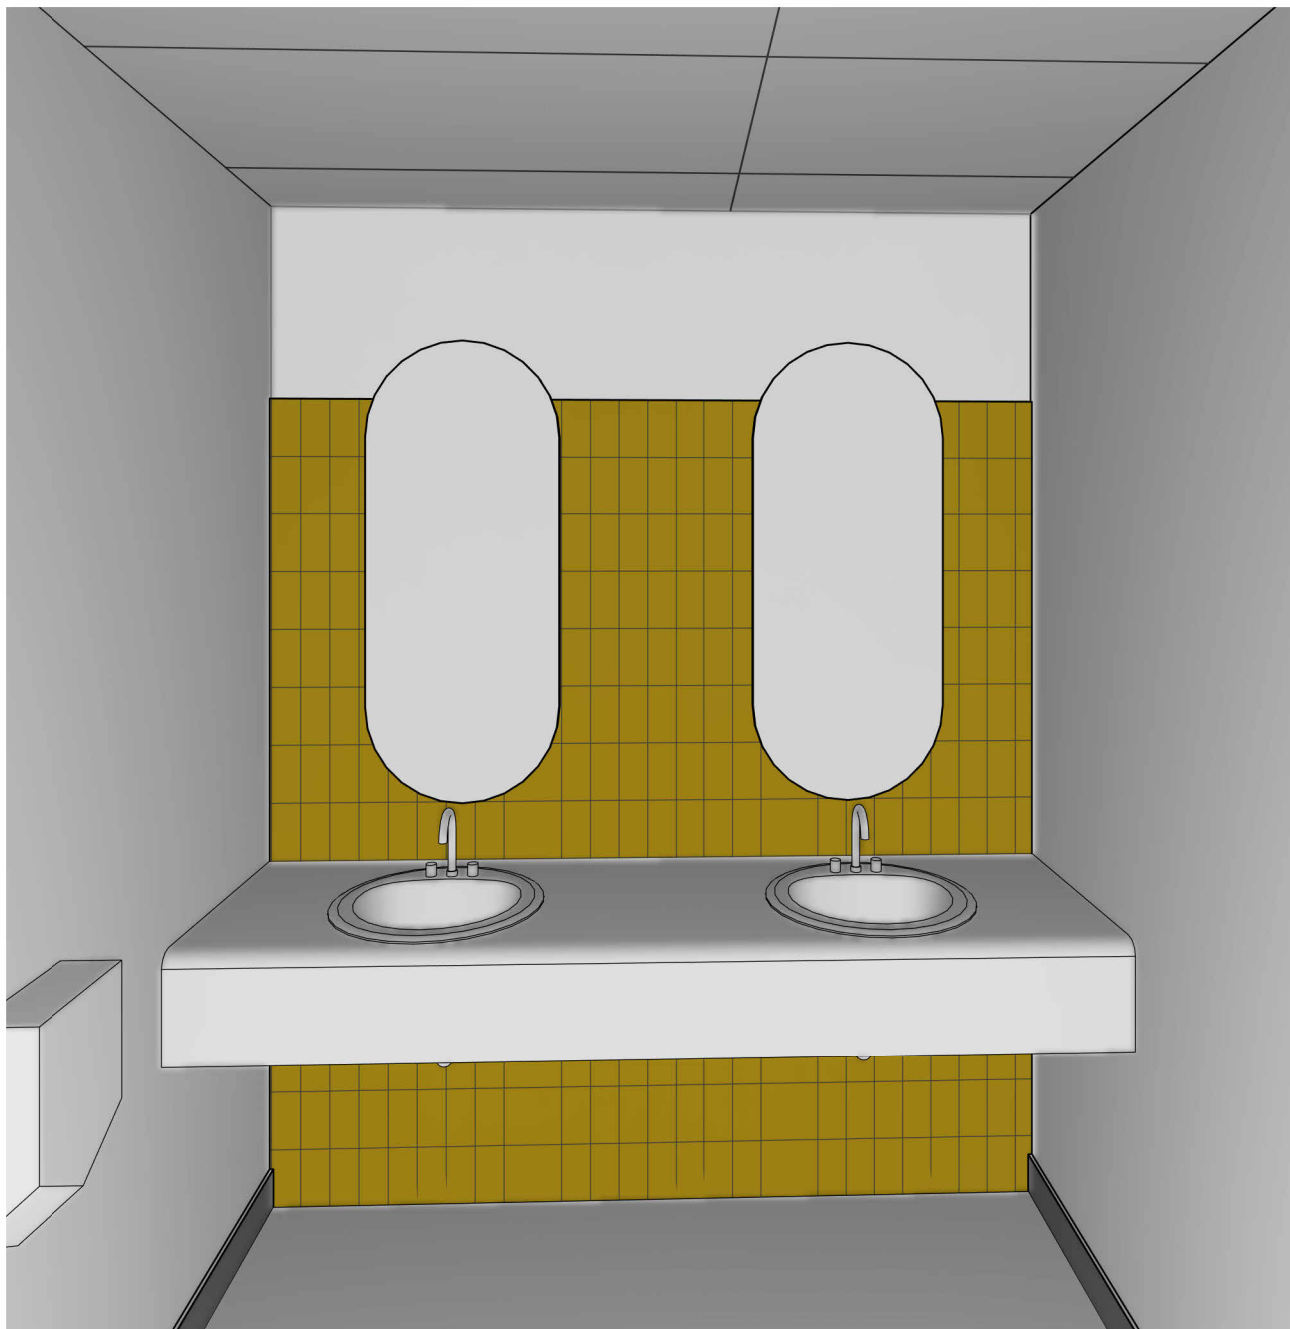

REVISIONS		
Rev	Description	Date
T1	TENDER ISSUE	12.03.2026

DO NOT SCALE THIS DRAWINGS




TENDER ISSUE



Project Details
WAREHOUSE REFURB
Address
STANWELL POWER STATION
Drawing Title
INTERNAL ELEVATIONS 5 - FEMALE AMENITIES

0483 988 655 M	
info@designelements.com.au E	
QBCC No: 1247120 BDAQ No: 0001677	
Scale: 1 : 50	Rev:
Date: MARCH 2026	T1
Drawn: Author	
Project No:	Drawing No:
25_003	A2-603


13/03/2026 11:27:59 AM

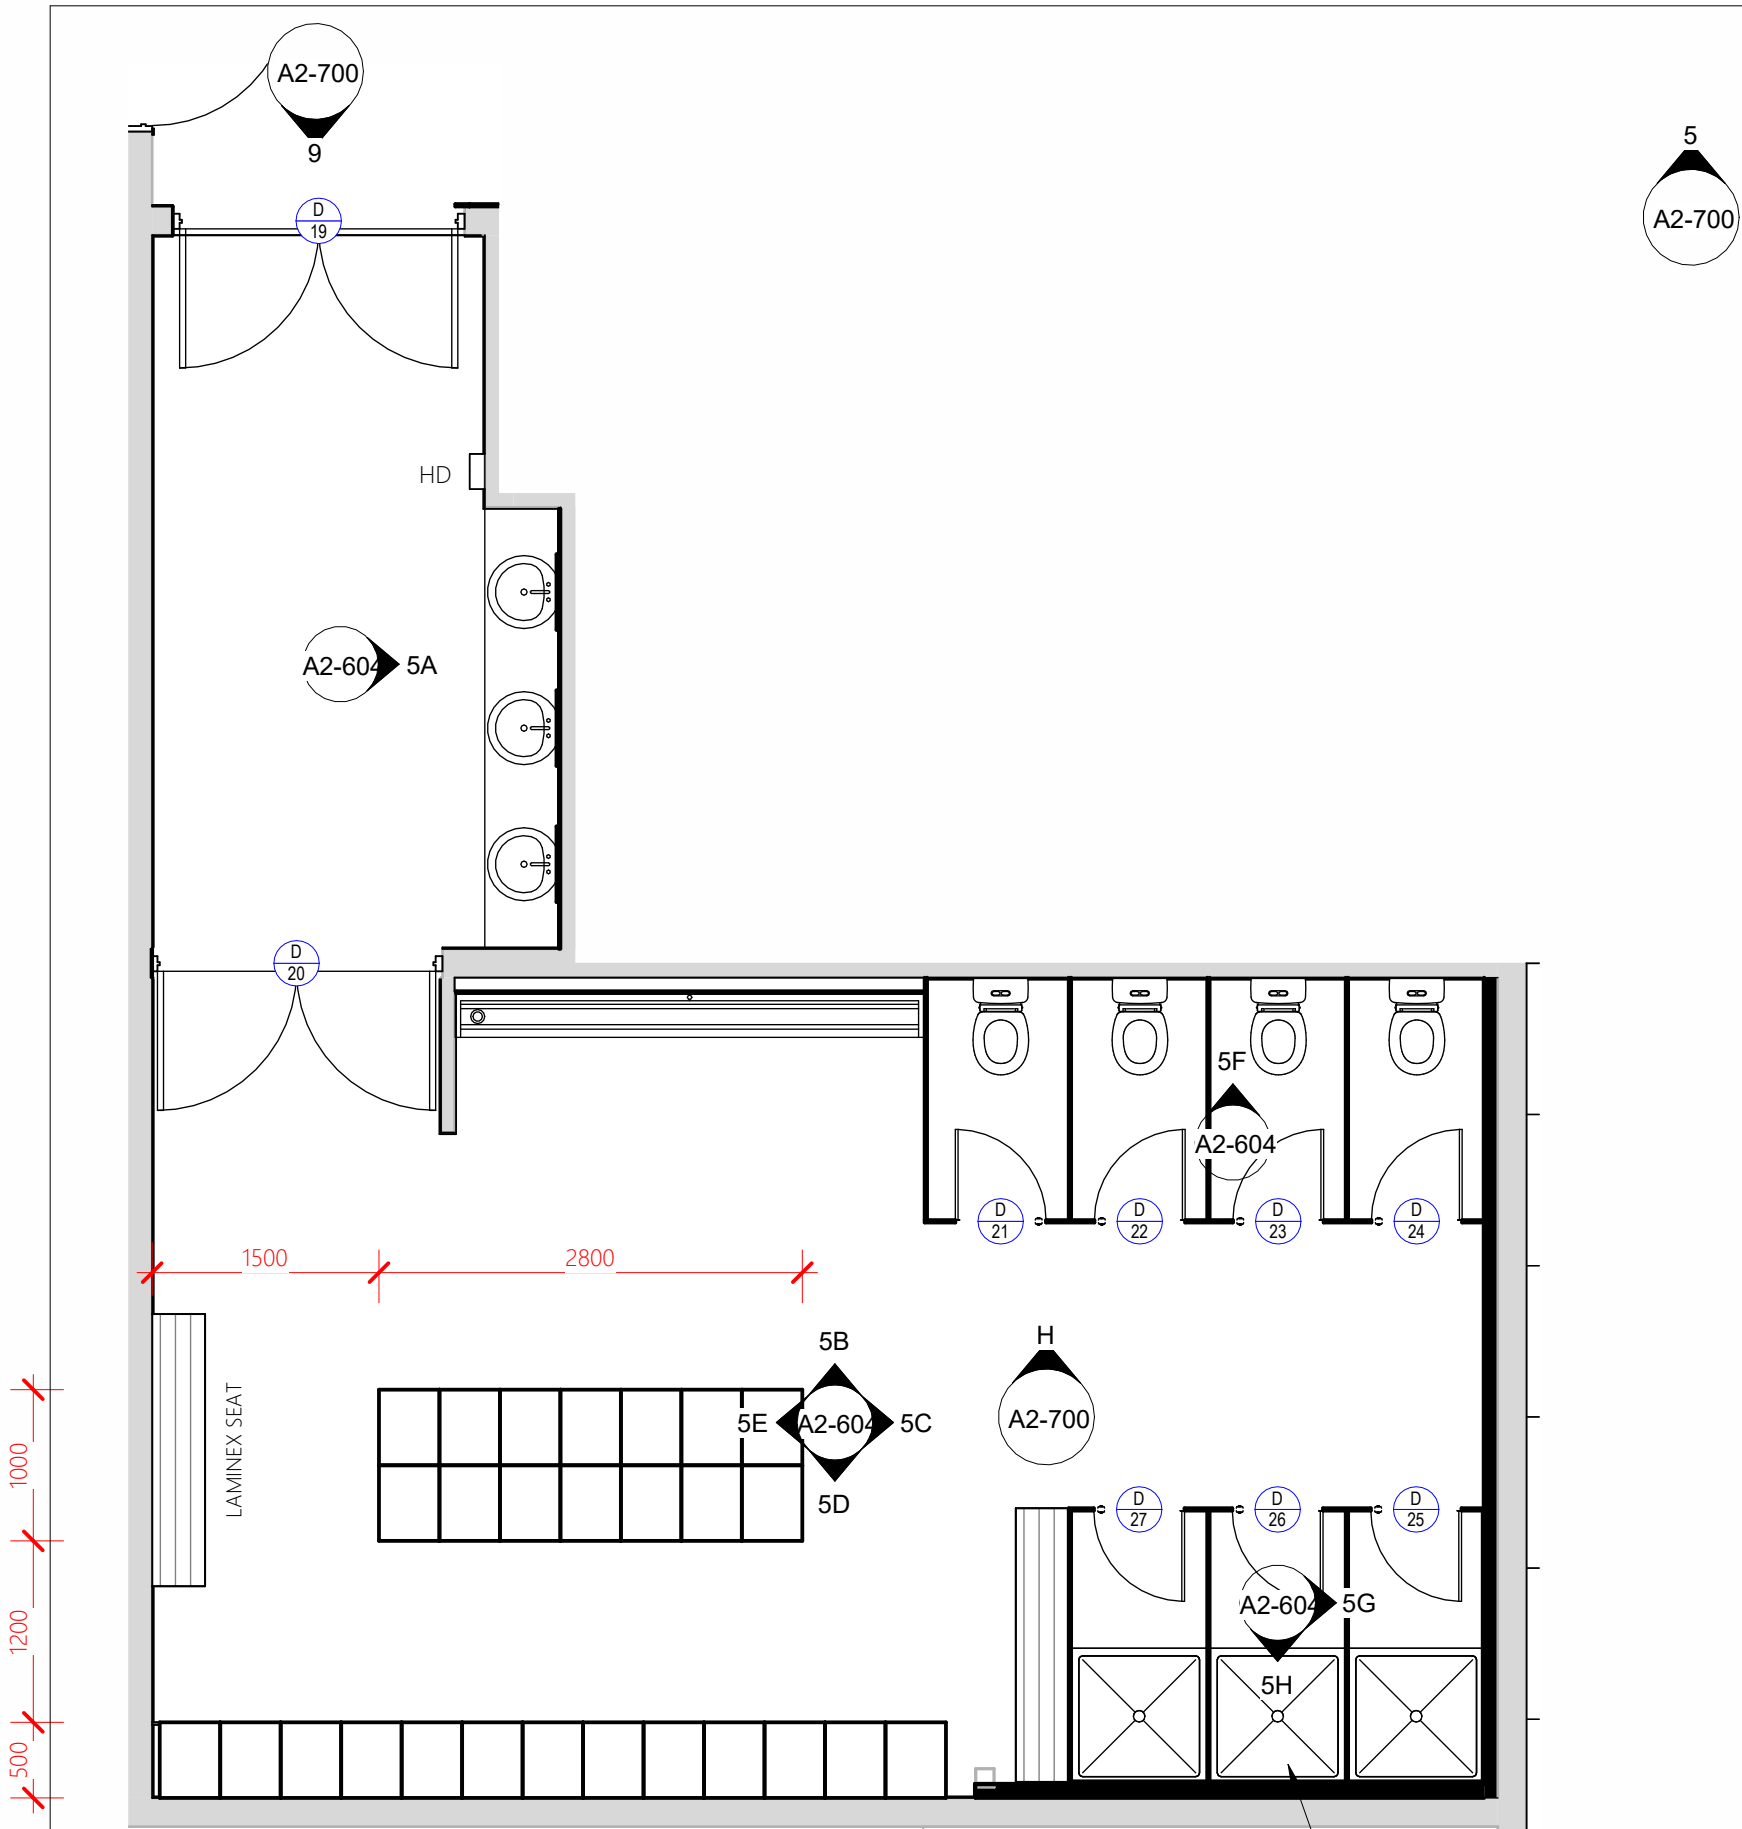

Joinery Plan 5

1:50

PROVIDE TWO COAT HOOKS
PER SHOWER CUBICAL

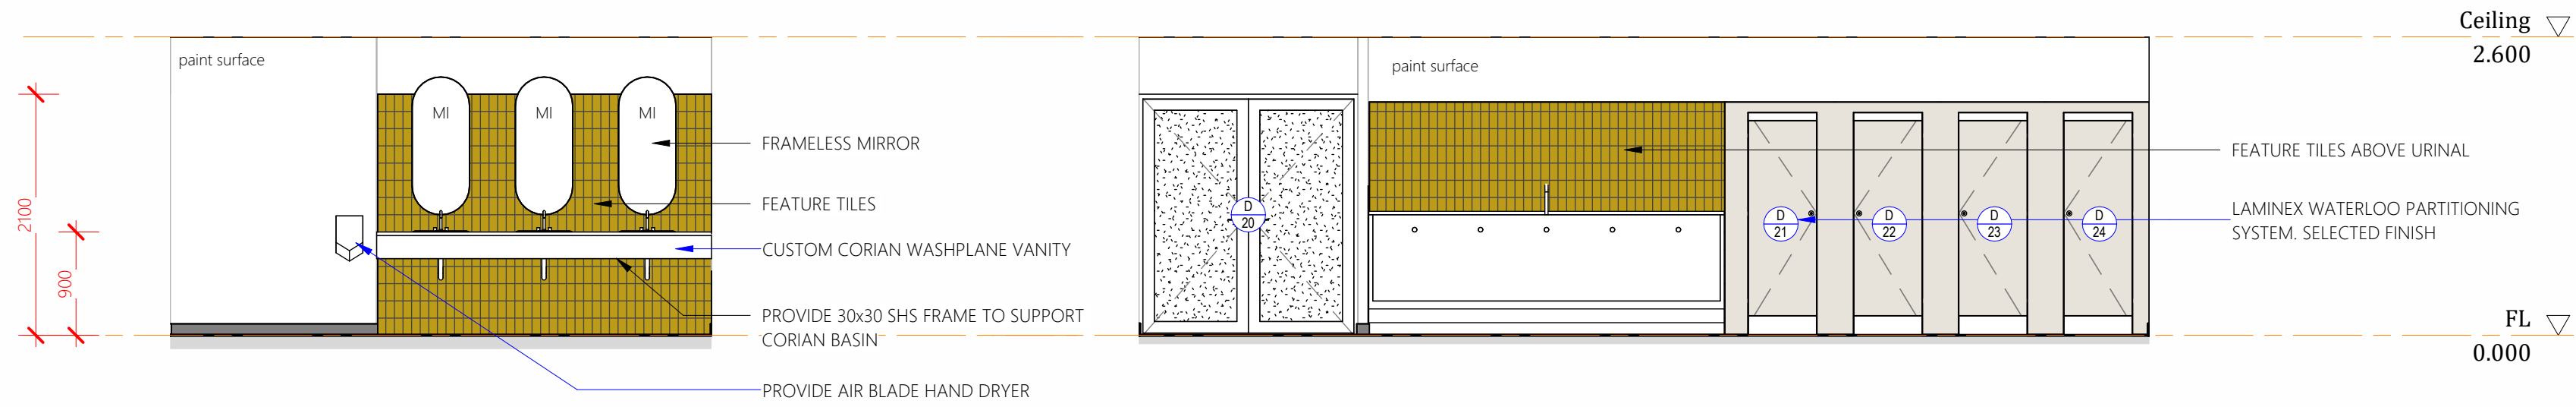


Elevation 5A

1:50

Elevation 5B

1:50

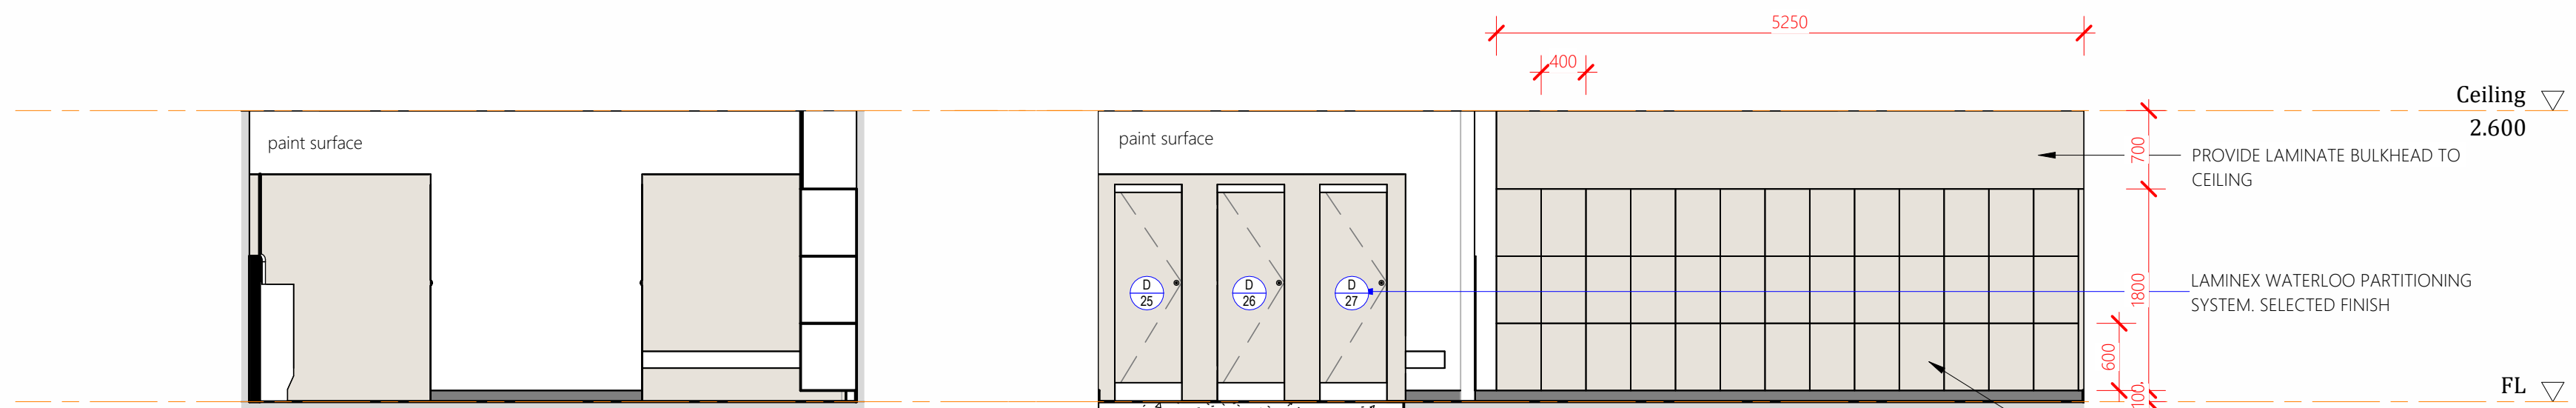


Elevation 5C

1:50

Elevation 5D

1:50

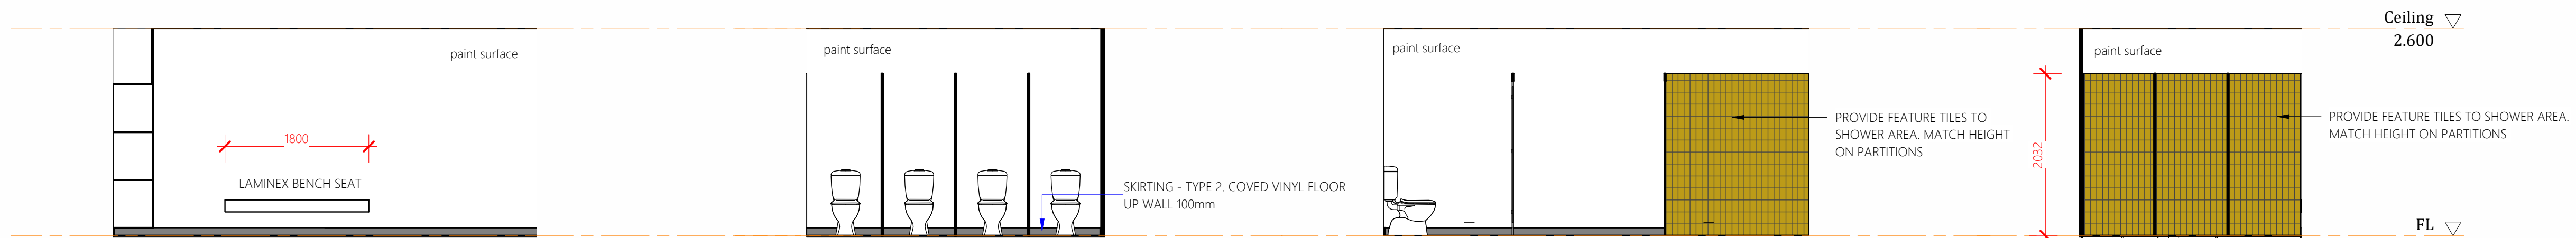

Elevation 5E

1:50

Elevation 5F


1:50

Elevation 5G

1:50

Elevation 5H


1:50

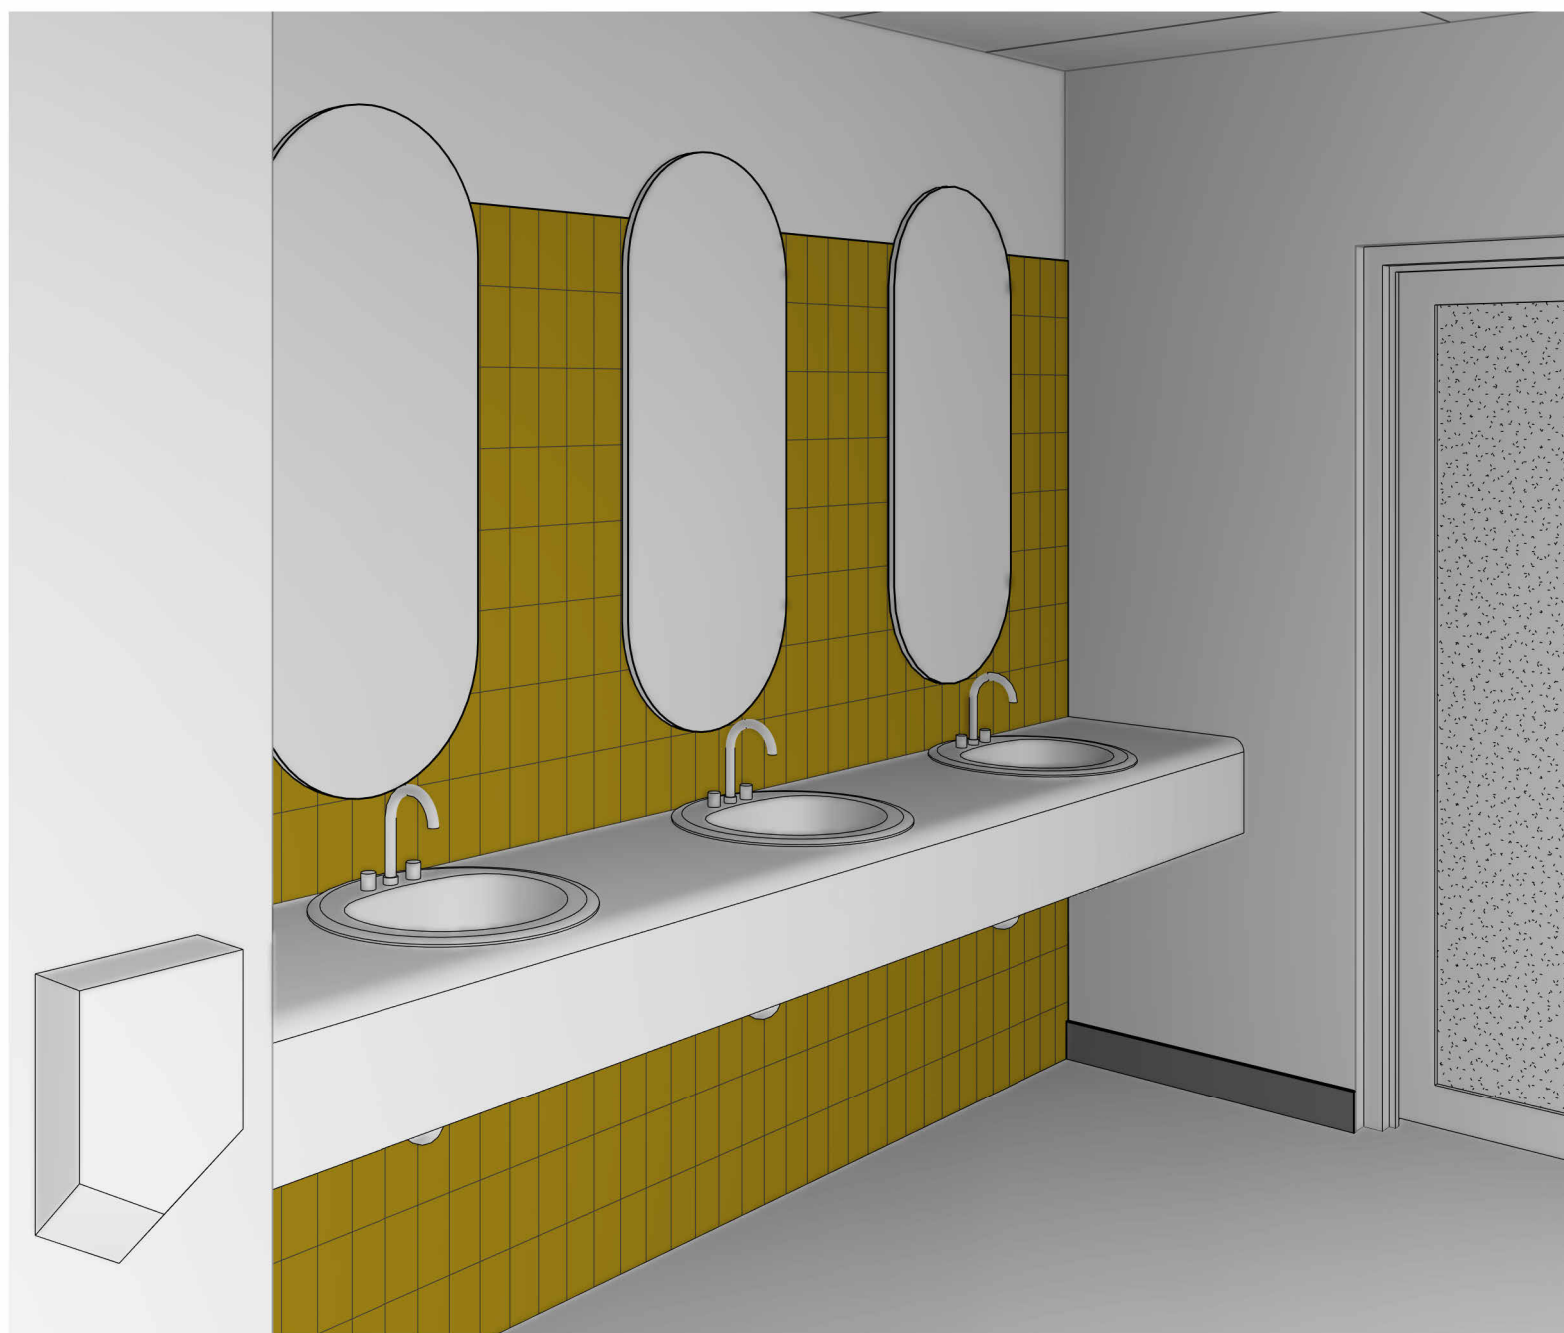

REVISIONS

Rev	Description	Date
T1	TENDER ISSUE	12.03.2026

DO NOT SCALE THIS DRAWINGS

 



TENDER ISSUE



Project Details
WAREHOUSE REFURB
Address
STANWELL POWER STATION
Drawing Title
INTERNAL ELEVATIONS 5 - MALE AMENITIES


dezi nelements BUILDING DESIGNERS
0483 988 655 M
info@dezi nelements.com.au E
QBCC No: 1247120 BDAQ No: 0001677
Scale: 1:50 Rev: T1
Date: MARCH 2026
Drawn: Author
Project No: Drawing No:
25_003 A2-604

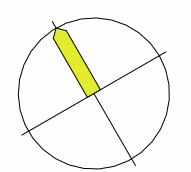

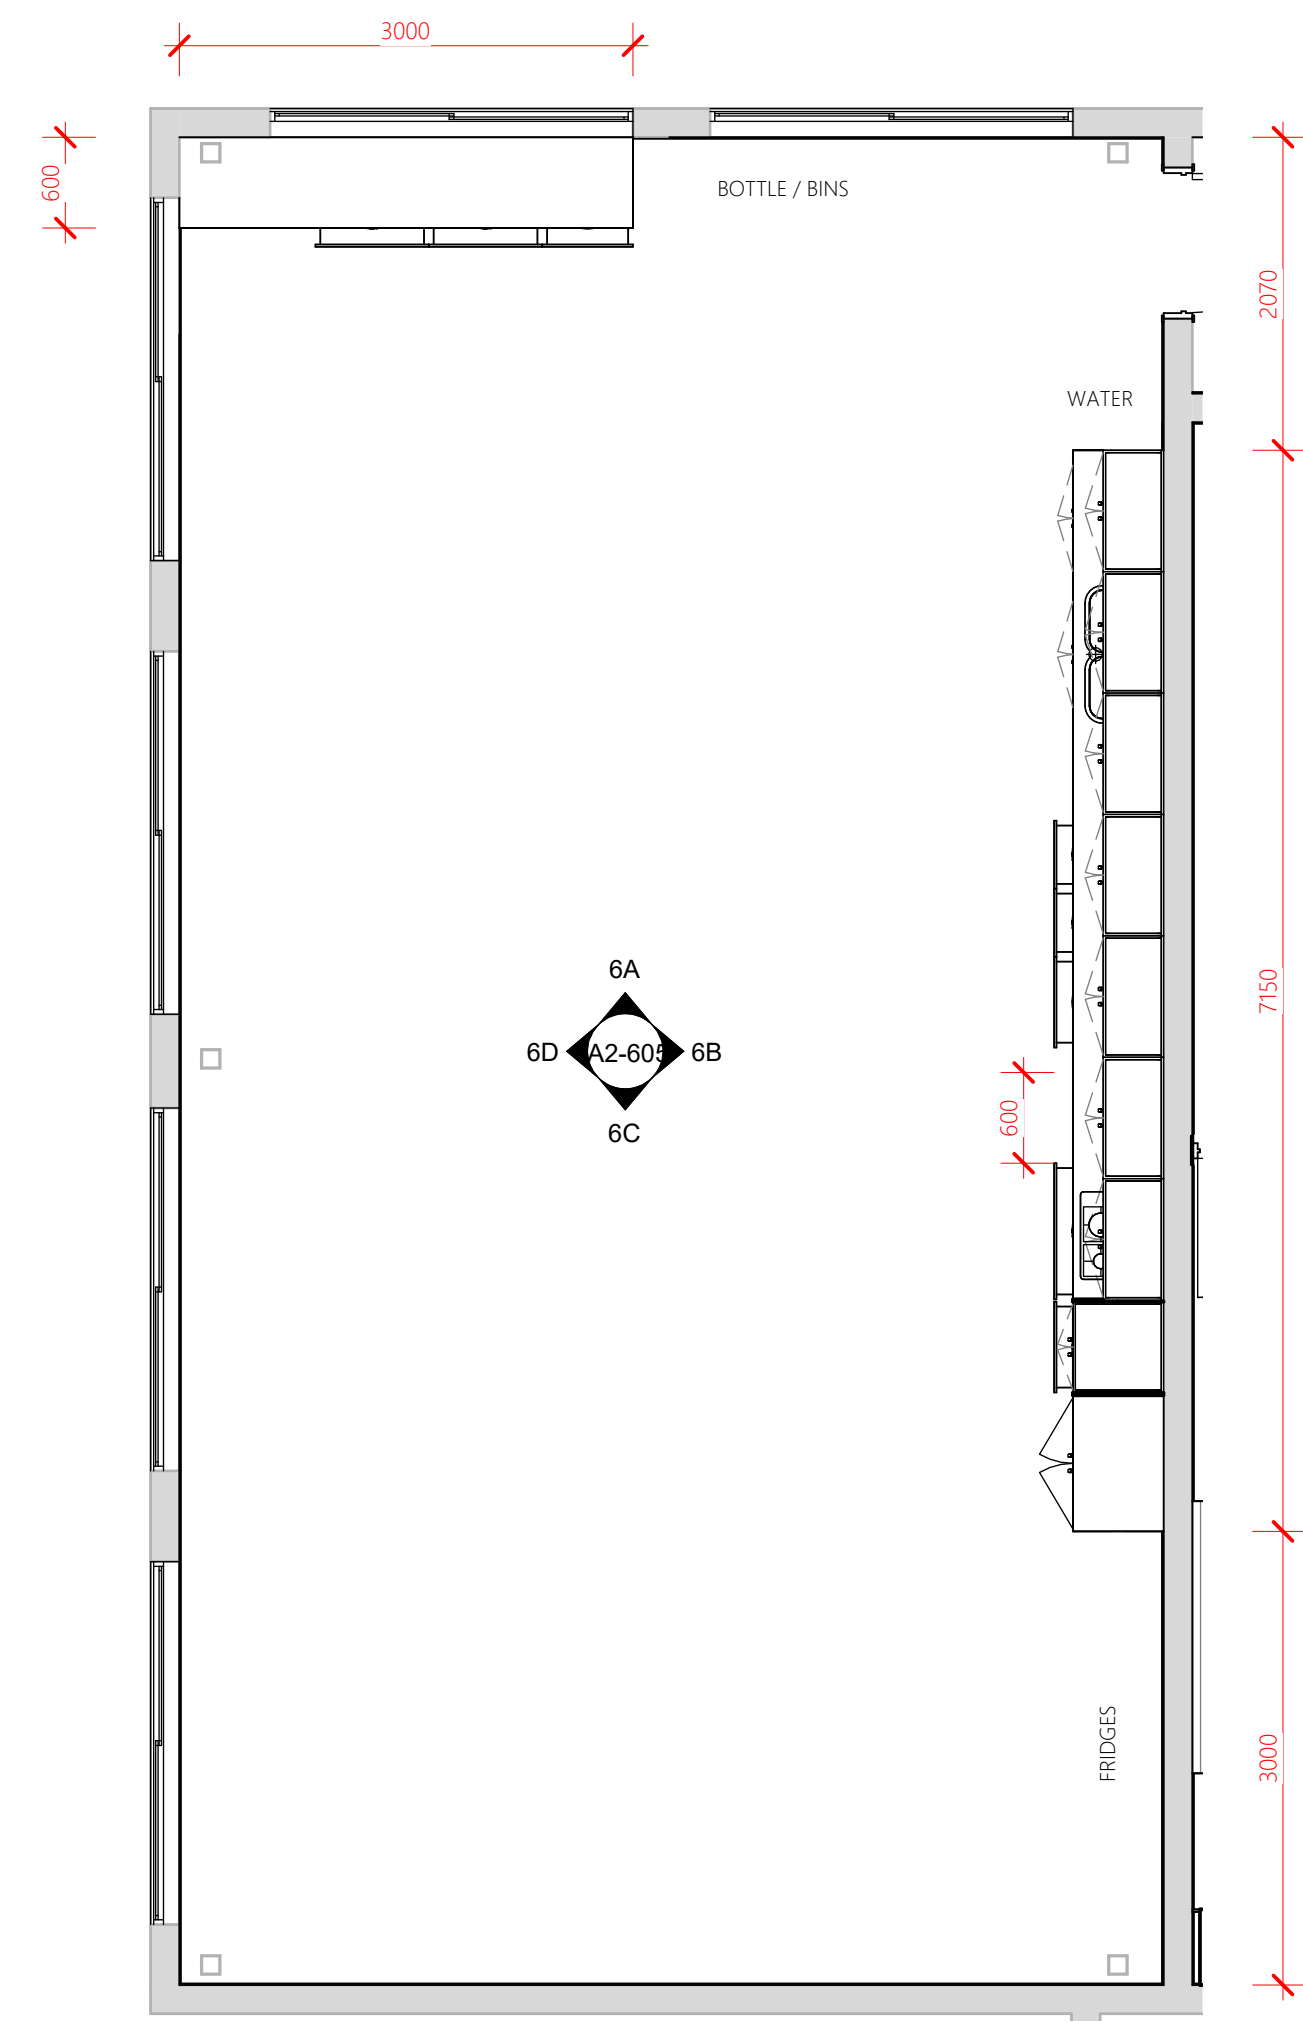

Joinery Plan 6

1 : 50

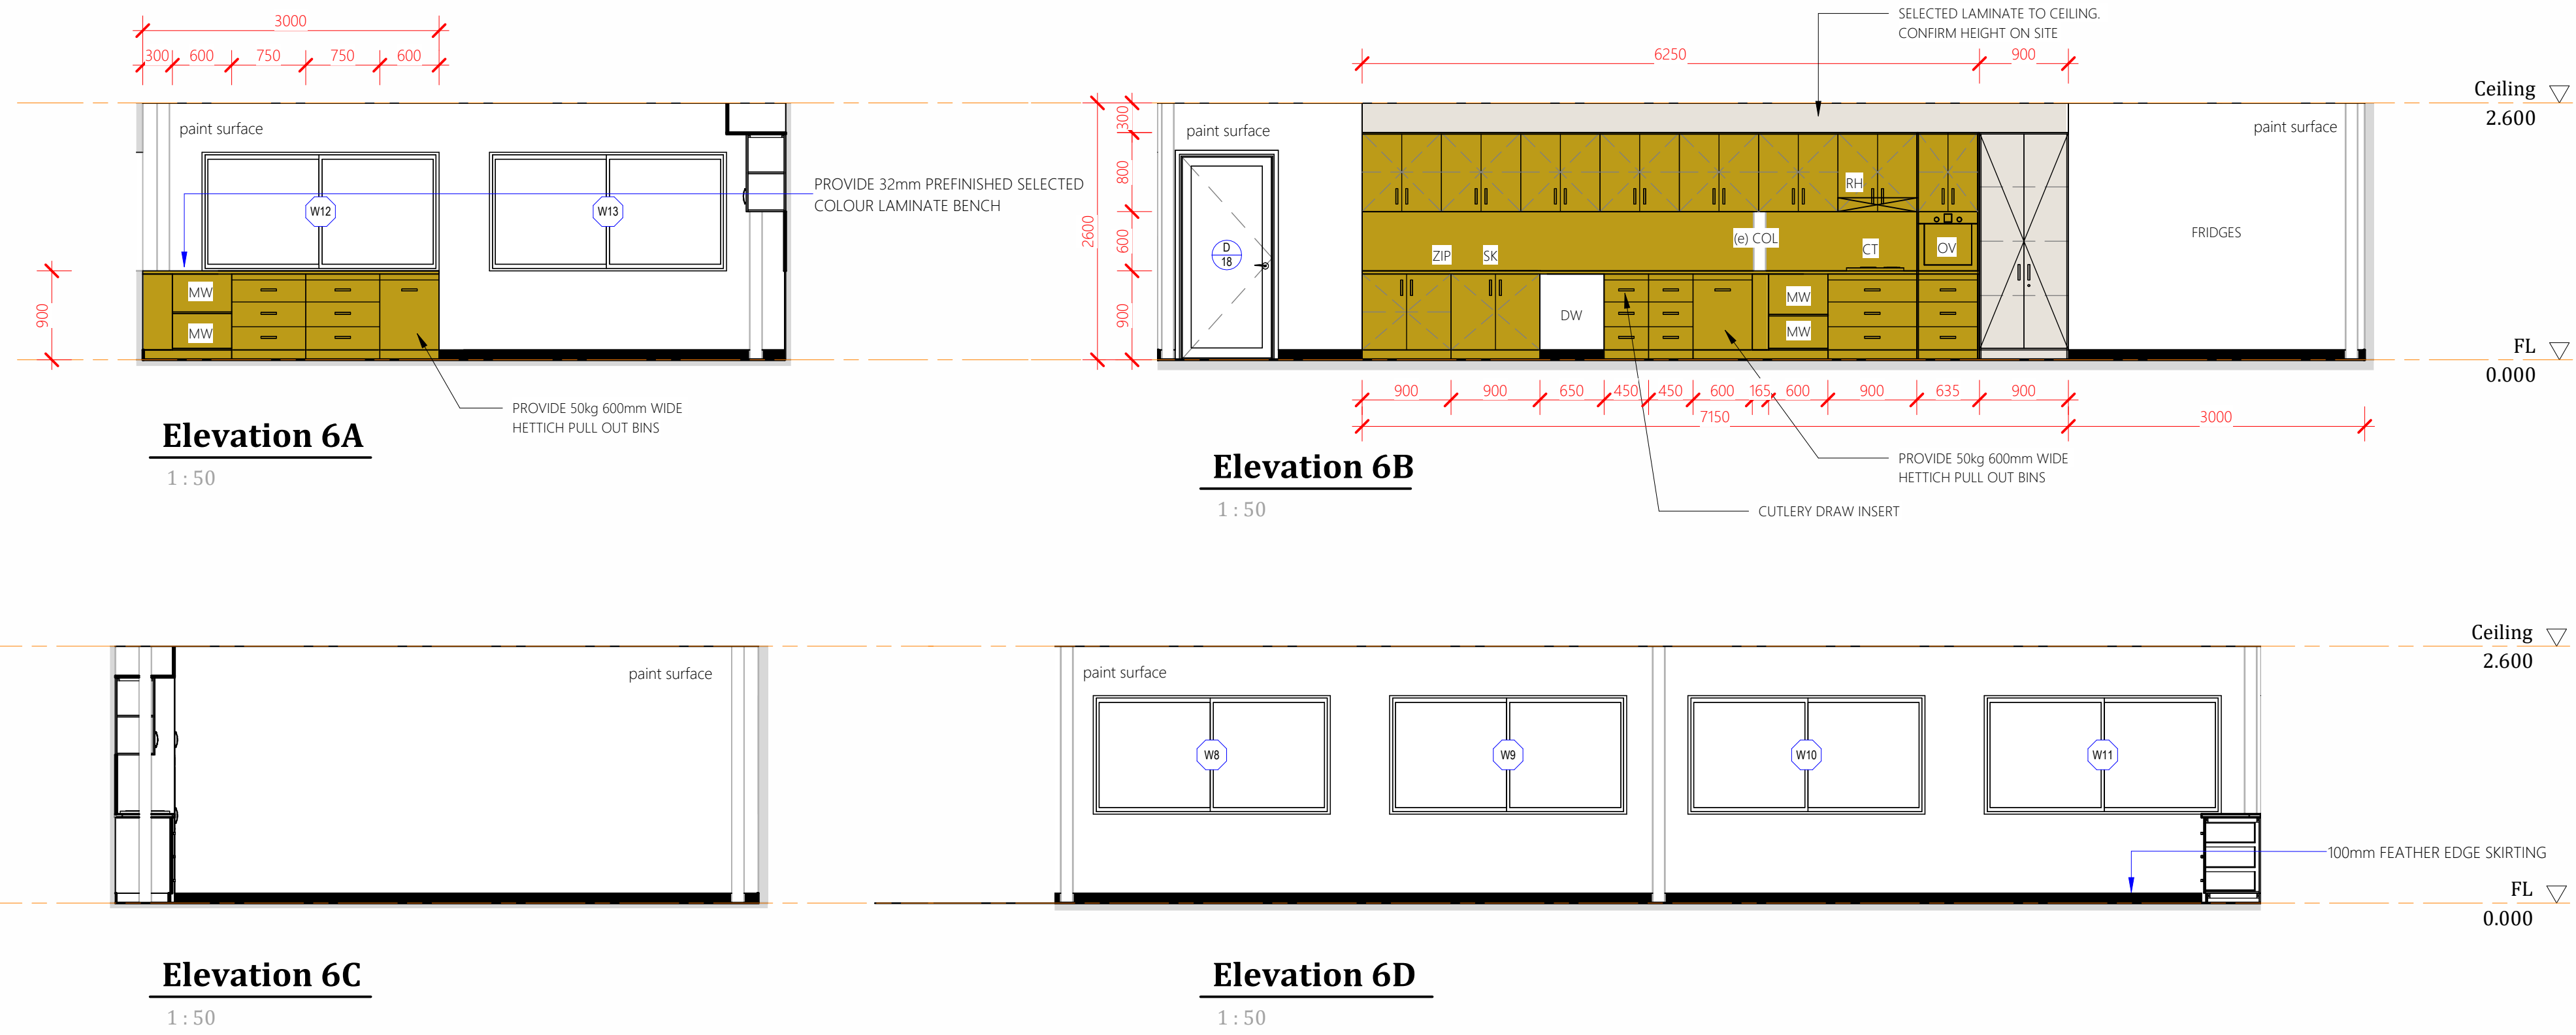

Elevation 6A

1 : 50

Elevation 6B

1 : 50

Elevation 6C

1 : 50

Elevation 6D

1 : 50

REVISIONS

Rev	Description	Date
T1	TENDER ISSUE	12.03.2026

DO NOT SCALE THIS DRAWINGS



TENDER ISSUE



Project Details
WAREHOUSE REFURB
Address
STANWELL POWER STATION
Drawing Title
INTERNAL ELEVATIONS 6 - LUNCH ROOM



0483 988 655 **M**
info@designelements.com.au **E**

QBCC No: 1247120 BDAQ No: 0001677

Scale: 1 : 50 Rev:


Date: MARCH 2026 **T1**

Drawn: Author


Project No: Drawing No:

25_003 A2-605

13/03/2026 11:28:11 AM

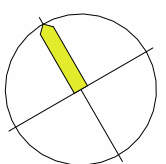


_Door Schedule	
DOOR NO.	Type Mark
1	TYPE A
2	TYPE A
3	TYPE H
4	TYPE D
5	TYPE D
6	TYPE E
7	TYPE E
8	TYPE A
9	TYPE E
10	TYPE G
11	TYPE G
12	TYPE H
13	TYPE H
14	TYPE H
15	TYPE I
16	TYPE E
18	TYPE D
19	TYPE F
20	TYPE F
21	TYPE H
22	TYPE H
23	TYPE H
24	TYPE H
25	TYPE H
26	TYPE H
27	TYPE H
28	TYPE D

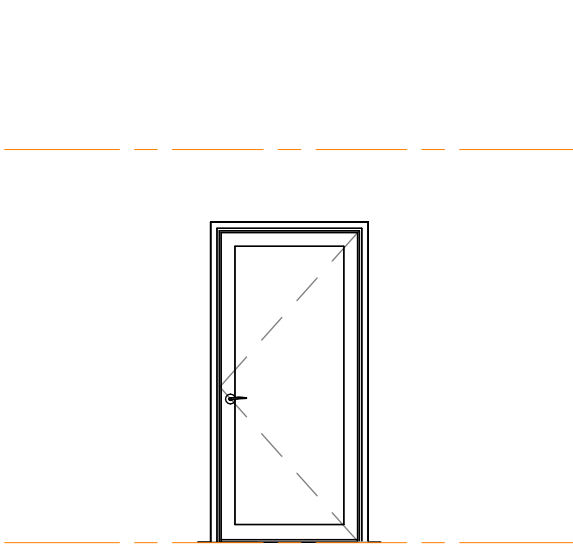


DOOR TYPE A

LOCATION: EXTERNAL
DOOR TYPE: HINGED ALUMINIUM FRAMED SINGLE DOOR
FRAME TYPE: G.JAMES 475 SERIES
FRAME FINISH: SELECTED POWDERCOAT
DOOR FINISH: SELECTED POWDERCOAT
INFILL: GREY SAFETY GLASS
THRESHOLD: REFER HARDWARE SCHEDULE
SEALS: REFER HARDWARE SCHEDULE
LOCK: REFER HARDWARE SCHEDULE
HARDWARE: DOOR CLOSER, DOOR STOP

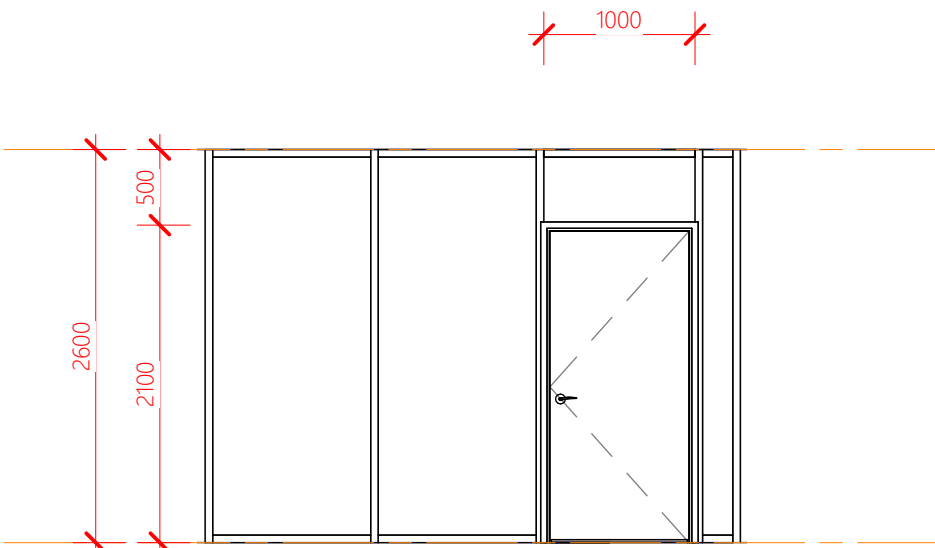


DOOR TYPE B

LOCATION: EXTERNAL
DOOR TYPE: HINGED ALUMINIUM FRAMED SINGLE DOOR
FRAME TYPE: G.JAMES 475 SERIES
FRAME FINISH: SELECTED POWDERCOAT
DOOR FINISH: SELECTED POWDERCOAT
INFILL: GREY SAFETY GLASS
THRESHOLD: REFER HARDWARE SCHEDULE
SEALS: REFER HARDWARE SCHEDULE
LOCK: REFER HARDWARE SCHEDULE
HARDWARE: DOOR CLOSER, DOOR STOP

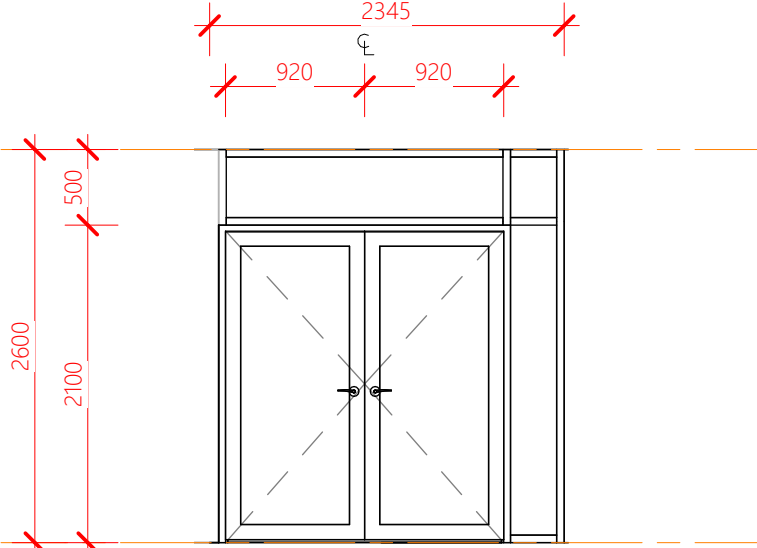


DOOR TYPE C

LOCATION: EXTERNAL
DOOR TYPE: HINGED ALUMINIUM FRAMED SINGLE DOOR
FRAME TYPE: G.JAMES 475 SERIES
FRAME FINISH: SELECTED POWDERCOAT
DOOR FINISH: SELECTED POWDERCOAT
INFILL: GREY SAFETY GLASS
THRESHOLD: REFER HARDWARE SCHEDULE
SEALS: REFER HARDWARE SCHEDULE
LOCK: REFER HARDWARE SCHEDULE
HARDWARE: DOOR CLOSER, DOOR STOP

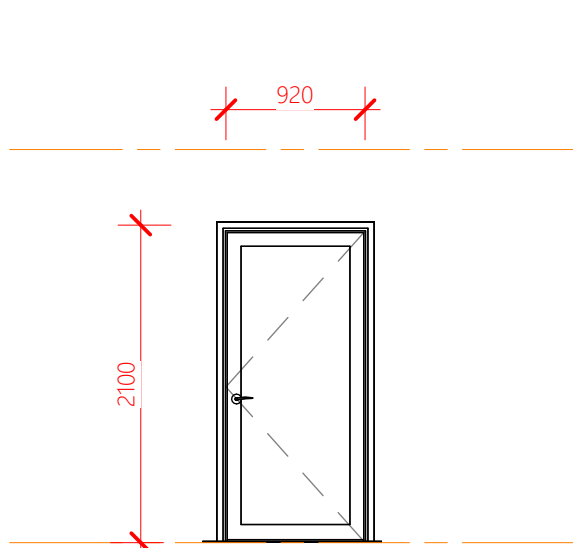


DOOR TYPE D

LOCATION: INTERNAL
DOOR TYPE: HINGED ALUMINIUM FRAMED SINGLE DOOR
FRAME TYPE: G.JAMES 475 SERIES
FRAME FINISH: SELECTED POWDERCOAT
DOOR FINISH: SELECTED POWDERCOAT
INFILL: GREY SAFETY GLASS
SEALS: NONE
LOCK: REFER HARDWARE SCHEDULE
HARDWARE: DOOR CLOSER, DOOR STOP

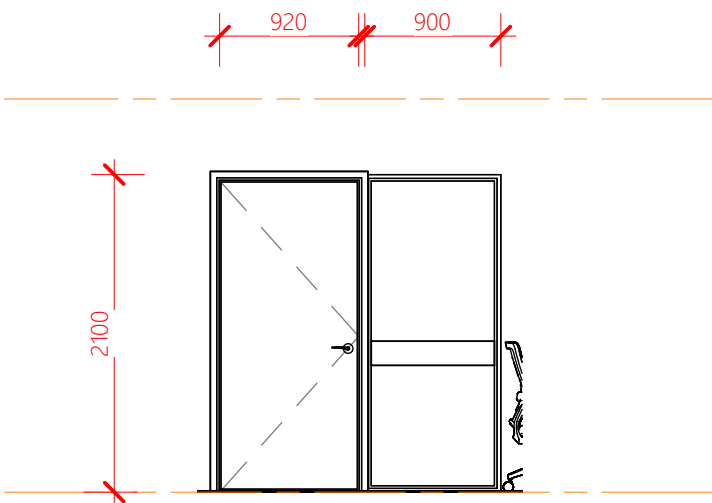


DOOR TYPE E

LOCATION: INTERNAL
DOOR TYPE: HINGED ALUMINIUM FRAMED SINGLE DOOR
FRAME TYPE: G.JAMES 475 SERIES
FRAME FINISH: SELECTED POWDERCOAT
DOOR FINISH: SELECTED POWDERCOAT
INFILL: GREY SAFETY GLASS
THRESHOLD: REFER HARDWARE SCHEDULE
SEALS: REFER HARDWARE SCHEDULE
LOCK: REFER HARDWARE SCHEDULE
HARDWARE: DOOR CLOSER, DOOR STOP

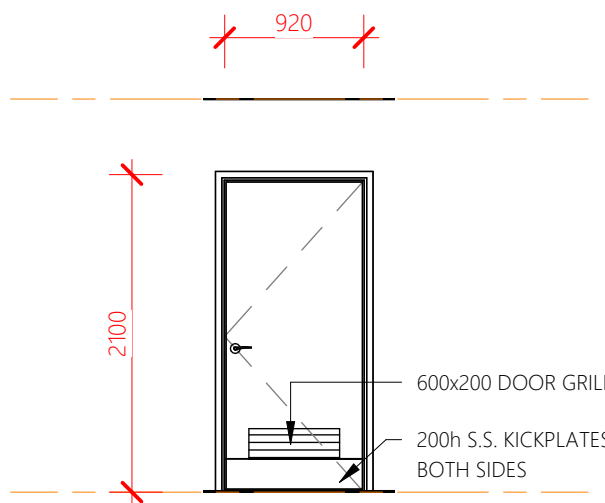


DOOR TYPE F

LOCATION: CLEANER / SERVICE
DOOR TYPE: 40mm HINGED SOLID CORE SINGLE DOOR
FRAME TYPE: TIMBER
FRAME FINISH: PAINT
DOOR FINISH: PAINT
SEALS: NONE
LOCK: REFER HARDWARE SCHEDULE
HARDWARE: KICK PLATES, DOOR CLOSER, DOOR STOP

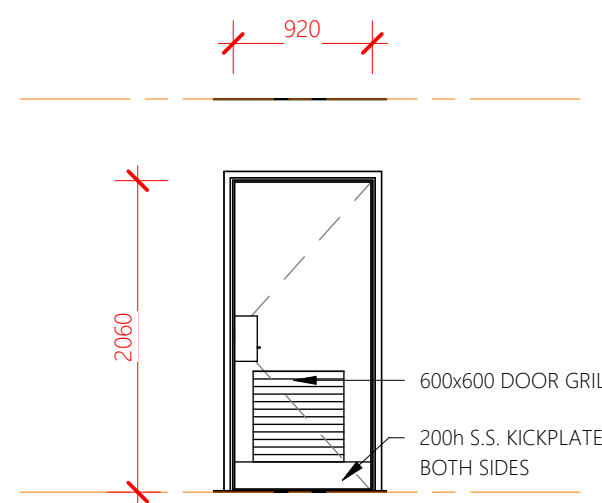


DOOR TYPE G

LOCATION: FEMALE AMENITIES
DOOR TYPE: 40mm HINGED SOLID CORE SINGLE DOOR
FRAME TYPE: TIMBER
FRAME FINISH: PAINT
DOOR FINISH: PAINT
SEALS: NONE
LOCK: PUSH PULL PLATES (NO LOCKING)
HARDWARE: KICK PLATES, DOOR CLOSER, DOOR STOP

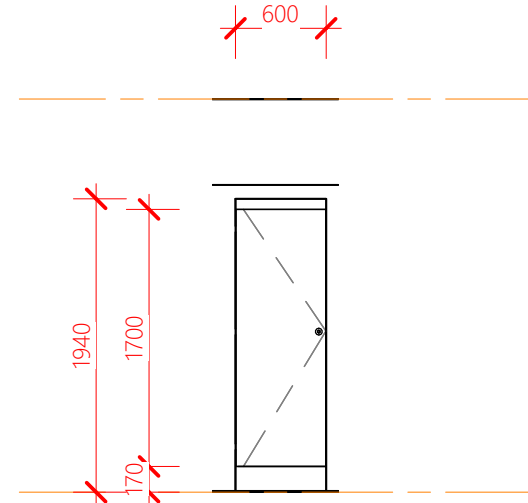


DOOR TYPE H

LOCATION: AMENITIES
DOOR TYPE: 13mm COMPACT LAMINATE PARTITION DOOR
FRAME TYPE: PROVIDE 30° PRIVACY BEVEL
DOOR FINISH: SELECTED LAMINATE
SEALS: NONE
LOCK: METLAM XCEL SLIDE LOCK & INDICATOR.
HARDWARE:

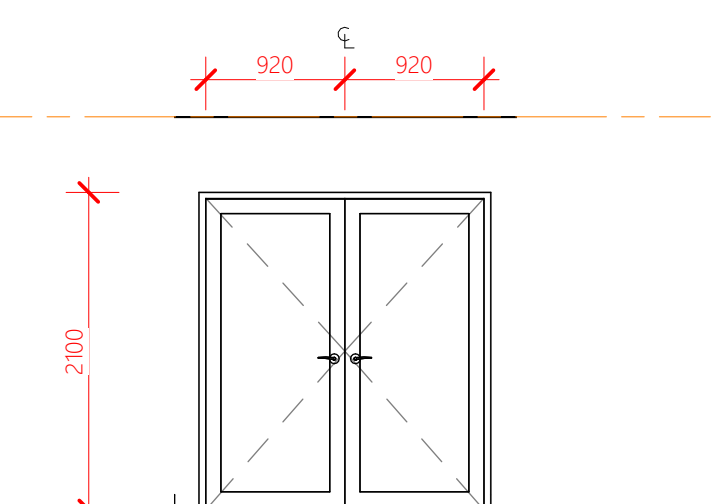

DOOR TYPE I

LOCATION: EXTERNAL
DOOR TYPE: HINGED ALUMINIUM FRAMED SINGLE DOOR
FRAME TYPE: G.JAMES 475 SERIES
FRAME FINISH: SELECTED POWDERCOAT
DOOR FINISH: SELECTED POWDERCOAT
INFILL: GREY SAFETY GLASS
THRESHOLD: REFER HARDWARE SCHEDULE
SEALS: REFER HARDWARE SCHEDULE
LOCK: REFER HARDWARE SCHEDULE
HARDWARE: DOOR CLOSER, DOOR STOP

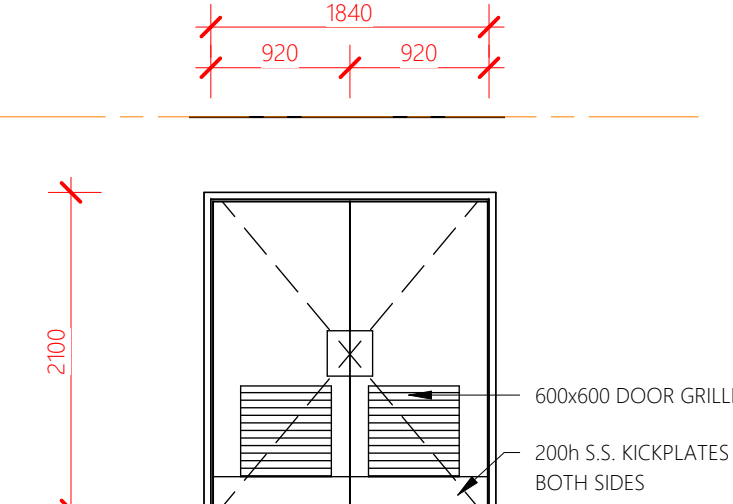


DOOR TYPE J

LOCATION: MALE AMENITIES
DOOR TYPE: 40mm HINGED DOULD CORE SINGLE DOOR
FRAME TYPE: TIMBER
FRAME FINISH: PAINT
DOOR FINISH: PAINT
SEALS: NONE
LOCK: PUSH PULL PLATES (NO LOCKING)
HARDWARE: KICK PLATES, DOOR CLOSER, DOOR STOP

CONFIRM EXISTING OPENING SIZE ON SITE AND ADVISE

REVISIONS		
Rev	Description	Date
T1	TENDER ISSUE	12.03.2026

DO NOT SCALE THIS DRAWINGS

 

TENDER ISSUE

Client



Project Details

WAREHOUSE REFURB

Address

STANWELL POWER STATION

Drawing Title

DOOR SCHEDULE



0483 988 655 
info@designelements.com.au 
QBCC No: 1247120 BDAQ No: 0001677

Scale: 1 : 50

Date: MARCH 2026


Drawn: Author

Rev: T1

Drawing No: A2-700


Project No: 25_003

_Window Schedule	
WINDOW NO.	Type Mark
1	TYPE A
2	TYPE A
3	TYPE B
4	TYPE C
5	TYPE D
6	TYPE E
7	TYPE E
8	TYPE F
9	TYPE F
10	TYPE F
11	TYPE F
12	TYPE F
13	TYPE F
14	TYPE G
15	TYPE H
16	TYPE I
17	TYPE J
18	TYPE J
19	

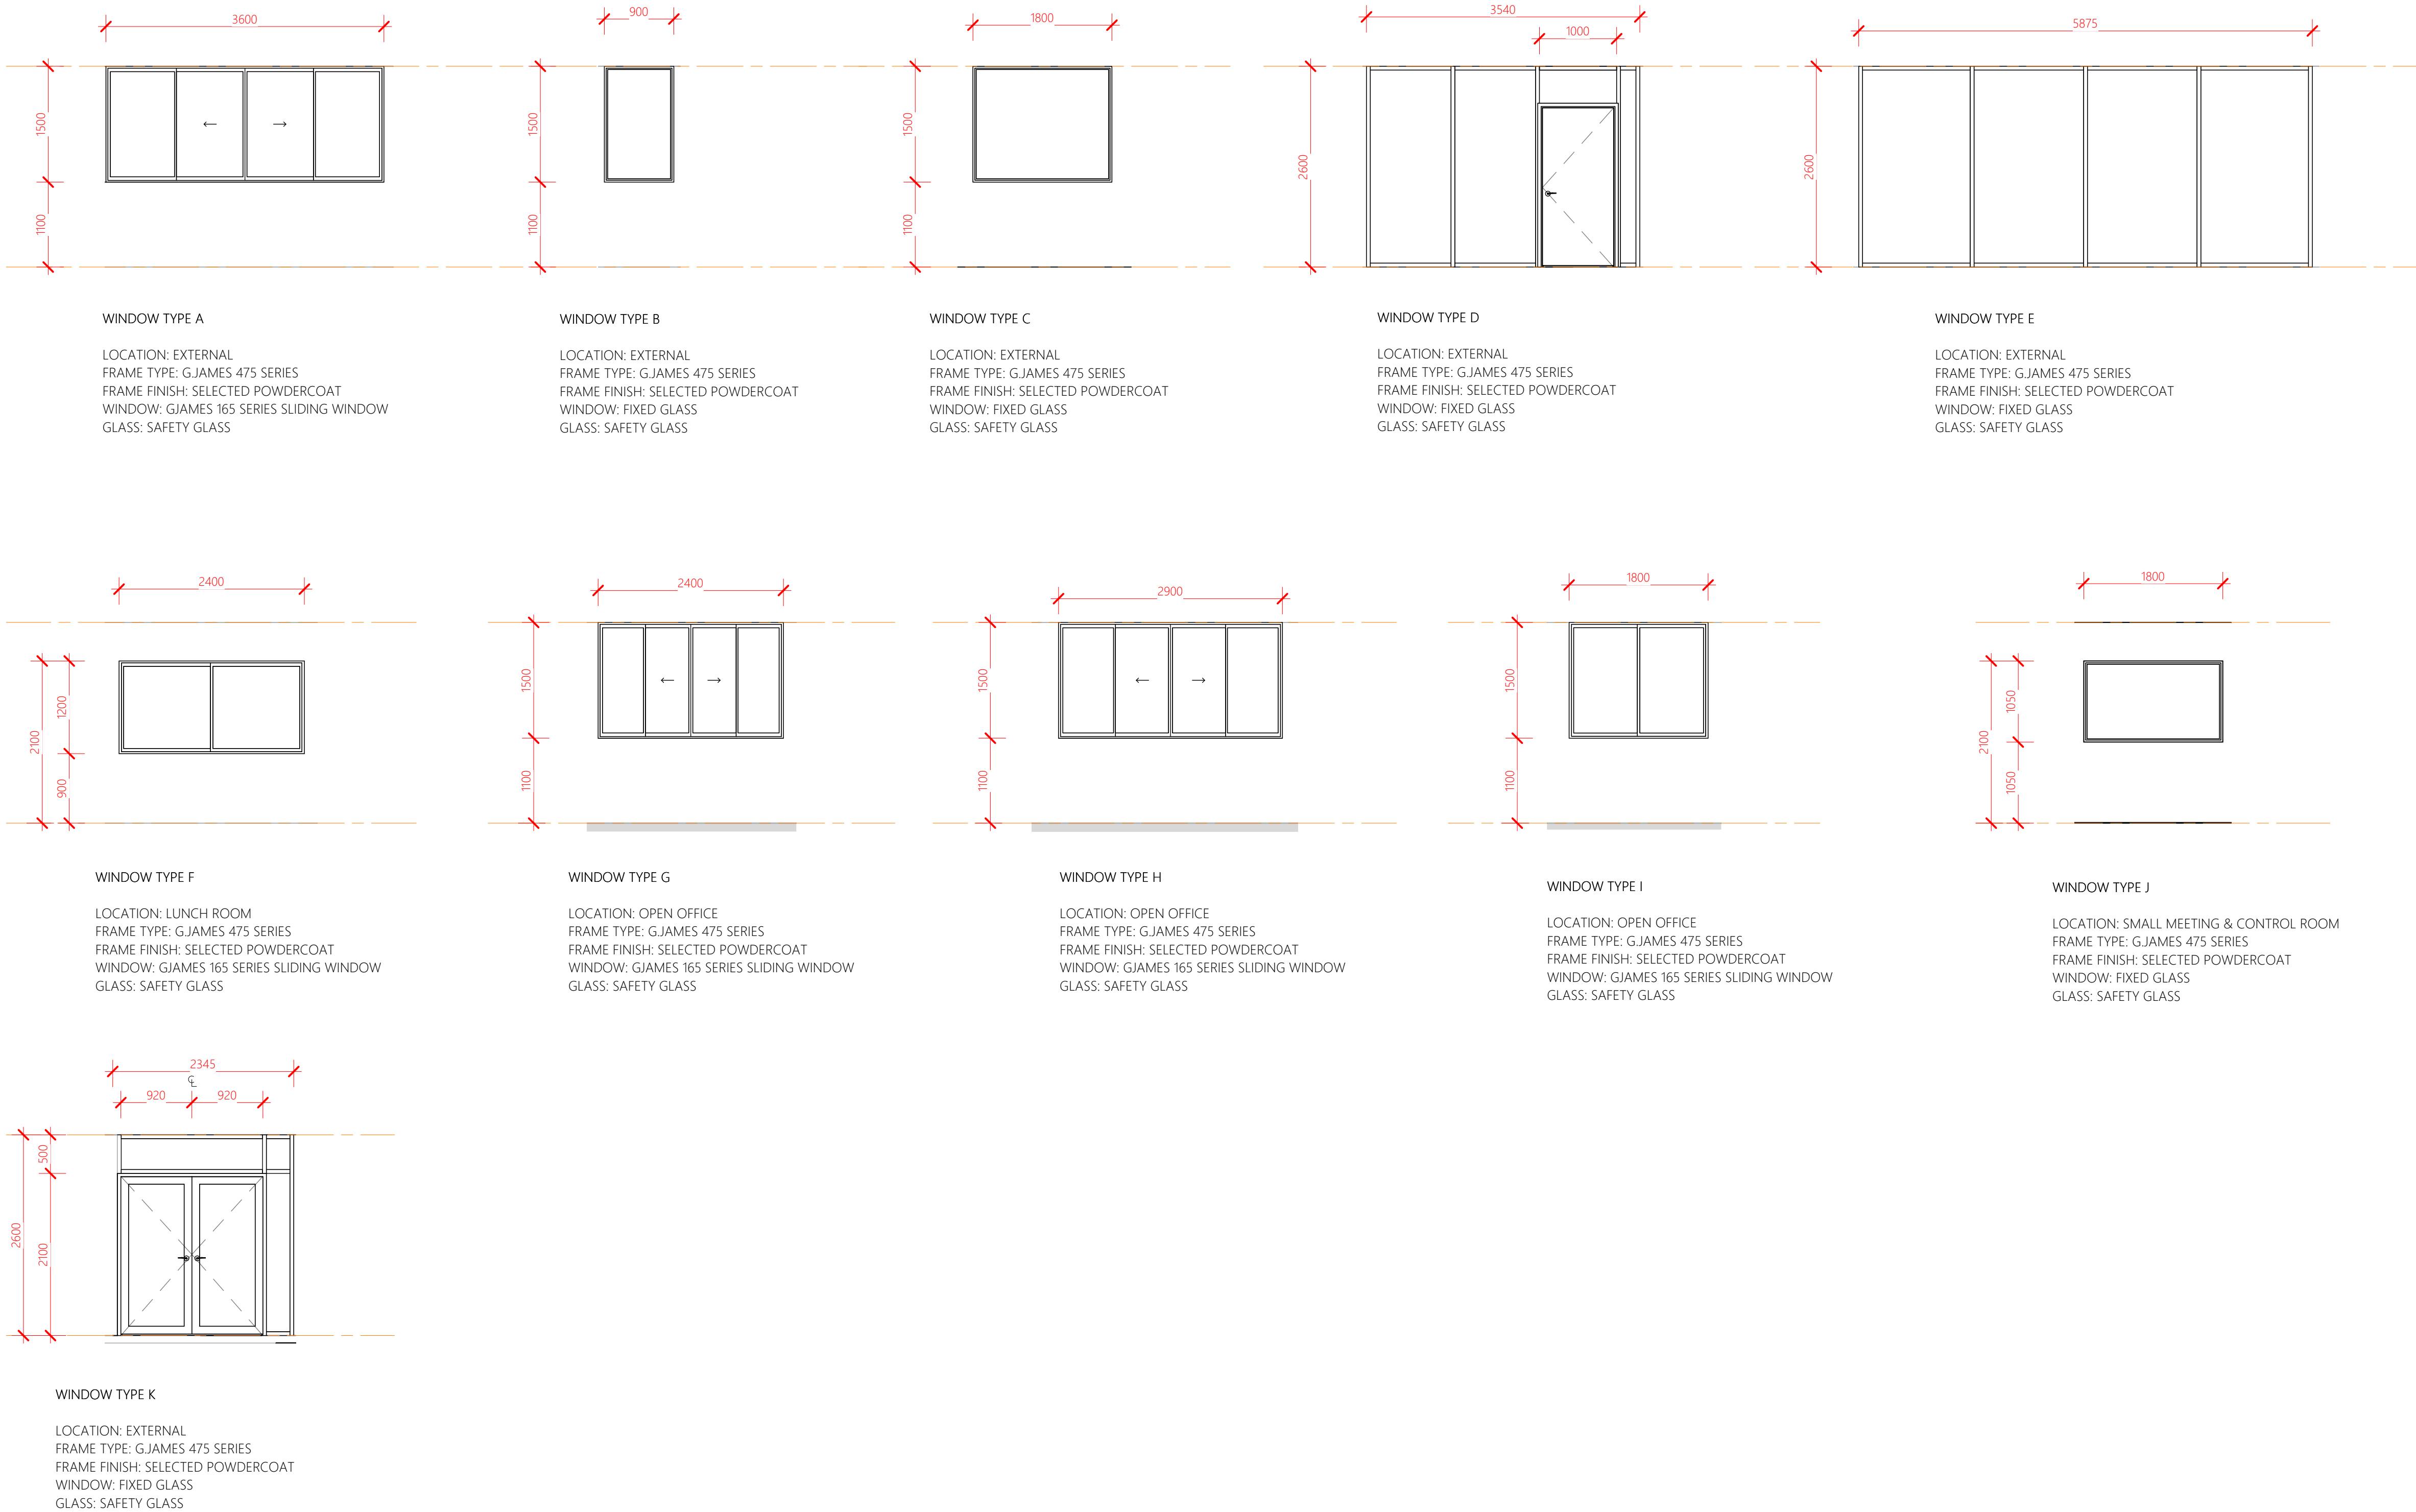

REVISIONS		
Rev	Description	Date
T1	TENDER ISSUE	12.03.2026

DO NOT SCALE THIS DRAWINGS

 

TENDER ISSUE

Client



Project Details

WAREHOUSE REFURB

Address

STANWELL POWER STATION

Drawing Title

WINDOW SCHEDULE



0483 988 655

info@designelements.com.au

QBCC No: 1247120

BDAQ No: 0001677

Scale: 1 : 50

Date: MARCH 2026

Drawn: Author

Rev: T1

Project No: 25_003

Drawing No: A2-701