


**REFER TO SITE PLAN & CONSULTANT
DRAWINGS FOR EXTERNAL SERVICES**

REVISIONS		
Rev	Description	Date
T1	TENDER ISSUE	12.03.2026

DO NOT SCALE THIS DRAWINGS

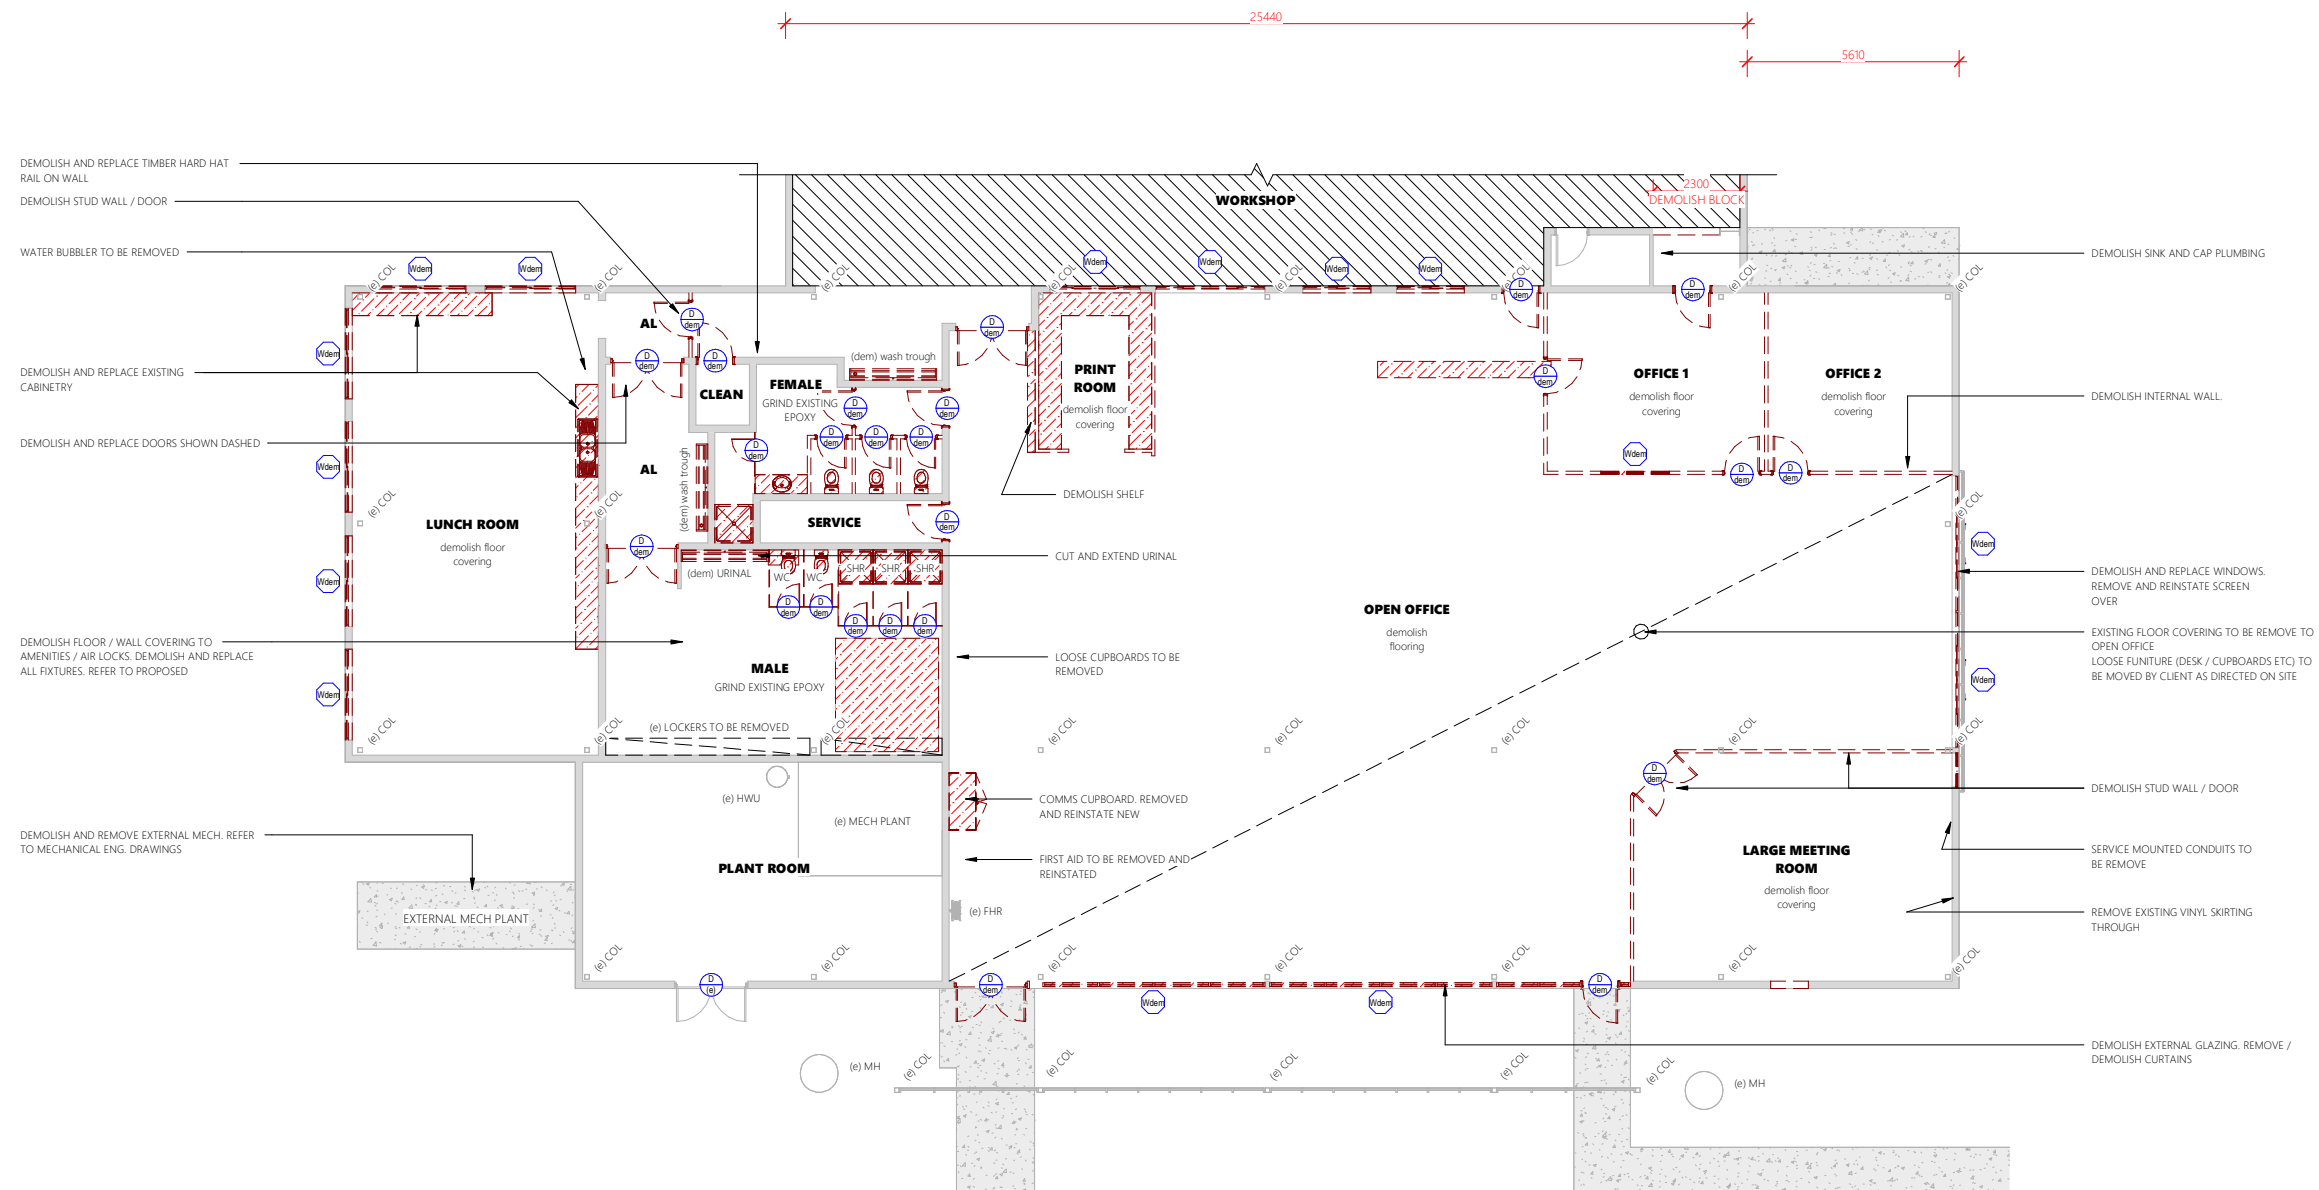

Existing Main Workshop Floor Plan

1 : 100

0 5m 1:100

TENDER ISSUE

Client



stanwell

Project Details	WAREHOUSE REFURB
Address	STANWELL POWER STATION
Drawing Title	EXISTING FLOOR PLAN

 **dezi nelements**
BUILDING DESIGNERS
0483 988 655 **M**
info@dezi nelements.com.au **E**
QBCC No: 1247120 BDAQ No: 0001677

Scale: 1:100	Rev:
Date: MARCH 2026	T1
Drawn: NJB	
Project No:	Drawing No:
25 003	A2-200



REFER TO SITE PLAN & CONSULTANT
DRAWINGS FOR EXTERNAL SERVICES

REVISIONS		
Rev	Description	Date
T1	TENDER ISSUE	12.03.2026

DO NOT SCALE THIS DRAWINGS

TENDER ISSUE

Client



Project Details

WAREHOUSE REFURB

Address

STANWELL POWER STATION

Drawing Title


EXISTING SLAB PLAN


BUILDING DESIGNERS
0483 988 655 M
info@dezi elements.com.au E
QBCC No: 1247120 BDAQ No: 0001677

Scale: 1 : 100
Date: MARCH 2026
Drawn: Author

Rev: T1
Project No: 25_003
Drawing No: A2-201

13/03/2026 11:25:09 AM

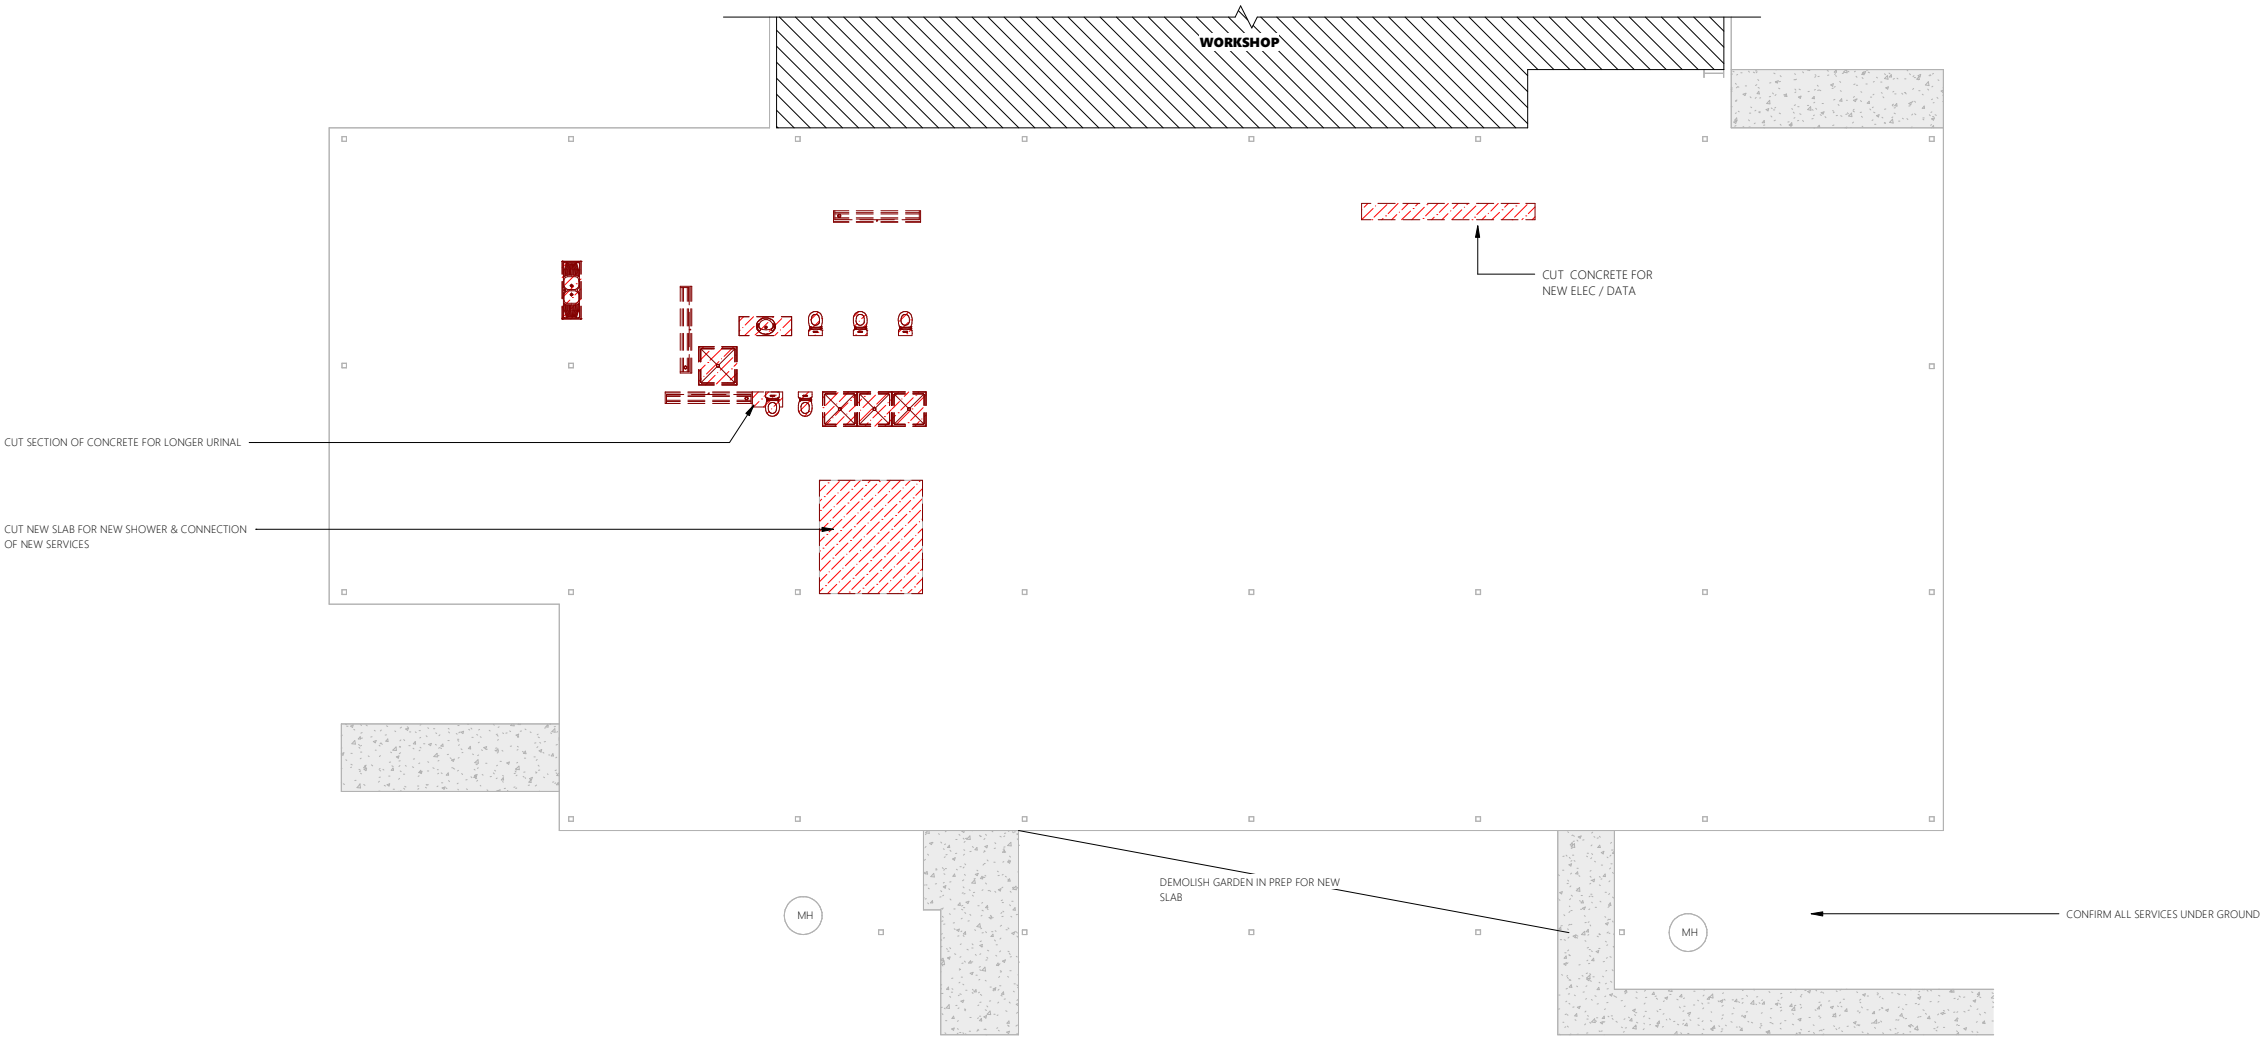

Existing Slab Plan



LIGHTS AND AC FIXTURES SHOWN FOR INDICATION ONLY. CONFIRM ON SITE AND READ IN CONJUNCTION WITH CONSULTANT DRAWINGS

REVISIONS		
Rev	Description	Date
T1	TENDER ISSUE	12.03.2026

DO NOT SCALE THIS DRAWINGS



Existing Ceiling Plan



TENDER ISSUE

Client

Project Details

WAREHOUSE REFURB

Address

STANWELL POWER STATION

Drawing Title

EXISTING CEILING PLAN

BUILDING DESIGNERS

0483 988 655 M

info@dezinements.com.au E

QBCC No: 1247120 BDAQ No: 0001677

Scale: 1 : 100

Date: MARCH 2026

Drawn: Author

Project No: 25_003

Drawing No: A2-202

Rev: T1

13/03/2026 11:25:10 AM



REVISIONS		
Rev	Description	Date
T1	TENDER ISSUE	12.03.2026

DO NOT SCALE THIS DRAWINGS

TENDER ISSUE

Client



Project Details

WAREHOUSE REFURB

Address

STANWELL POWER STATION

Drawing Title


EXISTING ROOF PLAN



0483 988 655 
info@dezi elements.com.au 
QBCC No: 1247120 BDAQ No: 0001677

Scale: 1 : 100 Rev: **T1**
Date: MARCH 2026
Drawn: Author
Project No: Drawing No:
25_003 A2-203

13/03/2026 11:25:10 AM

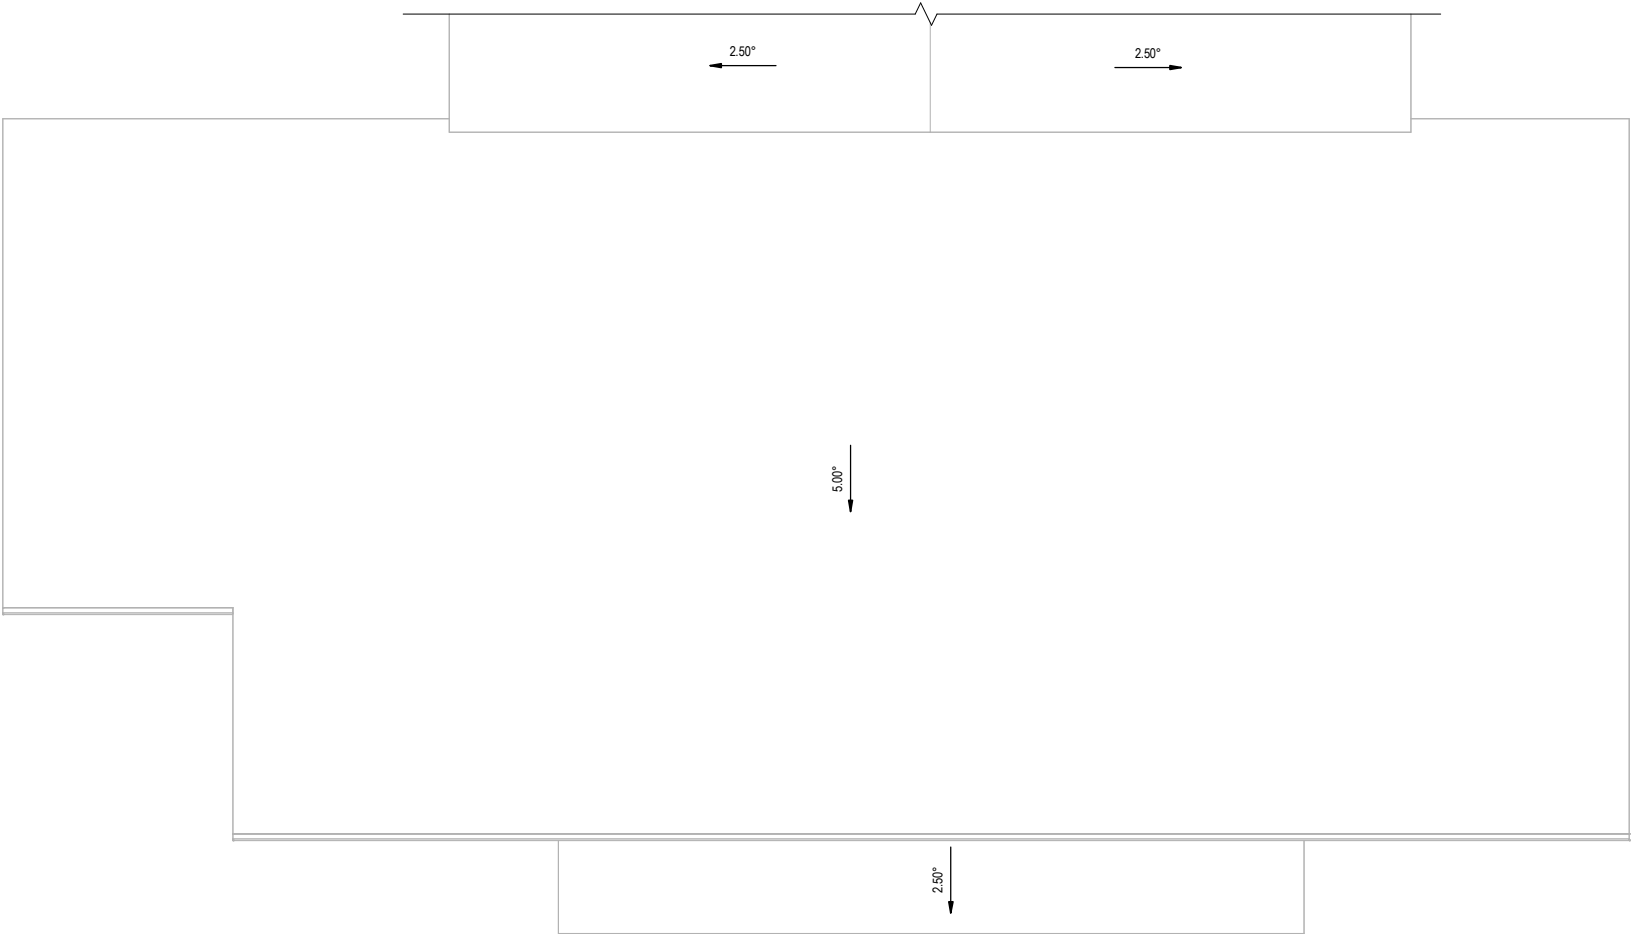


Existing Roof Plan




REVISIONS		
Rev	Description	Date
T1	TENDER ISSUE	12.03.2026

DO NOT SCALE THIS DRAWINGS

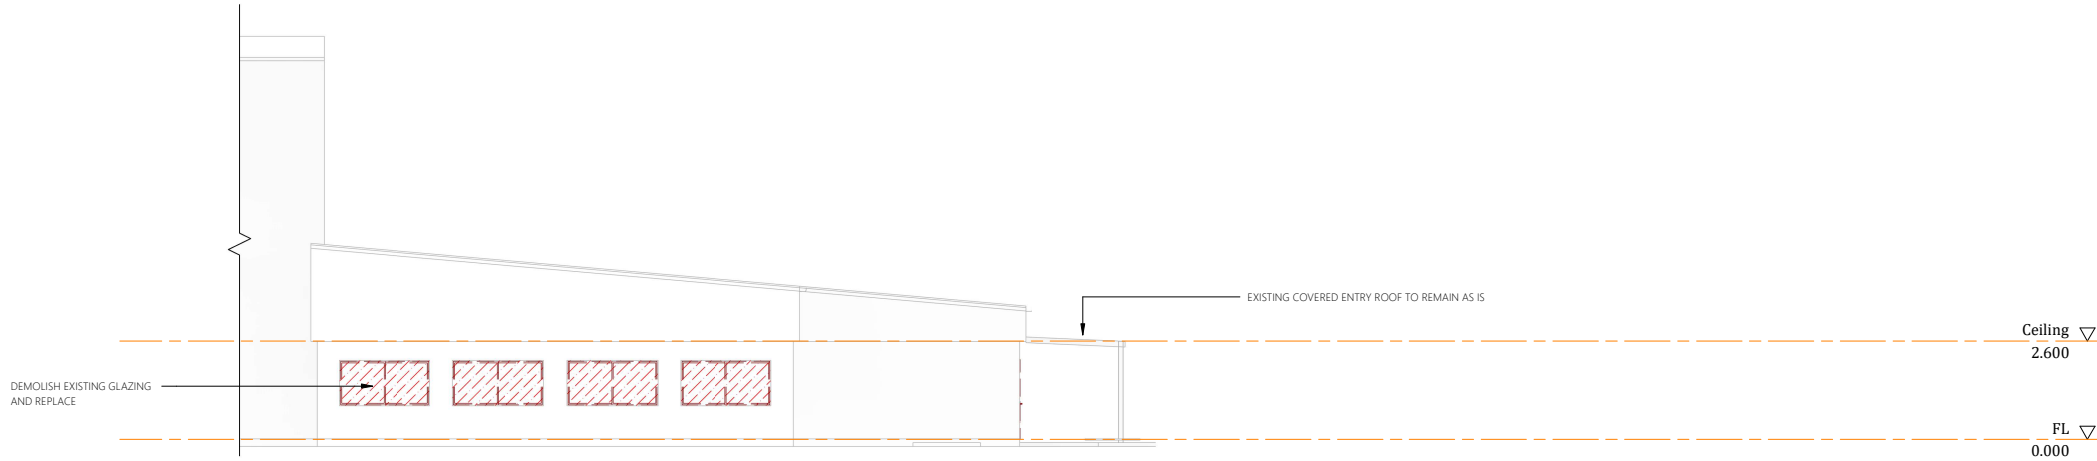


Existing Elevation 1

1 : 100

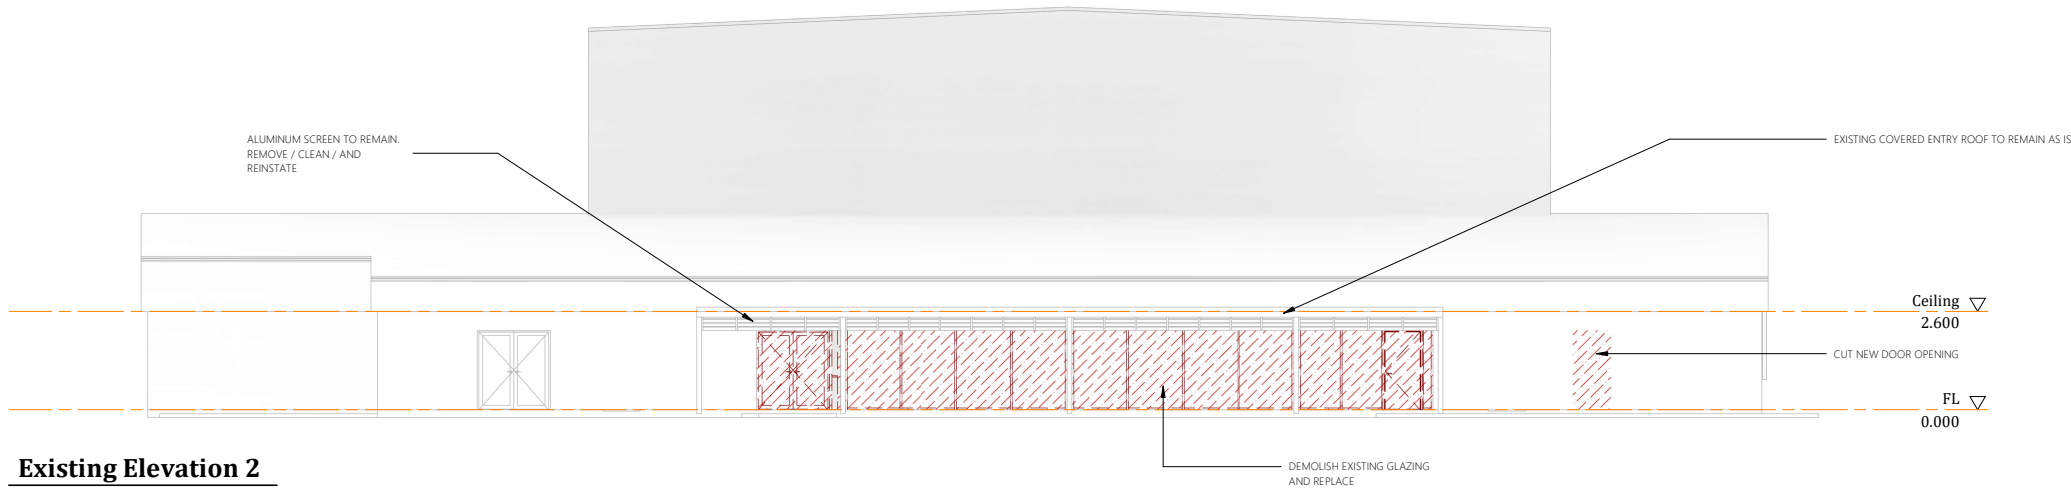

Existing Elevation 2

1 : 100

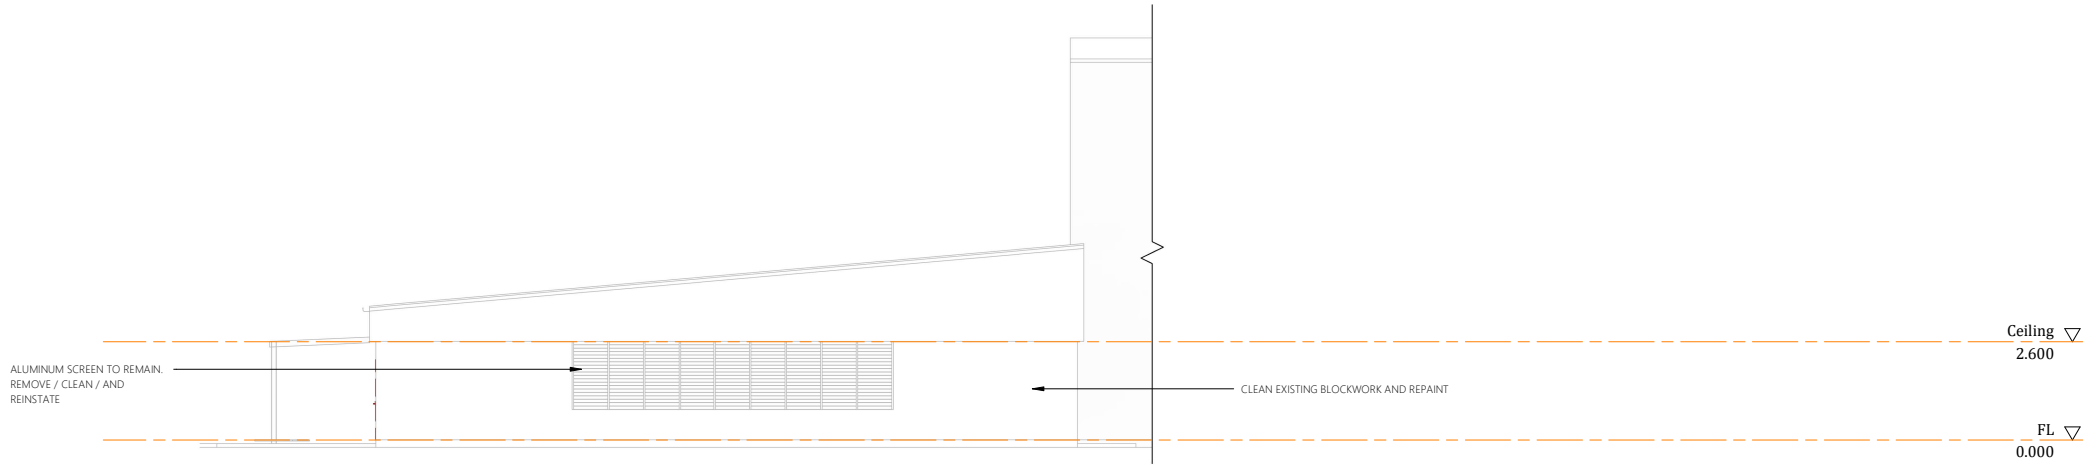

Existing Elevation 3

1 : 100

TENDER ISSUE



Project Details
WAREHOUSE REFURB
Address
STANWELL POWER STATION
Drawing Title
EXISTING ELEVATIONS




0483 988 655 M
info@dezi elements.com.au E
QBCC No: 1247120 BDAQ No: 0001677

Scale: 1 : 100	Rev: T1
Date: MARCH 2026	
Drawn: Author	
Project No: 25_003	Drawing No: A2-204

13/03/2026 11:25:13 AM

_Proposed Main Workshop Floor Plan

1 : 100

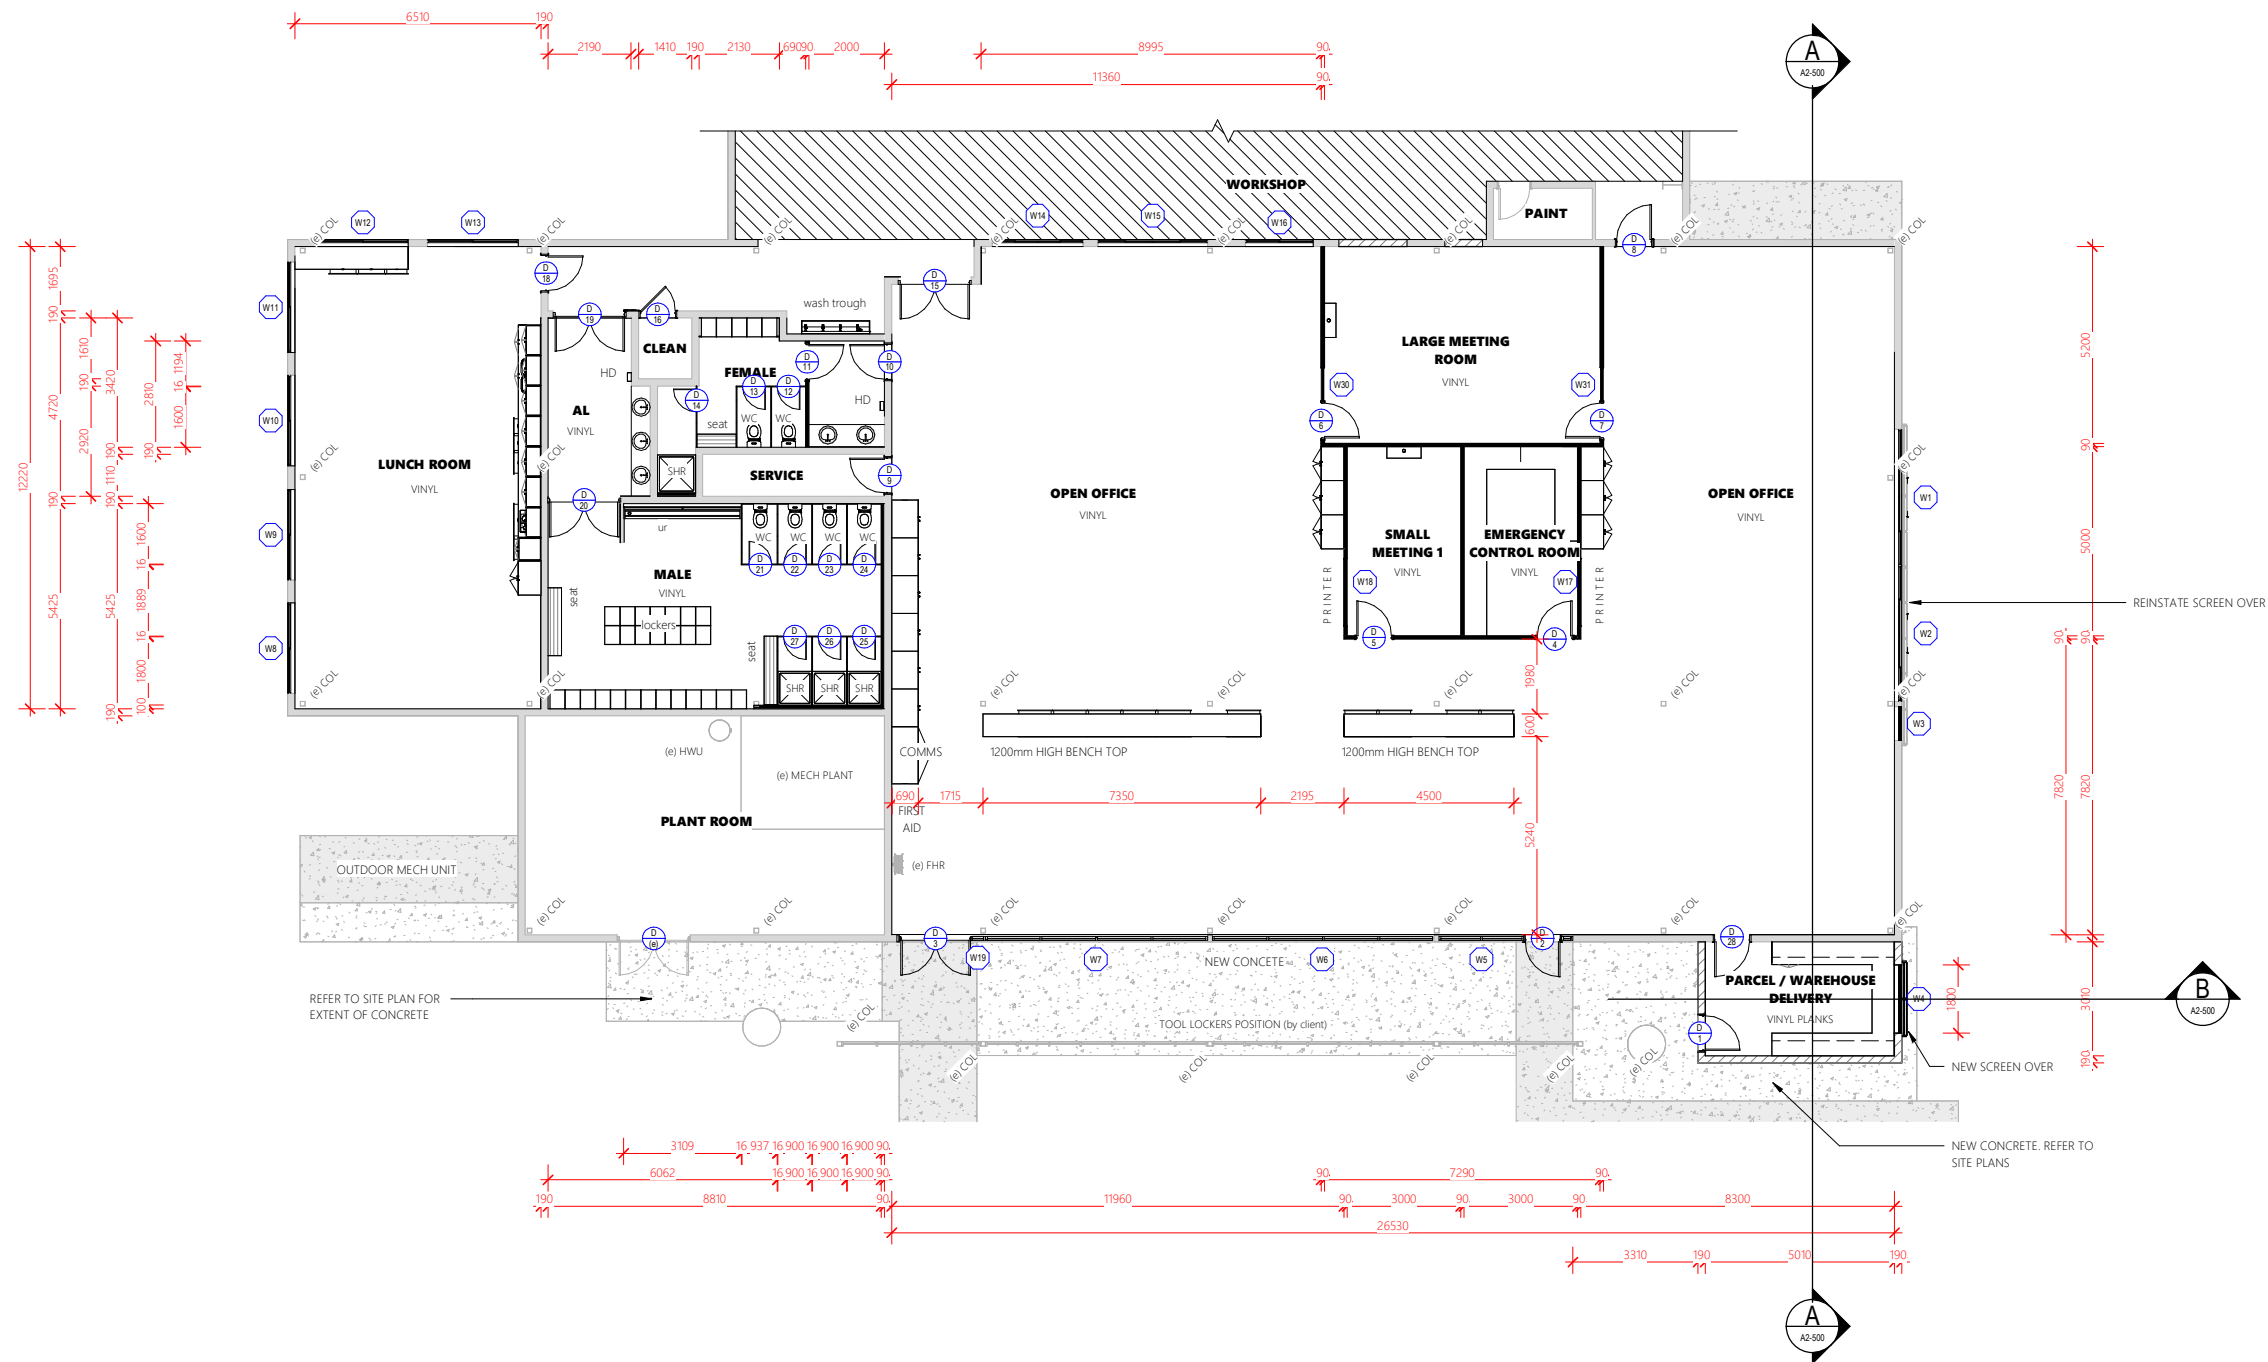

REVISIONS		
Rev	Description	Date
T1	TENDER ISSUE	12.03.2026

DO NOT SCALE THIS DRAWINGS

KEYNOTE LEGEND

(e) Existing
dem Demolish
(R) Remove / Reinstate

BSN Basin
COL Column
CON Condenser
CPD Cupboard
CS Cleaners Sink
CT Cooktop
DP Downpipe
DW Dish Washer
FAP Fire Alarm Panel
FHR Fire Hose Reel
FR Fridge (By Client)
L Locker
HD Hand Driver (Air Blade)
OV Oven
RH Range Hood
DW Dish Washer
SK Sink
SB Switch Board
UR Urinal

TENDER ISSUE



Project Details	
WAREHOUSE REFURB	
Address	
STANWELL POWER STATION	
Drawing Title	
PROPOSED FLOOR PLAN	

dezinelements
BUILDING DESIGNERS
0483 988 655 M
info@dezi

QBCC No: 1247120 BDAQ No: 0001677

Scale: 1 : 100 Rev:

Date: MARCH 2026 T1

Drawn: Author

Project No: Drawing No:

25_003 A2-300




CONFIRM LOCATION OF UNDERGROUND SERVICES
PRIOR TO CUTTING OR EXCAVATION.


REFER TO CONSULTANT DRAWINGS

REVISIONS		
Rev	Description	Date
T1	TENDER ISSUE	12.03.2026

DO NOT SCALE THIS DRAWINGS

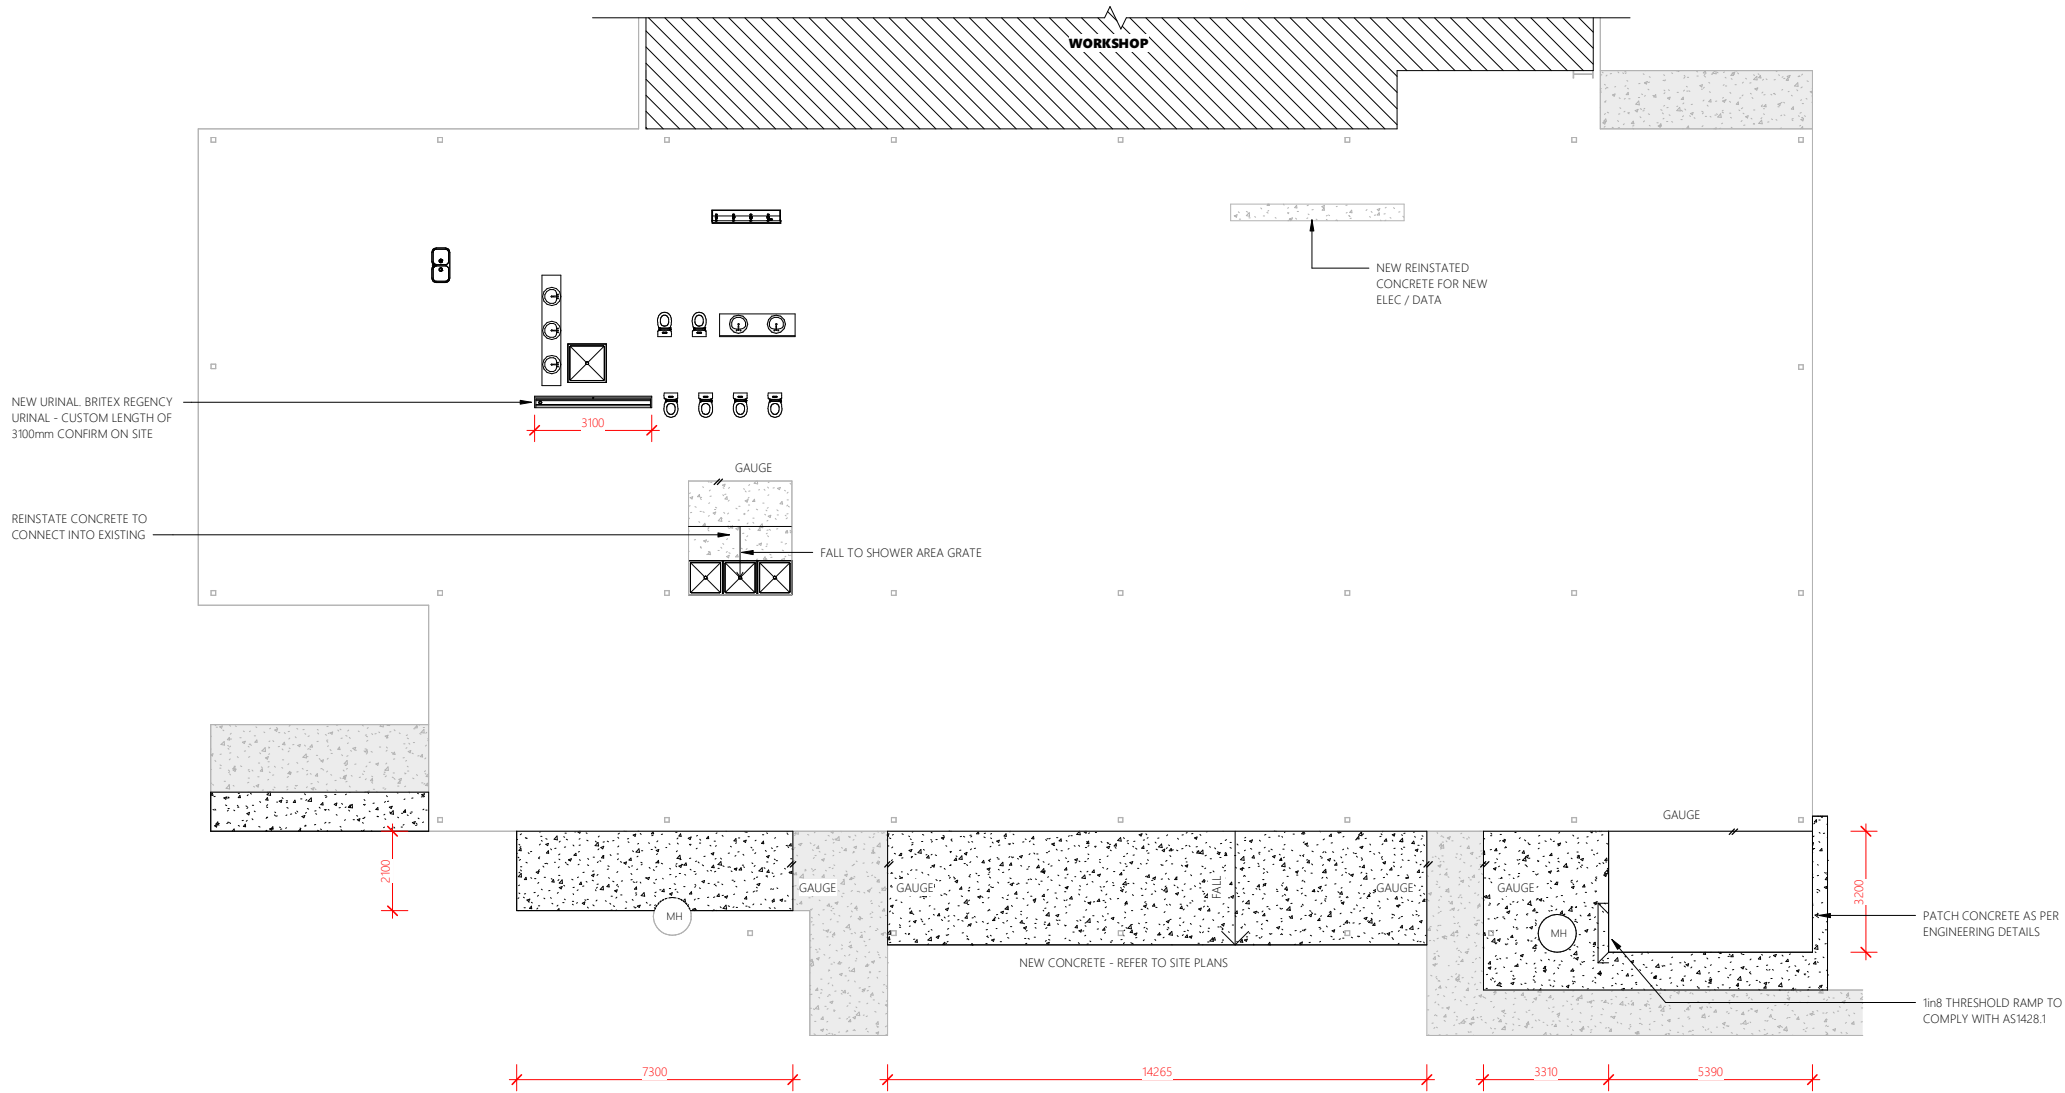

Proposed Slab Plan

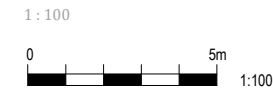

TENDER ISSUE

Client

stanwell

Project Details

WAREHOUSE REFURB

Address

STANWELL POWER STATION

Drawing Title

PROPOSED SLAB PLAN

designelements
BUILDING DESIGNERS

0483 988 655 M
info@designelements.com.au E

QBCC No: 1247120 BDAQ No: 0001677

Scale: 1 : 100 Rev: T1
Date: MARCH 2026
Drawn: Author

Project No: 25_003 Drawing No: A2-301


13/03/2026 11:25:16 AM



CONFIRM EXISTING GRID SETOUT ON SITE

NEW CEILING INSULATION THROUGHOUT
SHADED AREA - REFER SPEC

- CEILING LEGEND
- 1200 x 600 APEX ACOUSTIC CEILING TILES (OR APPROVED EQUAL NEW TILES THROUGH RENOVATED AREA)
 - PROVIDE CONCEALED FIX RIBBEDTRIMDEK SOFFIT SHEETING (TO MATCH EXISTING)
 - INSULATION ABOVE CEILING TILES

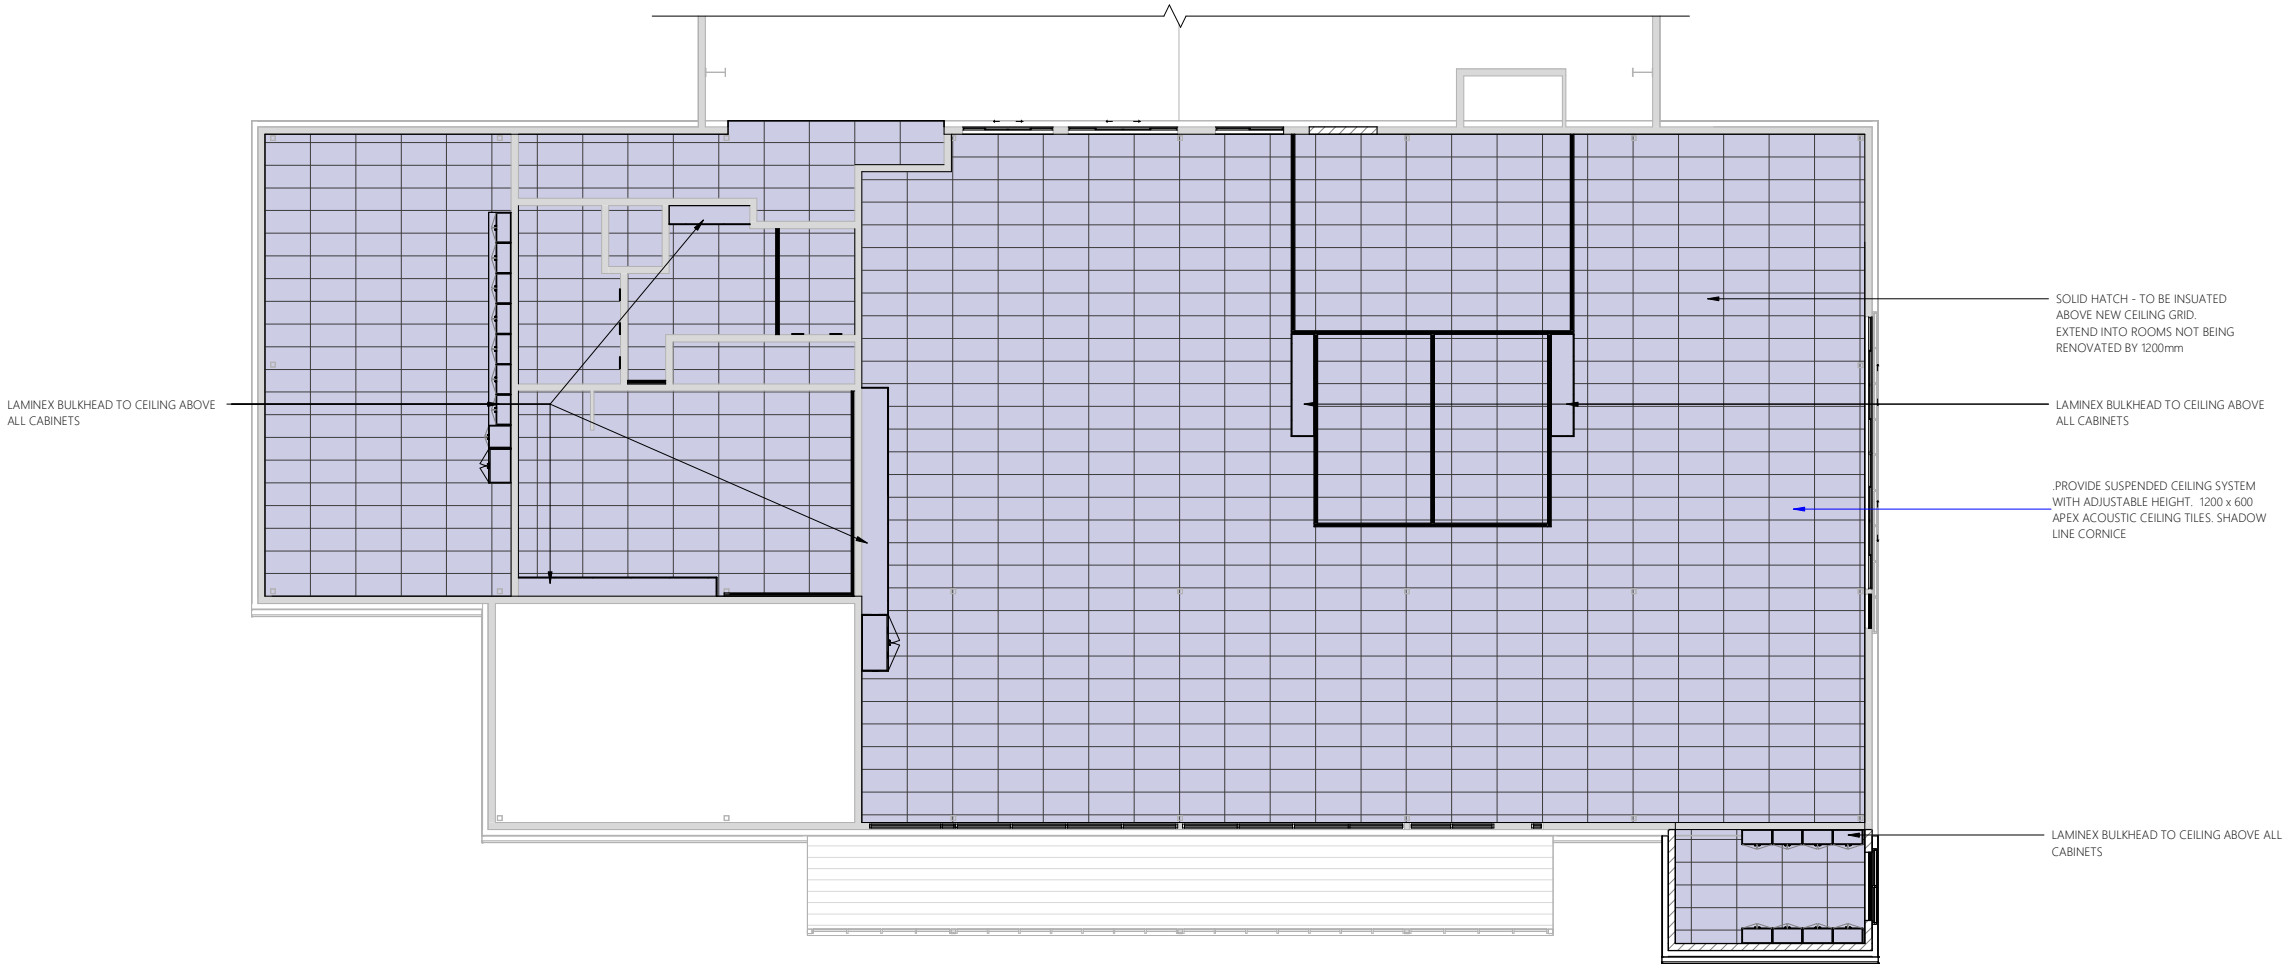

Proposed Ceiling Plan

1 : 100



REVISIONS

Rev	Description	Date
T1	TENDER ISSUE	12.03.2026

DO NOT SCALE THIS DRAWINGS

TENDER ISSUE

Client

 stanwell

Project Details

WAREHOUSE REFURB

Address

STANWELL POWER STATION

Drawing Title

PROPOSED CEILING PLAN

 **dezignelements**
BUILDING DESIGNERS

0483 988 655 M
info@dezignelements.com.au E

QBCC No: 1247120 BDAQ No: 0001677


Scale: 1 : 100 Rev: T1
Date: MARCH 2026
Drawn: Author
Project No: 25_003 Drawing No: A2-302



CONFIRM EXISTING ROOF PITCH ON SITE

REVISIONS		
Rev	Description	Date
T1	TENDER ISSUE	12.03.2026

DO NOT SCALE THIS DRAWINGS

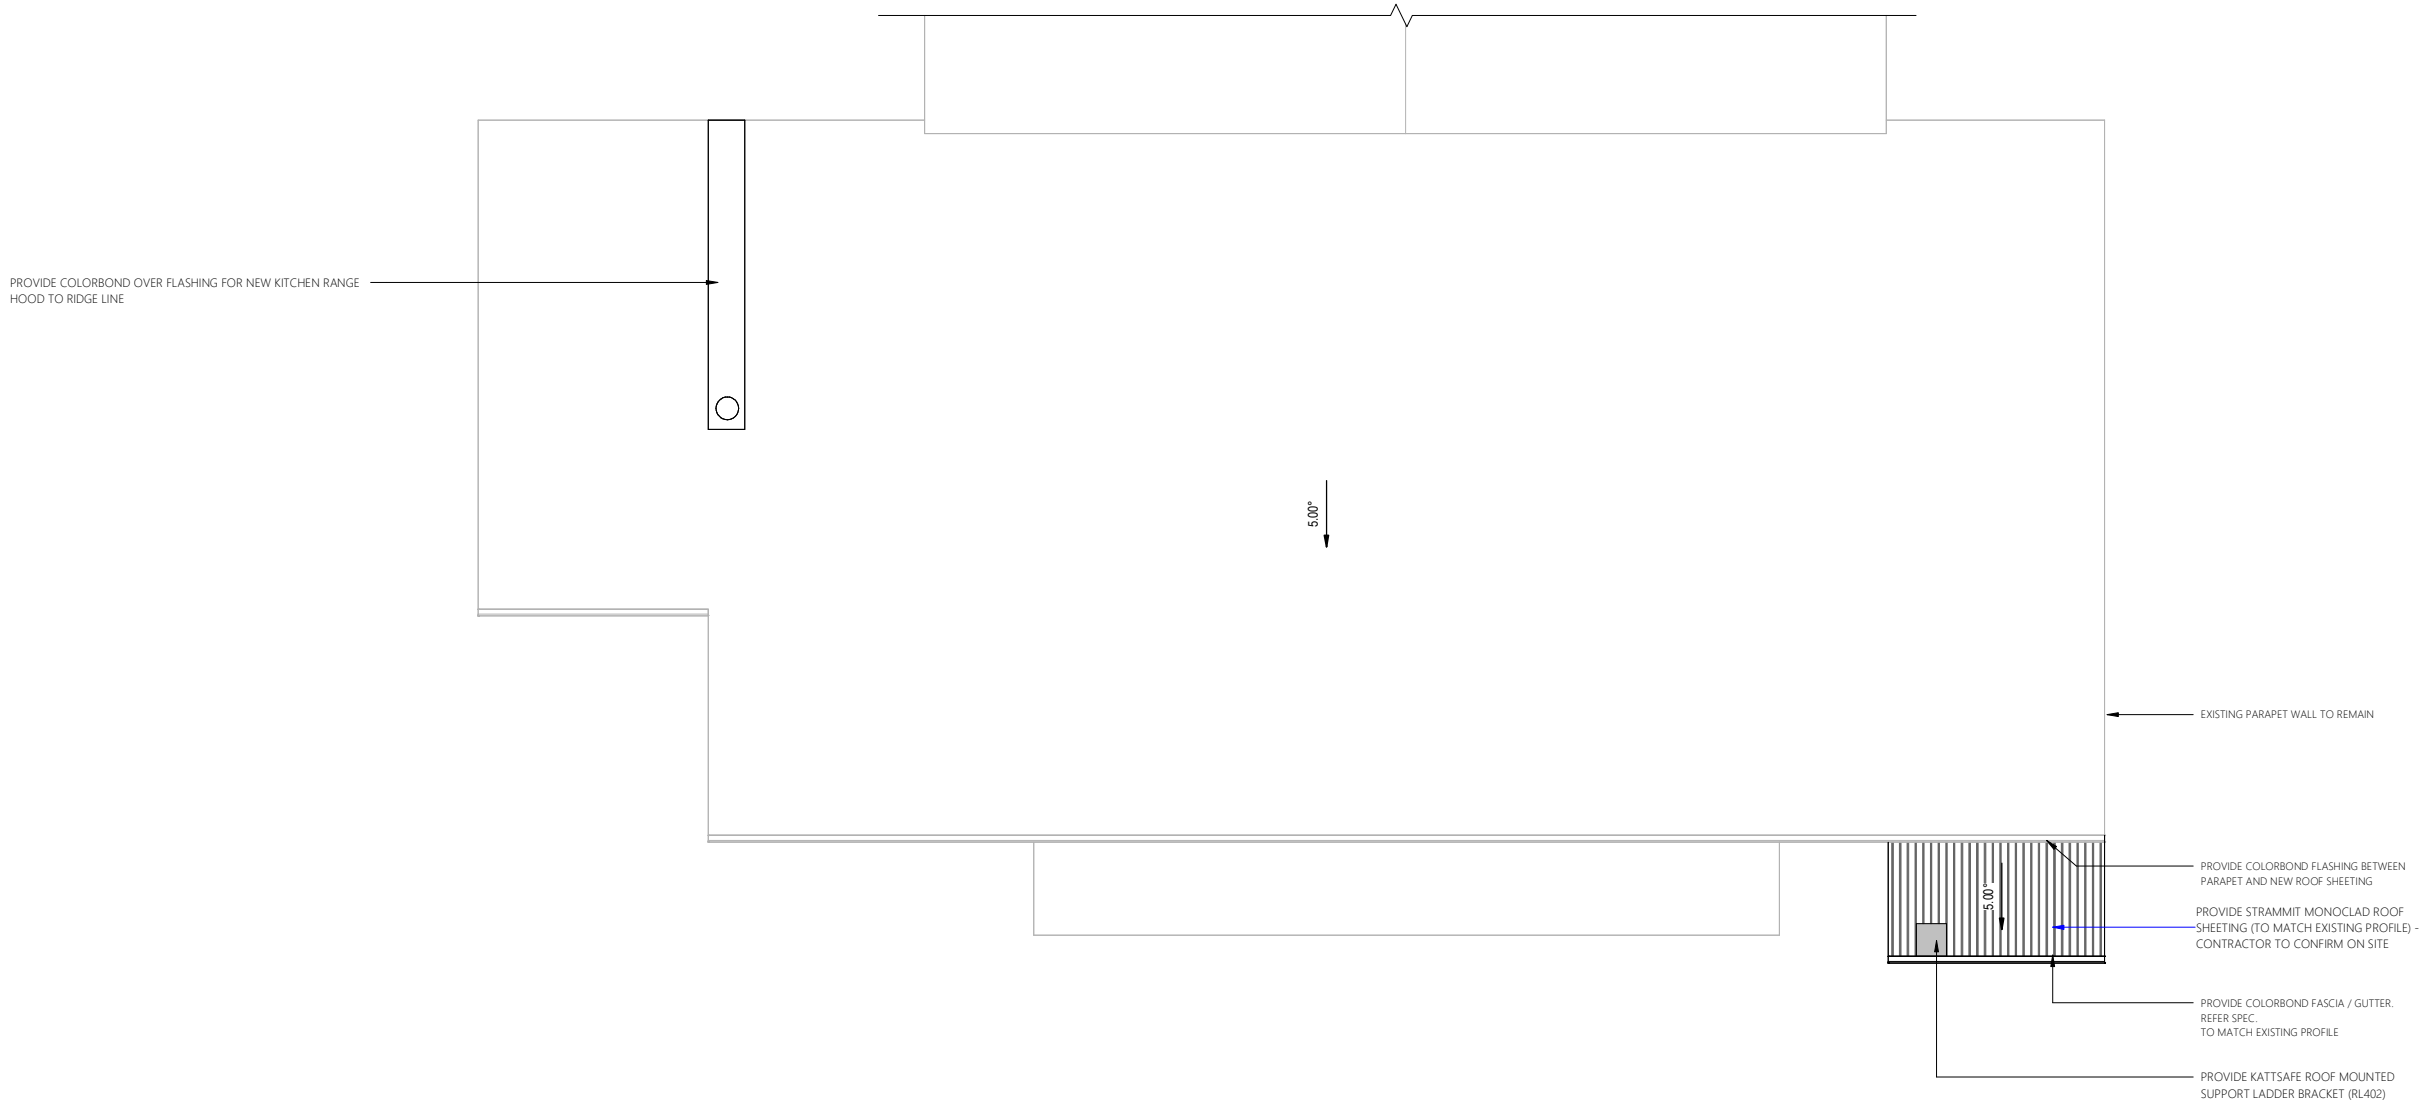

Proposed Roof Plan



TENDER ISSUE

Client

Project Details

WAREHOUSE REFURB

Address

STANWELL POWER STATION

Drawing Title










PROPOSED ROOF PLAN

0483 988 655 M
info@dezignelements.com.au E
QBCC No: 1247120 BDAQ No: 0001677

Scale: 1 : 100 Rev: T1
Date: MARCH 2026
Drawn: Author

Project No: 25_003 Drawing No: A2-303



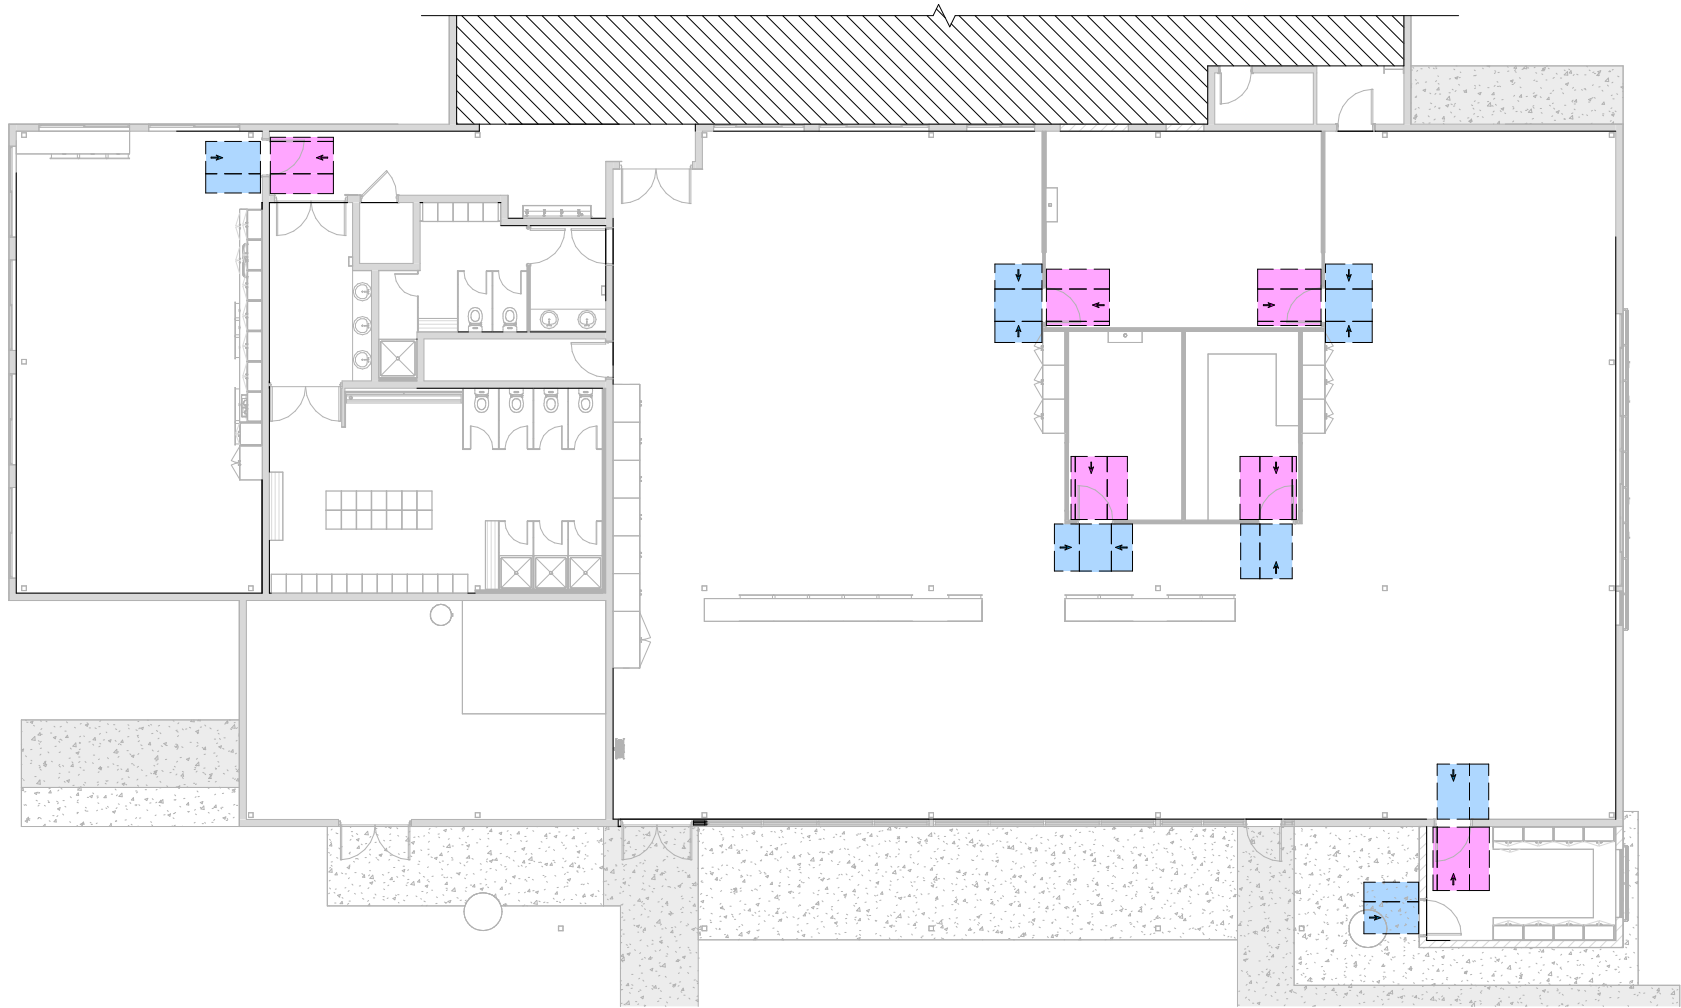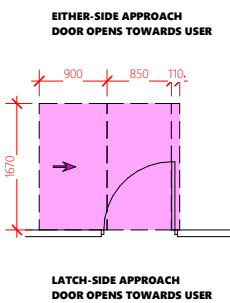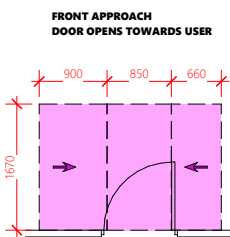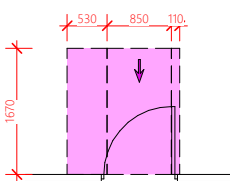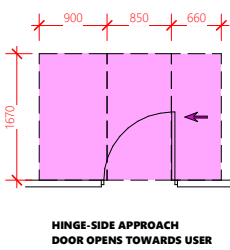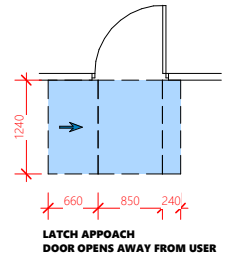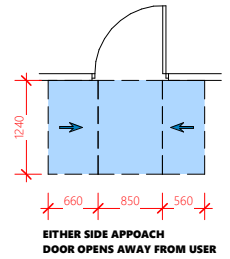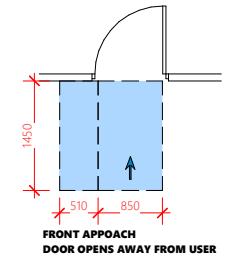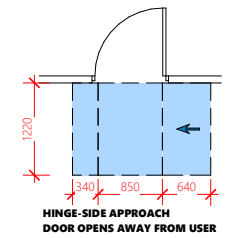

AS1428.1 - Clearance Plan

1 : 100



REVISIONS		
Rev	Description	Date
T1	TENDER ISSUE	12.03.2026

DO NOT SCALE THIS DRAWINGS



TENDER ISSUE

Client

Project Details

WAREHOUSE REFURB

Address

STANWELL POWER STATION


Drawing Title

AS1428.1 - CLEARANCE


0483 988 655 M
info@designelements.com.au E
QBCC No: 1247120 BDAQ No: 0001677

Scale:	As indicated	Rev:	T1
Date:	MARCH 2026		
Drawn:	Author		
Project No:	25_003	Drawing No:	A2-304



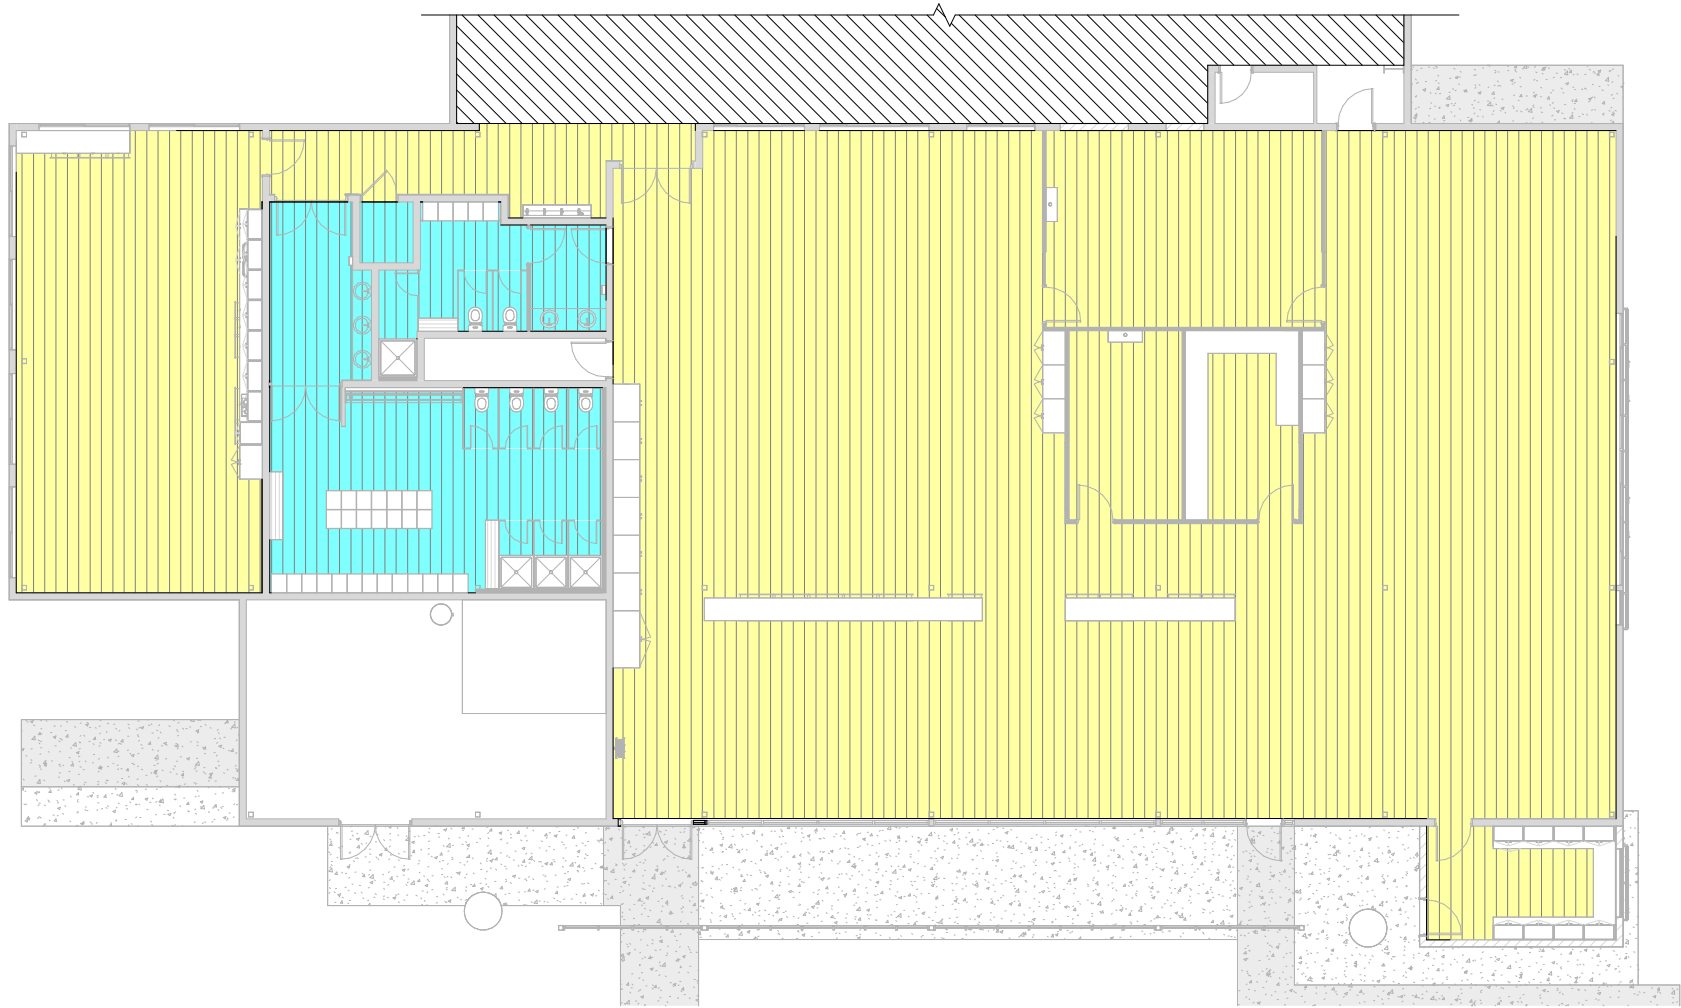

Floor Covering Plan

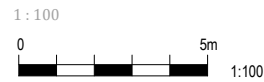

REVISIONS

Rev	Description	Date
T1	TENDER ISSUE	12.03.2026

DO NOT SCALE THIS DRAWINGS

FLOOR COVERING PLAN

	SHEET VINYL - TYPE 1 100mm FEATHER EDGE SKIRTING - BLACK
	SHEET VINYL - TYPE 2 100mm COVED UP SKIRTING
	SHEET VINYL - TYPE 3 100mm FEATHER EDGE SKIRTING - BLACK

TENDER ISSUE

Client

Project Details

WAREHOUSE REFURB

Address

STANWELL POWER STATION

Drawing Title

FLOOR COVERING PLAN

deizignelements
BUILDING DESIGNERS

0483 988 655

info@deizignelements.com.au


QBCC No: 1247120 BDAQ No: 0001677

Scale: 1 : 100	Rev: T1
Date: MARCH 2026	
Drawn: Author	
Project No: 25_003	Drawing No: A2-305



REVISIONS		
Rev	Description	Date
T1	TENDER ISSUE	12.03.2026

DO NOT SCALE THIS DRAWINGS

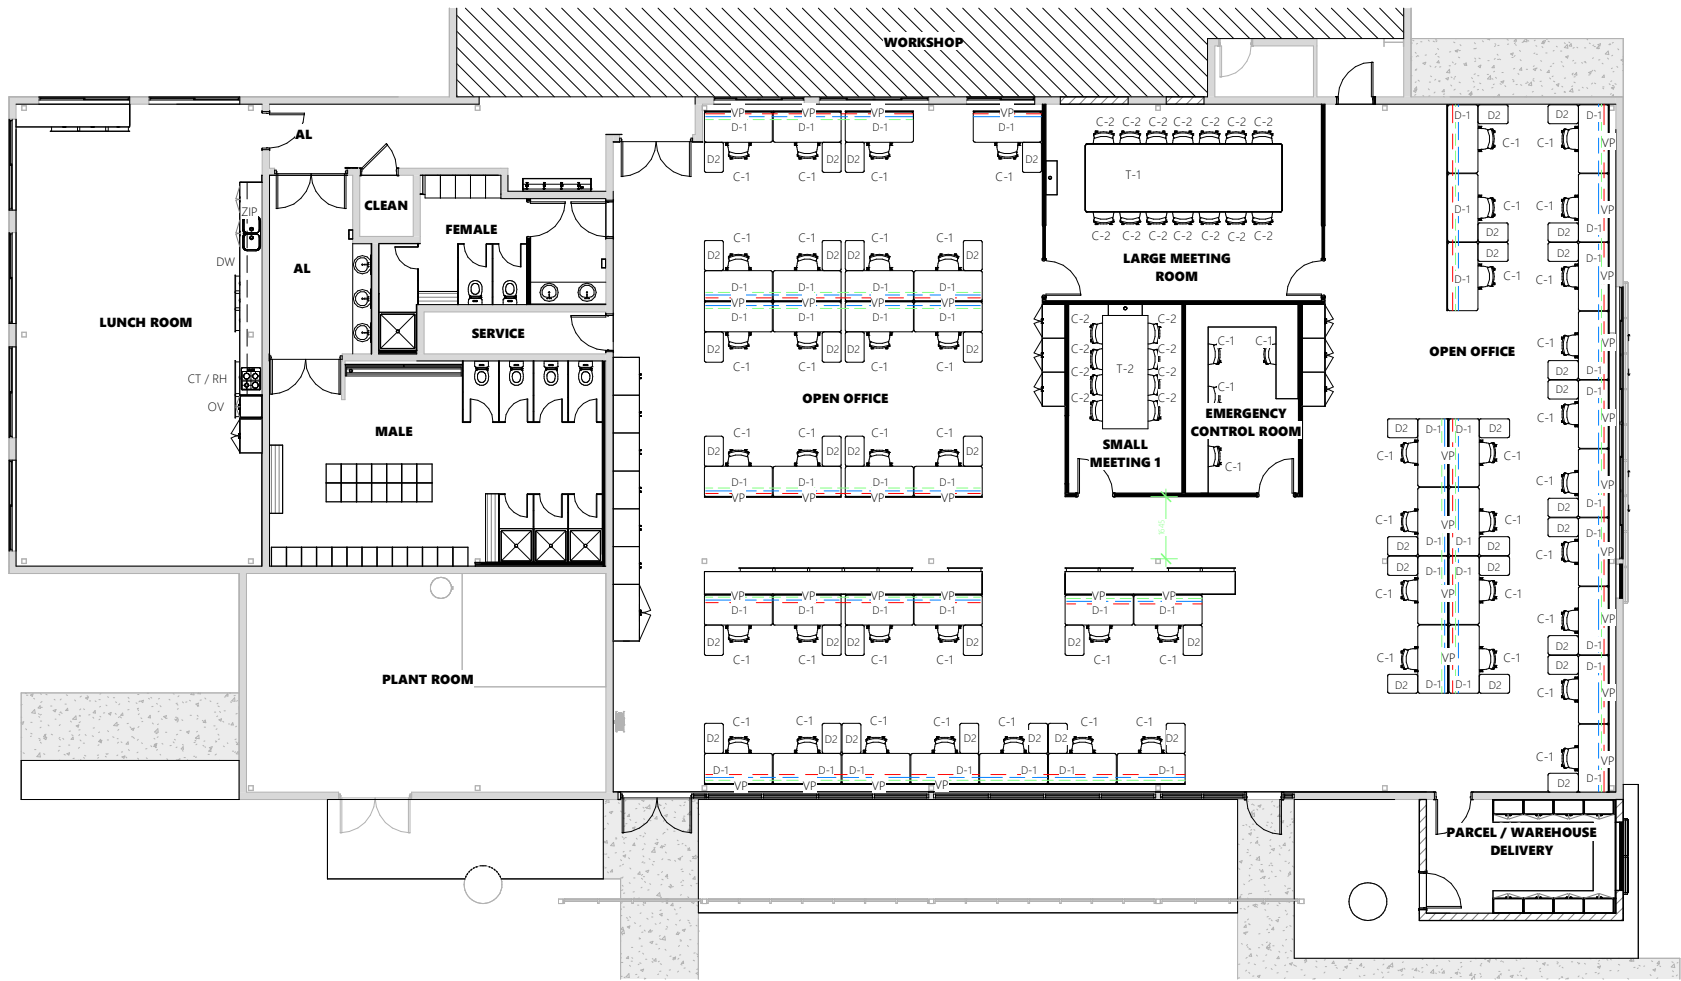

FURNITURE & APPLIANCE SCHEDULE

CODE	TYPE	SIZE	QTY	SUPPLIER
D-1	DESK	1800 x 800	50	SCHIAVELLA CLIMATE RECTANGLE WORK STATION
D-2	DESK	800 x 500	50	SCHIAVELLA CLIMATE RECTANGLE WORK STATION RETURN
C-1	CHAIR (workstation)	-	54	SCHIAVELLA HIGH BACK CHAIR BY OKAMURA, BLACK BODY, BLACK MESH BLACK AND UPHOLSTERED SEAT
C-2	CHAIR (meeting)	-	22	SHIBUSA HIGH BACK BY OKAMURA (BLACK)
T-1	LARGE TABLE	1800 x 5200	1	MEETING TABLE EONA - 25mm LAMINEX CHARCOAL NATURAL FINISH WITH ABS EDGING
T-2	SMALL TABLE	1250 x 3000	1	MEETING TABLE EONA - 25mm LAMINEX CHARCOAL NATURAL FINISH WITH ABS EDGING
—	CABLE CATCHER	AS REQUIRED	-	SCHIAVELLA
---	CABLE ARTICULATOR	AS REQUIRED	-	SCHIAVELLA
---	CABLE CHANNEL	AS REQUIRED	-	SCHIAVELLA
VP	VIDE SUSP. PANEL	1800 (600mm ABOVE DESK)	42	SCHIAVELLA - PROVIDE SUSPENDED BRACKETS TO EACH DESK
OV	OVEN	598 x 596	1	FISHER & PAYKEL 60CM SERIES 7 CONTEMPORARY PYROLYTIC OVEN 9 FUNCTION - BLACK
DW	DISHWASHER	597 x 600	1	FISHER & PAYKEL SERIES 7 CONTEMPORARY DISHWASHER - BLACK STEEL
CT	COOK TOP	600	1	FISHER & PAYKEL 60CM SERIES 7 4 ZONE INDUCTION COOKTOP 2 SMARTZONES - BLACK
RH	RANGE HOOD	600	1	FISHER & PAYKEL 60CM SERIES 7 INTEGRATED INSERT WALL RANGEHOOD EXTERNAL MOTOR - STEEL GLASS
ZIP	ZIP UNIT	-	1	HYDROTAP G5 BCSHA100 5-IN-1 CLASSIC TAP WITH CLASSIC MIXER BLACK

Proposed Furniture Layout

1 : 100



TENDER ISSUE

Client

Project Details

WAREHOUSE REFURB

Address

STANWELL POWER STATION

Drawing Title

FUNITURE LAYOUT

0483 988 655 M

info@designelements.com.au E

QBCC No: 1247120 BDAQ No: 0001677

Scale: 1 : 100 Rev:

Date: MARCH 2026 T1

Drawn: Author

Project No: Drawing No:


25_003 A2-306



13/03/2026 11:25:20 AM


REVISIONS		
Rev	Description	Date
T1	TENDER ISSUE	12.03.2026

DO NOT SCALE THIS DRAWINGS

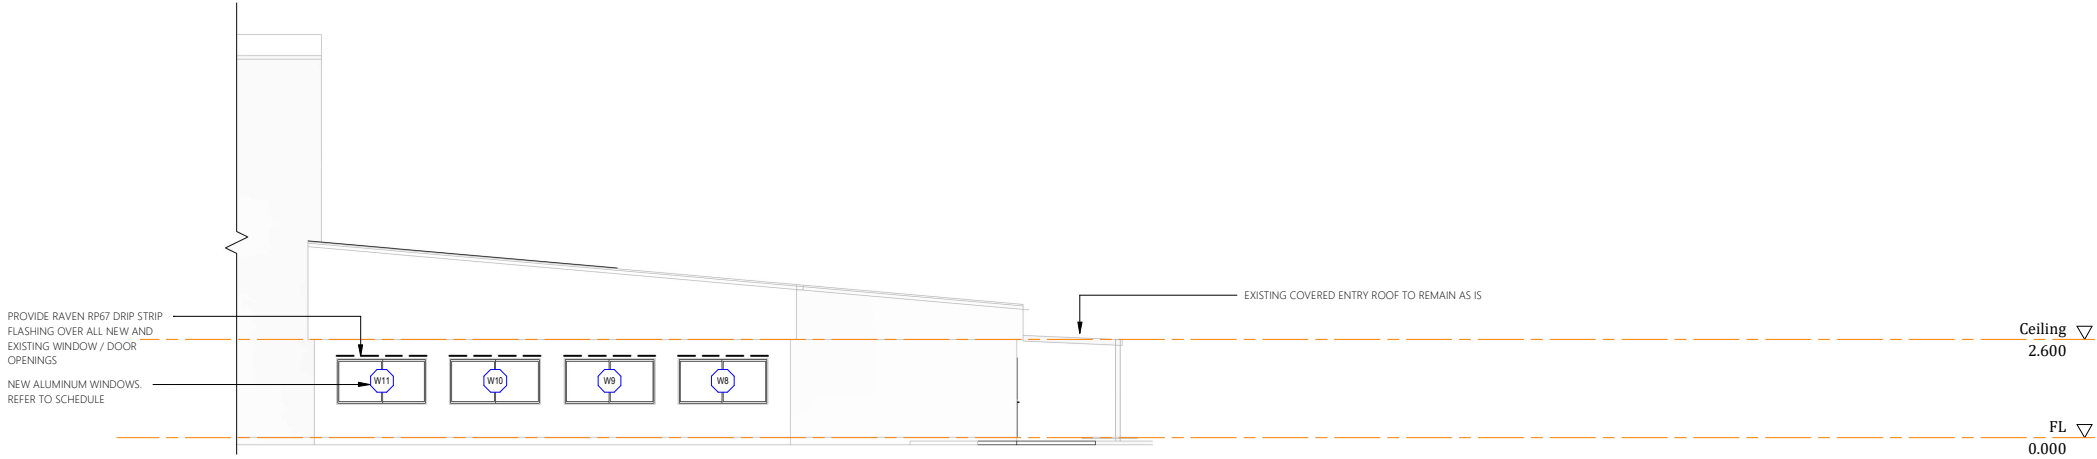


Proposed Elevation 1

1 : 100

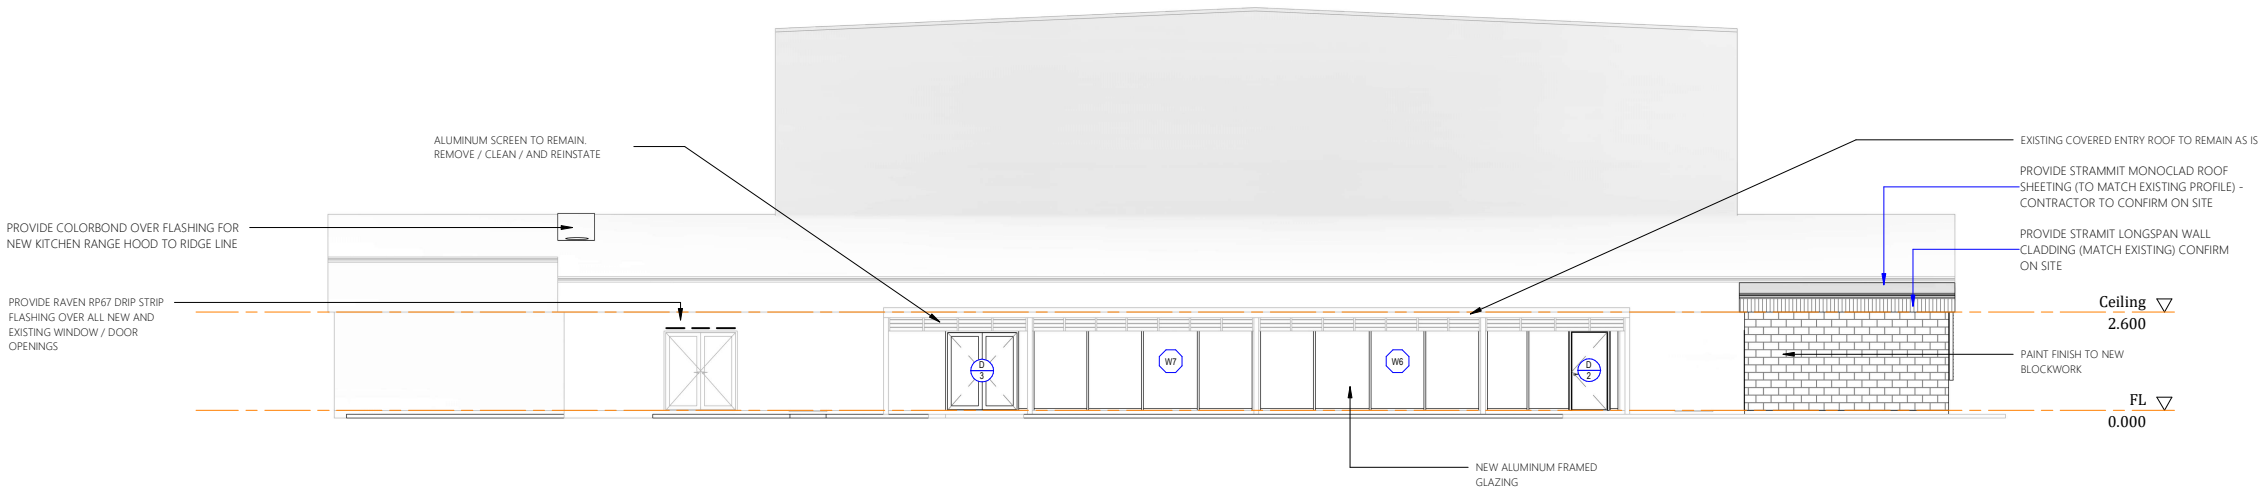

Proposed Elevation 2

1 : 100

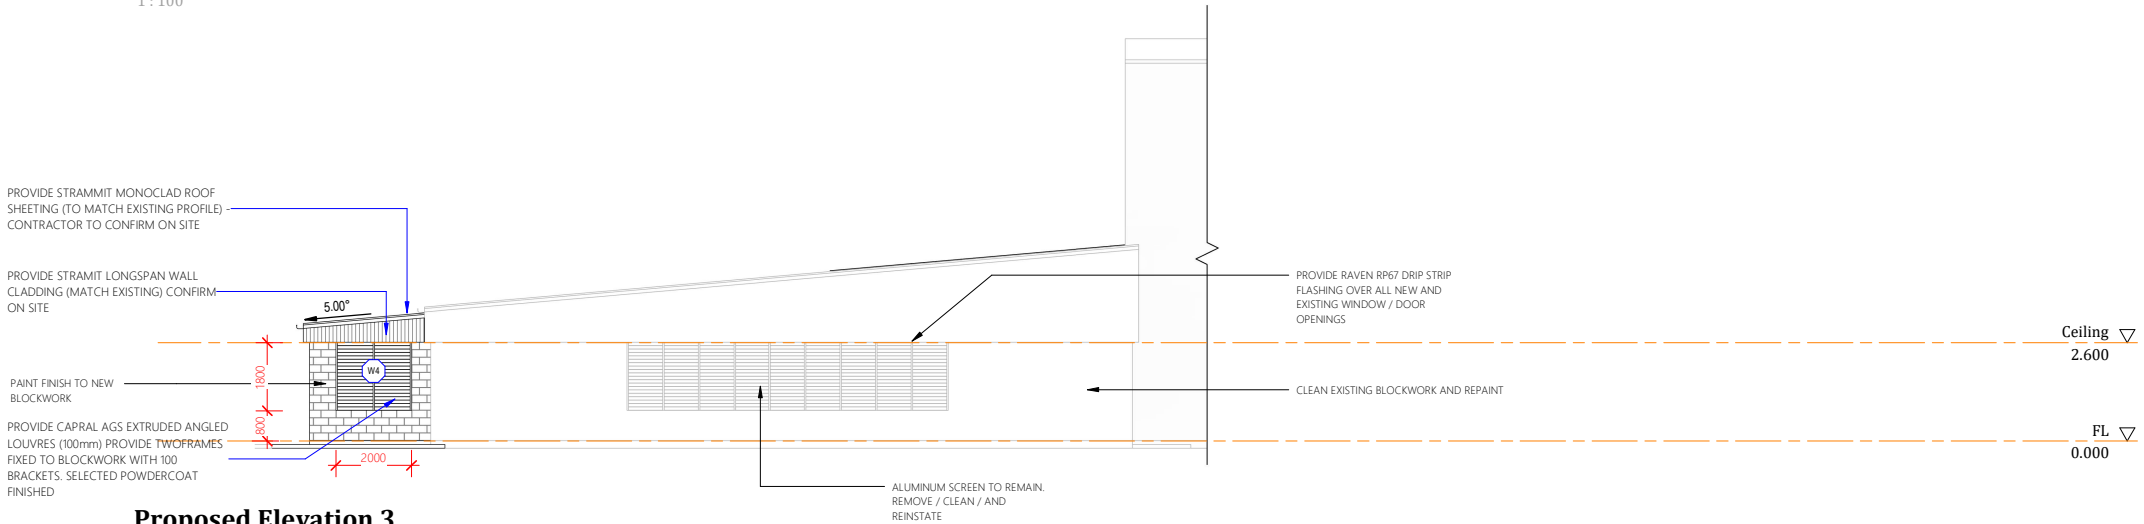

Proposed Elevation 3

1 : 100

TENDER ISSUE



Client
Project Details
WAREHOUSE REFURB
Address
STANWELL POWER STATION
Drawing Title
PROPOSED ELEVATIONS

dezi elements
BUILDING DESIGNERS


0483 988 655 M
info@dezi elements.com.au E
QBCC No: 1247120 BDAQ No: 0001677

Scale: 1 : 100	Rev: T1
Date: MARCH 2026	
Drawn: Author	
Project No: 25_003	Drawing No: A2-400


13/03/2026 11:25:32 AM

REVISIONS		
Rev	Description	Date
T1	TENDER ISSUE	12.03.2026

DO NOT SCALE THIS DRAWINGS

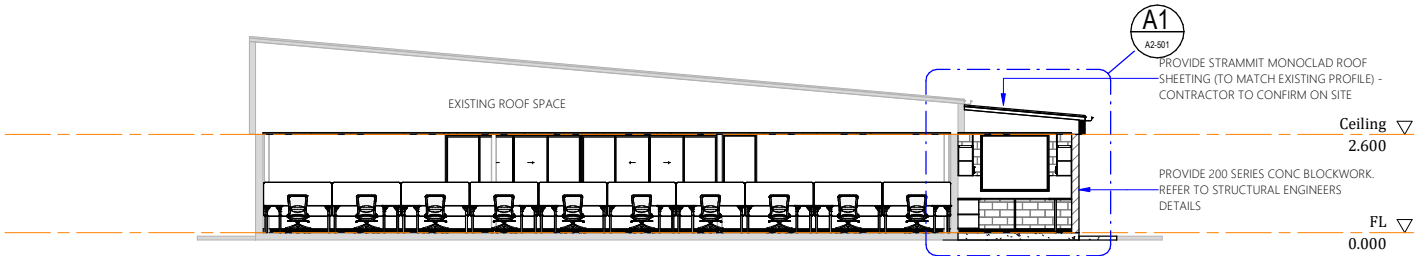

Section A
1 : 100

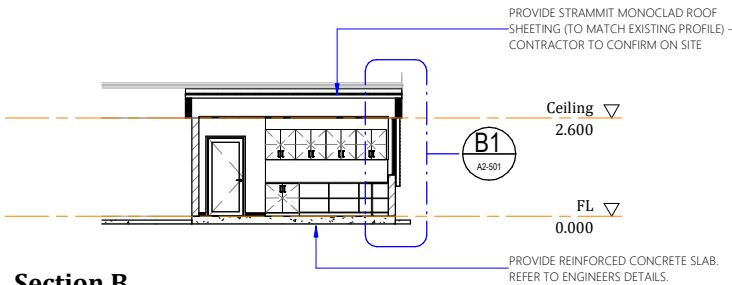

Section B
1 : 100

TENDER ISSUE

Client



Project Details

WAREHOUSE REFURB

Address

STANWELL POWER STATION

Drawing Title


PROPOSED SECTION


BUILDING DESIGNERS
0483 988 655 M
info@dezi elements.com.au E
QBCC No: 1247120 BDAQ No: 0001677

Scale: 1 : 100
Date: MARCH 2026
Drawn: Author


Rev: T1
Project No: 25_003
Drawing No: A2-500

13/03/2026 11:25:34 AM

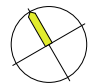


REVISIONS		
Rev	Description	Date
T1	TENDER ISSUE	12.03.2026

DO NOT SCALE THIS DRAWINGS

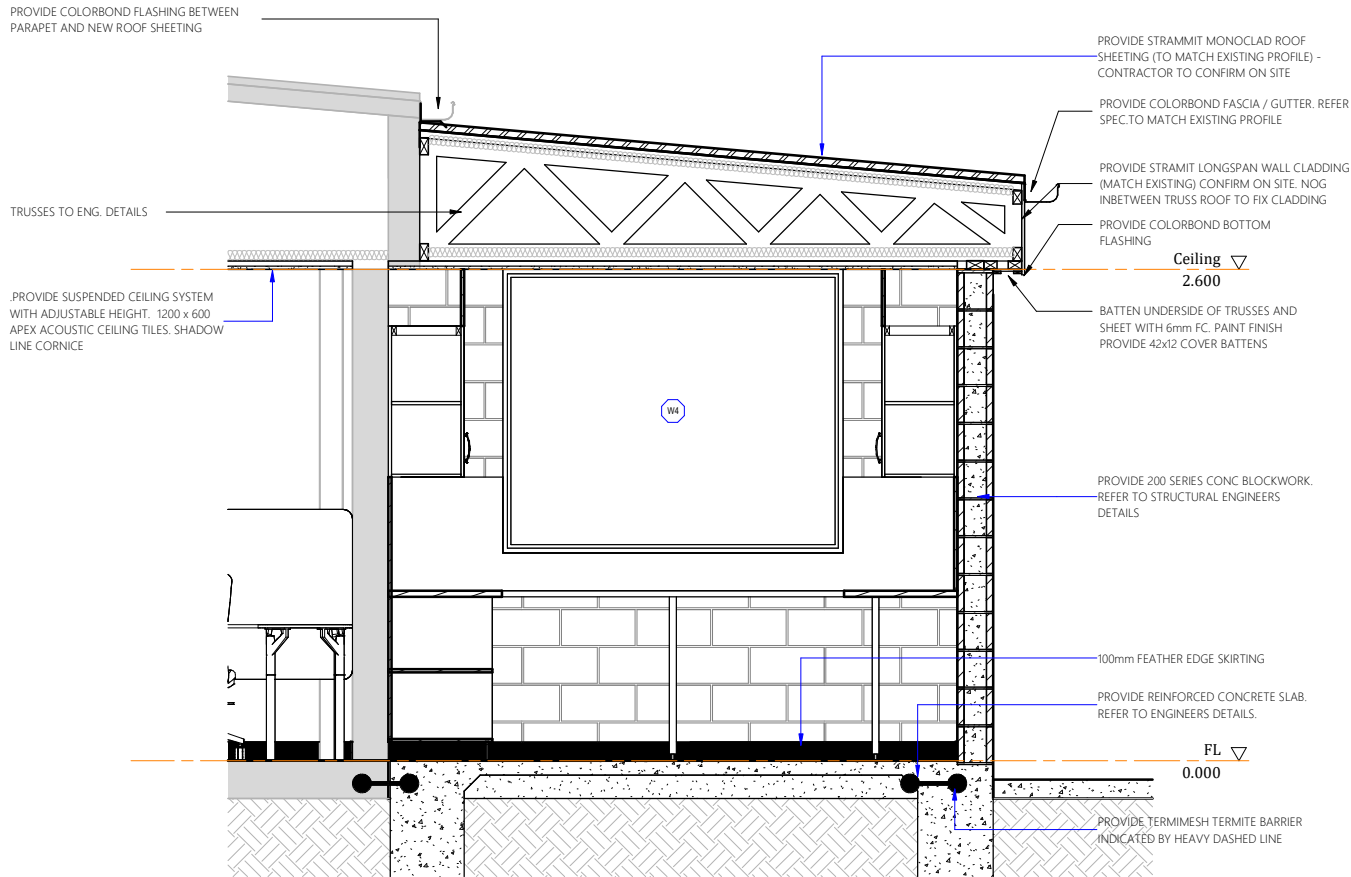

Section A1

1 : 20

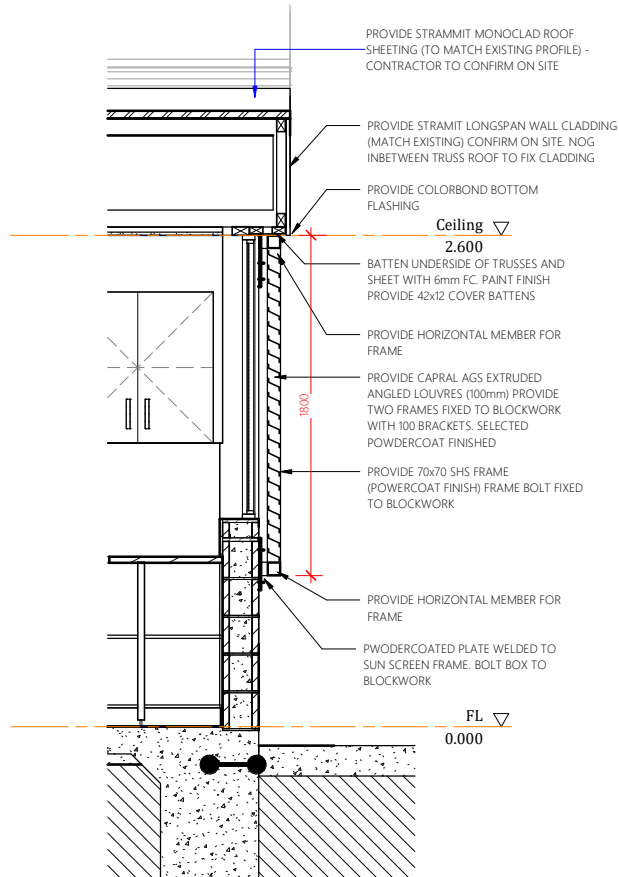

Section B1

1 : 20

TENDER ISSUE



Project Details
WAREHOUSE REFURB

Address
STANWELL POWER STATION

Drawing Title
SECTION DETAILS




0483 988 655 M
info@deignelements.com.au E
QBCC No: 1247120 BDAQ No: 0001677


Scale: 1 : 20 Rev: T1
Date: MARCH 2026
Drawn: Author

Project No: 25_003 Drawing No: A2-501




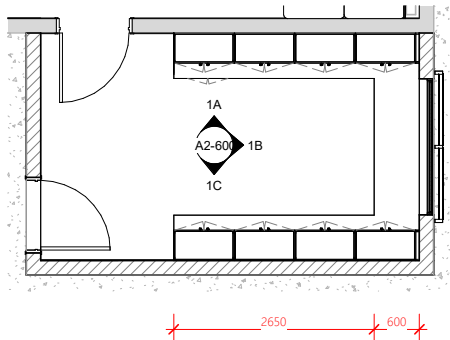


Internal Plan 1
1 : 50

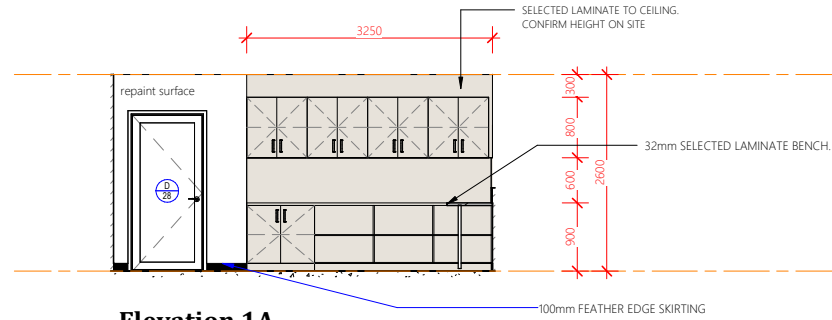

Elevation 1A
1 : 50

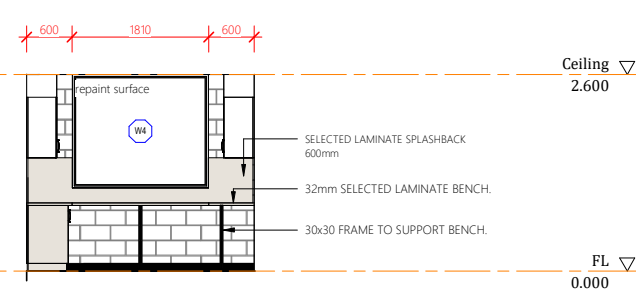

Elevation 1B
1 : 50

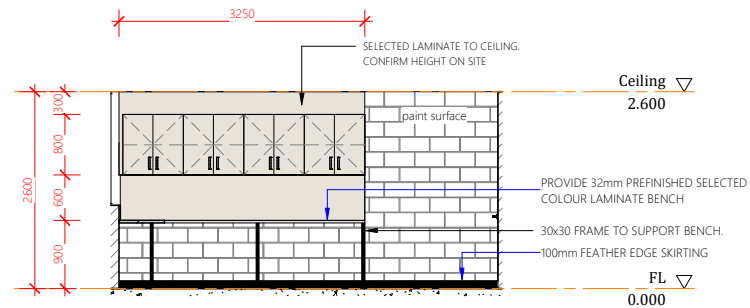

Elevation 1C
1 : 50



REVISIONS

Rev	Description	Date
T1	TENDER ISSUE	12.03.2026

DO NOT SCALE THIS DRAWINGS



TENDER ISSUE



Project Details
WAREHOUSE REFURB
Address
STANWELL POWER STATION
Drawing Title
INTERNAL ELEVATIONS 1 - PARCEL ROOM



Scale: 1 : 50	Rev: T1
Date: MARCH 2026	
Drawn: Author	
Project No: 25_003	Drawing No: A2-600



DO NOT SCALE THIS DRAWINGS

Client



stanwell

Drawing Title

**INTERNAL ELEVATIONS 2 -
OPEN OFFICE**

Scale: 1 : 50	Rev:
Date: MARCH 2026	T1
Drawn: Author	
Project No: 25_003	Drawing No: A2-601

13/03/2026 11:25:40 AM



REVISIONS		
Rev	Description	Date
T1	TENDER ISSUE	12.03.2026

DO NOT SCALE THIS DRAWINGS



TENDER ISSUE

Client



Project Details

WAREHOUSE REFURB

Address

STANWELL POWER STATION

Drawing Title


INTERNAL ELEVATIONS 3 - CENTRAL MEETING ROOMS



BUILDING DESIGNERS
0483 988 655 M
info@designelements.com.au E
QBCC No: 1247120 BDAQ No: 0001677

Scale: 1 : 50
Date: MARCH 2026
Drawn: Author

Rev: T1
Project No: 25_003
Drawing No: A2-602


13/03/2026 11:25:46 AM

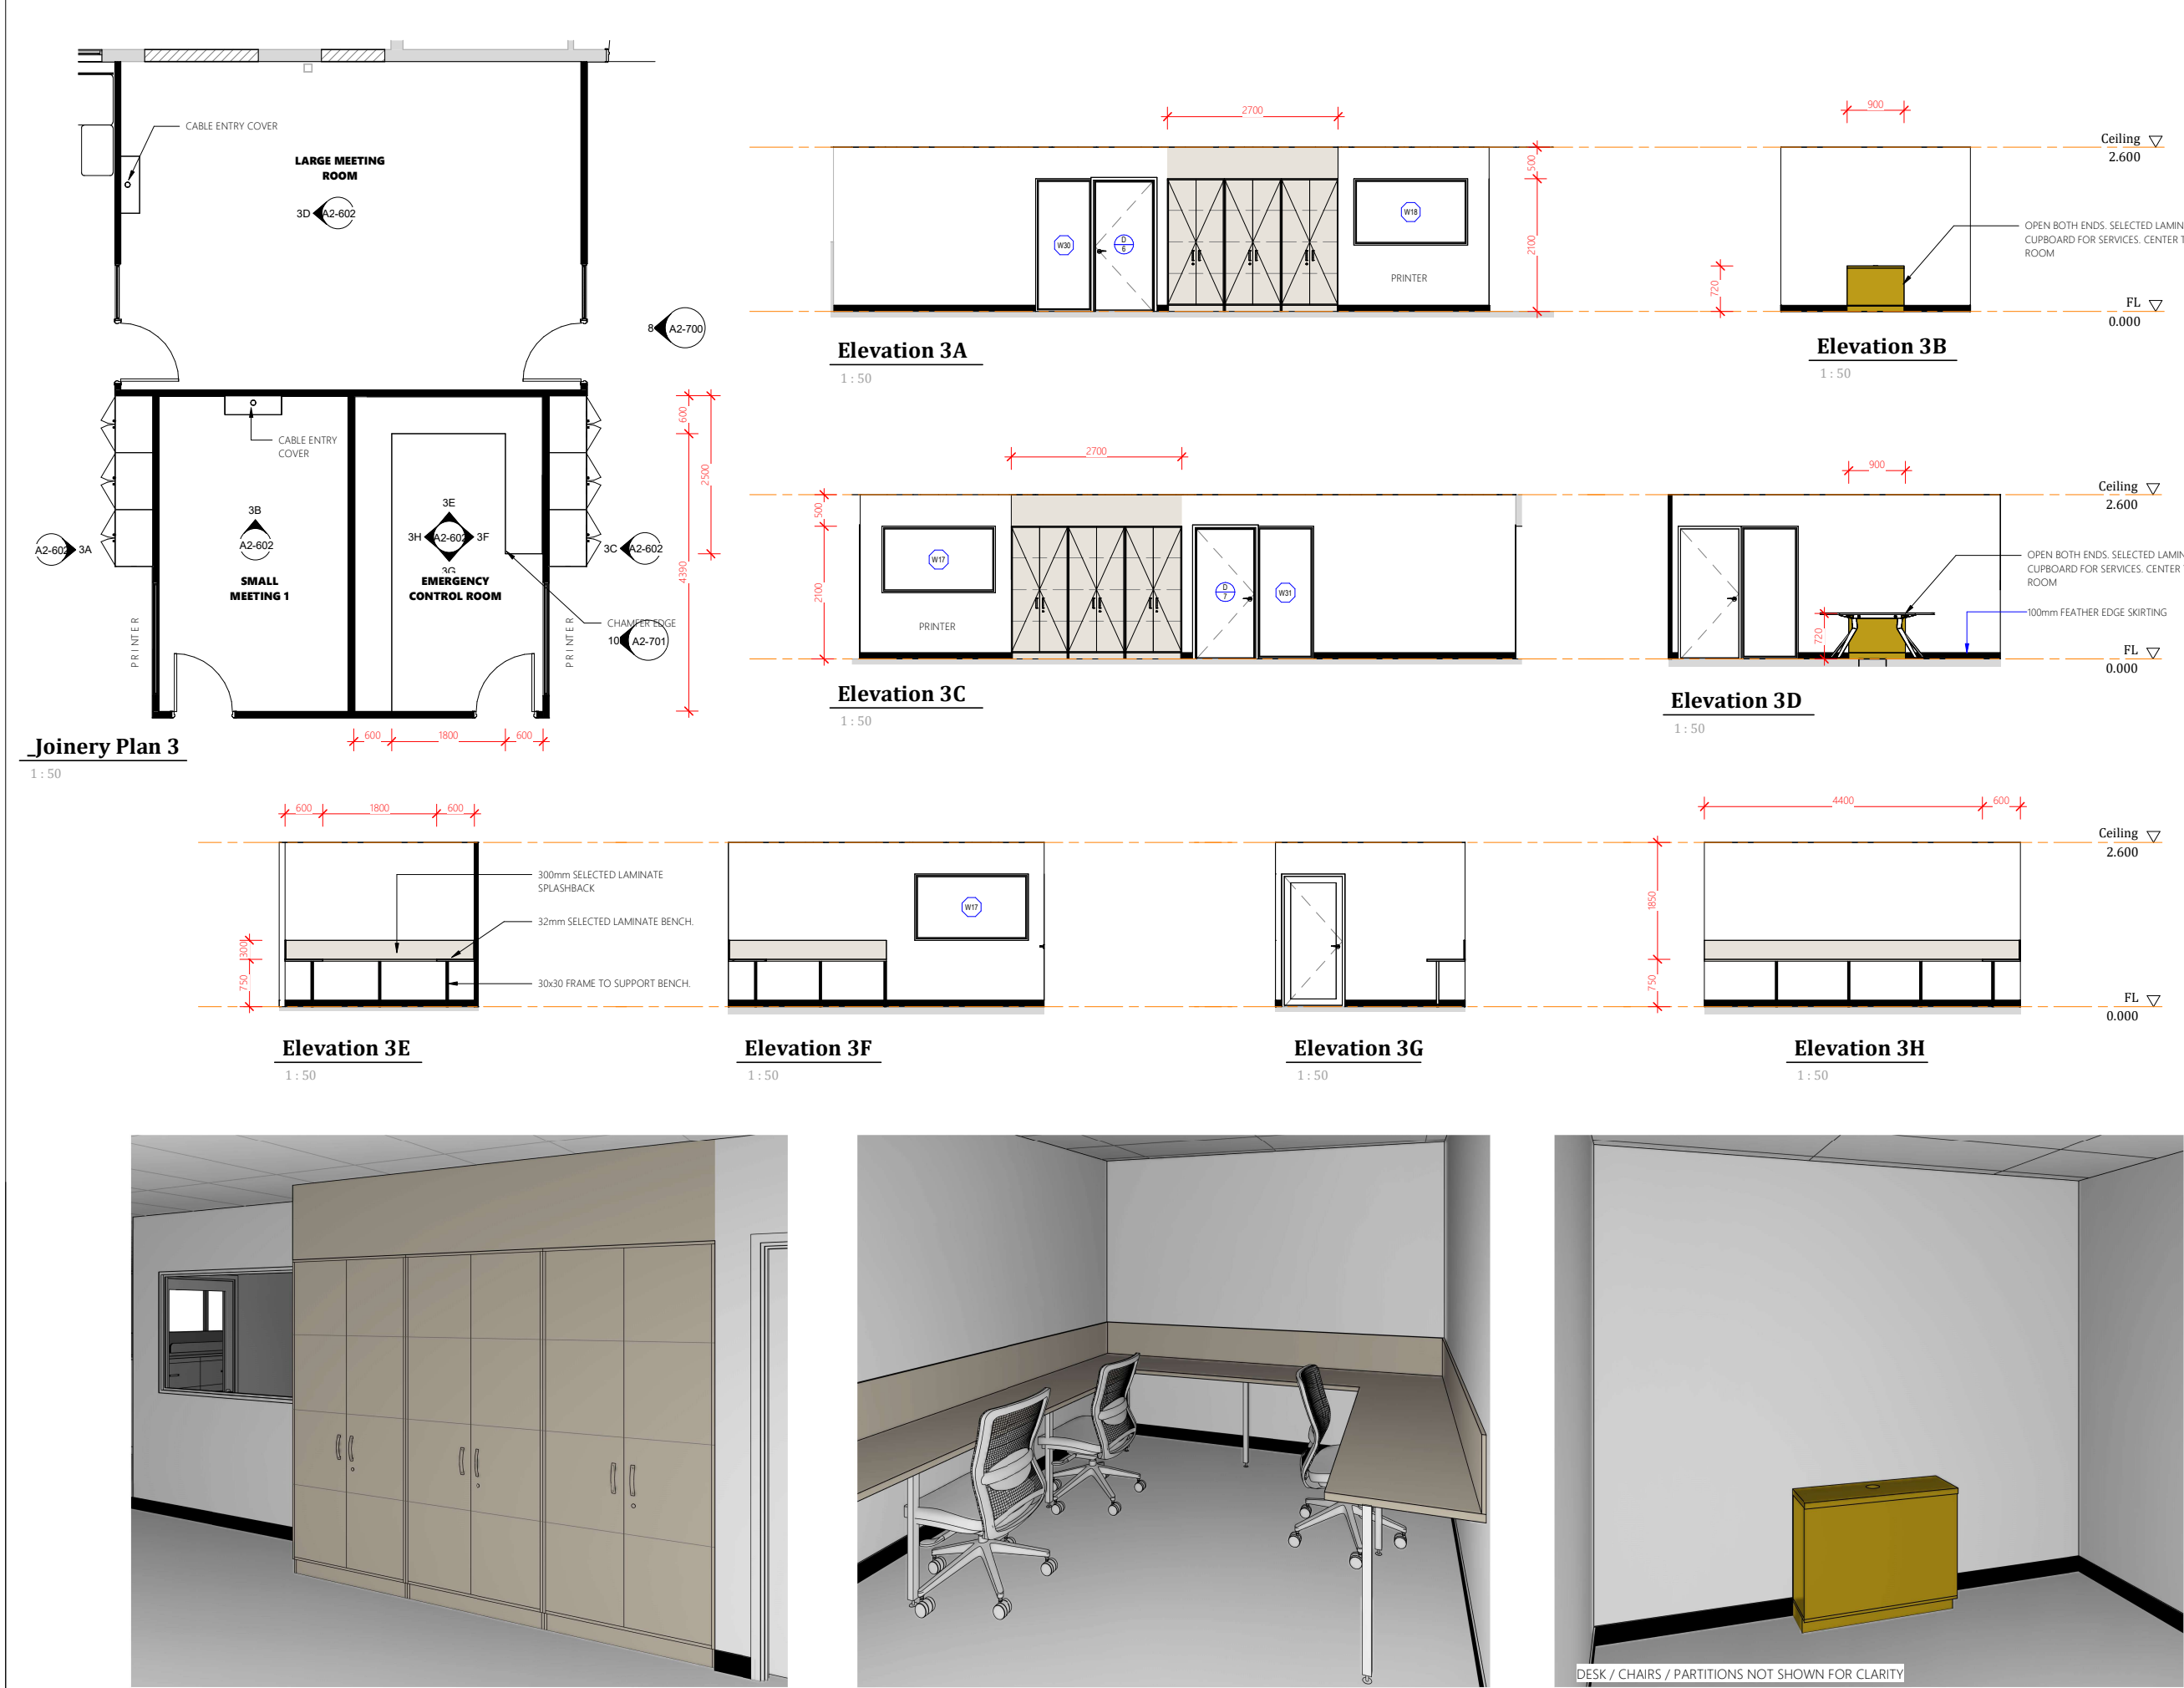

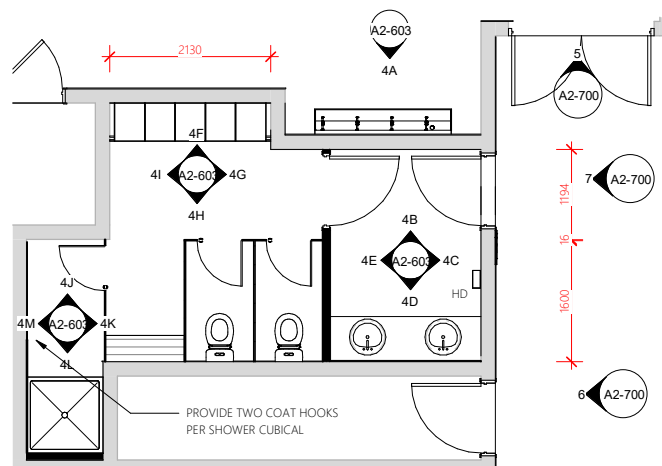

Joinery Plan 4

1: 50

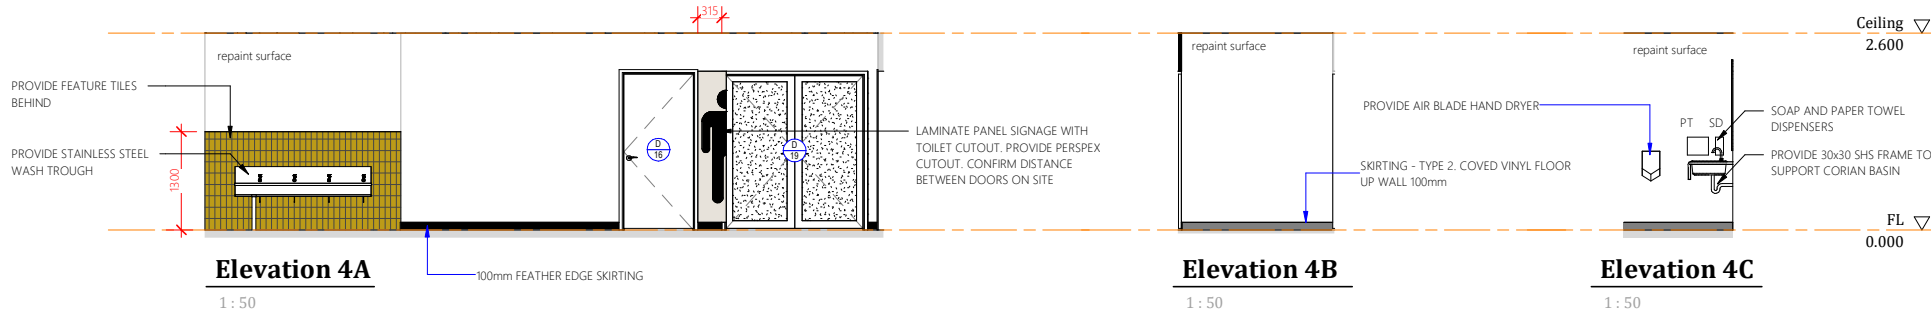

Elevation 4A


1: 50

Elevation 4B

1: 50

Elevation 4C

1: 50

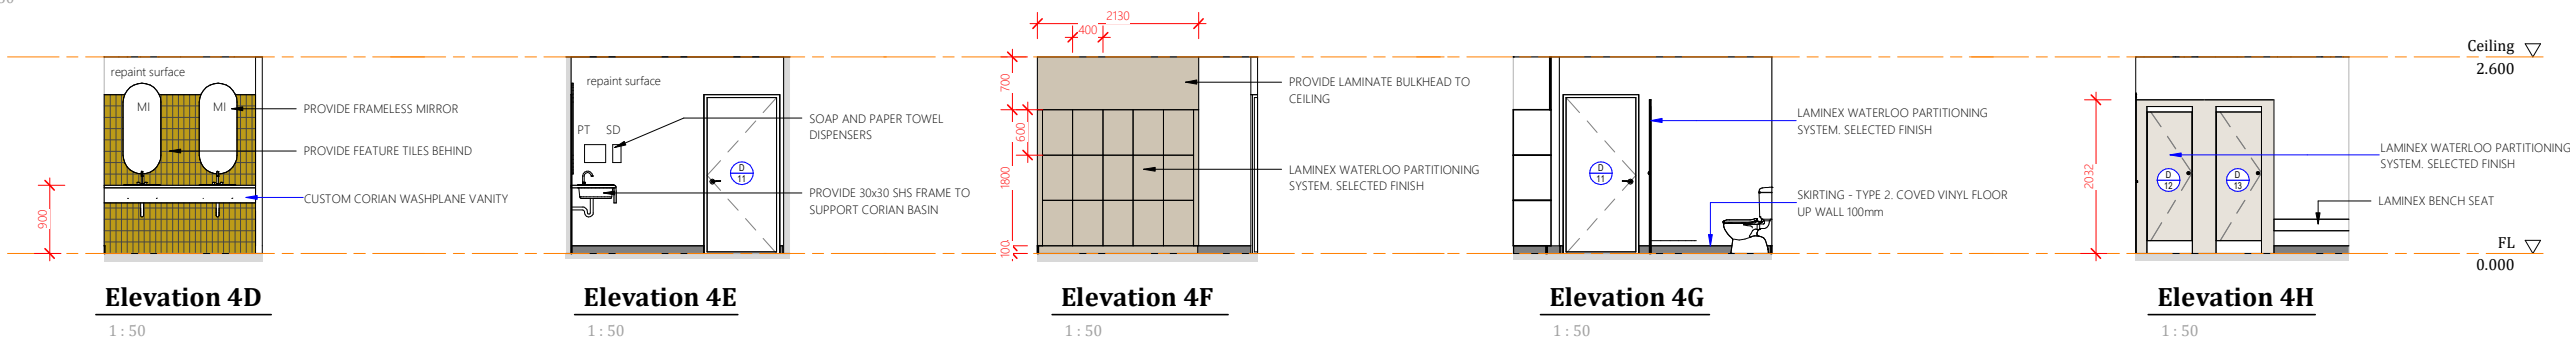

Elevation 4D

1: 50

Elevation 4E

1: 50

Elevation 4F


1: 50

Elevation 4G

1: 50

Elevation 4H

1: 50

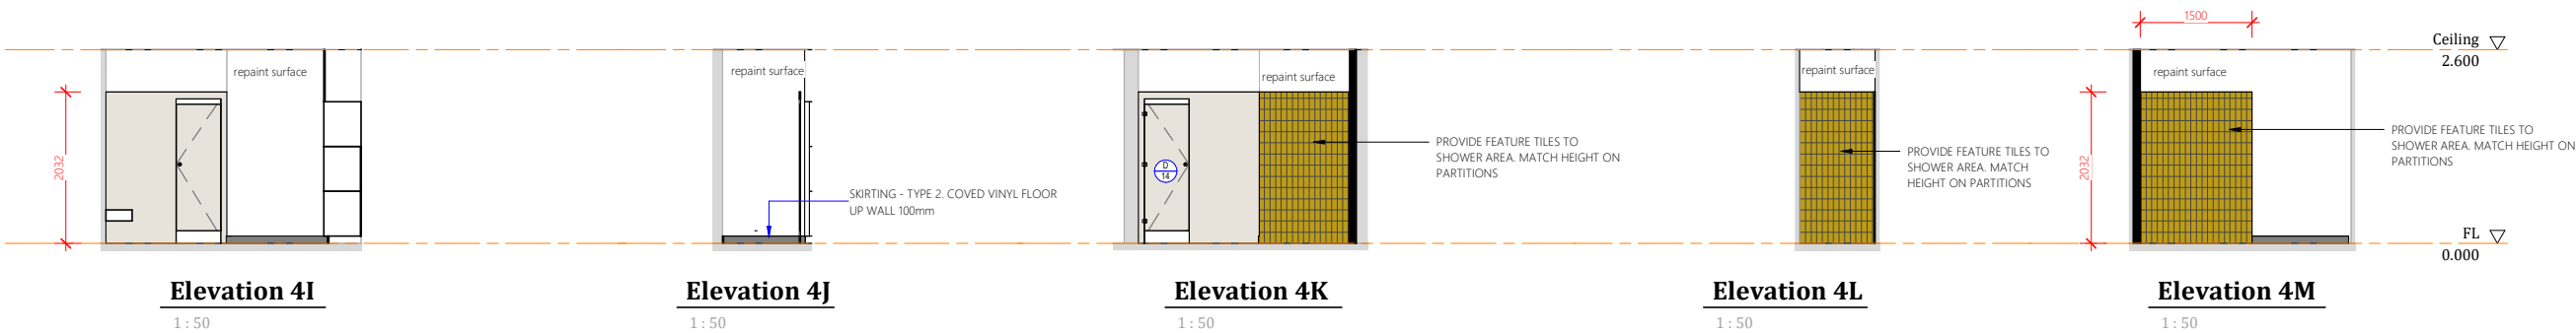

Elevation 4I

1: 50

Elevation 4J

1: 50

Elevation 4K


1: 50

Elevation 4L

1: 50

Elevation 4M

1: 50

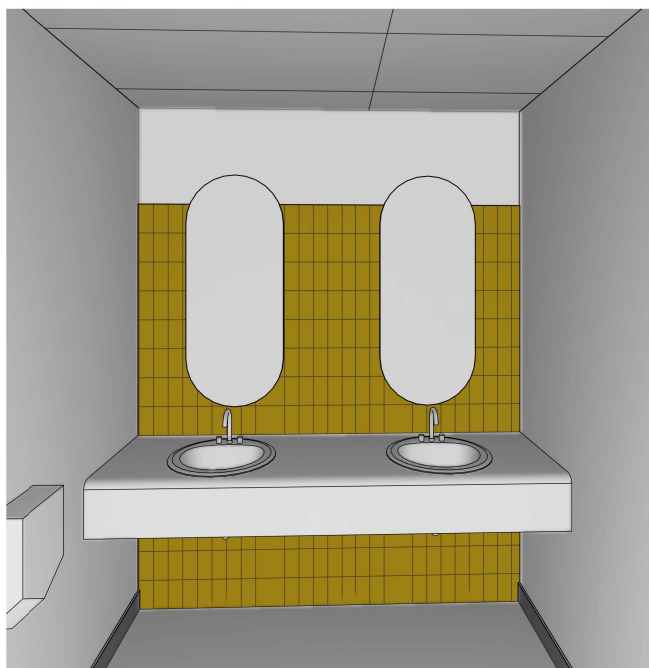

REVISIONS		
Rev	Description	Date
T1	TENDER ISSUE	12.03.2026


DO NOT SCALE THIS DRAWINGS

TENDER ISSUE

Client

Project Details
WAREHOUSE REFURB
Address
STANWELL POWER STATION
Drawing Title
INTERNAL ELEVATIONS 5 - FEMALE AMENITIES


0483 988 655 M
info@dezi elements.com.au E
QBCC No: 1247120 BDAQ No: 0001677
Scale: 1: 50
Date: MARCH 2026
Drawn: Author
Project No: 25_003
Drawing No: A2-603

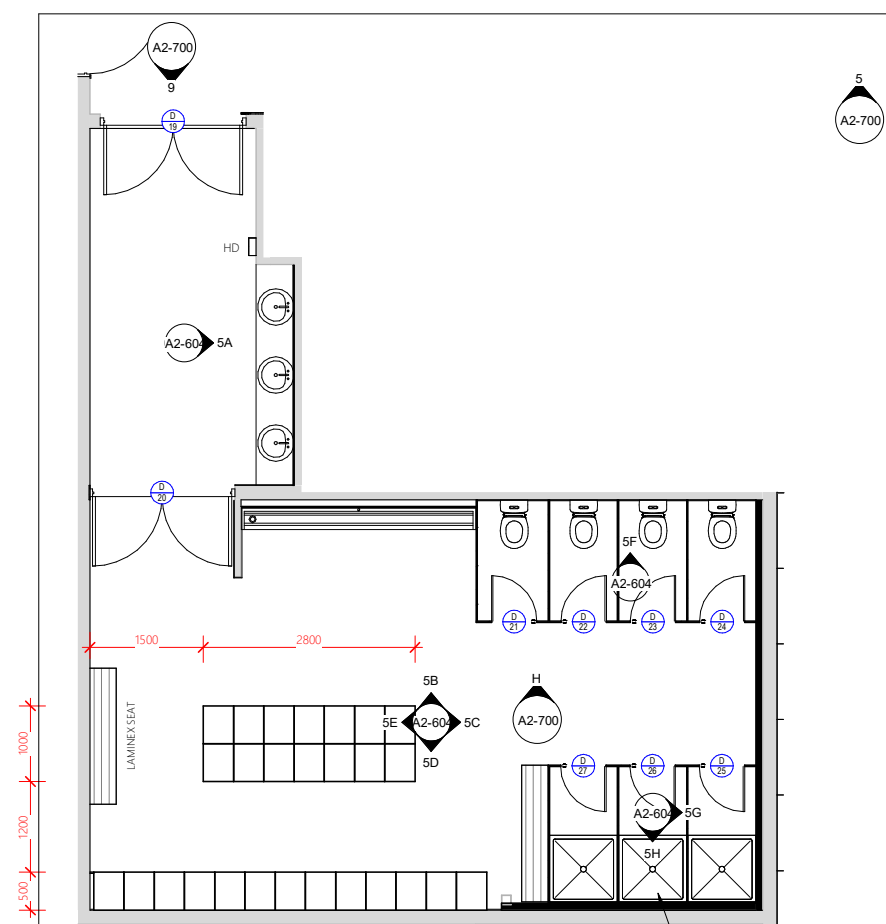

Joinery Plan 5


1 : 50

PROVIDE TWO COAT HOOKS
PER SHOWER CUBICAL

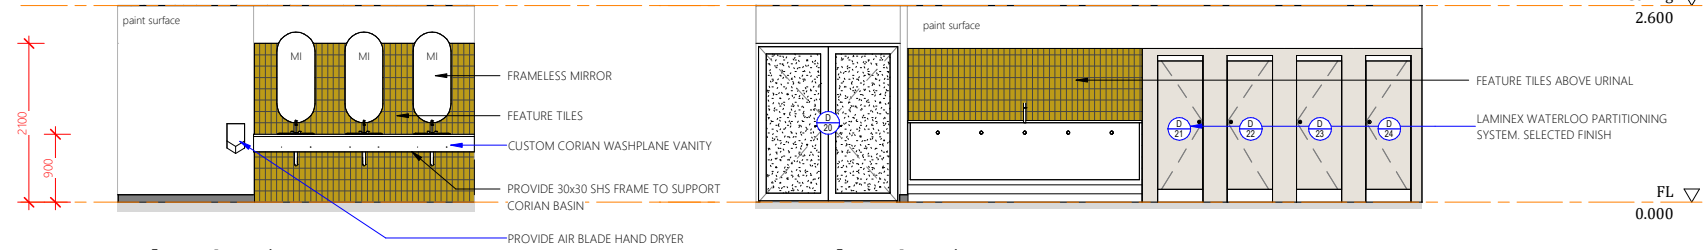


Elevation 5A

1 : 50

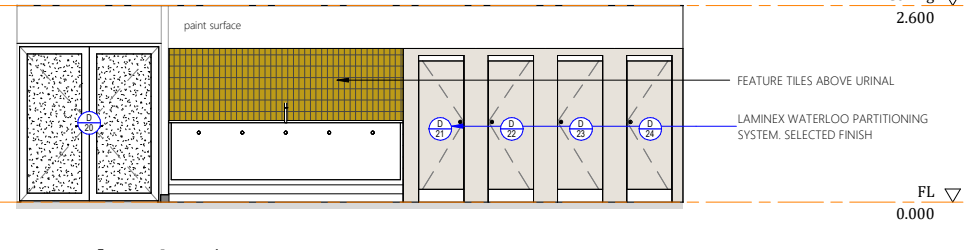


Elevation 5B

1 : 50

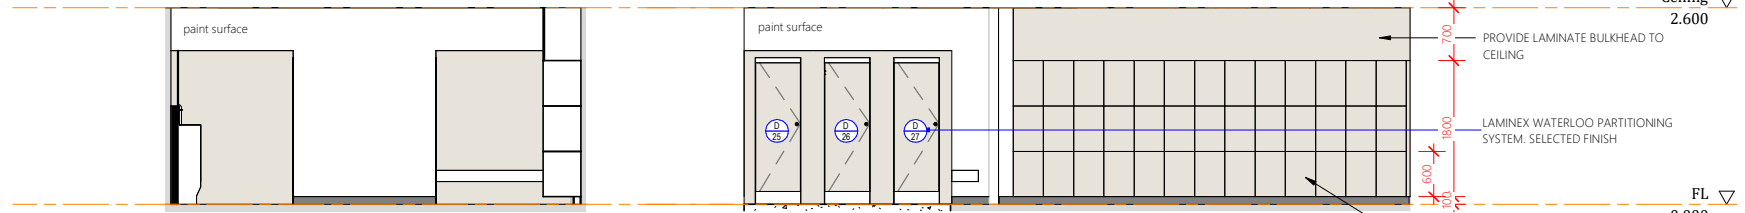

Elevation 5C

1 : 50

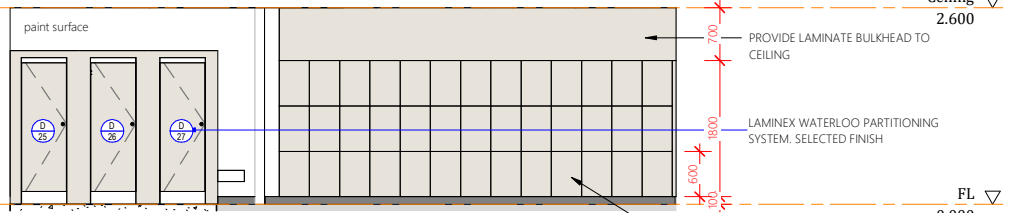


Elevation 5D

1 : 50



Elevation 5E

1 : 50

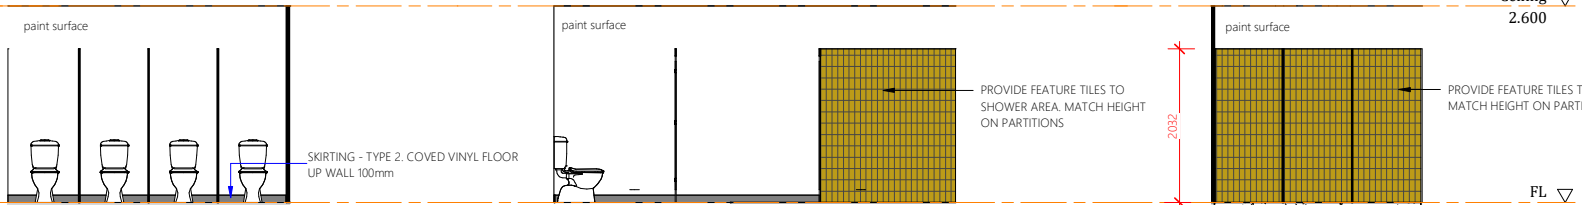


Elevation 5F

1 : 50





Elevation 5G

1 : 50

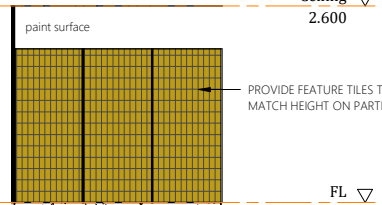

Elevation 5H


1 : 50

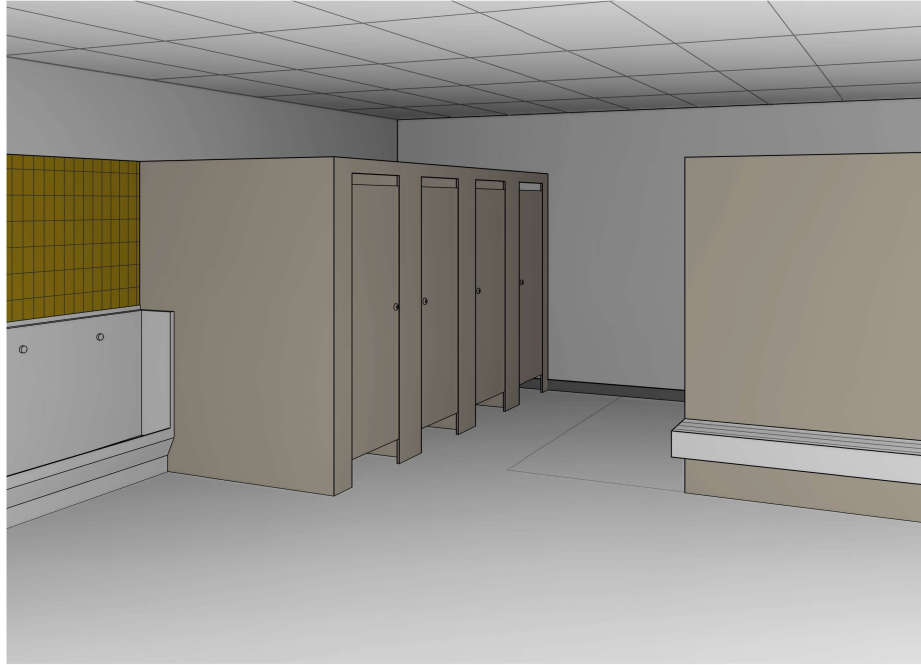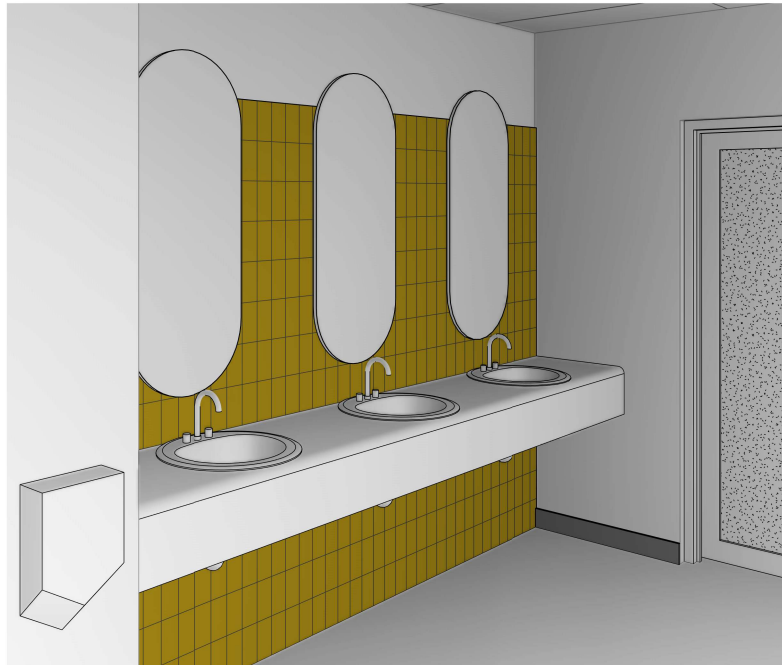

REVISIONS

Rev	Description	Date
T1	TENDER ISSUE	12.03.2026

DO NOT SCALE THIS DRAWINGS

 

TENDER ISSUE



Project Details
WAREHOUSE REFURB

Address
**STANWELL POWER
STATION**

Drawing Title
**INTERNAL ELEVATIONS 5 -
MALE AMENITIES**




0483 988 655 M
info@designelements.com.au E
QBCC No: 1247120 BDAQ No: 0001677

Scale: 1 : 50 Rev:
Date: MARCH 2026 T1
Drawn: Author


Project No: Drawing No:
25_003 A2-604



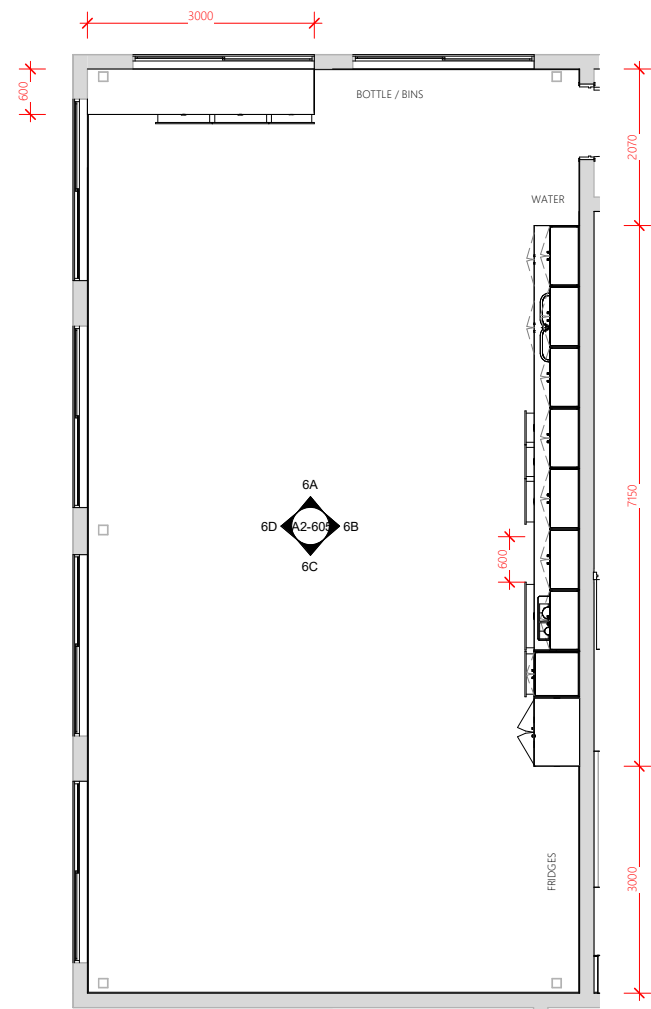

Joinery Plan 6

1 : 50

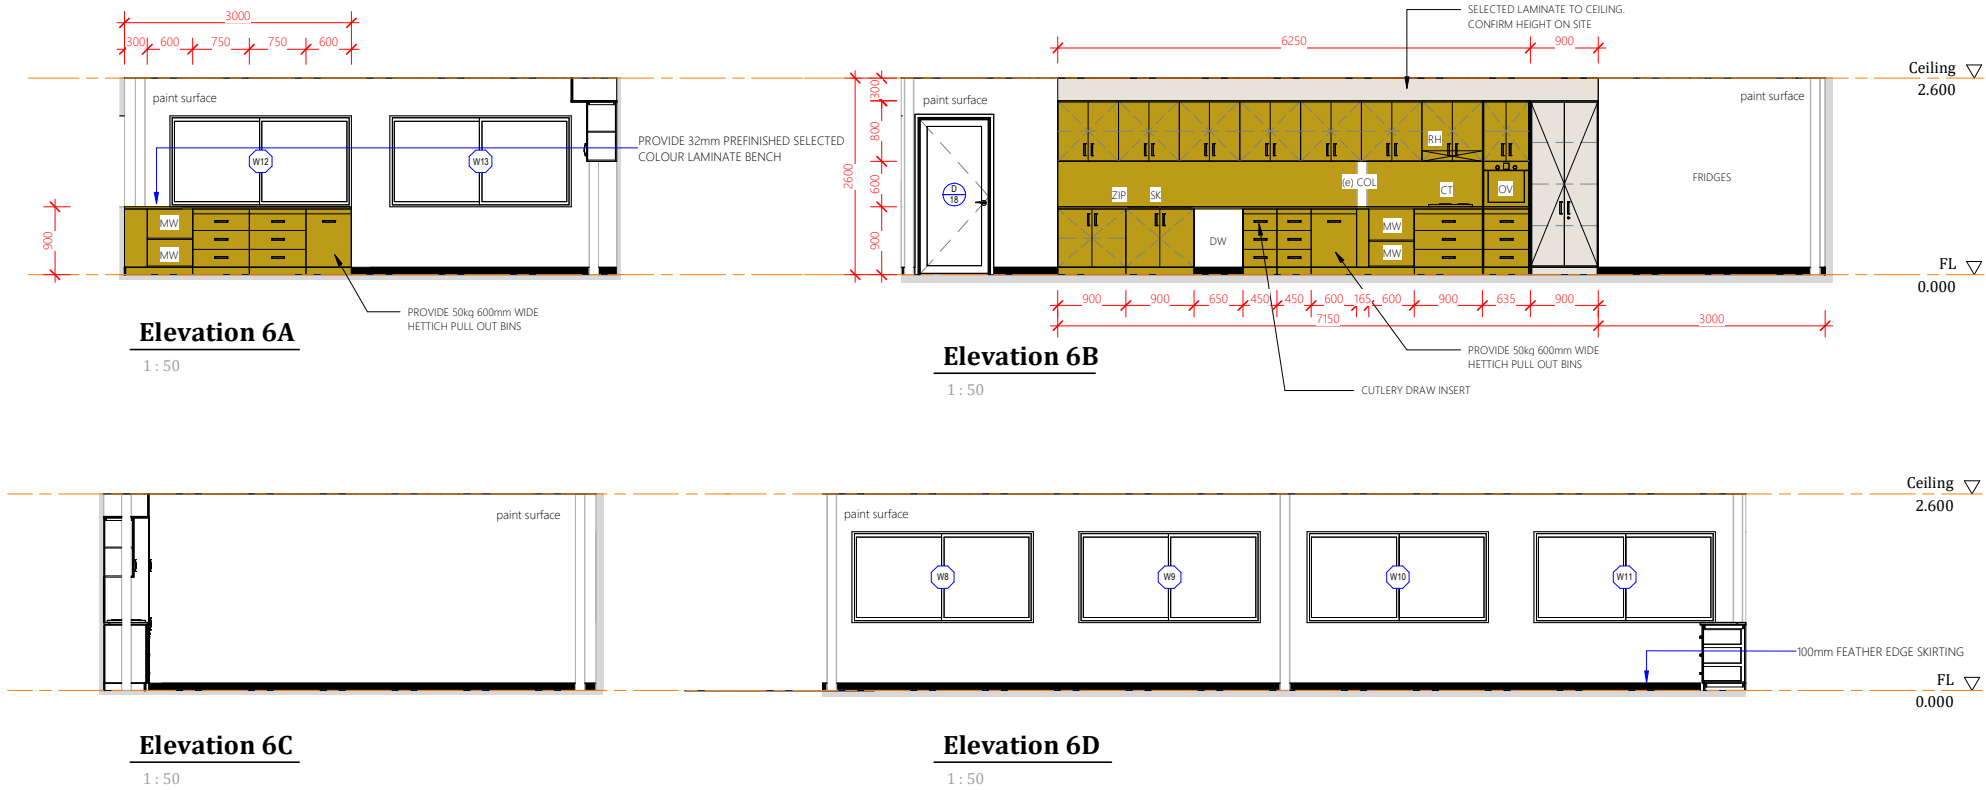

Elevation 6A

1 : 50

Elevation 6B

1 : 50

Elevation 6C

1 : 50

Elevation 6D

1 : 50

REVISIONS

Rev	Description	Date
T1	TENDER ISSUE	12.03.2026

DO NOT SCALE THIS DRAWINGS



TENDER ISSUE



Project Details
WAREHOUSE REFURB

Address
STANWELL POWER STATION

Drawing Title
INTERNAL ELEVATIONS 6 - LUNCH ROOM




0483 988 655 M
info@designelements.com.au E
QBCC No: 1247120 BDAQ No: 0001677

Scale: 1 : 50 Rev:
Date: MARCH 2026 T1
Drawn: Author

Project No: Drawing No:
25_003 A2-605




_Door Schedule	
DOOR NO.	Type Mark
1	TYPE A
2	TYPE A
3	TYPE H
4	TYPE D
5	TYPE D
6	TYPE E
7	TYPE E
8	TYPE A
9	TYPE E
10	TYPE G
11	TYPE G
12	TYPE H
13	TYPE H
14	TYPE H
15	TYPE I
16	TYPE E
18	TYPE D
19	TYPE F
20	TYPE F
21	TYPE H
22	TYPE H
23	TYPE H
24	TYPE H
25	TYPE H
26	TYPE H
27	TYPE H
28	TYPE D

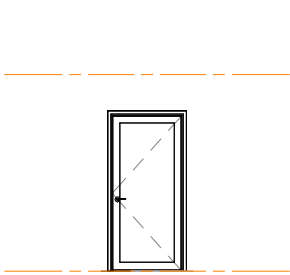


DOOR TYPE A

LOCATION: EXTERNAL
DOOR TYPE: HINGED ALUMINIUM FRAMED SINGLE DOOR
FRAME TYPE: G.JAMES 475 SERIES
FRAME FINISH: SELECTED POWDERCOAT
DOOR FINISH: SELECTED POWDERCOAT
INFILL: GREY SAFETY GLASS
THRESHOLD: REFER HARDWARE SCHEDULE
SEALS: REFER HARDWARE SCHEDULE
LOCK: REFER HARDWARE SCHEDULE
HARDWARE: DOOR CLOSER, DOOR STOP

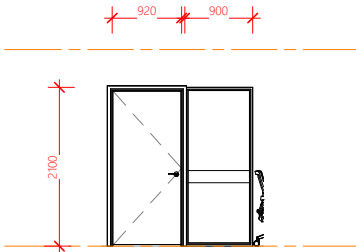


DOOR TYPE E

LOCATION: INTERNAL
DOOR TYPE: HINGED ALUMINIUM FRAMED SINGLE DOOR
FRAME TYPE: G.JAMES 475 SERIES
FRAME FINISH: SELECTED POWDERCOAT
DOOR FINISH: SELECTED POWDERCOAT
INFILL: GREY SAFETY GLASS
THRESHOLD:
SEALS:
LOCK: REFER HARDWARE SCHEDULE
HARDWARE: DOOR CLOSER, DOOR STOP

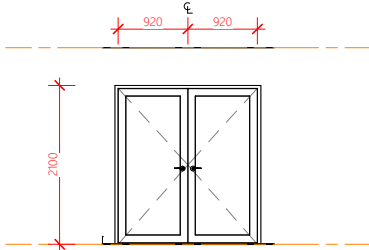


DOOR TYPE I

LOCATION: EXTERNAL
DOOR TYPE: HINGED ALUMINIUM FRAMED SINGLE DOOR
FRAME TYPE: G.JAMES 475 SERIES
FRAME FINISH: SELECTED POWDERCOAT
DOOR FINISH: SELECTED POWDERCOAT
INFILL: GREY SAFETY GLASS
THRESHOLD: REFER HARDWARE SCHEDULE
SEALS: REFER HARDWARE SCHEDULE
LOCK: REFER HARDWARE SCHEDULE
HARDWARE: DOOR CLOSER, DOOR STOP

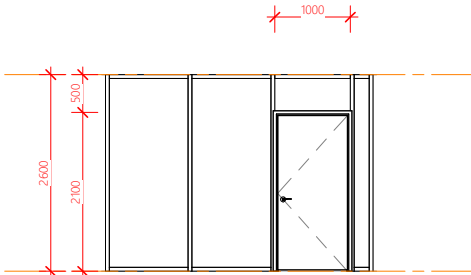


DOOR TYPE B

LOCATION: EXTERNAL
DOOR TYPE: HINGED ALUMINIUM FRAMED SINGLE DOOR
FRAME TYPE: G.JAMES 475 SERIES
FRAME FINISH: SELECTED POWDERCOAT
DOOR FINISH: SELECTED POWDERCOAT
INFILL: GREY SAFETY GLASS
THRESHOLD: REFER HARDWARE SCHEDULE
SEALS: REFER HARDWARE SCHEDULE
LOCK: REFER HARDWARE SCHEDULE
HARDWARE: DOOR CLOSER, DOOR STOP

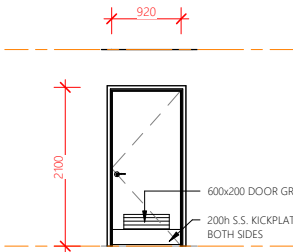

DOOR TYPE F


LOCATION: CLEANER / SERVICE
DOOR TYPE: 40mm HINGED SOLID CORE SINGLE DOOR
FRAME TYPE: TIMBER
FRAME FINISH: PAINT
DOOR FINISH: PAINT
SEALS: NONE
LOCK: REFER HARDWARE SCHEDULE
HARDWARE: KICK PLATES, DOOR CLOSER, DOOR STOP

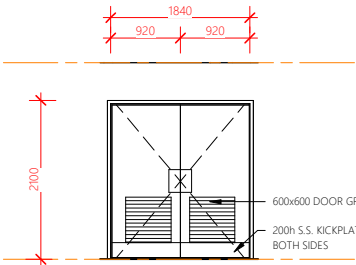

DOOR TYPE J


LOCATION: MALE AMENITIES
DOOR TYPE: 40mm HINGED DOULD CORE SINGLE DOOR
FRAME TYPE: TIMBER
FRAME FINISH: PAINT
DOOR FINISH: PAINT
SEALS: NONE
LOCK: PUSH PULL PLATES (NO LOCKING)
HARDWARE: KICK PLATES, DOOR CLOSER, DOOR STOP

CONFIRM EXISTING OPENING SIZE ON SITE AND ADVISE

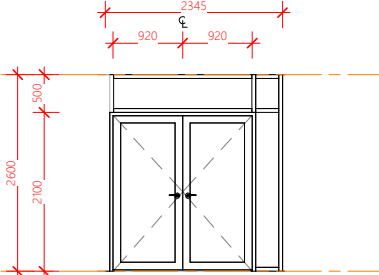


DOOR TYPE C

LOCATION: EXTERNAL
DOOR TYPE: HINGED ALUMINIUM FRAMED SINGLE DOOR
FRAME TYPE: G.JAMES 475 SERIES
FRAME FINISH: SELECTED POWDERCOAT
DOOR FINISH: SELECTED POWDERCOAT
INFILL: GREY SAFETY GLASS
THRESHOLD: REFER HARDWARE SCHEDULE
SEALS: REFER HARDWARE SCHEDULE
LOCK: REFER HARDWARE SCHEDULE
HARDWARE: DOOR CLOSER, DOOR STOP

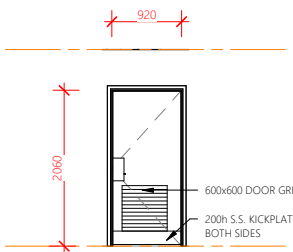


DOOR TYPE G

LOCATION: FEMALE AMENITIES
DOOR TYPE: 40mm HINGED SOLID CORE SINGLE DOOR
FRAME TYPE: TIMBER
FRAME FINISH: PAINT
DOOR FINISH: PAINT
SEALS: NONE
LOCK: PUSH PULL PLATES (NO LOCKING)
HARDWARE: KICK PLATES, DOOR CLOSER, DOOR STOP

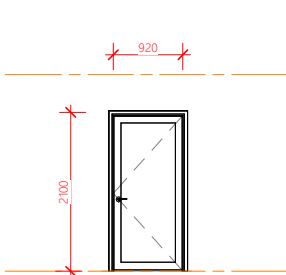

DOOR TYPE D

LOCATION: INTERNAL
DOOR TYPE: HINGED ALUMINIUM FRAMED SINGLE DOOR
FRAME TYPE: G.JAMES 475 SERIES
FRAME FINISH: SELECTED POWDERCOAT
DOOR FINISH: SELECTED POWDERCOAT
INFILL: GREY SAFETY GLASS
SEALS: NONE
LOCK: REFER HARDWARE SCHEDULE
HARDWARE: DOOR CLOSER, DOOR STOP

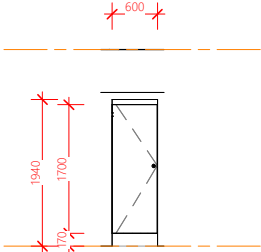

DOOR TYPE H

LOCATION: AMENITIES
DOOR TYPE: 13mm COMPACT LAMINATE PARTITION DOOR
FRAME TYPE: PROVIDE 30° PRIVACY BEVEL
DOOR FINISH: SELECTED LAMINATE
SEALS: NONE
LOCK: METLAM XCEL SLIDE LOCK & INDICATOR.
HARDWARE:

REVISIONS		
Rev	Description	Date
T1	TENDER ISSUE	12.03.2026

DO NOT SCALE THIS DRAWINGS



TENDER ISSUE



Project Details
WAREHOUSE REFURB
Address
STANWELL POWER STATION
Drawing Title
DOOR SCHEDULE



0483 988 655 M
info@dezignelements.com.au E
QBCC No: 1247120 BDAQ No: 0001677

Scale: 1 : 50	Rev:
Date: MARCH 2026	T1
Drawn: Author	
Project No:	Drawing No:
25_003	A2-700

13/03/2026 11:26:00 AM

_Window Schedule	
WINDOW NO.	Type Mark
1	TYPE A
2	TYPE A
3	TYPE B
4	TYPE C
5	TYPE D
6	TYPE E
7	TYPE E
8	TYPE F
9	TYPE F
10	TYPE F
11	TYPE F
12	TYPE F
13	TYPE F
14	TYPE G
15	TYPE H
16	TYPE I
17	TYPE J
18	TYPE J
19	

