





REVISIONS		
Rev	Description	Date
T1	TENDER ISSUE	12.03.2026

DO NOT SCALE THIS DRAWINGS

- CONFIRM HEIGHTS AND LEVELS ON SITE
- CONFIRM UNDERGROUND SERVICES ON SITE
- CONFIRM ALL DIMENSION ON SITE
- CONFIRM ALL WINDOW AND DOOR OPENING SIZES ON SITE

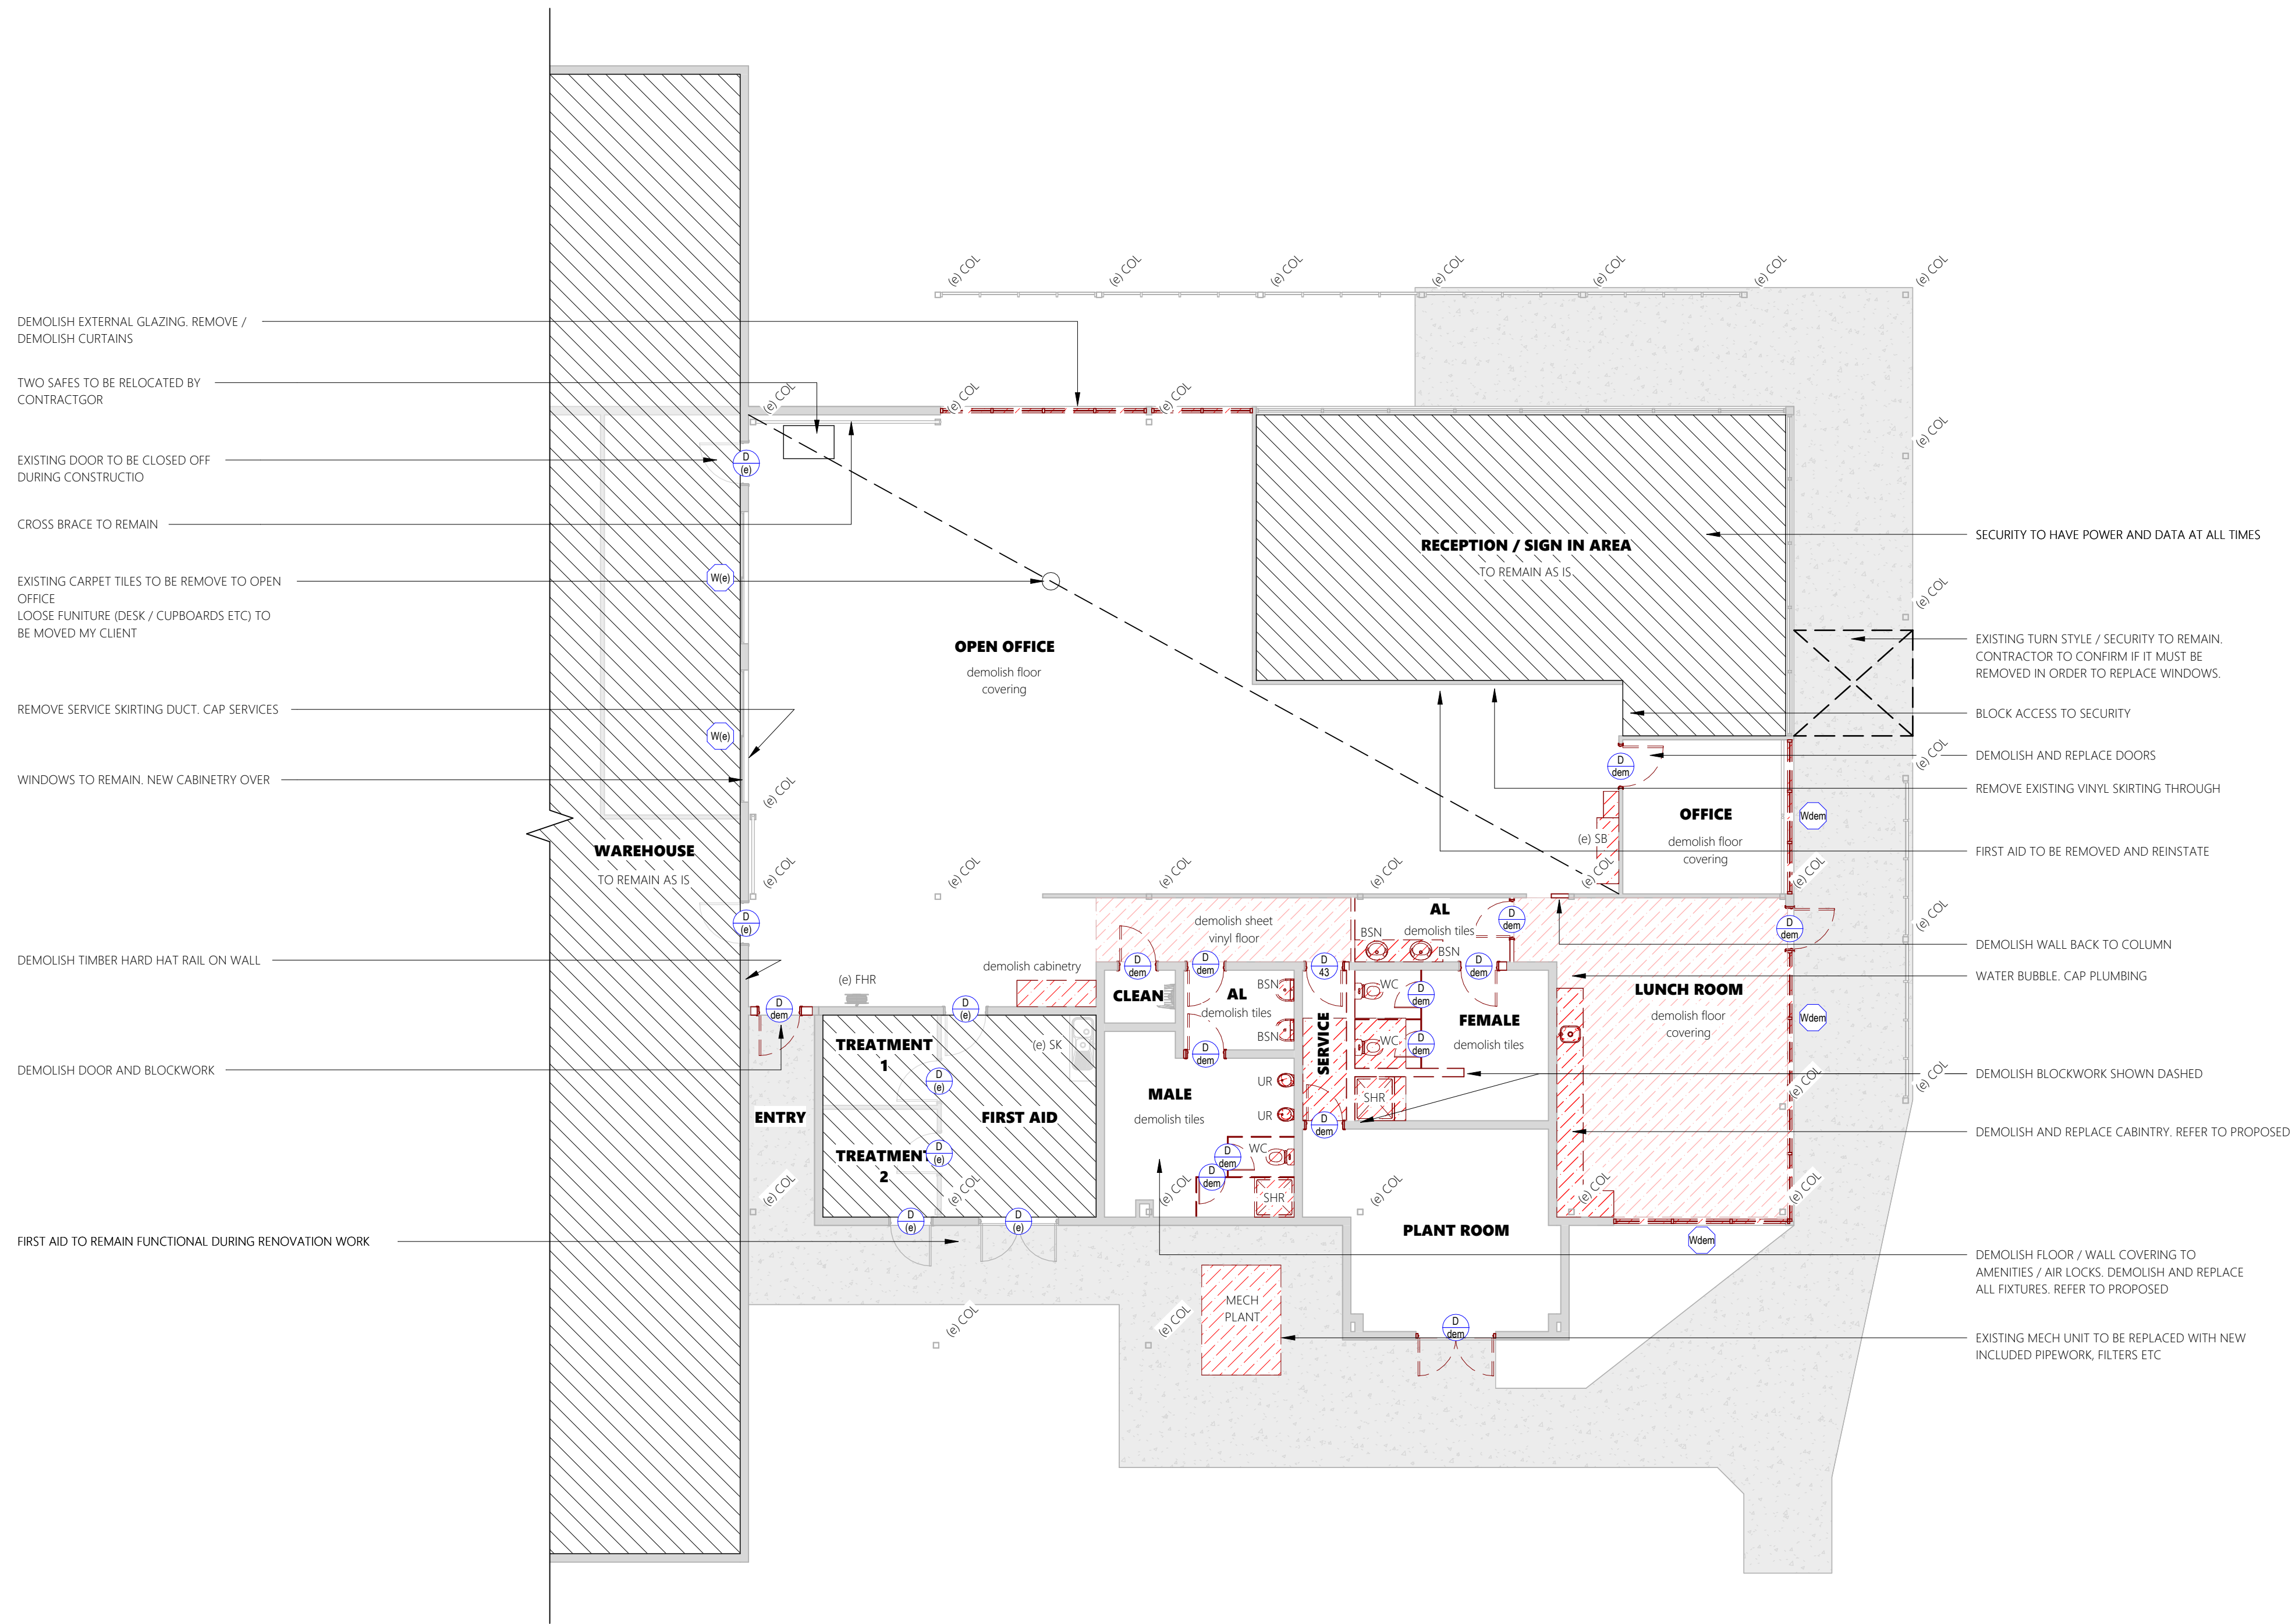

Existing Warehouse Floor Plan

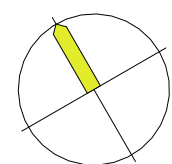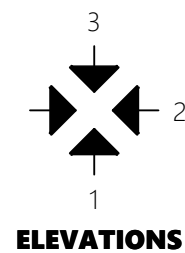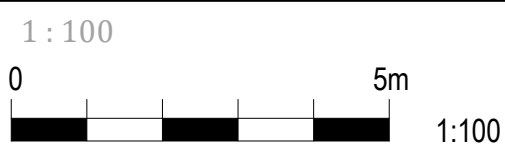

0483 988 655 M
info@designelements.com.au E
QBCC No: 1247120 BDAQ No: 0001677

Scale: 1 : 100 Rev:
Date: JAN 2025 T1
Drawn: NJB

Project No: Drawing No:
25_003 A3-201

12/03/2026 6:53:41 PM

REVISIONS		
Rev	Description	Date
T1	TENDER ISSUE	12.03.2026

DO NOT SCALE THIS DRAWINGS

TENDER ISSUE

Client



Project Details

MAIN WAREHOUSE
REFURBISHMENT

Address

STANWELL POWER
STATION

Drawing Title



EXISTING SLAB PLAN


BUILDING DESIGNERS

0483 988 655 
info@deziignelements.com.au 


QBCC No: 1247120 BDAQ No: 0001677

Scale: 1 : 100 Rev: **T1**
Date: JAN 2025
Drawn: Author
Project No: 25_003 Drawing No: A3-202

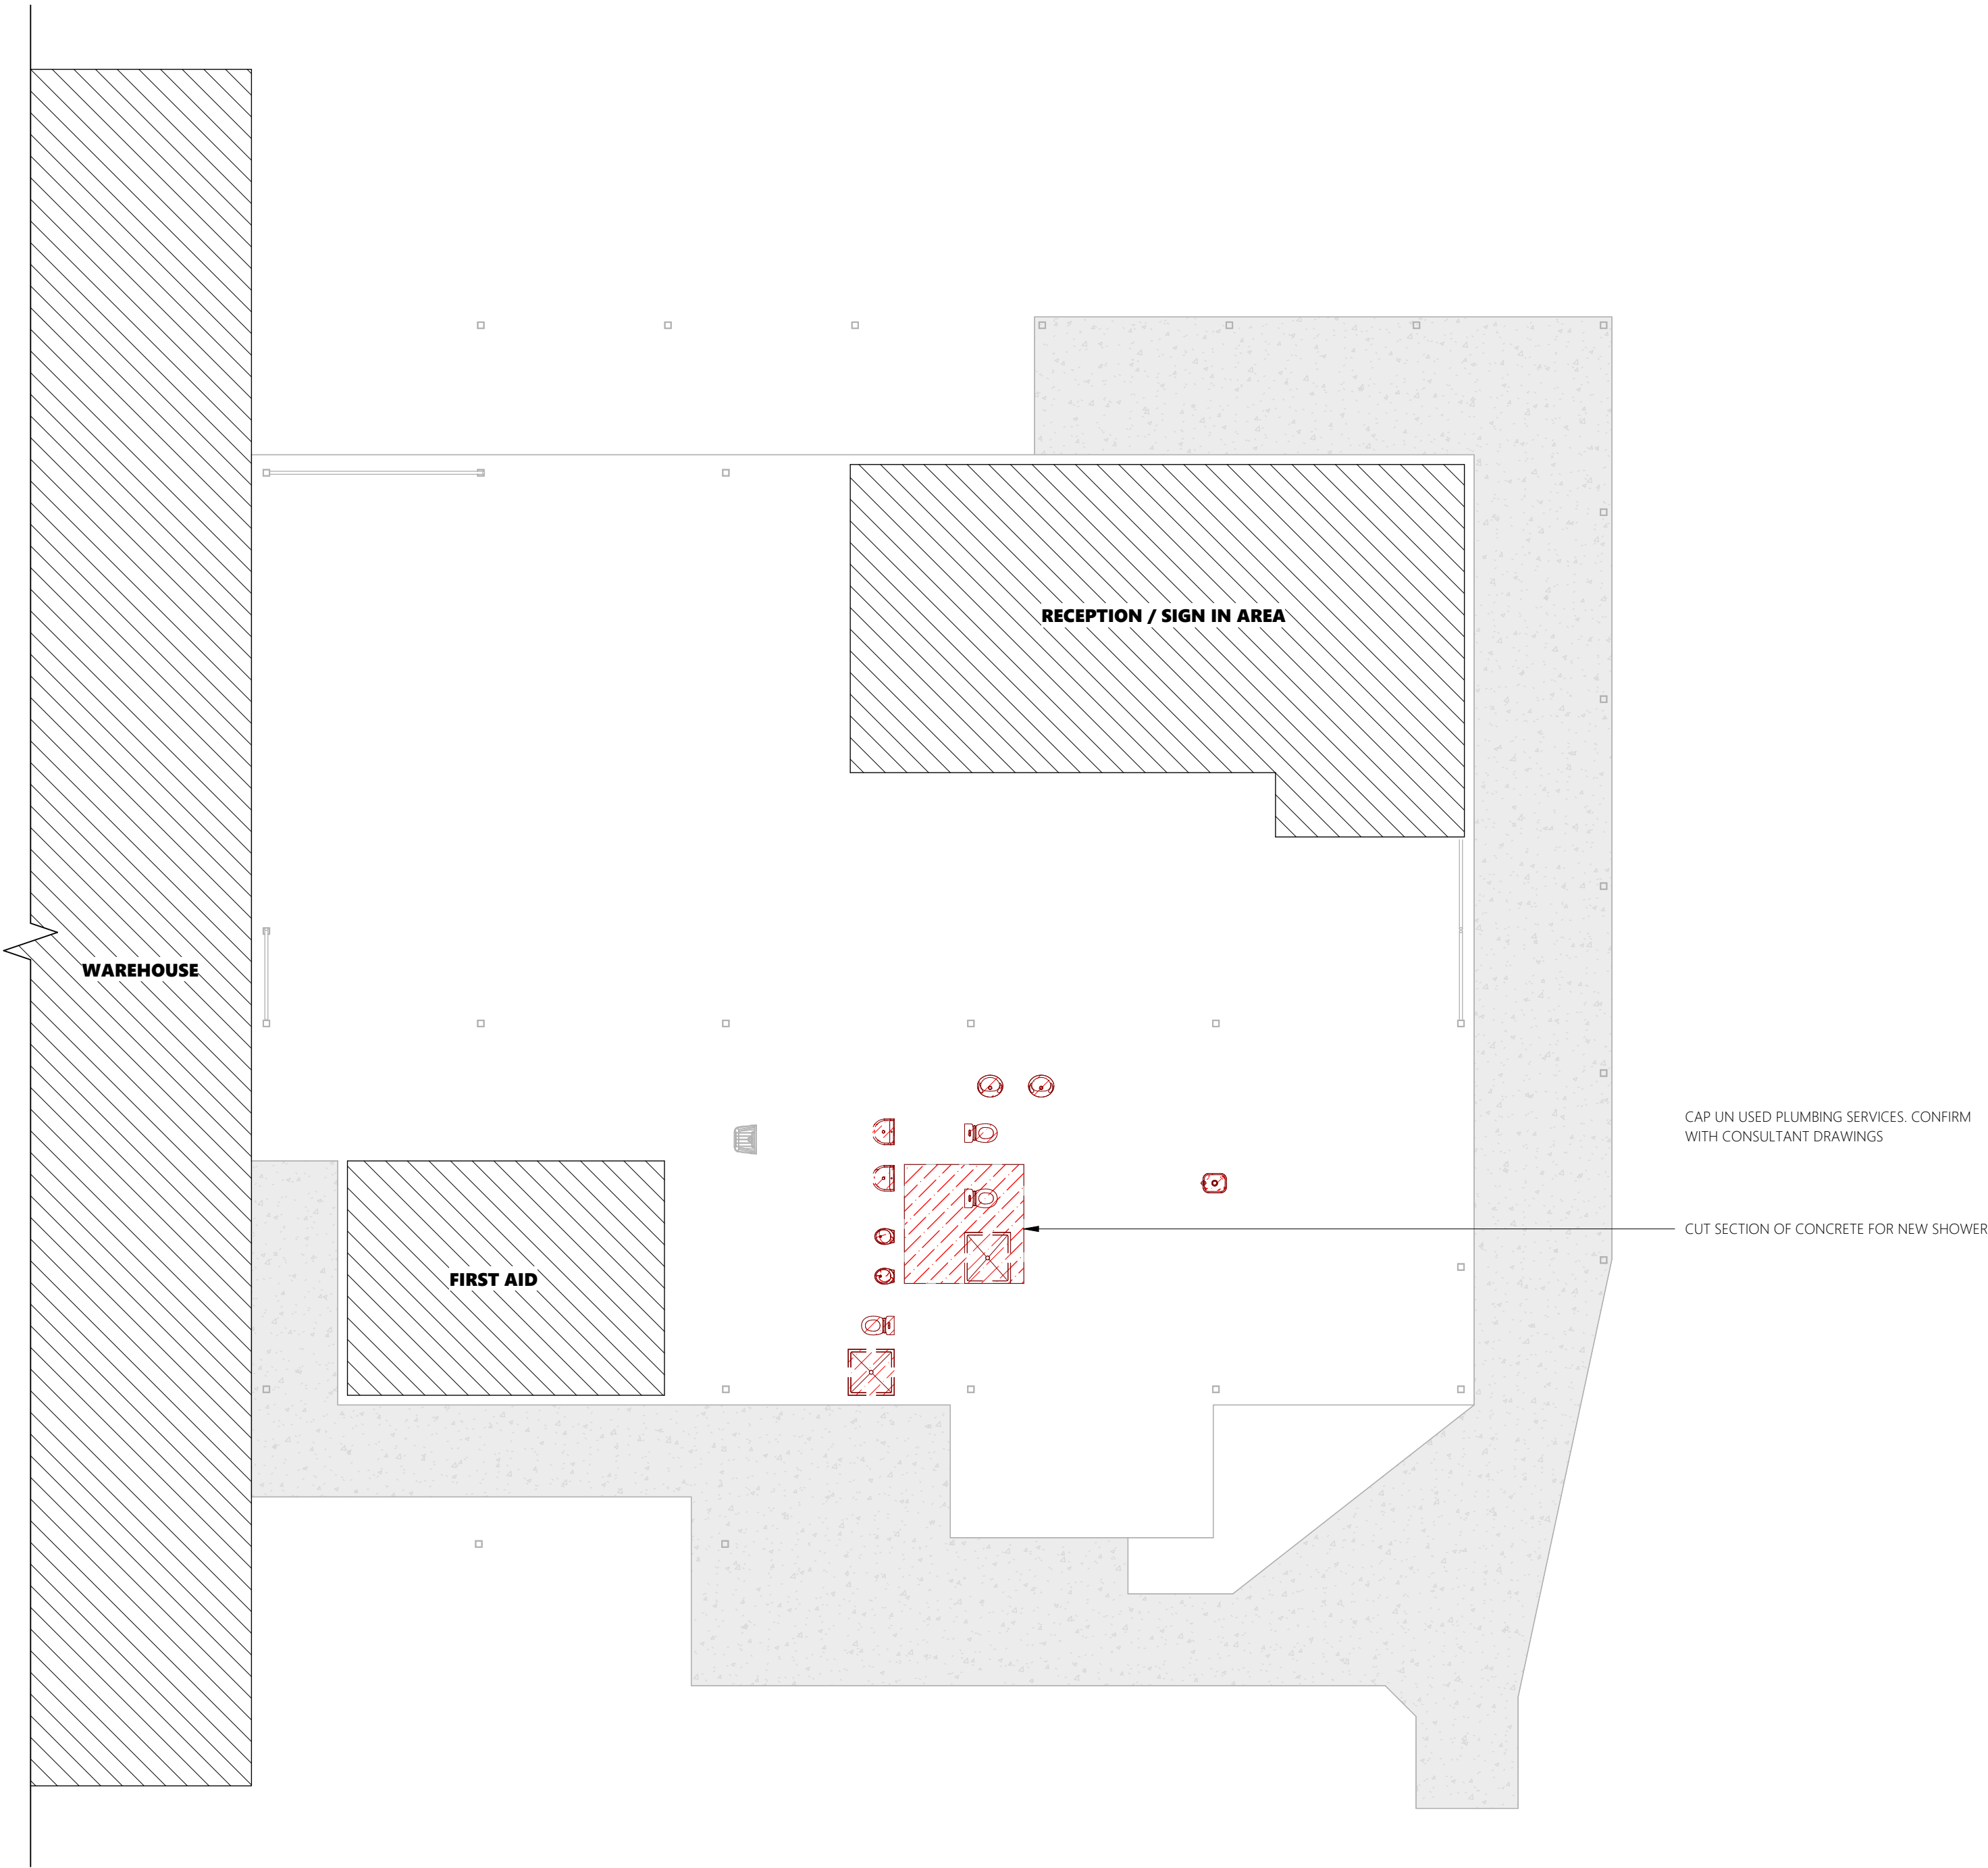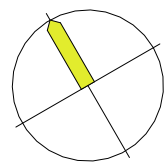

Existing Slab Plan


1 : 100

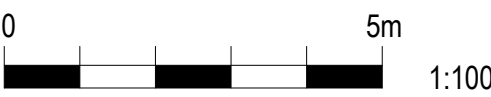

LIGHTS AND AC FIXTURES SHOWN FOR INDICATION ONLY. CONFIRM ON SITE AND READ IN CONJUNCTION WITH CONSULTANT DRAWINGS


REVISIONS		
Rev	Description	Date
T1	TENDER ISSUE	12.03.2026

DO NOT SCALE THIS DRAWINGS

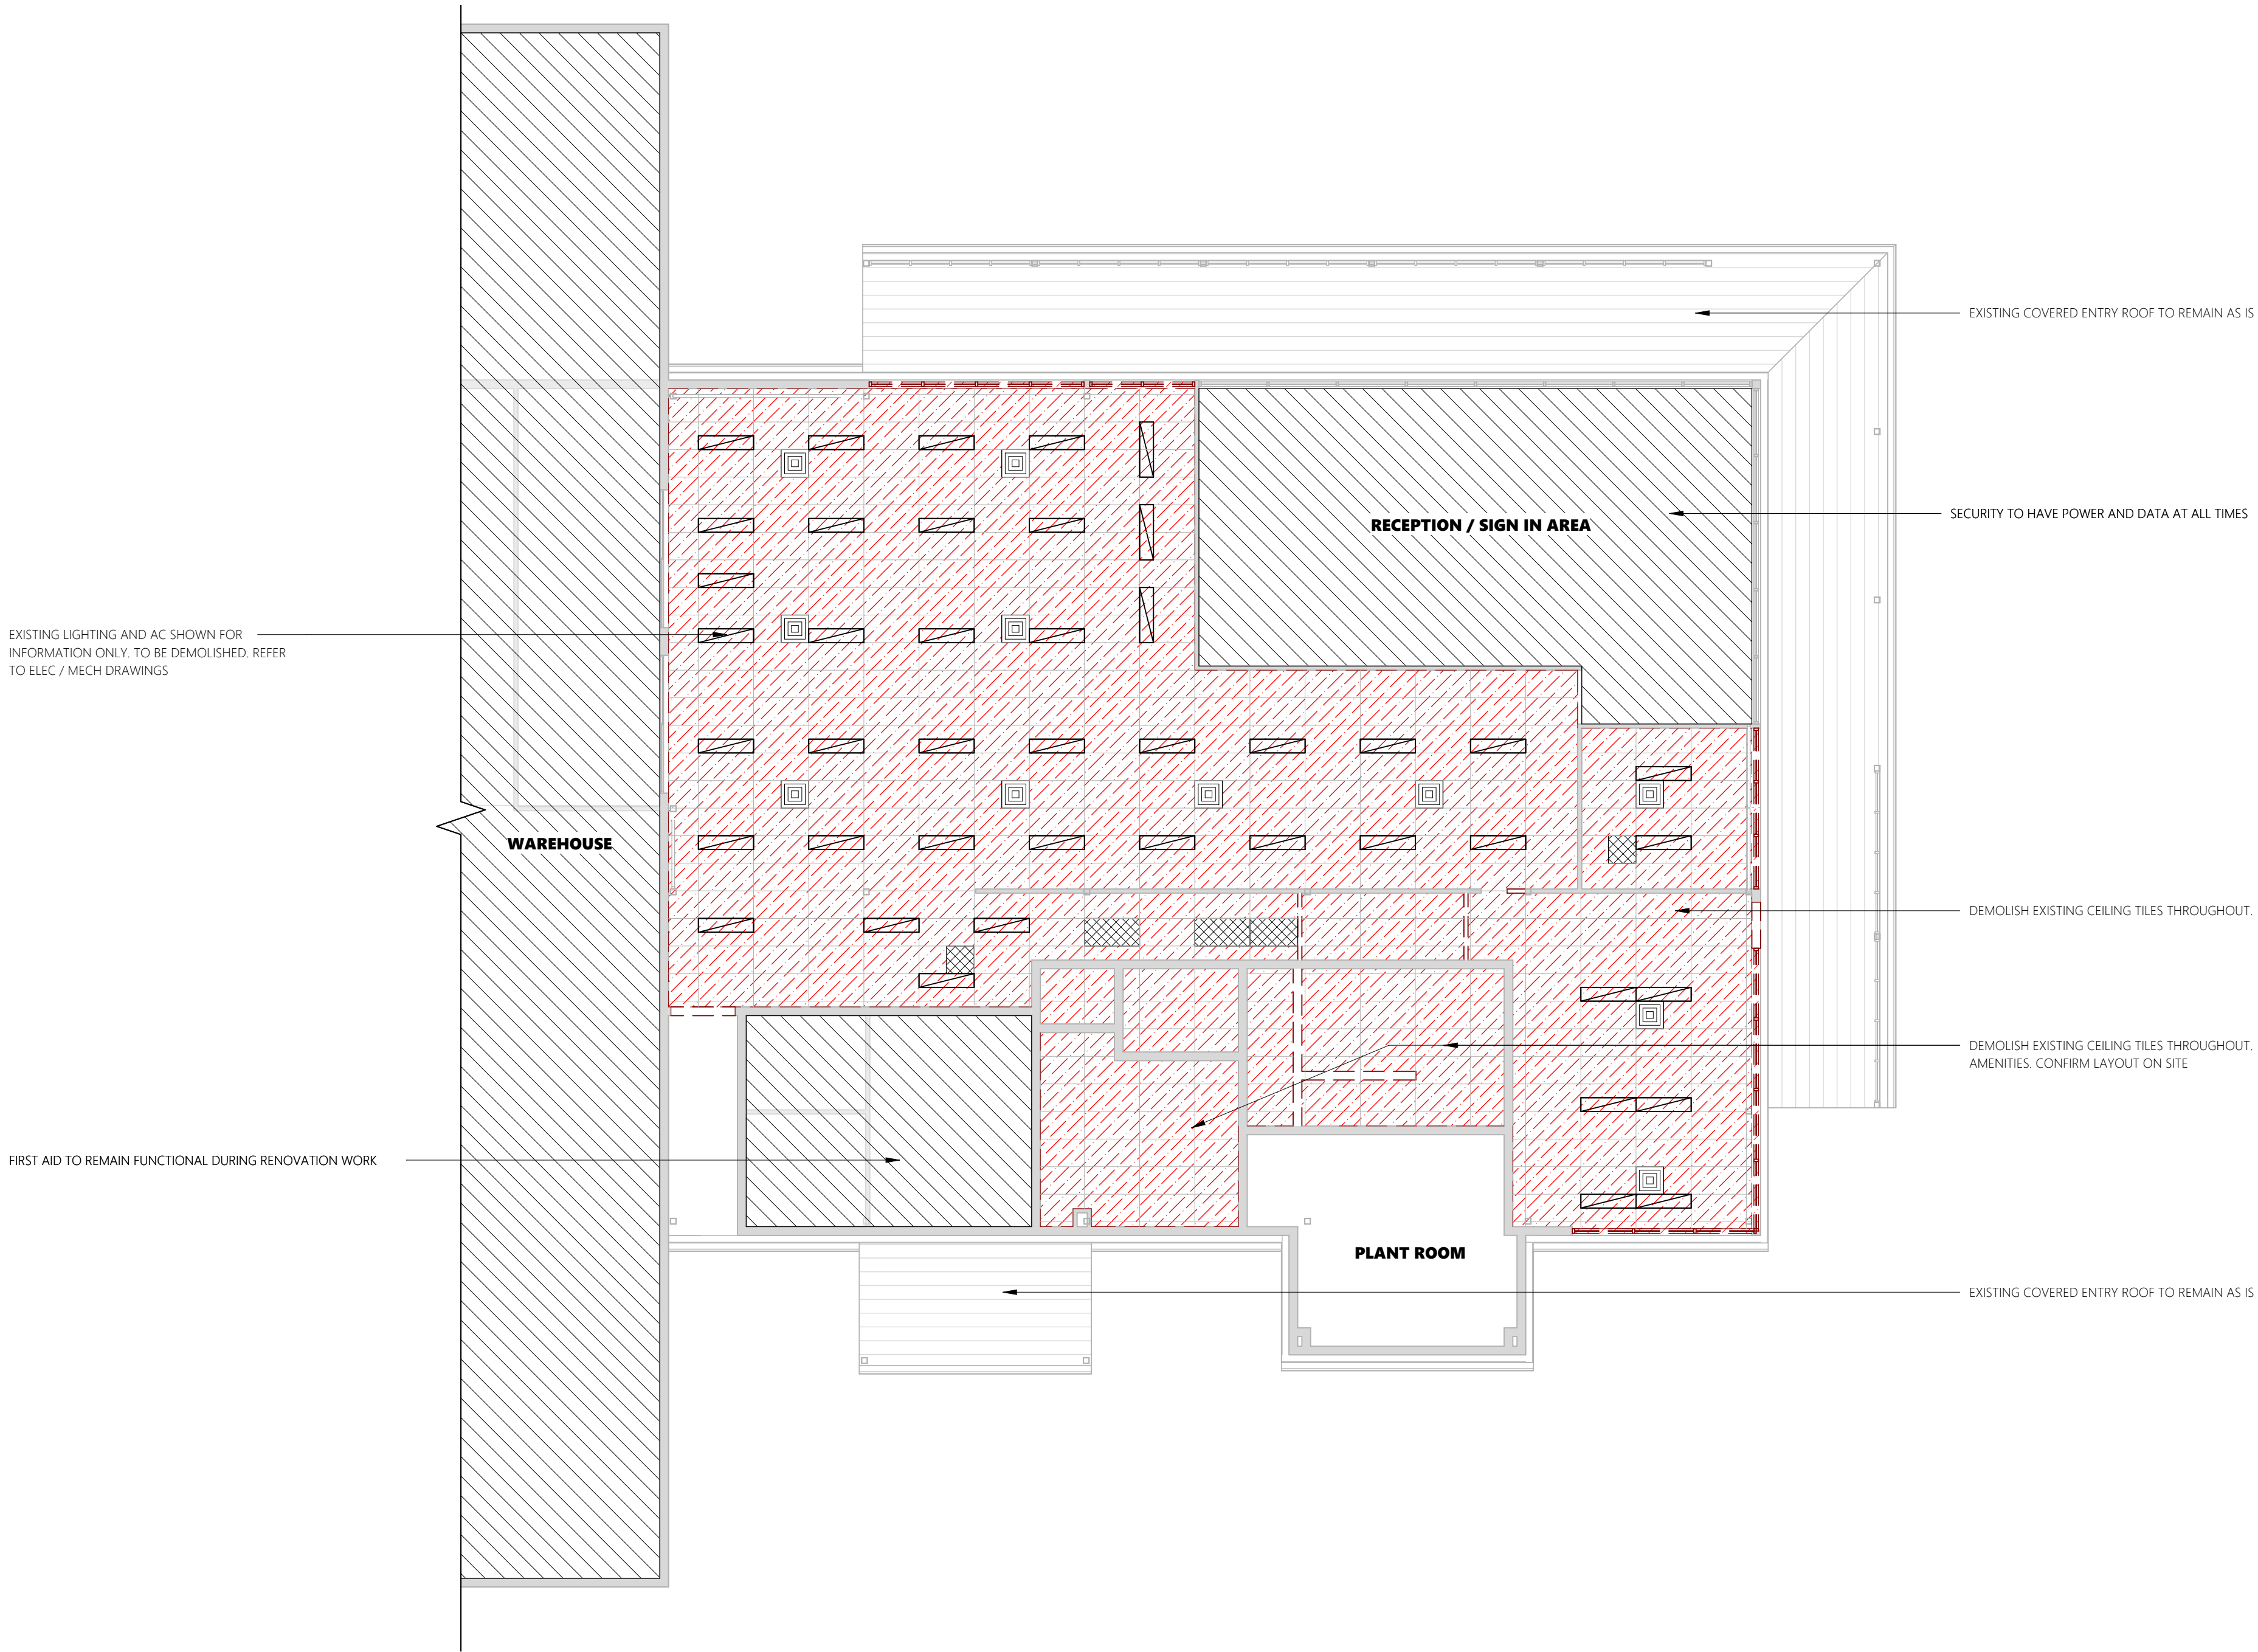

Existing Ceiling Plan

1 : 100

 

TENDER ISSUE

Client



Project Details

MAIN WAREHOUSE REFURBISHMENT

Address

STANWELL POWER STATION

Drawing Title


EXISTING CEILING PLAN



0483 988 655 **M**
info@designelements.com.au **E**
QBCC No: 1247120 BDAQ No: 0001677


Scale:	1 : 100	Rev:	
Date:	JAN 2025		T1
Drawn:	Author		
Project No:		Drawing No:	
25_003		A3-203	

12/03/2026 6:53:42 PM

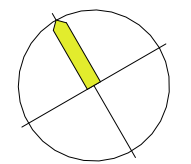

REVISIONS		
Rev	Description	Date
T1	TENDER ISSUE	12.03.2026

DO NOT SCALE THIS DRAWINGS

 

TENDER ISSUE

Client



Project Details

MAIN WAREHOUSE
REFURBISHMENT

Address

STANWELL POWER
STATION


Drawing Title

EXISTING ROOF PLAN



0483 988 655 
info@deziignelements.com.au 
QBCC No: 1247120 BDAQ No: 0001677

Scale: 1 : 100 Rev: **T1**
Date: JAN 2025
Drawn: Author
Project No: 25_003 Drawing No: A3-204

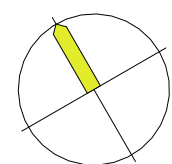

Existing Roof Plan



REVISIONS		
Rev	Description	Date
T1	TENDER ISSUE	12.03.2026

DO NOT SCALE THIS DRAWINGS



TENDER ISSUE

Client



Project Details

**MAIN WAREHOUSE
REFURBISHMENT**

Address

**STANWELL POWER
STATION**

Drawing Title

EXISTING ELEVATIONS



0483 988 655 
info@designelements.com.au 
QBCC No: 1247120 BDAQ No: 0001677


Scale: 1 : 100 Rev: **T1**
Date: JAN 2025
Drawn: Author
Project No: Drawing No:
25_003 A3-205

12/03/2026 6:53:48 PM



Existing Elevation 1

1 : 100

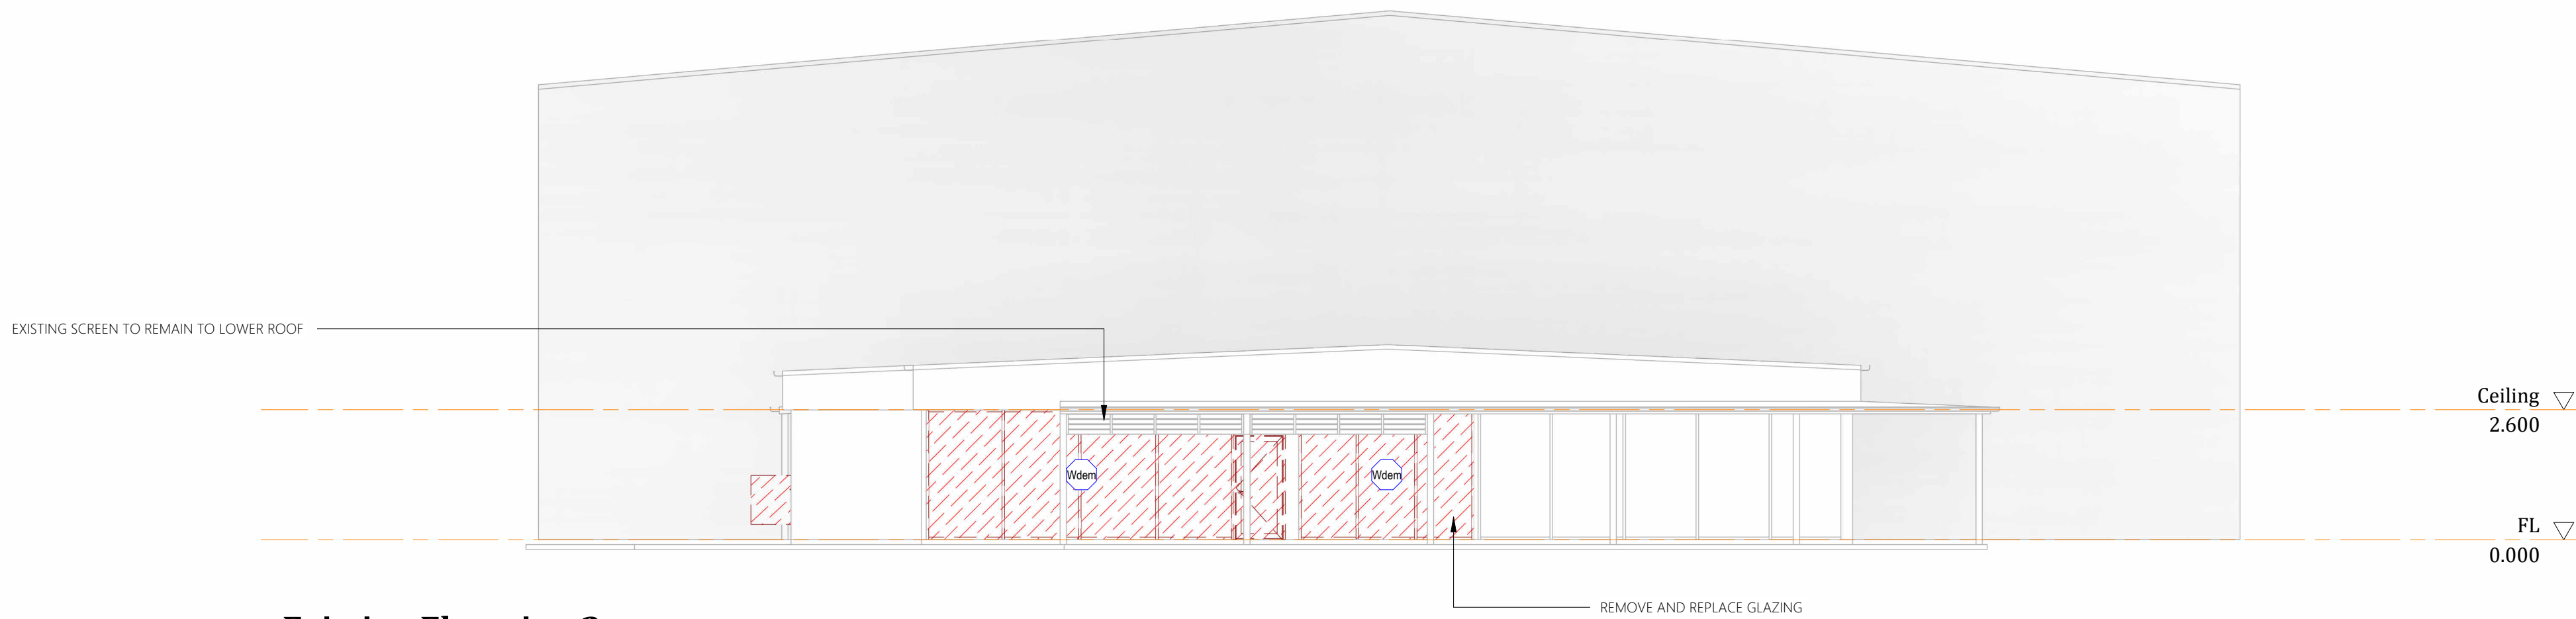

Existing Elevation 2

1 : 100



Existing Elevation 3


1 : 100

REVISIONS		
Rev	Description	Date
T1	TENDER ISSUE	12.03.2026

DO NOT SCALE THIS DRAWINGS


KEYNOTE LEGEND

(e)	Existing
dem	Demolish
(R)	Remove / Reinstate
BSN	Basin
COL	Column
CON	Condenser
CPD	Cupboard
CS	Cleaners Sink
CT	Cooktop
DP	Downpipe
DW	Dish Washer
FAP	Fire Alarm Panel
FHR	Fire Hose Reel
FR	Fridge (By Client)
HD	Hand Driver (Air Blade)
L	Locker
OV	Oven
RH	Range Hood
DW	Dish Washer
SK	Sink
SB	Switch Board
UR	Urinal

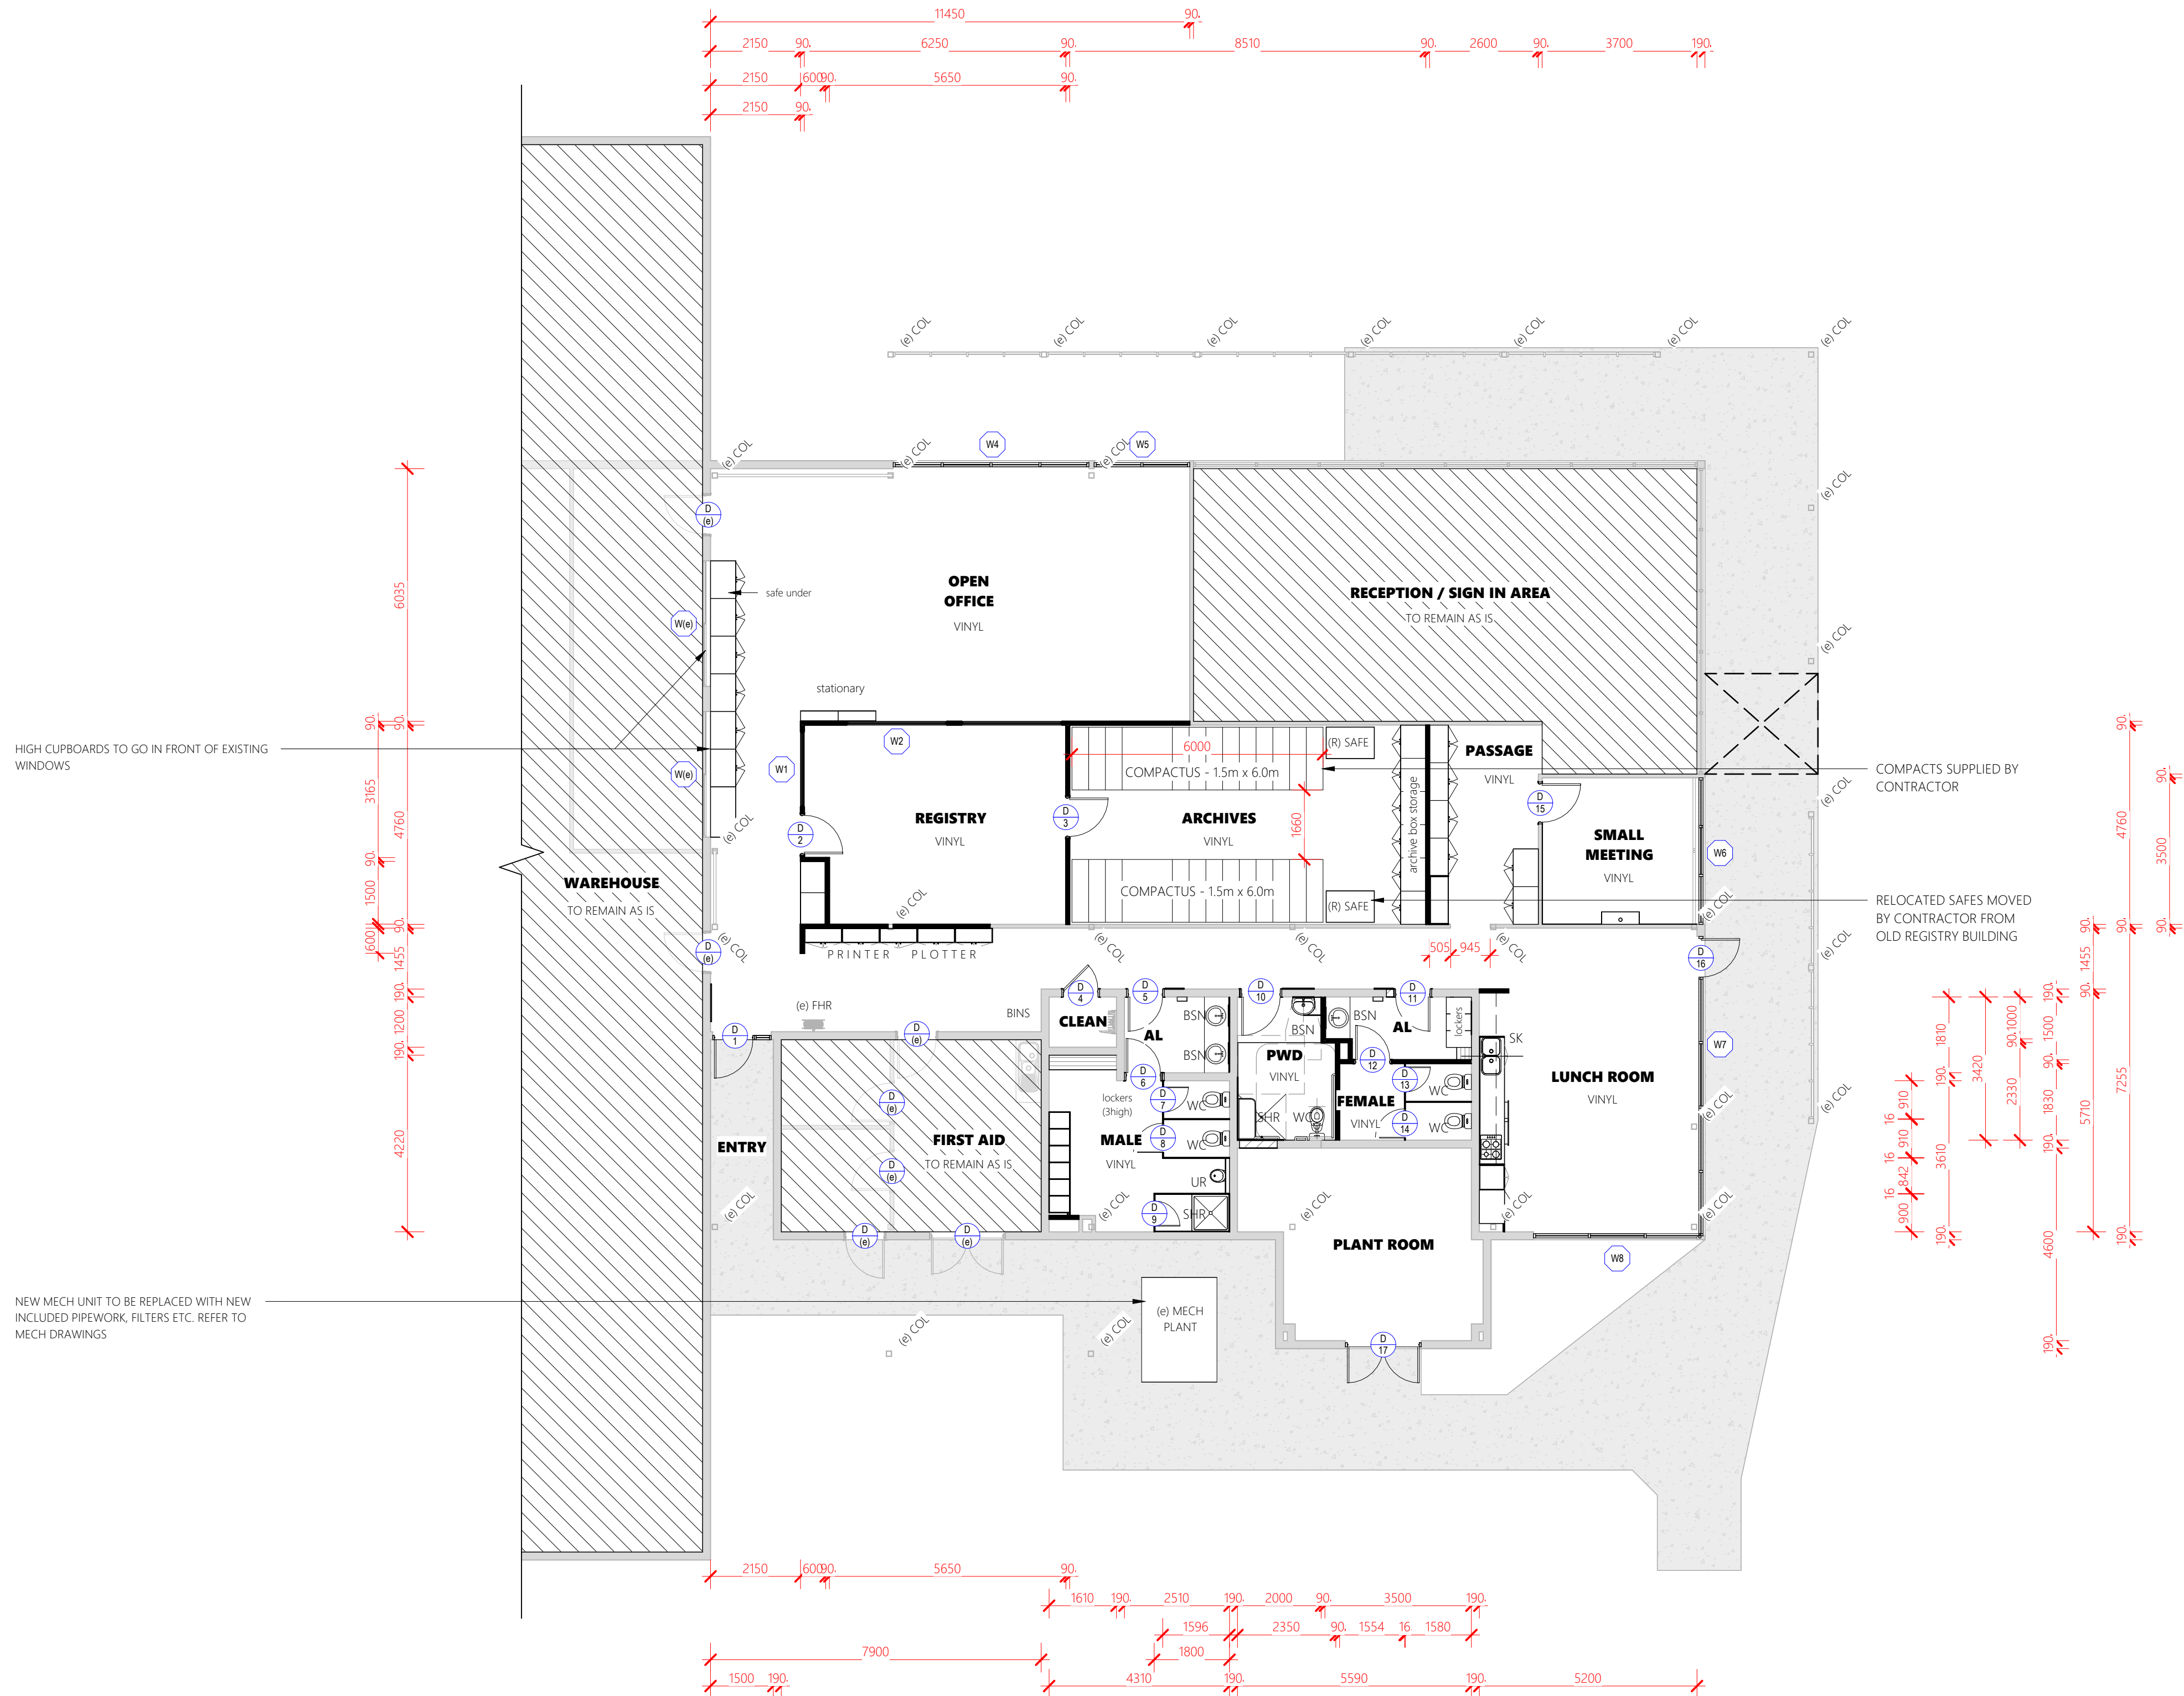

Proposed Warehouse Floor Plan

1 : 100

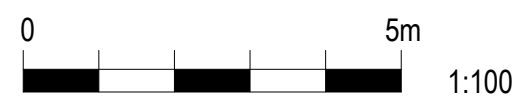

TENDER ISSUE




Project Details
MAIN WAREHOUSE REFURBISHMENT
Address
STANWELL POWER STATION
Drawing Title
PROPOSED FLOOR PLAN



0483 988 655 
info@designelements.com.au 
QBCC No: 1247120 BDAQ No: 0001677

Scale: 1 : 100 Rev: **T1**
Date: JAN 2025
Drawn: Author
Project No: Drawing No:
25_003 A3-300

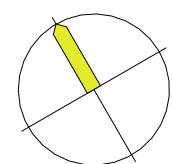

REVISIONS		
Rev	Description	Date
T1	TENDER ISSUE	12.03.2026

DO NOT SCALE THIS DRAWINGS

TENDER ISSUE

Client



Project Details

**MAIN WAREHOUSE
REFURBISHMENT**

Address

**STANWELL POWER
STATION**



Drawing Title

PROPOSED SLAB PLAN



0483 988 655 
info@deziignelements.com.au 
QBCC No: 1247120 BDAQ No: 0001677

Scale: 1 : 100 Rev: **T1**
Date: JAN 2025
Drawn: Author
Project No: 25_003 Drawing No: **A3-301**

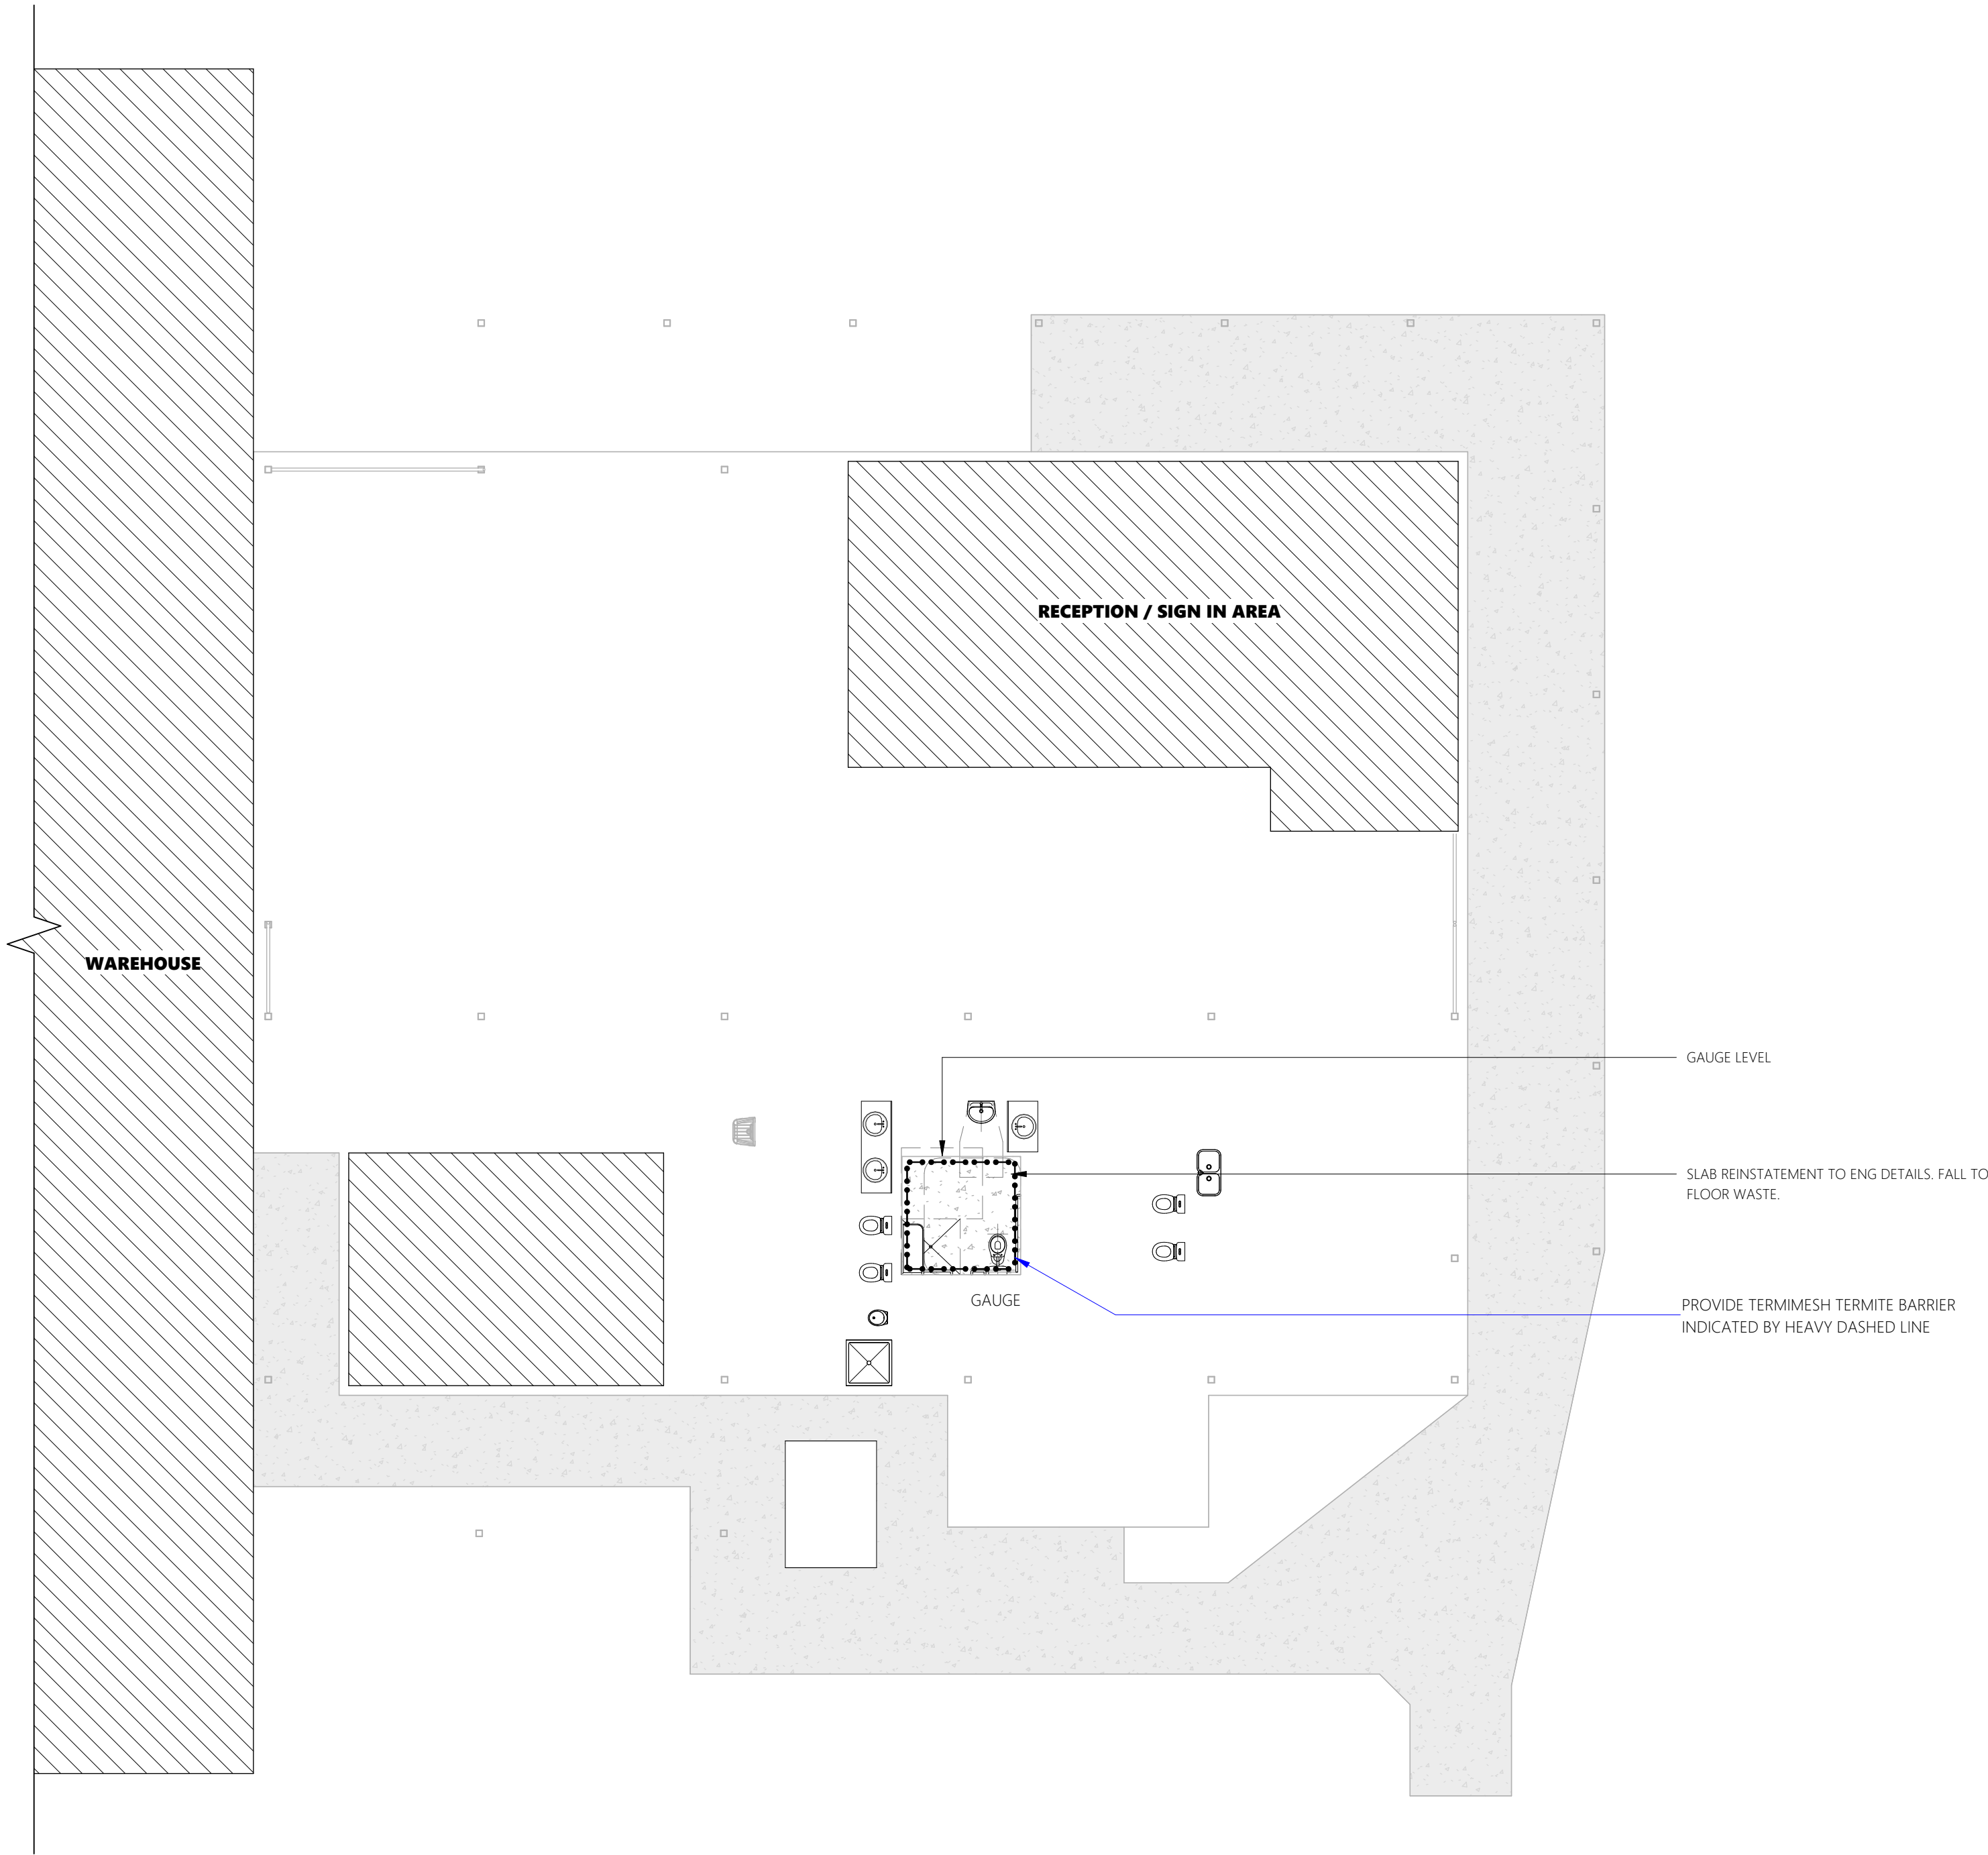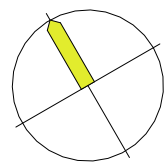


_Proposed Slab Plan
1 : 100
0 5m 1:100

CONFIRM EXISTING GRID SETOUT ON SITE

NEW CEILING INSULATION THROUGHOUT
SHADED AREA - REFER SPEC


CEILING LEGEND

- 1200 x 600 APEX ACOUSTIC CEILING
TILES (OR APPROVED EQUAL - NEW
TILES THROUGH RENOVATED AREA)
- PROVIDE CONCEALED FIX RIBBEDTRIMDEK
SOFFIT SHEETING (TO MATCH EXISTING)
- INSULATION ABOVE CEILING TILES

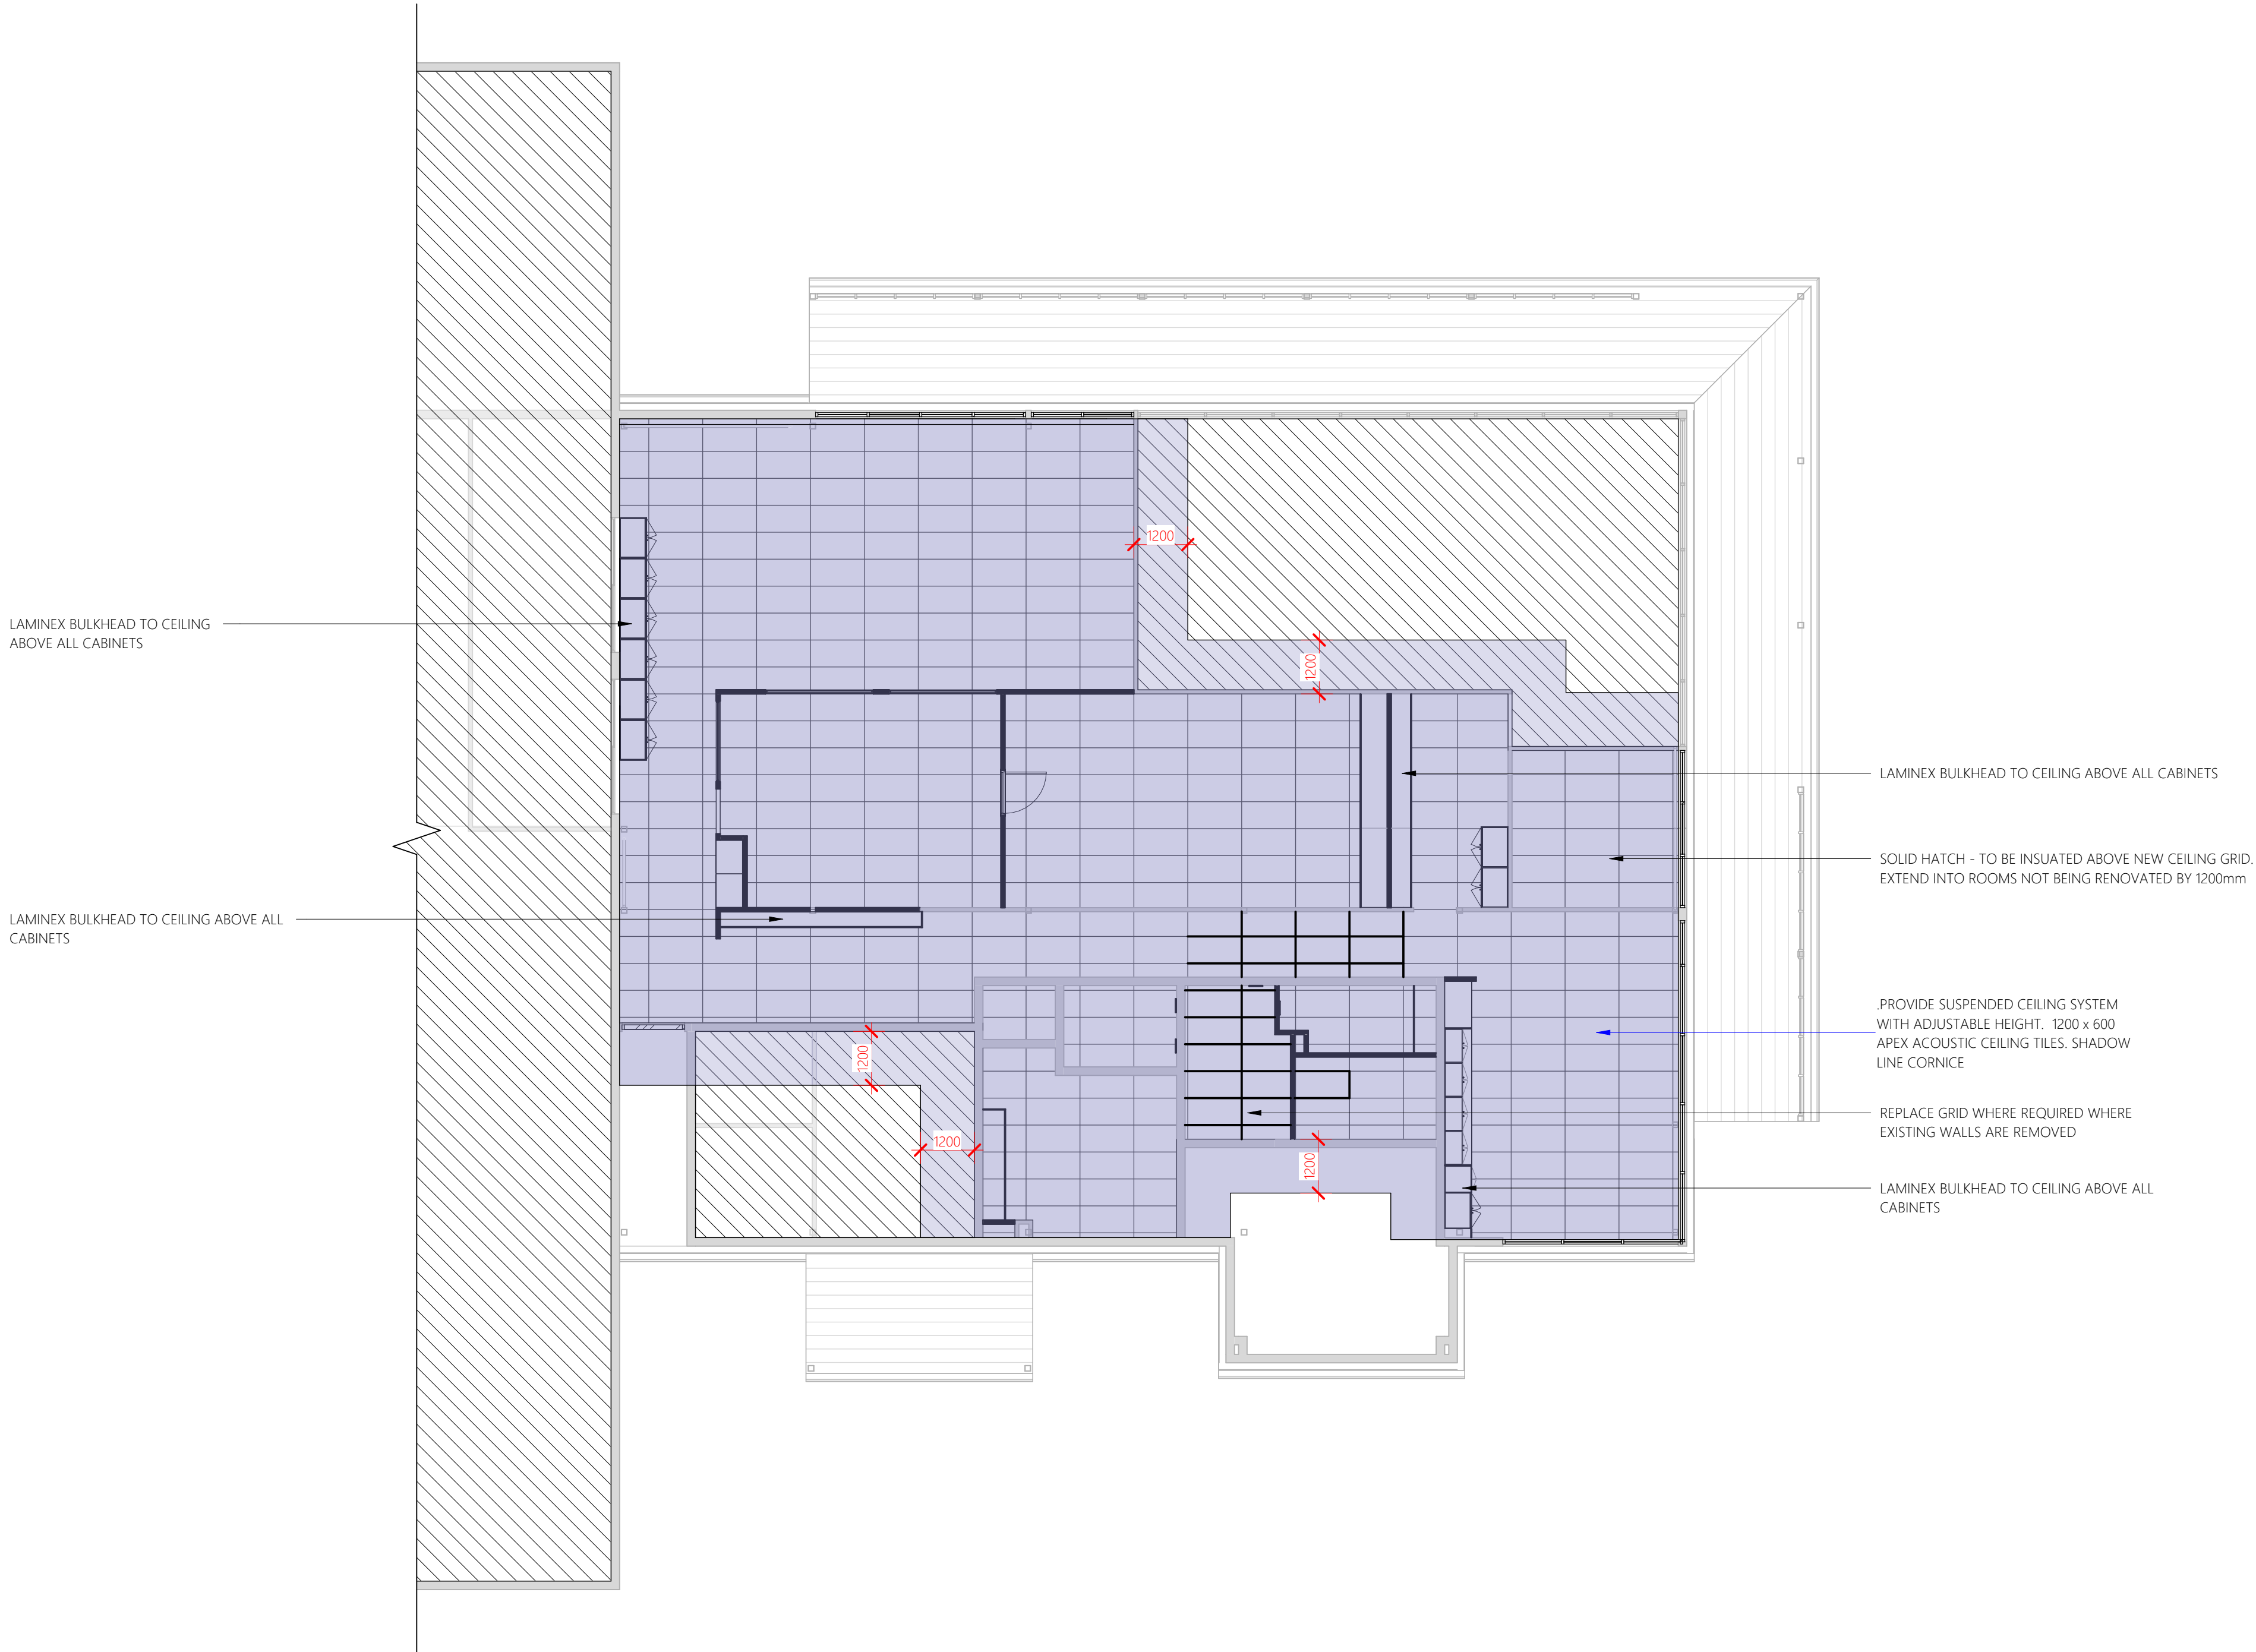

Proposed Ceiling Plan


1 : 100

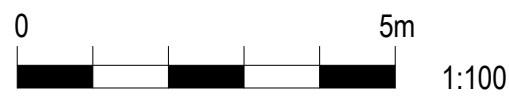

REVISIONS

Rev	Description	Date
T1	TENDER ISSUE	12.03.2026

DO NOT SCALE THIS DRAWINGS

 

TENDER ISSUE

Client



Project Details

**MAIN WAREHOUSE
REFURBISHMENT**

Address

**STANWELL POWER
STATION**


Drawing Title

PROPOSED CEILING PLAN



0483 988 655 
info@designelements.com.au 
QBCC No: 1247120 BDAQ No: 0001677

Scale: 1 : 100 Rev: **T1**
Date: JAN 2025
Drawn: Author
Project No: Drawing No:
25_003 A3-302

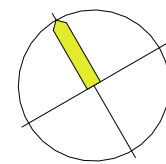

REVISIONS		
Rev	Description	Date
T1	TENDER ISSUE	12.03.2026

DO NOT SCALE THIS DRAWINGS

TENDER ISSUE

Client

 **stanwell**

Project Details

**MAIN WAREHOUSE
REFURBISHMENT**

Address

**STANWELL POWER
STATION**

Drawing Title

PROPOSED ROOF PLAN



0483 988 655

info@dezi elements.com.au

QBCC No: 1247120 BDAQ No: 0001677

Scale: 1 : 100

Date: JAN 2025

Drawn: Author

Rev:


T1










Project No:

Drawing No:


25_003

A3-303

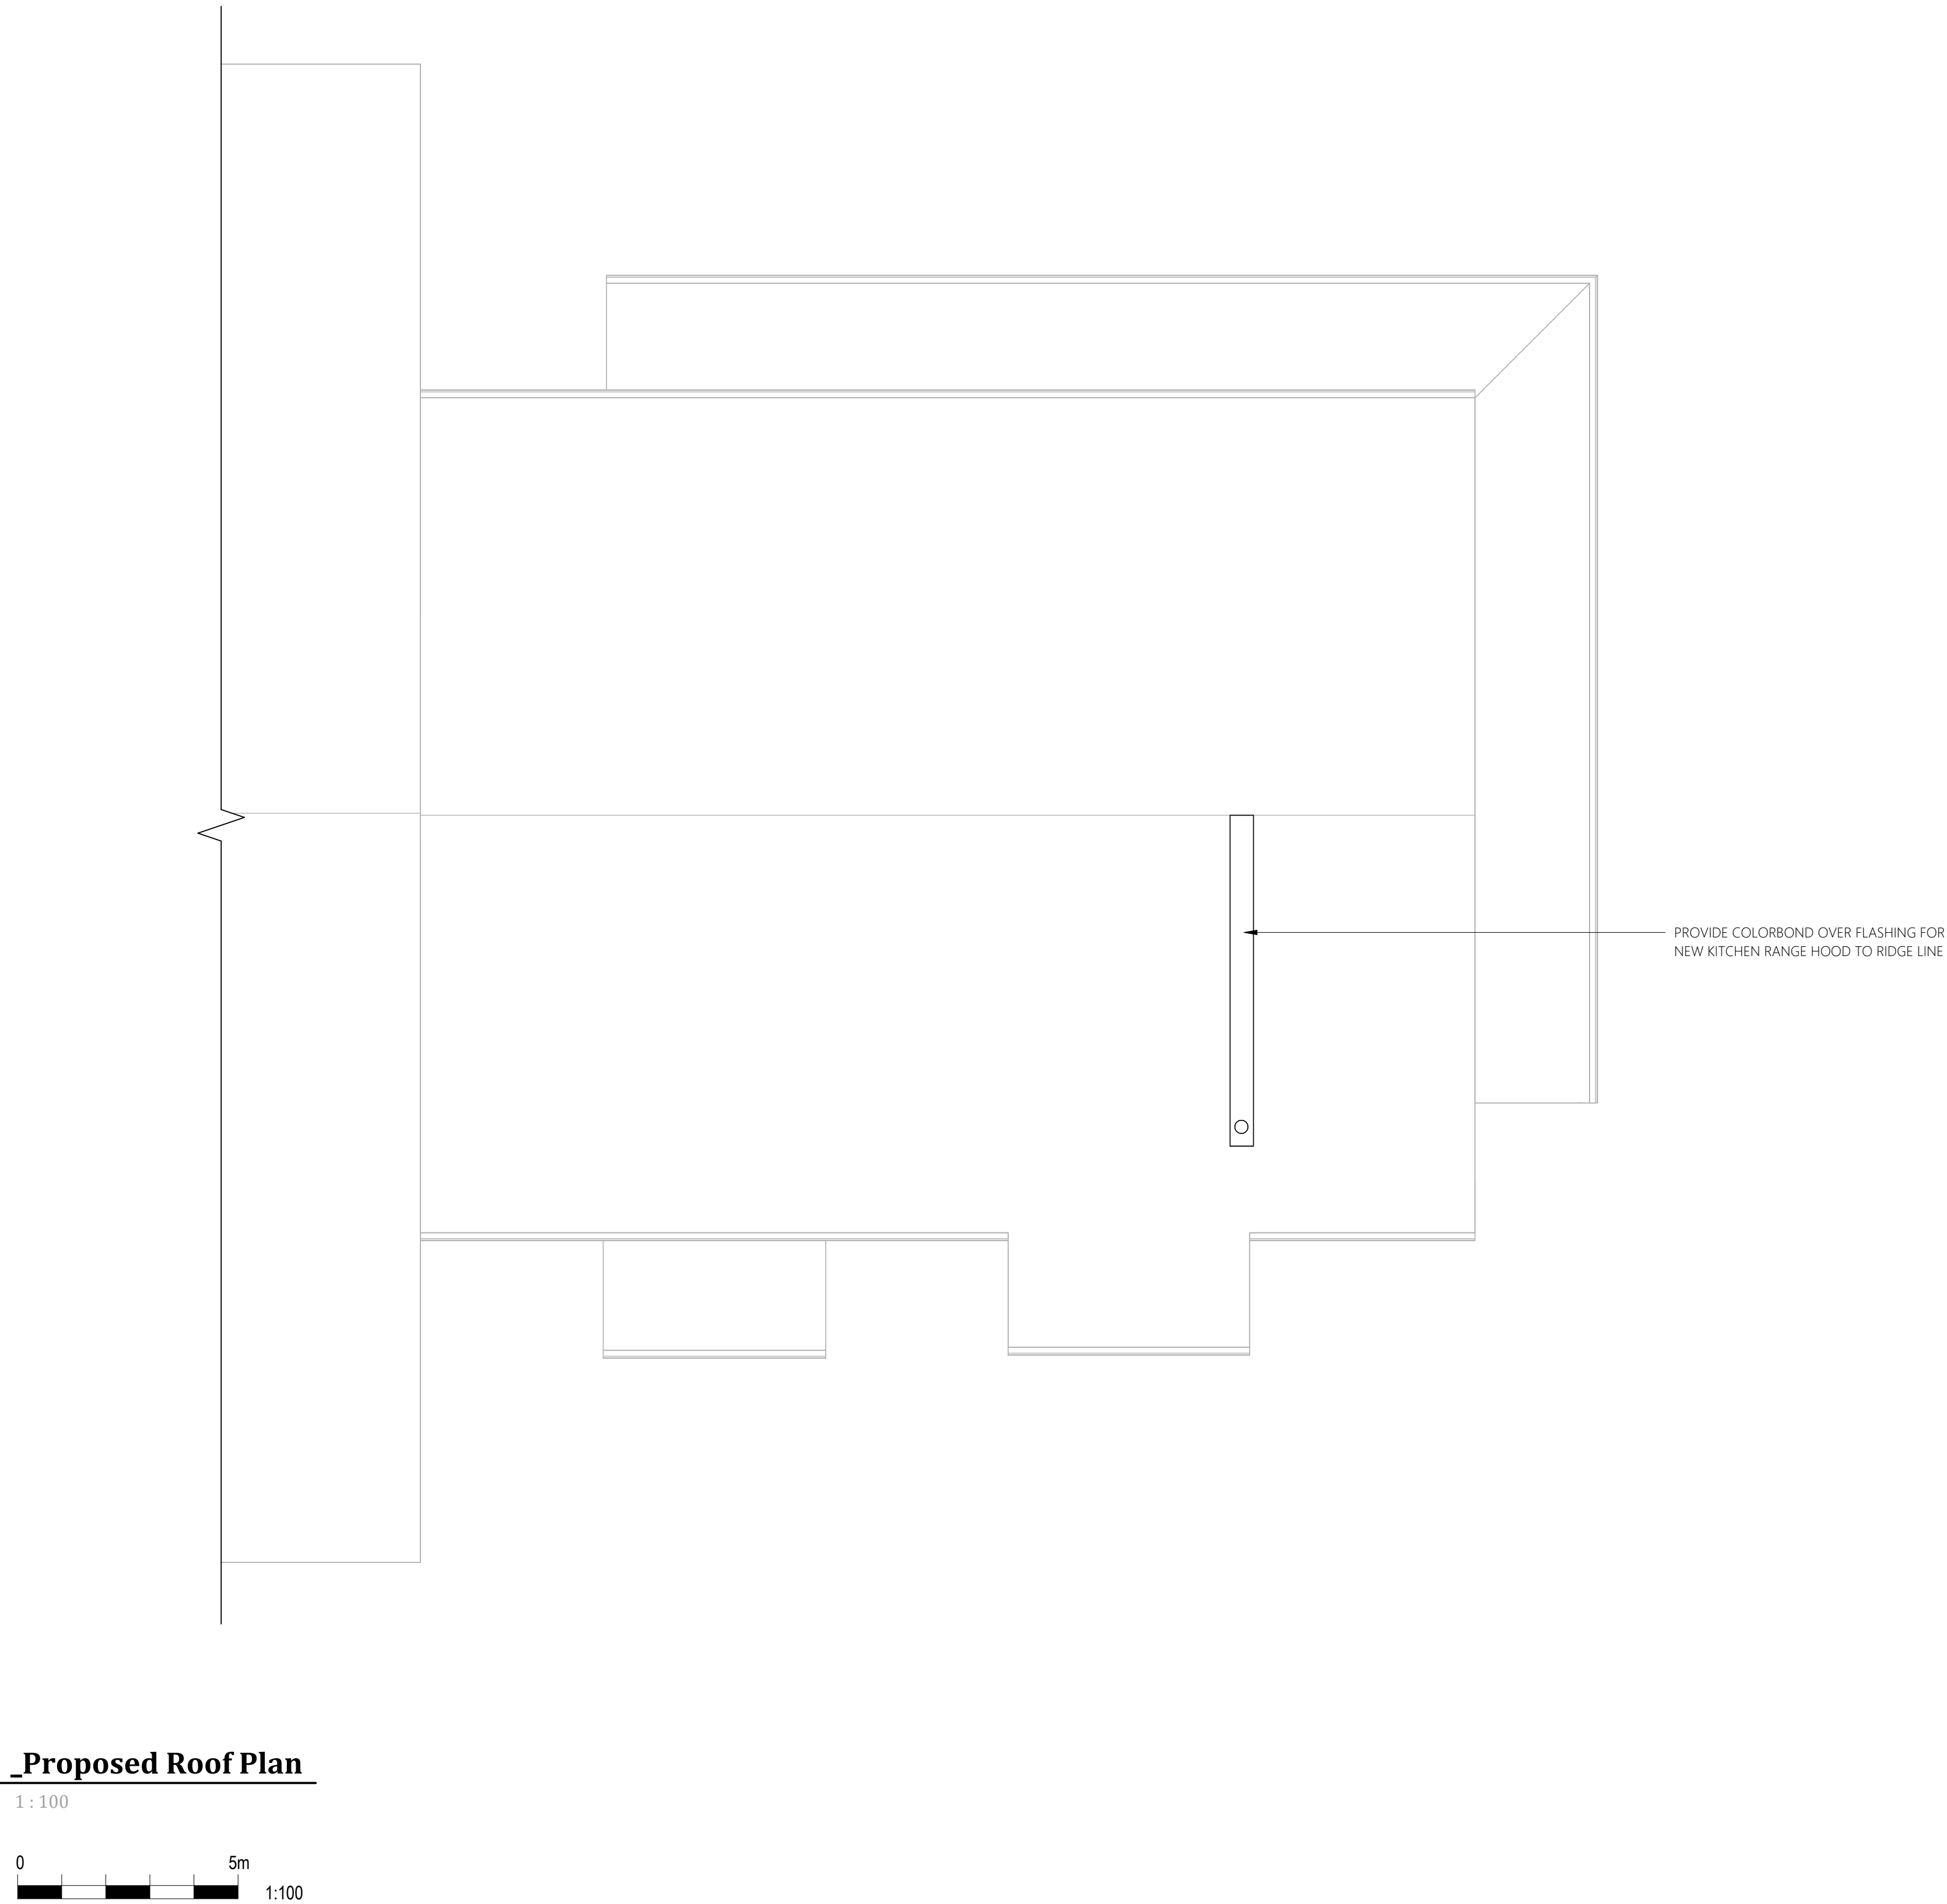

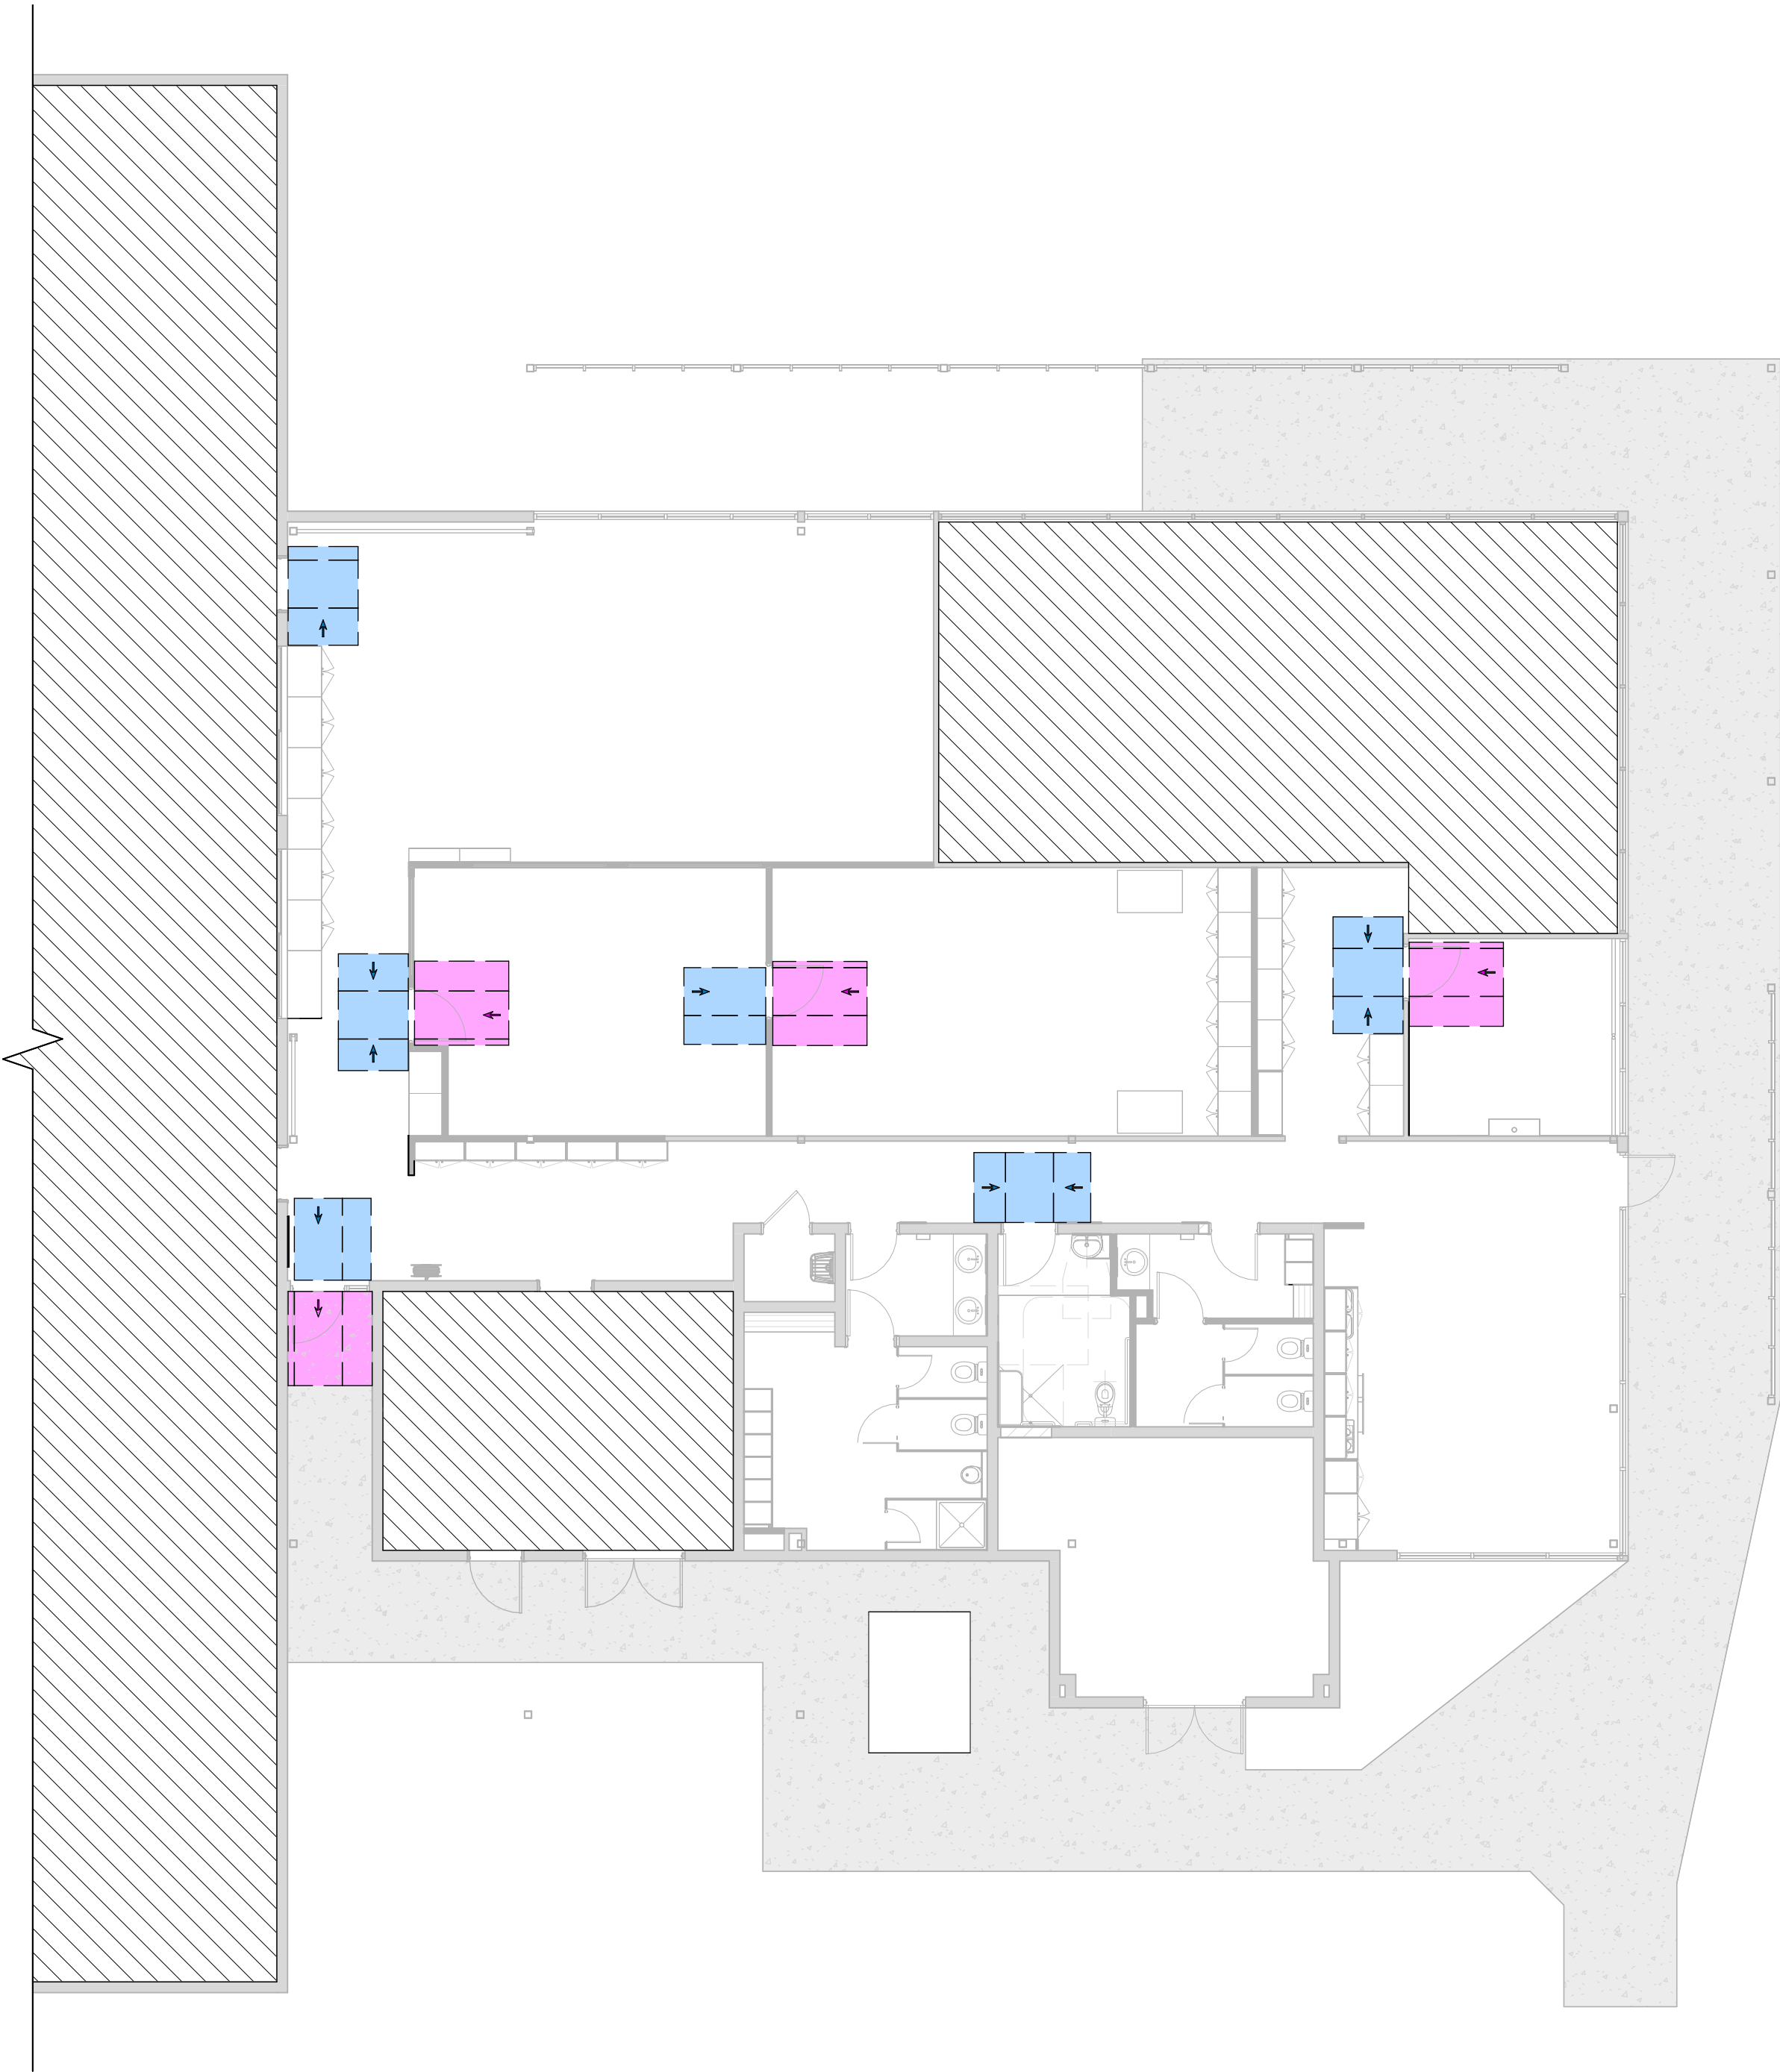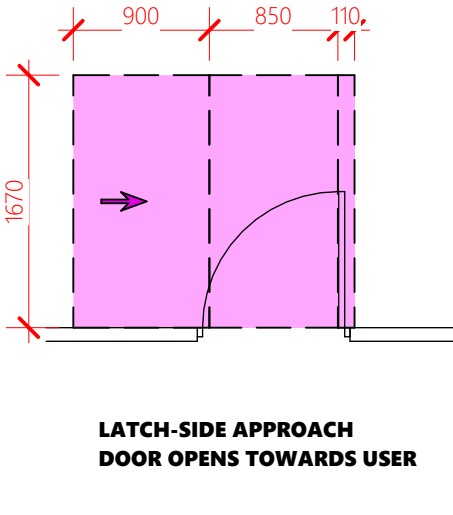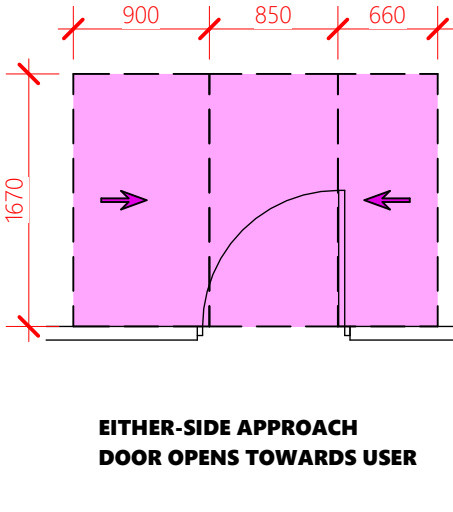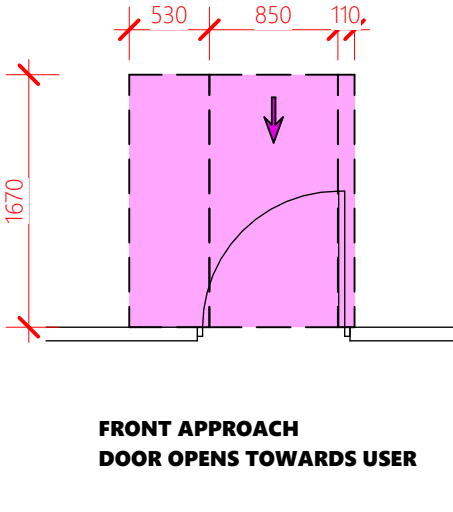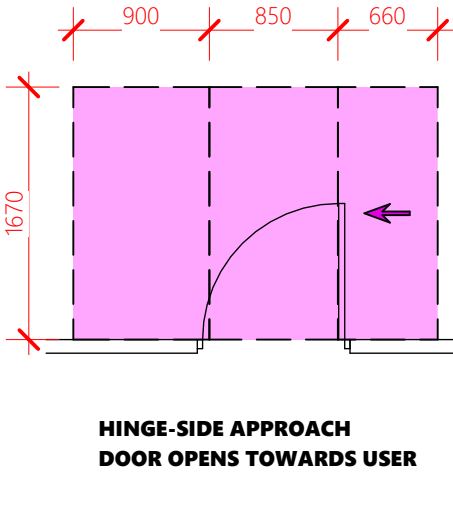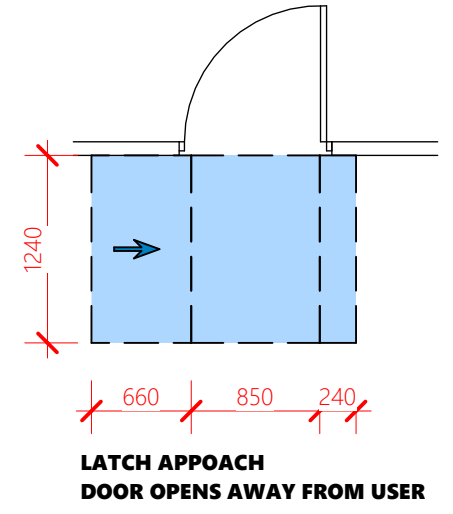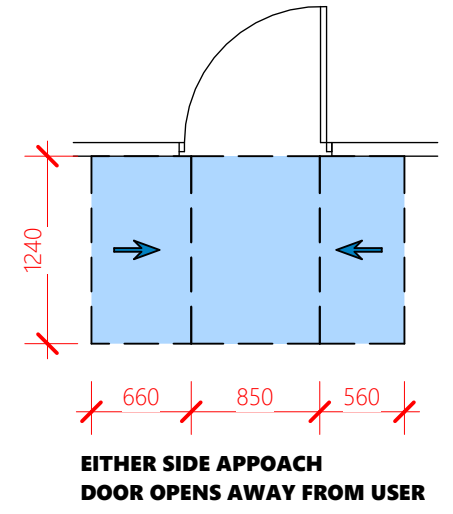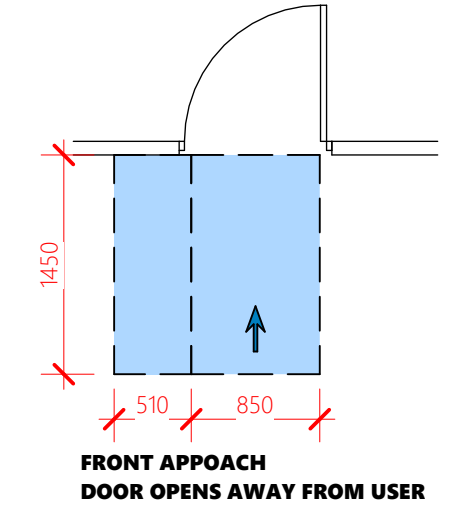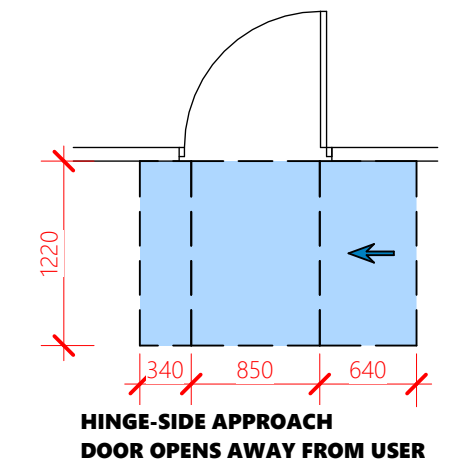

AS1428.1 - Clearance Plan

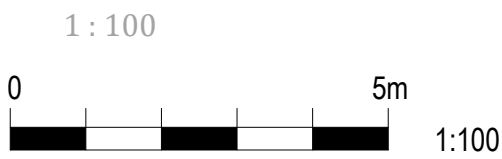

REVISIONS		
Rev	Description	Date
T1	TENDER ISSUE	12.03.2026

DO NOT SCALE THIS DRAWINGS



TENDER ISSUE

Client

Project Details

**MAIN WAREHOUSE
REFURBISHMENT**

Address

**STANWELL POWER
STATION**

Drawing Title

AS1428.1 - CLEARANCE

dezi nelements
BUILDING DESIGNERS

0483 988 655

info@dezi nelements.com.au

QBCC No: 1247120 BDAQ No: 0001677


Scale: As indicated Rev:

Date: JAN 2025 **T1**

Drawn: Author

Project No: Drawing No:

25_003 A3-304

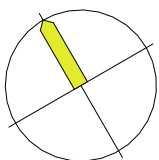

REVISIONS		
Rev	Description	Date
T1	TENDER ISSUE	12.03.2026

DO NOT SCALE THIS DRAWINGS

FLOOR COVERING PLAN

SHEET VINYL - TYPE 1
100mm FEATHER EDGE SKIRTING - BLACK

SHEET VINYL - TYPE 2
100mm COVERED UP SKIRTING

SHEET VINYL - TYPE 3
100mm FEATHER EDGE SKIRTING - BLACK

TENDER ISSUE

Client



Project Details

MAIN WAREHOUSE
REFURBISHMENT

Address

STANWELL POWER
STATION

Drawing Title

FLOOR COVERING PLAN



0483 988 655 
info@deziignelements.com.au 
QBCC No: 1247120 BDAQ No: 0001677

Scale: 1 : 100

Date: JAN 2025

Drawn: Author

Rev:


T1

Project No:

25_003

Drawing No:

A3-305

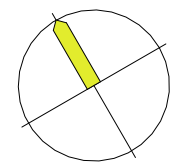

Floor Covering Plan


1 : 100

05m

1:100

REVISIONS		
Rev	Description	Date
T1	TENDER ISSUE	12.03.2026

DO NOT SCALE THIS DRAWINGS


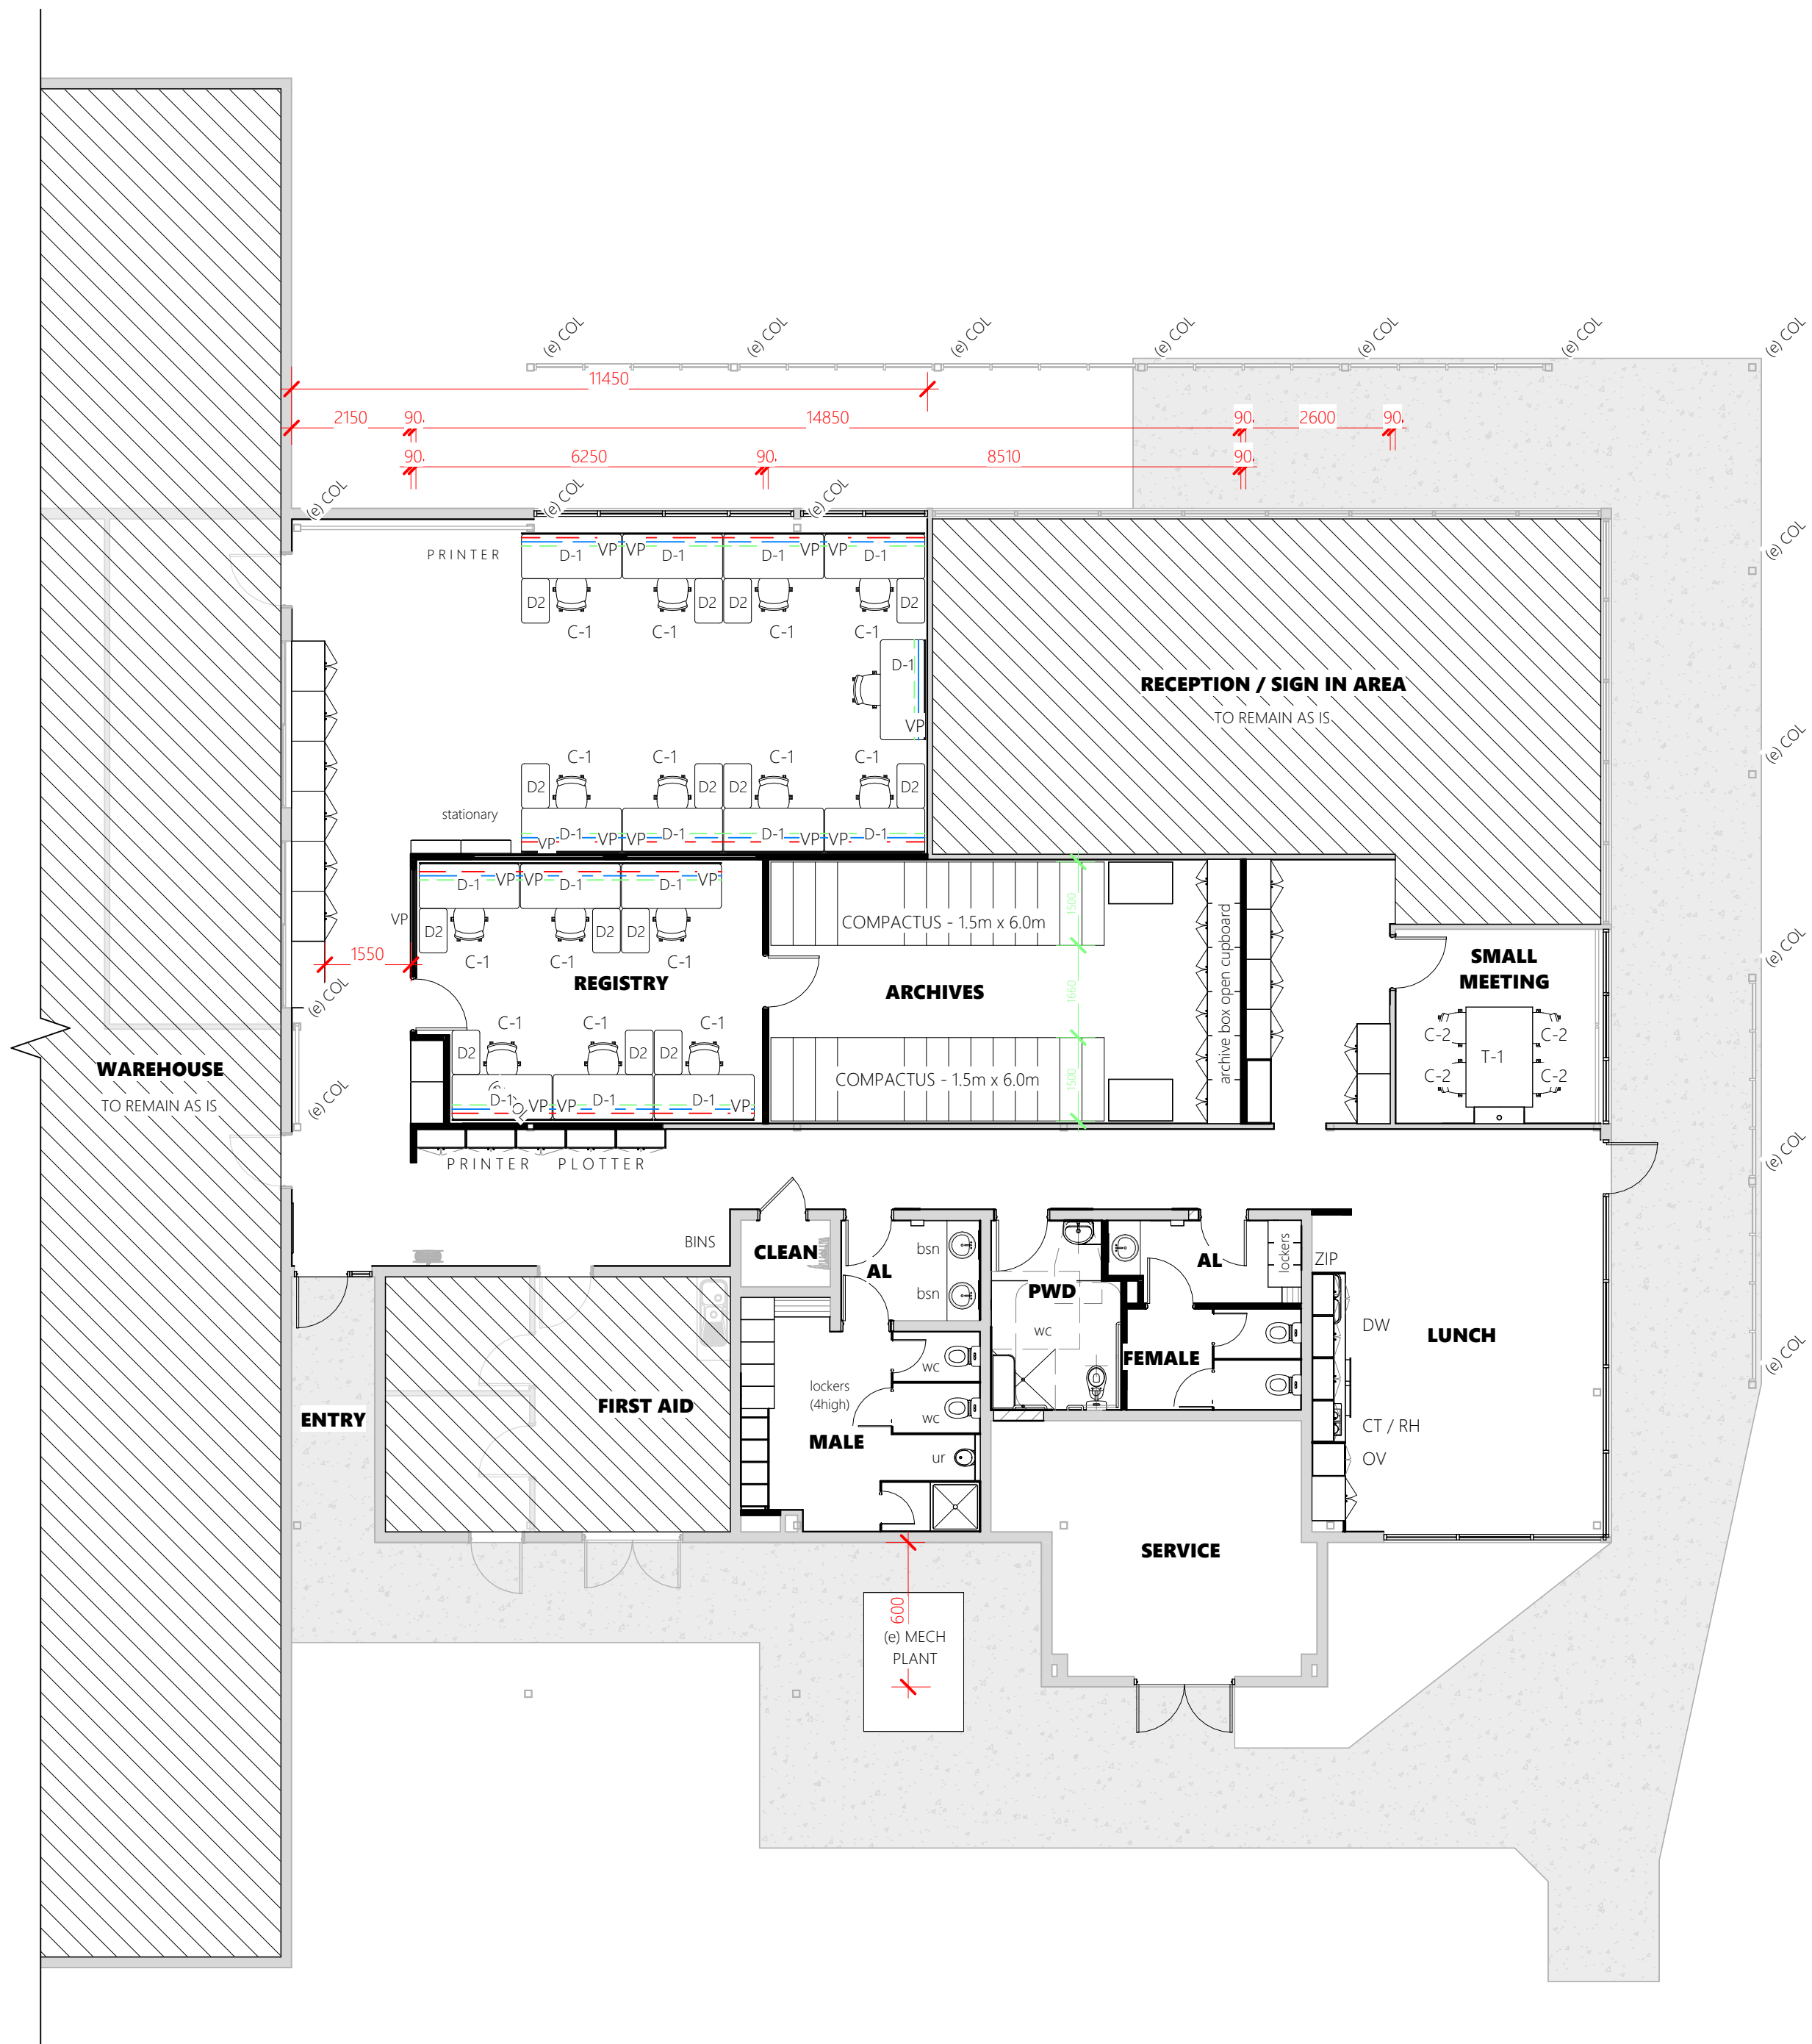


FURNITURE & APPLIANCE SCHEDULE

CODE	TYPE	SIZE	QTY	SUPPLIER
D-1	DESK	1800 x 800	15	SCHIAVELLA CLIMATE RECTANGLE WORK STATION
D-2	DESK	800 x 500	14	SCHIAVELLA CLIMATE RECTANGLE WORK STATION RETURN
C-1	CHAIR (workstation)	-	15	SCHIAVELLA HIGH BACK CHAIR BY OKAMURA, BLACK BODY, BLACK MESH BLACK AND UPHOLSTERED SEAT
C-2	CHAIR (meeting)	-	4	SHIBUSA HIGH BACK BY OKAMURA (BLACK)
T-1	TABLE	1200 x 1800	1	MEETING TABLE EONA - 25mm LAMINEX CHARCOAL NATURAL FINISH WITH ABS EDGING
---	CABLE CATCHER	AS REQUIRED	-	SCHIAVELLA
---	CABLE ARTICULATOR	AS REQUIRED	-	SCHIAVELLA
---	CABLE CHANNEL	AS REQUIRED	-	SCHIAVELLA
VP	VIDE SUSP. PANEL	1800 (600mm ABOVE DESK)	15	SCHIAVELLA - PROVIDE SUSPENDED BRACKETS TO EACH DESK
COMP	COMPACTUS	1500 x 6000	2	TBC
OV	OVEN	598 x 596	1	FISHER & PAYKEL 60CM SERIES 7 CONTEMPORARY PYROLYTIC OVEN 9 FUNCTION - BLACK
DW	DISHWASHER	597 x 600	1	FISHER & PAYKEL SERIES 7 CONTEMPORARY DISHWASHER - BLACK STEEL
CT	COOK TOP	600	1	FISHER & PAYKEL 60CM SERIES 7 4 ZONE INDUCTION COOKTOP 2 SMARTZONES - BLACK
RH	RANGE HOOD	600	1	FISHER & PAYKEL 60CM SERIES 7 INTEGRATED INSERT WALL RANGEHOOD EXTERNAL MOTOR - STEEL GLASS
ZIP	ZIP UNIT	-	1	HYDROTAP GS BC5HA100 5-IN-1 CLASSIC TAP WITH CLASSIC MIXER BLACK


_Furniture Layout

1 : 100

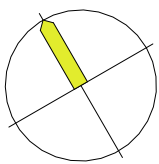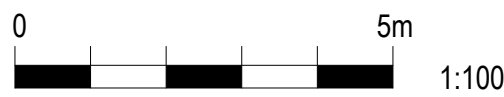

REVISIONS		
Rev	Description	Date
T1	TENDER ISSUE	12.03.2026

DO NOT SCALE THIS DRAWINGS

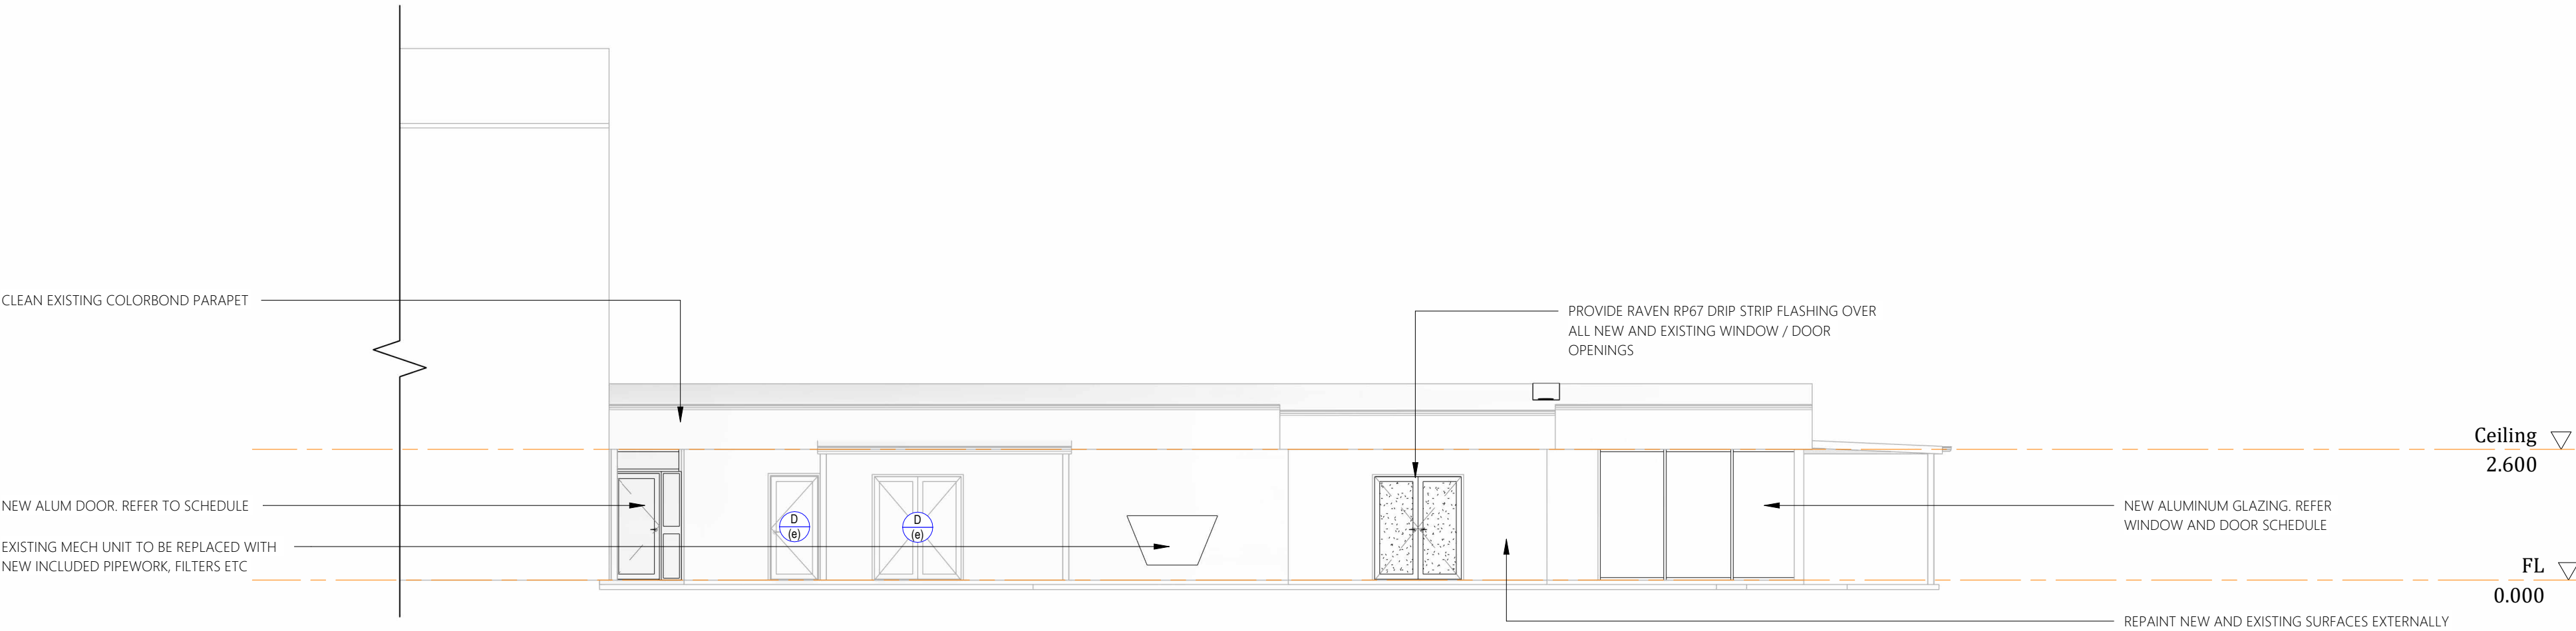

Proposed Elevation 1
1 : 100



Proposed Elevation 2
1 : 100



Proposed Elevation 3
1 : 100

TENDER ISSUE

Client



Project Details

**MAIN WAREHOUSE
REFURBISHMENT**

Address

**STANWELL POWER
STATION**


Drawing Title


PROPOSED ELEVATIONS



0483 988 655 **M**
info@designelements.com.au **E**
QBCC No: 1247120 BDAQ No: 0001677




Scale: 1 : 100	Rev: T1
Date: JAN 2025	
Drawn: Author	
Project No: 25_003	Drawing No: A3-400

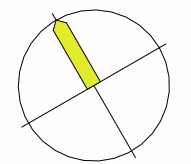

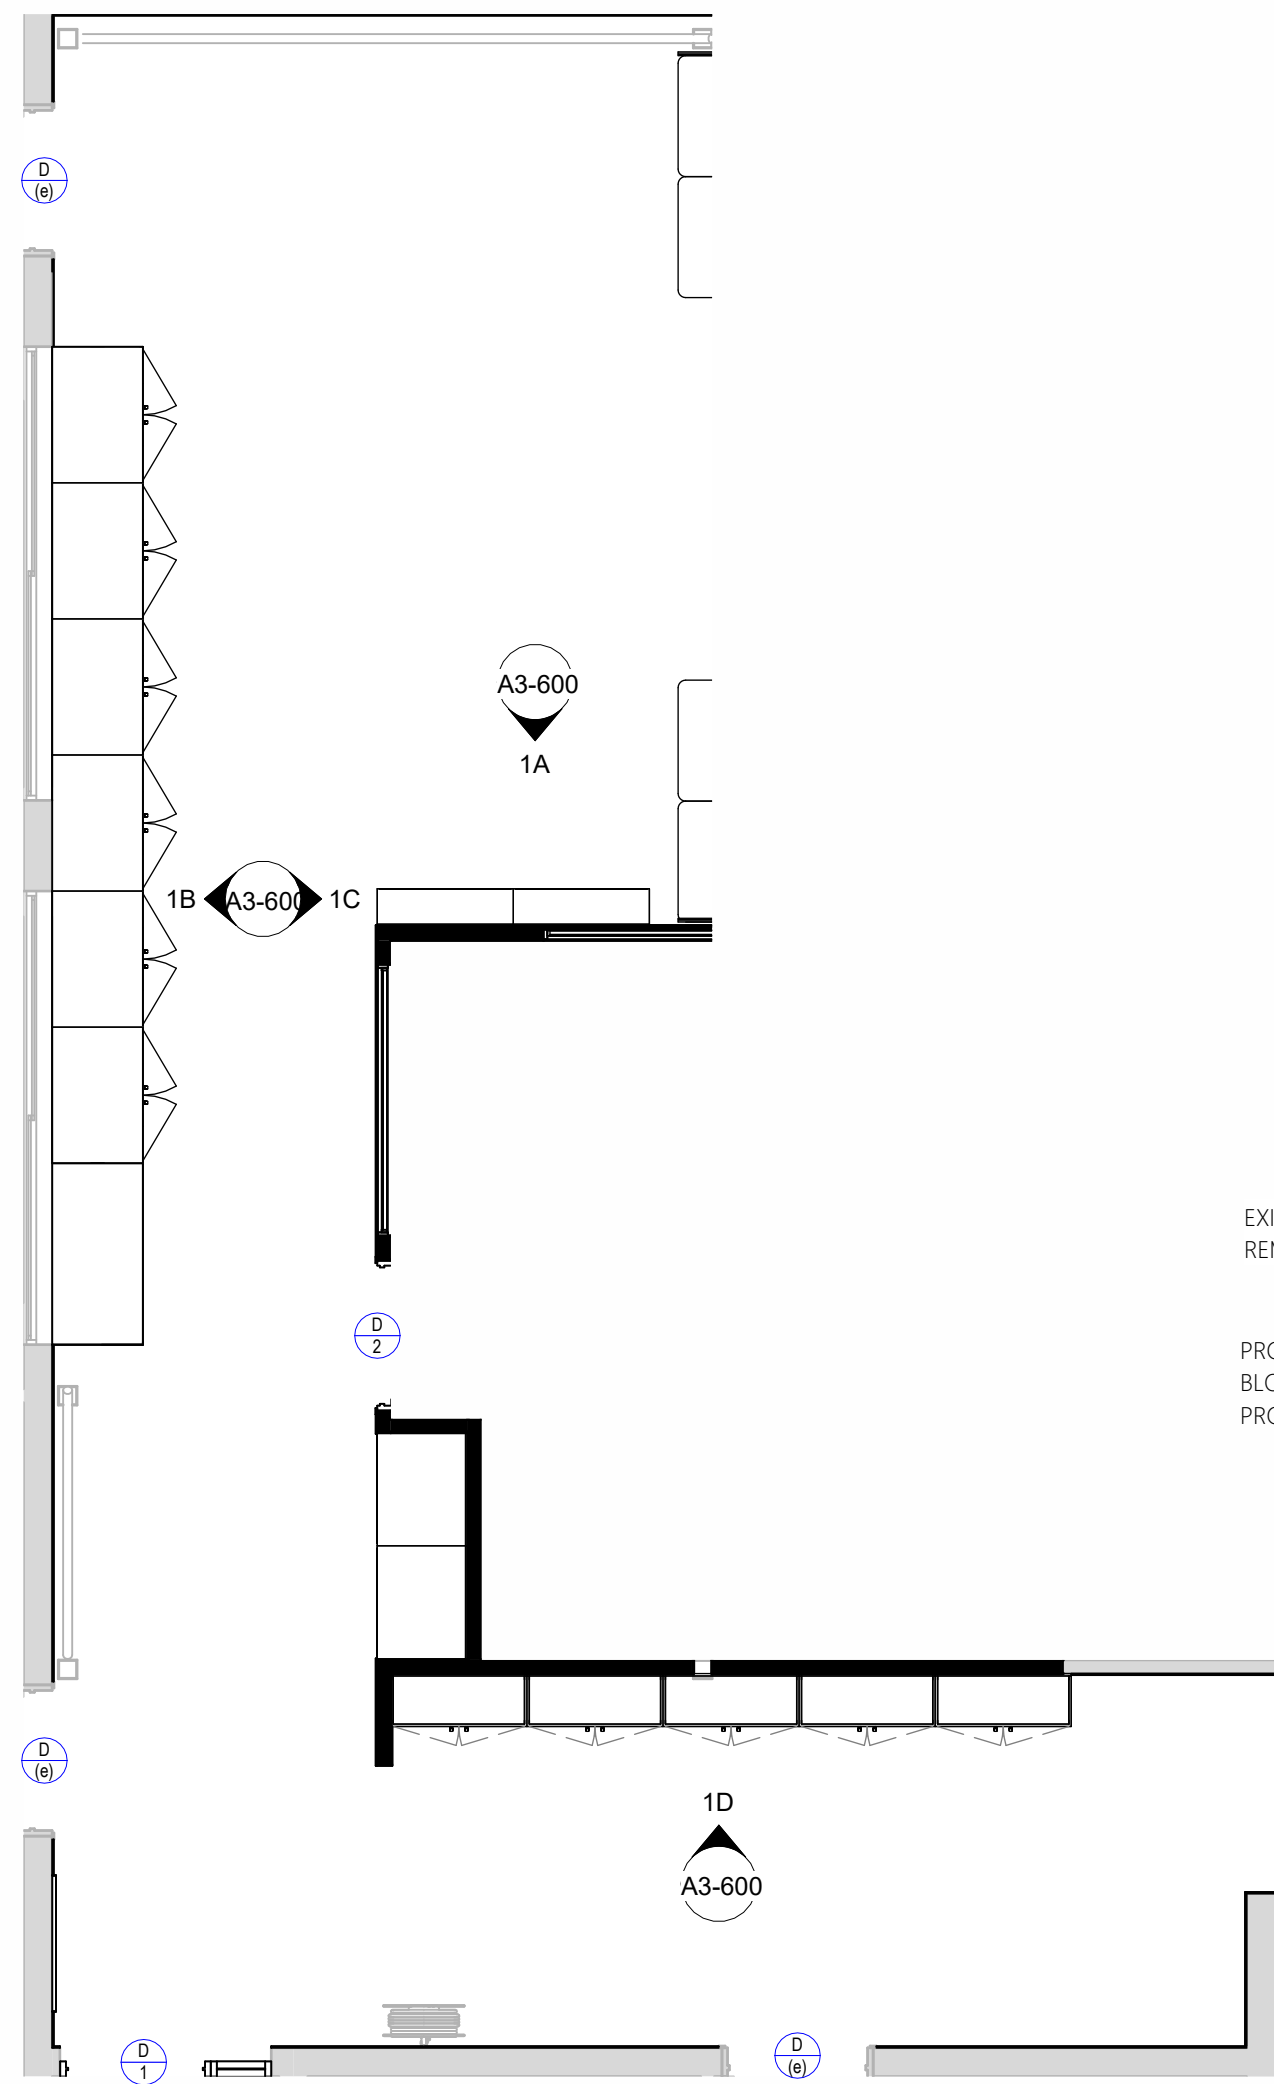

Internal Plan 1

1:50

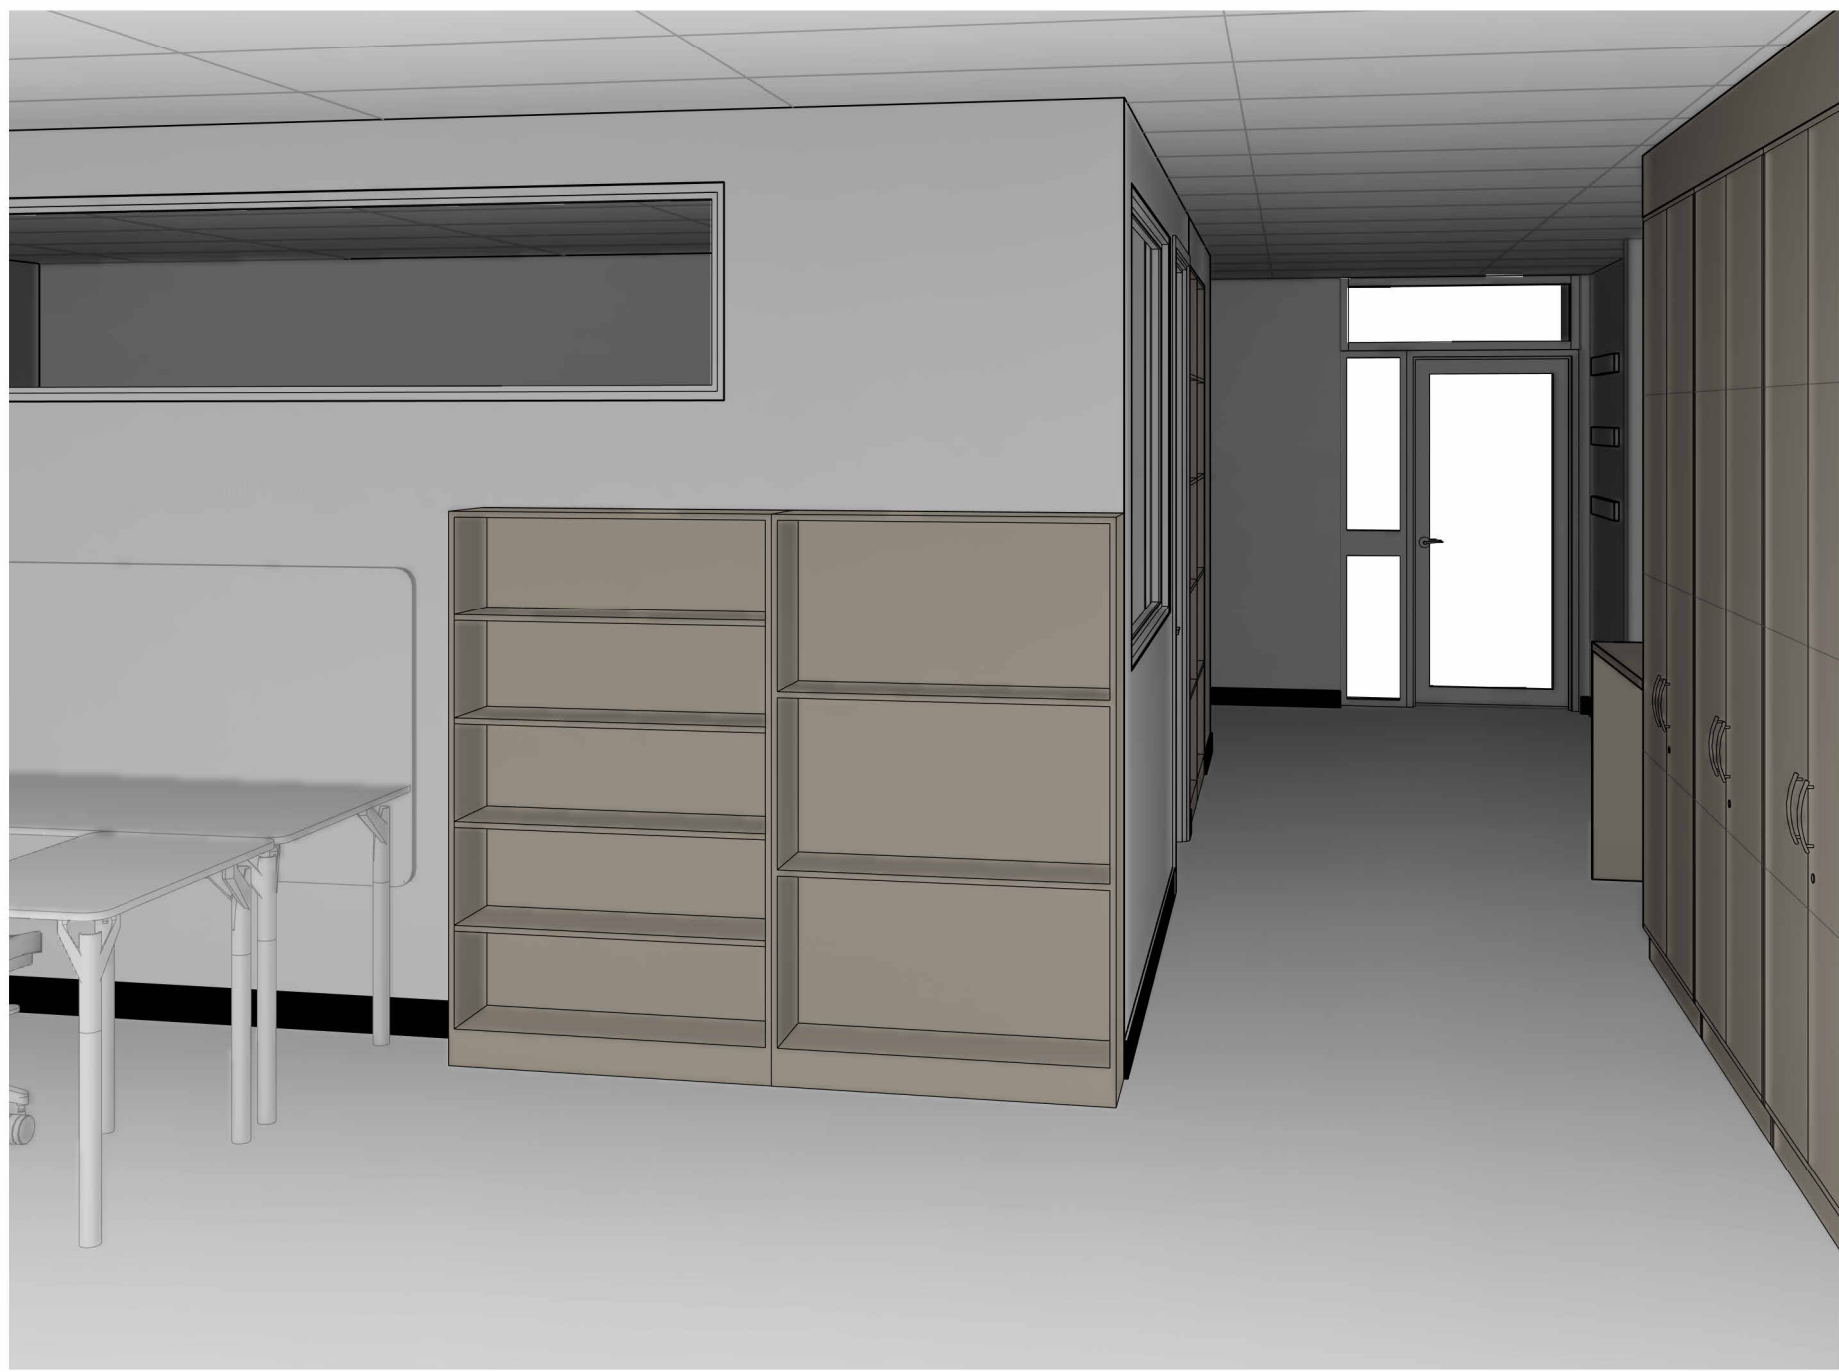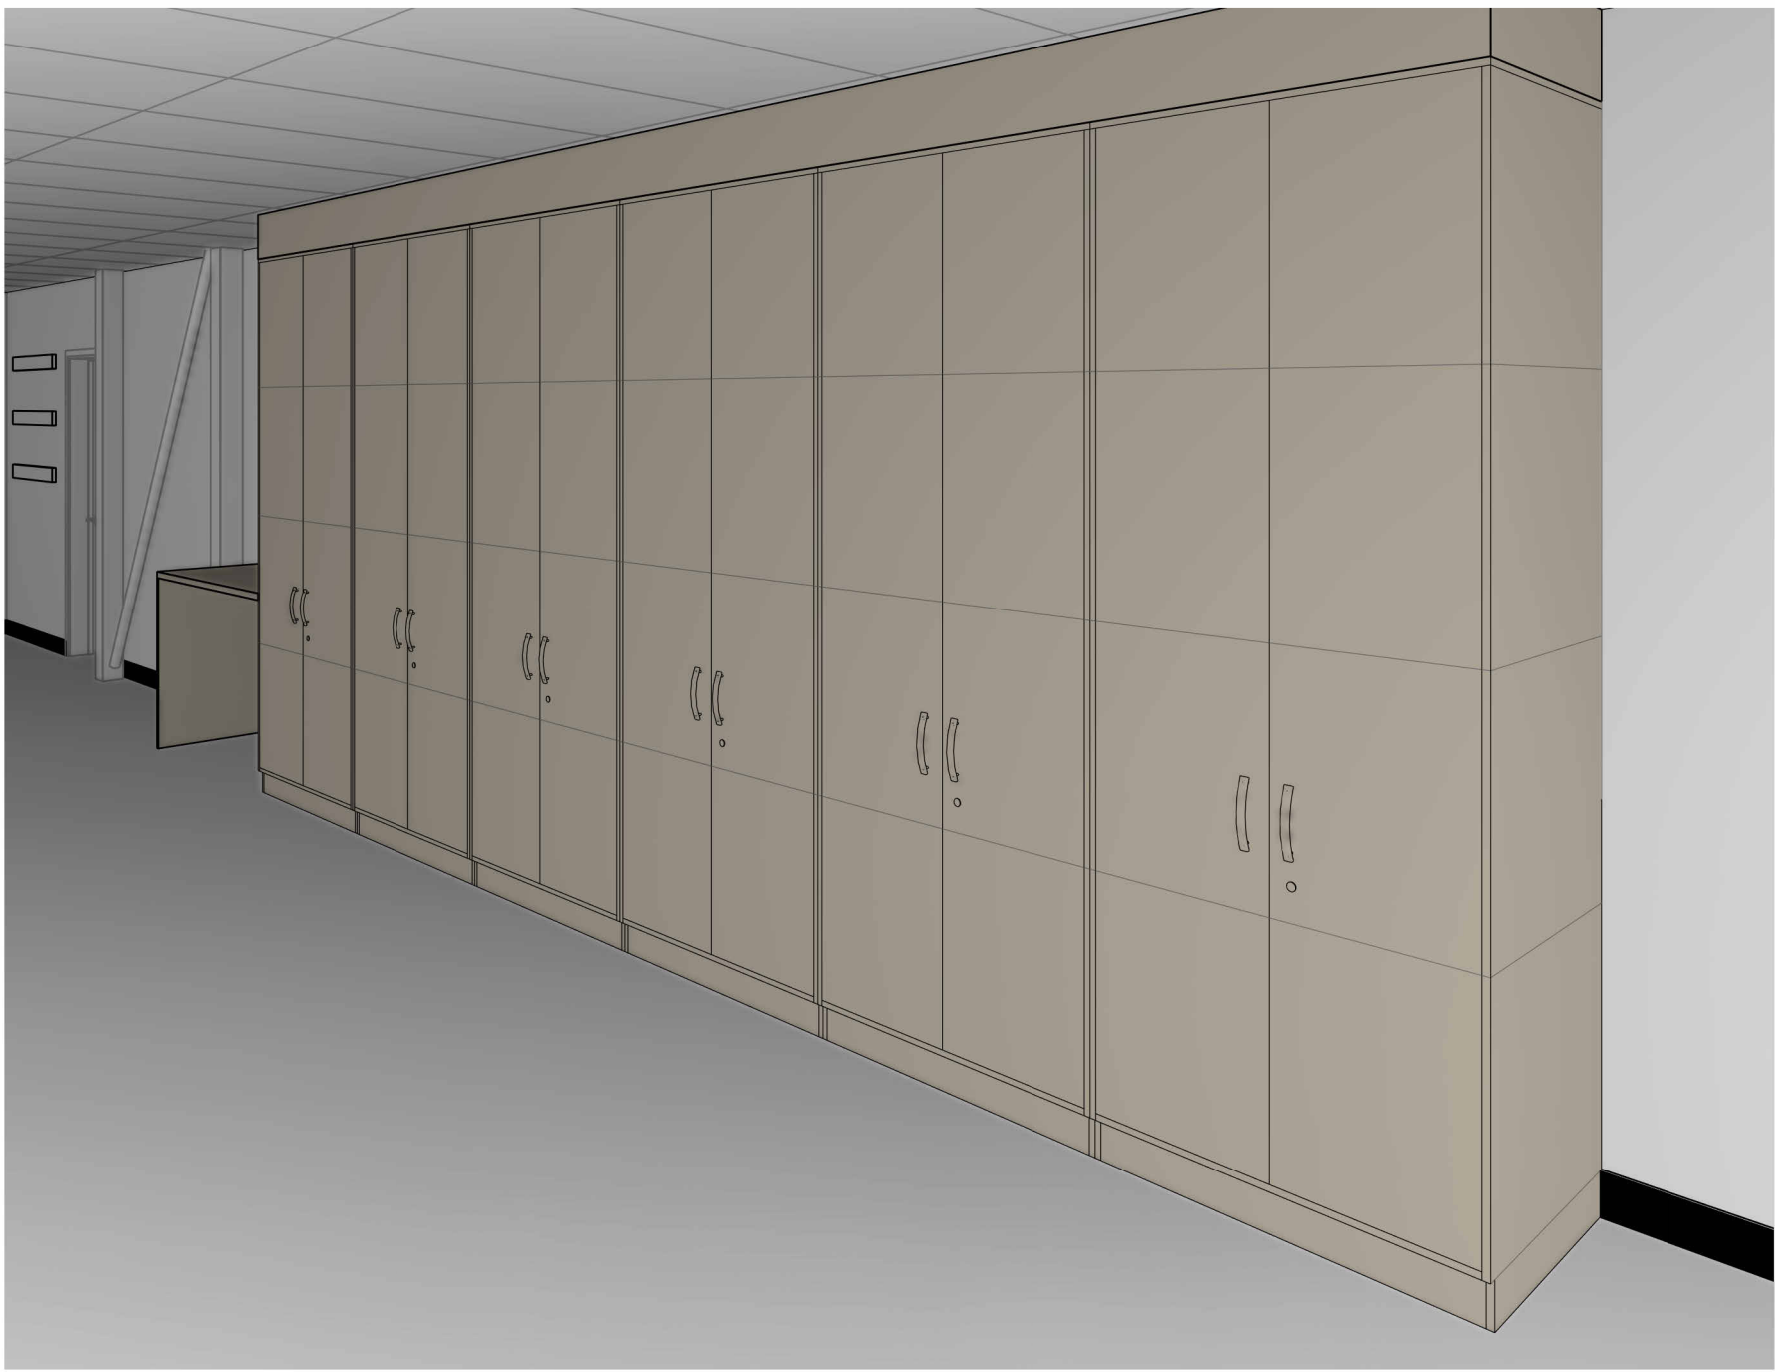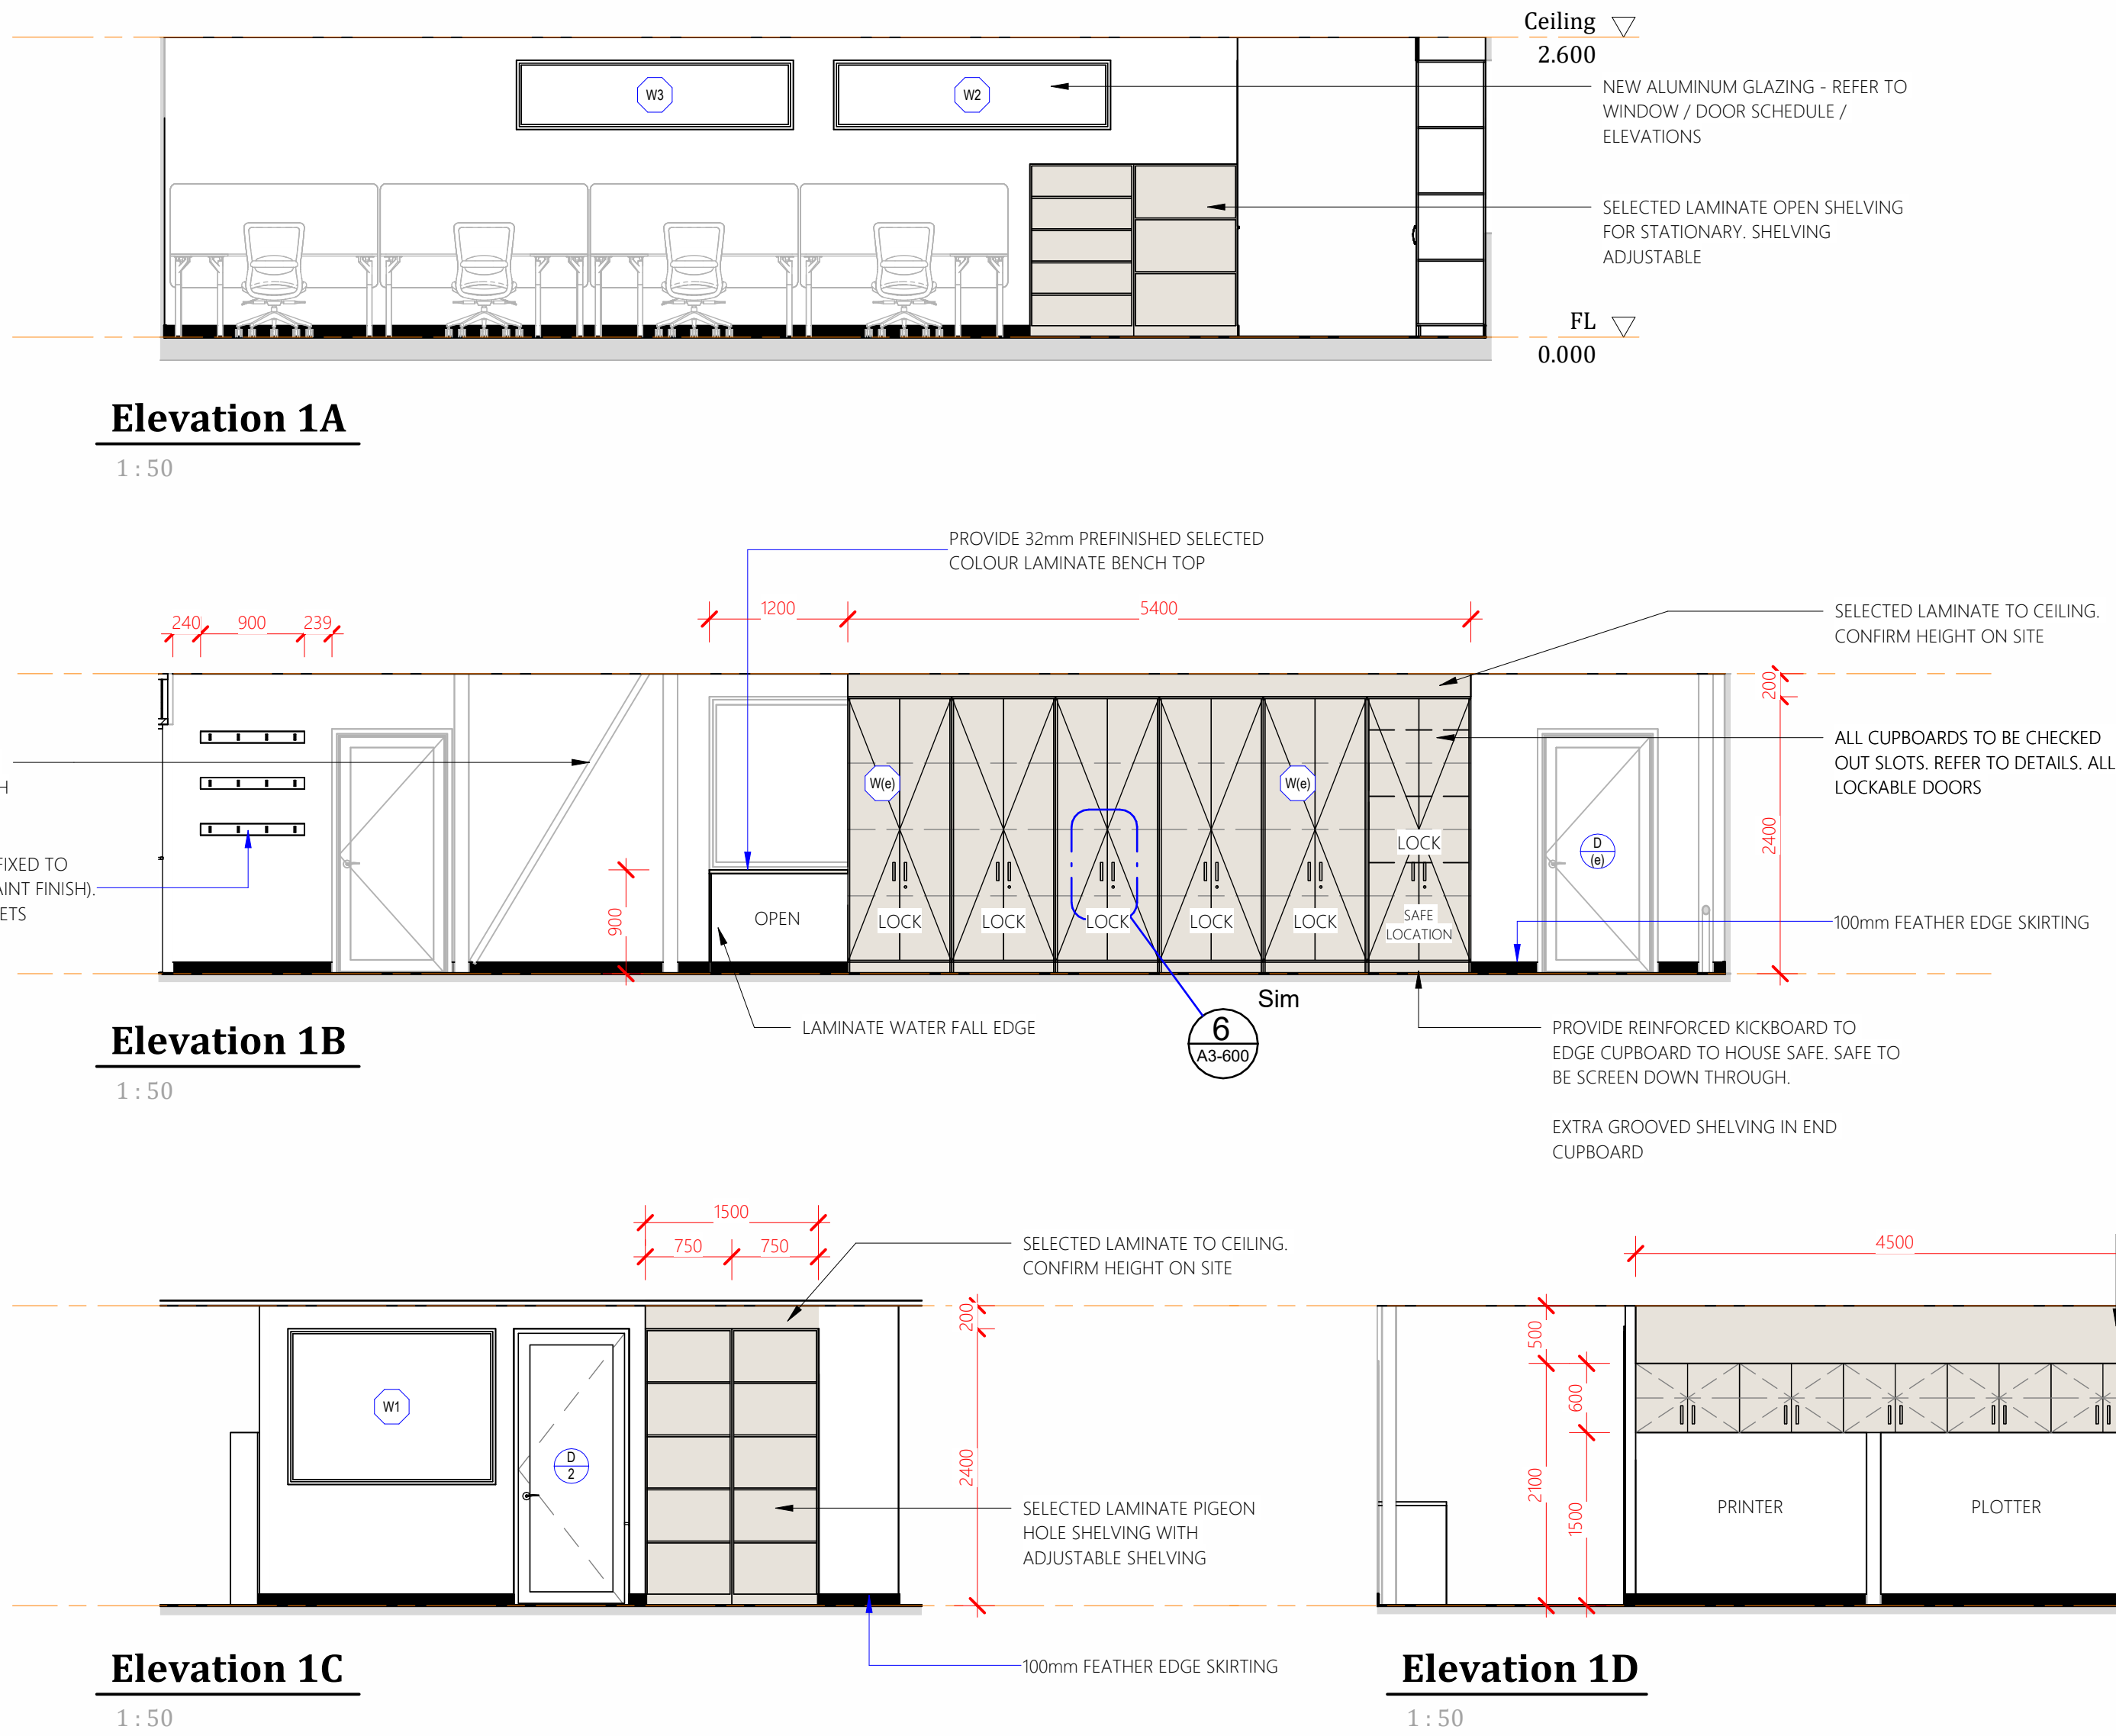

REVISIONS		
Rev	Description	Date
T1	TENDER ISSUE	12.03.2026

DO NOT SCALE THIS DRAWINGS



TENDER ISSUE

Client

Project Details

MAIN WAREHOUSE REFURBISHMENT

Address

STANWELL POWER STATION

Drawing Title

INTERNAL ELEVATIONS 1 - ENTRY / HALLWAYS

0483 988 655 **M**
info@dezi elements.com.au **E**
QBCC No: 1247120 BDAQ No: 0001677

Scale: As indicated

Rev: **T1**


Date: JAN 2025

12/03/2026 6:54:08 PM

Drawn: Author


Project No: **25_003**

Drawing No: **A3-600**

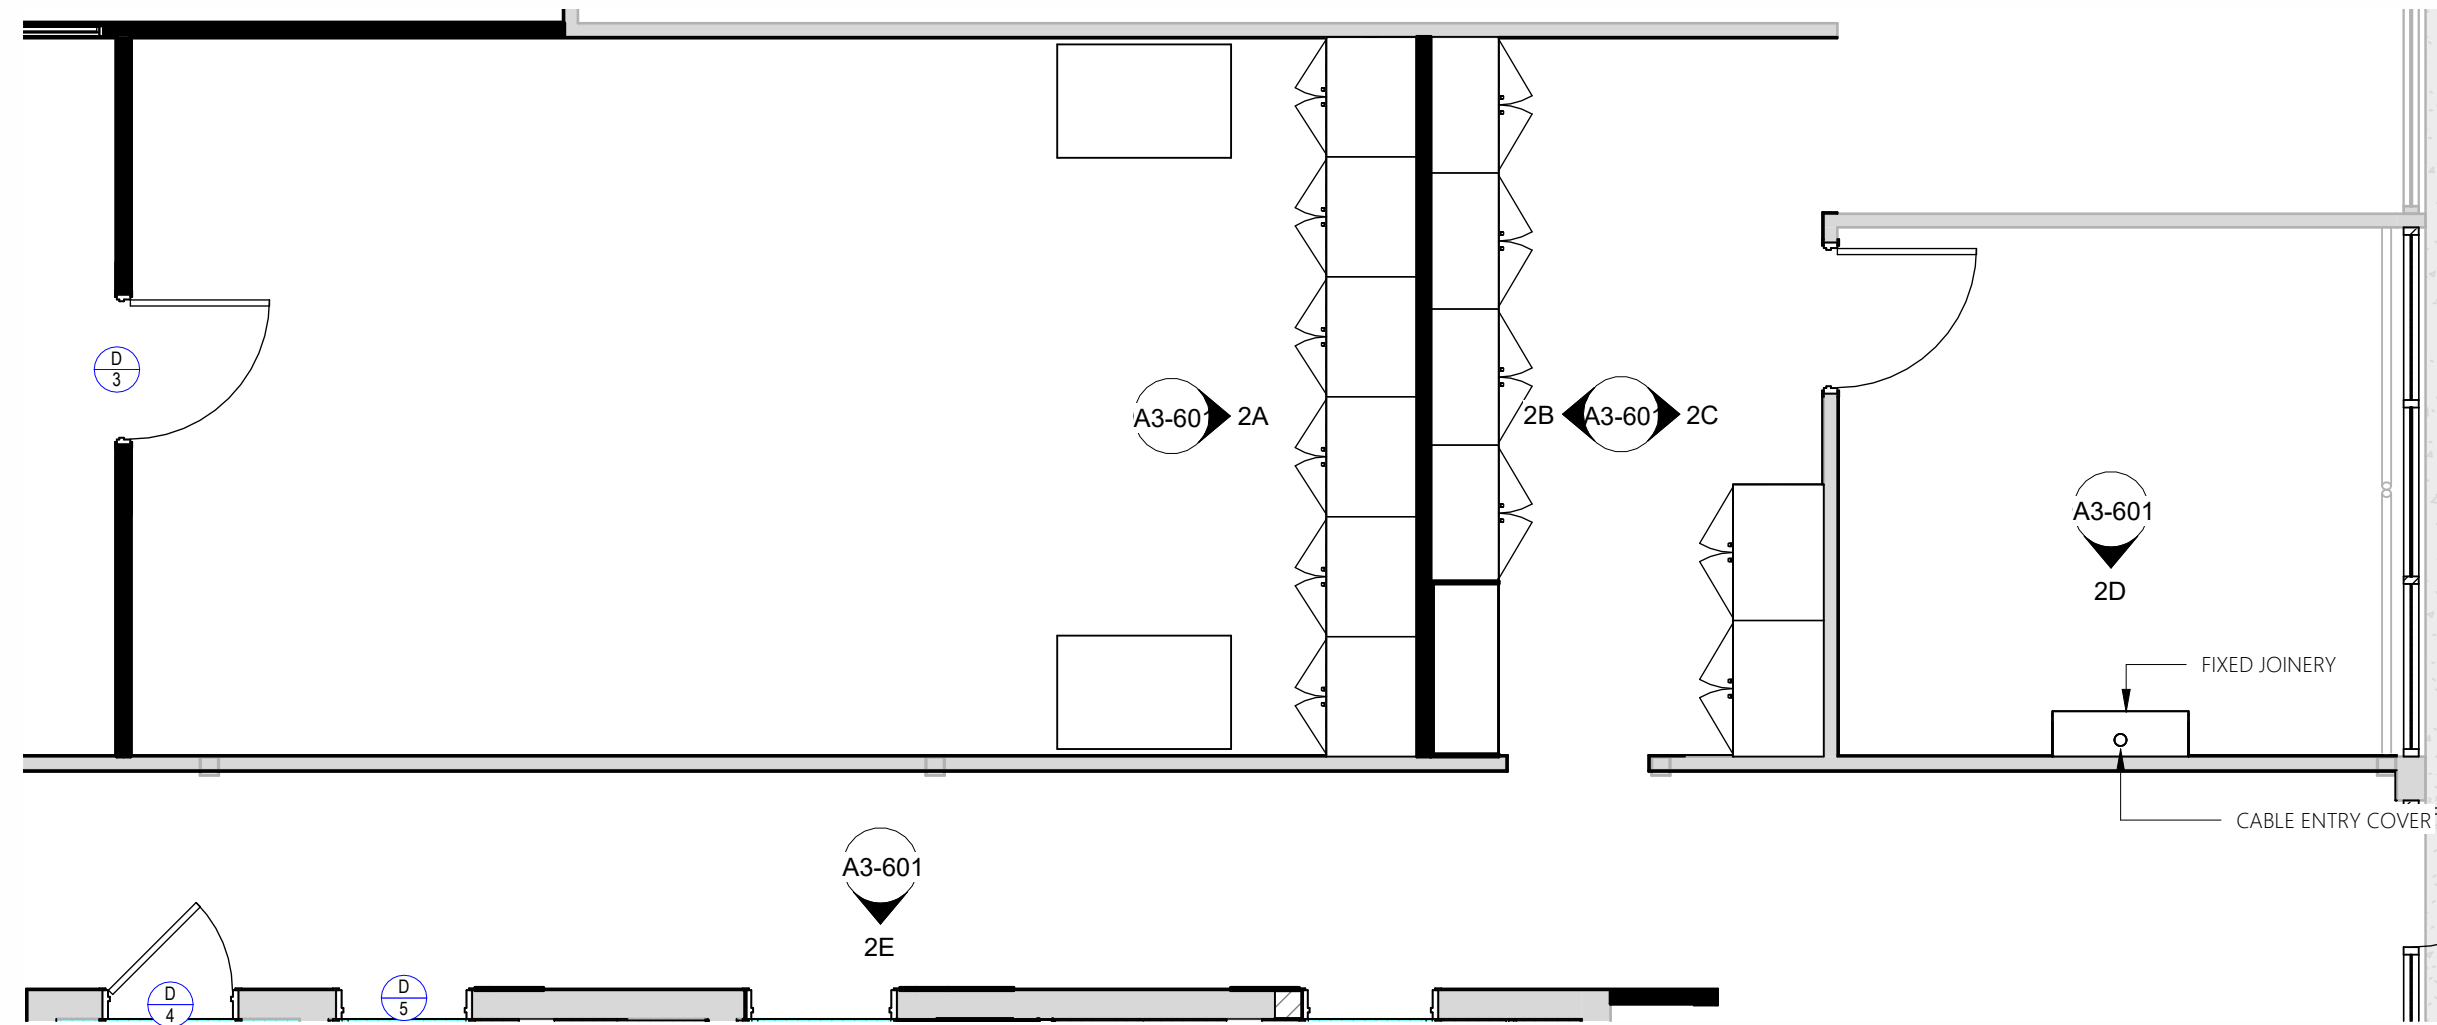

Internal Plan 2

1 : 50

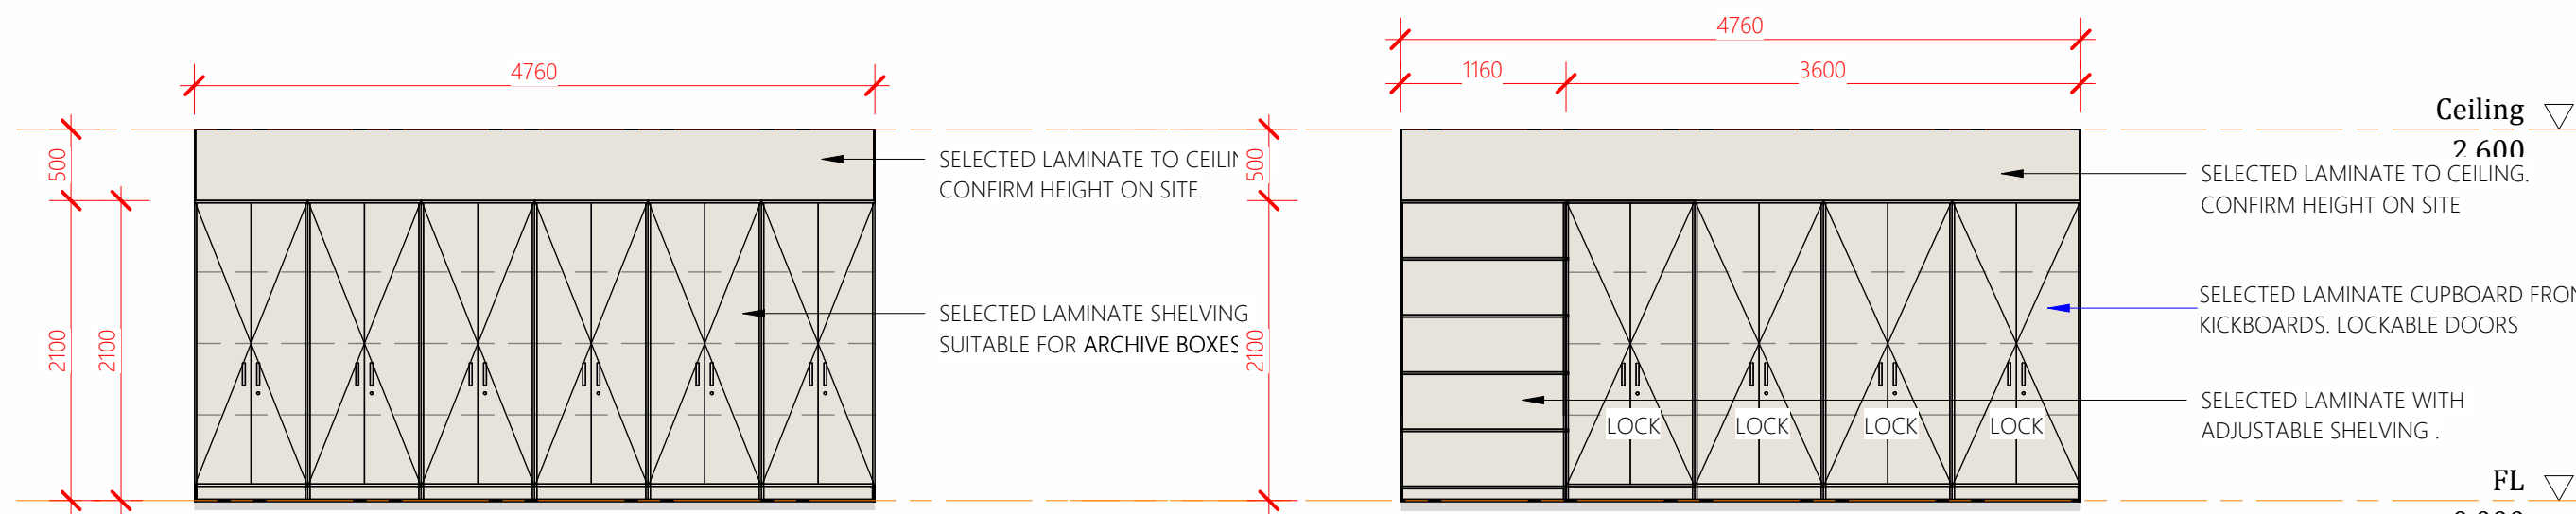


Elevation 2A

1 : 50

Elevation 2B

1 : 50

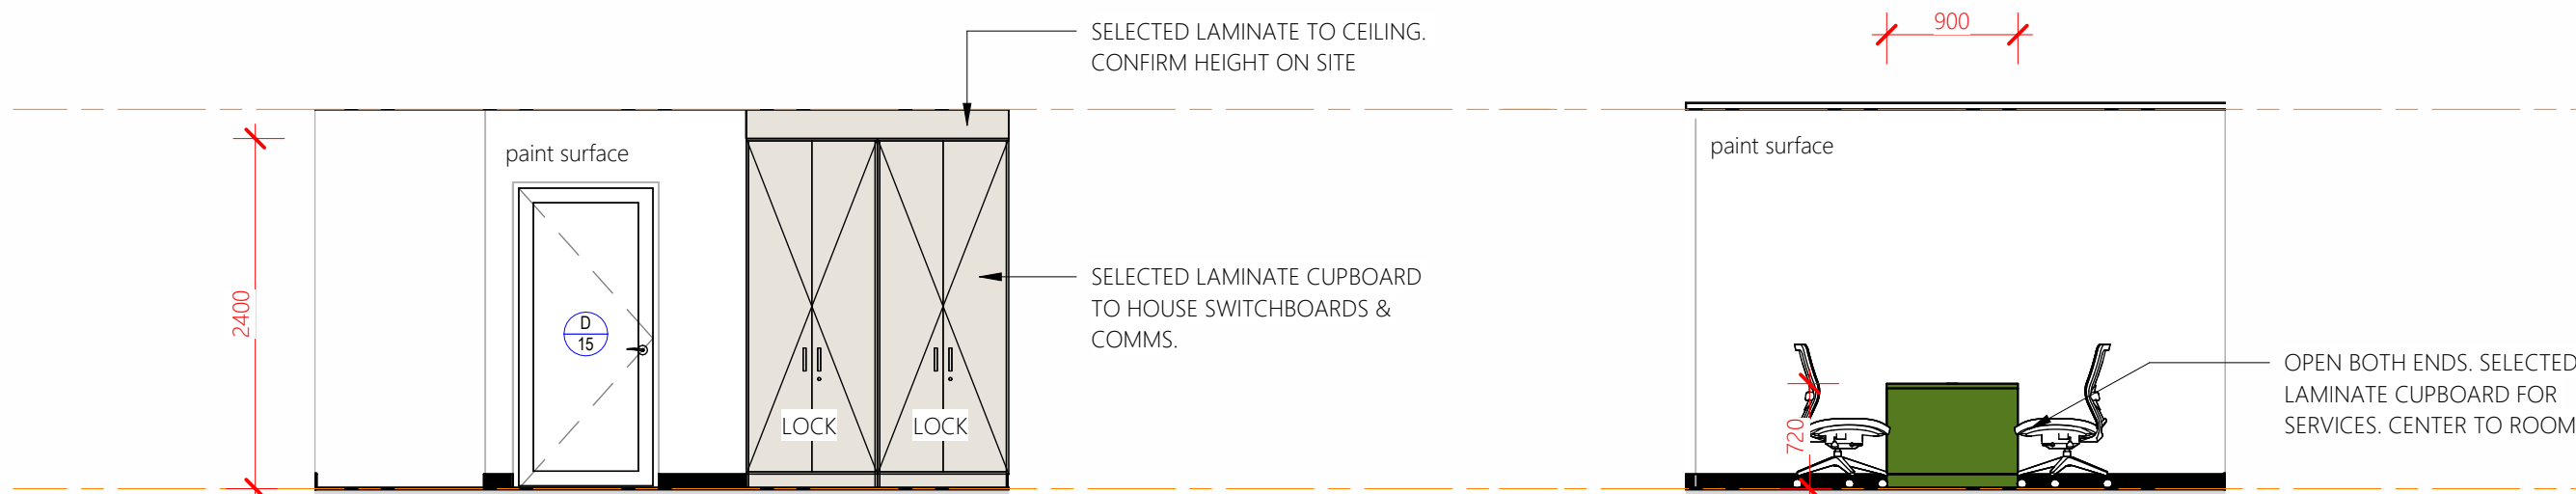


Elevation 2C

1 : 50


Elevation 2D

1 : 50

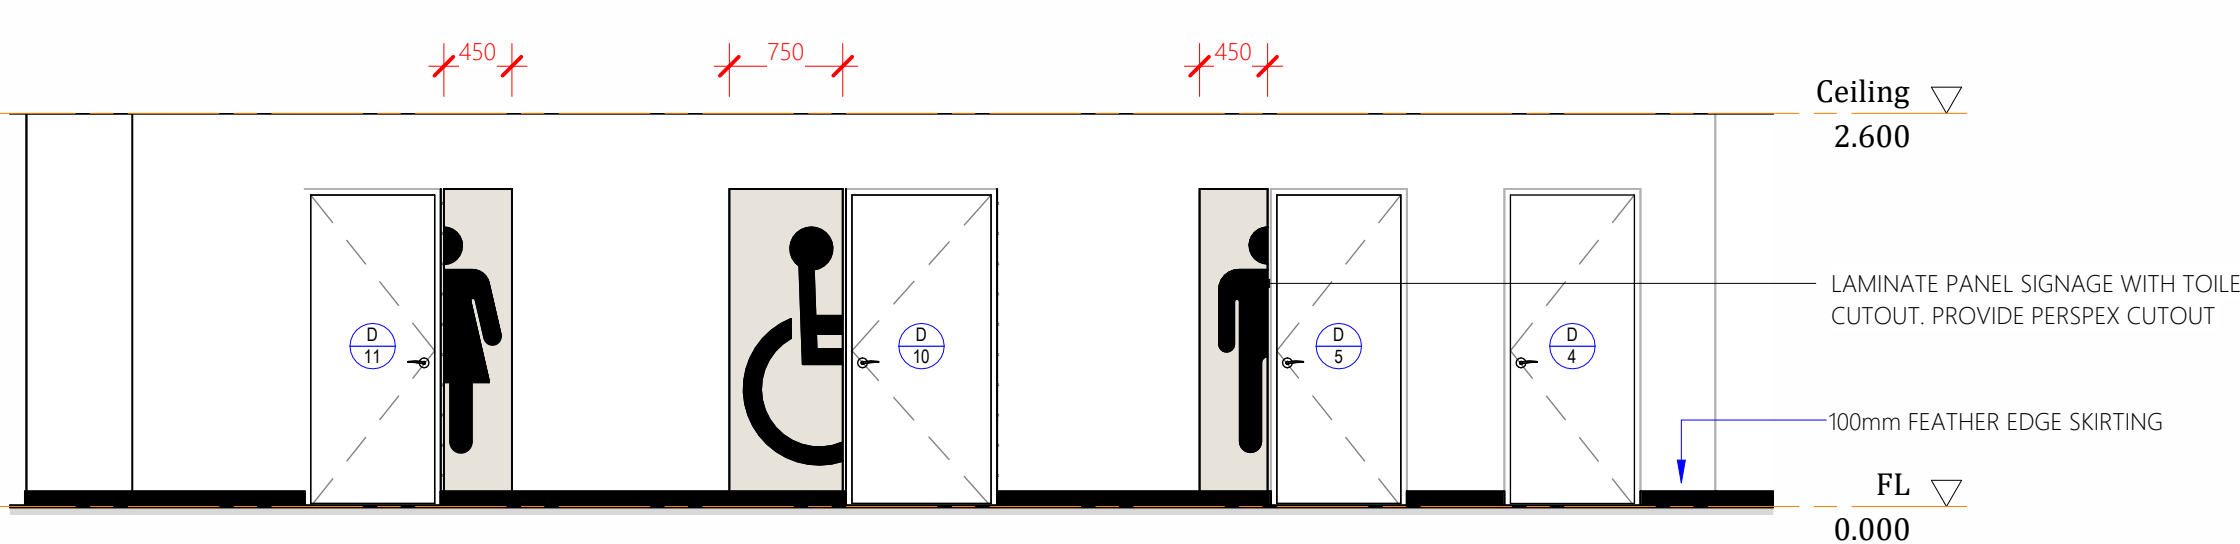

Elevation 2E

1 : 50

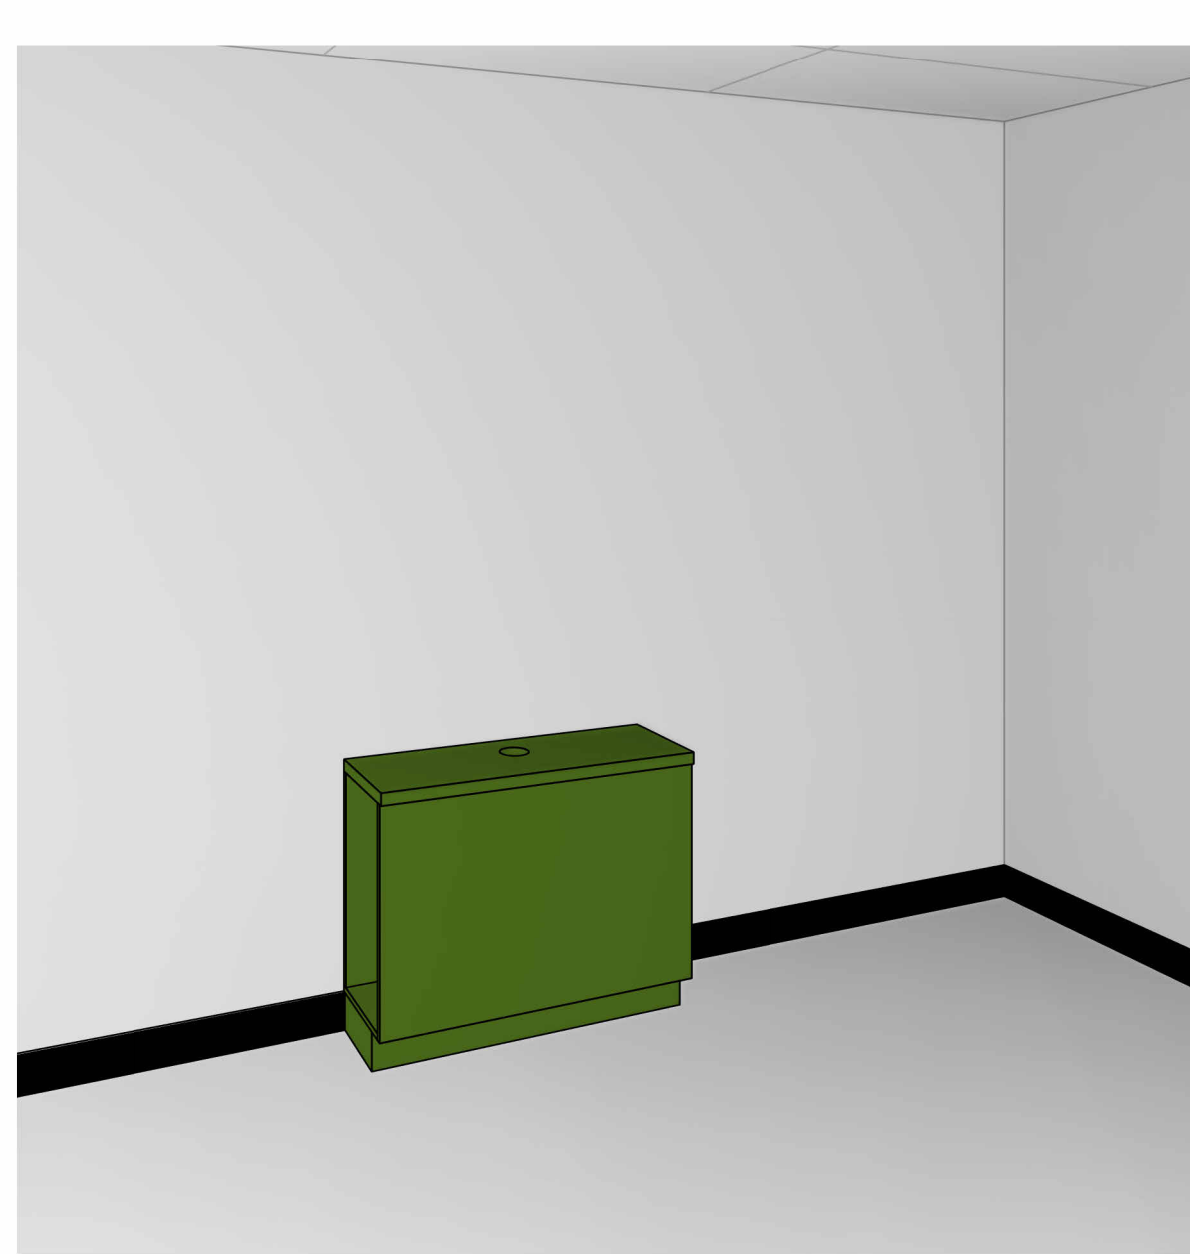

REVISIONS		
Rev	Description	Date
T1	TENDER ISSUE	12.03.2026

DO NOT SCALE THIS DRAWINGS


TENDER ISSUE




Project Details
MAIN WAREHOUSE REFURBISHMENT
Address
STANWELL POWER STATION
Drawing Title
INTERNAL ELEVATIONS 2 - ARCHIVES, PASSAGE & SMALL MEET




Scale: 1 : 50	Rev: T1
Date: JAN 2025	
Drawn: Author	
Project No: 25_003	Drawing No: A3-601

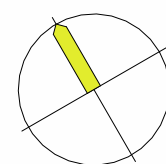

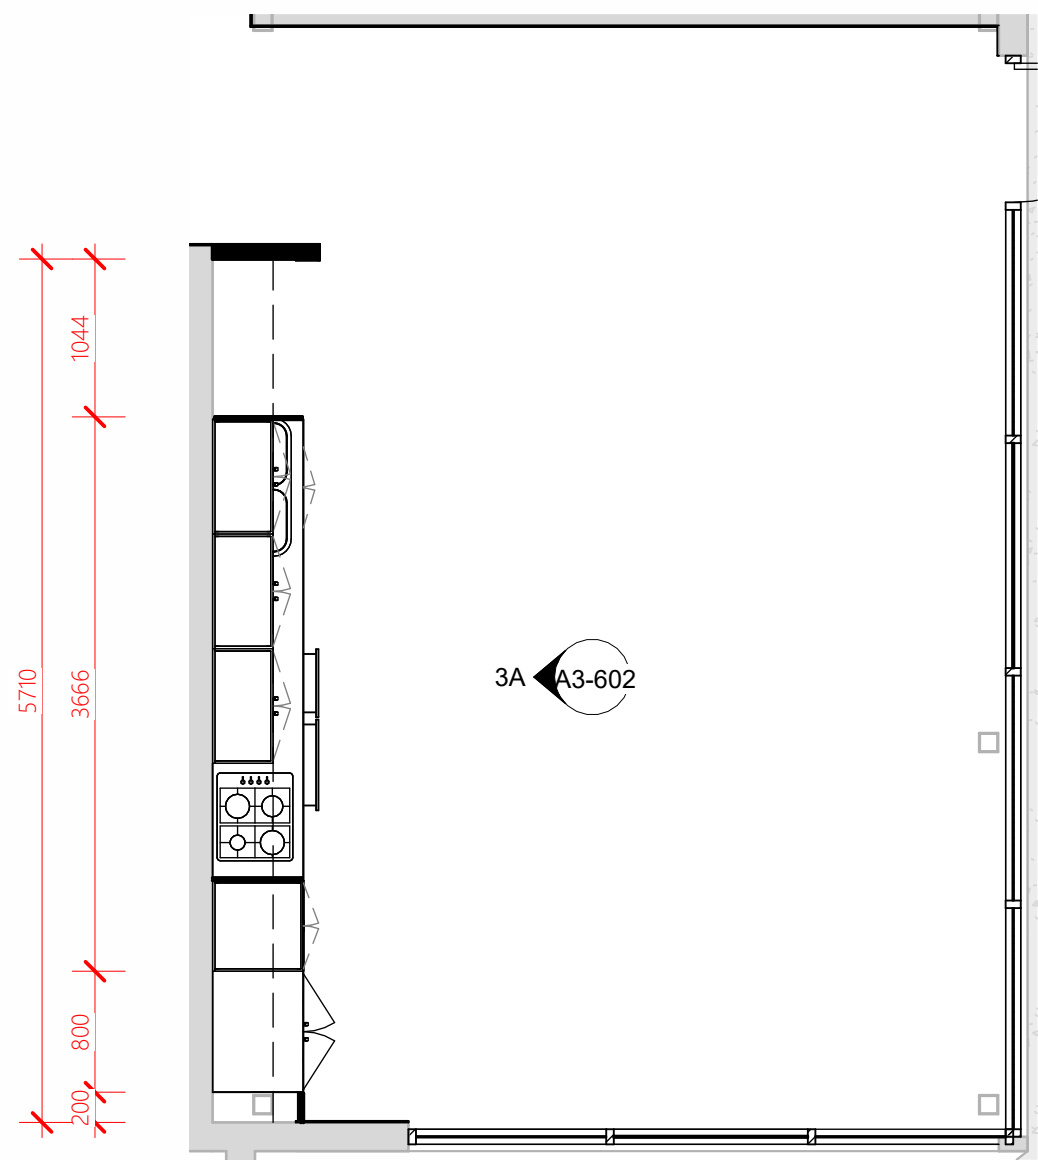

Internal Plan 3

1 : 50

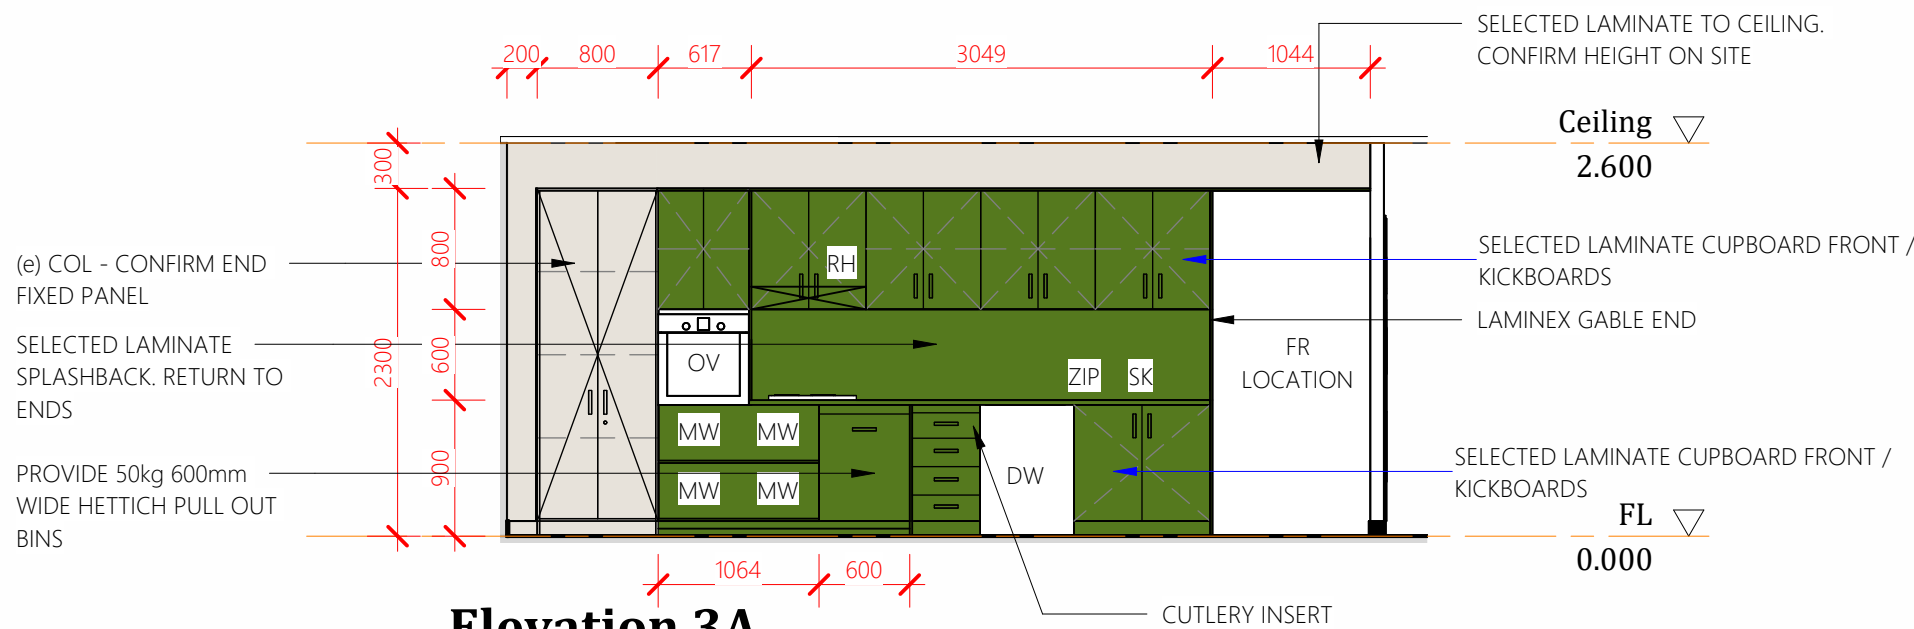

Elevation 3A

1 : 50



REVISIONS

Rev	Description	Date
T1	TENDER ISSUE	12.03.2026

DO NOT SCALE THIS DRAWINGS




TENDER ISSUE




Project Details
MAIN WAREHOUSE REFURBISHMENT
Address
STANWELL POWER STATION
Drawing Title
INTERNAL ELEVATIONS 3 - LUNCH ROOM



Scale: 1 : 50	Rev: T1
Date: JAN 2025	
Drawn: Author	
Project No: 25_003	Drawing No: A3-602

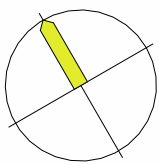

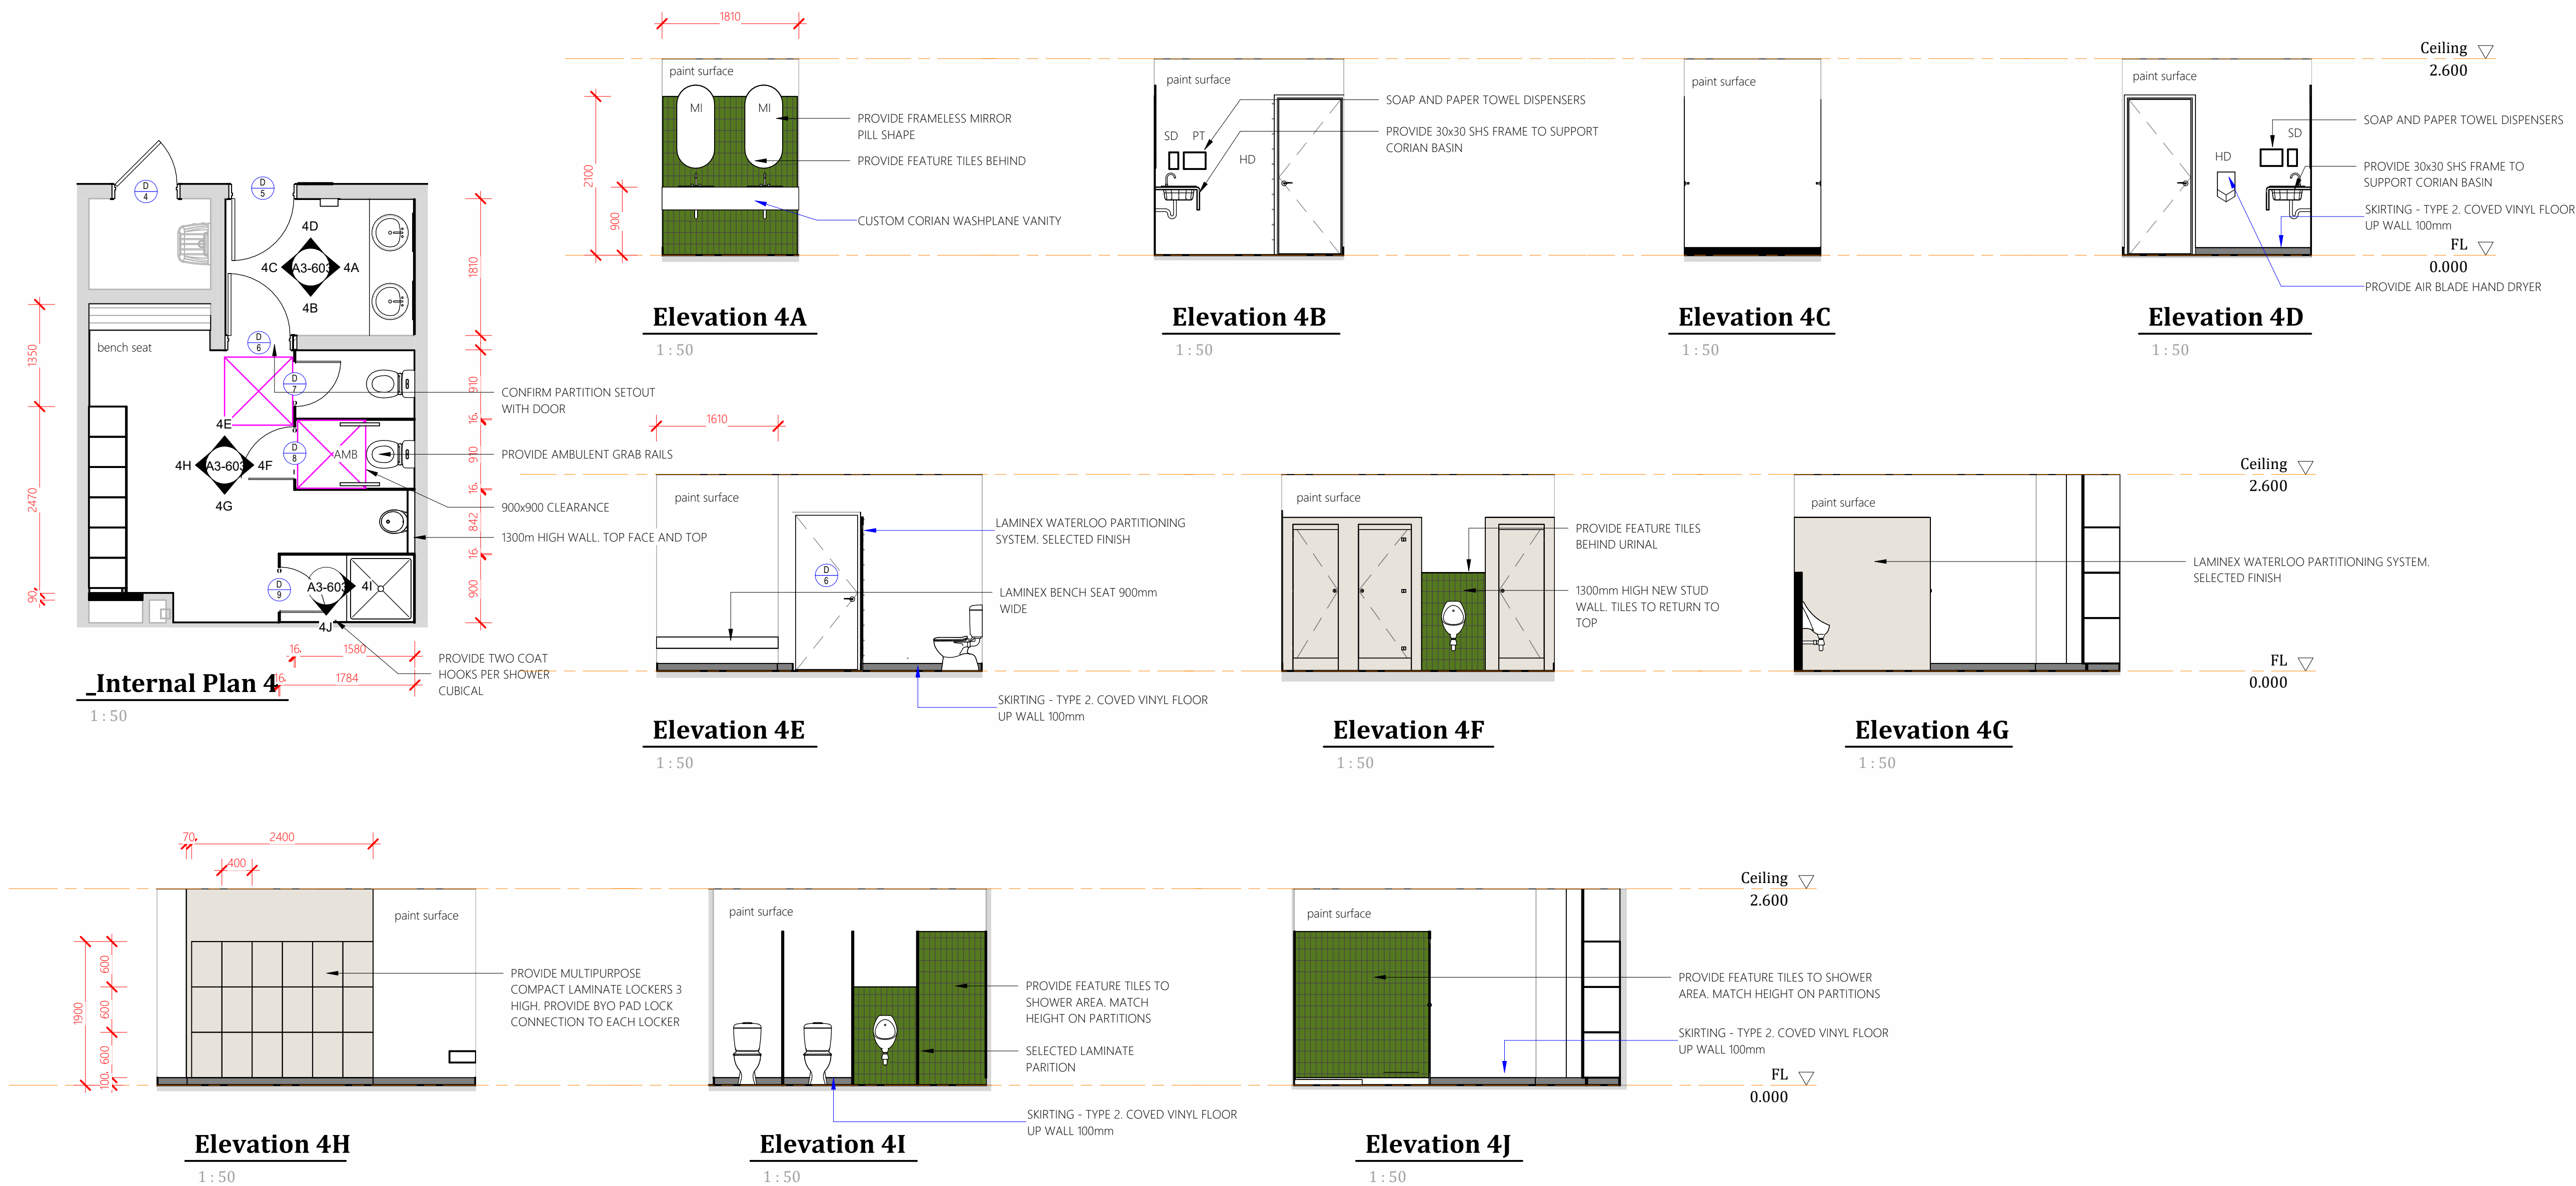

REVISIONS		
Rev	Description	Date
T1	TENDER ISSUE	12.03.2026

DO NOT SCALE THIS DRAWINGS



TENDER ISSUE

Client



Project Details

MAIN WAREHOUSE REFURBISHMENT

Address

STANWELL POWER STATION

Drawing Title


INTERNAL ELEVATIONS 4 - MALE AMENITIES

**designelements**
BUILDING DESIGNERS

0483 988 655 **M**
info@designelements.com.au **E**

QBCC No: 1247120 BDAQ No: 0001677



Scale: 1:50 Rev: **T1**
Date: JAN 2025
Drawn: Author
Project No: Drawing No:
25_003 A3-603

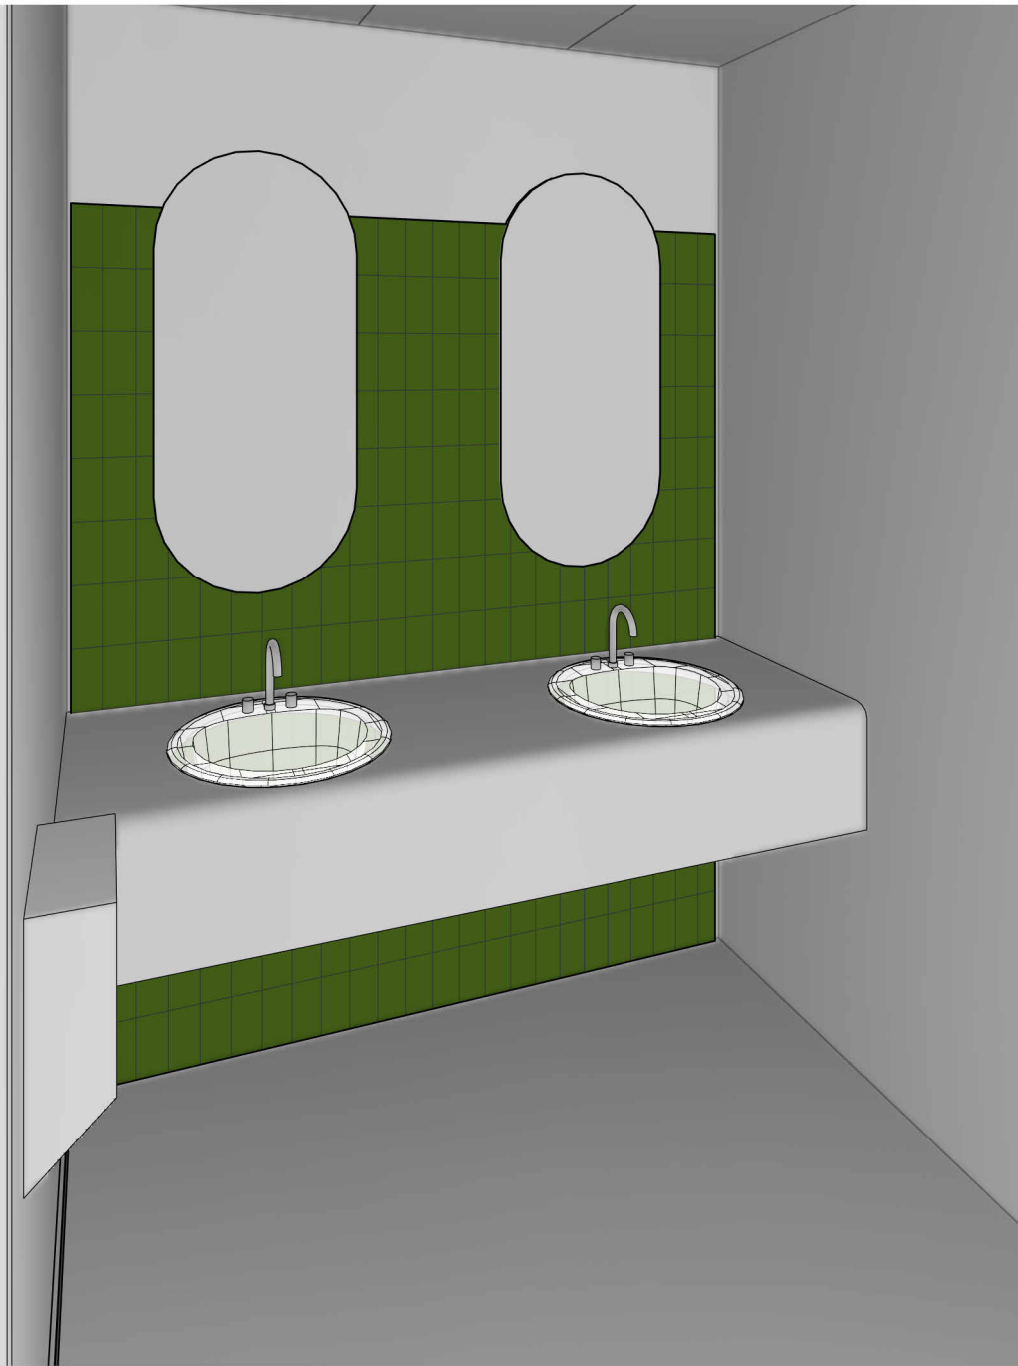

REVISIONS


Rev	Description	Date
T1	TENDER ISSUE	12.03.2026

DO NOT SCALE THIS DRAWINGS

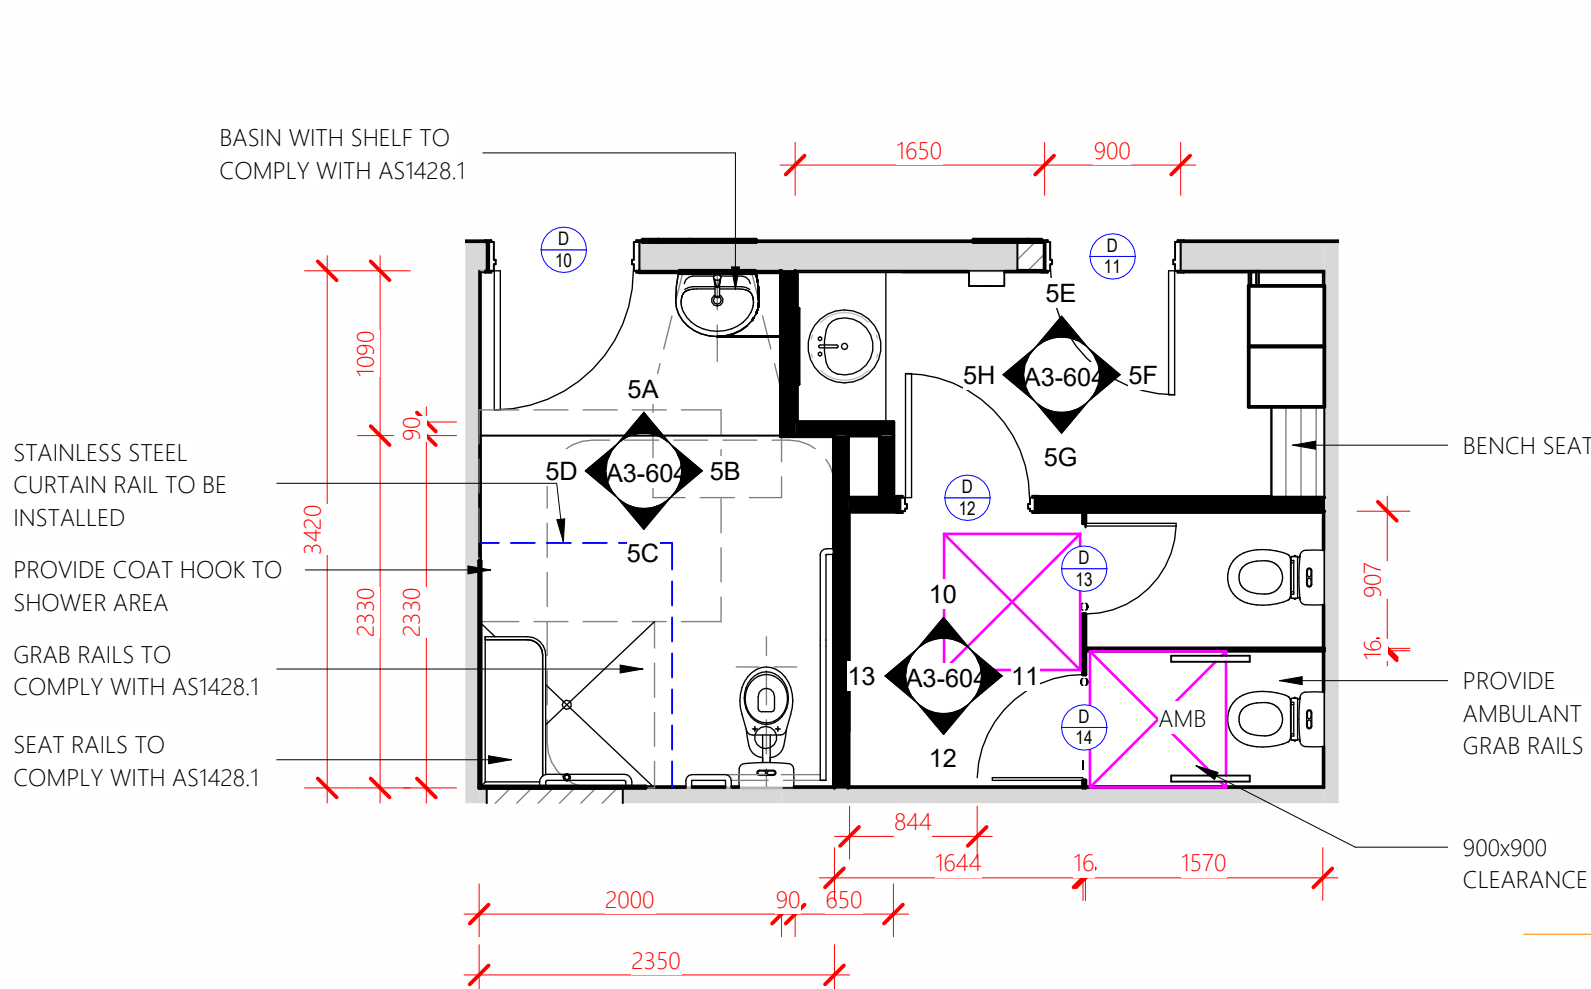 

Internal Plan 5

1 : 50

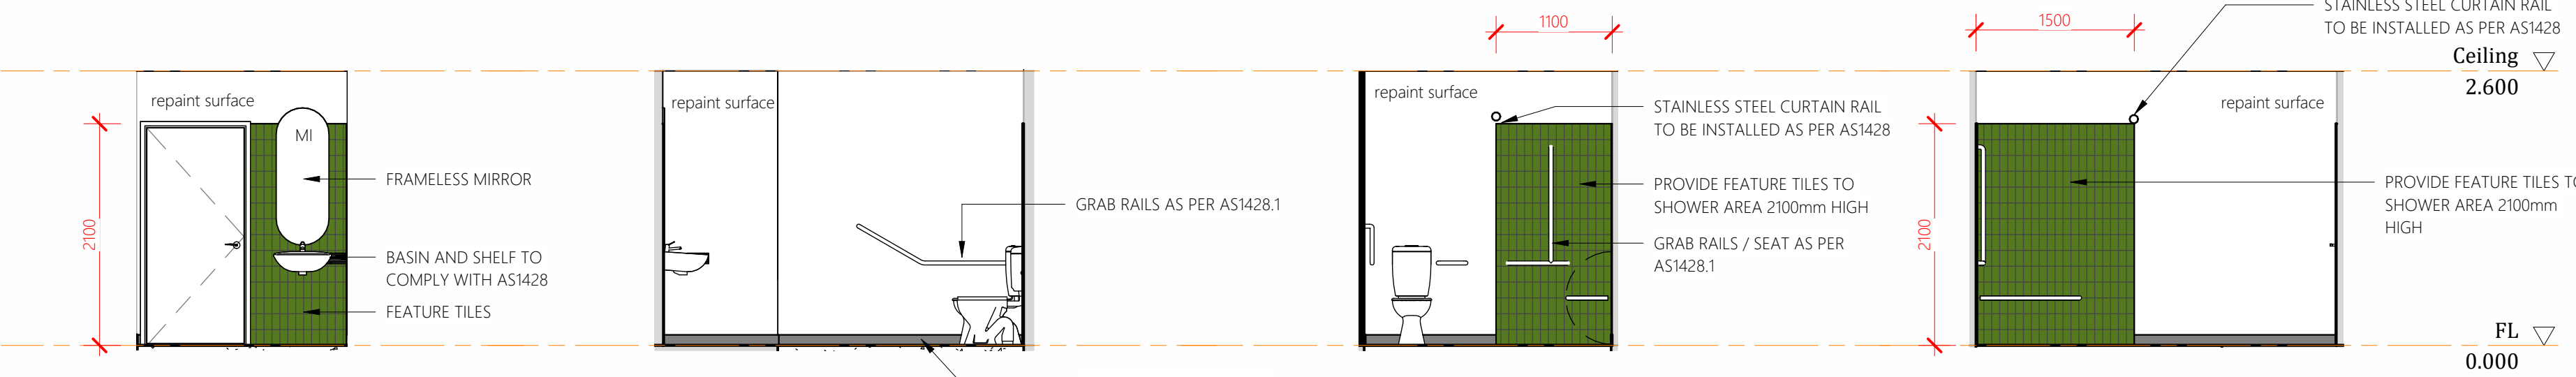

Elevation 5A

1 : 50

Elevation 5B


1 : 50

Elevation 5C

1 : 50

Elevation 5D

1 : 50

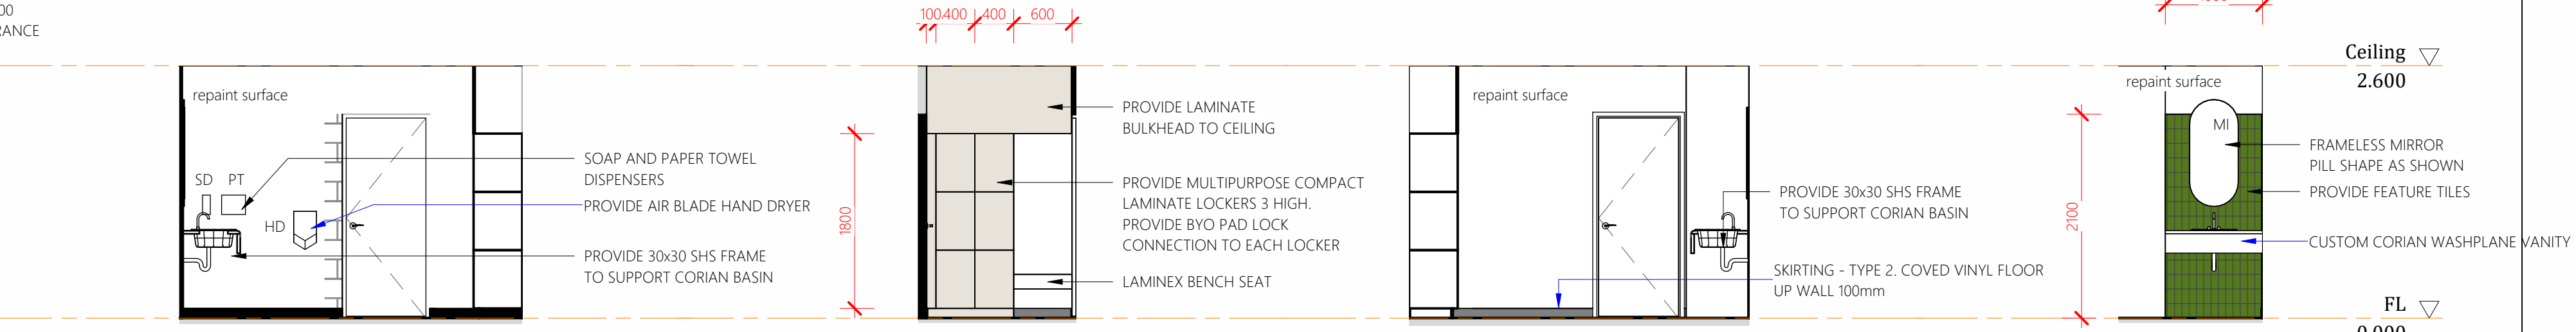

Elevation 5E

1 : 50

Elevation 5F

1 : 50

Elevation 5G

1 : 50

Elevation 5H

1 : 50



Elevation 5I

1 : 50

Elevation 5J


1 : 50

Elevation 5K

1 : 50

Elevation 5L

1 : 50

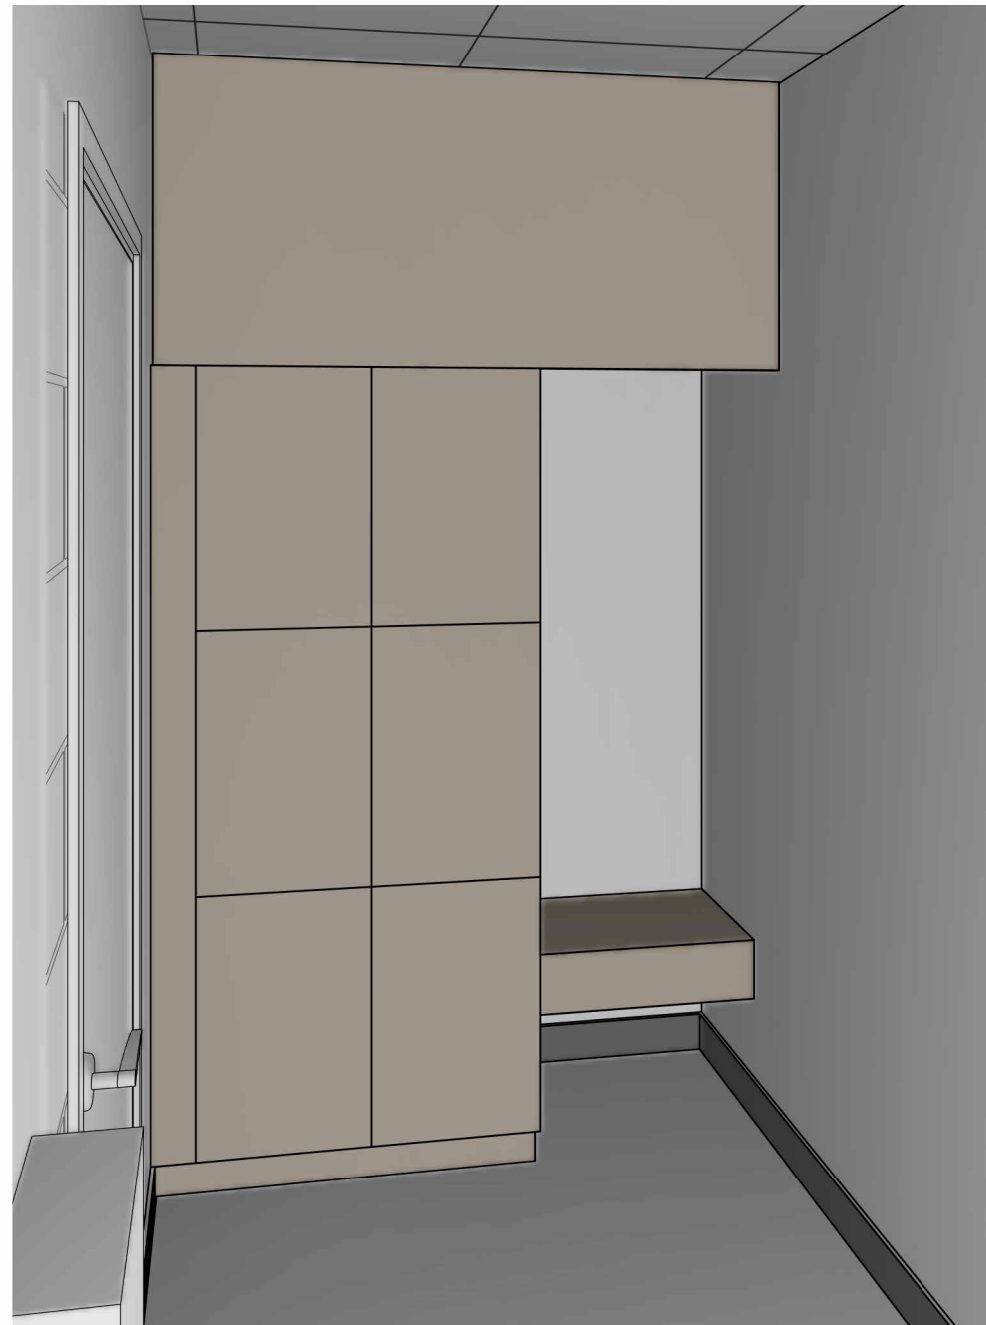

TENDER ISSUE



Project Details
MAIN WAREHOUSE REFURBISHMENT
Address
STANWELL POWER STATION
Drawing Title
INTERNAL ELEVATIONS 5 - PWD & FEMALE AMENITIES


dezi^{ne}lements
BUILDING DESIGNERS

0483 988 655 M
info@dezi^{ne}lements.com.au E

QBCC No: 1247120 BDAQ No: 0001677


Scale: 1 : 50 Rev: T1
Date: JAN 2025
Drawn: Author
Project No: Drawing No:
25_003 A3-604

Door Schedule	
Door NO.	Type Mark
1	TYPE A
2	TYPE B
3	TYPE B
4	TYPE C
5	TYPE D
6	TYPE D
7	TYPE E
8	TYPE F
9	TYPE E
10	TYPE G
11	TYPE D
12	TYPE D
13	TYPE E
14	TYPE F
15	TYPE H
16	TYPE H
17	TYPE I

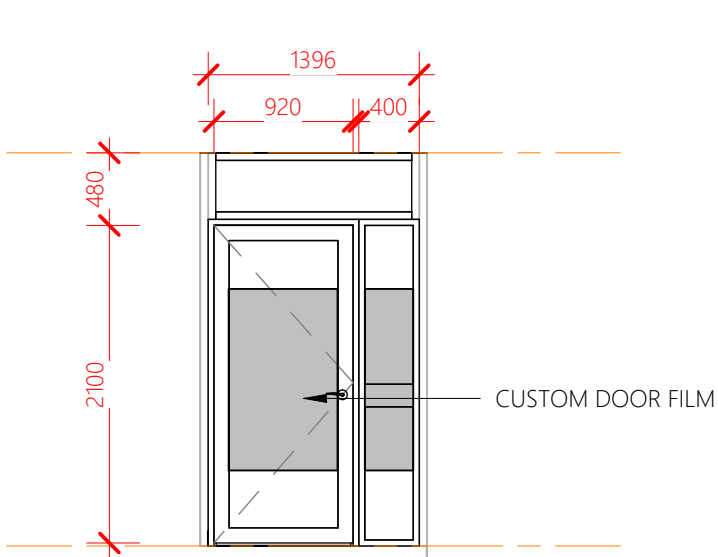


DOOR TYPE A

LOCATION: EXTERNAL
DOOR TYPE: HINGED ALUMINIUM FRAMED SINGLE DOOR
FRAME TYPE: G.JAMES 475 SERIES
FRAME FINISH: SELECTED POWDERCOAT
DOOR FINISH: SELECTED POWDERCOAT
INFILL: GREY SAFETY GLASS
THRESHOLD: DOOR CLOSER, DOOR STOP
SEALS: DOOR CLOSER, DOOR STOP
LOCK: REFER HARDWARE SCHEDULE
HARDWARE: DOOR CLOSER, DOOR STOP

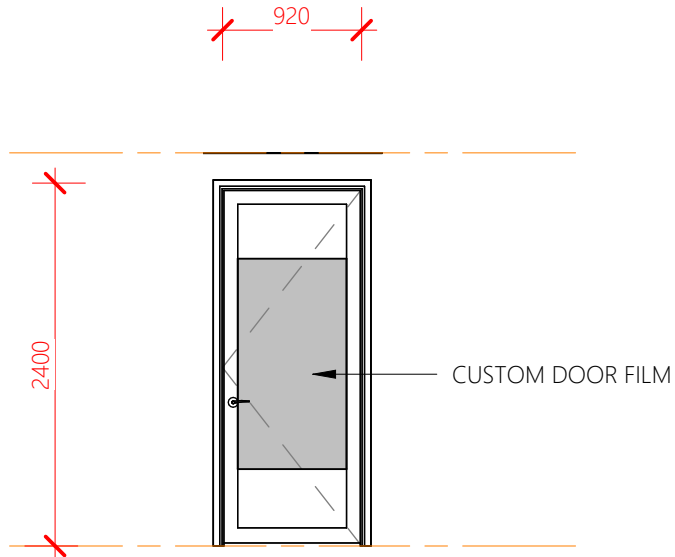


DOOR TYPE B

LOCATION: INTERNAL
DOOR TYPE: HINGED ALUMINIUM FRAMED SINGLE DOOR
FRAME TYPE: G.JAMES 475 SERIES
FRAME FINISH: SELECTED POWDERCOAT
DOOR FINISH: SELECTED POWDERCOAT
INFILL: GREY SAFETY GLASS
SEALS: NONE
LOCK: REFER HARDWARE SCHEDULE
HARDWARE: DOOR CLOSER, DOOR STOP

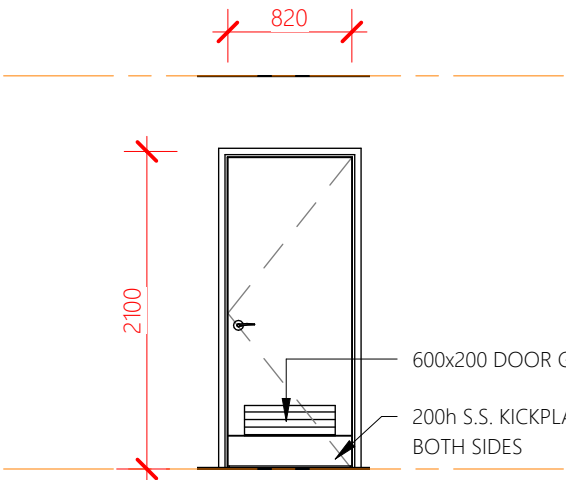


DOOR TYPE C

LOCATION: CLEANER / SERVICE
DOOR TYPE: 40mm HINGED SOLID CORE SINGLE DOOR
FRAME TYPE: TIMBER
FRAME FINISH: PAINT
DOOR FINISH: PAINT
SEALS: NONE
LOCK: REFER HARDWARE SCHEDULE
HARDWARE: KICK PLATES, DOOR CLOSER, DOOR STOP

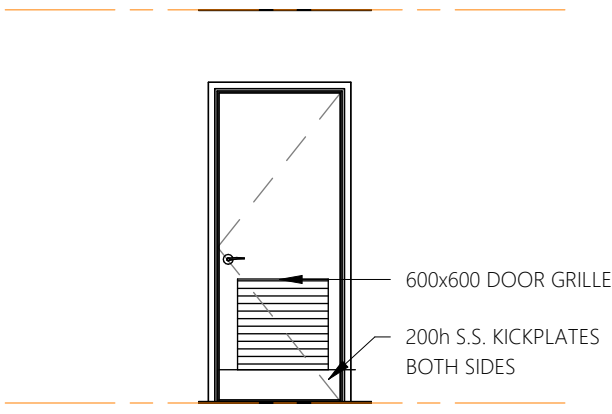


DOOR TYPE D

LOCATION: FEMALE AMENITIES
DOOR TYPE: 40mm HINGED SOLID CORE SINGLE DOOR
FRAME TYPE: TIMBER
FRAME FINISH: PAINT
DOOR FINISH: PAINT
SEALS: NONE
LOCK: PUSH PULL PLATES (NO LOCKING)
HARDWARE: KICK PLATES, DOOR CLOSER, DOOR STOP

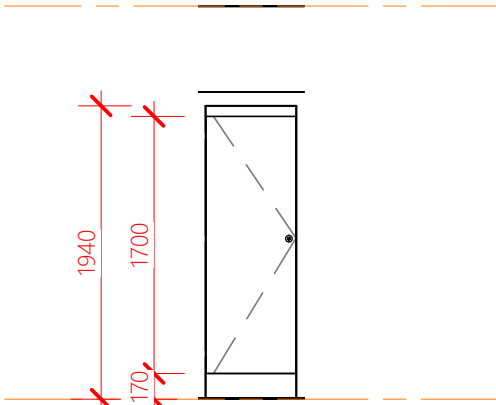


DOOR TYPE E

LOCATION: AMENITIES
DOOR TYPE: 13mm COMPACT LAMINATE PARTITION DOOR
FRAME TYPE: PROVIDE 30° PRIVACY BEVEL
DOOR FINISH: SELECTED LAMINATE
SEALS: NONE
LOCK: METLAM XCEL SLIDE LOCK & INDICATOR.
HARDWARE:

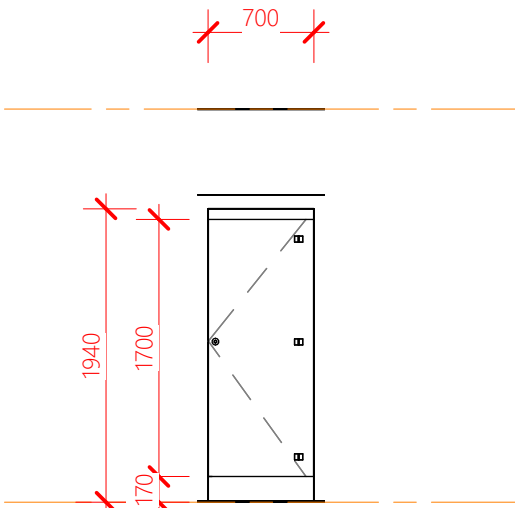


DOOR TYPE F

LOCATION: AMENITIES (AMBULANT)
DOOR TYPE: 13mm COMPACT LAMINATE PARTITION DOOR
FRAME TYPE: PROVIDE 30° PRIVACY BEVEL
DOOR FINISH: SELECTED LAMINATE
SEALS: NONE
LOCK: METLAM XCEL SLIDE LOCK & INDICATOR.
HARDWARE:

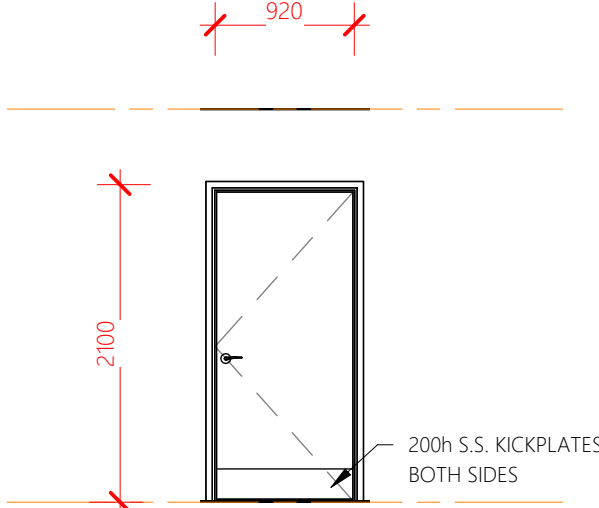


DOOR TYPE G

LOCATION: PWD
DOOR TYPE: 40mm HINGED SOLID CORE SINGLE DOOR
FRAME TYPE: TIMBER
FRAME FINISH: PAINT
DOOR FINISH: PAINT
SEALS: NONE
LOCK: PRIVACY LATCH LEVER HANDLE WITH INDICATOR BOLT
HARDWARE: KICK PLATES, DOOR CLOSER, DOOR STOP

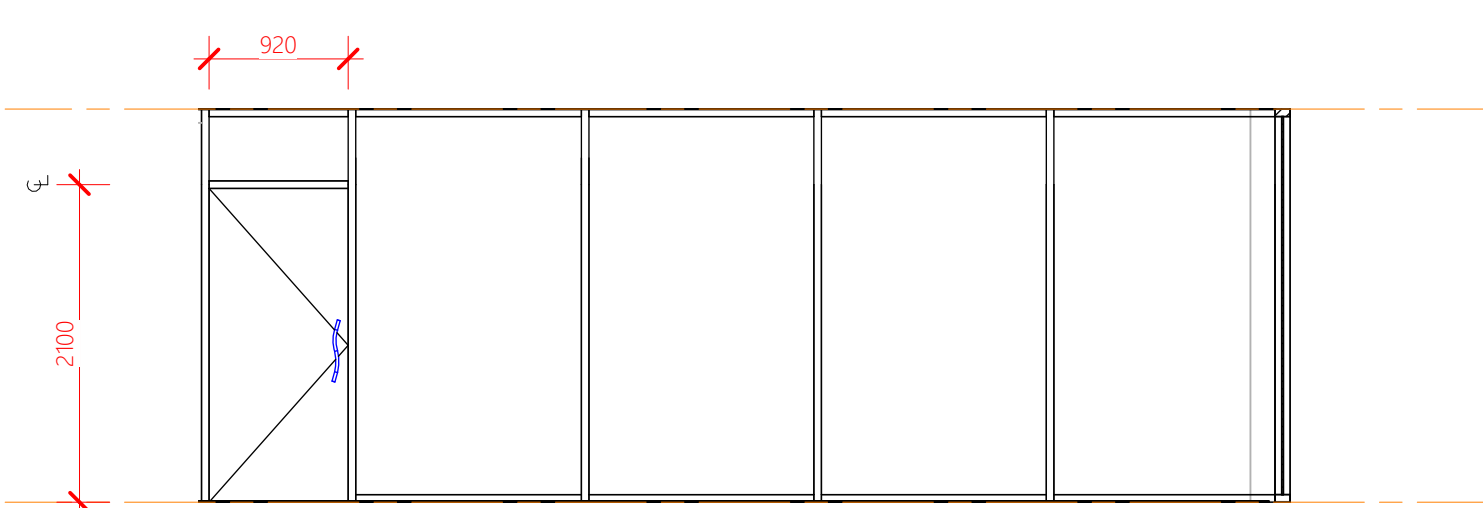


DOOR TYPE H

LOCATION: EXTERNAL
DOOR TYPE: HINGED ALUMINIUM FRAMED SINGLE DOOR
FRAME TYPE: G.JAMES 475 SERIES
FRAME FINISH: SELECTED POWDERCOAT
DOOR FINISH: SELECTED POWDERCOAT
INFILL: GREY SAFETY GLASS
THRESHOLD: REFER HARDWARE SCHEDULE
SEALS: REFER HARDWARE SCHEDULE
LOCK: REFER HARDWARE SCHEDULE
HARDWARE: DOOR CLOSER, DOOR STOP

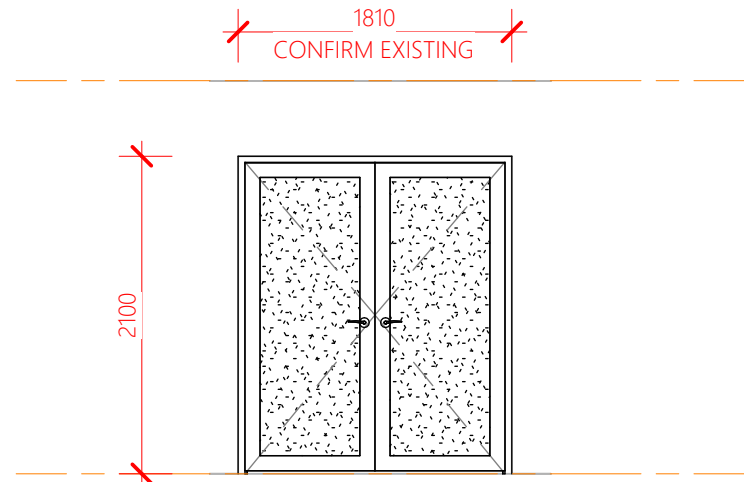

DOOR TYPE I

LOCATION: EXTERNAL, MECH STORES
DOOR TYPE: HINGED ALUMINIUM FRAMED DOUBLE DOOR
FRAME TYPE: G.JAMES 475 SERIES
FRAME FINISH: SELECTED POWDERCOAT
DOOR FINISH: SELECTED POWDERCOAT
INFILL: 9mm CFC, PAINT FINISH
THRESHOLD:
SEALS: REFER HARDWARE SCHEDULE
LOCK: VESTIBULE LOCK
HARDWARE: REFER HARDWARE SCHEDULE

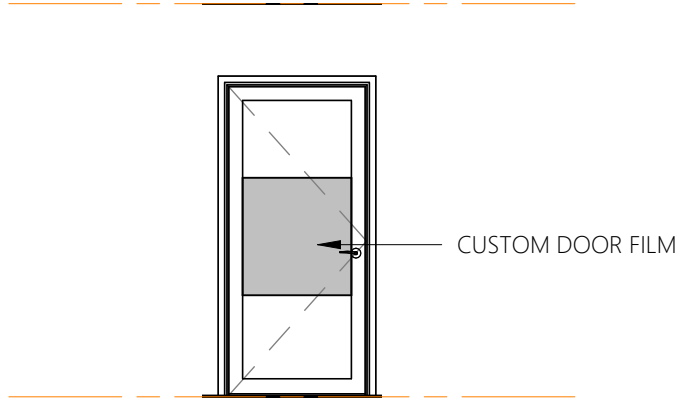


DOOR TYPE J

LOCATION: INTERNAL
DOOR TYPE: HINGED ALUMINIUM FRAMED SINGLE DOOR
FRAME TYPE: G.JAMES 475 SERIES
FRAME FINISH: SELECTED POWDERCOAT
DOOR FINISH: SELECTED POWDERCOAT
INFILL: GREY SAFETY GLASS
SEALS: NONE
LOCK: REFER HARDWARE SCHEDULE
HARDWARE: DOOR CLOSER, DOOR STOP

REVISIONS		
Rev	Description	Date
T1	TENDER ISSUE	12.03.2026

DO NOT SCALE THIS DRAWINGS

 

TENDER ISSUE



Project Details
MAIN WAREHOUSE REFURBISHMENT
Address
STANWELL POWER STATION
Drawing Title
DOOR SCHEDULE

dezinelements
BUILDING DESIGNERS

0483 988 655 **M**
info@dezi nelements.com.au **E**


QBCC No: 1247120 BDAQ No: 0001677

Scale: 1 : 50 Rev: **T1**
Date: JAN 2025
Drawn: Author

Project No: Drawing No:
25_003 A3-700

REVISIONS		
Rev	Description	Date
T1	TENDER ISSUE	12.03.2026

DO NOT SCALE THIS DRAWINGS

 

TENDER ISSUE

Client



Project Details

**MAIN WAREHOUSE
REFURBISHMENT**

Address

**STANWELL POWER
STATION**

Drawing Title


WINDOW SCHEDULES


BUILDING DESIGNERS

0483 988 655 
info@deziignelements.com.au 

QBCC No: 1247120 BDAQ No: 0001677


Scale: 1 : 50 Rev: **T1**
Date: JAN 2025
Drawn: Author
Project No: Drawing No:
25_003 A3-701

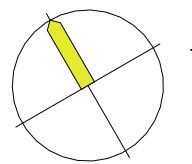

1800

1350

1050

 


WINDOW TYPE A

LOCATION: REGISTRY
FRAME TYPE: G.JAMES 475 SERIES
FRAME FINISH: SELECTED POWDERCOAT
WINDOW: FIXED GLASS
GLASS: SAFETY GLASS

2400

600

1800

 


WINDOW TYPE B

LOCATION: REGISTRY
FRAME TYPE: G.JAMES 475 SERIES
FRAME FINISH: SELECTED POWDERCOAT
WINDOW: FIXED GLASS
GLASS: SAFETY GLASS

4675

2600

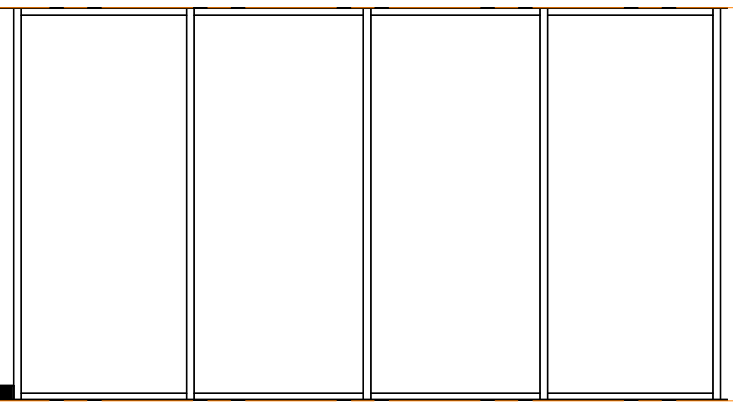


WINDOW TYPE C

LOCATION: EXTERNAL
FRAME TYPE: G.JAMES 475 SERIES
FRAME FINISH: SELECTED POWDERCOAT
WINDOW: FIXED GLASS
GLASS: SAFETY GLASS

2285

2600

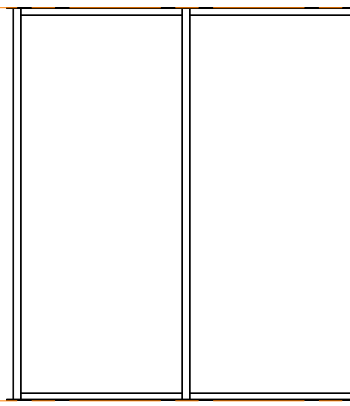


WINDOW TYPE D

LOCATION: EXTERNAL
FRAME TYPE: G.JAMES 475 SERIES
FRAME FINISH: SELECTED POWDERCOAT
WINDOW: FIXED GLASS
GLASS: SAFETY GLASS

3500

2600

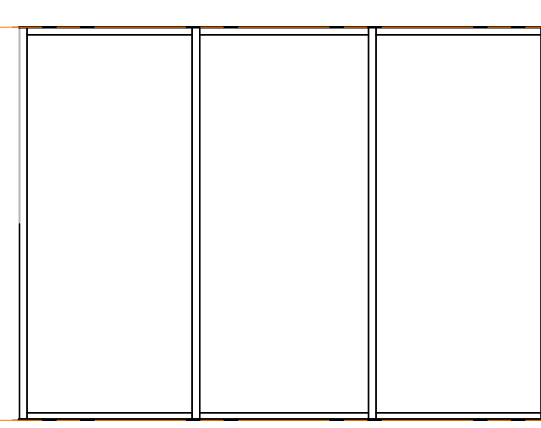


WINDOW TYPE E

LOCATION: EXTERNAL
FRAME TYPE: G.JAMES 475 SERIES
FRAME FINISH: SELECTED POWDERCOAT
WINDOW: FIXED GLASS
GLASS: SAFETY GLASS

7100

2600

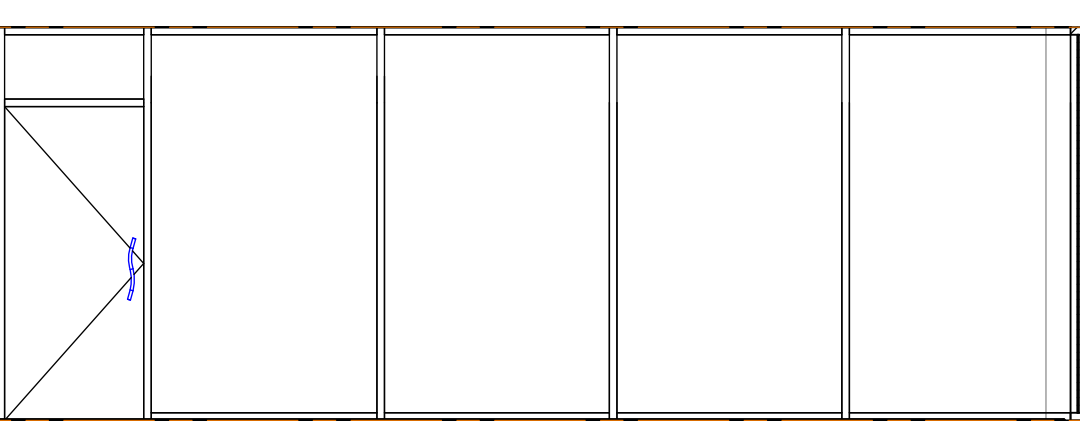


WINDOW TYPE F

LOCATION: EXTERNAL
FRAME TYPE: G.JAMES 475 SERIES
FRAME FINISH: SELECTED POWDERCOAT
WINDOW: FIXED GLASS
GLASS: SAFETY GLASS

3950

2600

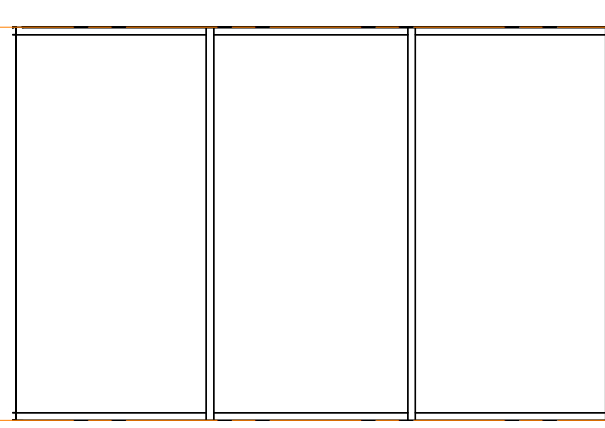

WINDOW TYPE G

LOCATION: EXTERNAL
FRAME TYPE: G.JAMES 475 SERIES
FRAME FINISH: SELECTED POWDERCOAT
WINDOW: FIXED GLASS
GLASS: SAFETY GLASS

_Window Schedule	
WINDOW NO.	Type Mark
1	TYPE A
2	TYPE B
3	TYPE B
4	TYPE C
5	TYPE D
6	TYPE E
7	TYPE F
8	TYPE G