



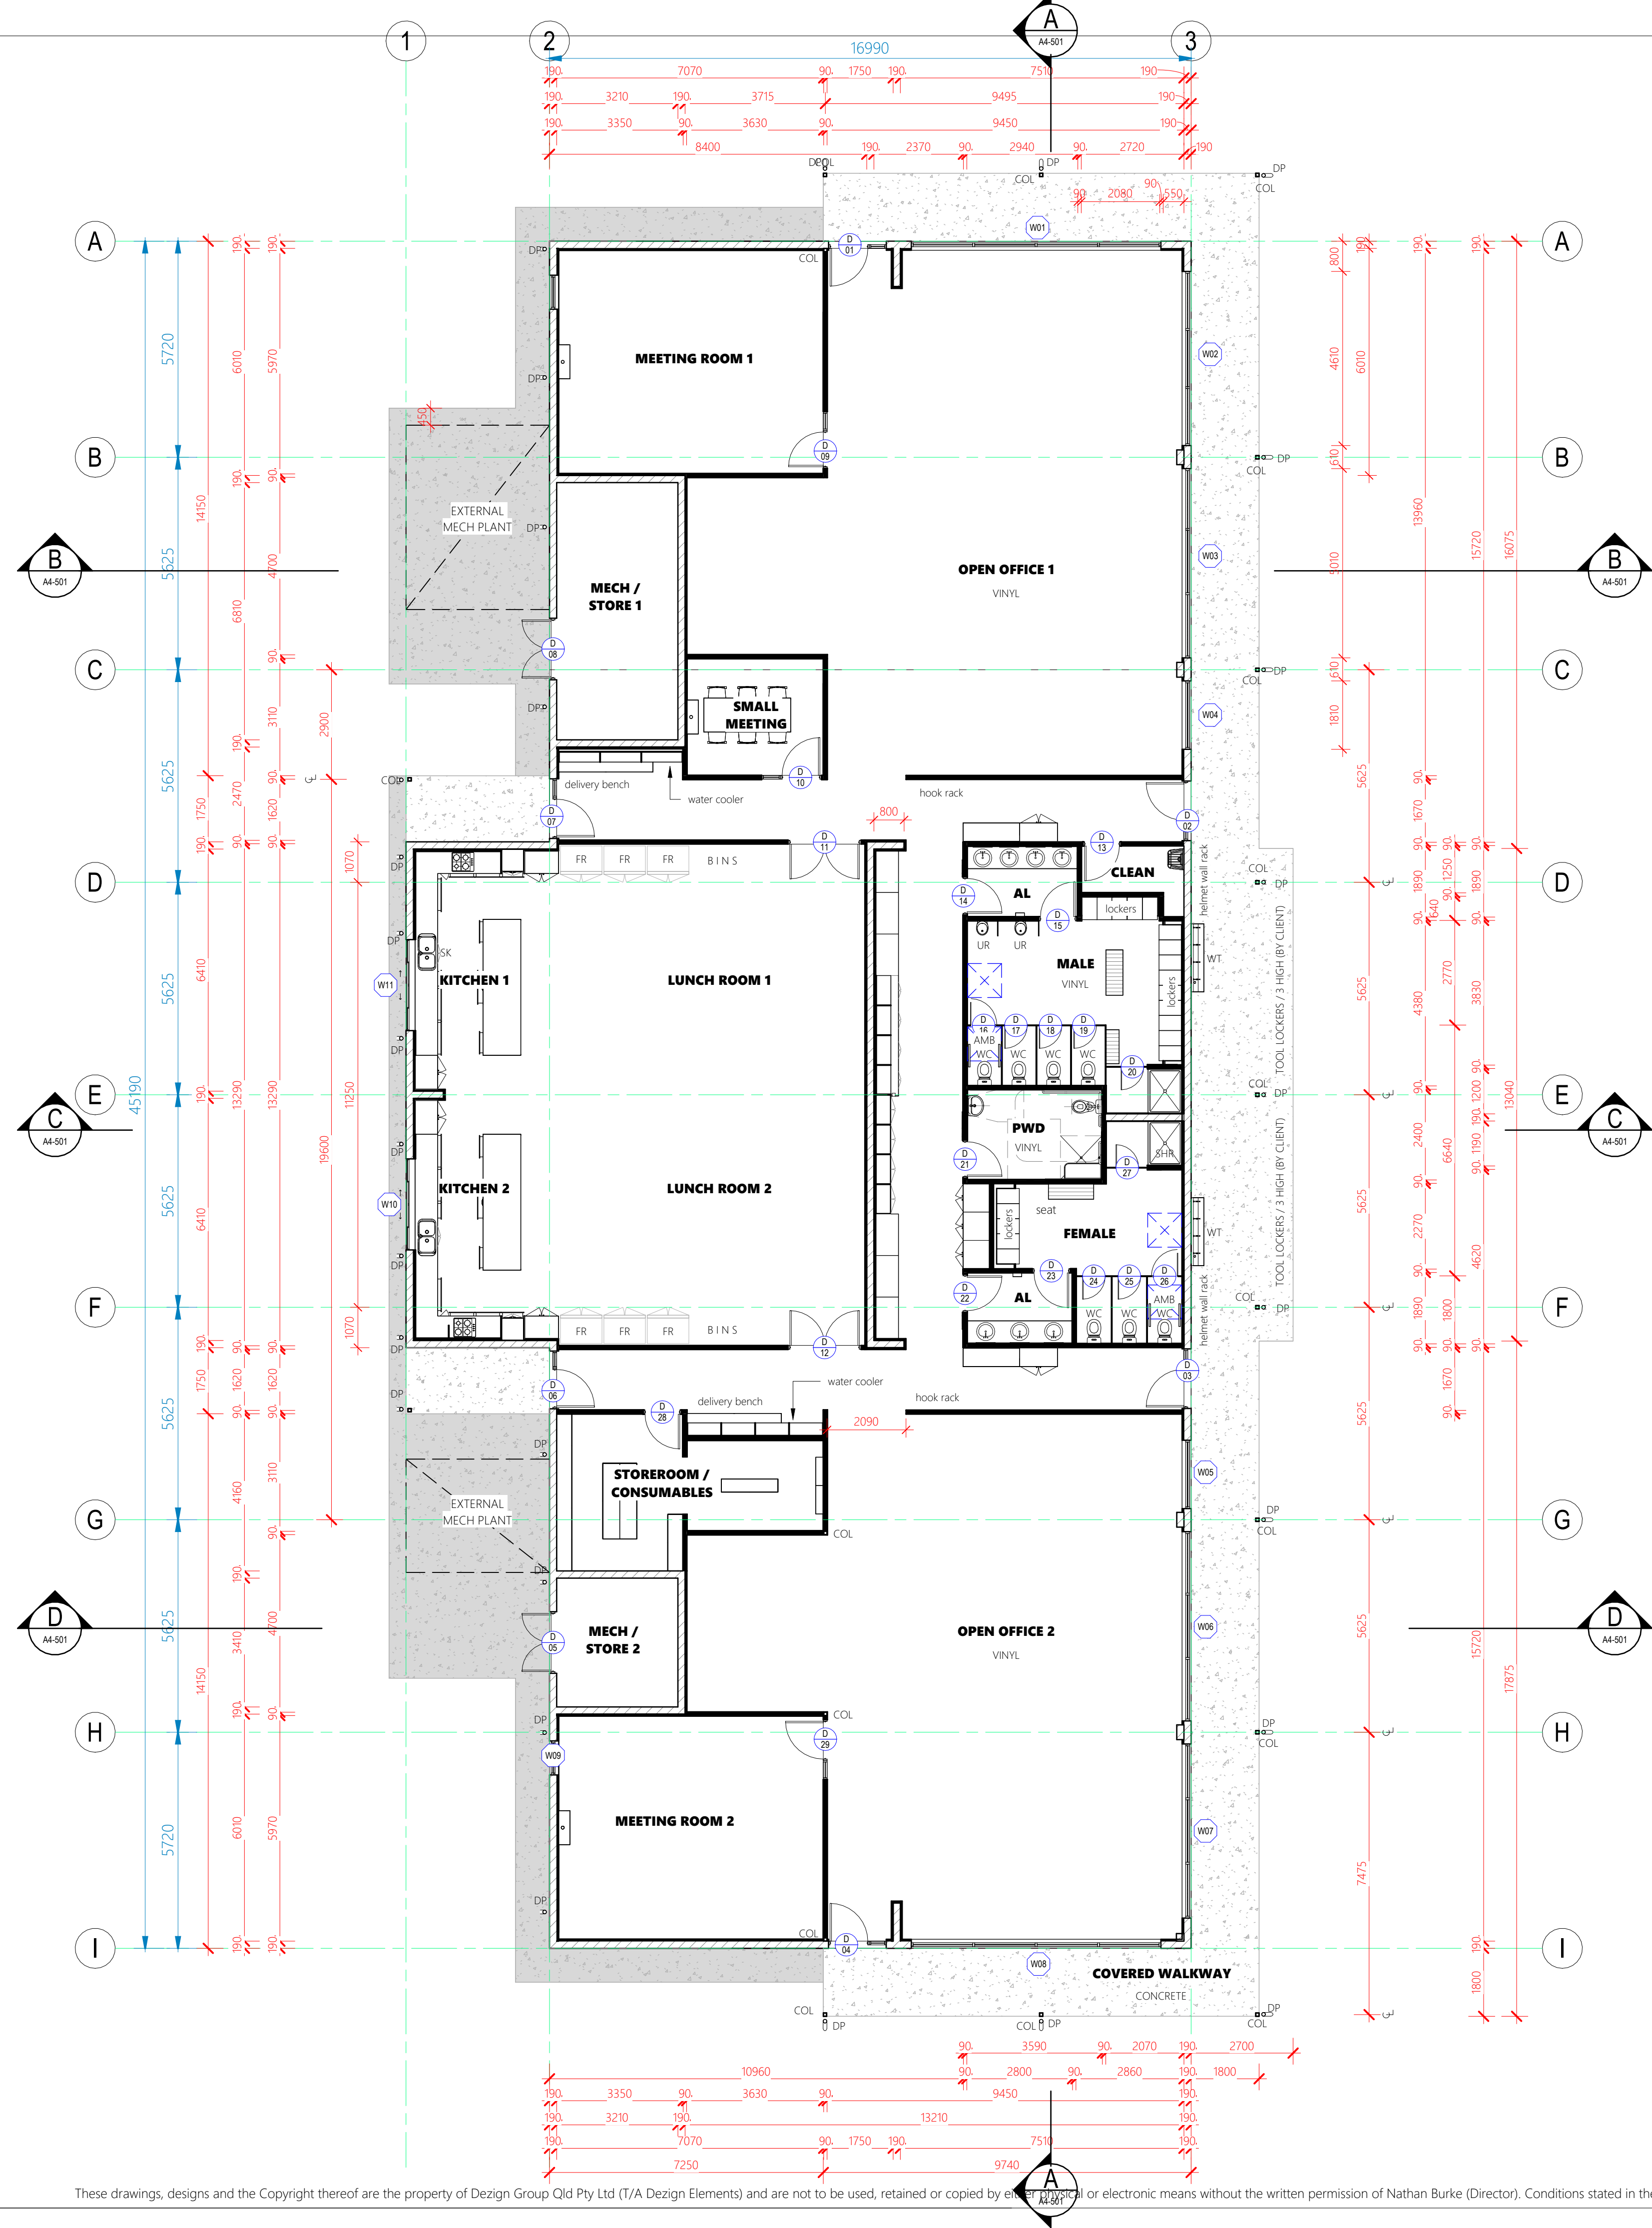

Proposed Floor Plan

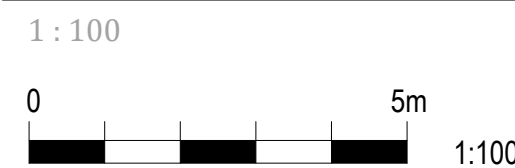

These drawings, designs and the Copyright thereof are the property of Design Group Qld Pty Ltd (T/A Design Elements) and are not to be used, retained or copied by any person or electronic means without the written permission of Nathan Burke (Director). Conditions stated in the terms and conditions. Design Elements accepts no responsibility for the completeness, accuracy or compatibility of electronically transferred documents.

REVISIONS		
Rev	Description	Date
T1	TENDER ISSUE	12.03.2026

DO NOT SCALE THIS DRAWINGS

KEYNOTE LEGEND

BSN	Basin
COL	Column
CON	Condenser
CPD	Cupboard
CS	Cleaners Sink
CT	Cooktop
DP	Downpipe
DW	Dish Washer
FAP	Fire Alarm Panel
FHR	Fire Hose Reel
FR	Fridge (By Client)
HD	Hand Driver (Air Blade)
L	Locker
OV	Oven
RH	Range Hood
DW	Dish Washer
SK	Sink
SB	Switch Board
UR	Urinal


TENDER ISSUE





Project Details	
OFFICE REFURBS	
Address	
STANWELL POWER STATION	
Drawing Title	
PROPOSED FLOOR PLAN	



0483 988 655 M	
info@designelements.com.au E	
QBCC No: 1247120 BDAQ No: 0001677	
Scale: 1 : 100	Rev: T1
Date: MAR 2026	
Drawn: Author	
Project No: 25_003	Drawing No: A4-300

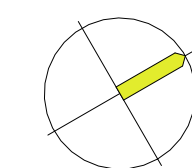


12/03/2026 7:55:07 PM

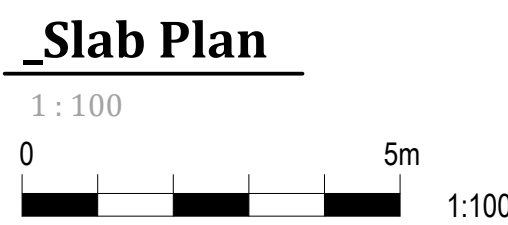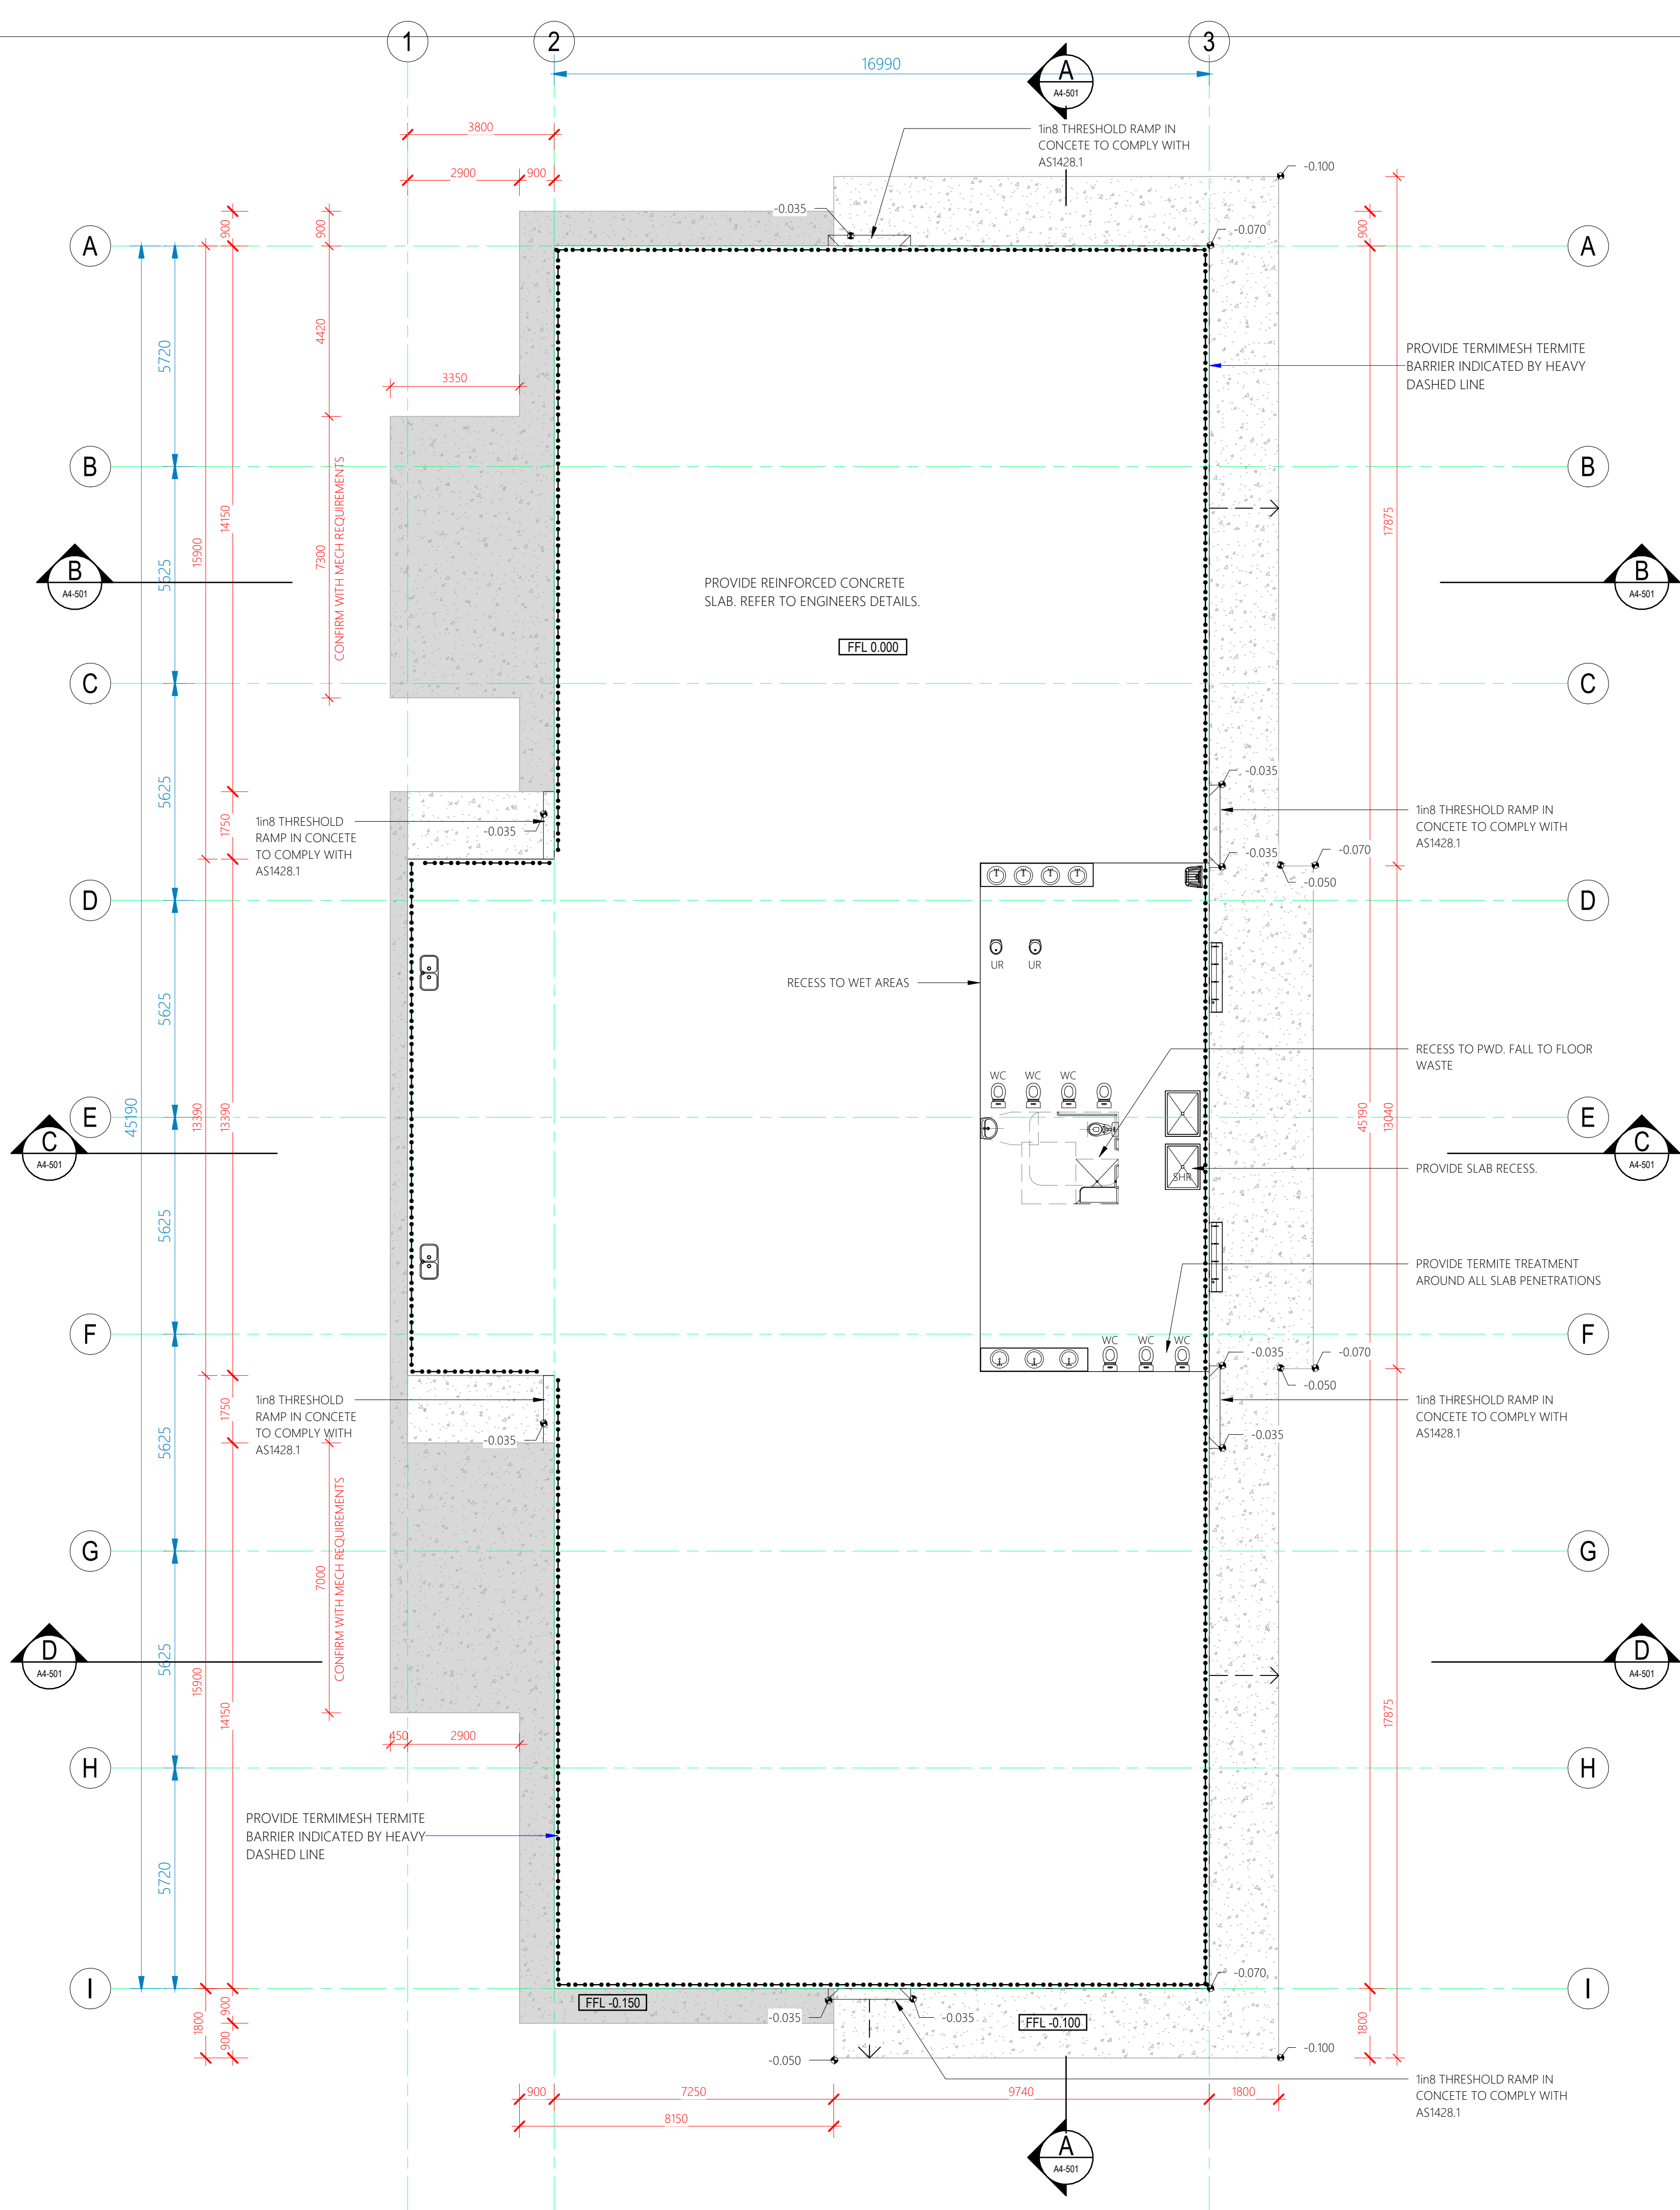

REVISIONS		
Rev	Description	Date
T1	TENDER ISSUE	12.03.2026

DO NOT SCALE THIS DRAWINGS

 

TENDER ISSUE

Client

 **stanwell**

Project Details

OFFICE REFURBS

Address

STANWELL POWER STATION

Drawing Title


PROPOSED SLAB SETOUT PLAN


 **designelements**
BUILDING DESIGNERS

0483 988 655 **M**
info@designelements.com.au **E**

QBCC No: 1247120 BDAQ No: 0001677


Scale: 1 : 100 Rev: **T1**
Date: MAR 2026
Drawn: Author
Project No: Drawing No:
25_003 A4-301

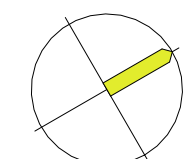

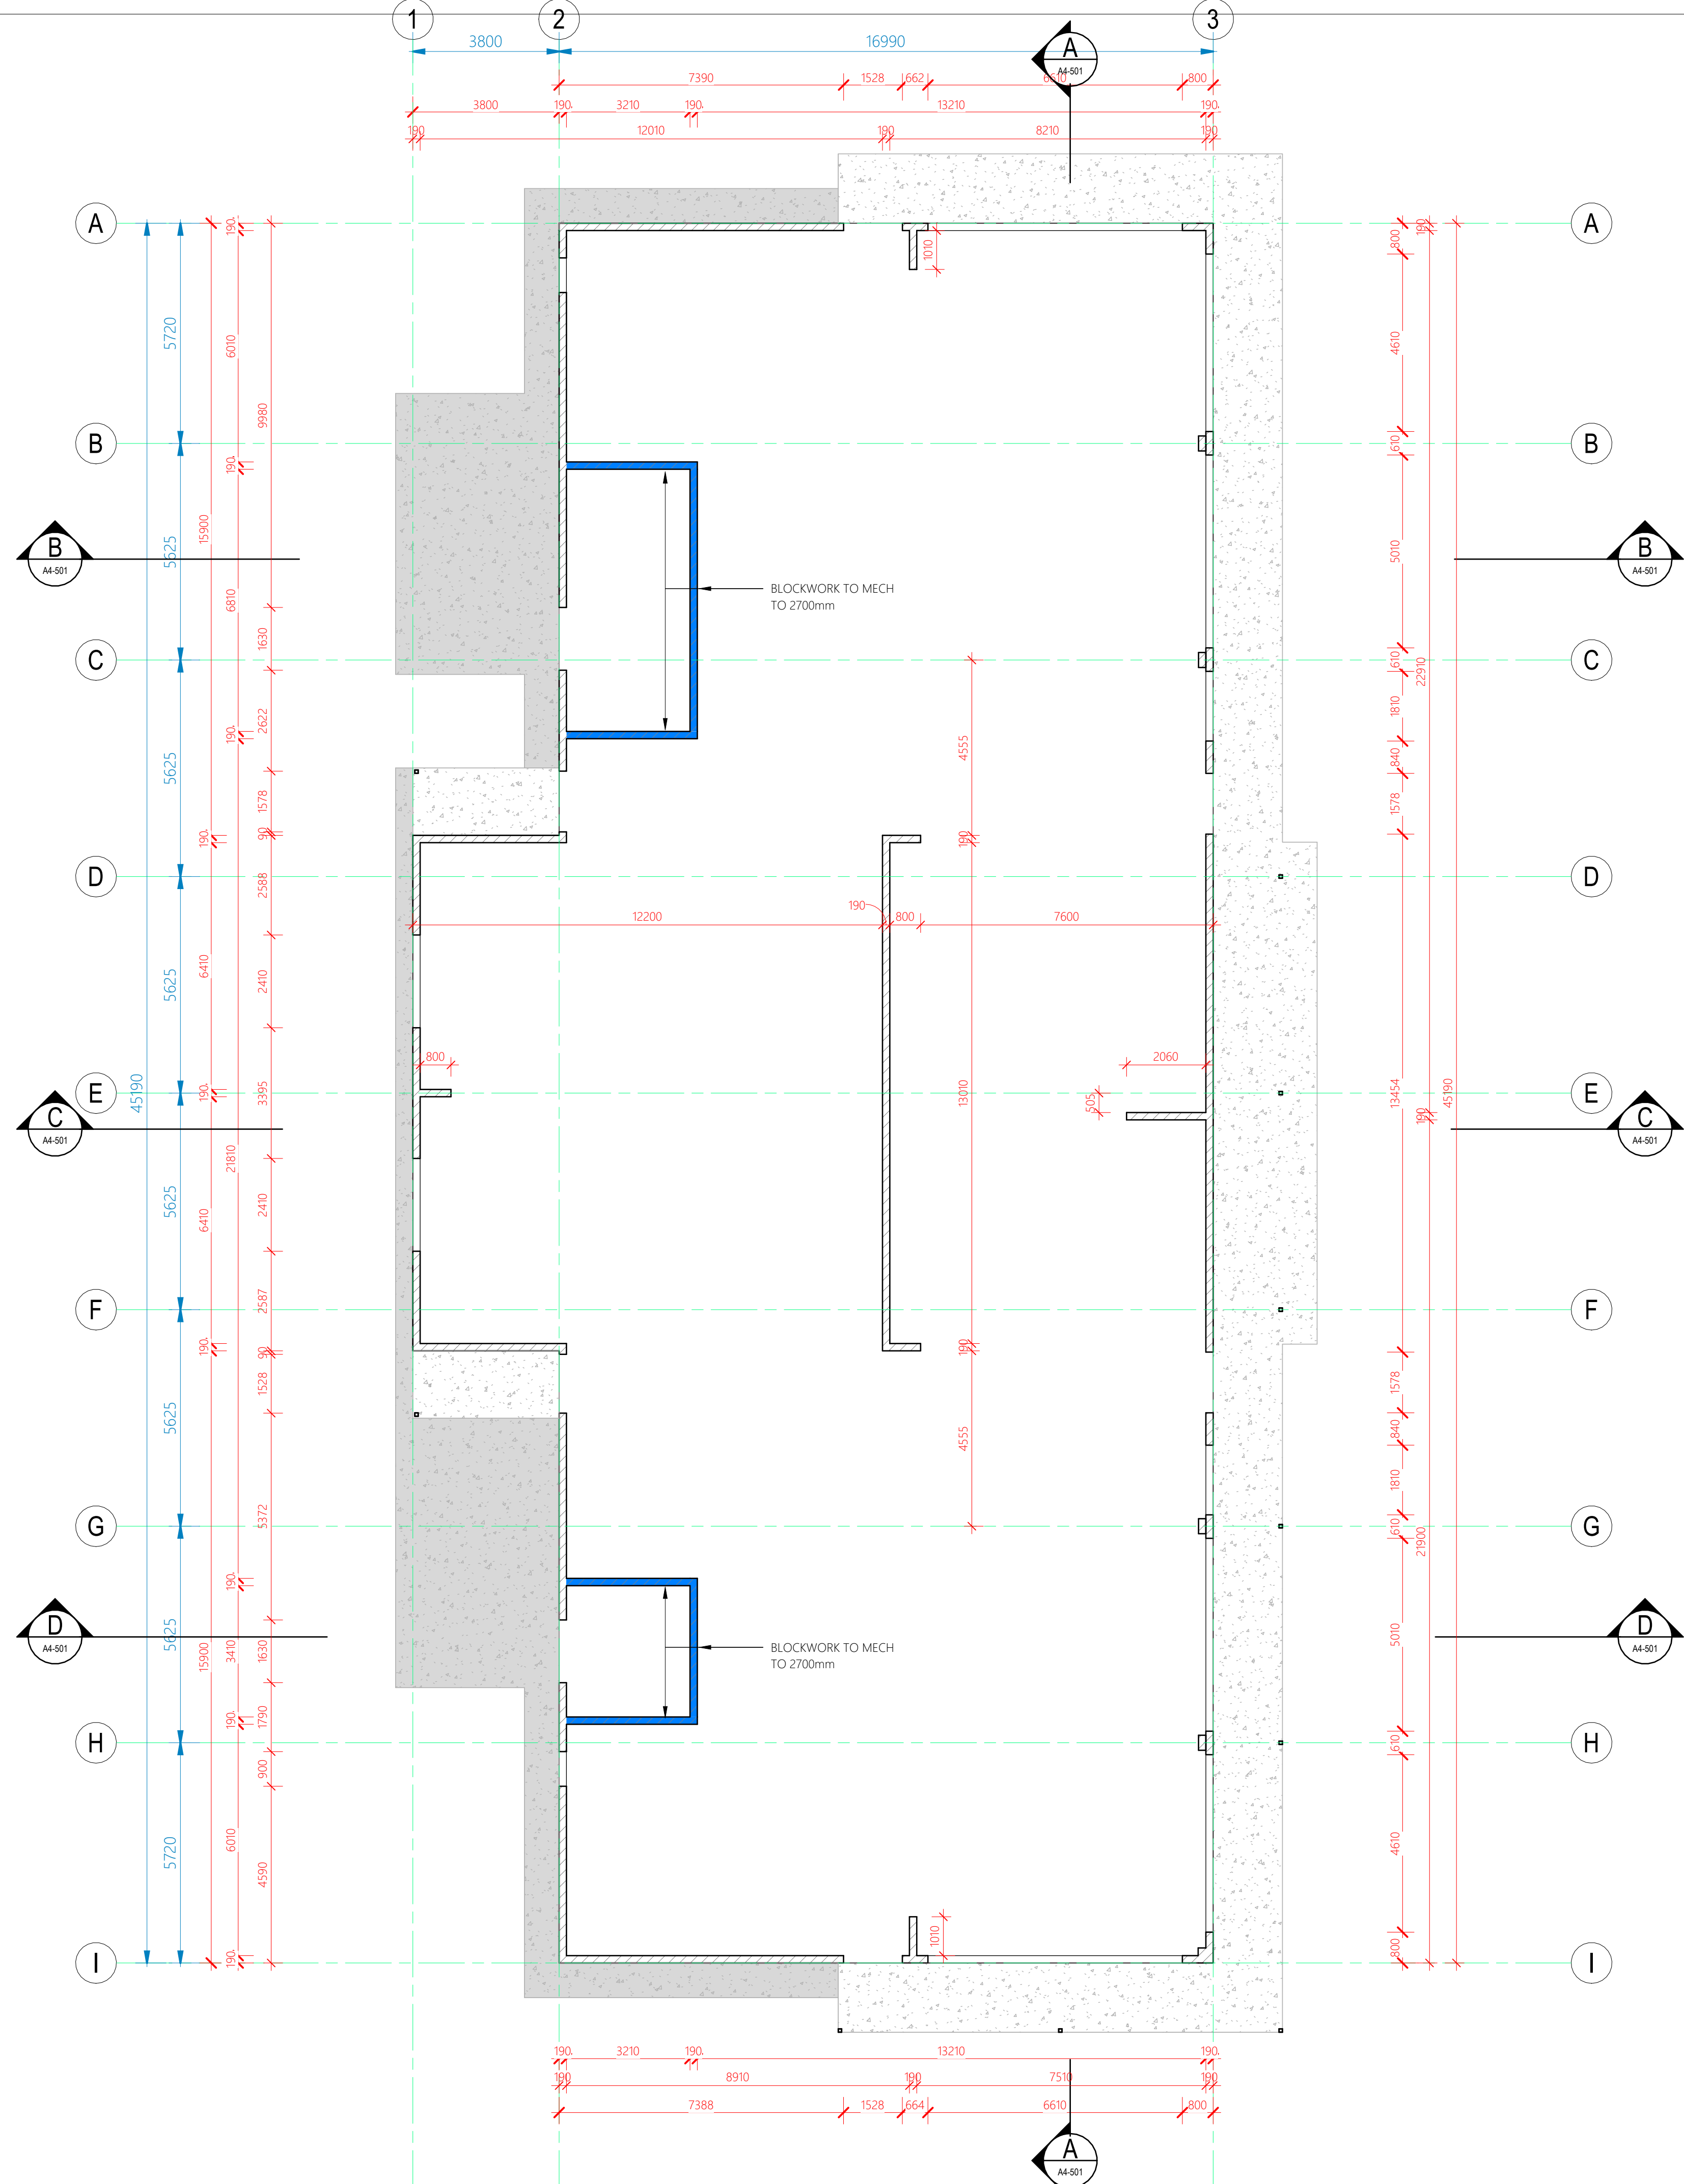

REVISIONS		
Rev	Description	Date
T1	TENDER ISSUE	12.03.2026

DO NOT SCALE THIS DRAWINGS

 

TENDER ISSUE

Client



Project Details

OFFICE REFURBS

Address

STANWELL POWER STATION

Drawing Title

PROPOSED BLOCK SETOUT




0483 988 655 
info@designelements.com.au 
QBCC No: 1247120 BDAQ No: 0001677

Scale: 1 : 100 Rev: **T1**
Date: MAR 2026
Drawn: Author
Project No: Drawing No:
25_003 A4-302

12/03/2026 7:55:08 PM

Block Setout

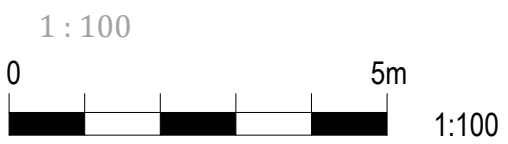

CONFIRM EXISTING GRID SETOUT ON SITE


NEW CEILING INSULATION THROUGHOUT
SHADED AREA - REFER SPEC

CEILING LEGEND

1200 x 600 APEX ACOUSTIC CEILING
TILES (OR APPROVED EQUAL - NEW
TILES THROUGH RENOVATED AREA)


INSULATED PANELING WITH FLAT
COLORBOND SOFFIT LINING

INSULATION ABOVE CEILING TILES

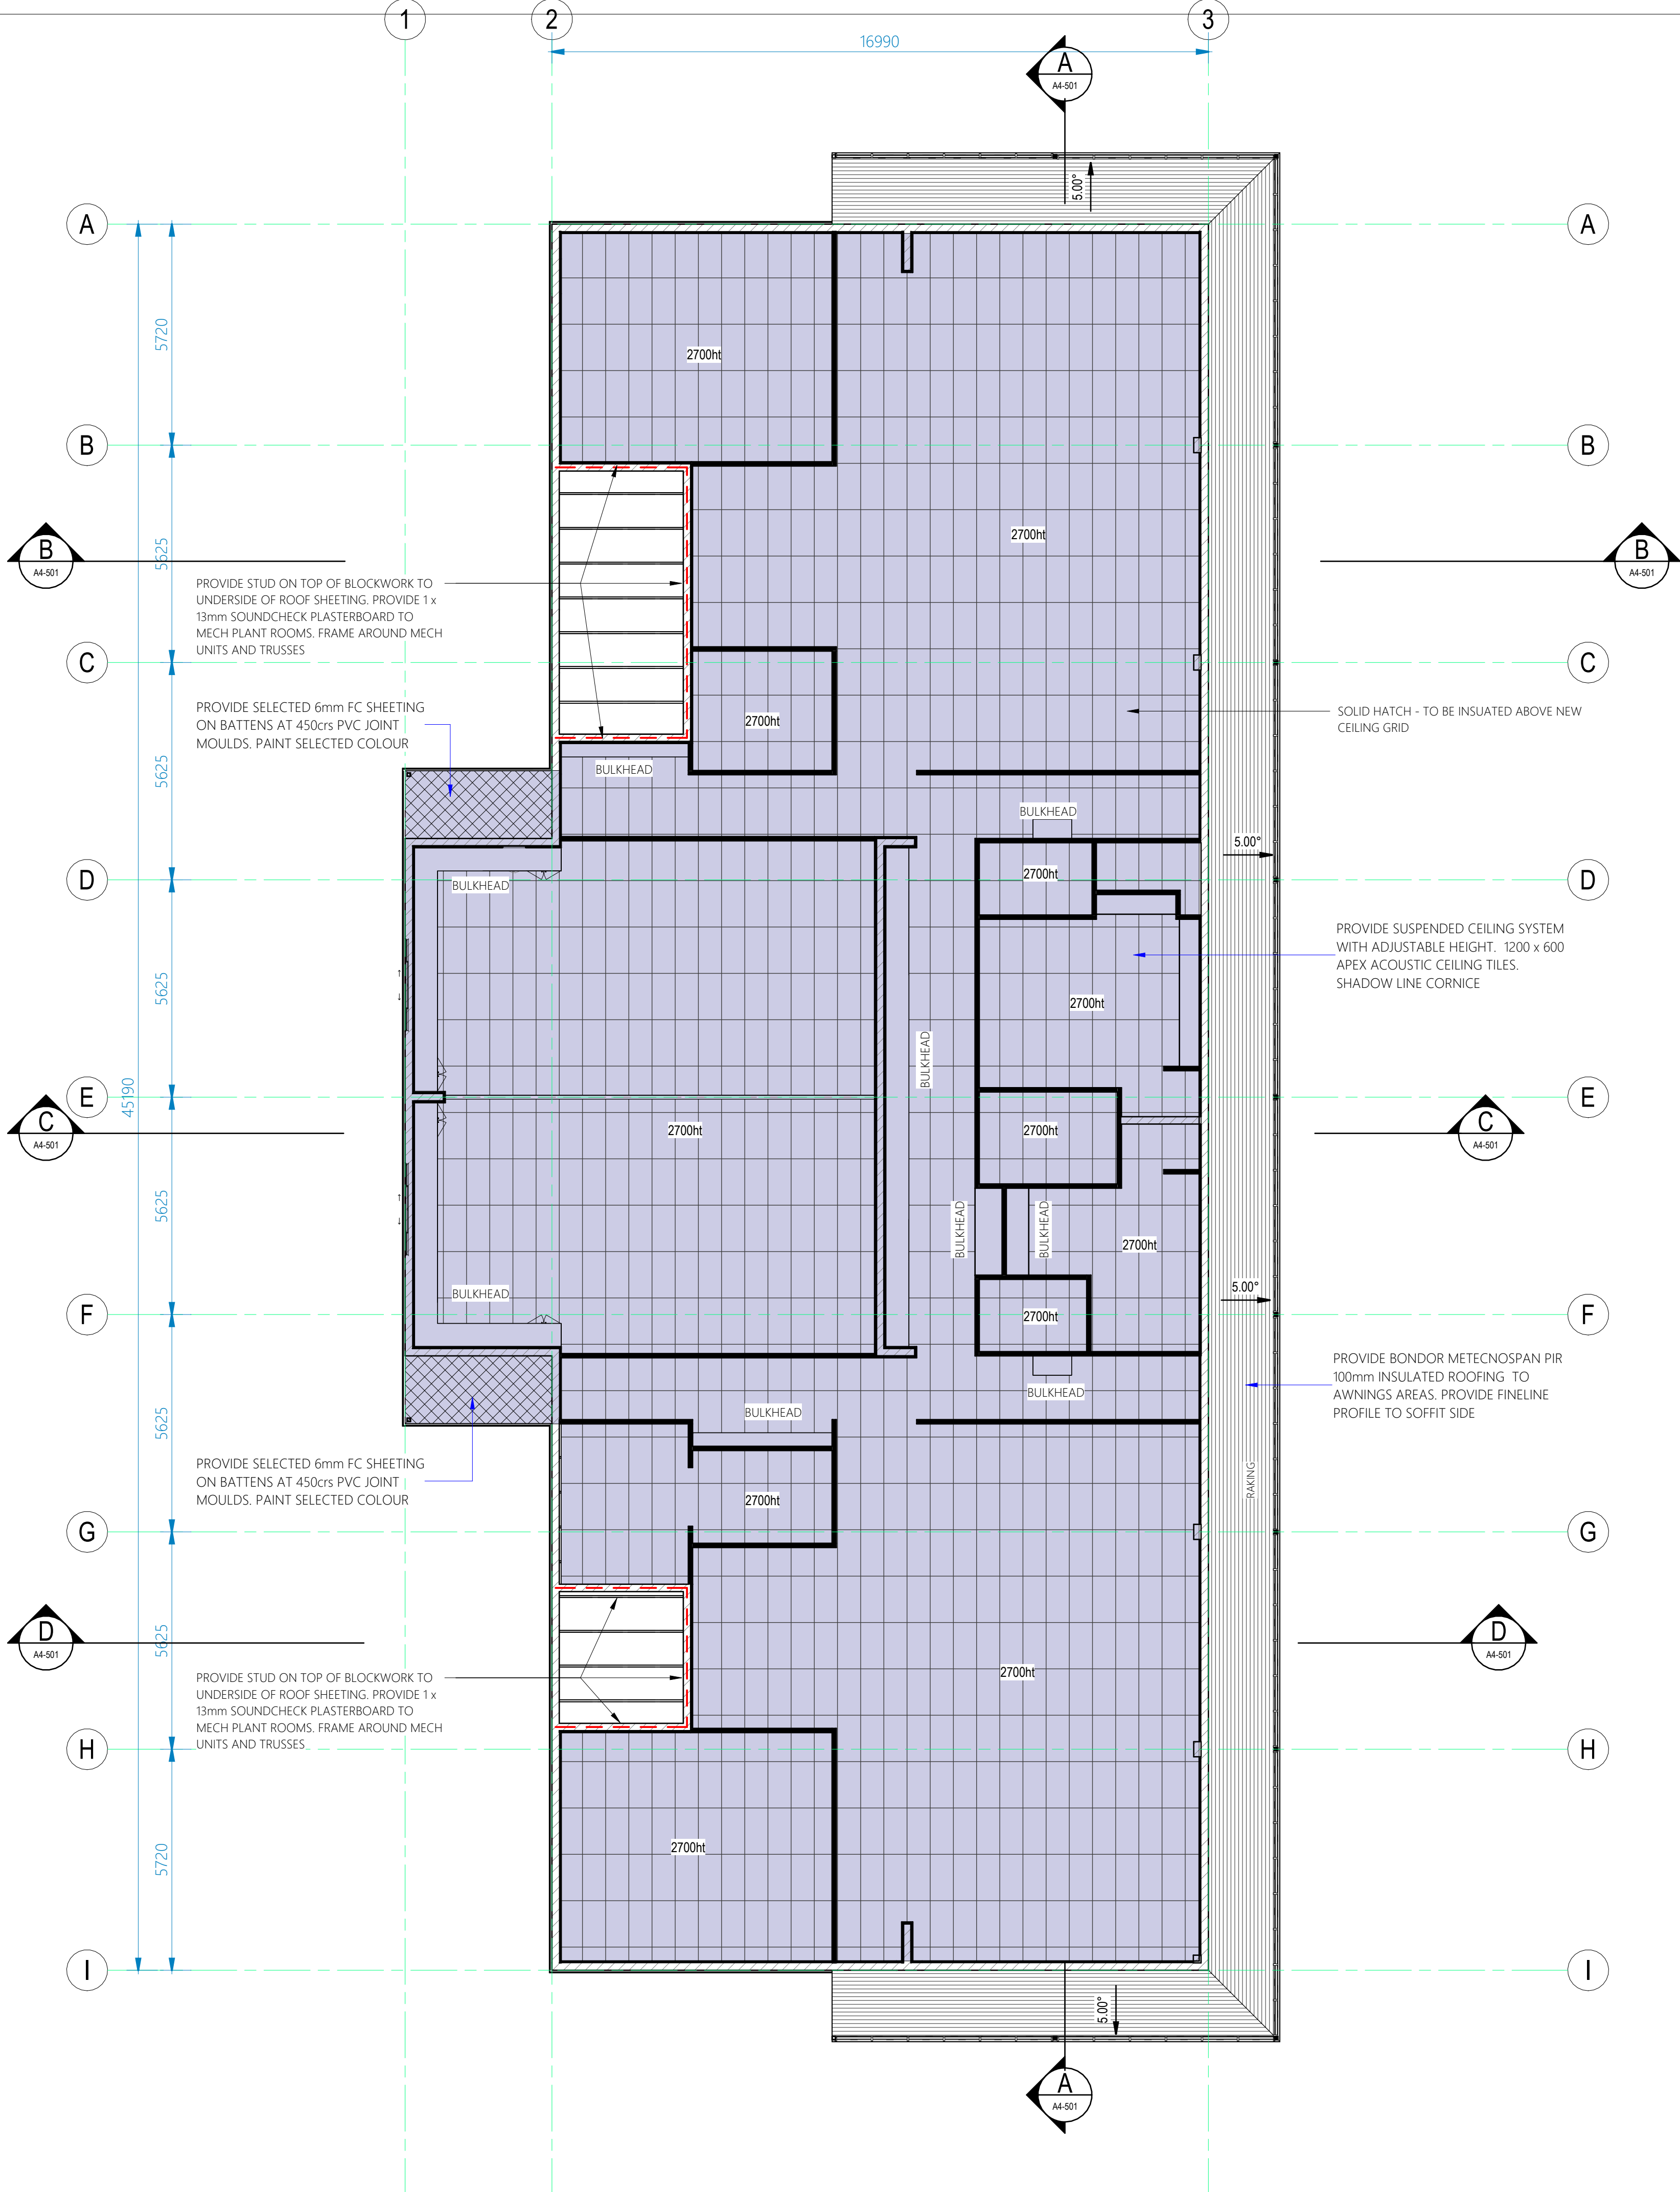

REVISIONS		
Rev	Description	Date
T1	TENDER ISSUE	12.03.2026

DO NOT SCALE THIS DRAWINGS

 

TENDER ISSUE

Client

Project Details

OFFICE REFURBS

Address

STANWELL POWER STATION

Drawing Title

PROPOSED CEILING PLAN

0483 988 655 **M**

info@dezi nelements.com.au **E**

QBCC No: 1247120 BDAQ No: 0001677


Scale: 1 : 100 Rev: **T1**

Date: MAR 2026

Drawn: Author


Project No: Drawing No:

25_003 A4-303

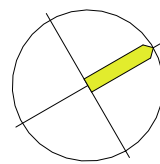


Ceiling Plan



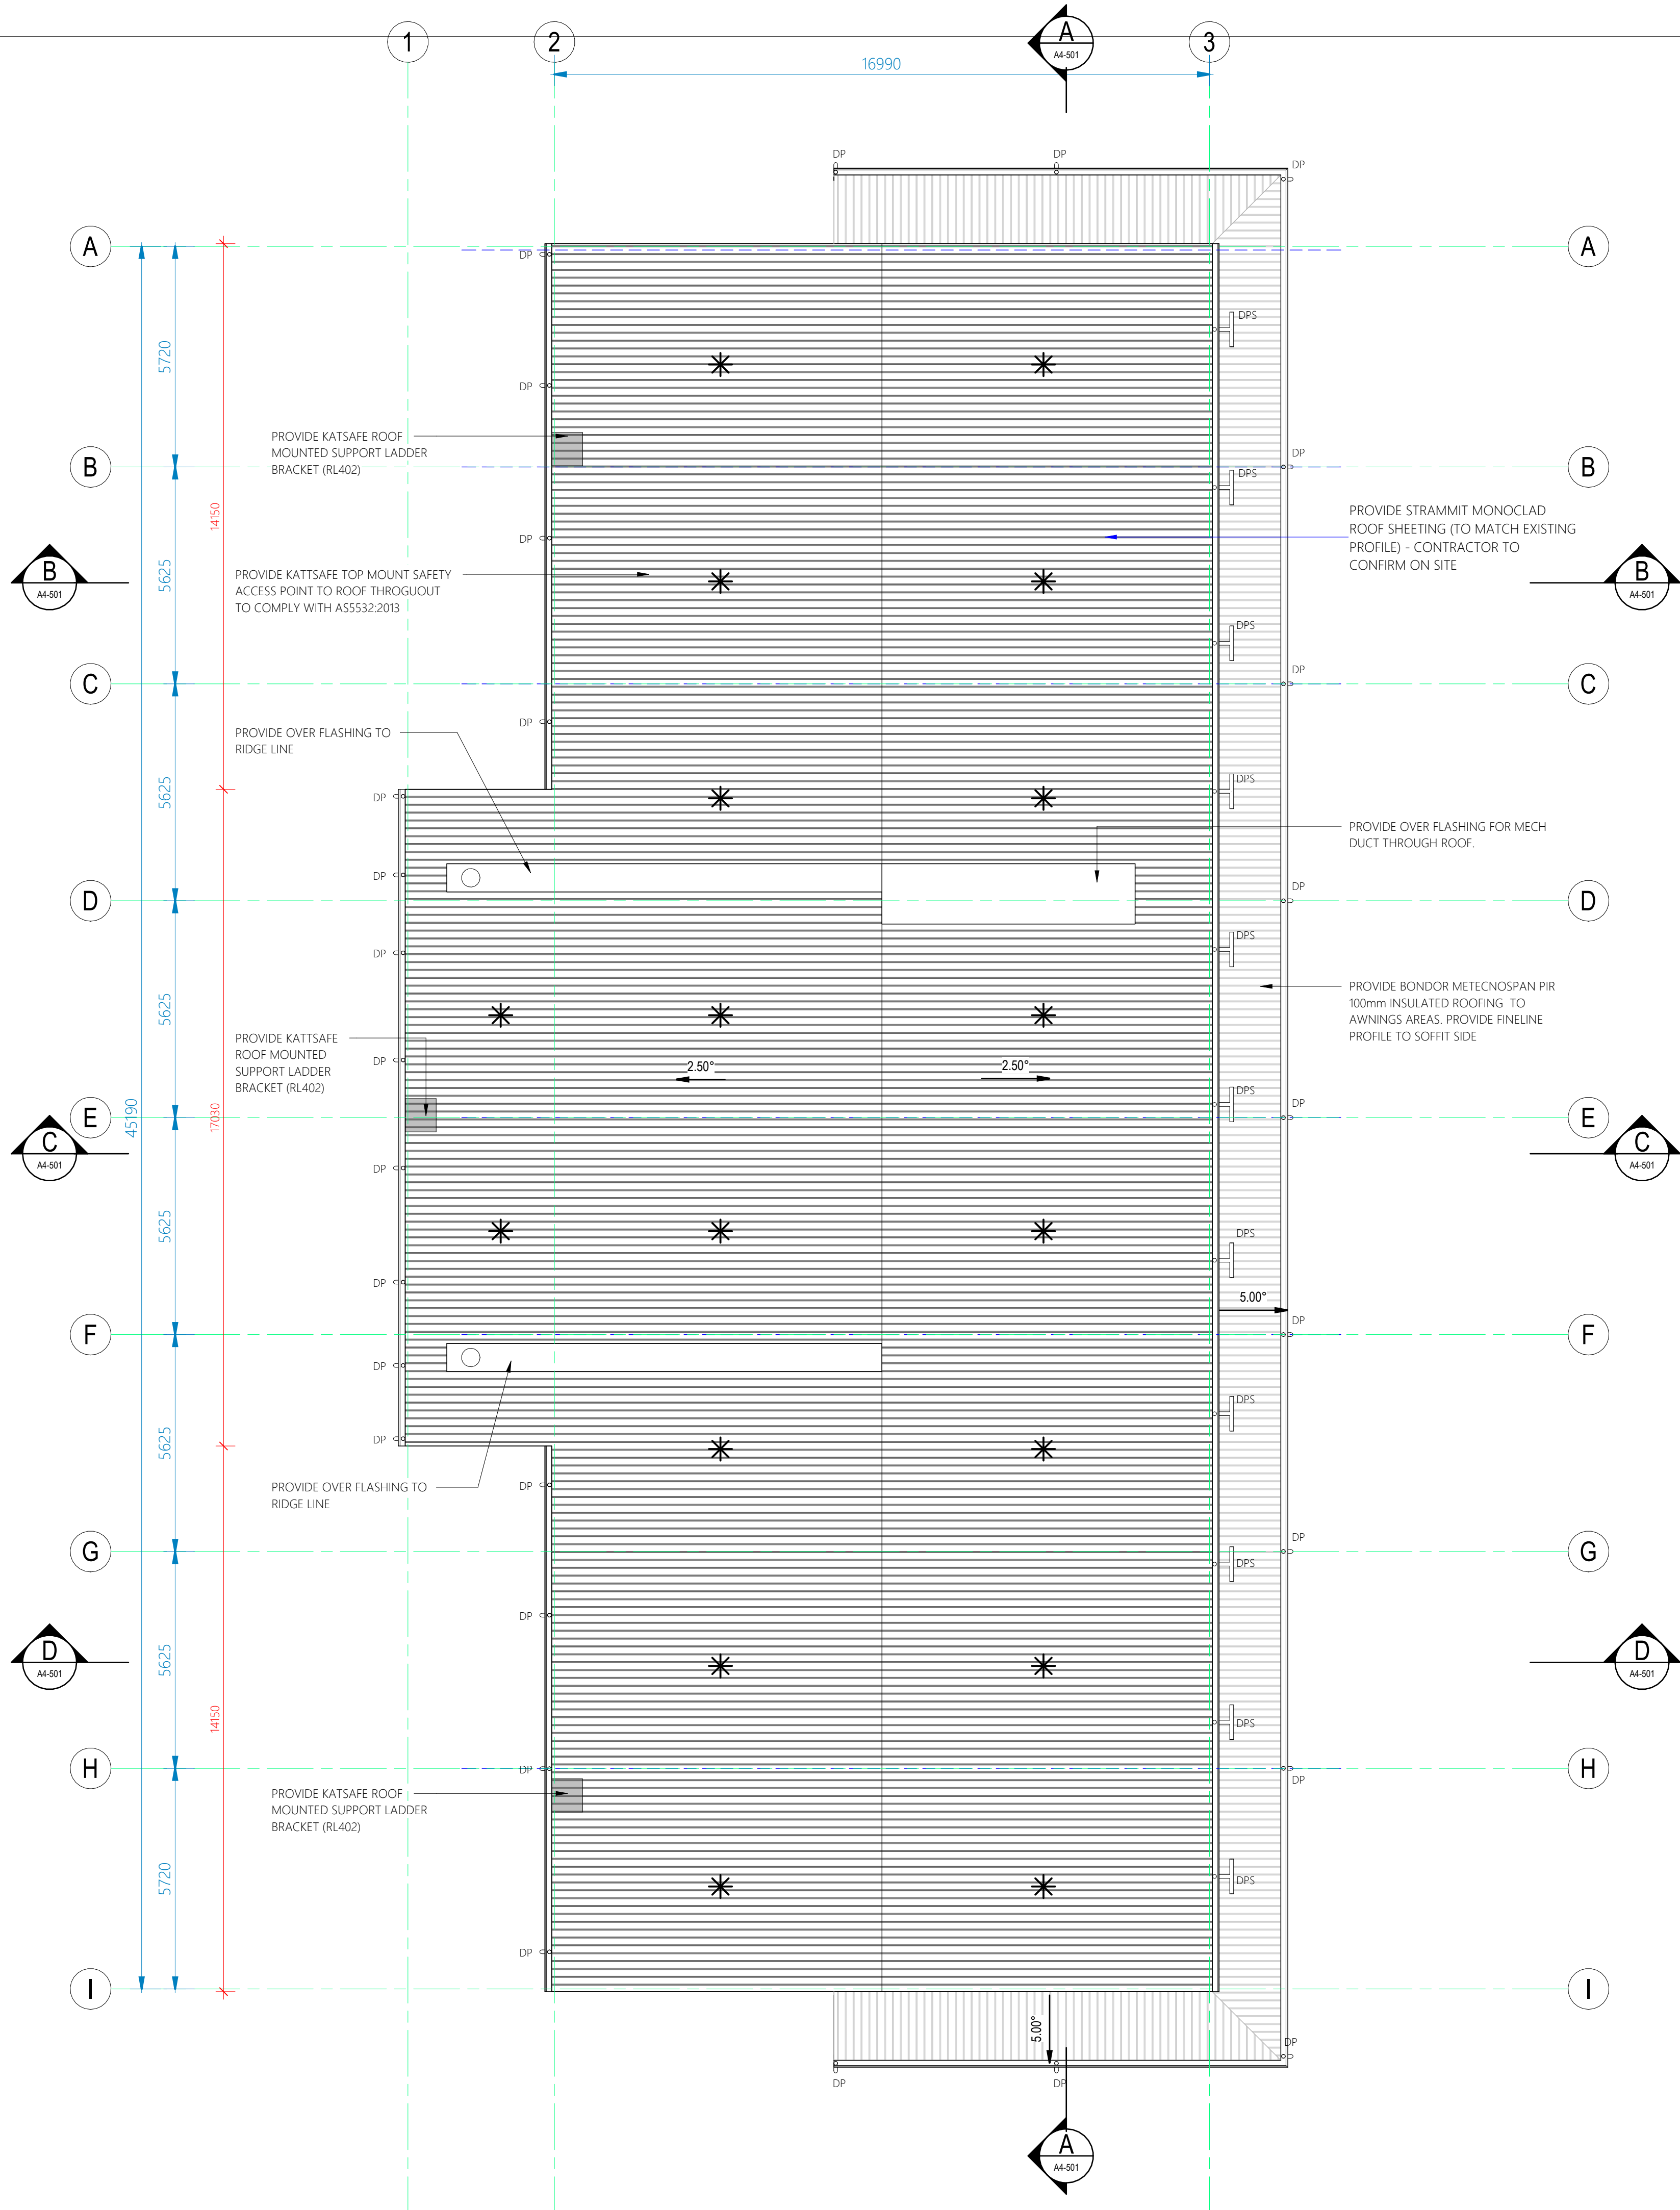

Proposed Roof Plan

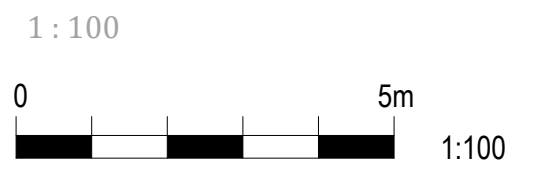

REVISIONS

Rev	Description	Date
T1	TENDER ISSUE	12.03.2026

DO NOT SCALE THIS DRAWINGS

TENDER ISSUE

Client

Project Details

OFFICE REFURBS

Address

STANWELL POWER STATION

Drawing Title









PROPOSED ROOF PLAN

0483 988 655 **M**
info@dezi elements.com.au **E**
QBCC No: 1247120 BDAQ No: 0001677


Scale: 1 : 100	Rev:
Date: MAR 2026	T1
Drawn: Author	Project No: Drawing No:
25_003	A4-304

12/03/2026 7:55:09 PM

These drawings, designs and the Copyright thereof are the property of Design Group Qld Pty Ltd (T/A Design Elements) and are not to be used, retained or copied by either physical or electronic means without the written permission of Nathan Burke (Director). Conditions stated in the terms and conditions. Design Elements accepts no responsibility for the completeness, accuracy or compatibility of electronically transferred documents.

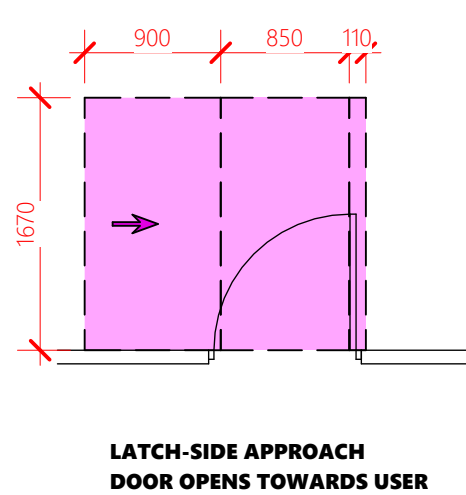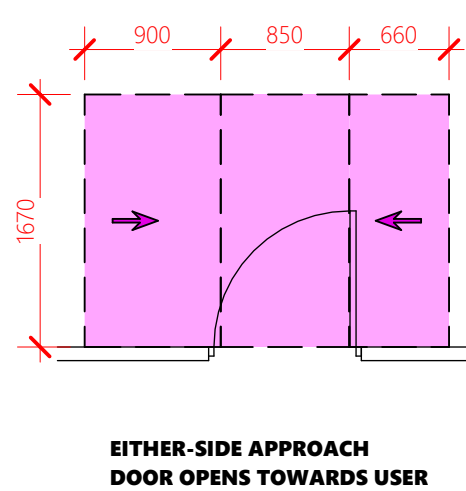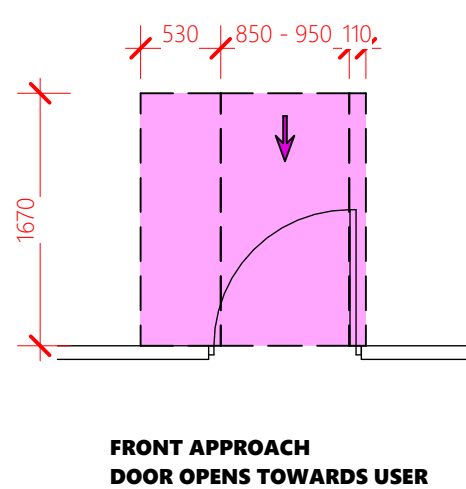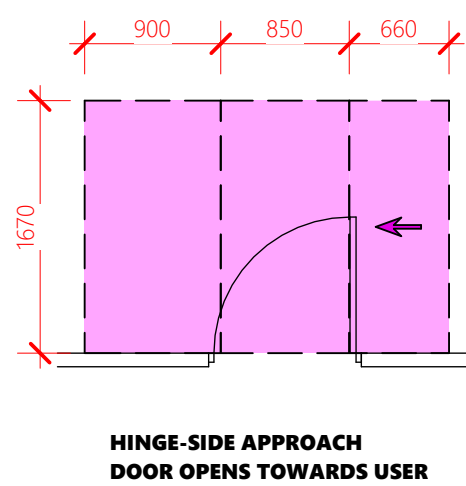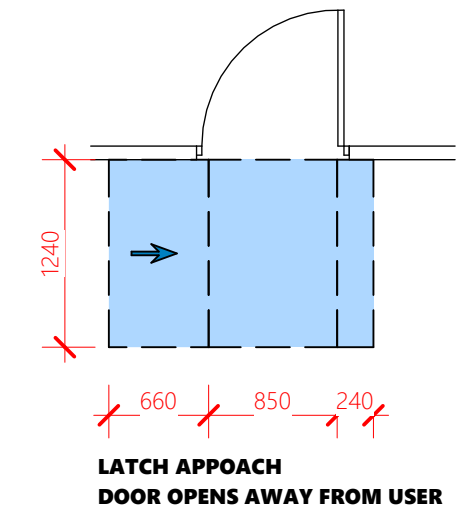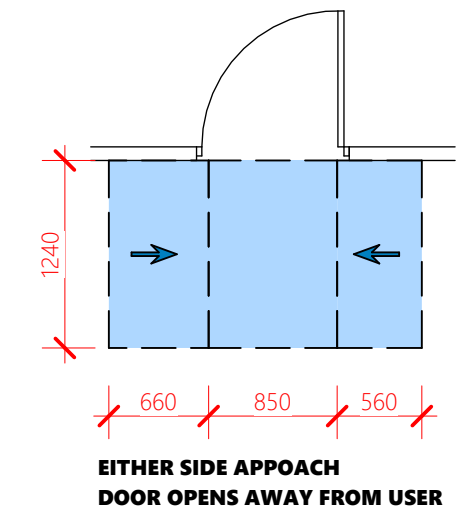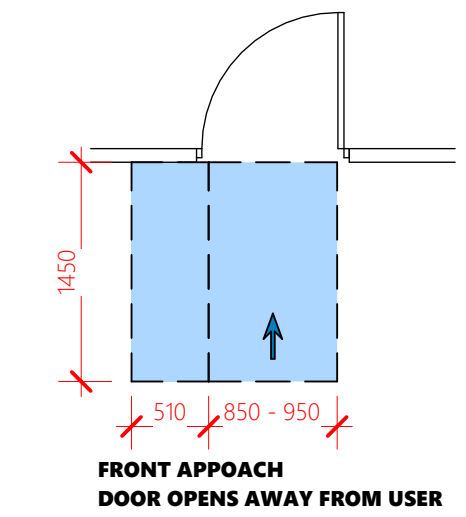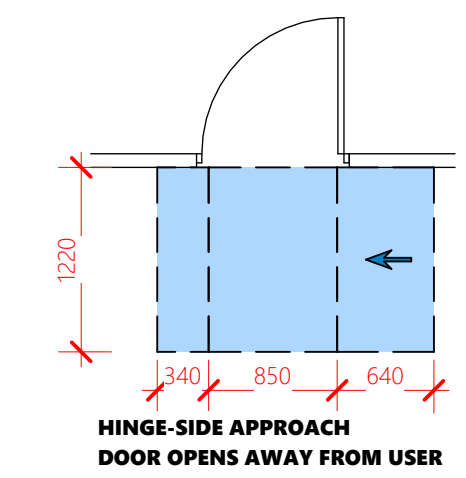

AS1428.1 - Clearance Plan

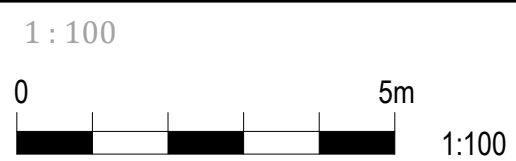

REVISIONS		
Rev	Description	Date
T1	TENDER ISSUE	12.03.2026

DO NOT SCALE THIS DRAWINGS



TENDER ISSUE

Client

Project Details

OFFICE REFURBS

Address

STANWELL POWER STATION


Drawing Title


AS1428.1 - CLEARANCE PLAN

0483 988 655 **M**
info@dezi elements.com.au **E**
QBCC No: 1247120 BDAQ No: 0001677

Scale:	As indicated	Rev:
Date:	MAR 2026	T1
Drawn:	Author	
Project No:	Drawing No:	
25_003	A4-305	

12/03/2026 7:55:10 PM

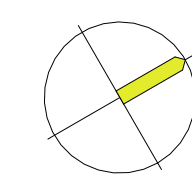

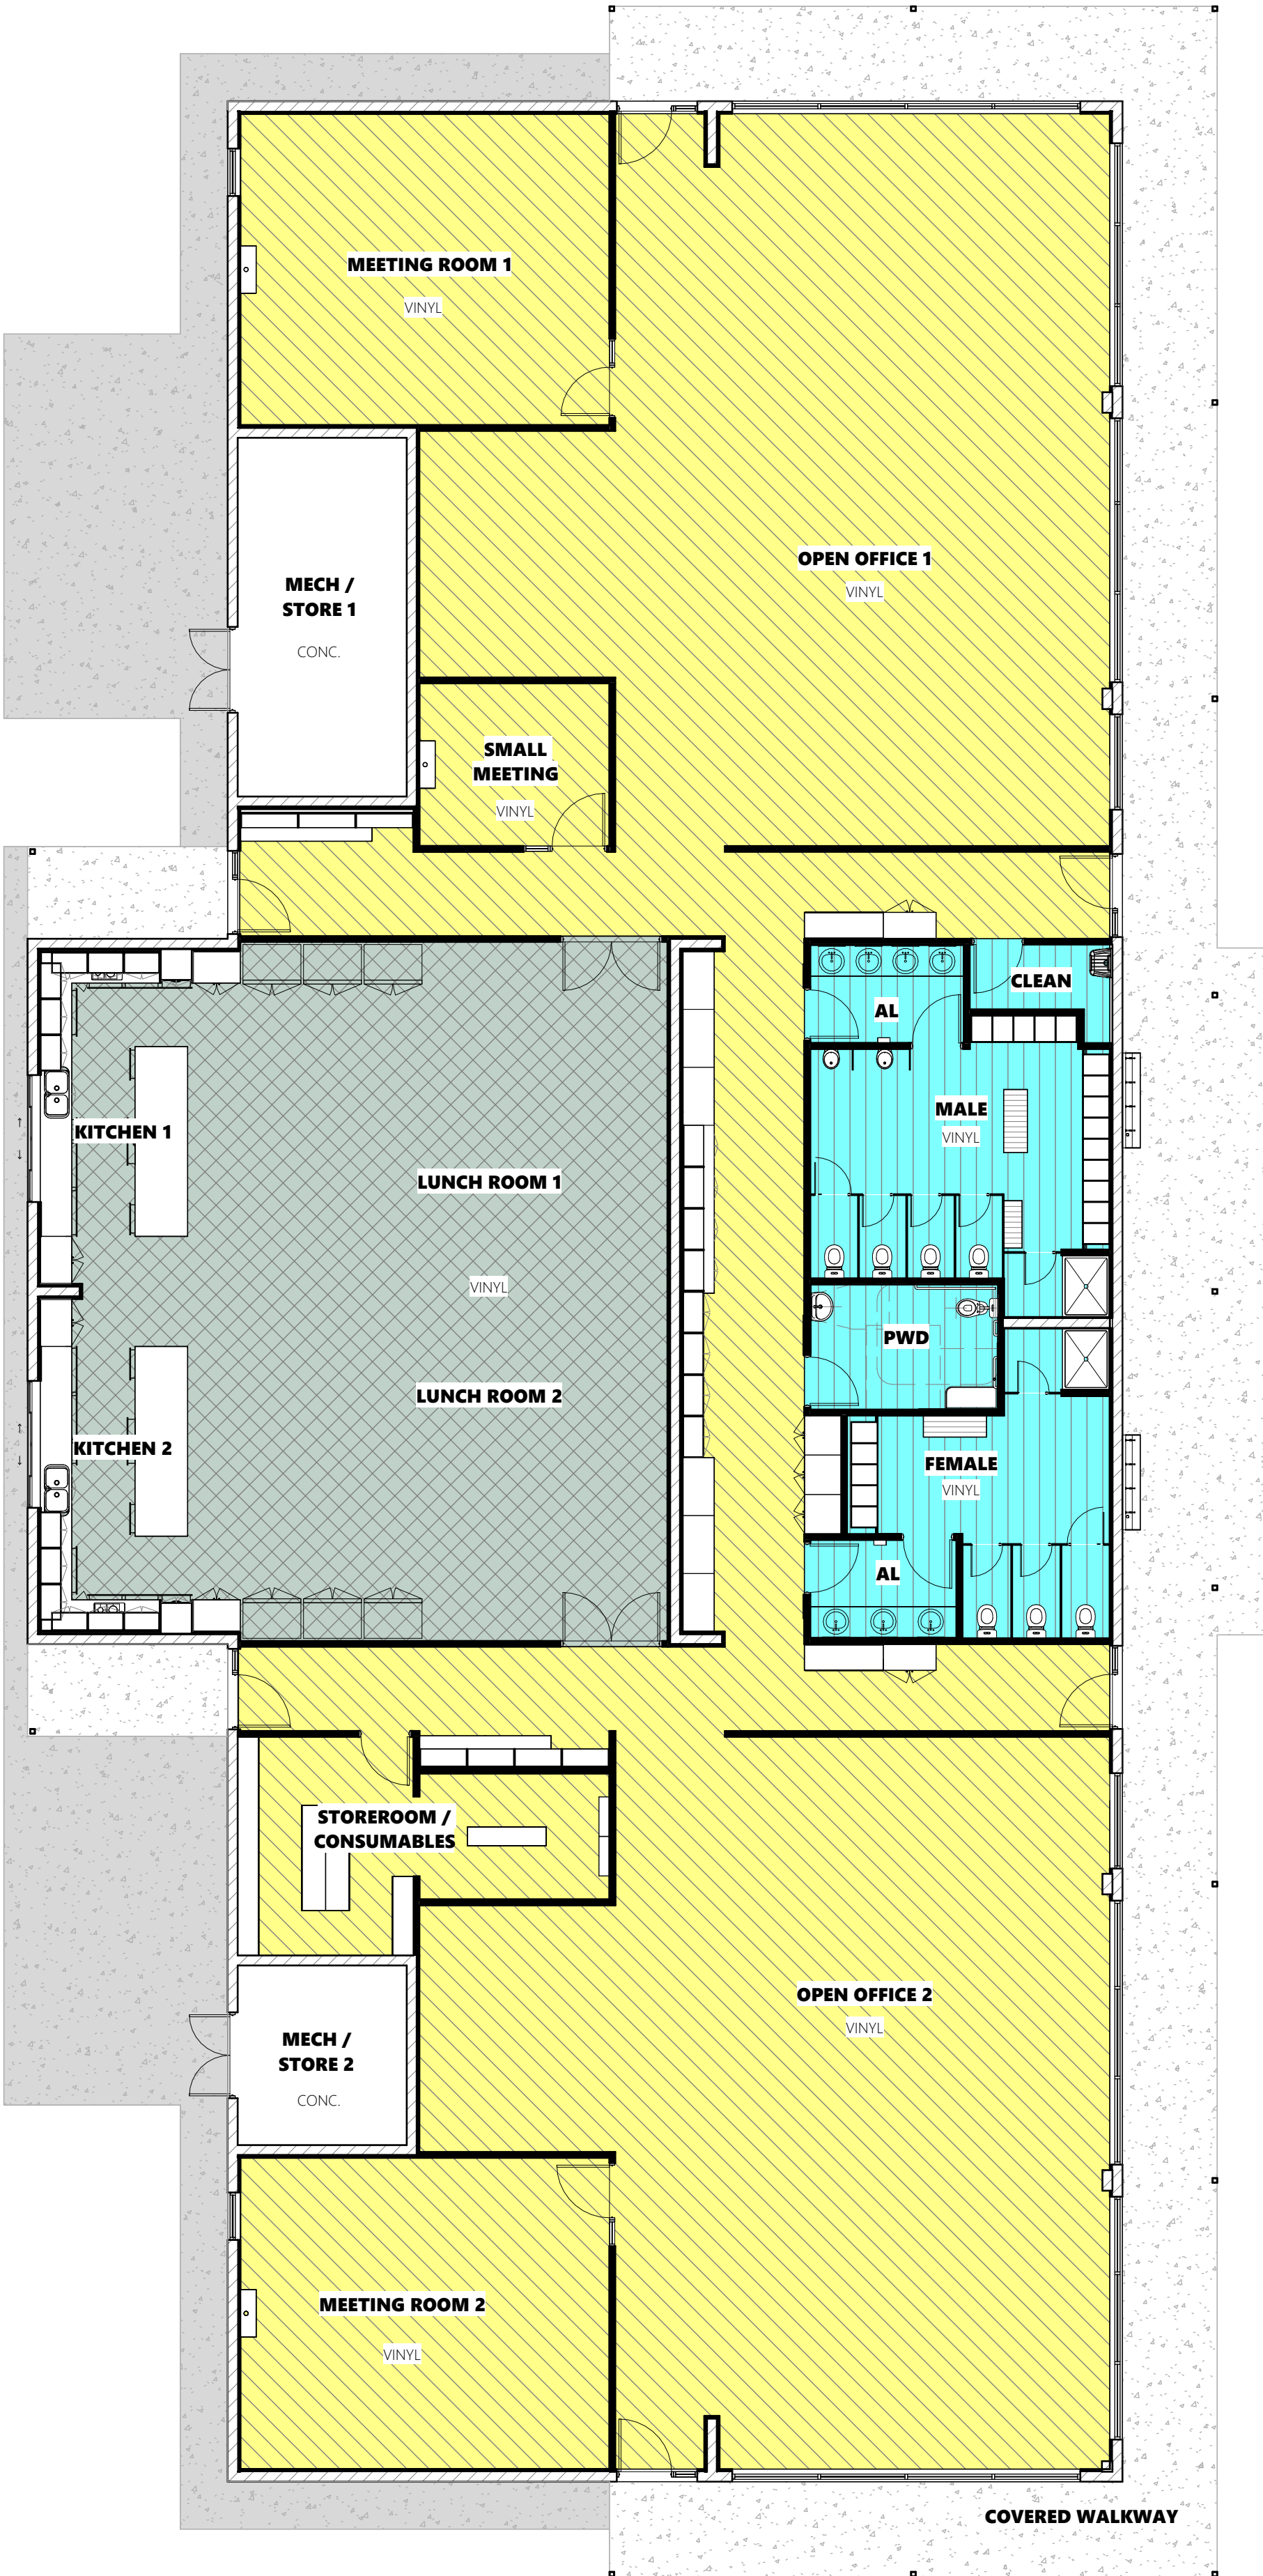

Floor Covering Plan



1:100

0 5m 1:100

REVISIONS		
Rev	Description	Date
T1	TENDER ISSUE	12.03.2026

DO NOT SCALE THIS DRAWINGS

FLOOR COVERING PLAN

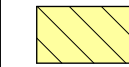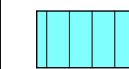-  SHEET VINYL - TYPE 1
100mm FEATHER EDGE SKIRTING - BLACK
-  SHEET VINYL - TYPE 2
100mm COVERED UP SKIRTING
-  SHEET VINYL - TYPE 3
100mm FEATHER EDGE SKIRTING - BLACK

TENDER ISSUE

Client



Project Details

OFFICE REFURBS

Address

STANWELL POWER STATION

Drawing Title

FLOOR COVERING PLAN




0483 988 655 

info@designelements.com.au 



QBCC No: 1247120 BDAQ No: 0001677

Scale: 1 : 100	Rev:
Date: MAR 2026	T1
Drawn: Author	
Project No: 25_003	Drawing No: A4-306

12/03/2026 7:55:11 PM

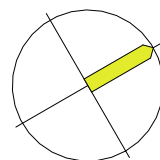

Proposed Furniture Layout

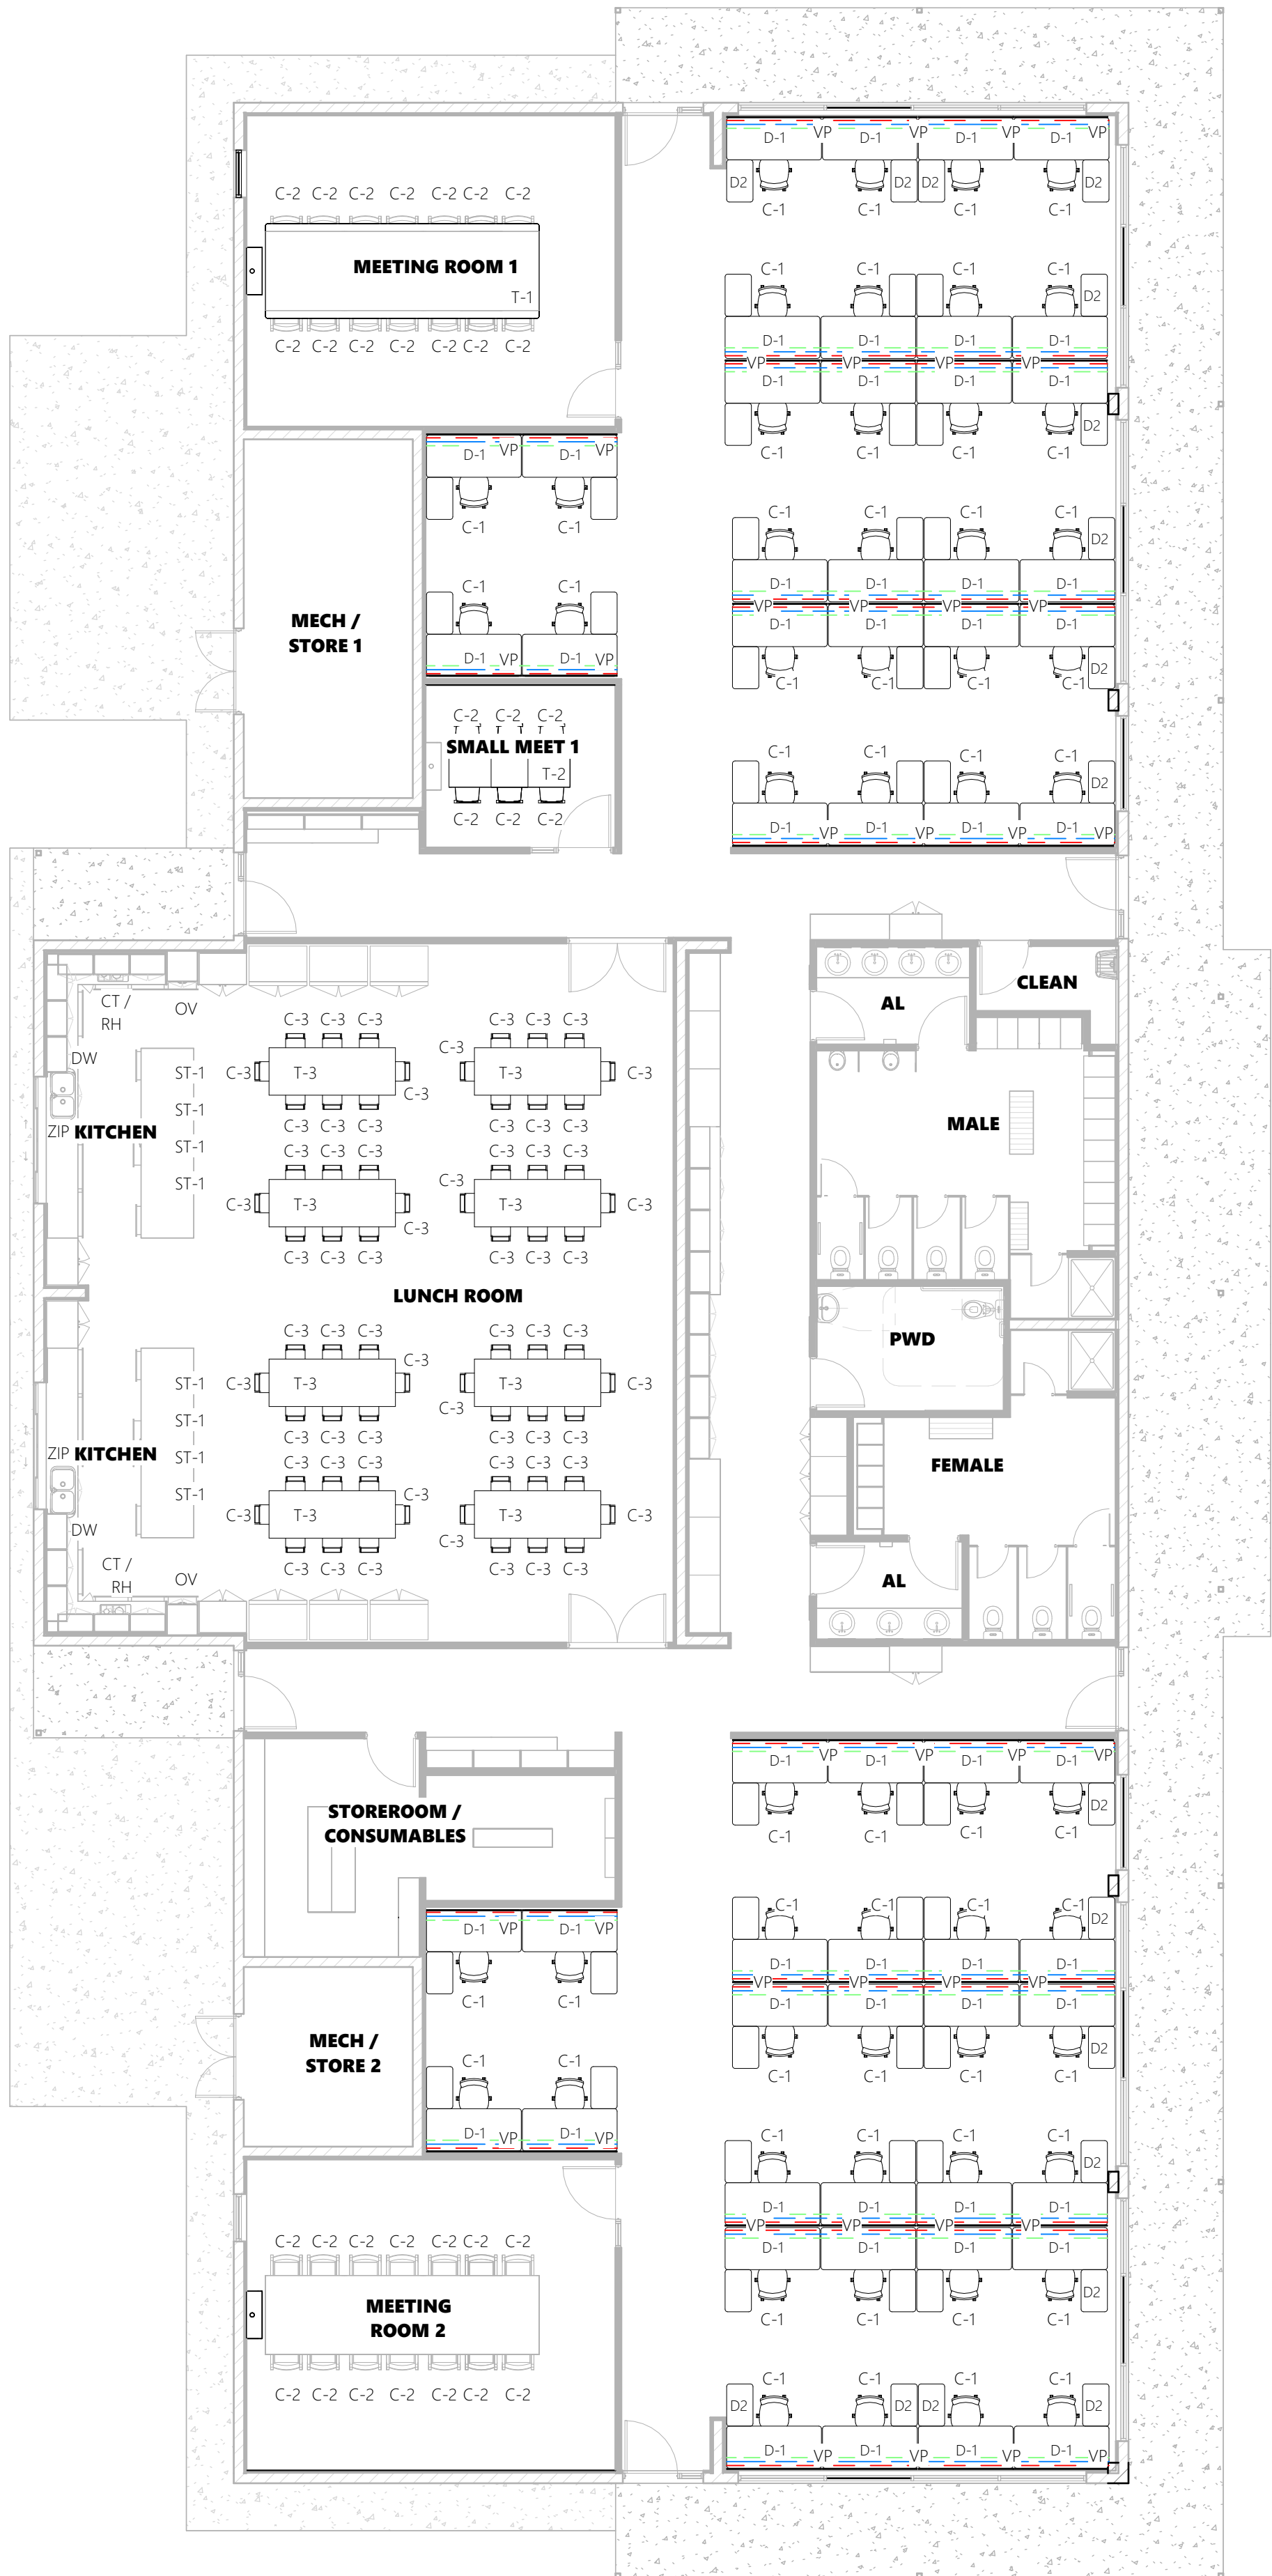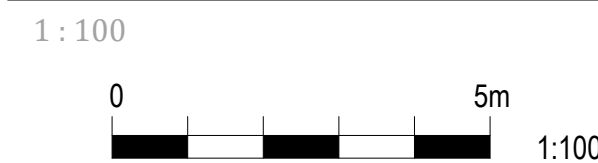

FURNITURE & APPLIANCE SCHEDULE

CODE	TYPE	SIZE	QTY	SUPPLIER
D-1	DESK	1800 x 800	56	SCHIAVELLA CLIMATE RECTANGLE WORK STATION
D-2	DESK	800 x 500	56	SCHIAVELLA CLIMATE RECTANGLE WORK STATION RETURN
C-1	CHAIR (workstation)	-	56	SCHIAVELLA HIGH BACK CHAIR BY OKAMURA, BLACK BODY, BLACK MESH BLACK AND UPHOLSTERED SEAT
C-2	CHAIR (meeting)	-	34	SHIBUSA HIGH BACK BY OKAMURA (BLACK)
C-3	CHAIR (dining)	-	64	MEXICA CHAIR (plywood with natural oak finish / no arms)
T-1	TABLE (large meet)	1800 x 5200	2	MEETING TABLE EONA - 25mm LAMINEX CHARCOAL NATURAL FINISH WITH ABS EDGING
T-2	TABLE (small meet)	900 x 2000	1	MEETING TABLE EONA - 25mm LAMINEX CHARCOAL NATURAL FINISH WITH ABS EDGING
T-3	TABLE (dining)	900 x 2400	8	JOGGLE TABLE BY IMPOSTER - 25mm LAMINEX WHITE. STEEL FRAME WHITE POWDERCOAT
ST-1	STOOL (kitchen)	-	8	MEXICA STOOL (plywood with natural oak finish)
	CABLE CATCHER	AS REQUIRED	-	SCHIAVELLA
	CABLE ARTICULATOR	AS REQUIRED	-	SCHIAVELLA
	CABLE CHANNEL	AS REQUIRED	-	SCHIAVELLA
VP	VIDE SUSP. PANEL	1800 (600mm ABOVE DESK)	40	SCHIAVELLA - PROVIDE SUSPENDE BRACKETS TO EACH DESK
OV	OVEN	598 x 596	2	FISHER & PAYKEL 60CM SERIES 7 CONTEMPORARY PYROLYTIC OVEN 9 FUNCTION - BLACK
DW	DISHWASHER	597 x 600	2	FISHER & PAYKEL SERIES 7 CONTEMPORARY DISHWASHER - BLACK STEEL
CT	COOK TOP	600	2	FISHER & PAYKEL 60CM SERIES 7 4 ZONE INDUCTION COOKTOP 2 SMARTZONES - BLACK
RH	RANGE HOOD	600	2	FISHER & PAYKEL 60CM SERIES 7 INTEGRATED INSERT WALL RANGEHOOD EXTERNAL MOTOR - STEEL GLASS
ZIP	ZIP UNIT	-	2	HYDROTAP G5 BCSHA100 5-IN-1 CLASSIC TAP WITH CLASSIC MIXER BLACK

REVISIONS

Rev	Description	Date
T1	TENDER ISSUE	12.03.2026

DO NOT SCALE THIS DRAWINGS



TENDER ISSUE

Client

Project Details

OFFICE REFURBS

Address

STANWELL POWER STATION

Drawing Title

FURNITURE LAYOUT

0483 988 655

info@designelements.com.au

QBCC No: 1247120 BDAQ No: 0001677

Scale: 1 : 100	Rev:
Date: MAR 2026	T1
Drawn: Author	
Project No:	Drawing No:
25_003	A4-307

12/03/2026 7:55:12 PM

REVISIONS		
Rev	Description	Date
T1	TENDER ISSUE	12.03.2026

DO NOT SCALE THIS DRAWINGS



TENDER ISSUE

Client

Project Details

OFFICE REFURBS

Address

STANWELL POWER STATION

Drawing Title

PROPOSED ELEVATIONS

dezi nelements
BUILDING DESIGNERS

0483 988 655

info@dezi nelements.com.au

QBCC No: 1247120 BDAQ No: 0001677

Scale: 1 : 100 Rev: **T1**


Date: MAR 2026

Drawn: Author

Project No: Drawing No:

25_003 A4-401


12/03/2026 7:55:29 PM

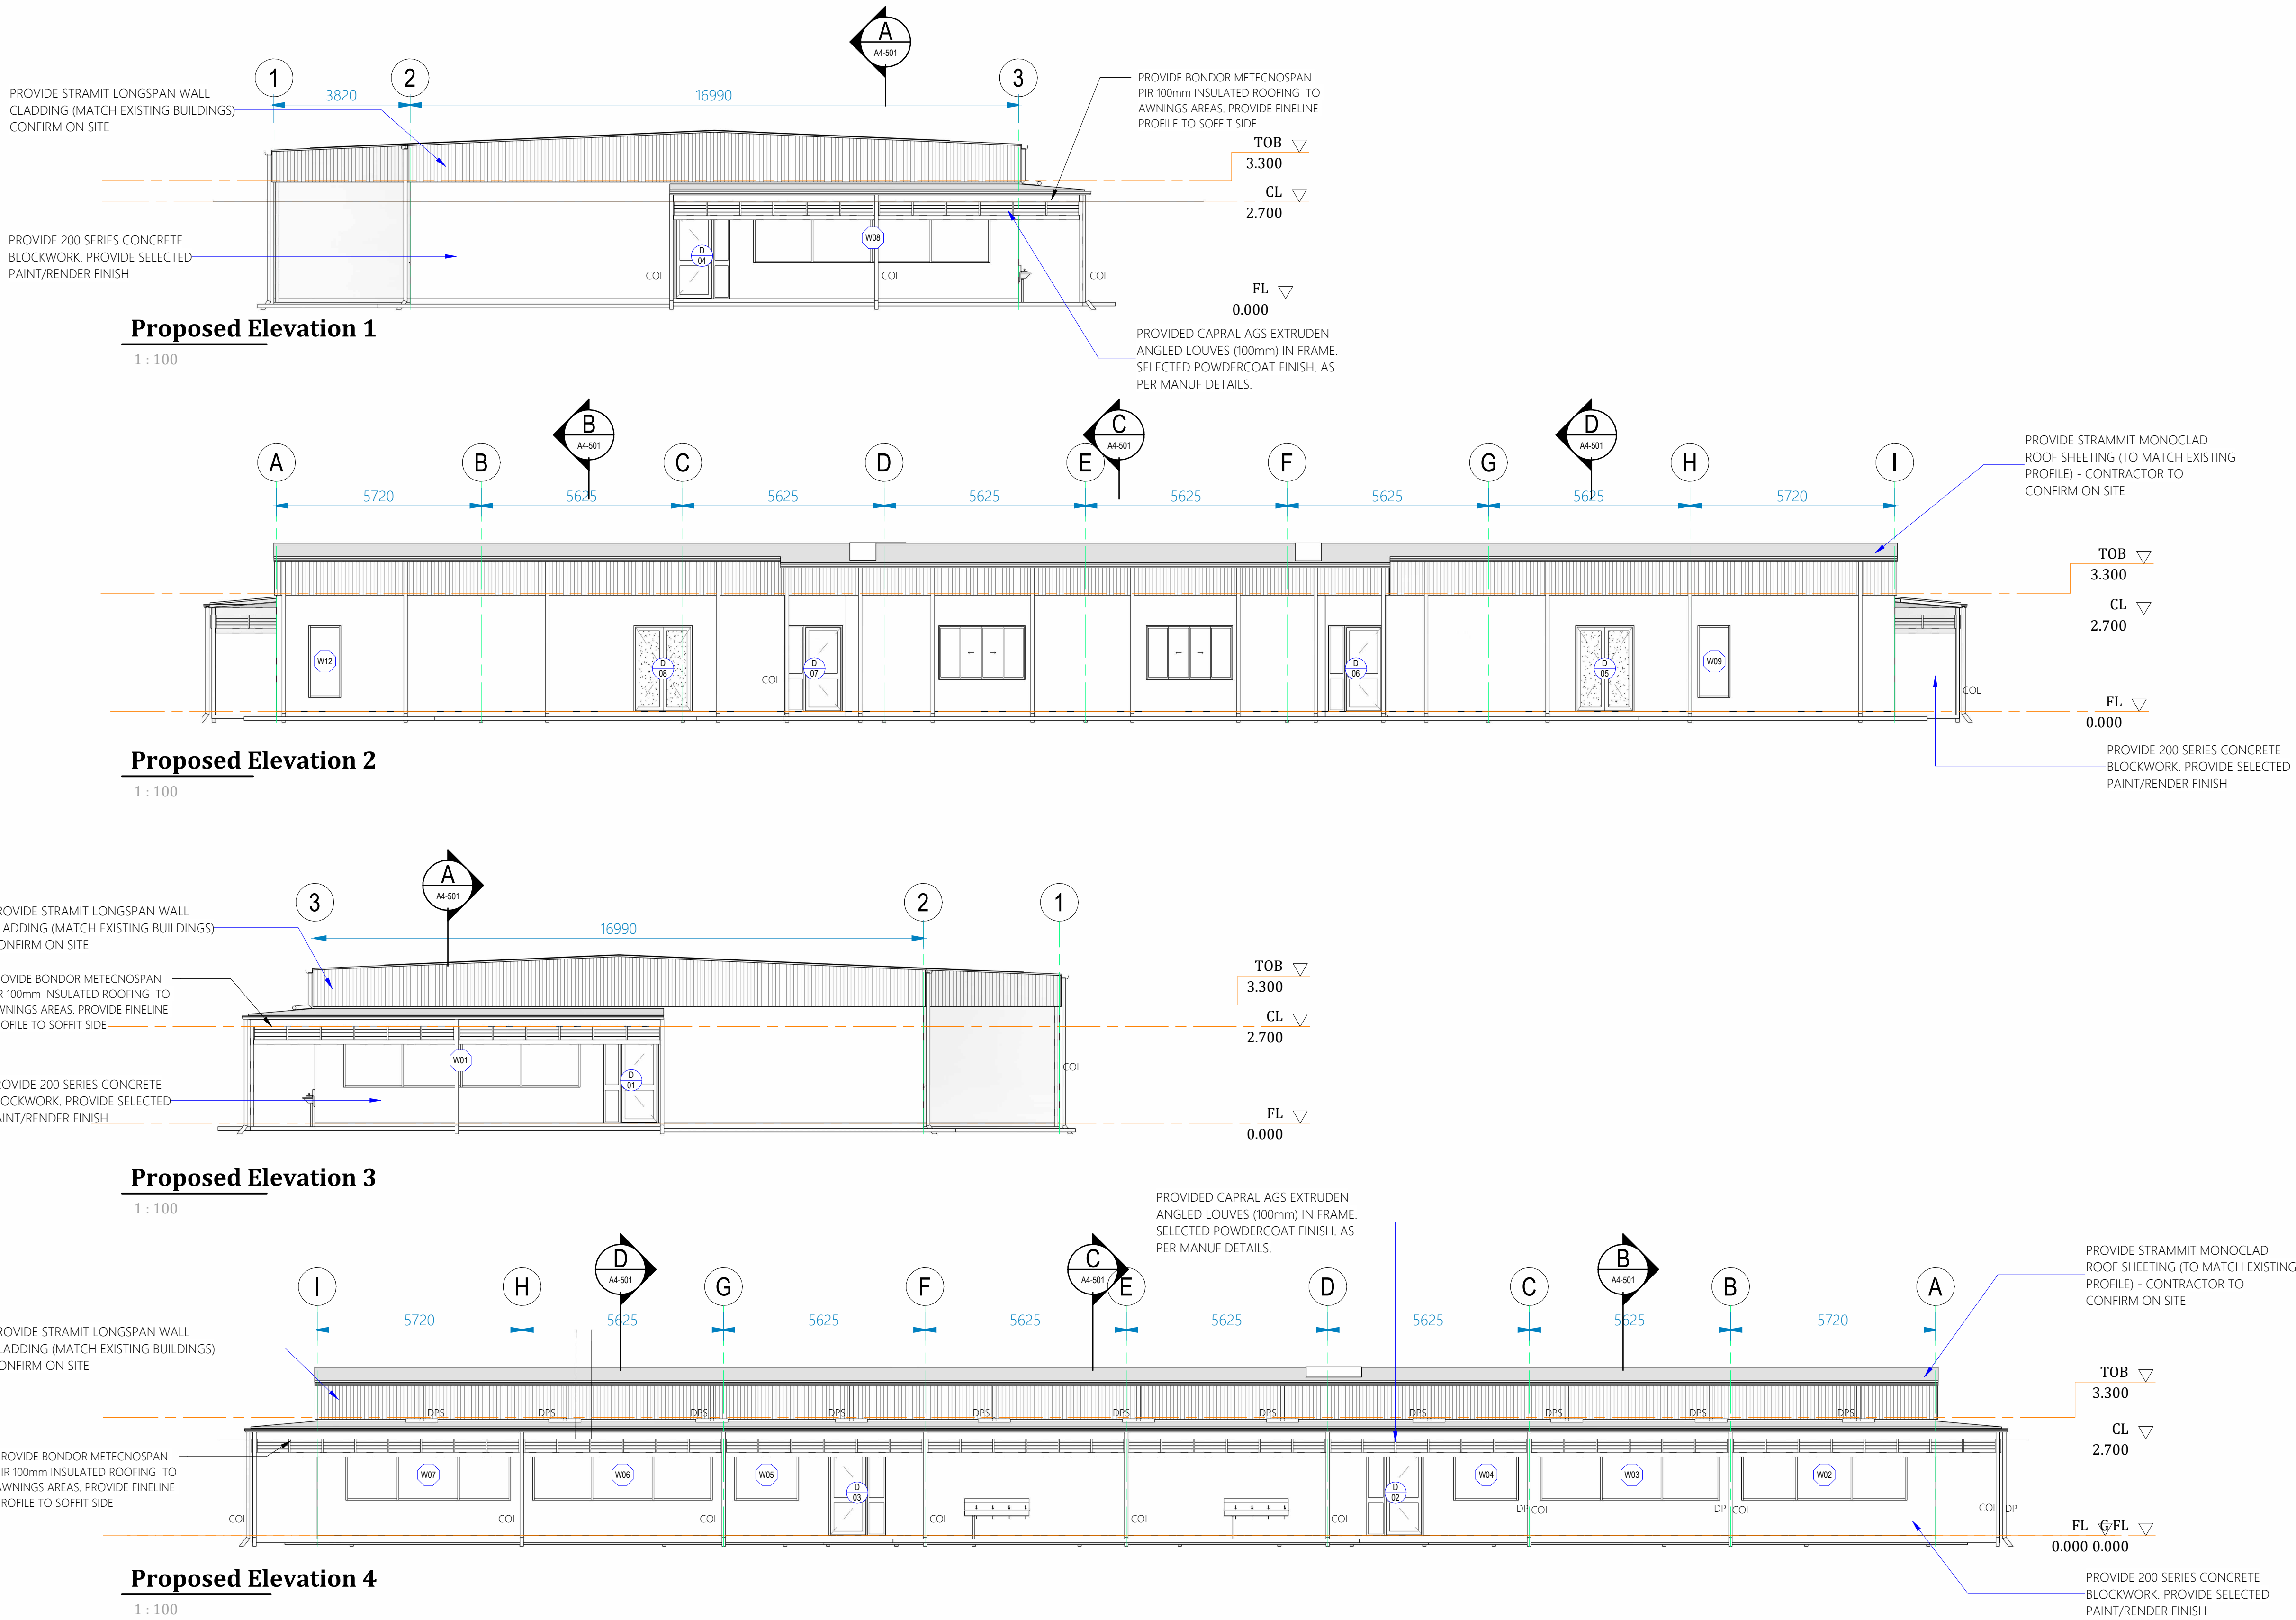


REVISIONS

Rev	Description	Date
T1	TENDER ISSUE	12.03.2026


DO NOT SCALE THIS DRAWINGS

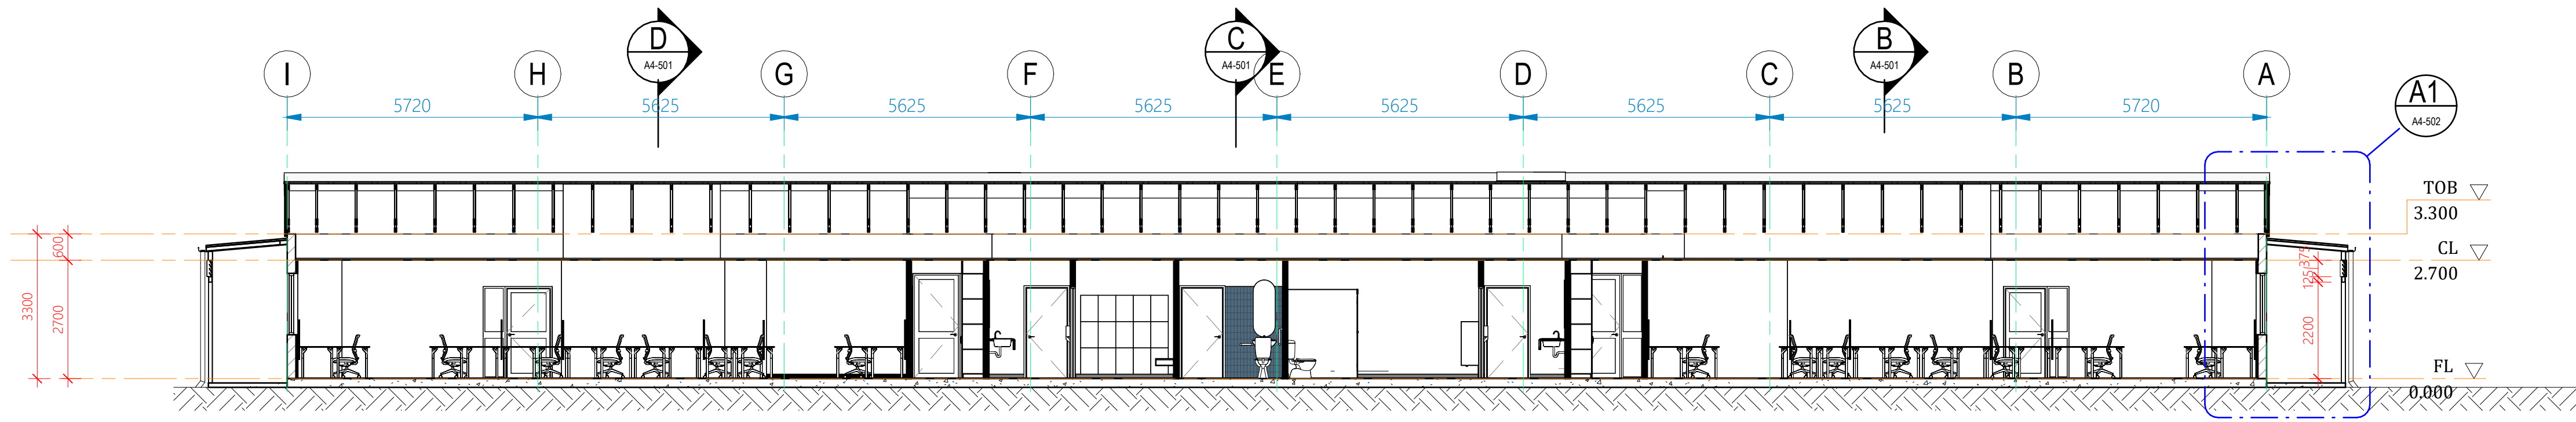


SECTION A
1 : 100

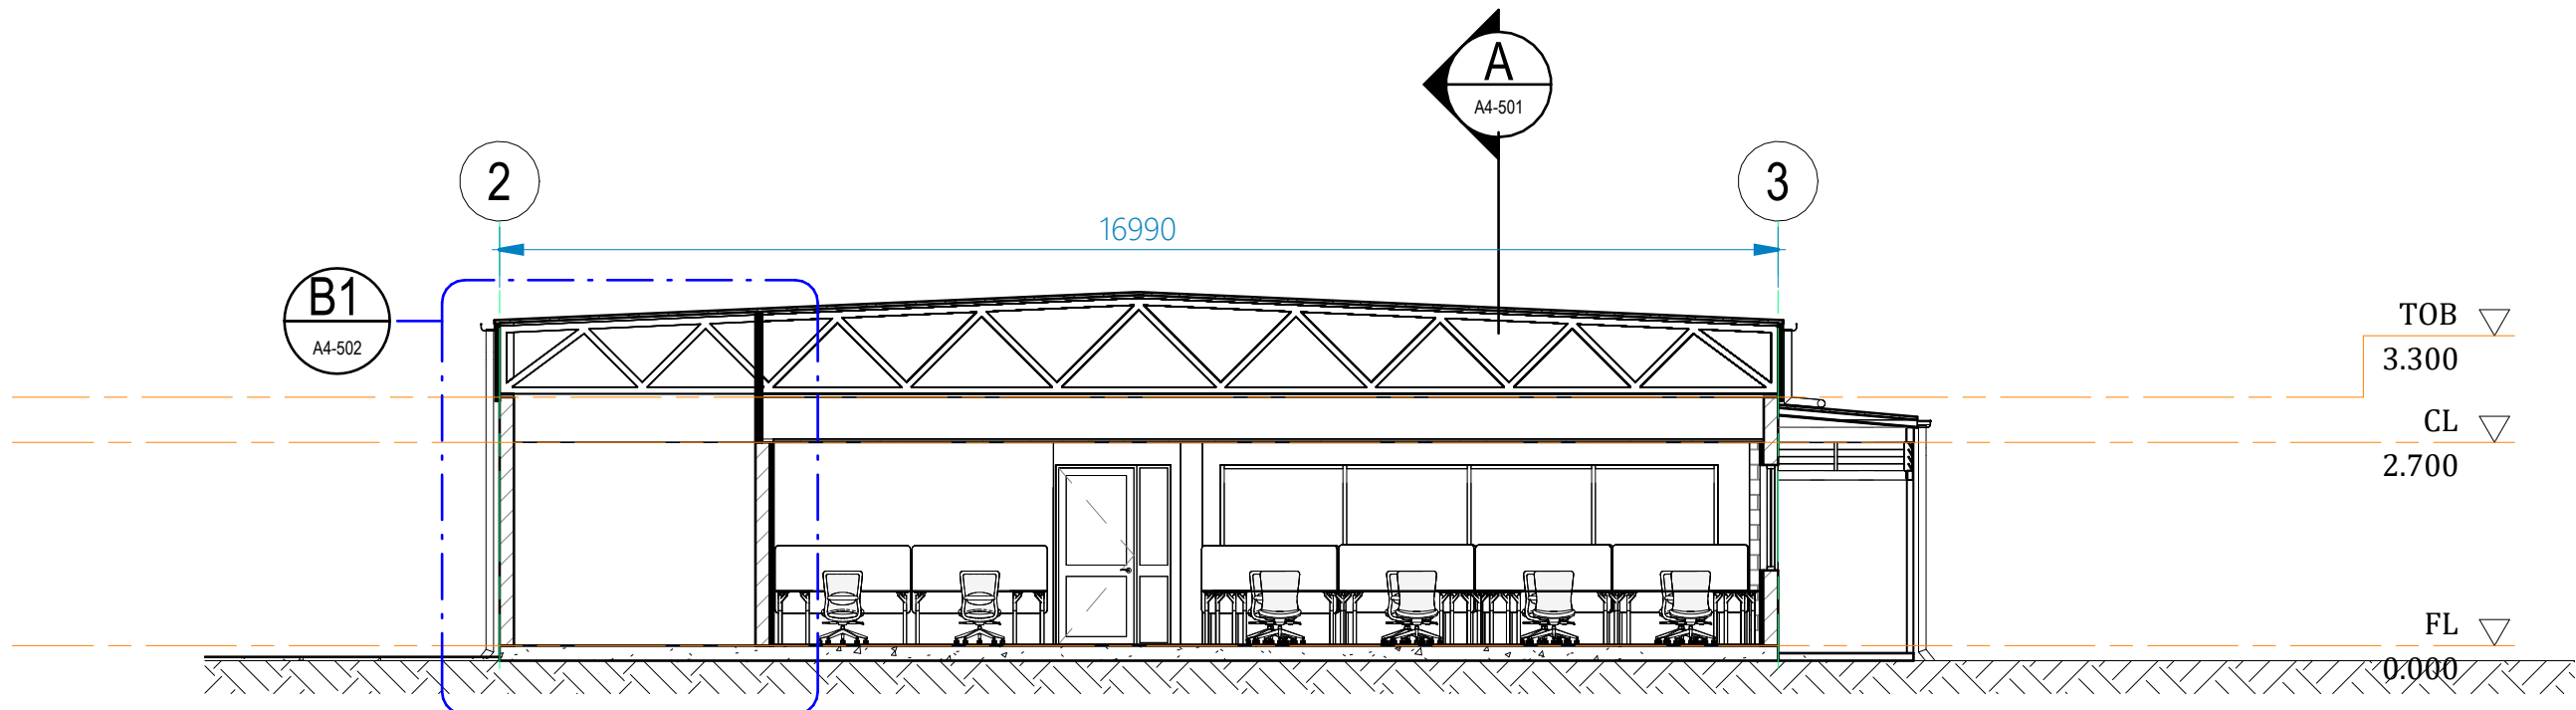

SECTION B
1 : 100

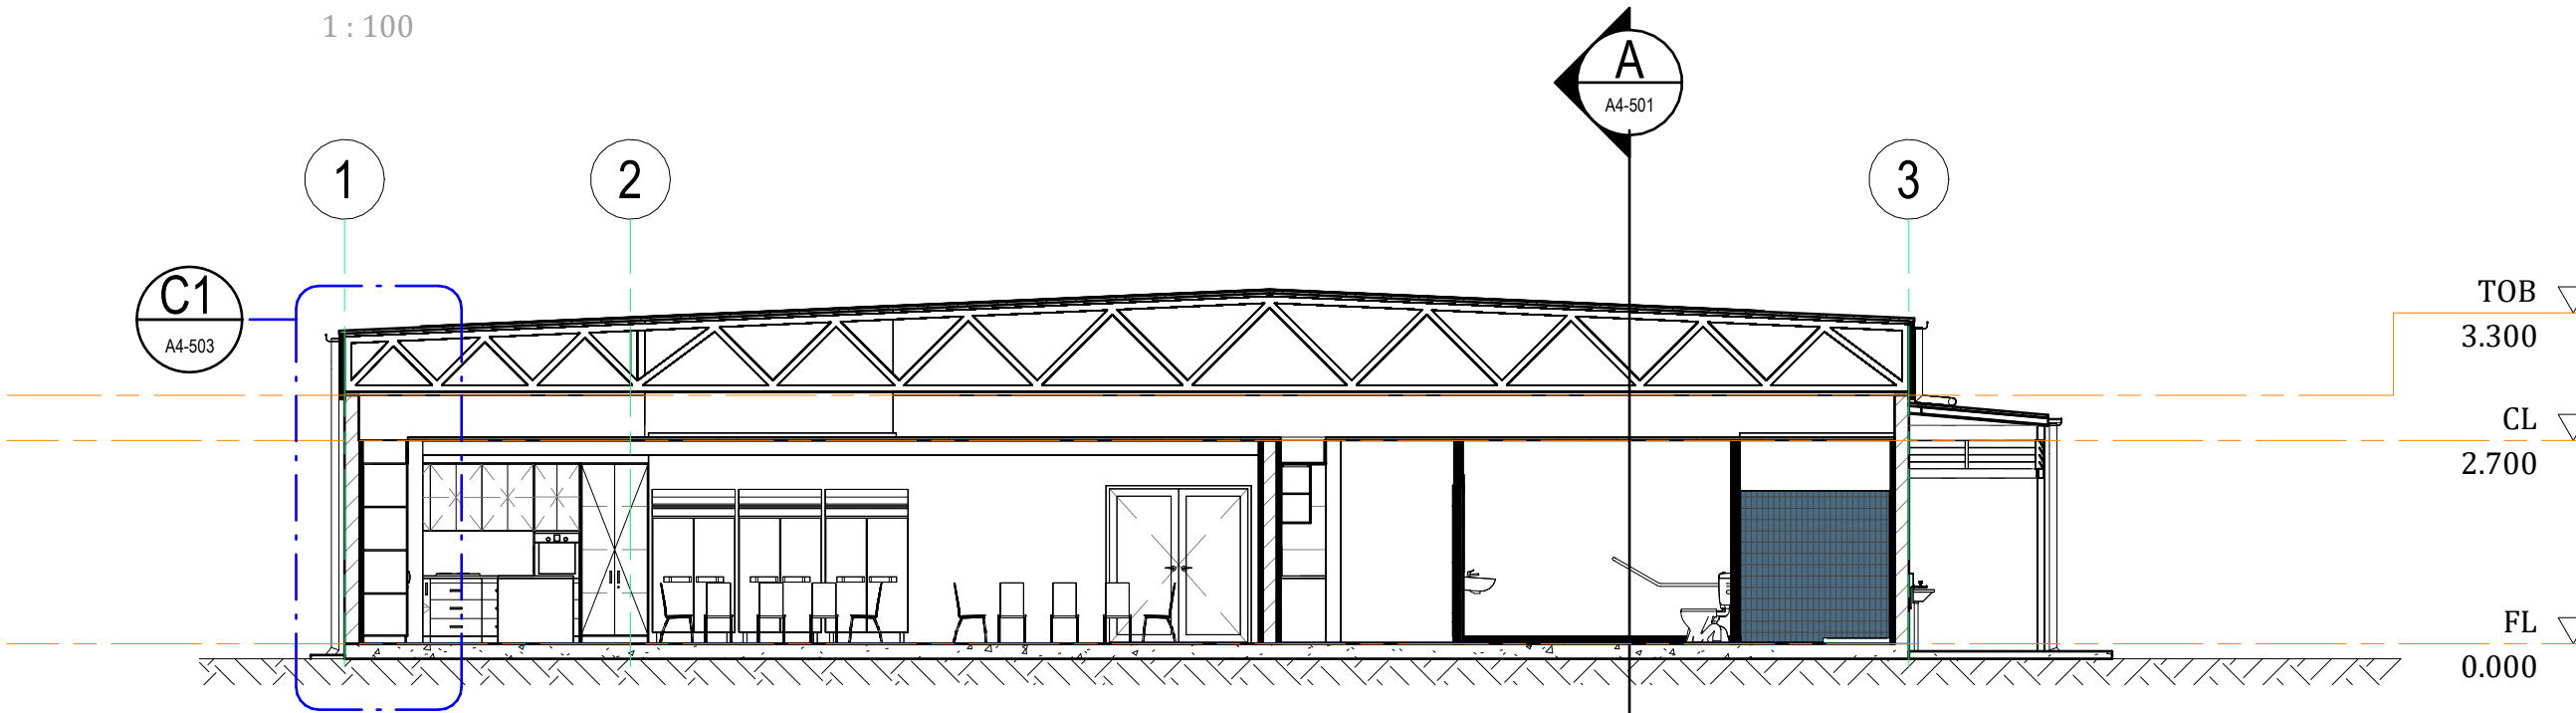

SECTION C
1 : 100

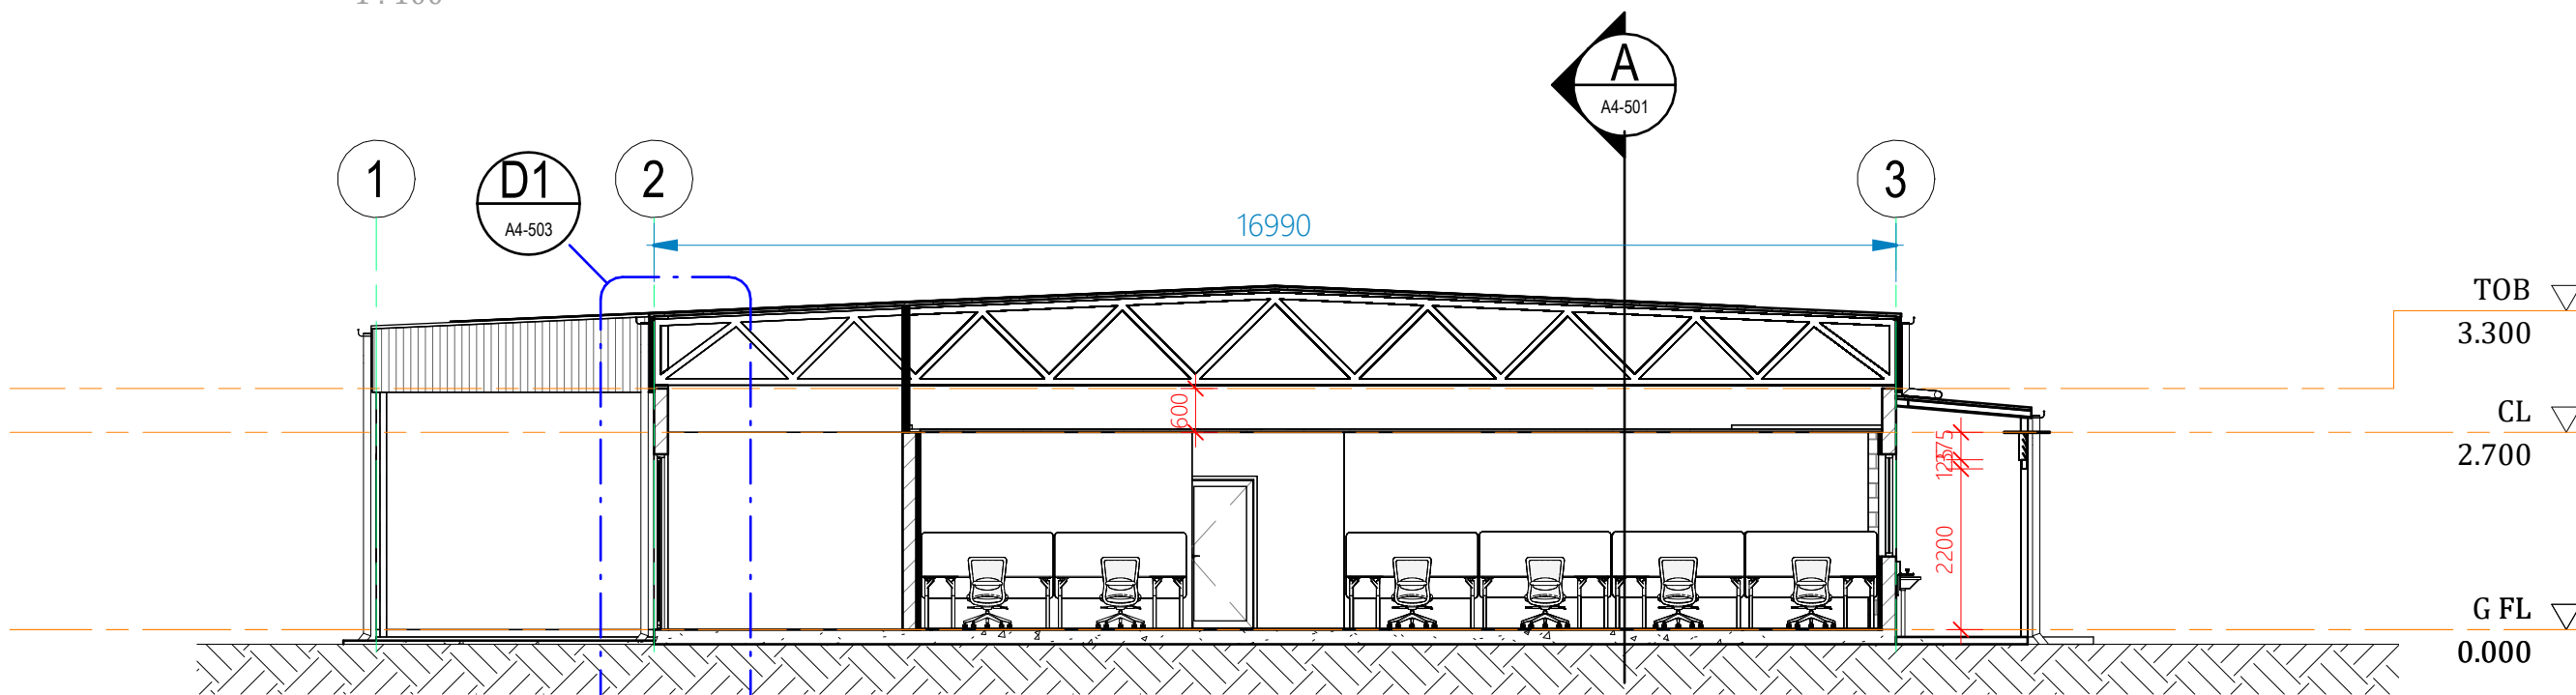

SECTION D
1 : 100

TENDER ISSUE




Project Details
OFFICE REFURBS
Address
STANWELL POWER STATION
Drawing Title
PROPOSED SECTIONS



0483 988 655 **M**
info@dezienelements.com.au **E**
QBCC No: 1247120 BDAQ No: 0001677


Scale: 1 : 100 Rev:
Date: MAR 2026 **T1**
Drawn: Author

Project No: Drawing No:
25_003 A4-501

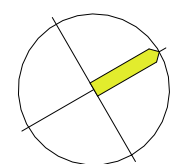

REVISIONS		
Rev	Description	Date
T1	TENDER ISSUE	12.03.2026

DO NOT SCALE THIS DRAWINGS

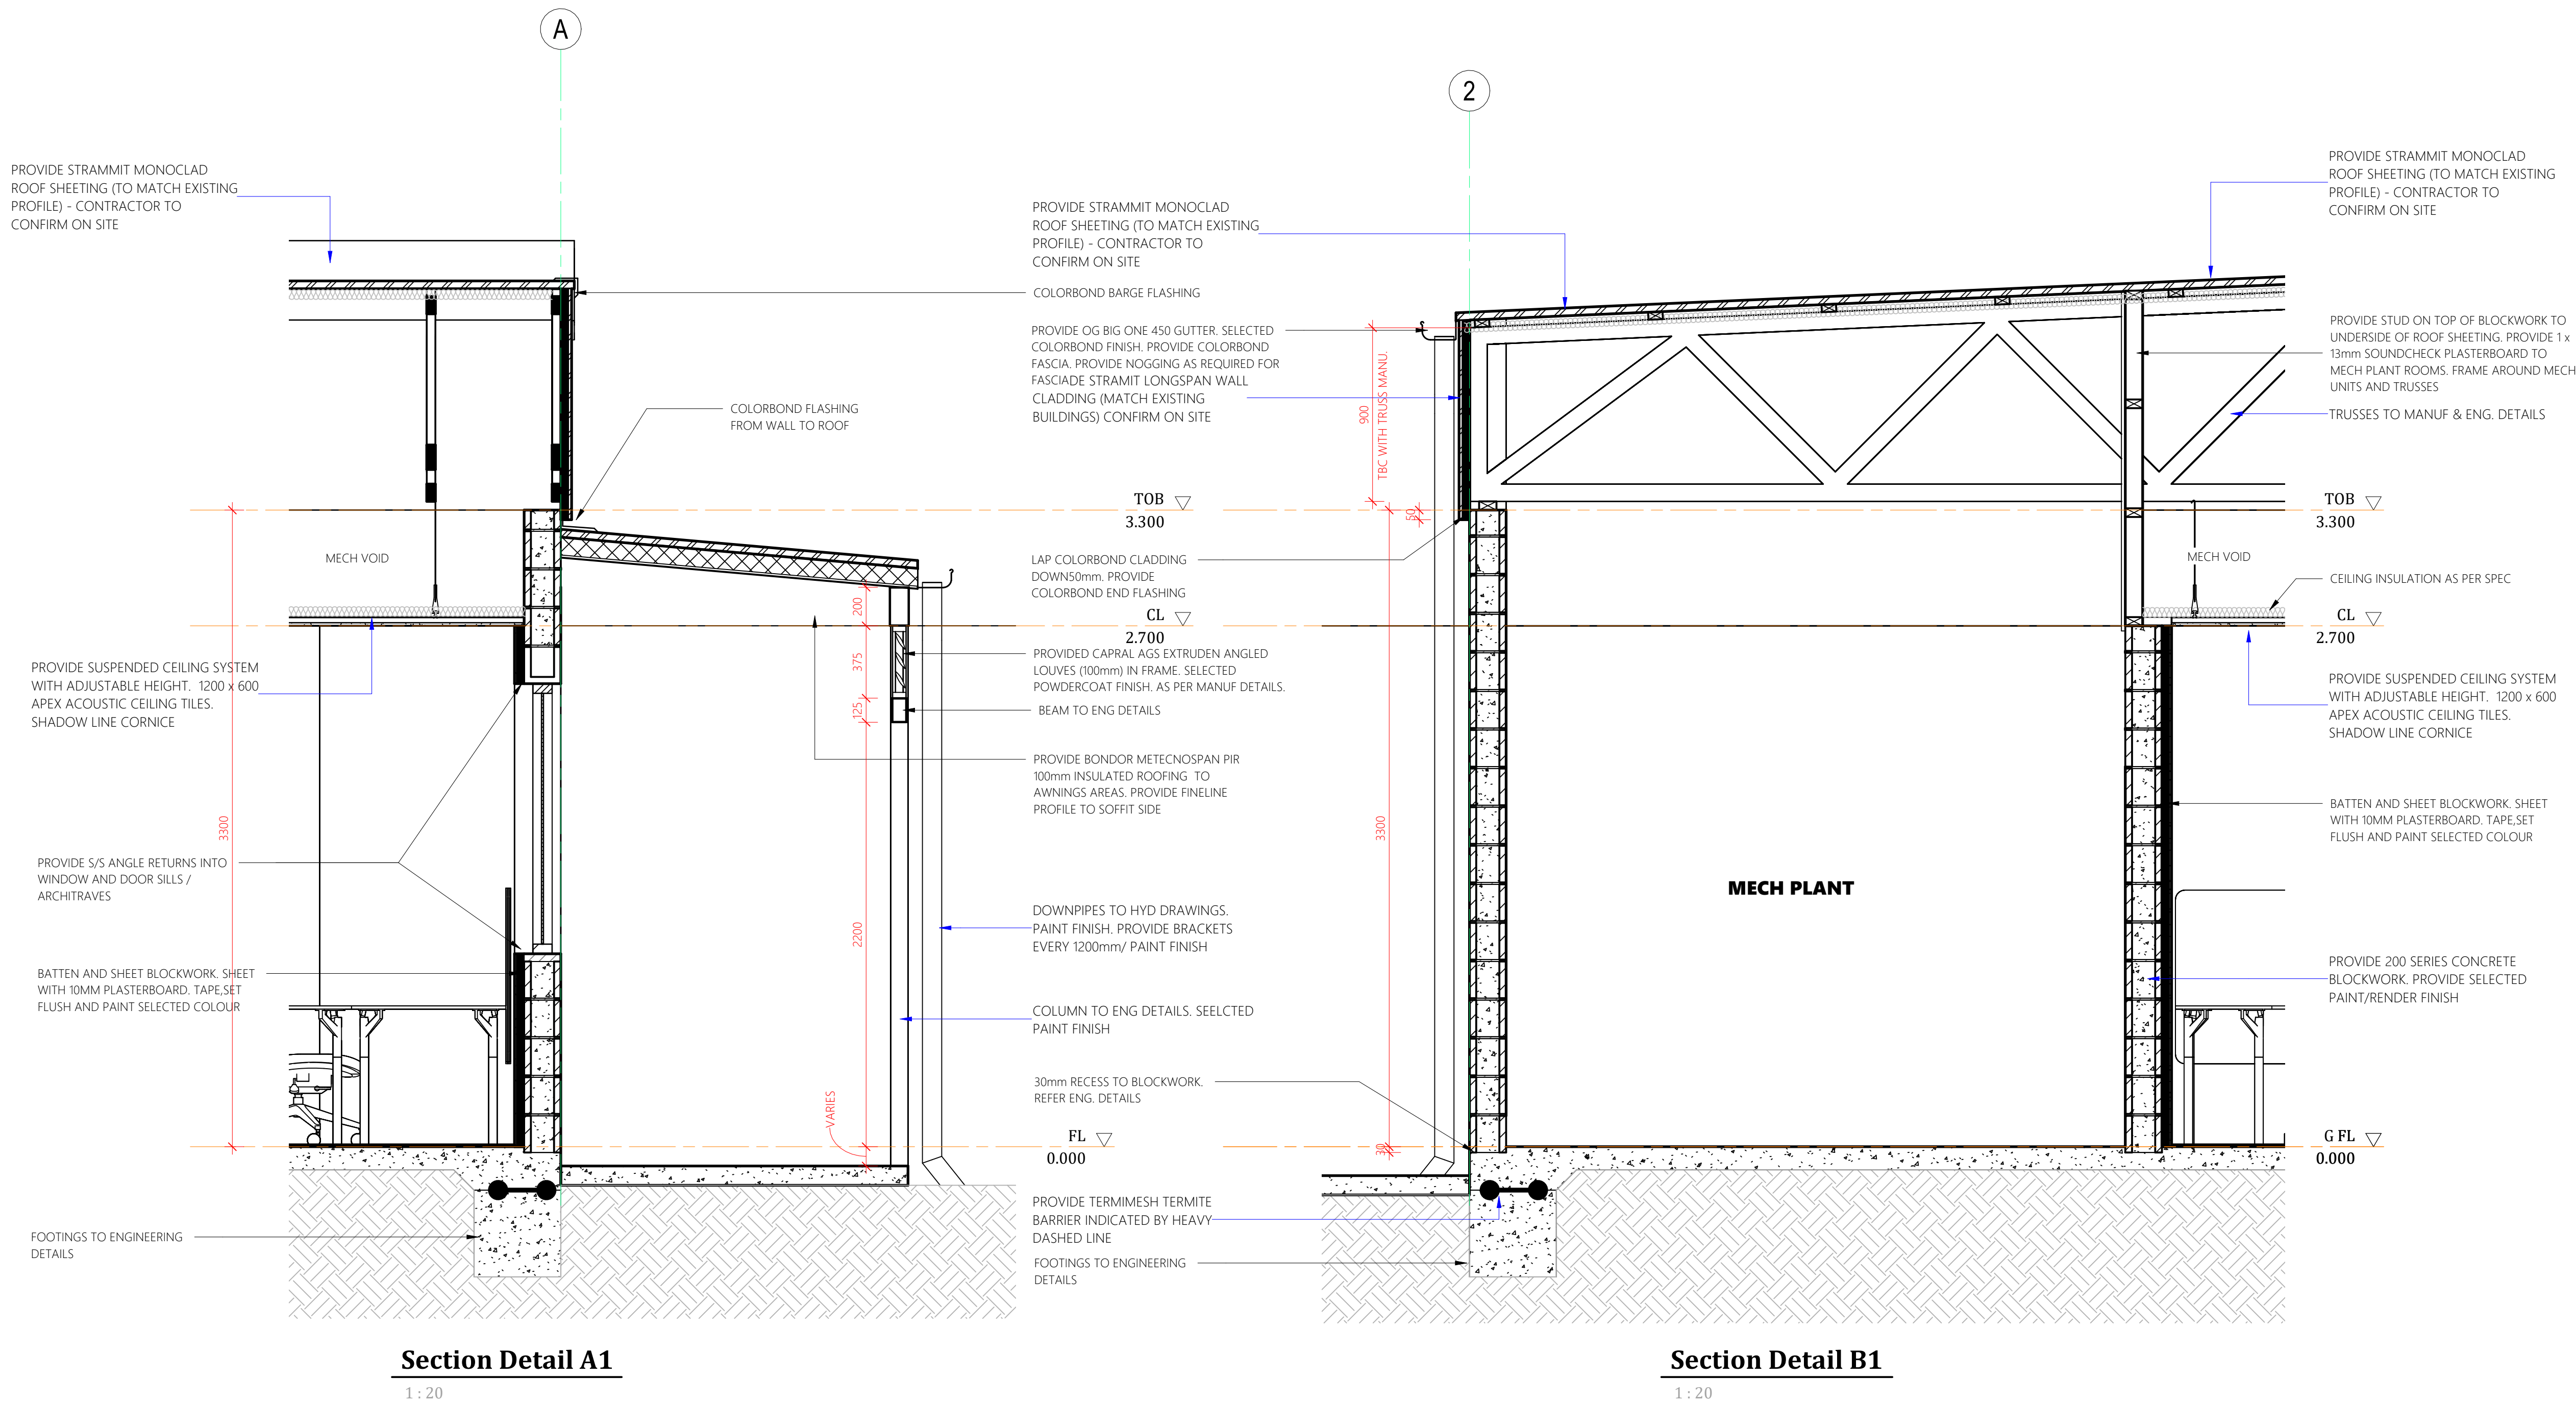

TENDER ISSUE

Client

 **stanwell**

Project Details

OFFICE REFURBS

Address

STANWELL POWER STATION

Drawing Title

PROPOSED SECTION DETAILS

 **designelements**
BUILDING DESIGNERS

0483 988 655 **M**
info@designelements.com.au **E**

QBCC No: 1247120 BDAQ No: 0001677

Scale: 1 : 20 Rev: **T1**
Date: MAR 2026
Drawn: Author

Project No: Drawing No:
25_003 A4-502

12/03/2026 7:55:36 PM


DO NOT SCALE THIS DRAWINGS



Client



 stanwell

 designelements BUILDING DESIGNERS		0483 988 655 M info@designelements.com.au E
QBCC No: 1247120 BDAQ No: 0001677		
Scale:	1: 20	Rev:
Date:	MAR 2026	T1 12/03/2026 7:55:36 PM
Drawn:	Author	
Project No:	Drawing No:	
25_003	A4-503	

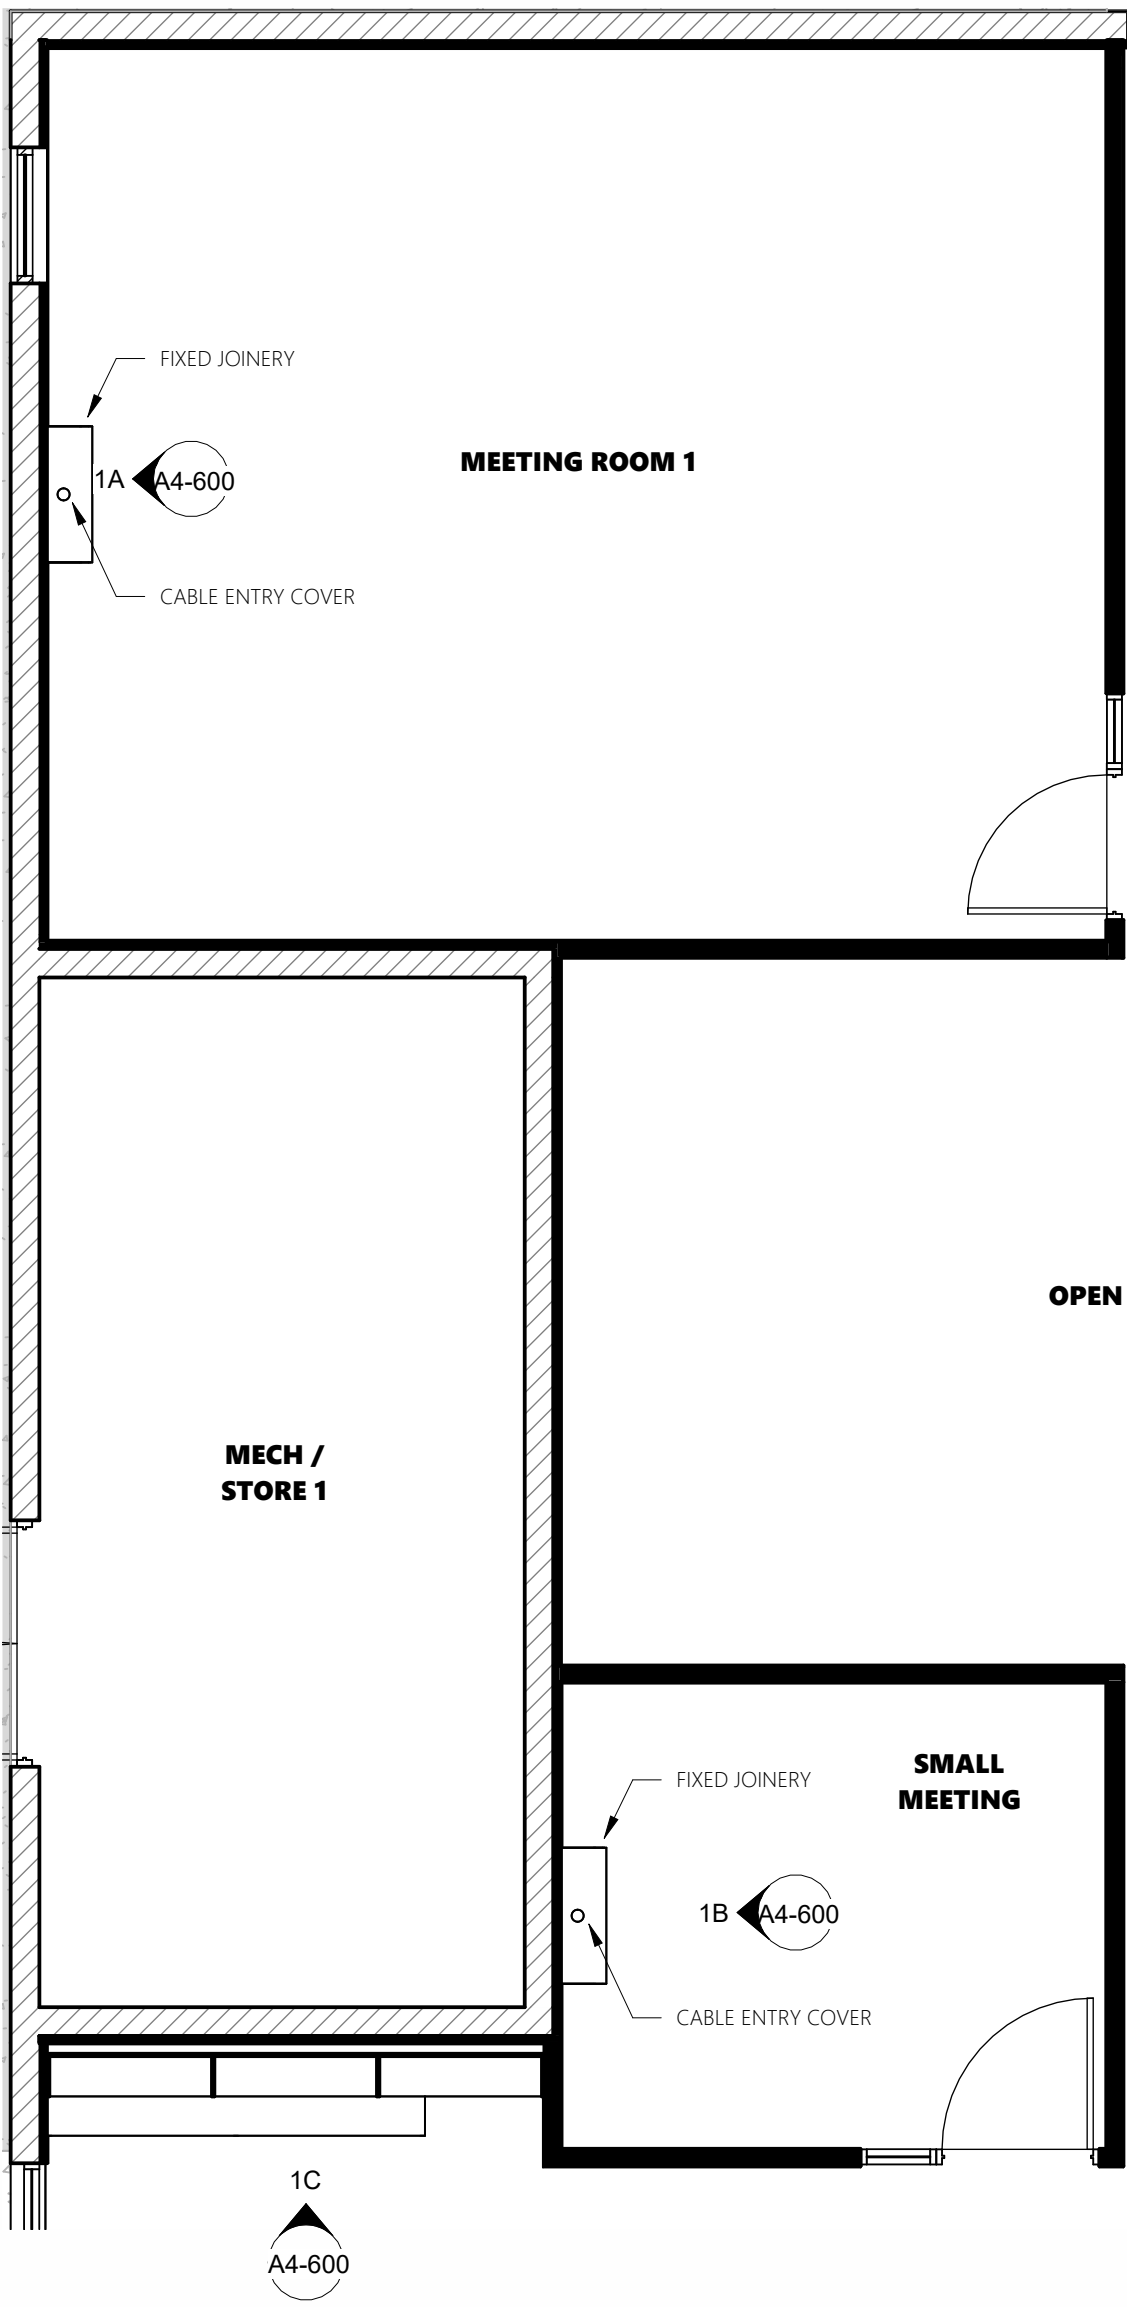

Internal Plan 2 - Consumables

1 : 50

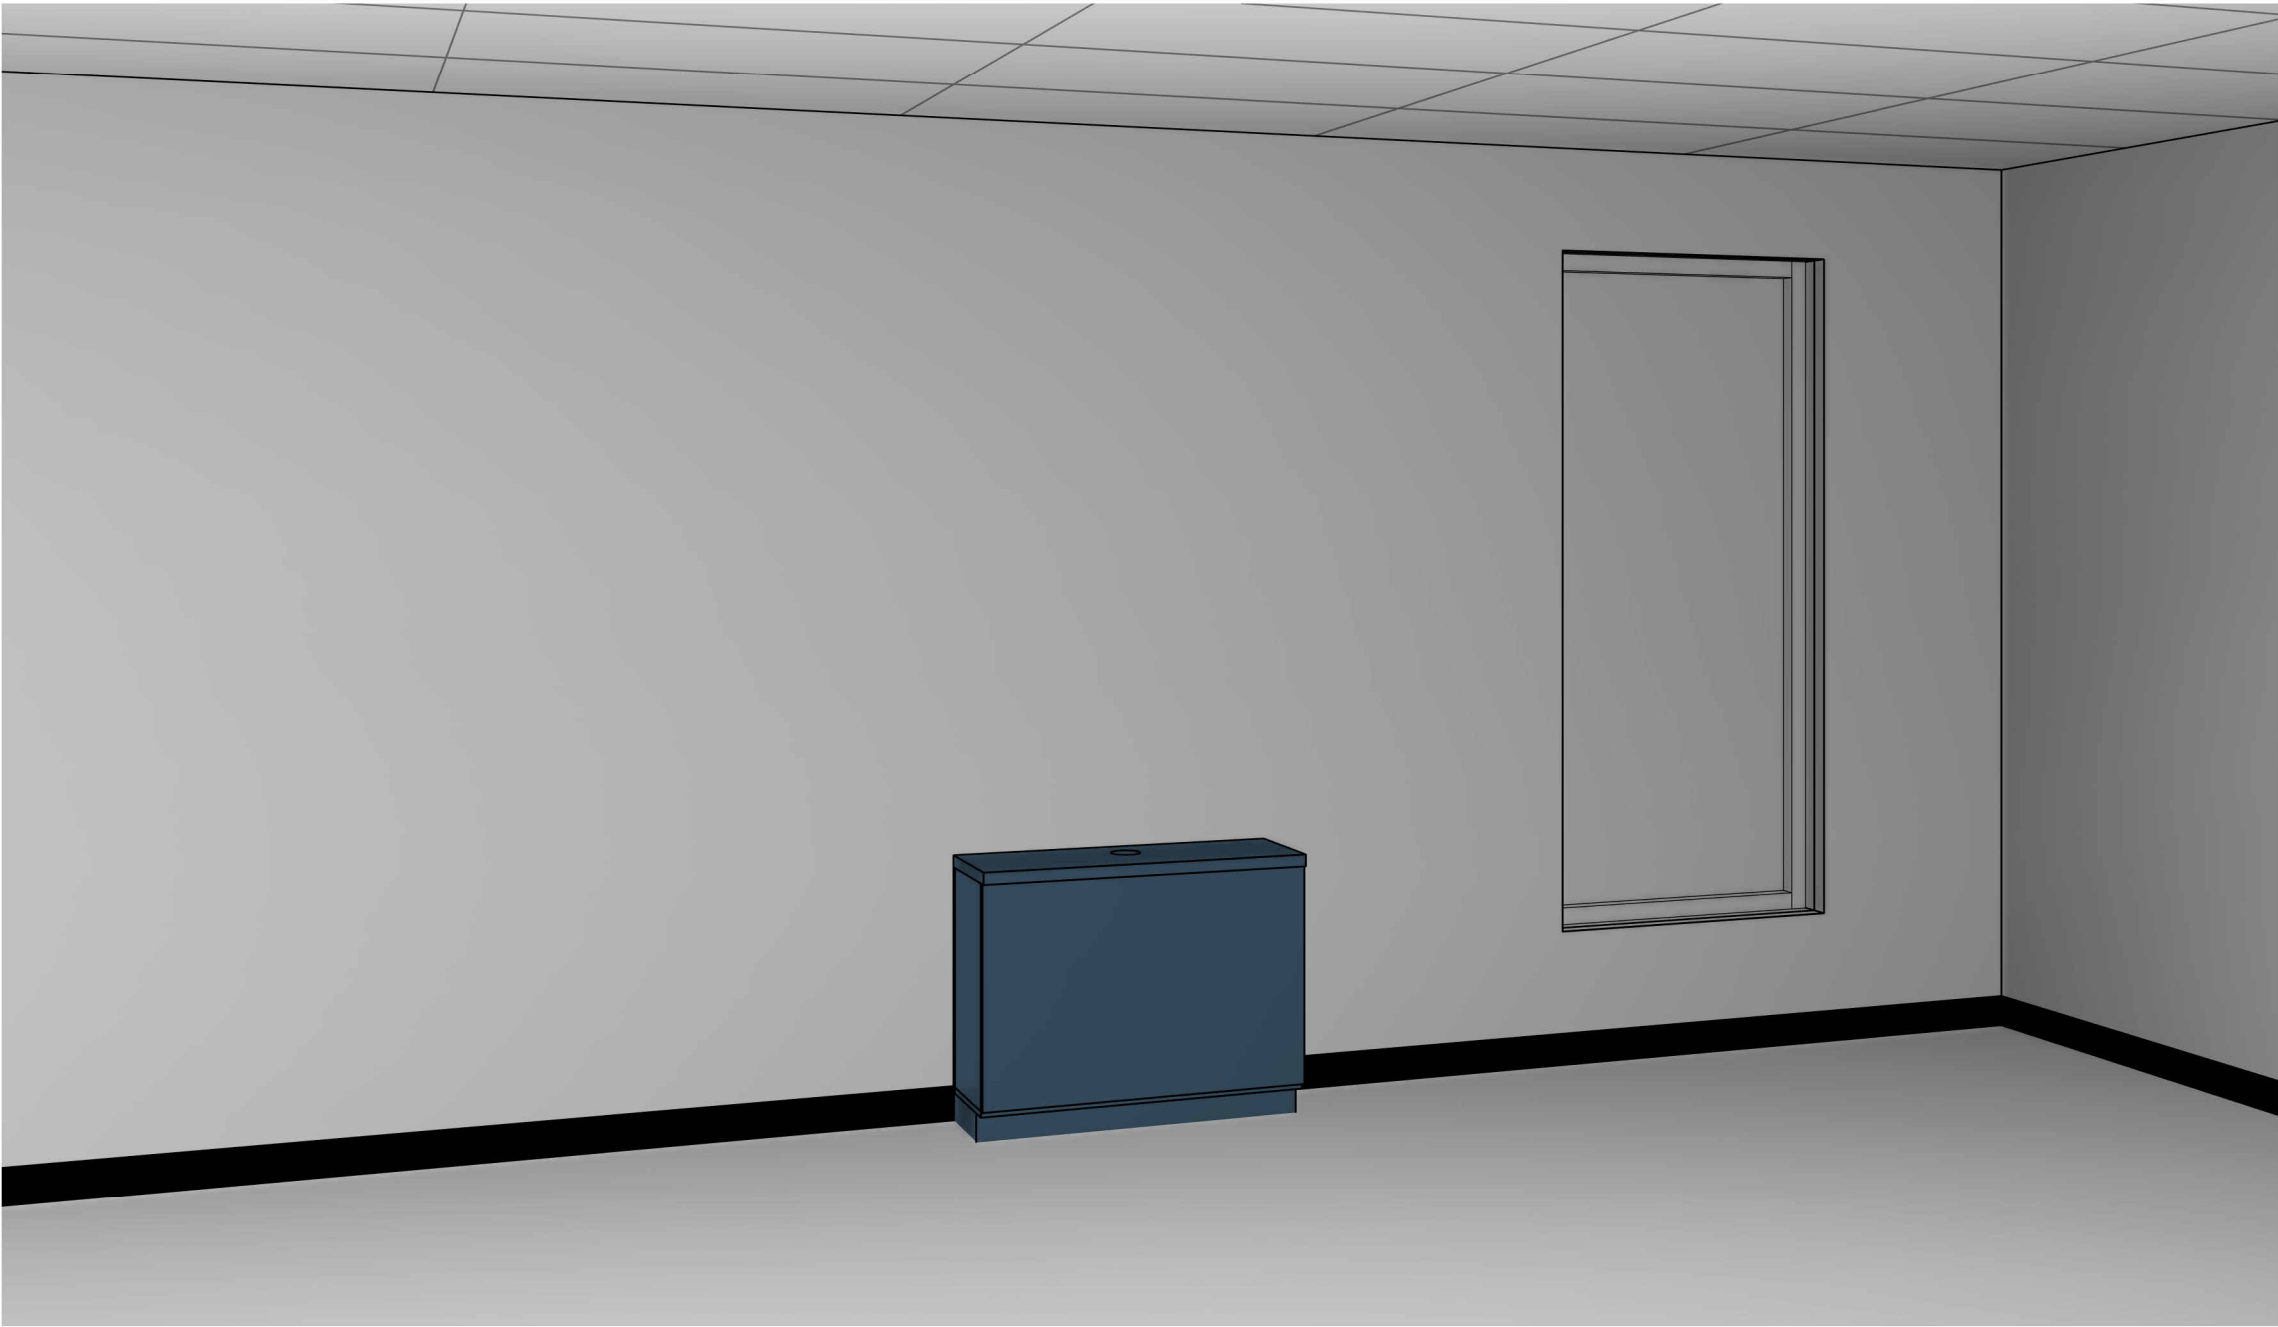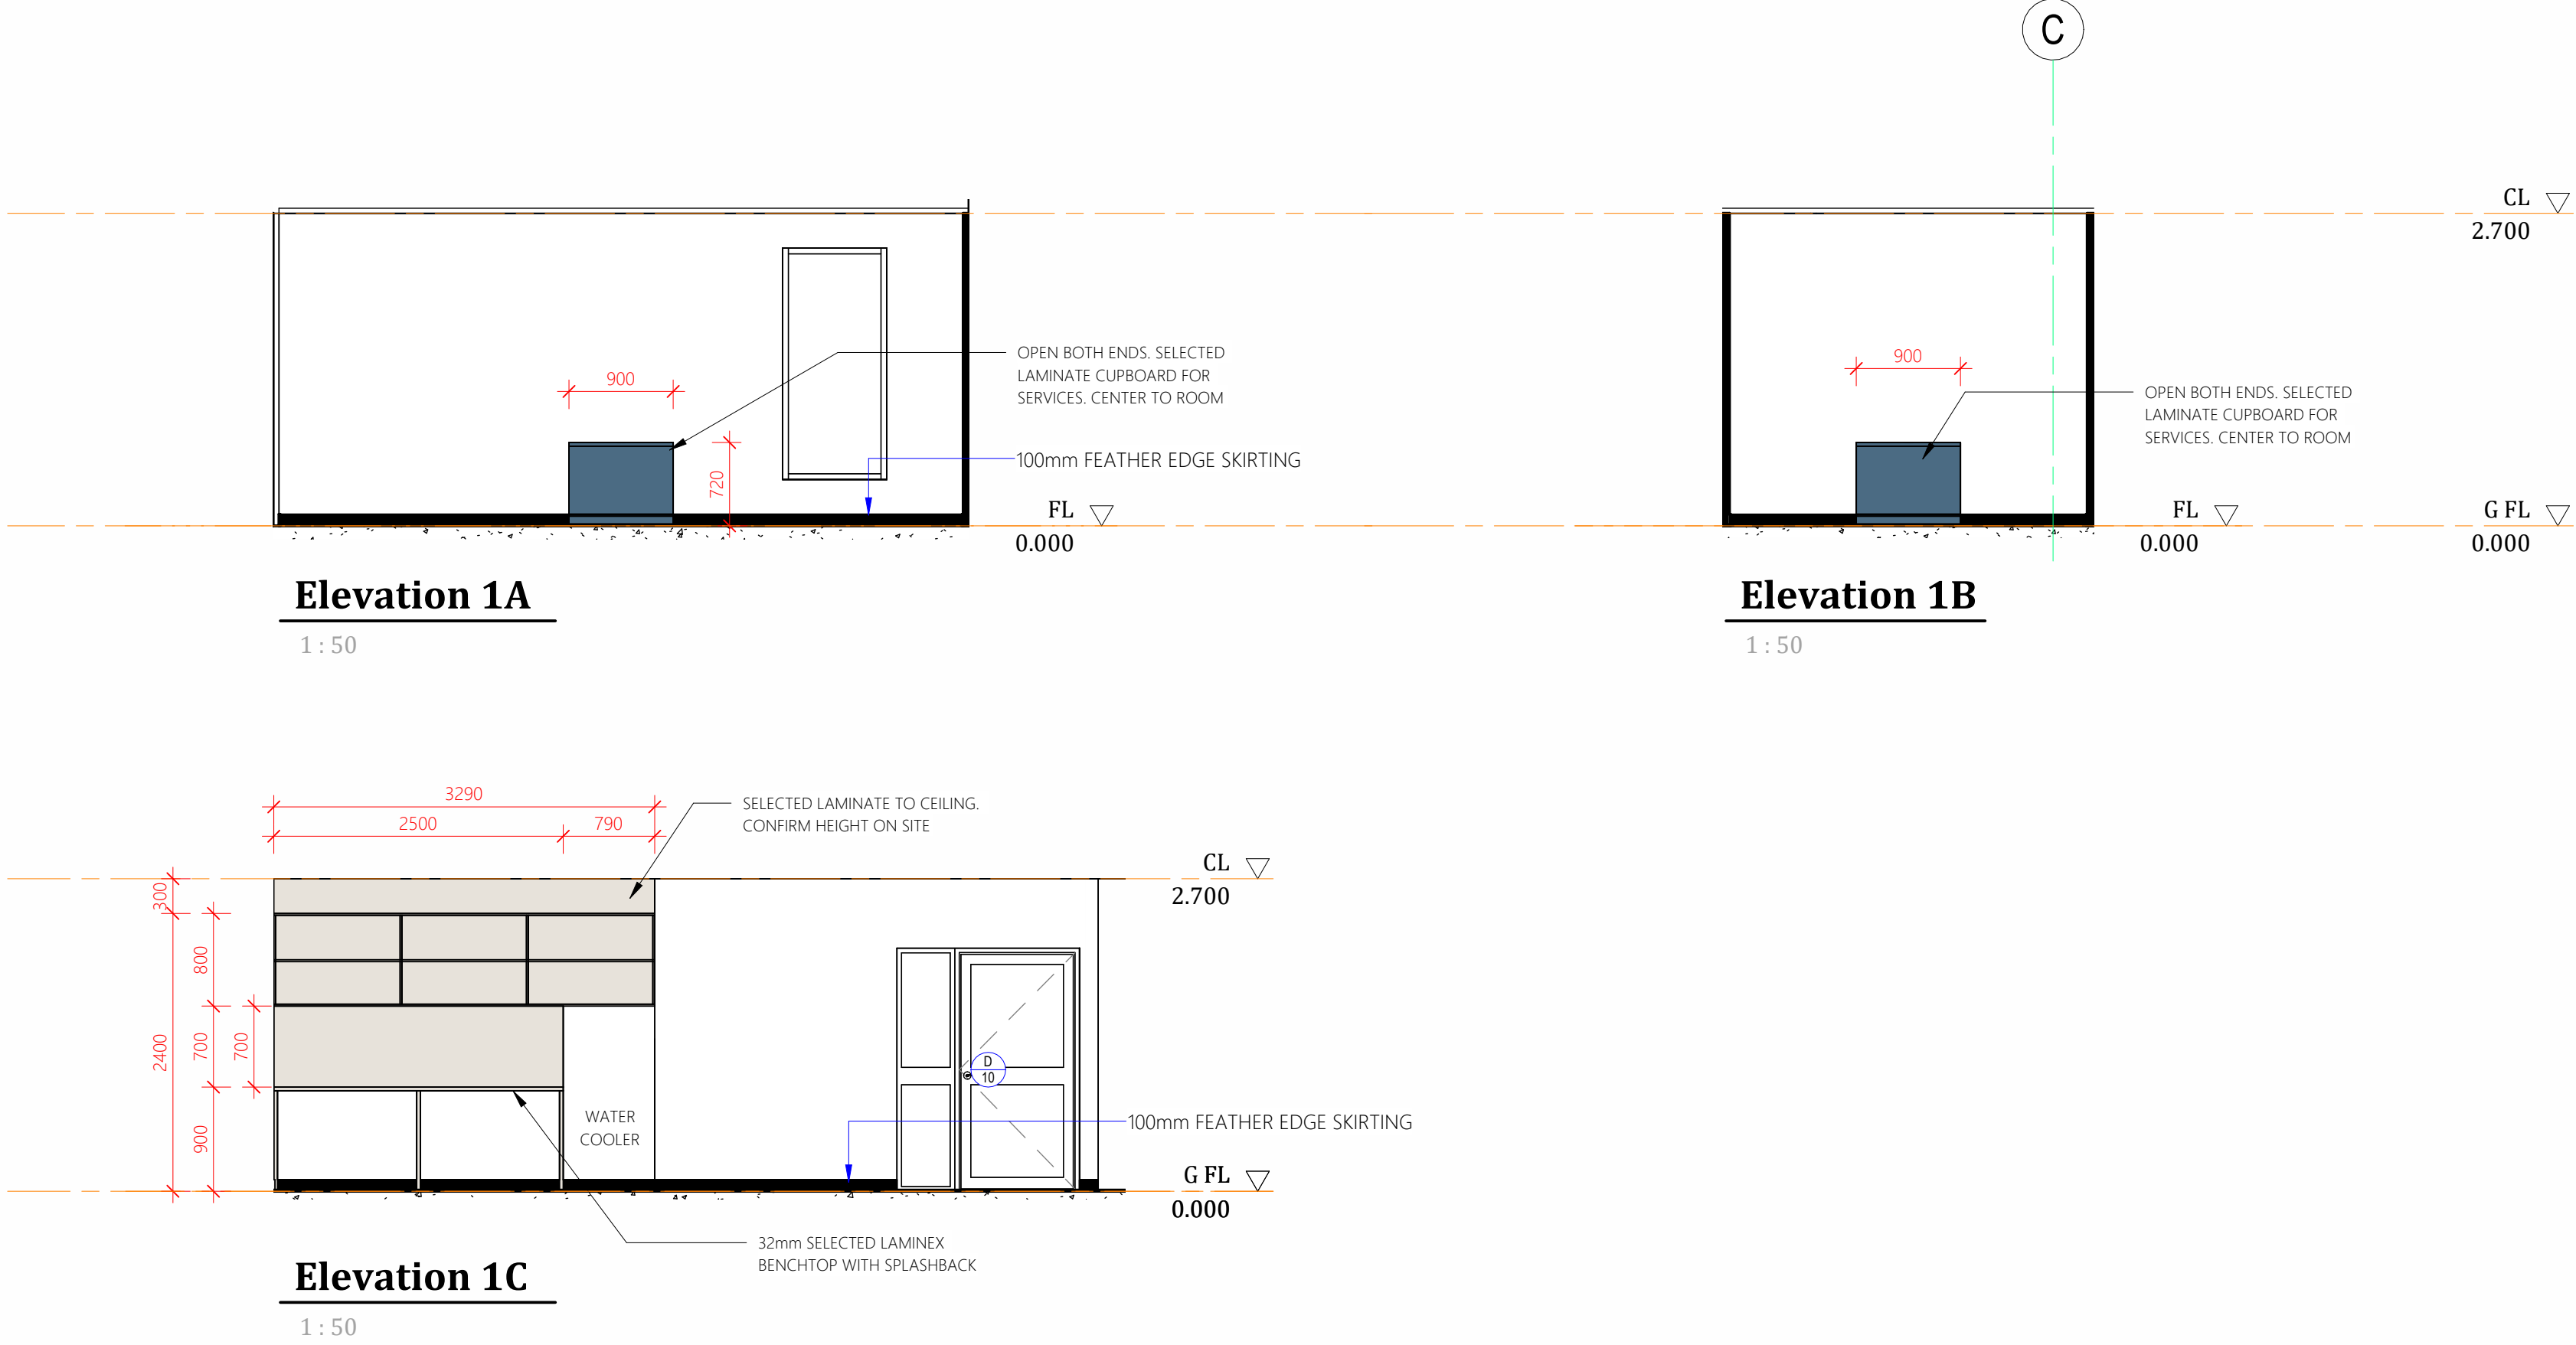

REVISIONS		
Rev	Description	Date
T1	TENDER ISSUE	12.03.2026

DO NOT SCALE THIS DRAWINGS



TENDER ISSUE

Client

 **stanwell**

Project Details

OFFICE REFURBS

Address

STANWELL POWER STATION

Drawing Title

INTERNAL DETAILS 1 - MEETING ROOM 1, SMALL MEETING


 **designelements**
BUILDING DESIGNERS


0483 988 655 **M**

info@designelements.com.au **E**

QBCC No: 1247120 BDAQ No: 0001677


Scale: 1 : 50	Rev: T1
Date: MAR 2026	
Drawn: Author	
Project No: 25_003	Drawing No: A4-600

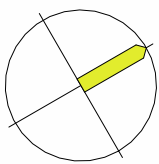

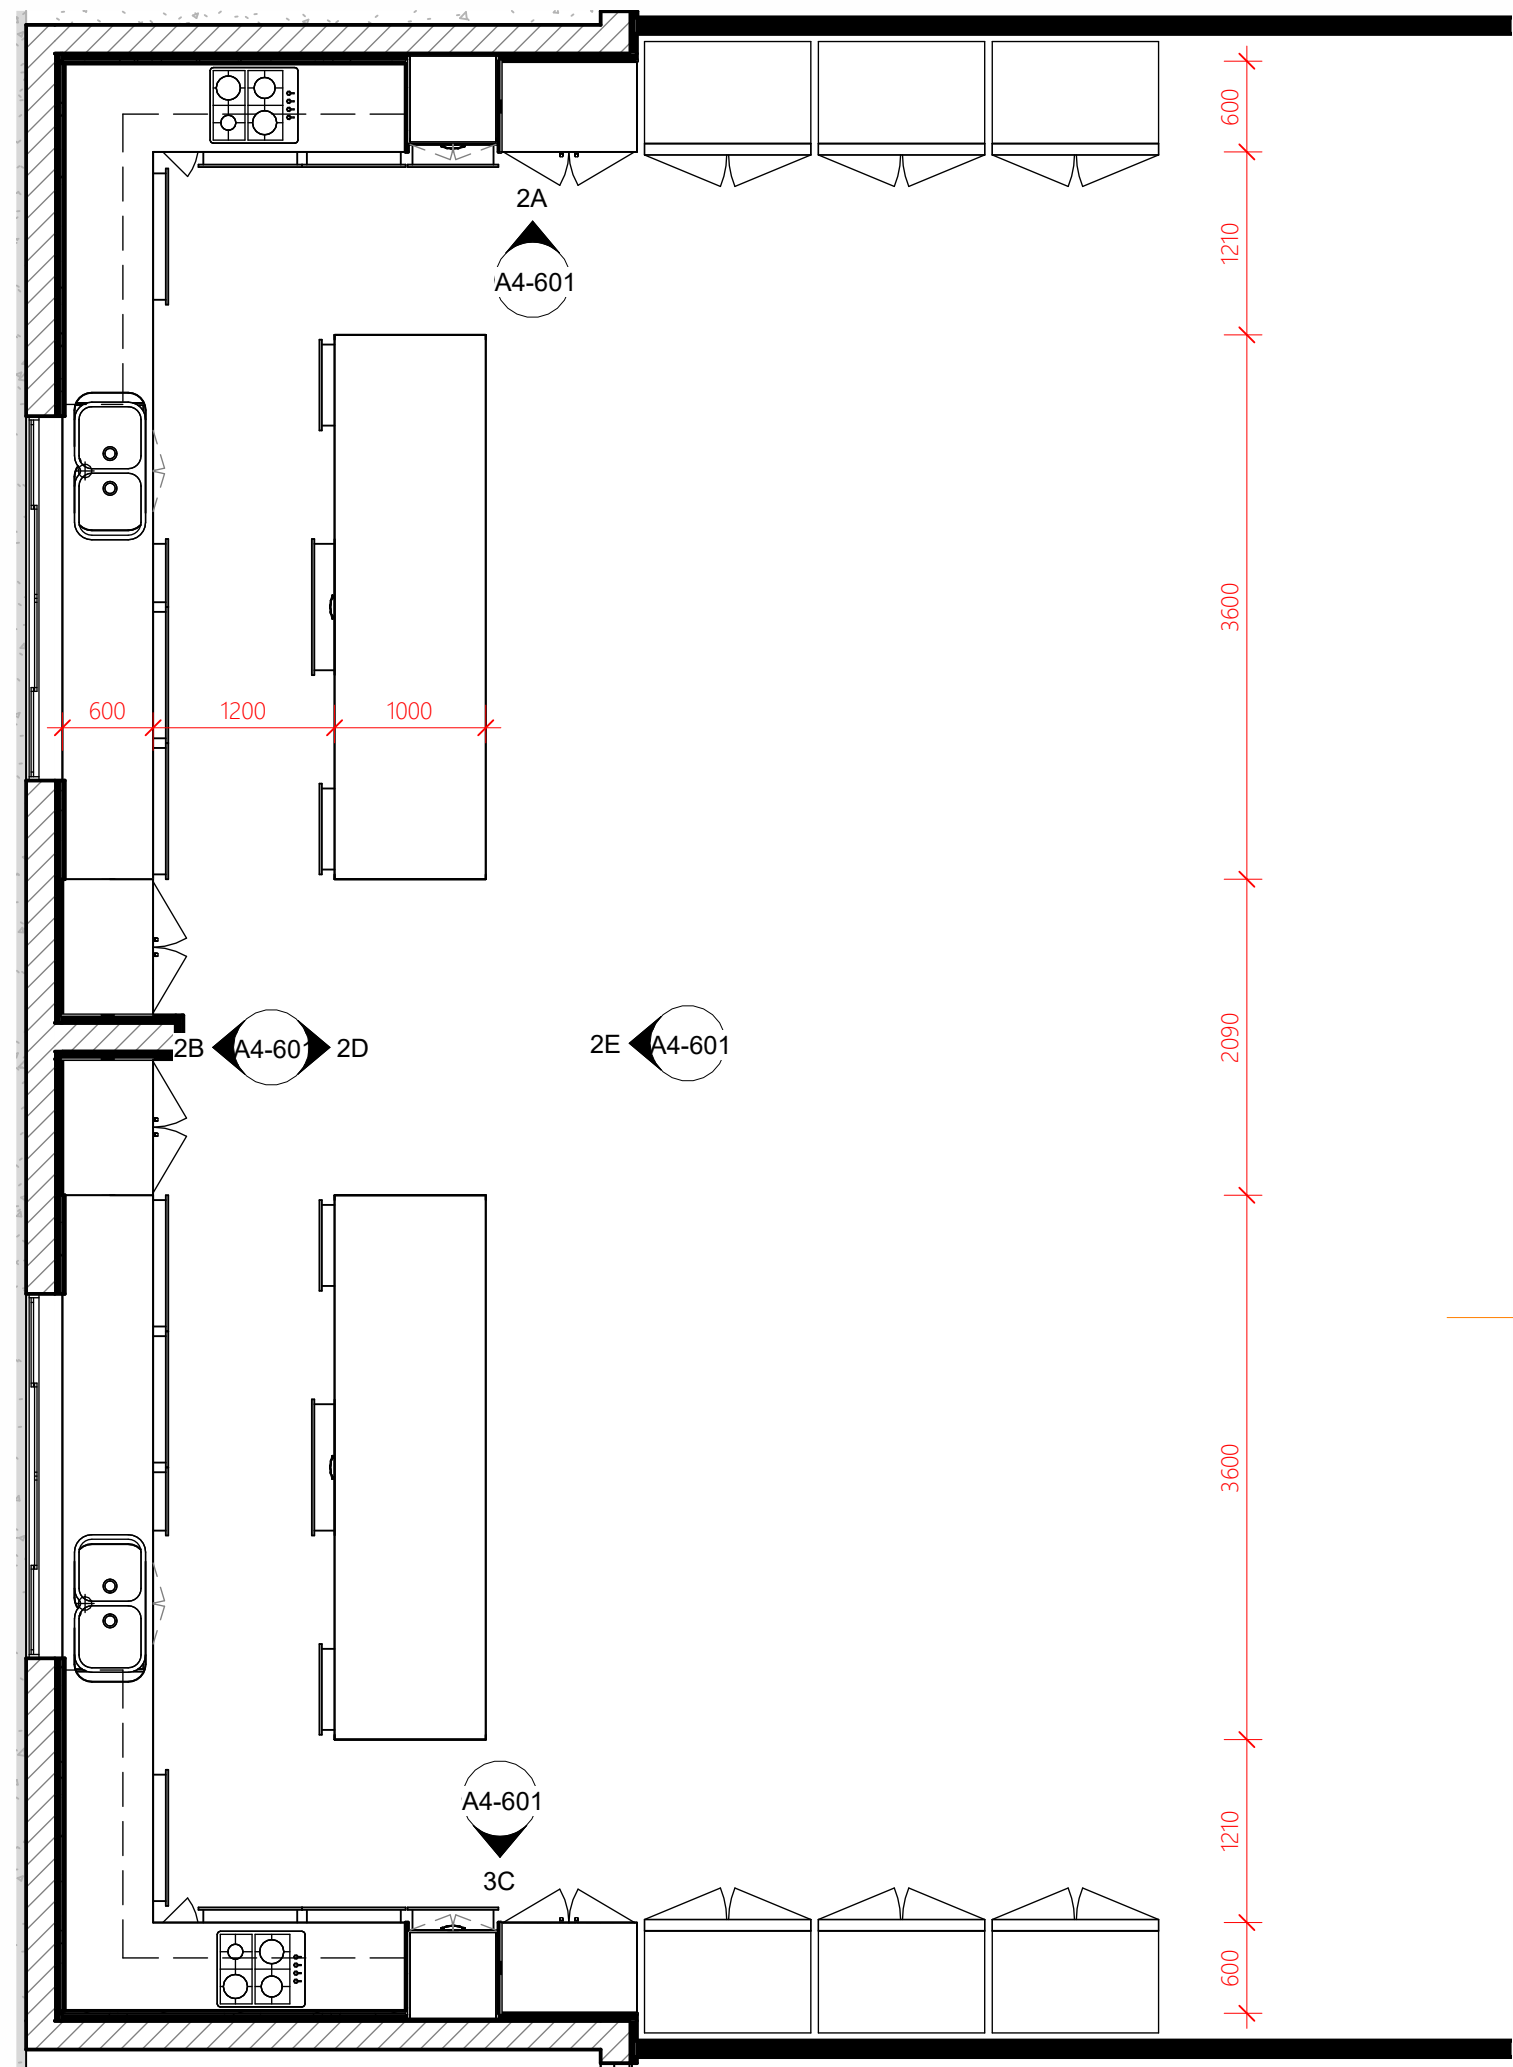


Internal Plan 1 - Kitchen

1 : 50

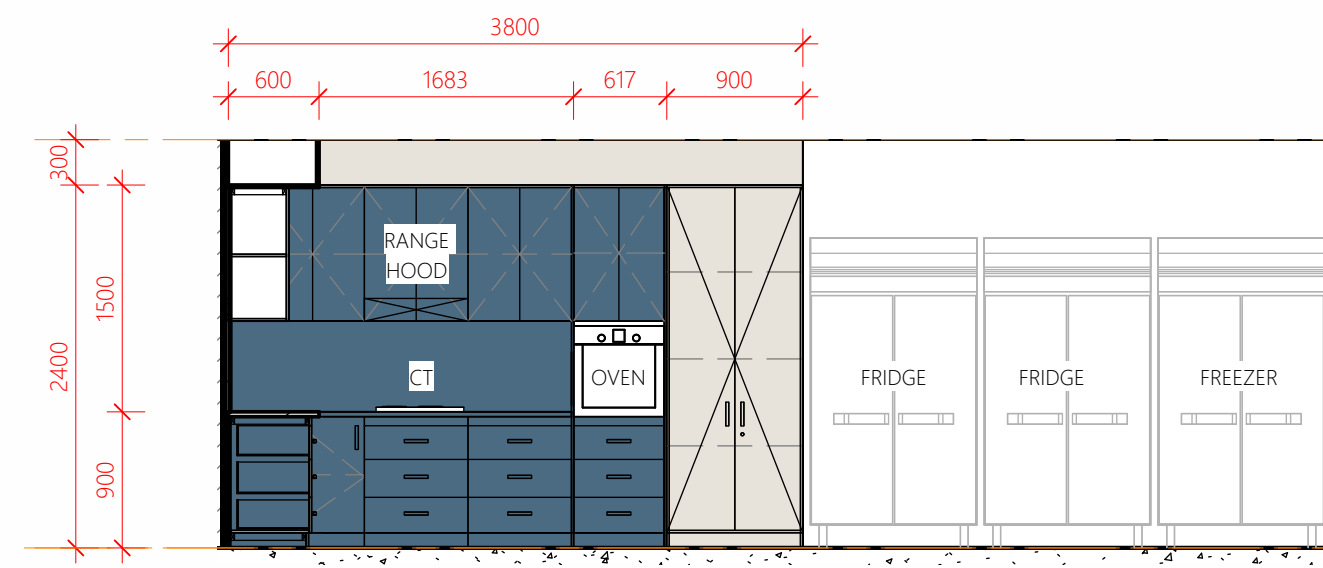


Elevation 2A

1 : 50

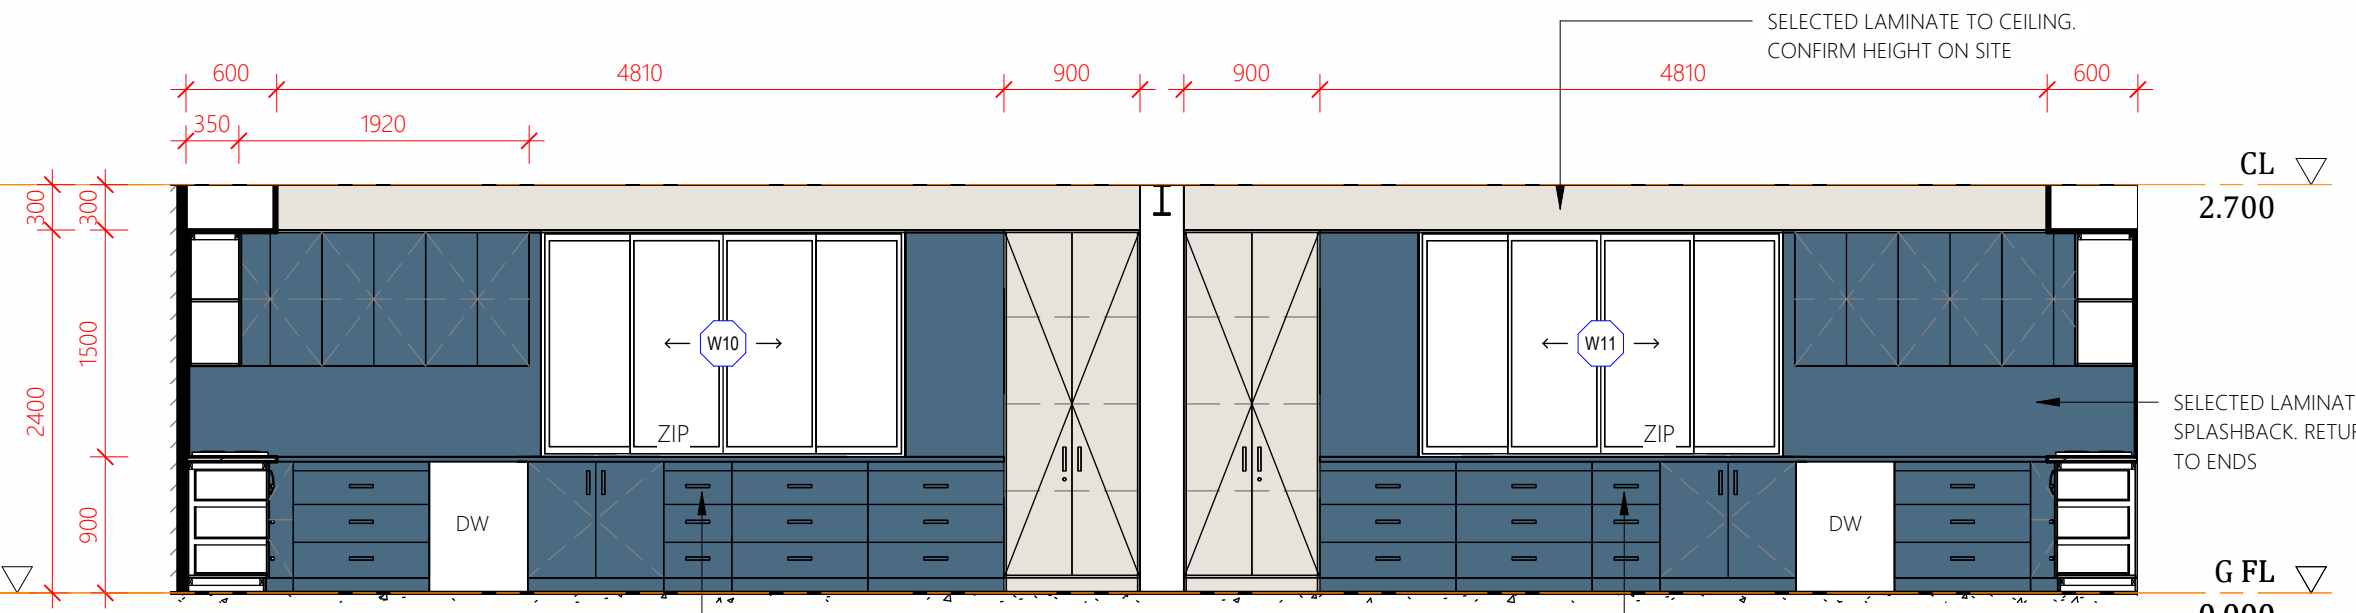


Elevation 2B

1 : 50

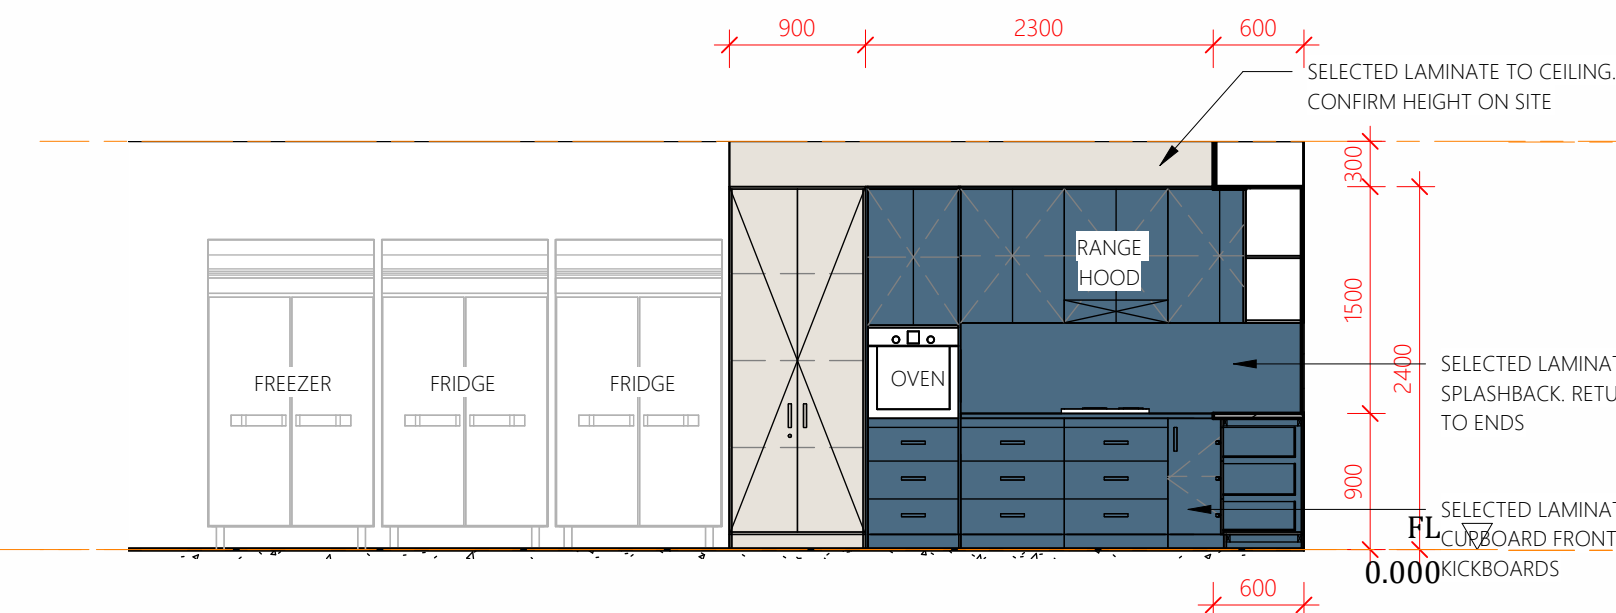


Elevation 2C

1 : 50

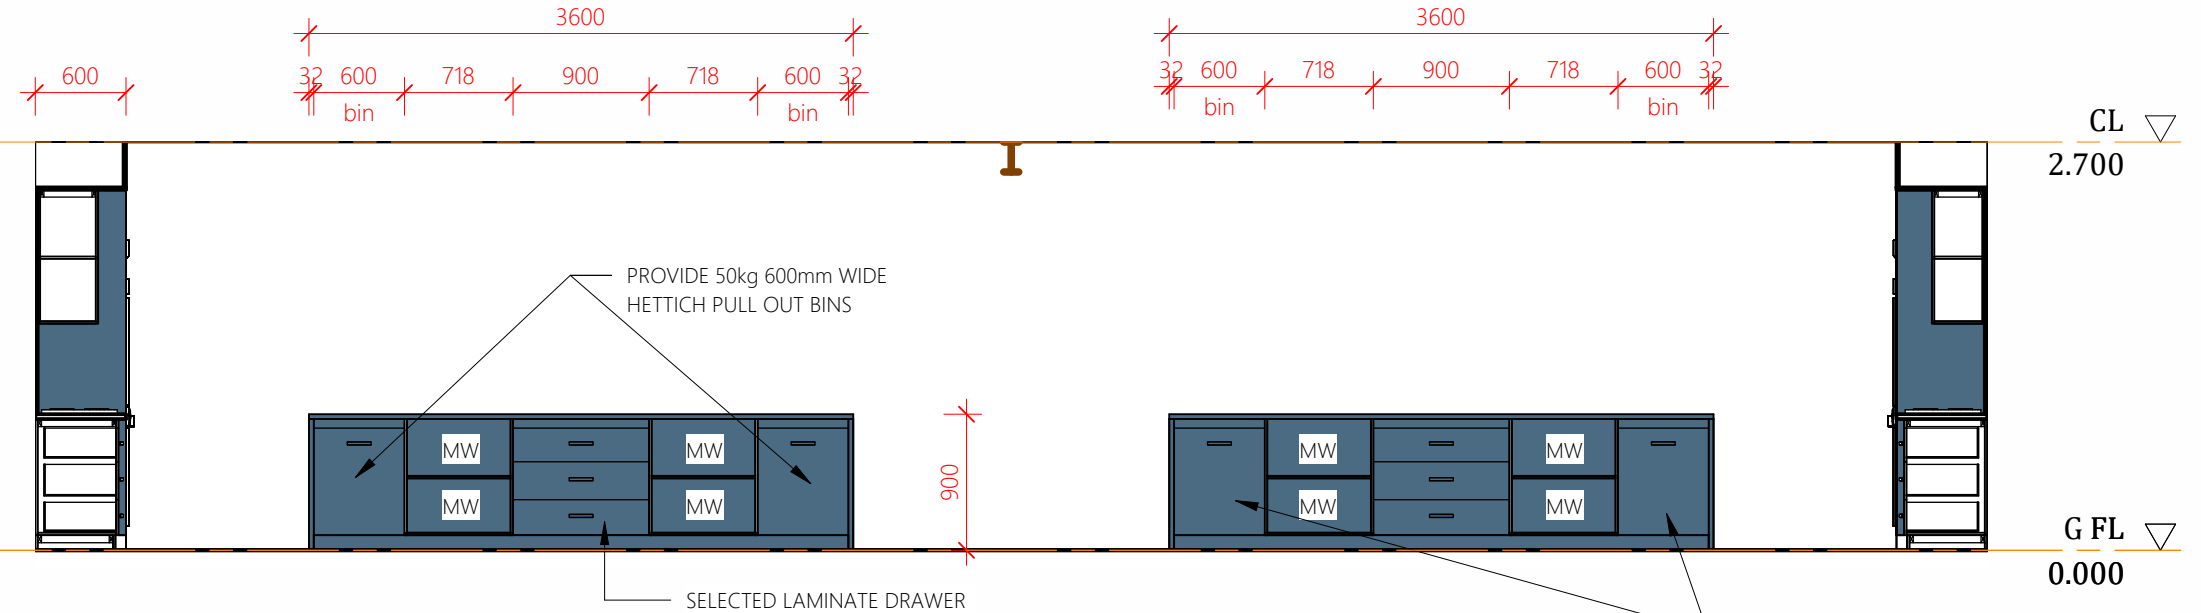


Elevation 2D

1 : 50

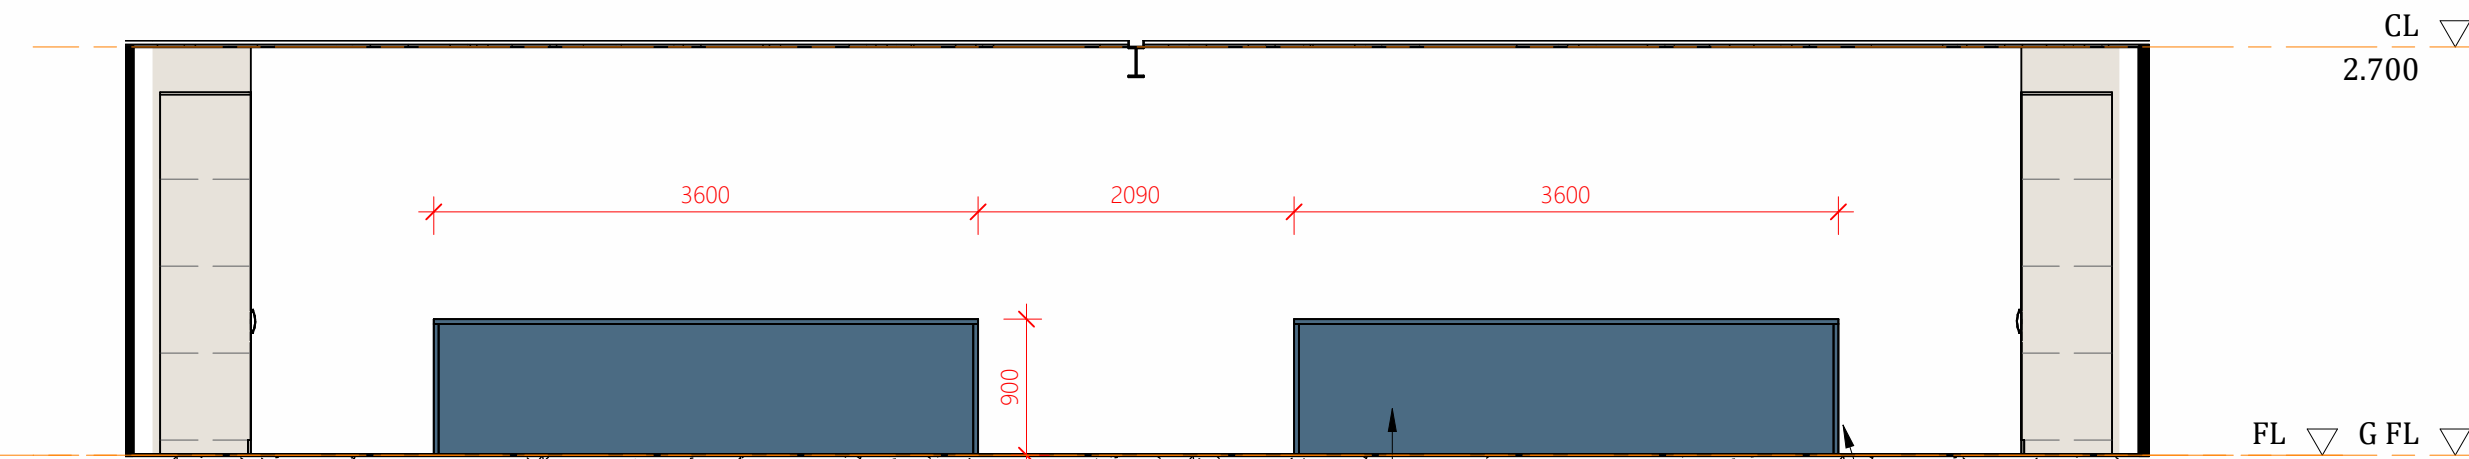

Elevation 2E


1 : 50

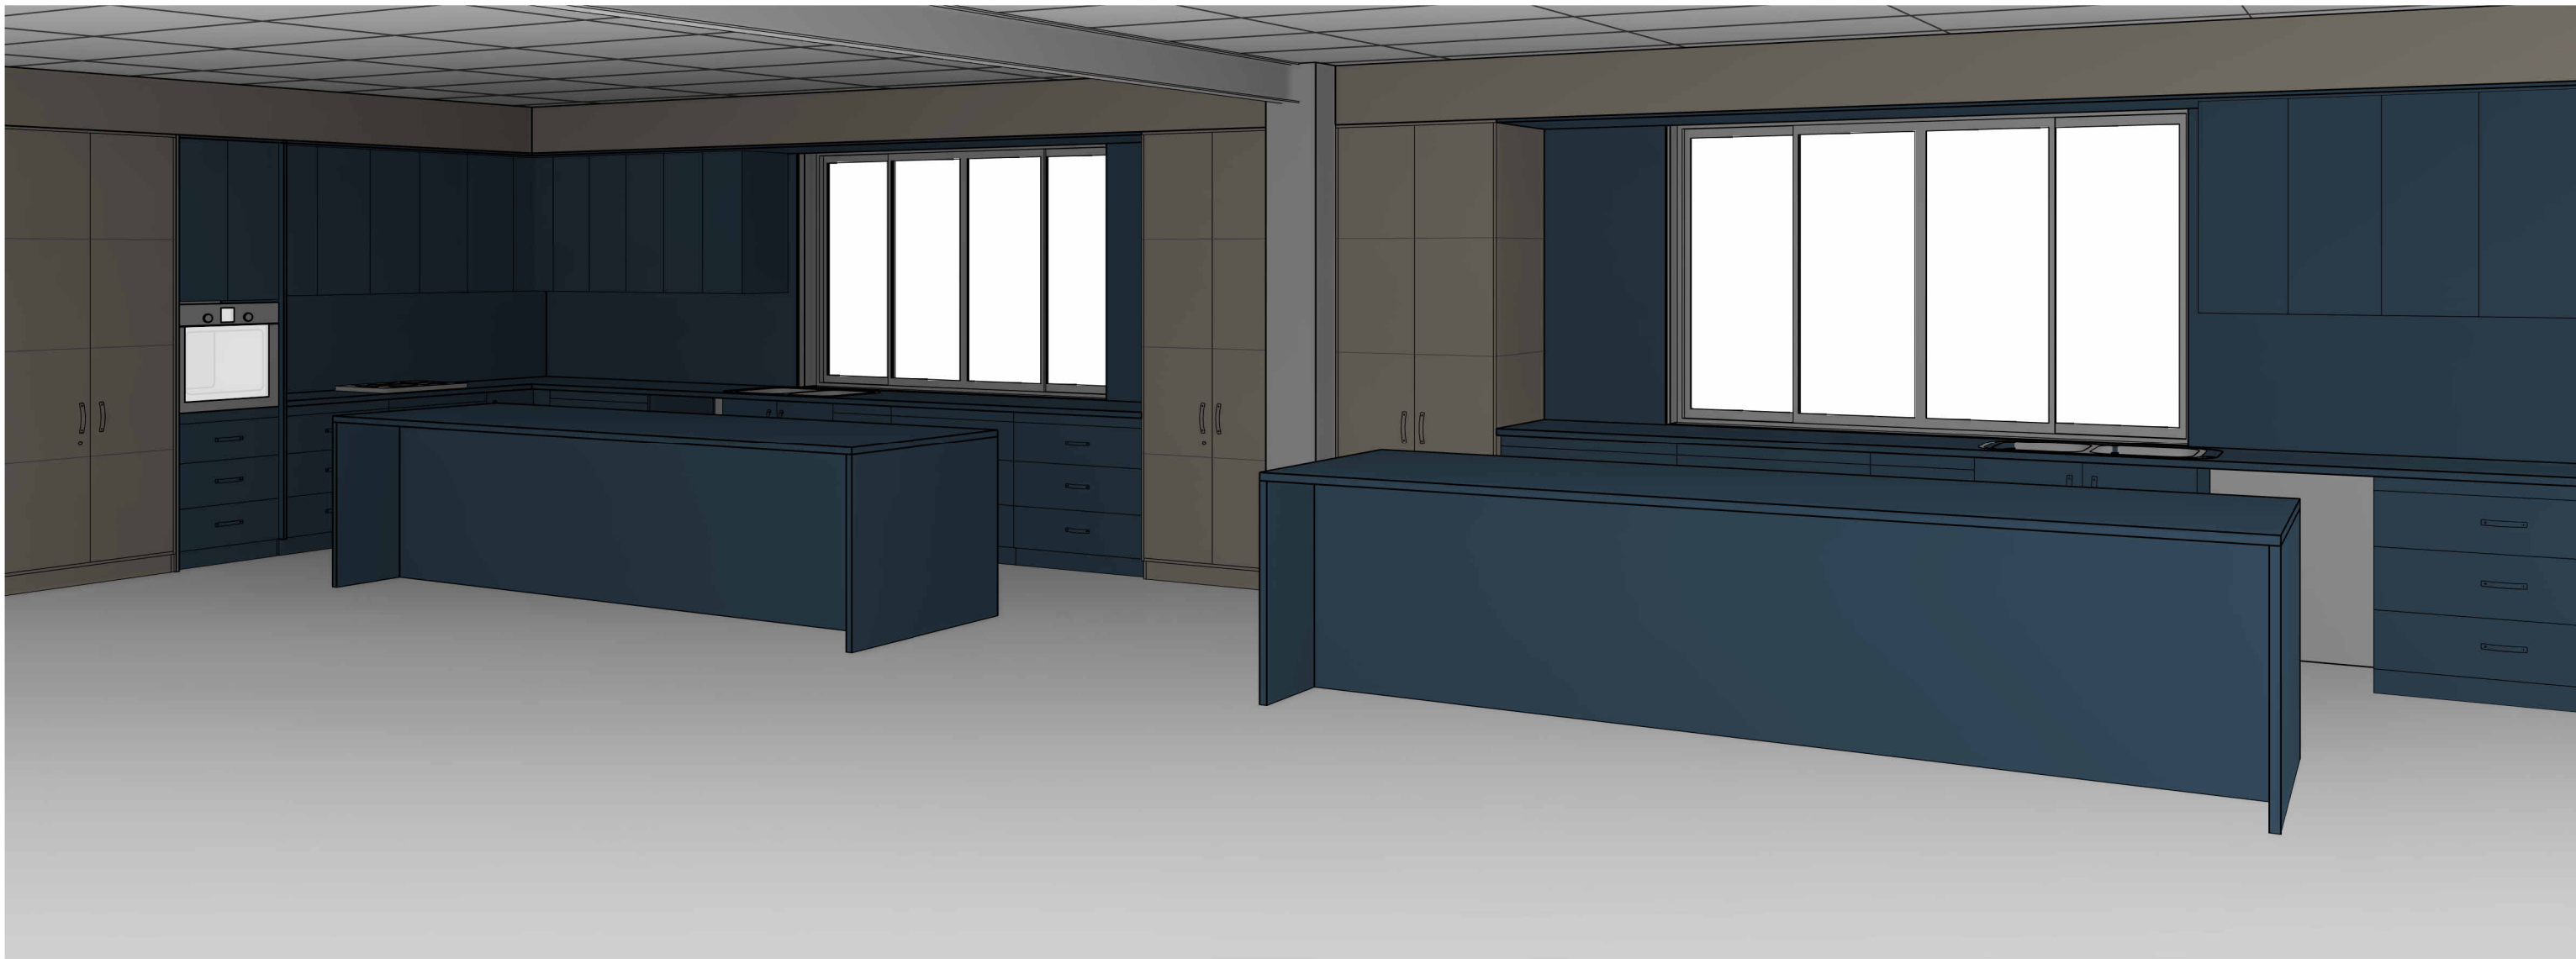

REVISIONS

Rev	Description	Date
T1	TENDER ISSUE	12.03.2026

DO NOT SCALE THIS DRAWINGS

 

TENDER ISSUE



Project Details
OFFICE REFURBS

Address
STANWELL POWER STATION


Drawing Title
INTERNAL DETAILS 2 - LUNCH ROOM



0483 988 655 M
info@designelements.com.au E
QBCC No: 1247120 BDAQ No: 0001677


Scale: 1 : 50 Rev:
Date: MAR 2026 **T1**
Drawn: Author

Project No: Drawing No:
25_003 A4-601

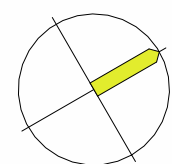


Internal Plan 3 - Amenities

1:50

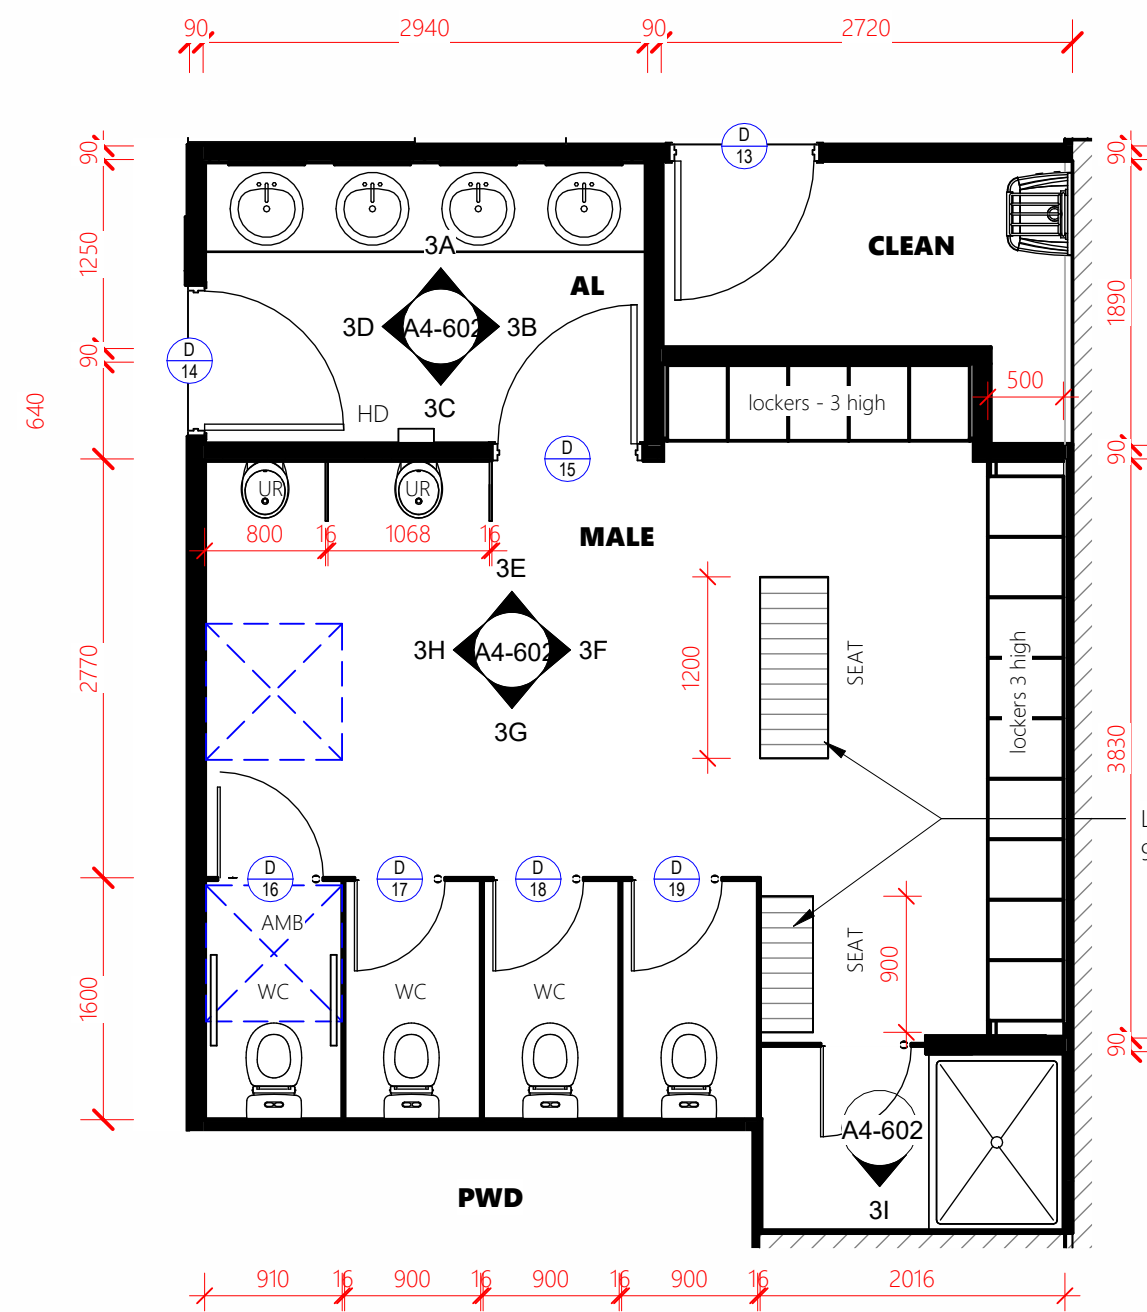


Elevation 3A

1:50

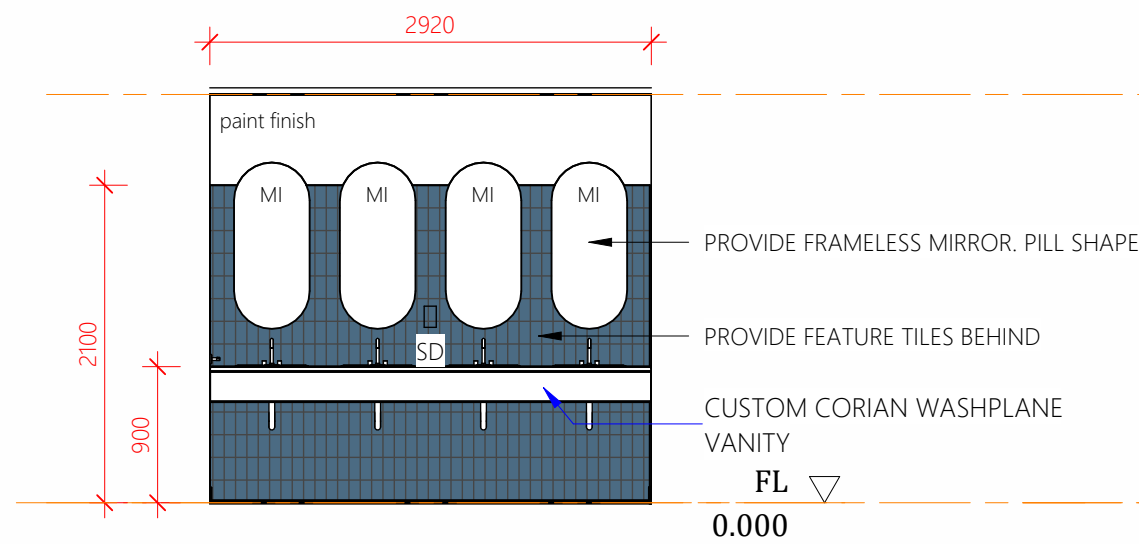


Elevation 3B

1:50

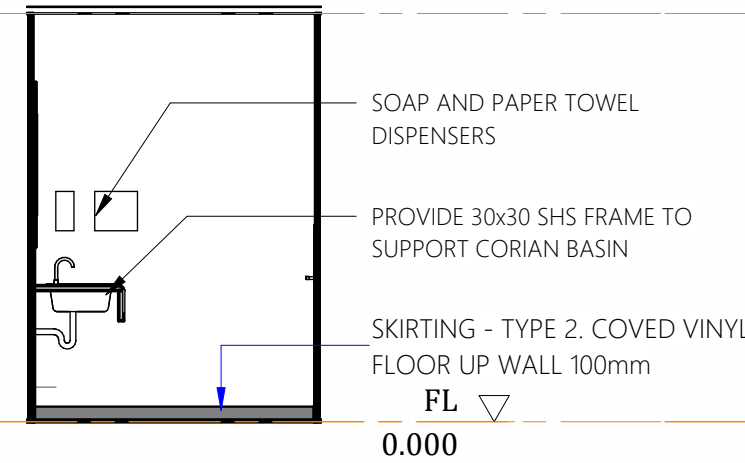


Elevation 3C

1:50

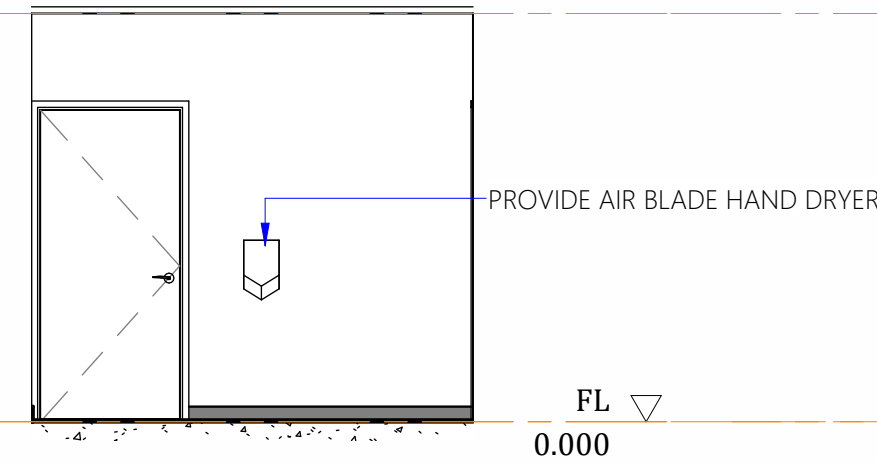


Elevation 3D

1:50

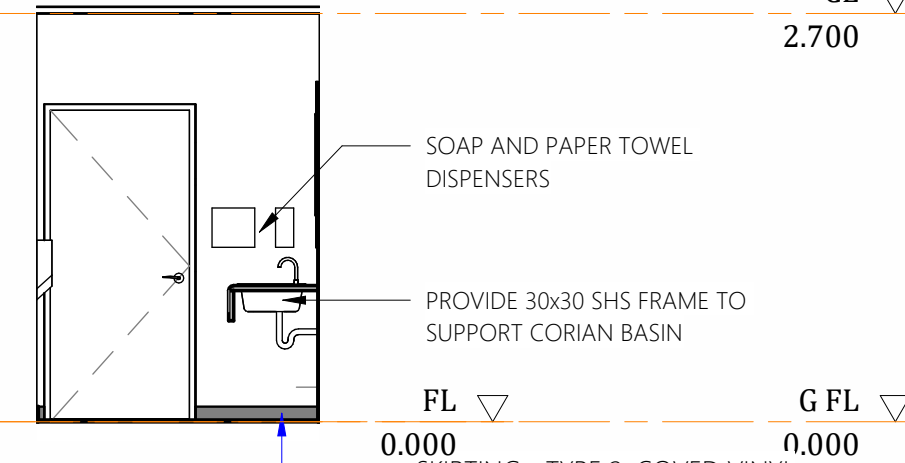


Elevation 3E

1:50

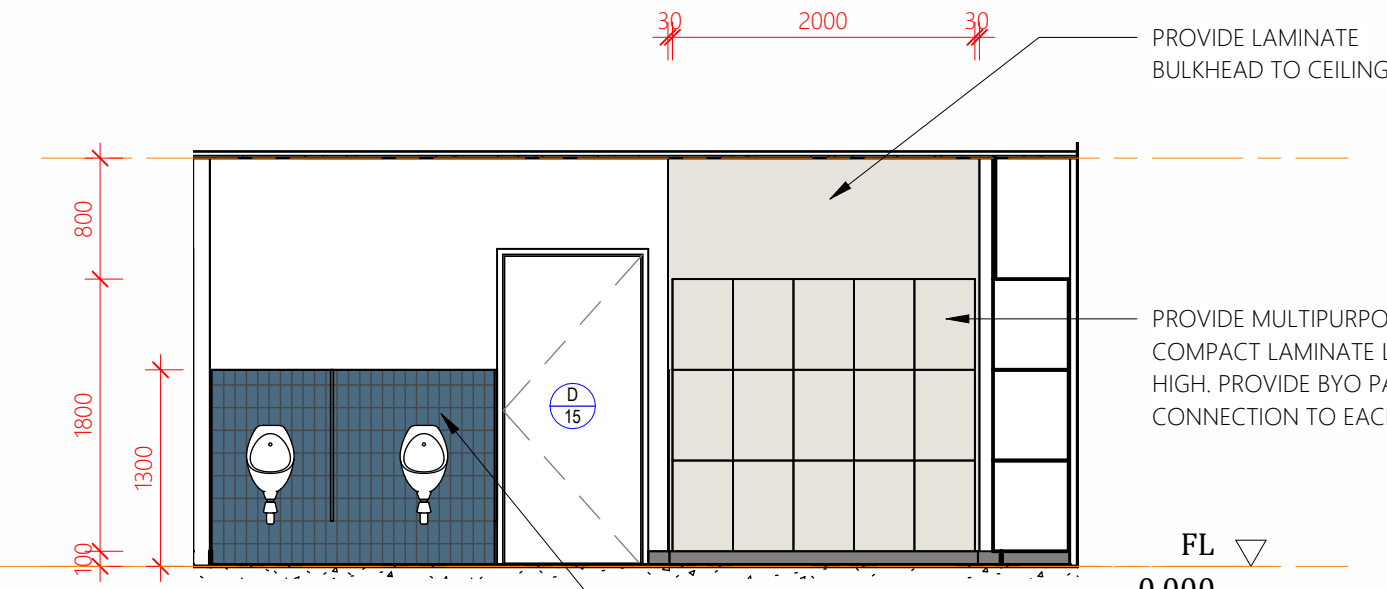


Elevation 3F

1:50

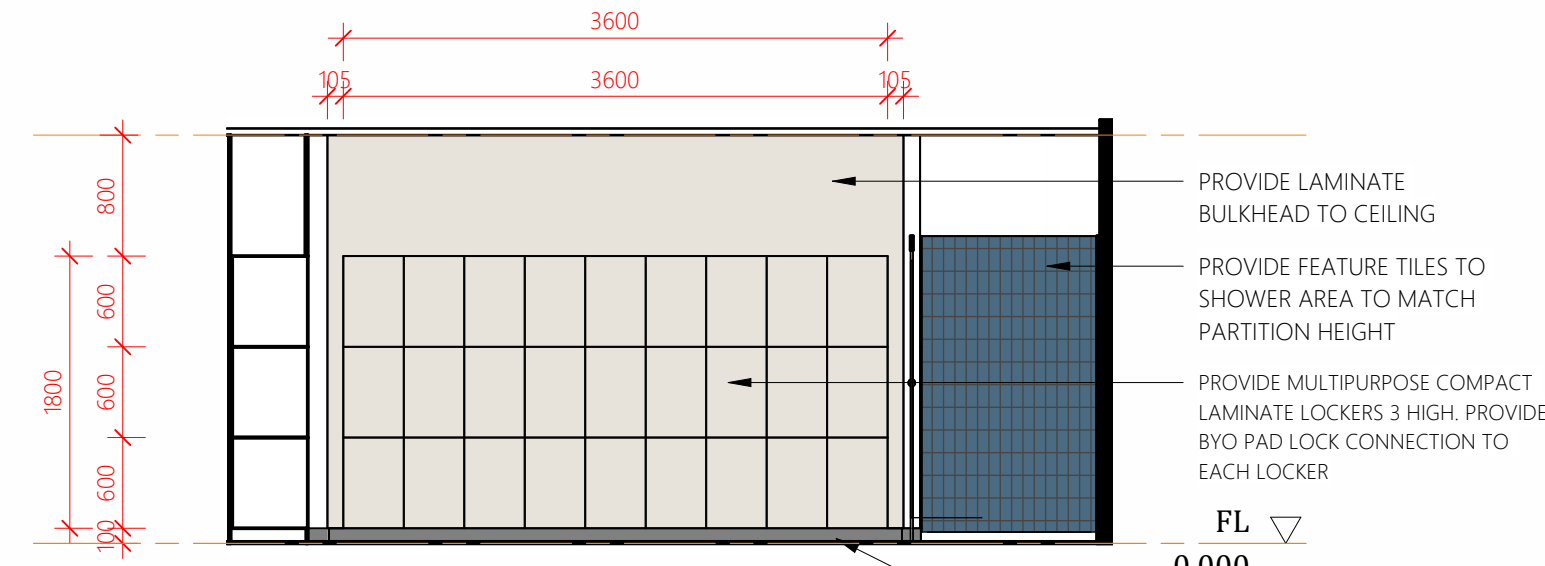


Elevation 3G

1:50

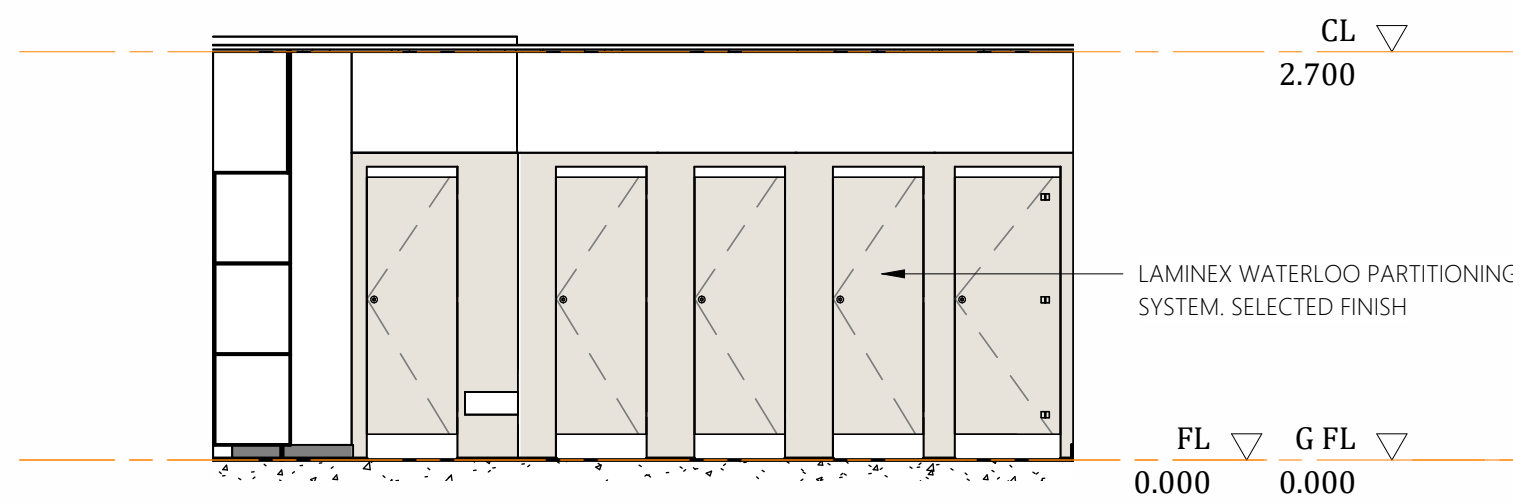


Elevation 3H

1:50

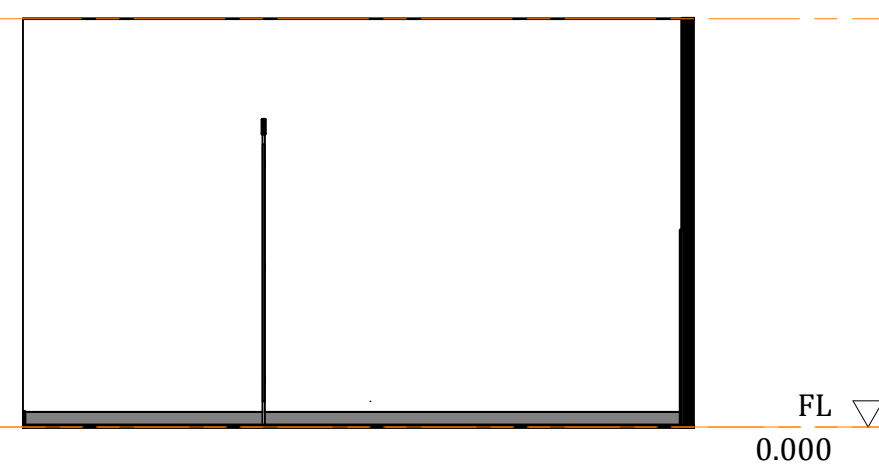

Elevation 3I


1:50

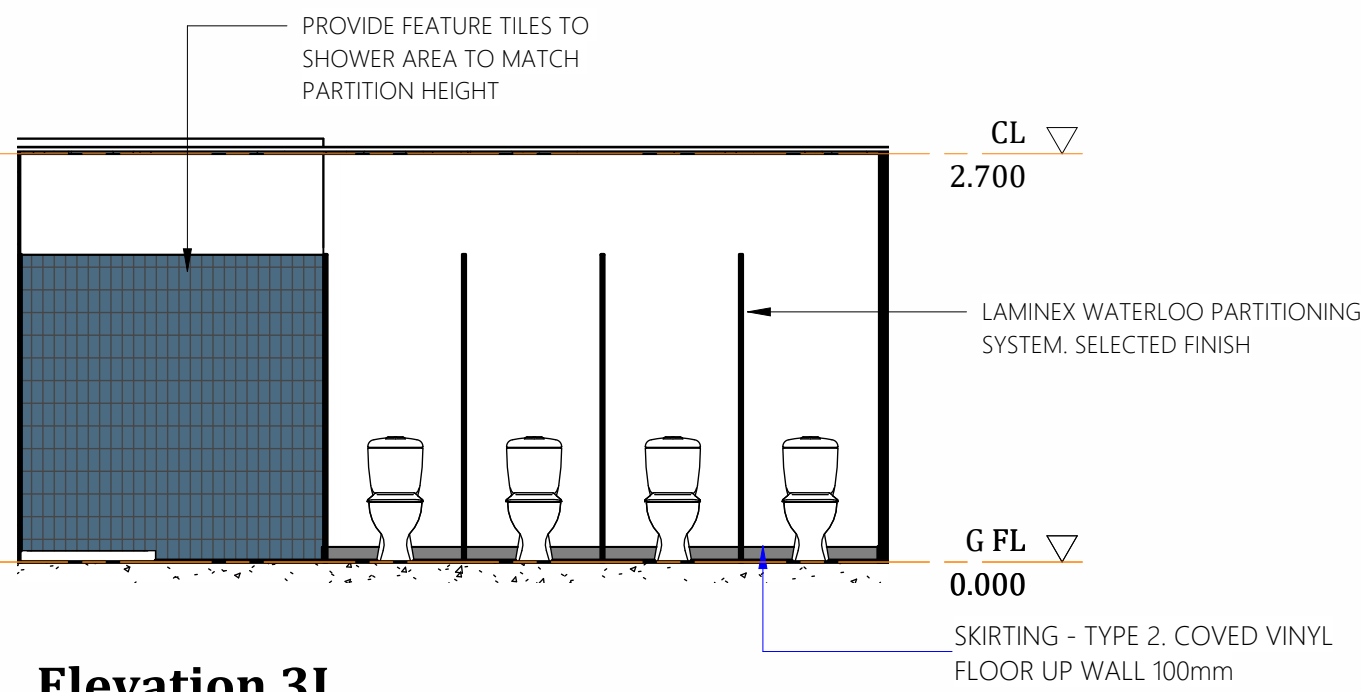

REVISIONS

Rev	Description	Date
T1	TENDER ISSUE	12.03.2026

DO NOT SCALE THIS DRAWINGS

 

TENDER ISSUE



Project Details
OFFICE REFURBS
Address
STANWELL POWER STATION
Drawing Title
INTERNAL DETAILS 3 - MALE AMENITIES



0483 988 655 M
info@designelements.com.au E

QBCC No: 1247120 BDAQ No: 0001677


Scale: 1:50 Rev:


Date: MAR 2026 T1

Drawn: Author

Project No: Drawing No:


25_003 A4-602

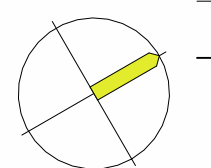

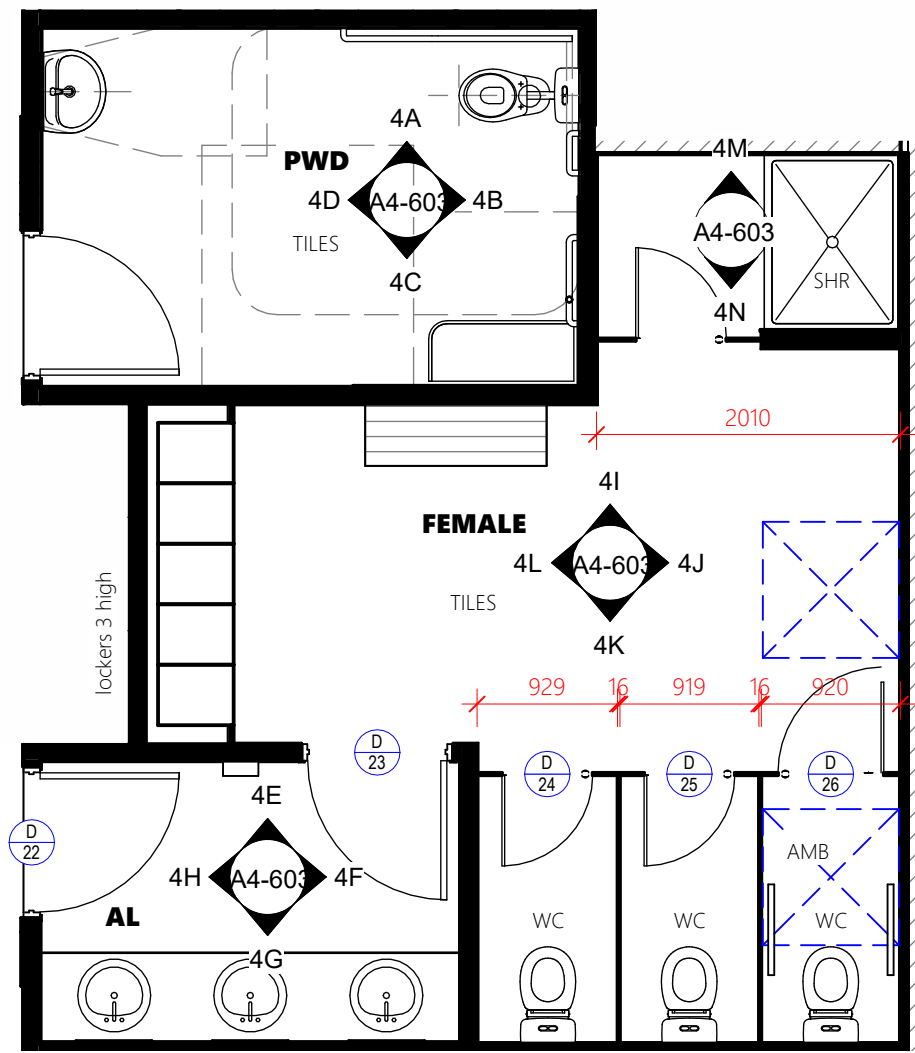

Internal Plan 3 - Amenities

1:50

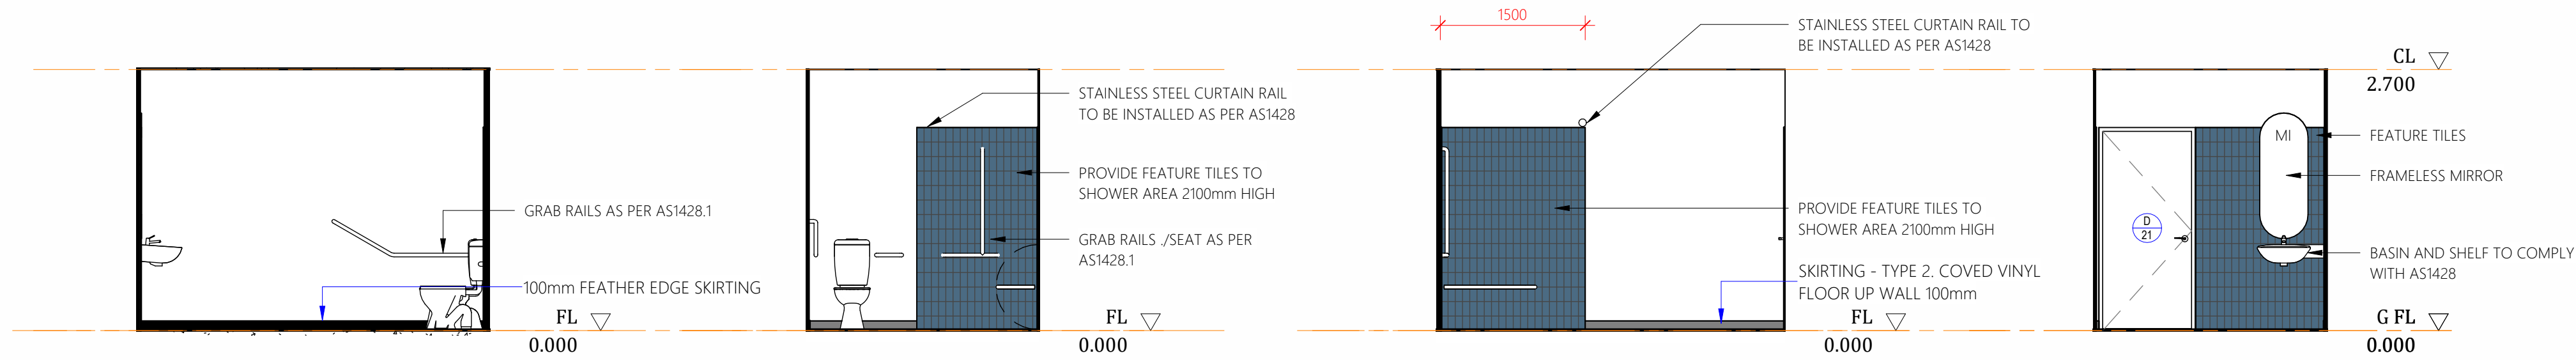

Elevation 4A

1:50

Elevation 4B


1:50

Elevation 4C

1:50

Elevation 4D

1:50

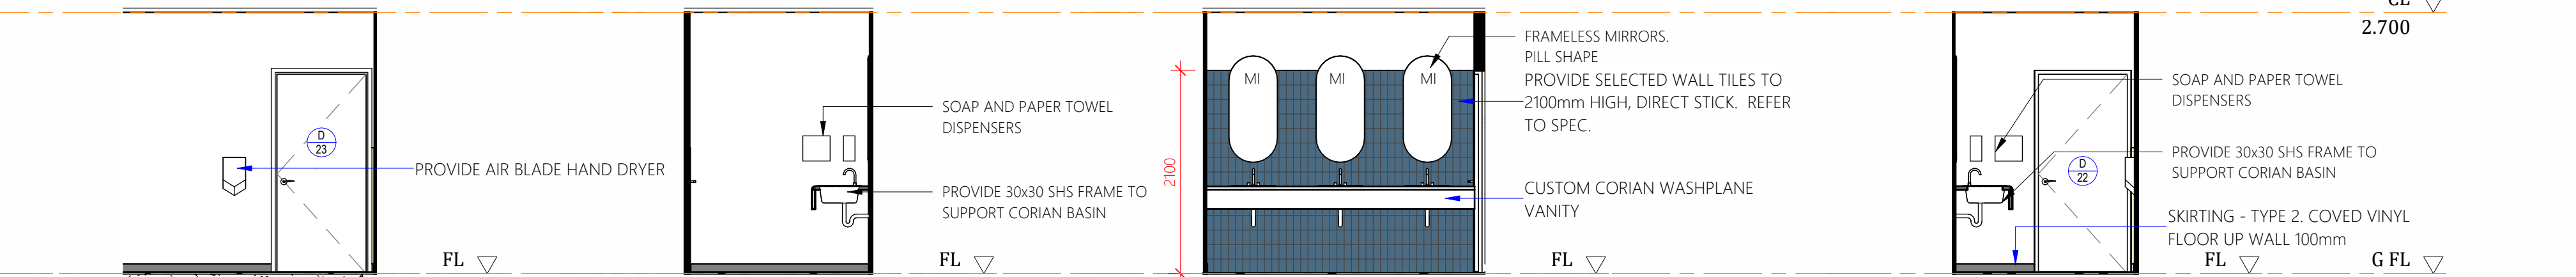

Elevation 4E

1:50

Elevation 4F


1:50

Elevation 4G

1:50

Elevation 4H

1:50

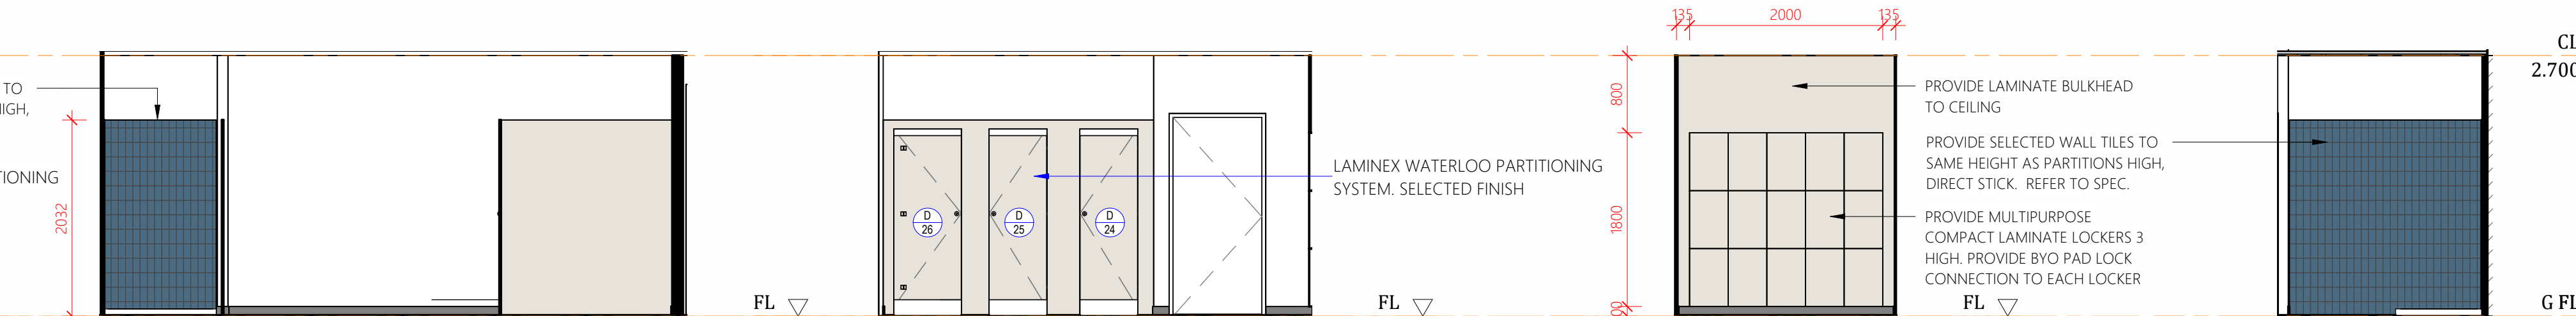

Elevation 4I

1:50

Elevation 4J

1:50

Elevation 4K

1:50

Elevation 4L



1:50

Elevation 4M

1:50

Elevation 4N

1:50

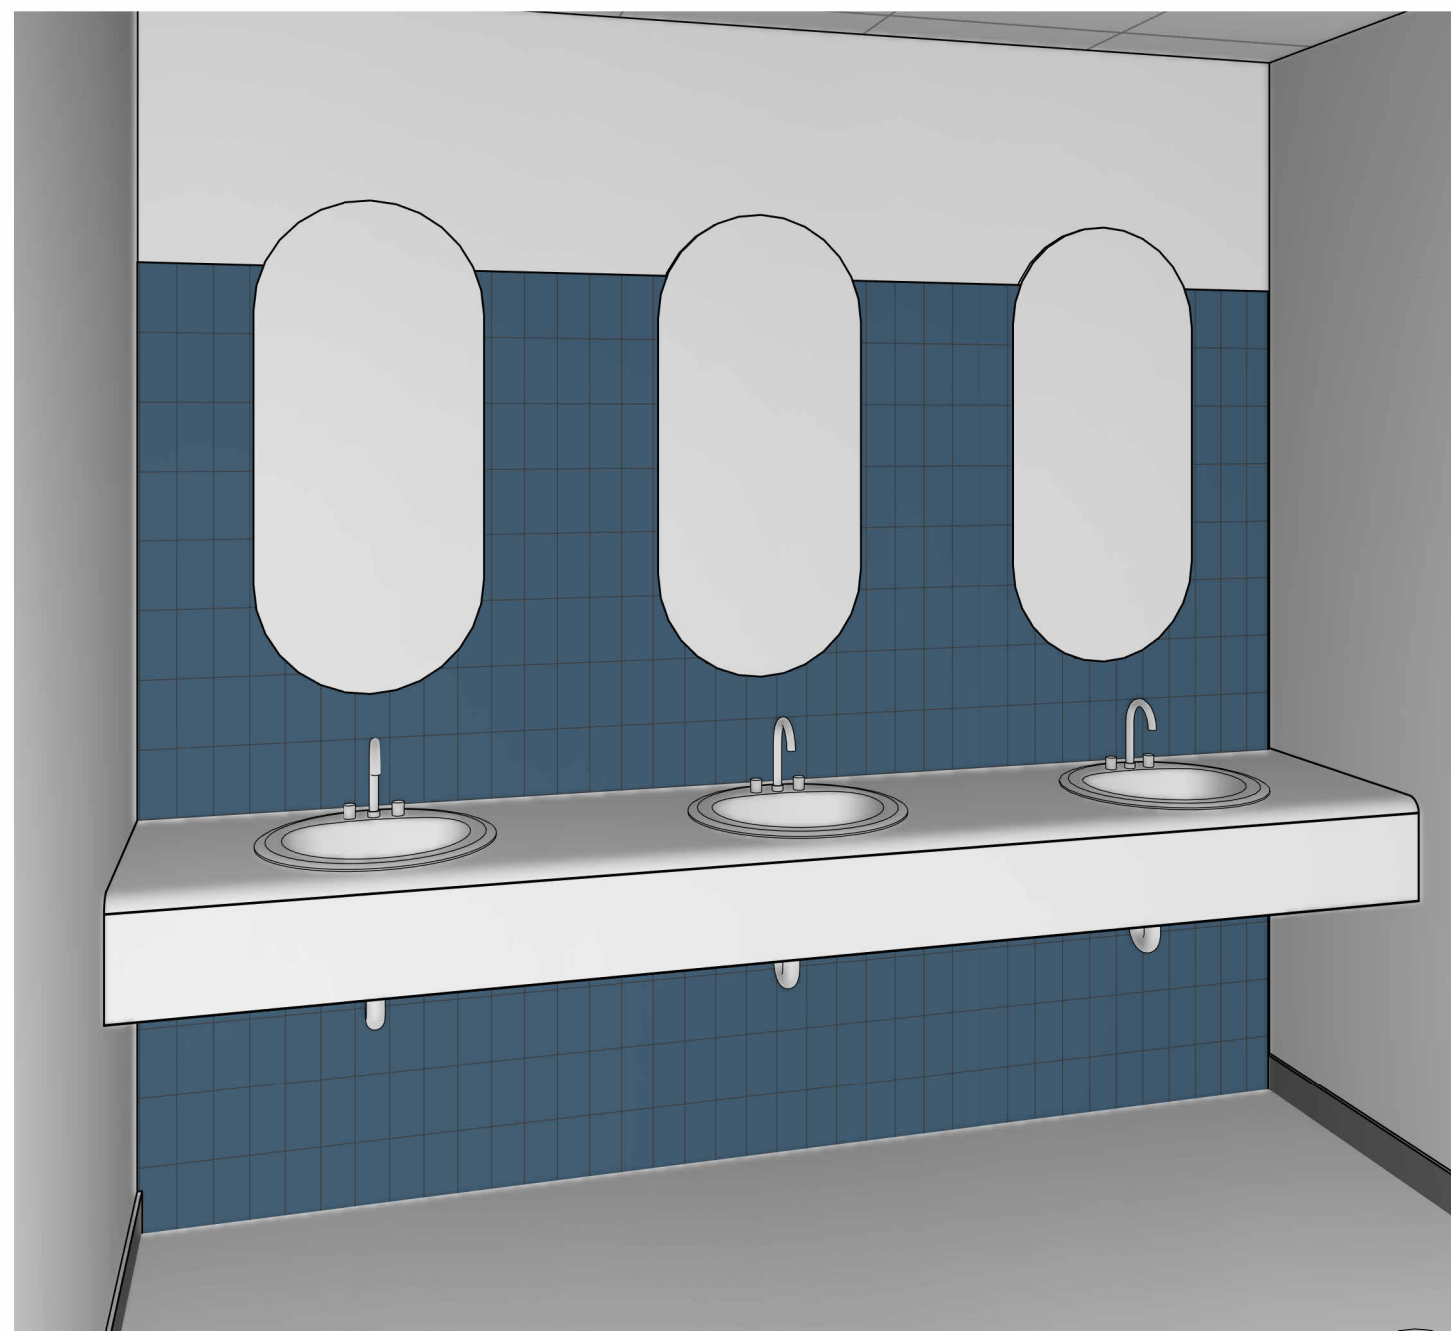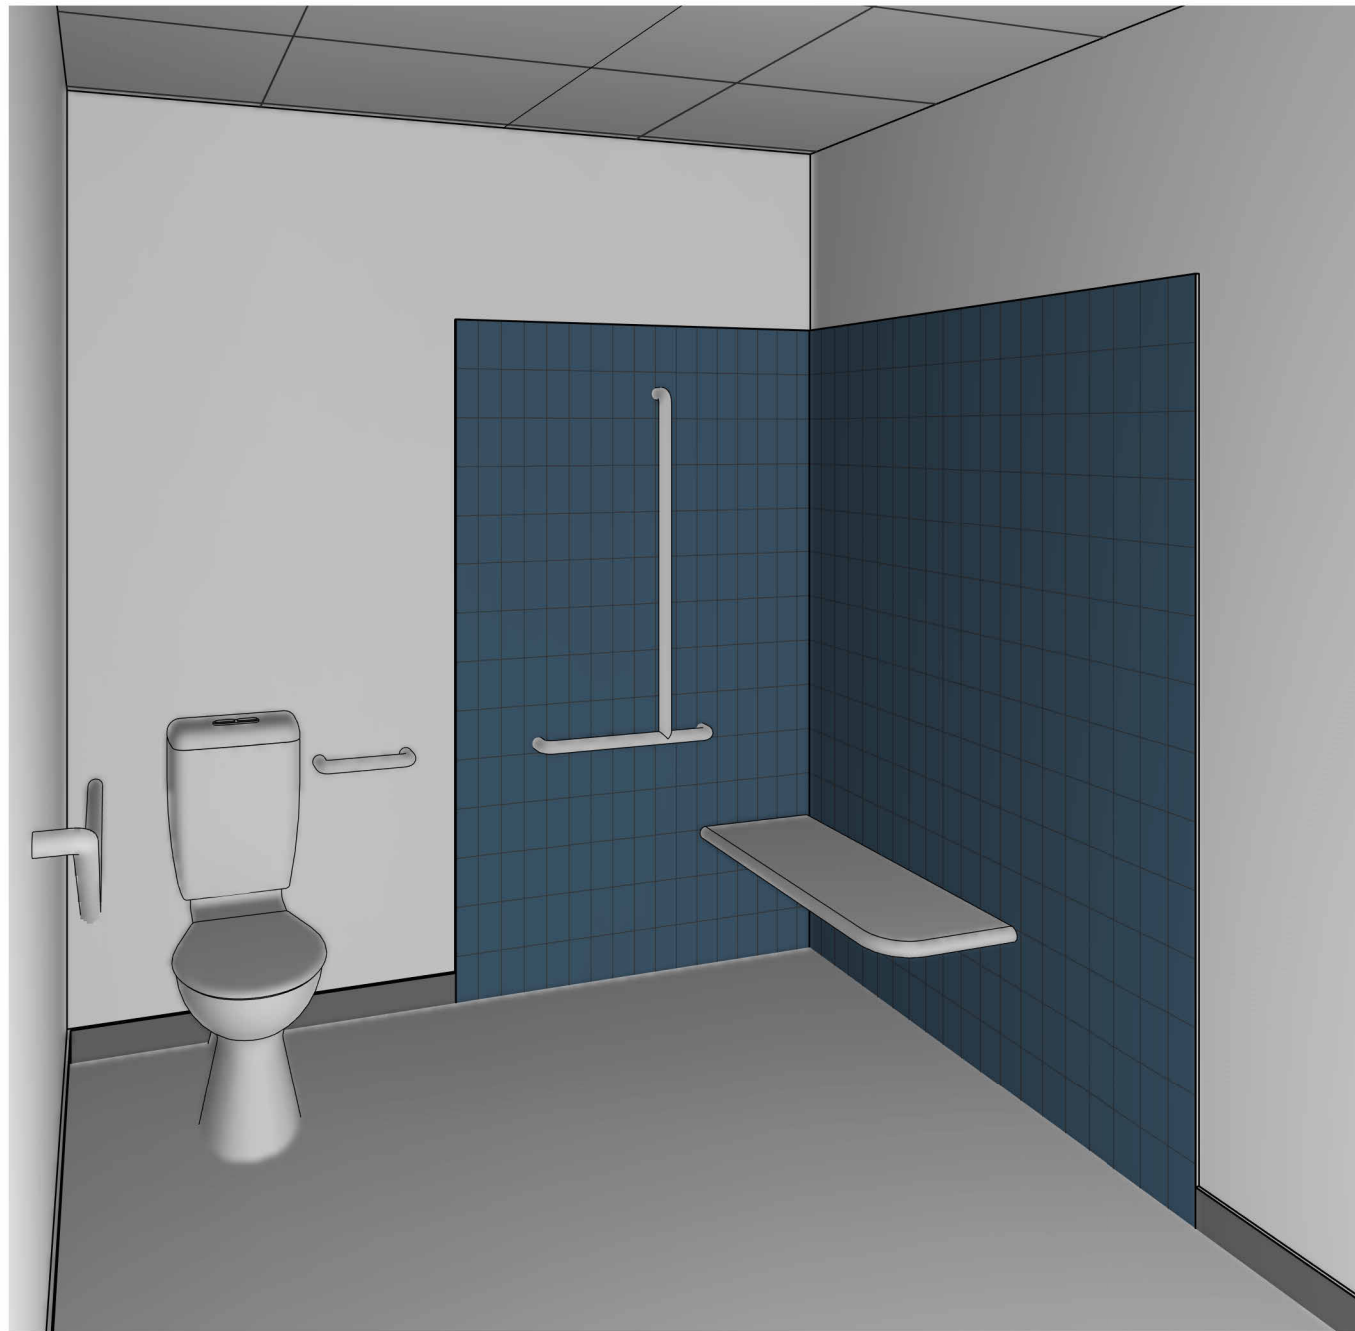

REVISIONS		
Rev	Description	Date
T1	TENDER ISSUE	12.03.2026

DO NOT SCALE THIS DRAWINGS



TENDER ISSUE



Project Details	
OFFICE REFURBS	
Address	
STANWELL POWER STATION	
Drawing Title	
INTERNAL DETAILS 3 - FEMALE AMENITIES	

dezinelements
BUILDING DESIGNERS


0483 988 655 **M**
info@dezi nelements.com.au **E**

QBCC No: 1247120 BDAQ No: 0001677

Scale: 1:50 Rev: **T1**
Date: MAR 2026
Drawn: Author


Project No: Drawing No:
25_003 A4-603

12/03/2026 7:56:00 PM

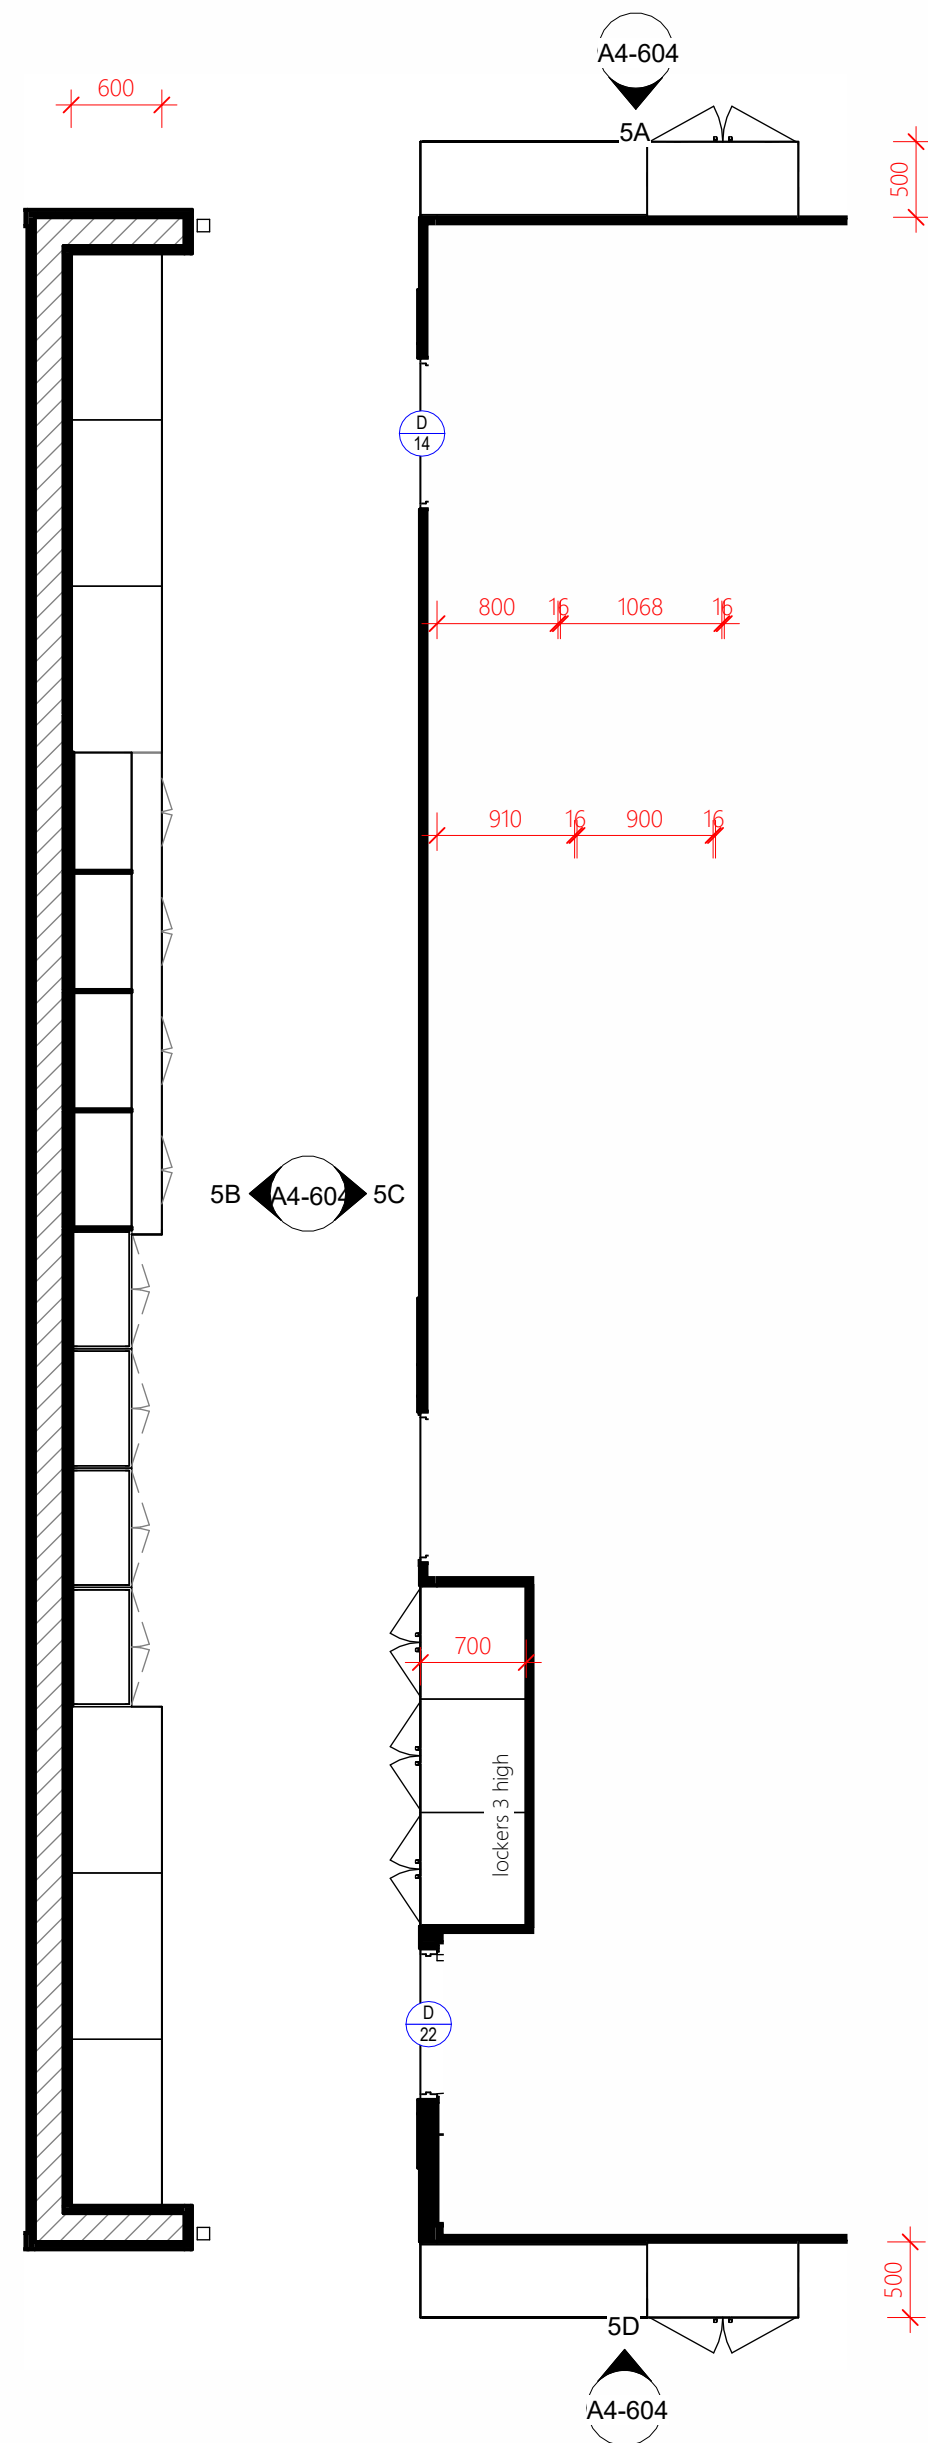

Internal Plan 5 - Central Corridor

1:50

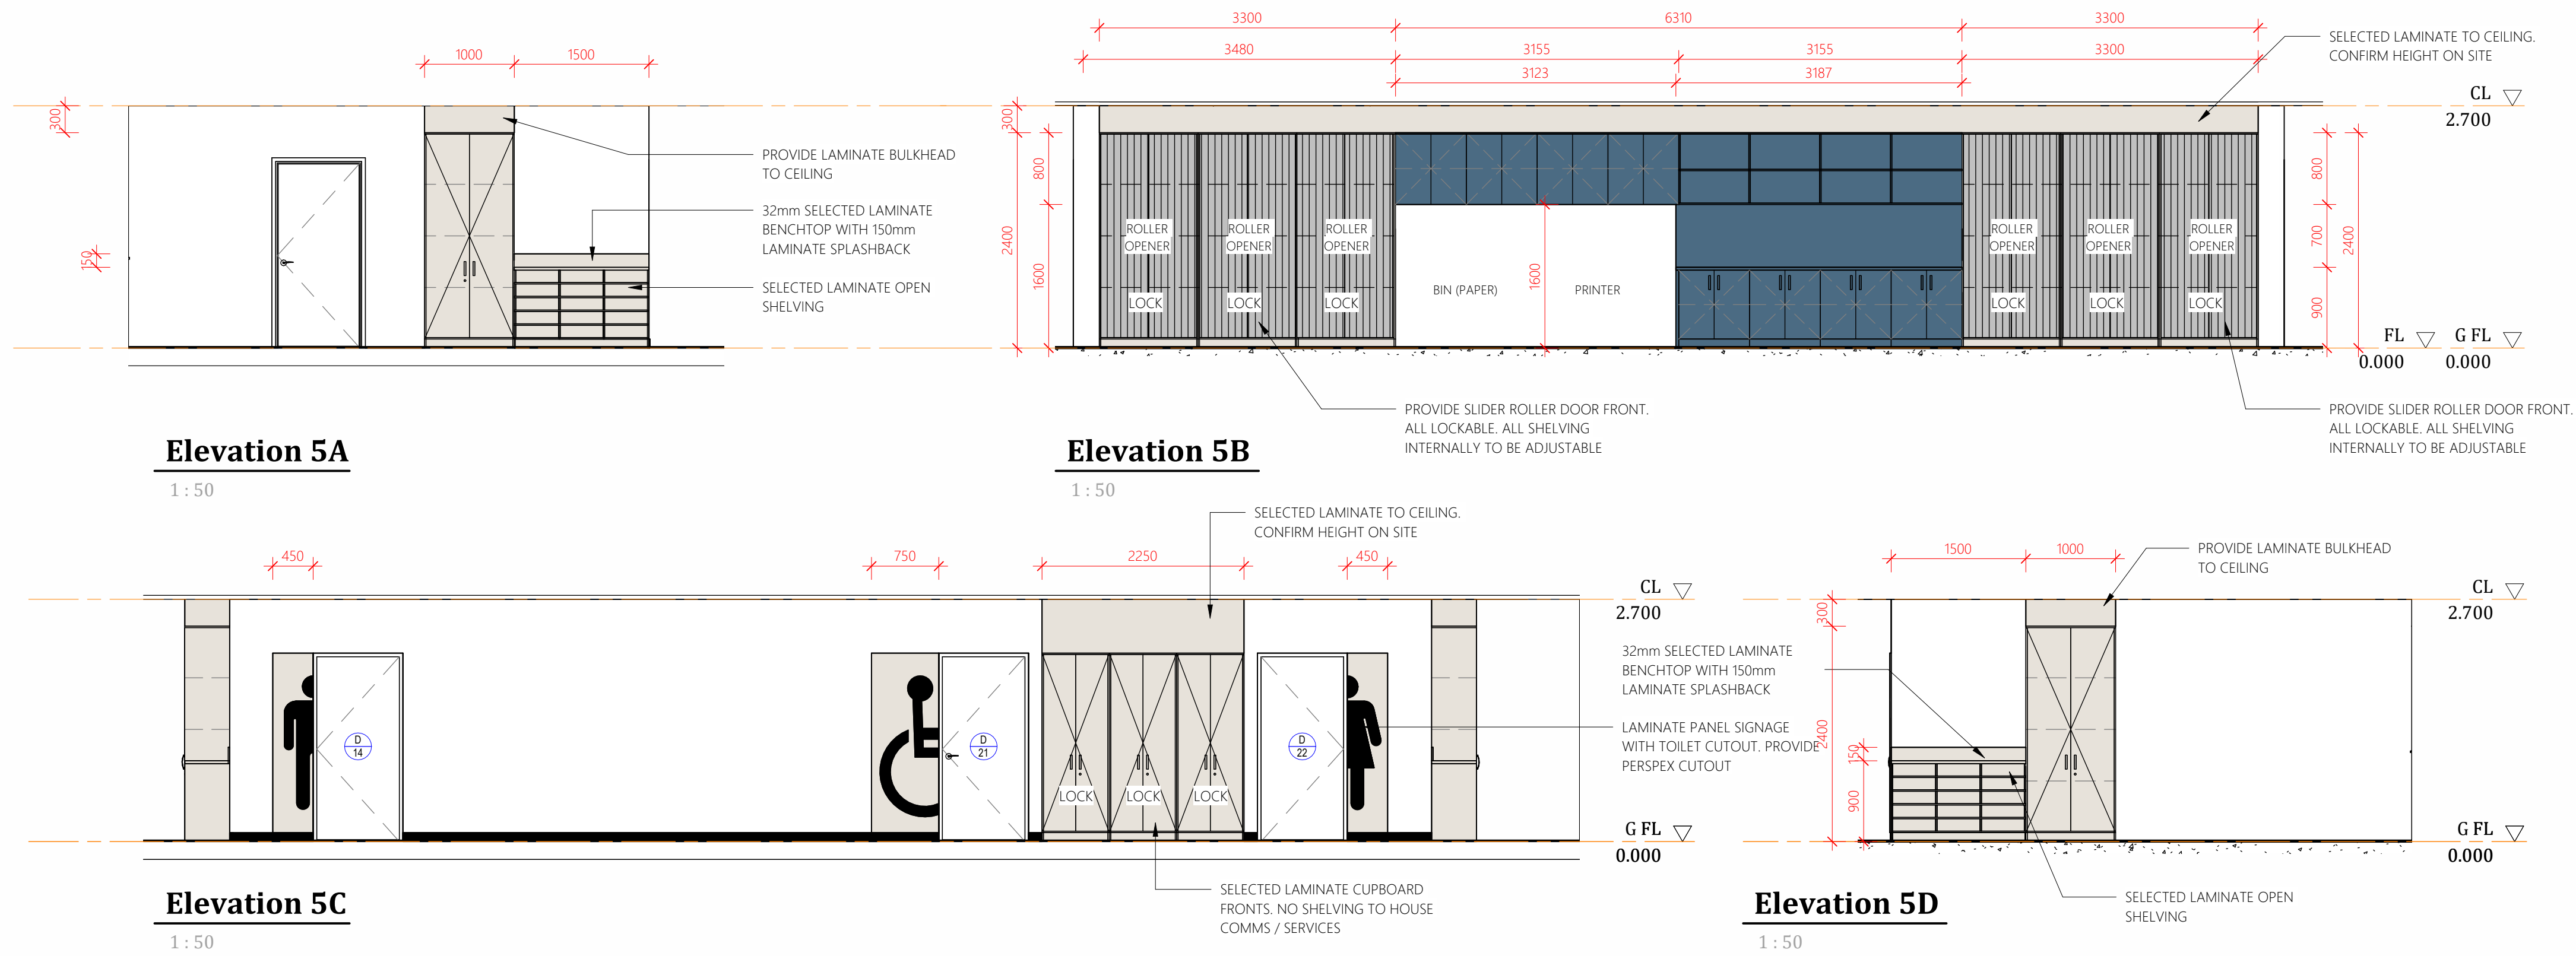

REVISIONS

Rev	Description	Date
T1	TENDER ISSUE	12.03.2026

DO NOT SCALE THIS DRAWINGS



TENDER ISSUE




Project Details
OFFICE REFURBS
Address
STANWELL POWER STATION
Drawing Title
INTERNAL DETAILS 5 - CENTRAL CORRIDOR


dezinelements
BUILDING DESIGNERS

0483 988 655 **M**
info@dezi nelements.com.au **E**
QBCC No: 1247120 BDAQ No: 0001677

Scale: 1:50 Rev: **T1**
Date: MAR 2026
Drawn: Author
Project No: Drawing No:
25_003 A4-604

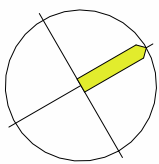


DOOR SCHEDULE	
DOOR NO.	DOOR TYPE
01	TYPE A
02	TYPE A
03	TYPE A
04	TYPE A
05	TYPE B
06	TYPE A
07	TYPE A
08	TYPE B
09	TYPE D
10	TYPE D
11	TYPE C
12	TYPE C
13	TYPE F
14	TYPE G
15	TYPE G
16	TYPE J
17	TYPE K
18	TYPE K
19	TYPE K
20	TYPE K
21	TYPE H
22	TYPE G
23	TYPE G
24	TYPE K
25	TYPE K
26	TYPE J
27	TYPE K
28	TYPE E
29	TYPE D

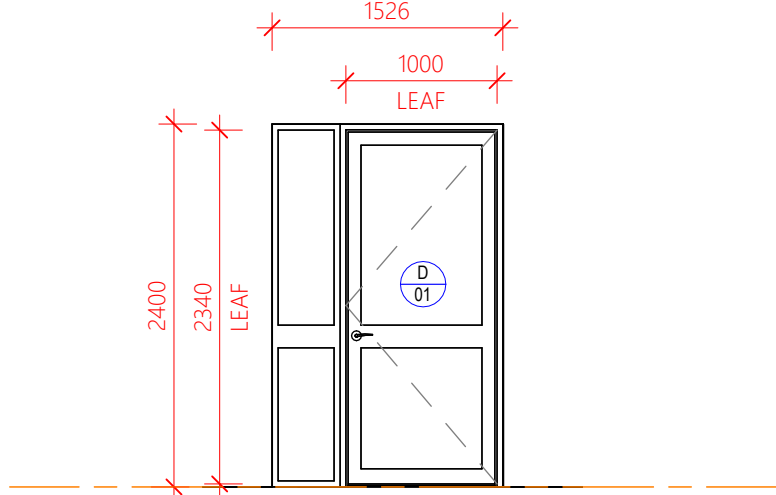


DOOR TYPE A

LOCATION: EXTERNAL
DOOR TYPE: HINGED ALUMINIUM FRAMED SINGLE DOOR
FRAME TYPE: G.JAMES 475 SERIES
FRAME FINISH: SELECTED POWDERCOAT
DOOR FINISH: SELECTED POWDERCOAT
INFILL: GREY SAFETY GLASS
THRESHOLD:
SEALS:
LOCK: VESTIBULE LOCK
HARDWARE: DOOR CLOSER, DOOR STOP

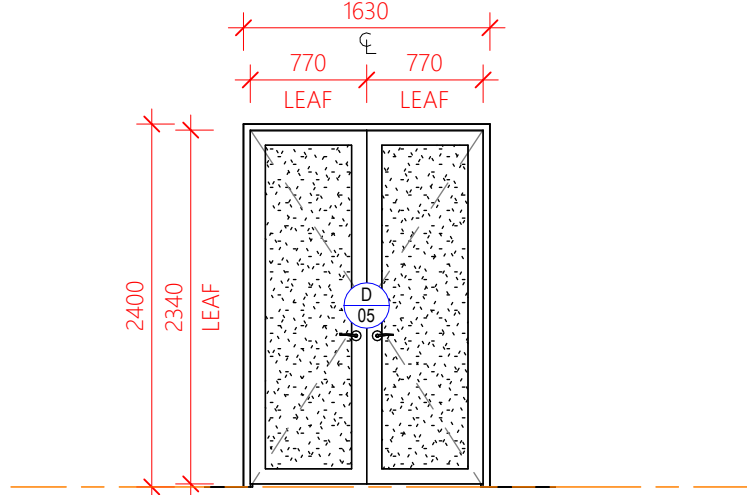


DOOR TYPE B

LOCATION: EXTERNAL, MECH STORES
DOOR TYPE: HINGED ALUMINIUM FRAMED DOUBLE DOOR
FRAME TYPE: G.JAMES 475 SERIES
FRAME FINISH: SELECTED POWDERCOAT
DOOR FINISH: SELECTED POWDERCOAT
INFILL: 9mm CFC, PAINT FINISH
THRESHOLD:
SEALS:
LOCK: VESTIBULE LOCK
HARDWARE:

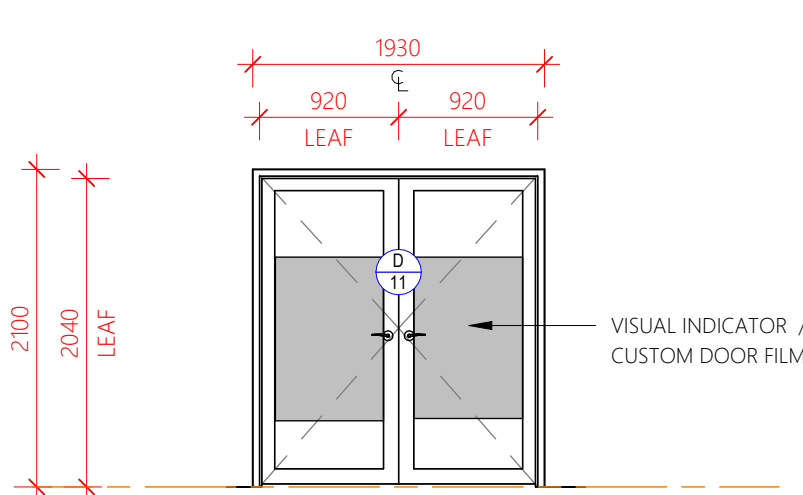


DOOR TYPE C

LOCATION: INTERNAL, LUNCH ROOM
DOOR TYPE: HINGED ALUMINIUM FRAMED DOUBLE DOOR
FRAME TYPE: G.JAMES 475 SERIES
FRAME FINISH: SELECTED POWDERCOAT
DOOR FINISH: SELECTED POWDERCOAT
INFILL: CLEAR SAFETY GLASS
THRESHOLD:
SEALS:
LOCK: VESTIBULE LOCK
HARDWARE:

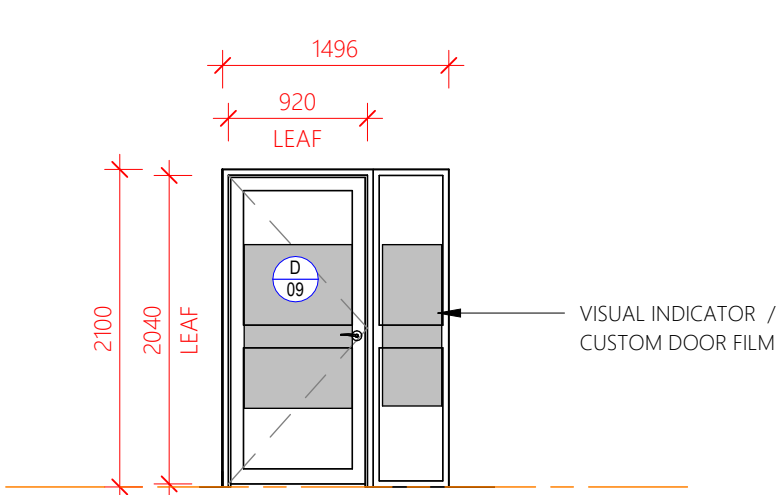


DOOR TYPE D

LOCATION: INTERNAL, MEETING ROOMS
DOOR TYPE: HINGED ALUMINIUM FRAMED SINGLE DOOR
FRAME TYPE: G.JAMES 475 SERIES
FRAME FINISH: SELECTED POWDERCOAT
DOOR FINISH: SELECTED POWDERCOAT
INFILL: GREY SAFETY GLASS
THRESHOLD:
SEALS:
LOCK: VESTIBULE LOCK
HARDWARE: DOOR CLOSER, DOOR STOP

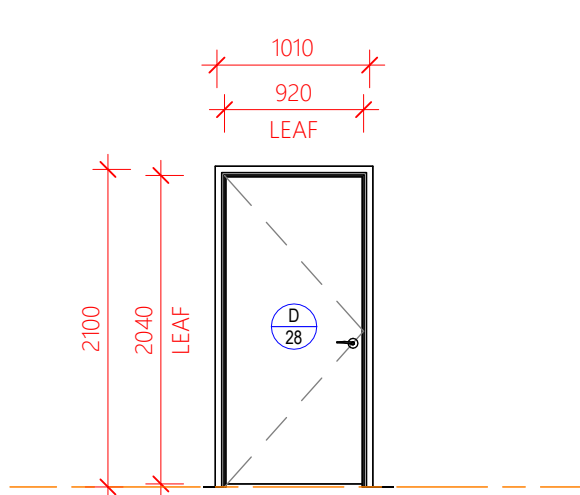


DOOR TYPE E

LOCATION: INTERNAL
DOOR TYPE: 40mm HINGED SOLID CORE SINGLE DOOR
FRAME TYPE: TIMBER
FRAME FINISH: PAINT
DOOR FINISH: PAINT
SEALS: NONE
LOCK: VESTIBULE LOCK
HARDWARE: DOOR CLOSER, DOOR STOP

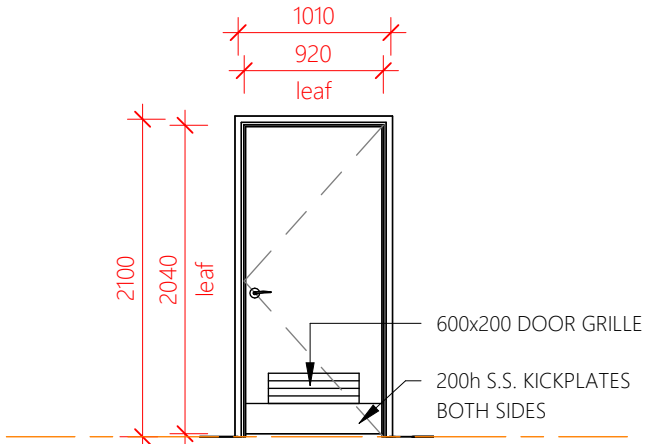


DOOR TYPE F

LOCATION: CLEANER
DOOR TYPE: 40mm HINGED SOLID CORE SINGLE DOOR
FRAME TYPE: TIMBER
FRAME FINISH: PAINT
DOOR FINISH: PAINT
SEALS: NONE
LOCK: VESTIBULE LOCK
HARDWARE: KICK PLATES, DOOR CLOSER, DOOR STOP

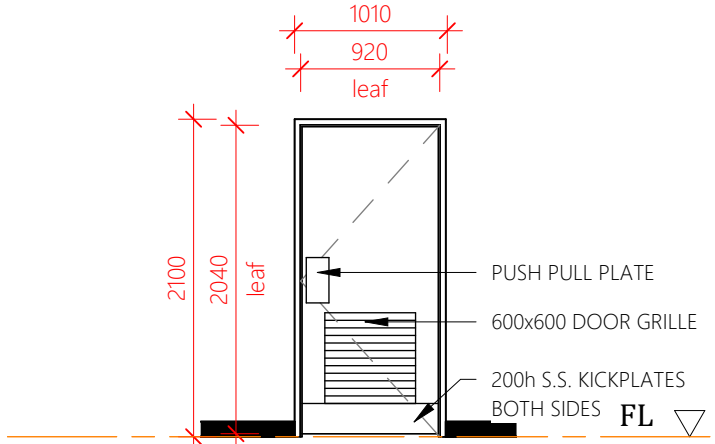


DOOR TYPE G

LOCATION: MALE & FEMALE AMENITIES
DOOR TYPE: 40mm HINGED SOLID CORE SINGLE DOOR
FRAME TYPE: TIMBER
FRAME FINISH: PAINT
DOOR FINISH: PAINT
SEALS: NONE
LOCK: PUSH PULL PLATES (NO LOCKING)
HARDWARE: KICK PLATES, DOOR CLOSER, DOOR STOP

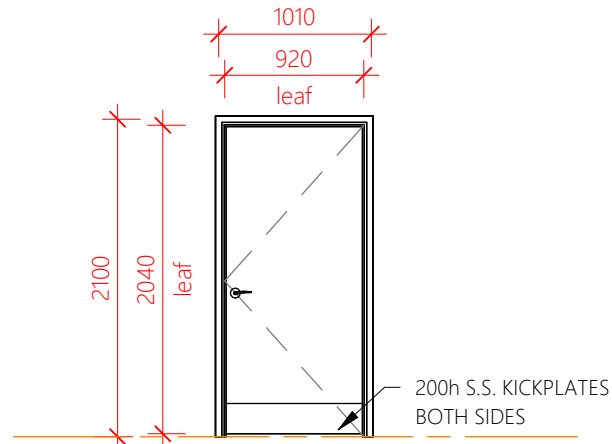


DOOR TYPE H

LOCATION: PWD
DOOR TYPE: 40mm HINGED SOLID CORE SINGLE DOOR
FRAME TYPE: TIMBER
FRAME FINISH: PAINT
DOOR FINISH: PAINT
SEALS: NONE
LOCK: PRIVACY LATCH LEVER HANDLE WITH INDICATOR BOLT
HARDWARE: KICK PLATES, DOOR CLOSER, DOOR STOP

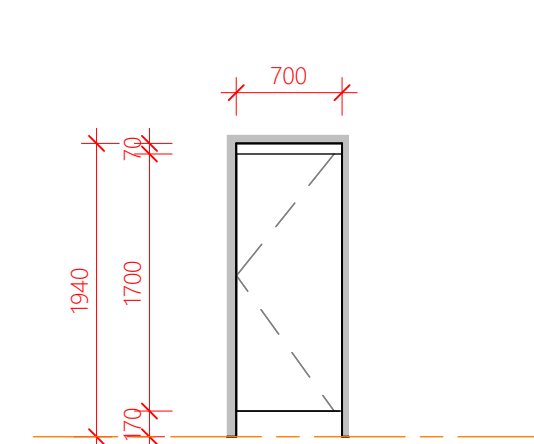


DOOR TYPE J

LOCATION: AMENITIES AMB WC
DOOR TYPE: 13mm COMPACT LAMINATE PARTITION DOOR
FRAME TYPE: PROVIDE 30° PRIVACY BEVEL
DOOR FINISH: SELECTED LAMINATE
SEALS: NONE
LOCK: METLAM XCEL SLIDE LOCK & INDICATOR.
HARDWARE:

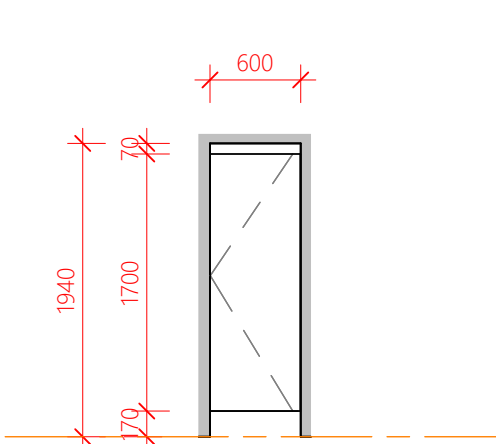


DOOR TYPE K

LOCATION: AMENITIES
DOOR TYPE: 13mm COMPACT LAMINATE PARTITION DOOR
FRAME TYPE: PROVIDE 30° PRIVACY BEVEL
DOOR FINISH: SELECTED LAMINATE
SEALS: NONE
LOCK: METLAM XCEL SLIDE LOCK & INDICATOR.
HARDWARE:

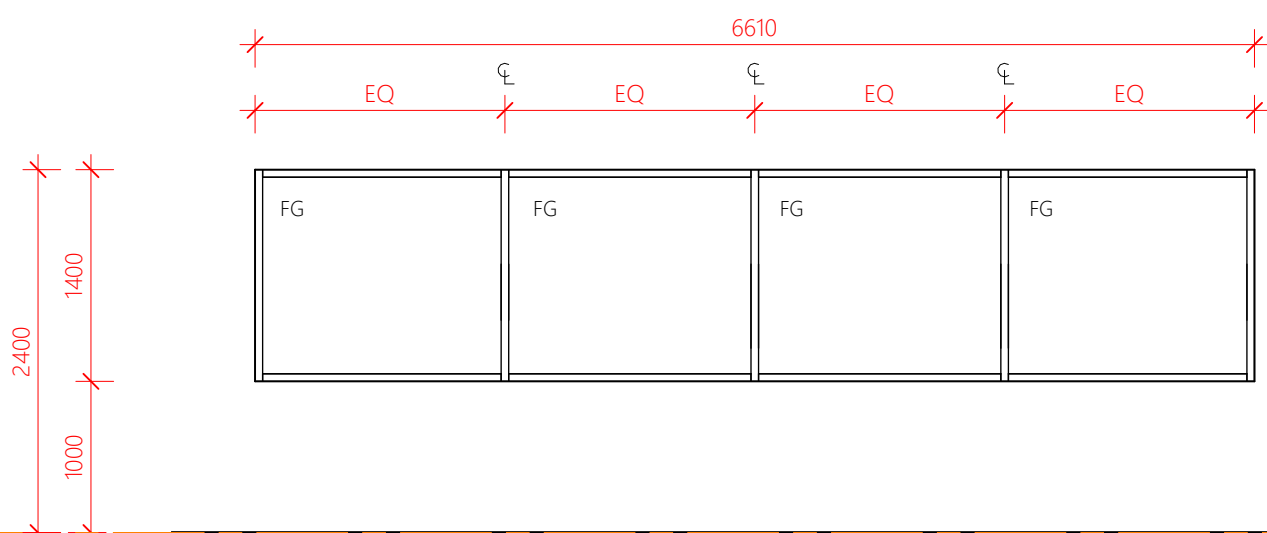


WINDOW TYPE A

LOCATION: EXTERNAL
FRAME TYPE: G.JAMES 475 SERIES
FRAME FINISH: SELECTED POWDERCOAT
WINDOW: FIXED GLASS
GLASS: SAFETY GLASS

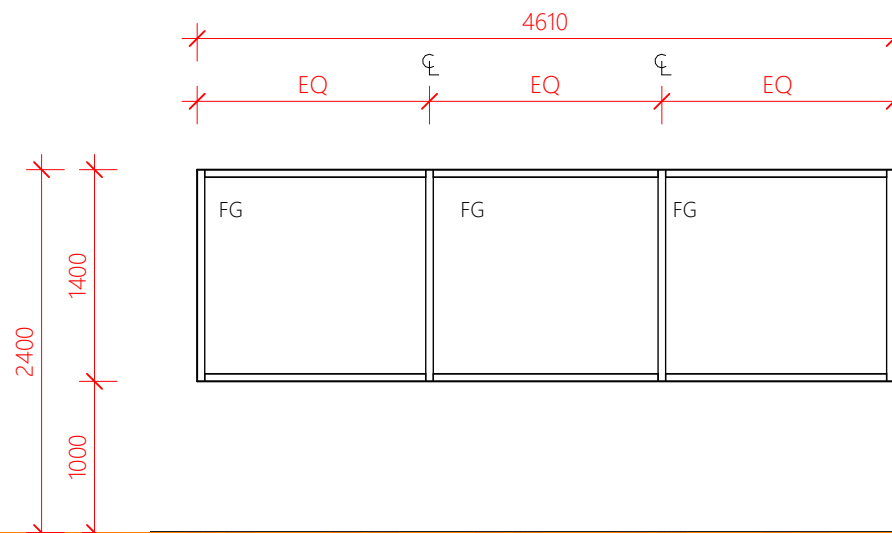


WINDOW TYPE B

LOCATION: EXTERNAL
FRAME TYPE: G.JAMES 475 SERIES
FRAME FINISH: SELECTED POWDERCOAT
WINDOW: FIXED GLASS
GLASS: SAFETY GLASS

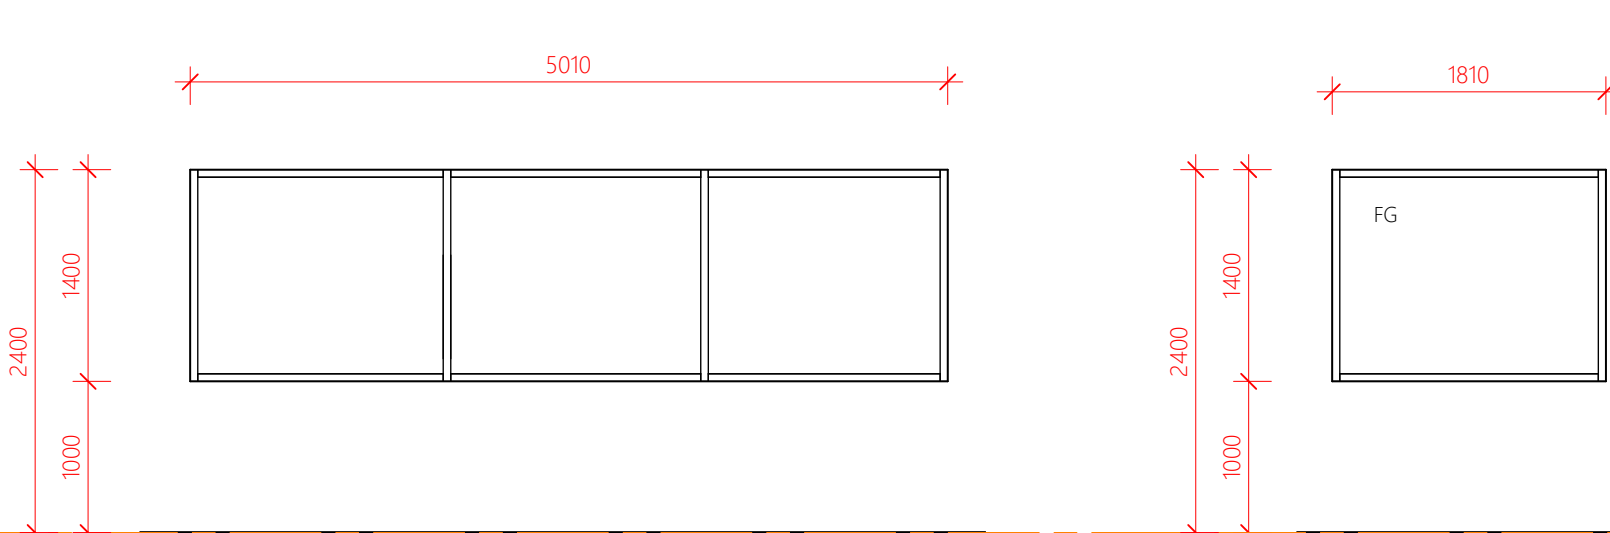


WINDOW TYPE C

LOCATION: EXTERNAL
FRAME TYPE: G.JAMES 475 SERIES
FRAME FINISH: SELECTED POWDERCOAT
WINDOW: FIXED GLASS
GLASS: SAFETY GLASS

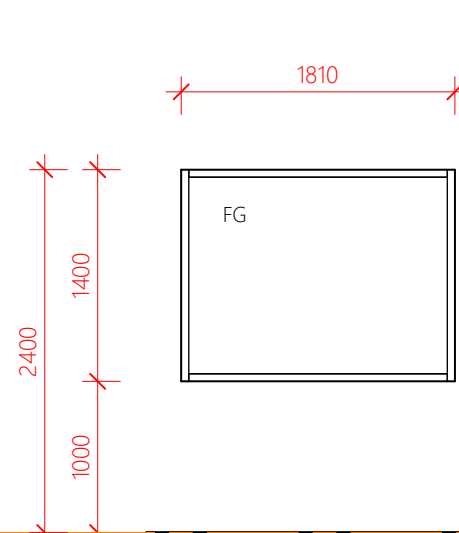

WINDOW TYPE D


LOCATION: EXTERNAL
FRAME TYPE: G.JAMES 475 SERIES
FRAME FINISH: SELECTED POWDERCOAT
WINDOW: FIXED GLASS
GLASS: SAFETY GLASS

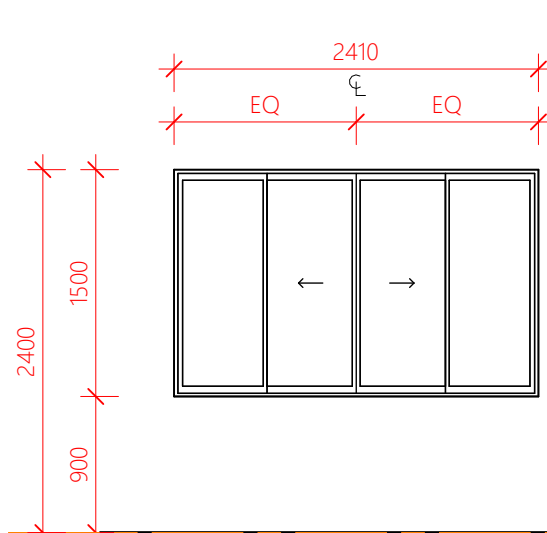

WINDOW TYPE E


LOCATION: EXTERNAL
FRAME TYPE: G.JAMES 475 SERIES
FRAME FINISH: SELECTED POWDERCOAT
WINDOW: G.JAMES 165 SERIES SLIDING WINDOW
GLASS: SAFETY GLASS

WINDOW SCHEDULE	
WINDOW NO.	WINDOW TYPE
01	TYPE A
02	TYPE B
03	TYPE B
04	TYPE C
05	TYPE C
06	TYPE B
07	TYPE B
08	TYPE A
09	TYPE C
10	TYPE E
11	TYPE E
12	TYPE F
13	TYPE G
14	TYPE G
15	TYPE H
16	TYPE I
17	TYPE I
18	TYPE I
19	TYPE I
20	TYPE I
21	TYPE I
22	TYPE H
23	TYPE G
24	TYPE G

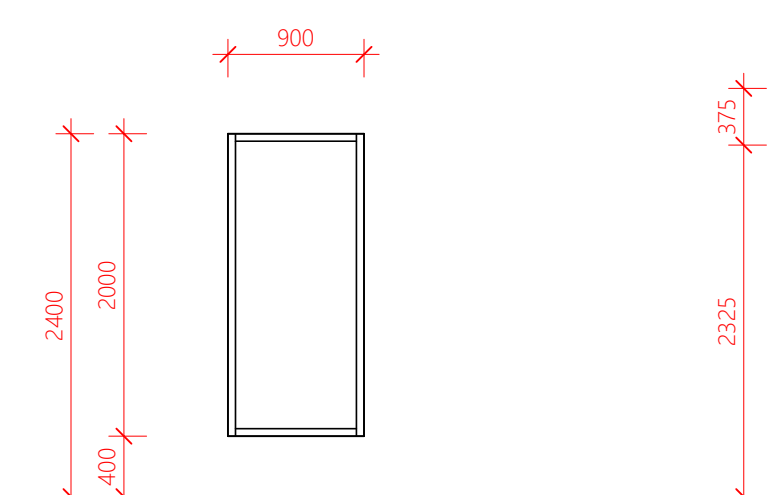


WINDOW TYPE F

LOCATION: EXTERNAL
FRAME TYPE: G.JAMES 475 SERIES
FRAME FINISH: SELECTED POWDERCOAT
WINDOW: FIXED GLASS
GLASS: SAFETY GLASS

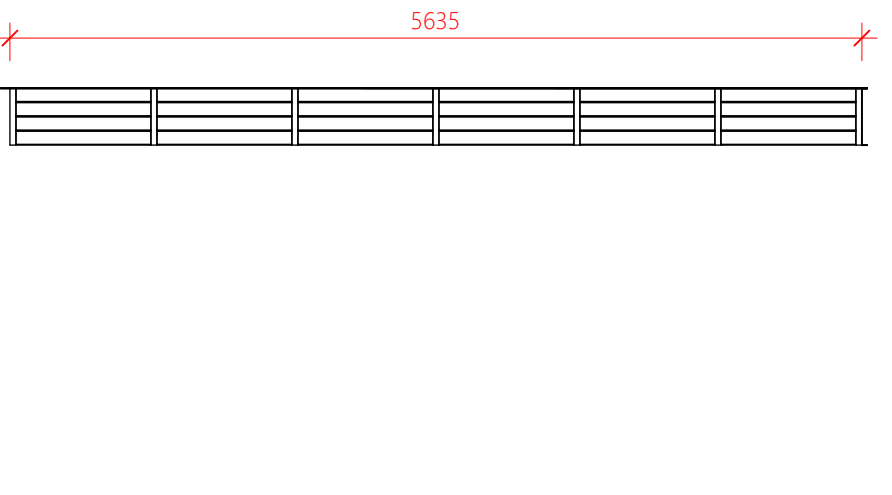


WINDOW TYPE G

LOCATION: EXTERNAL
FRAME TYPE: CAPRAL EXTRUDED LOUVRE BLADES.
FRAME FINISH: SELECTED POWDERCOAT
WINDOW: -
GLASS: -

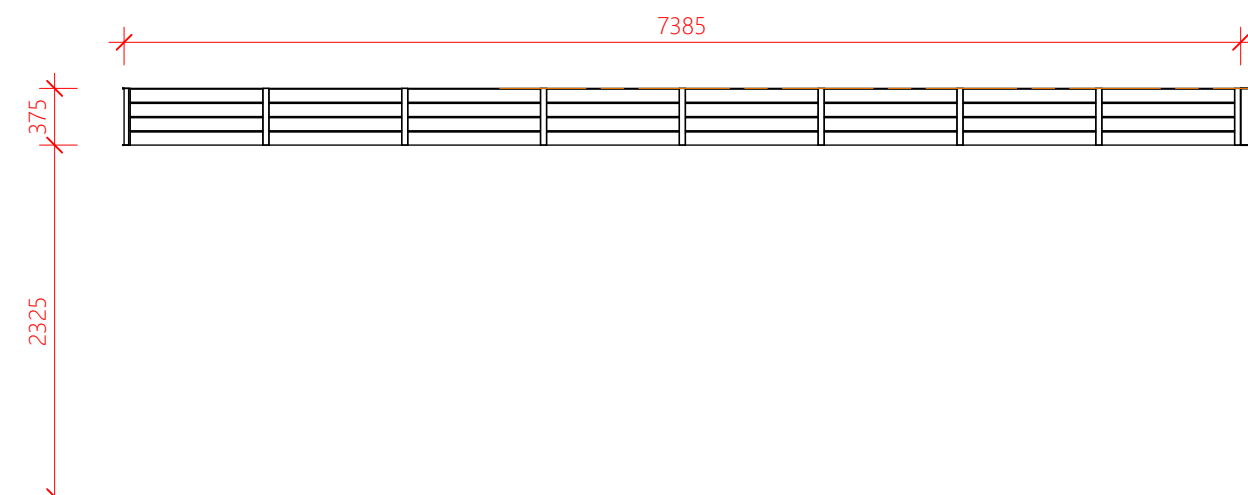

WINDOW TYPE H

LOCATION: EXTERNAL
FRAME TYPE: CAPRAL EXTRUDED LOUVRE BLADES.
FRAME FINISH: SELECTED POWDERCOAT
WINDOW: -
GLASS: -

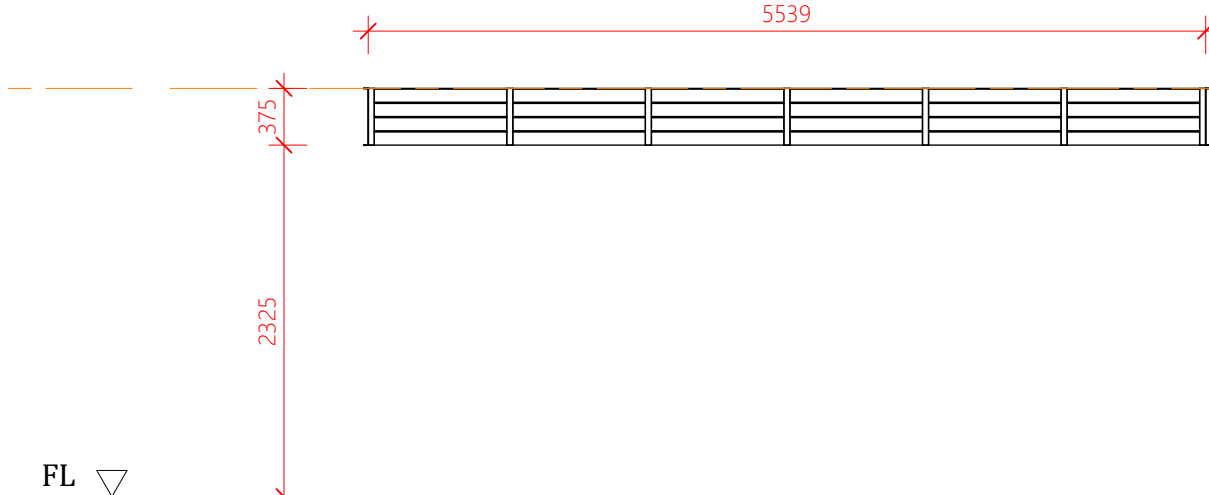

WINDOW TYPE I

LOCATION: EXTERNAL
FRAME TYPE: CAPRAL EXTRUDED LOUVRE BLADES.
FRAME FINISH: SELECTED POWDERCOAT
WINDOW: -
GLASS: -

REVISIONS

Rev	Description	Date
T1	TENDER ISSUE	12.03.2026

DO NOT SCALE THIS DRAWINGS

TENDER ISSUE



Project Details

OFFICE REFURBS

Address

STANWELL POWER STATION

Drawing Title

DOOR & WINDOW SCHEDULE



0483 988 655 M

info@designelements.com.au E

QBCC No: 1247120 BDAQ No: 0001677

Scale: 1 : 50

Rev:

Date: MAR 2026

T1

Drawn: Author

Project No:

Drawing No:

25_003

A4-701