


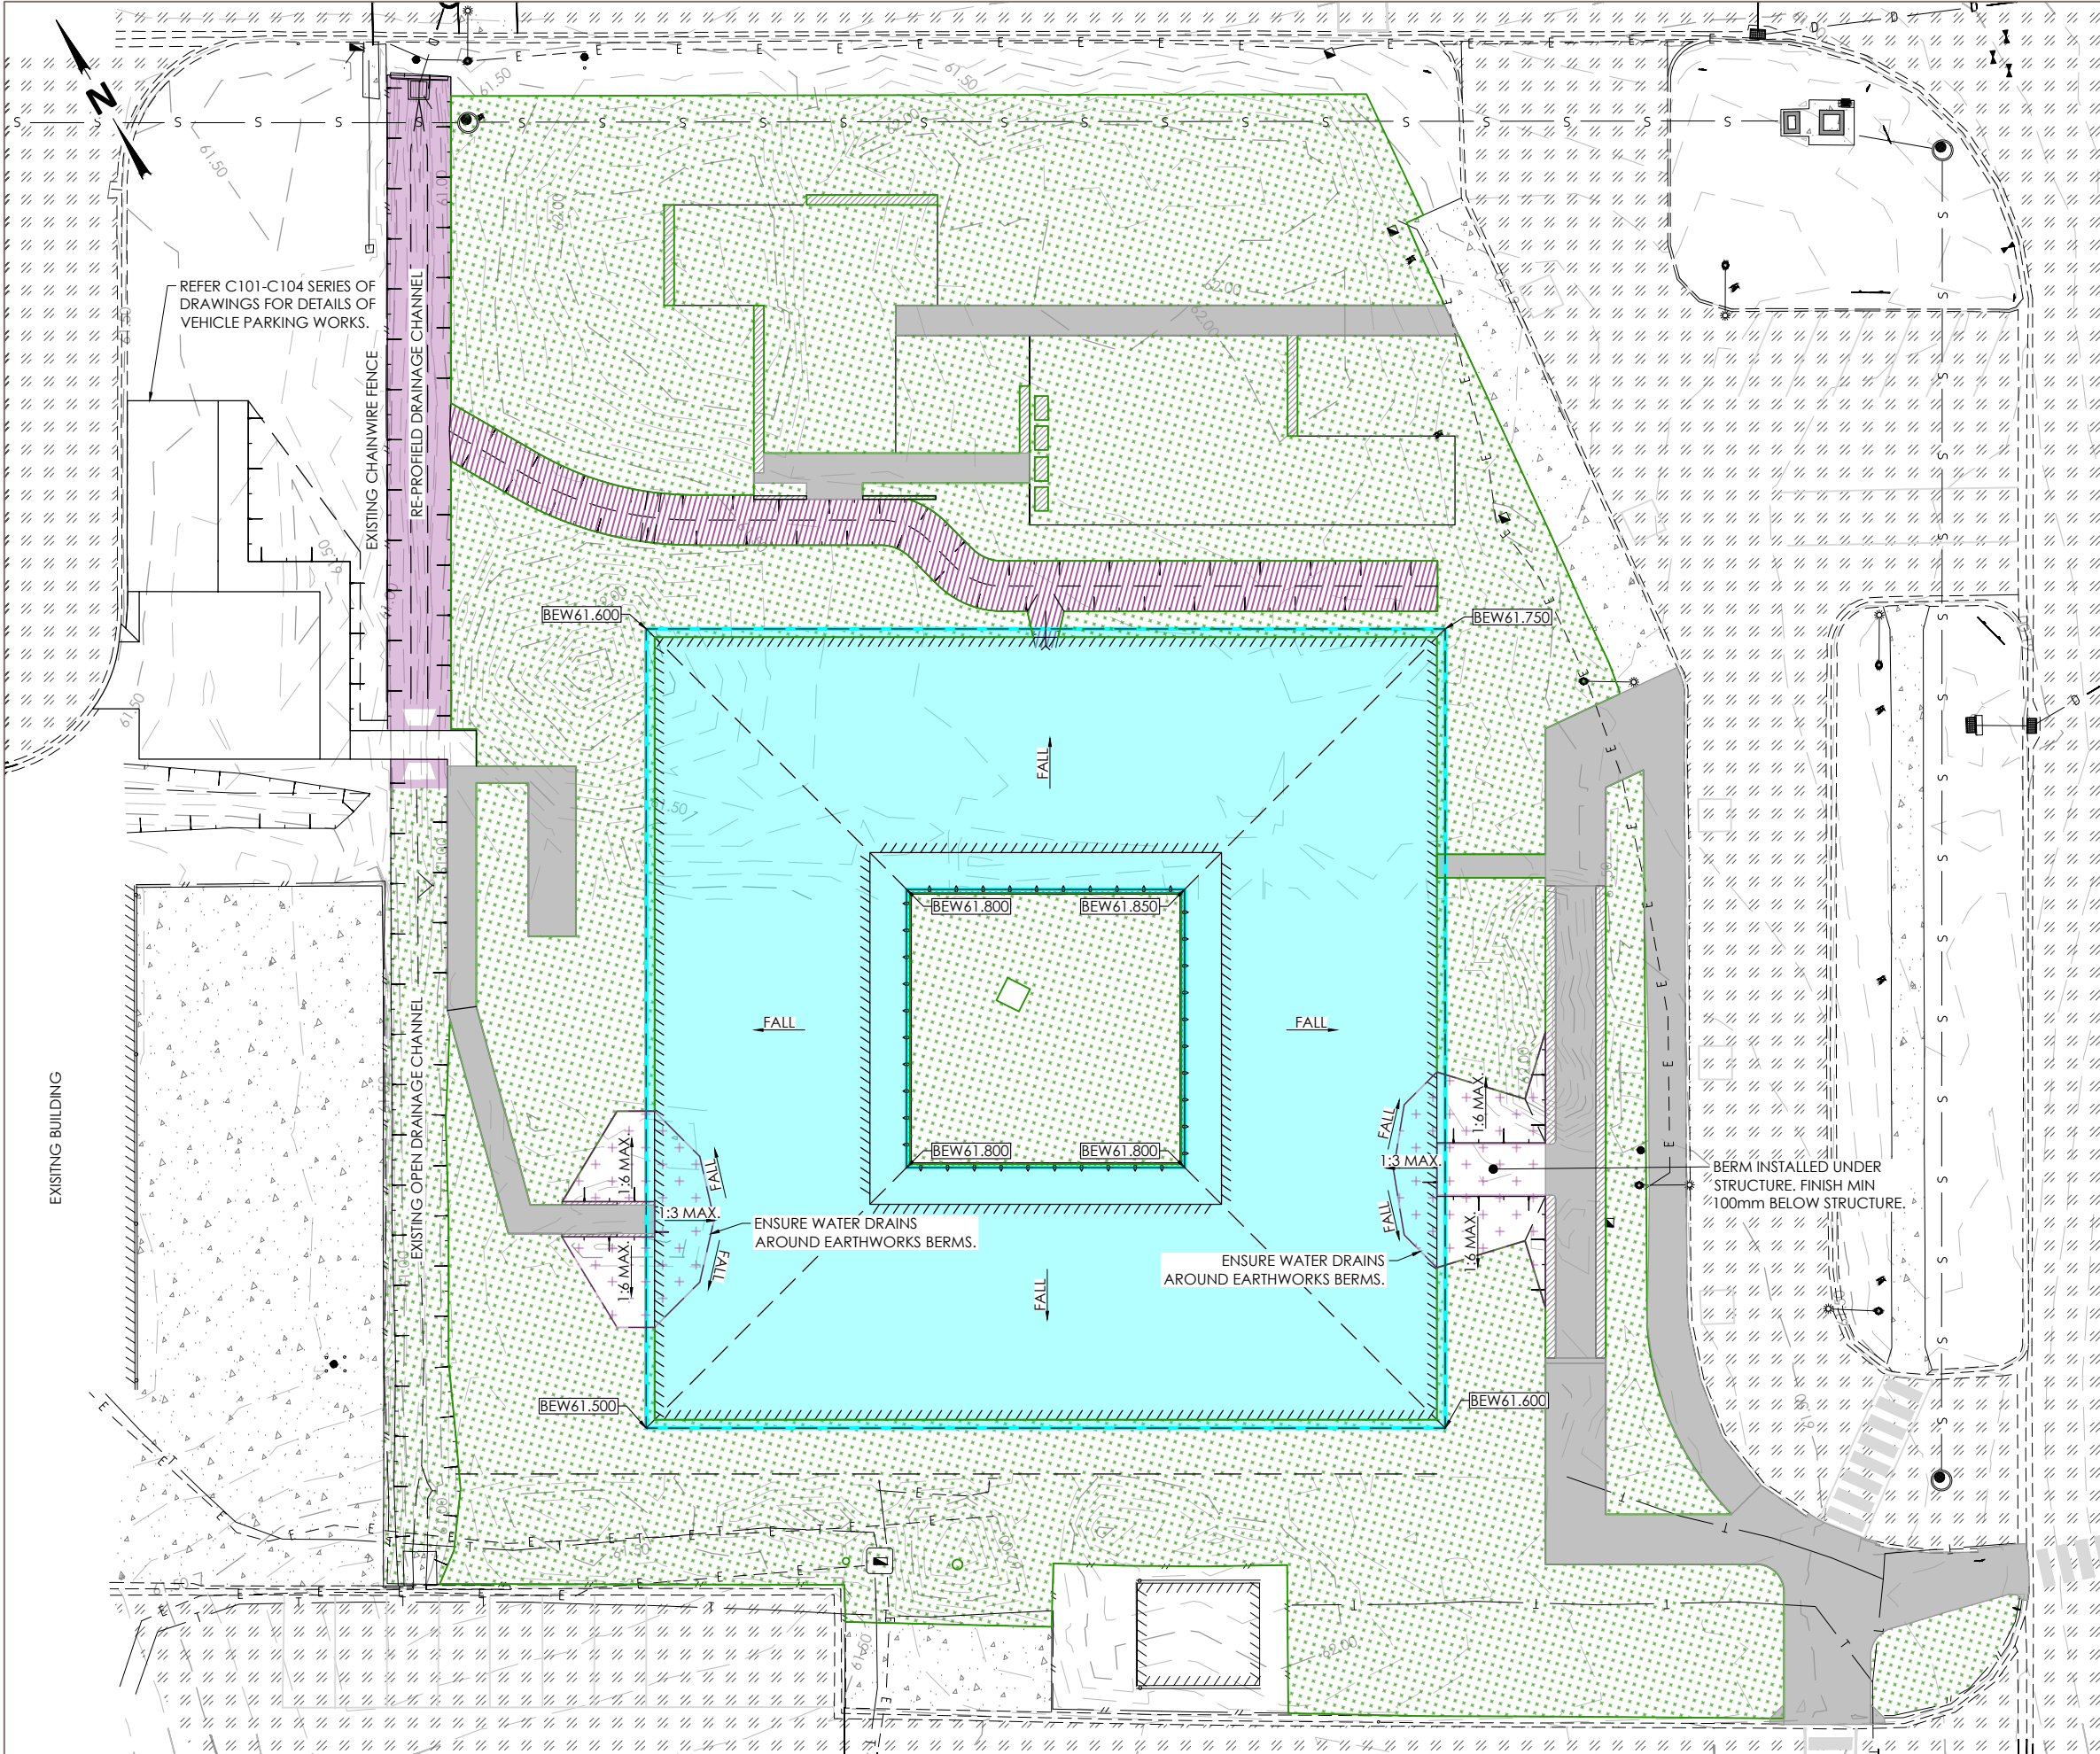

REFER C101-C104 SERIES OF DRAWINGS FOR DETAILS OF VEHICLE PARKING WORKS.

LEGEND	
	EXISTING SEAL AREA
	EXISTING CONCRETE AREA
	PROPOSED BULK EARTHWORKS FINISHED LEVEL
	EXISTING FENCE
	EXISTING TOE OF BATTER
	EXISTING TOP OF BATTER
	PROPOSED FENCE
	PROPOSED BUILDING OUTLINE
	PROPOSED TOE OF BATTER
	PROPOSED TOP OF BATTER
	PROPOSED CROWN LINE
	EXISTING CONTOUR
	PROPOSED GRAVEL WORKING PAD UNDER BUILDING. (MIN 150mm THICK CBR15 IMPORTED FILL). REFER SPECIFICATION NOTES.
	PROPOSED EARTHWORKS BERMS
	EXISTING OPEN DRAINAGE CHANNEL RE-PROFIED
	PROPOSED EXTERNAL CONCRETE AREA. REFER ARCHITECTS AND STRUCTURAL ENGINEERS DRAWINGS FOR DETAILS. REFER SPECIFICATION NOTES FOR SUBGRADE PREPARATION.
	PROPOSED LANDSCAPING & EARTHWORKS (REFER LANDSCAPE ARCHITECTS DRAWINGS FOR DETAILS).
	PROPOSED DRAINAGE SWALE.

- NOTES**
- FOR EXTENT OF DEMOLITION PRIOR TO EARTHWORKS REFER TO ARCHITECTURAL DOCUMENTATION.
 - REFER TO ARCHITECTS AND LANDSCAPE DOCUMENTS FOR LEVELS OF WORKS IN LANDSCAPE AREA.
 - REFER SPECIFICATION NOTES ON DRAWING C01 FOR EARTHWORKS REQUIREMENTS.

FINISHED LEVEL

BULK EARTHWORKS LEVEL (BEW)

PROPOSED CONCRETE. REFER STRUCTURAL DRAWINGS.
PROPOSED SAND BEDDING. REFER STRUCTURAL DRAWINGS.

**EXTERNAL CONCRETE AREA
PAVEMENT DETAIL**
SCALE 1:20

<table><tr><th>Revision</th><th>Date</th><th>Revision Description</th><th>Drawn</th><th>Design</th><th>Checked</th></tr><tr><td>1</td><td>03/09/2025</td><td>PRELIMINARY</td><td>JC</td><td>JC</td><td>MD</td></tr><tr><td>2</td><td>23/09/2025</td><td>DD ISSUE</td><td>JC</td><td>JC</td><td>MD</td></tr><tr><td>3</td><td>03/11/2025</td><td>50% CD ISSUE</td><td>JC</td><td>JC</td><td>MD</td></tr><tr><td>4</td><td>28/11/2025</td><td>90% CD ISSUE</td><td>JC</td><td>JC</td><td>MD</td></tr><tr><td>5</td><td>19/12/2025</td><td>100% CD ISSUE</td><td>JC</td><td>JC</td><td>MD</td></tr><tr><td>A</td><td>09/03/2026</td><td>FOR TENDER</td><td>JC</td><td>JC</td><td>MD</td></tr></table>			Revision	Date	Revision Description	Drawn	Design	Checked	1	03/09/2025	PRELIMINARY	JC	JC	MD	2	23/09/2025	DD ISSUE	JC	JC	MD	3	03/11/2025	50% CD ISSUE	JC	JC	MD	4	28/11/2025	90% CD ISSUE	JC	JC	MD	5	19/12/2025	100% CD ISSUE	JC	JC	MD	A	09/03/2026	FOR TENDER	JC	JC	MD	<table><tr><td colspan="2">MATTHEW DENNIS R.P.E.Q.24862</td></tr><tr><td colspan="2">APPROVAL FOR ISSUE FOR AND ON BEHALF OF JANES AND STEWART STRUCTURES PTY LTD</td></tr></table>		MATTHEW DENNIS R.P.E.Q.24862		APPROVAL FOR ISSUE FOR AND ON BEHALF OF JANES AND STEWART STRUCTURES PTY LTD		02.00 0 2.0 8.0m 1:400 A3 SHEET - DO NOT SCALE		Client STANWELL Janes and Stewart Structures Pty Ltd 120 William Street Po Box 1072 Rockhampton 4700 07 4922 1948 janes.and.stewart@jsstructures.com.au ABN 30 620 233 025		Project STANWELL NEW PROJECTS OFFICE SWITCHYARD ROAD, STANWELL, QLD, 4702		TENDER NOT FOR CONSTRUCTION PURPOSES BULK EARTHWORKS PLAN		<table><tr><td>Project Number</td><td>25052</td></tr><tr><td>Title</td><td>Drawing</td></tr><tr><td>Revision</td><td>C02</td></tr><tr><td></td><td>A</td></tr></table>		Project Number	25052	Title	Drawing	Revision	C02		A
Revision	Date	Revision Description	Drawn	Design	Checked	
1	03/09/2025	PRELIMINARY	JC	JC	MD	
2	23/09/2025	DD ISSUE	JC	JC	MD	
3	03/11/2025	50% CD ISSUE	JC	JC	MD	
4	28/11/2025	90% CD ISSUE	JC	JC	MD	
5	19/12/2025	100% CD ISSUE	JC	JC	MD	
A	09/03/2026	FOR TENDER	JC	JC	MD	
MATTHEW DENNIS R.P.E.Q.24862	
APPROVAL FOR ISSUE FOR AND ON BEHALF OF JANES AND STEWART STRUCTURES PTY LTD	
Project Number	25052	
Title	Drawing	
Revision	C02	
	A	