



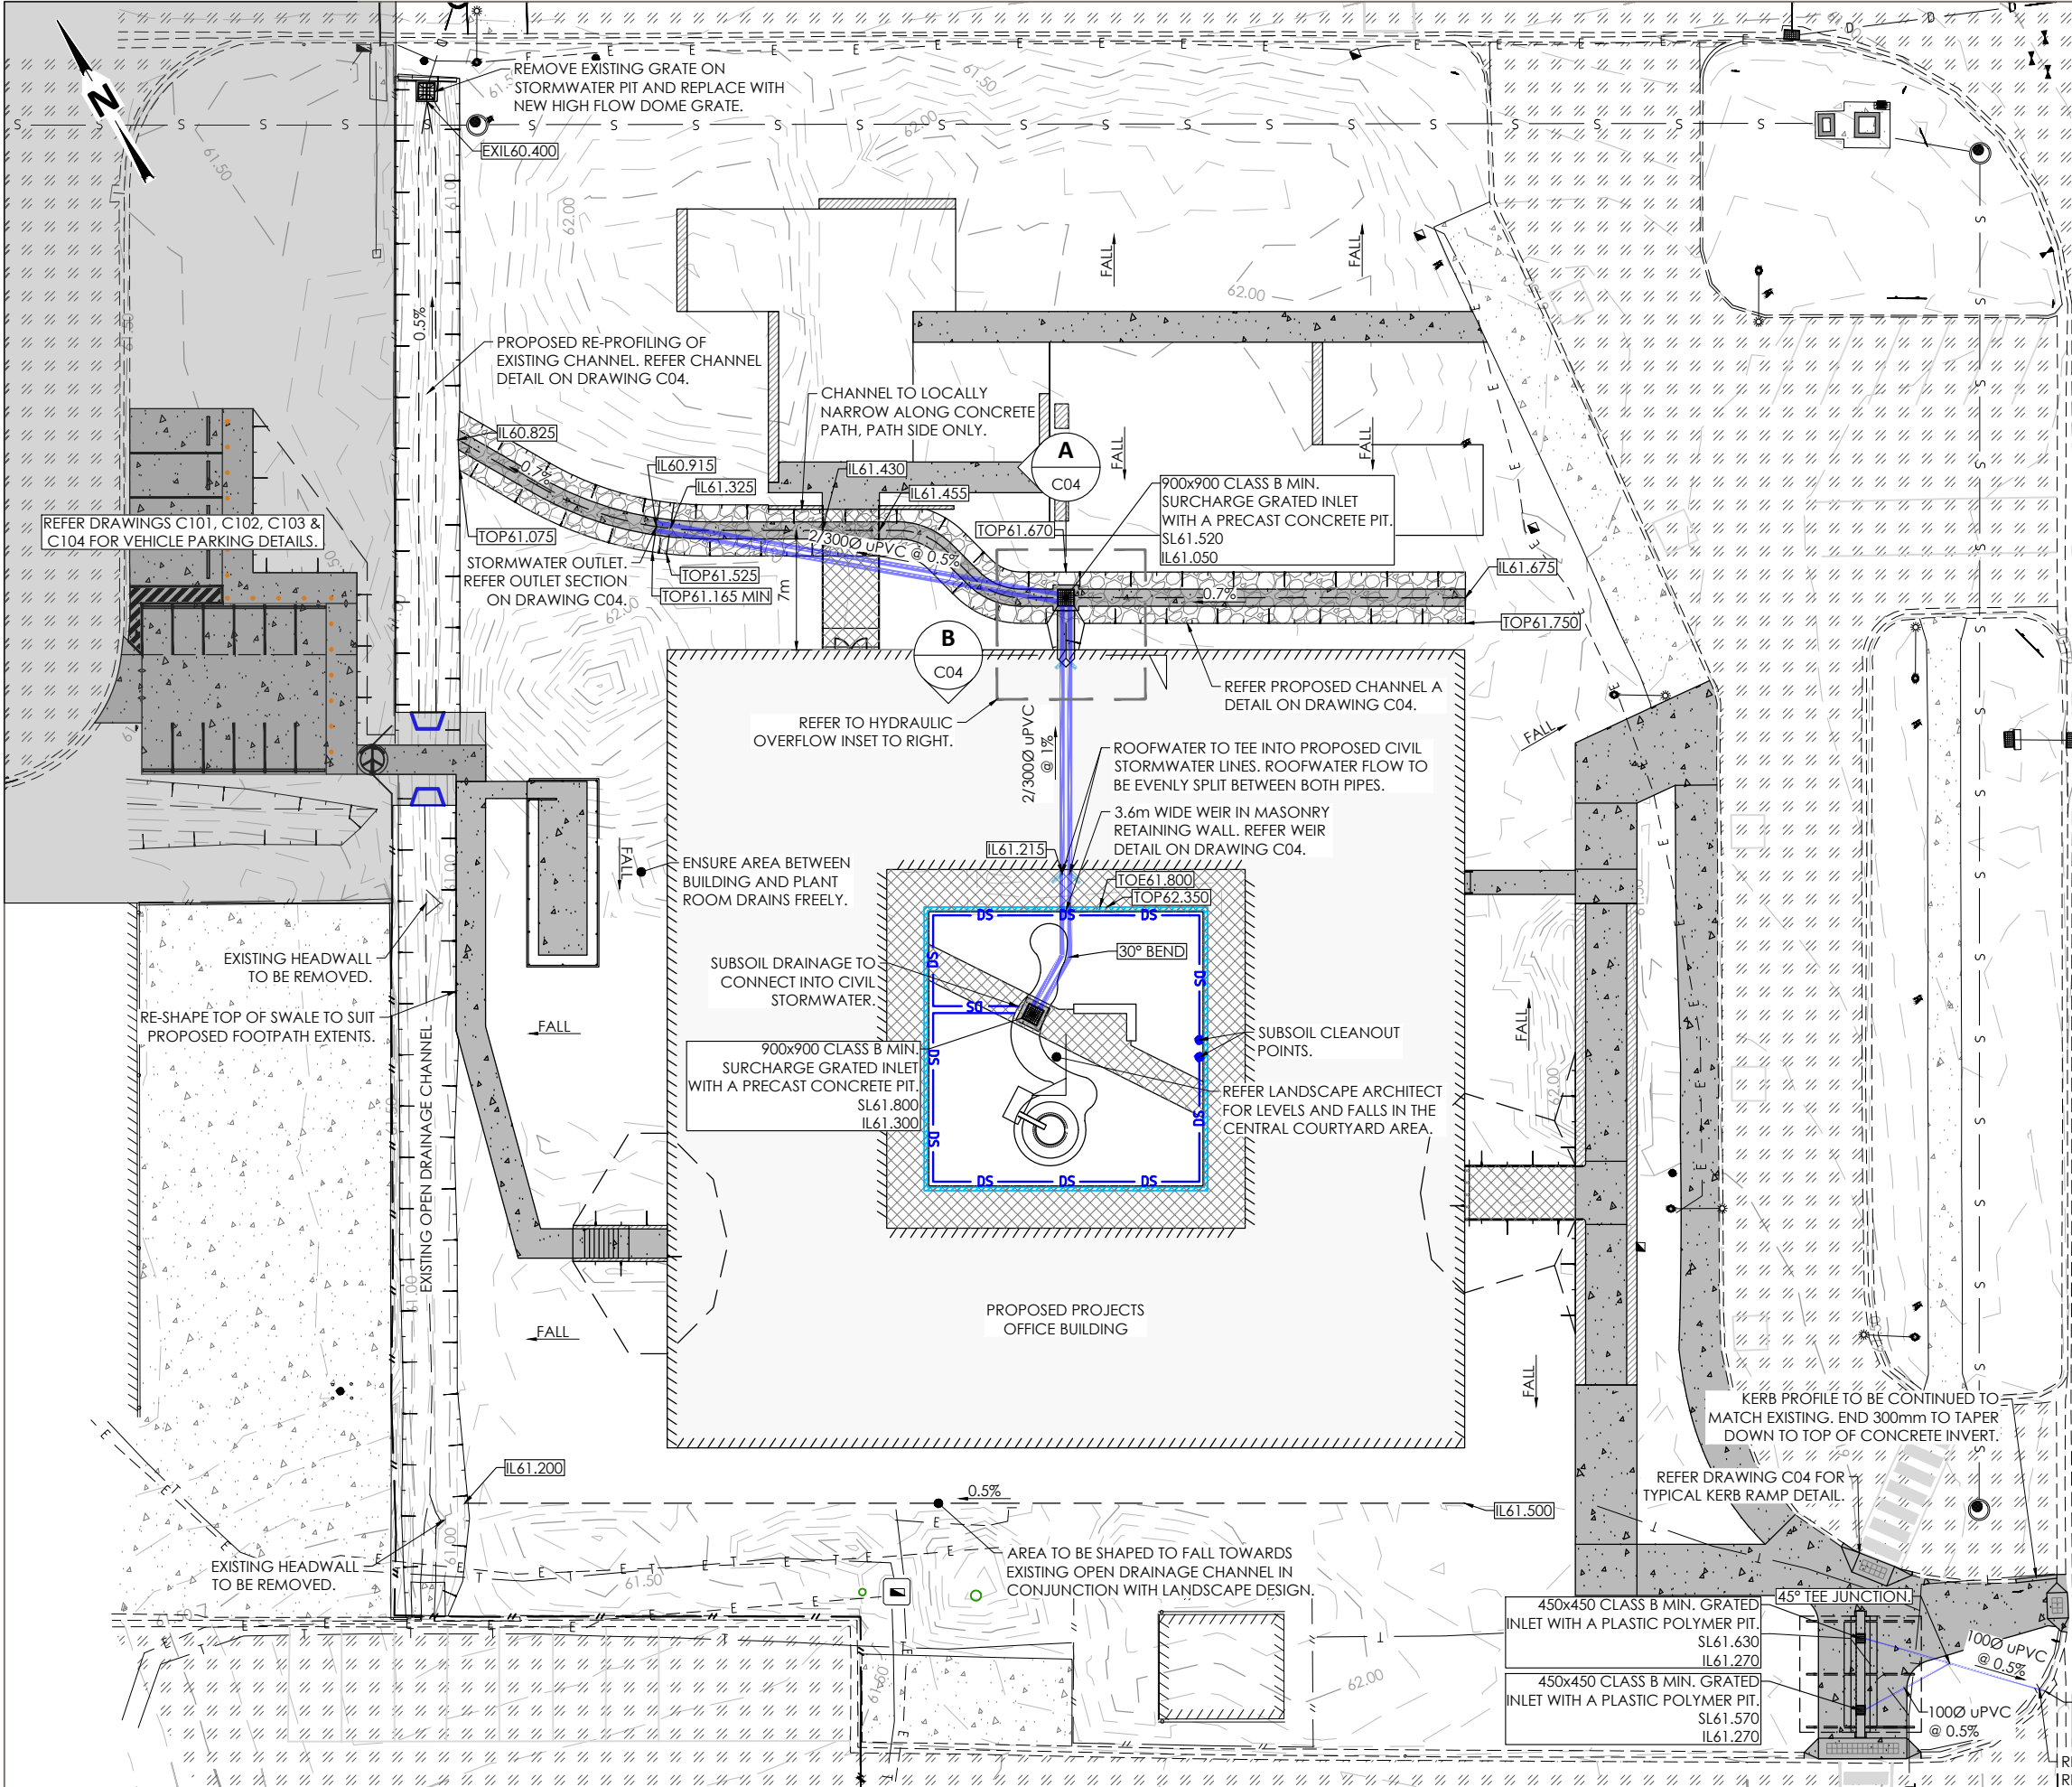

LEGEND	
	EXISTING SEAL AREA
	EXISTING CONCRETE AREA
	PROPOSED ROCK AREA - REFER LANDSCAPE ARCHITECT
	PROPOSED CONCRETE AREA
	PROPOSED SUSPENDED WALKWAY AREA
	PROPOSED SURFACE LEVEL
	PROPOSED INVERT LEVEL
	PROPOSED TOP OF BATTER LEVEL
	EXISTING LOT BOUNDARY
	EXISTING STORMWATER DRAINAGE
	EXISTING UNDERGROUND ELECTRICAL
	EXISTING SEWER MAIN & MANHOLE
	EXISTING TELECOMMUNICATIONS
	EXISTING FENCE
	EXISTING TOE OF BATTER
	EXISTING TOP OF BATTER
	EXISTING EDGE OF SEAL
	EXISTING KERB
	EXISTING BUILDING OUTLINE
	PROPOSED RETAINING WALL
	PROPOSED STORMWATER DRAINAGE (SIZE. AS NOTED)
	PROPOSED SUBSOIL DRAINAGE
	PROPOSED FENCE
	PROPOSED TOE OF BATTER
	PROPOSED TOP OF BATTER
	PROPOSED CROWN LINE
	EXISTING CONTOUR

NOTES


1. LEVELS SHOWN ON THIS PLAN FOR STORMWATER DRAINAGE ONLY. REFER DRAWING C07 FOR FOOTPATH LEVELS. REFER ARCHITECT/LANDSCAPE ARCHITECT DRAWINGS FOR ALL OTHER LEVELS.

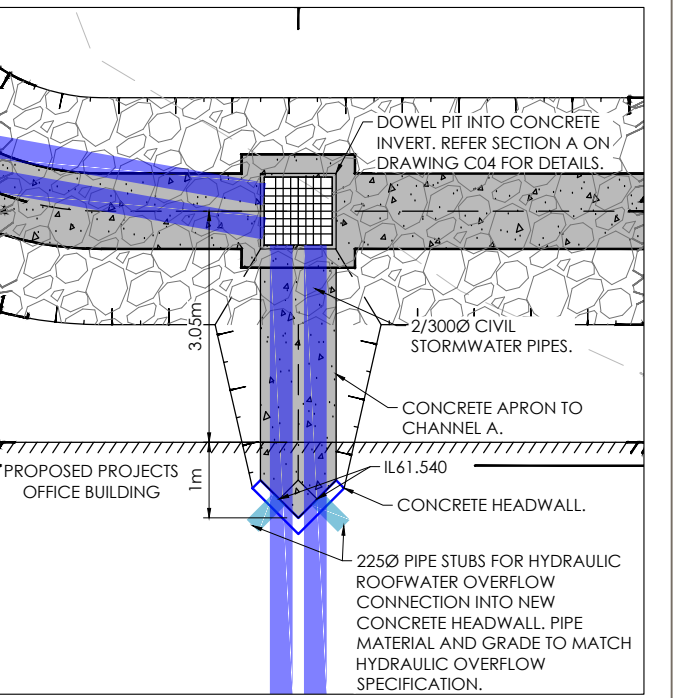

Revision	Date	Revision Description	Drawn	Design	Checked
1	03/09/2025	PRELIMINARY	JC	JC	MD
2	23/09/2025	DD ISSUE	JC	JC	MD
3	03/11/2025	50% CD ISSUE	JC	JC	MD
4	28/11/2025	90% CD ISSUE	JC	JC	MD
5	19/12/2025	100% CD ISSUE	JC	JC	MD
A	09/03/2026	FOR TENDER	JC	JC	MD

MATTHEW DENNIS R.P.E.Q.24862

APPROVAL FOR ISSUE FOR AND ON BEHALF OF
JANES AND STEWART STRUCTURES PTY LTD

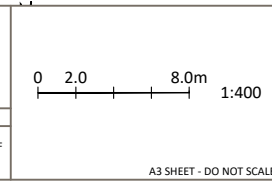

Client
STANWELL

Janes and Stewart Structures Pty Ltd
120 William Street | Po Box 1072
Rockhampton 4700
07 4922 1948
janes.and.stewart@jsstructures.com.au
ABN 30 620 233 025



Project
STANWELL NEW PROJECTS OFFICE

TENDER		Project Number
NOT FOR CONSTRUCTION PURPOSES		25052
Title		Drawing
		C03
Revision		A
CIVIL WORKS PLAN		