




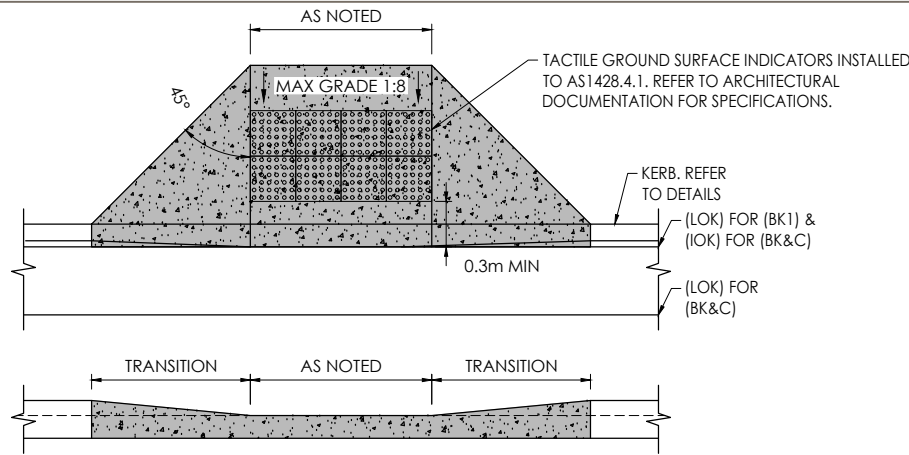


KERB RAMP DETAIL
KERB RAMP TO COMPLY WITH AS1428.1
SCALE 1:50

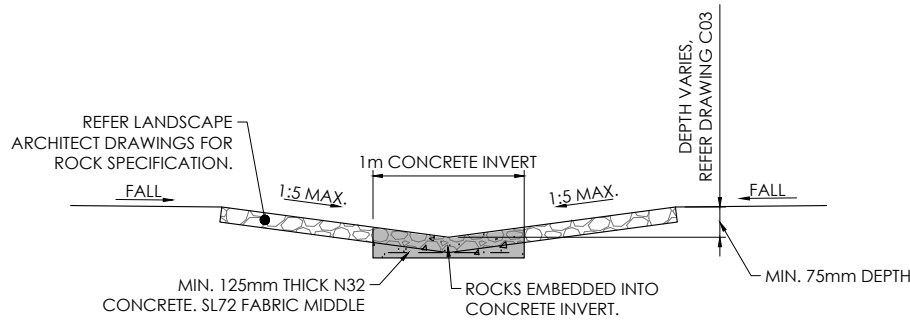


CHANNEL A - TYPICAL DETAIL
SCALE 1:50

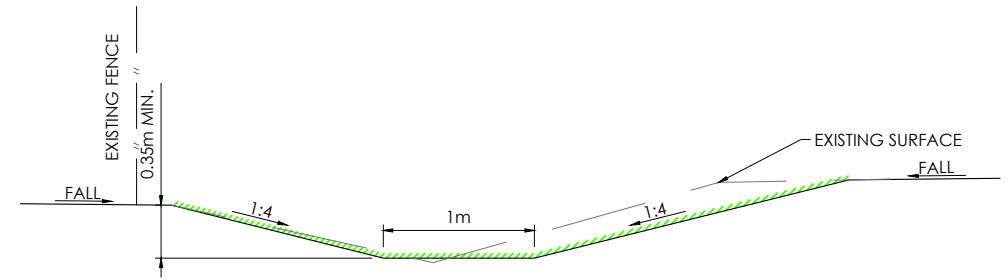


EXISTING RE-PROFILED CHANNEL TYPICAL DETAIL
SCALE 1:50

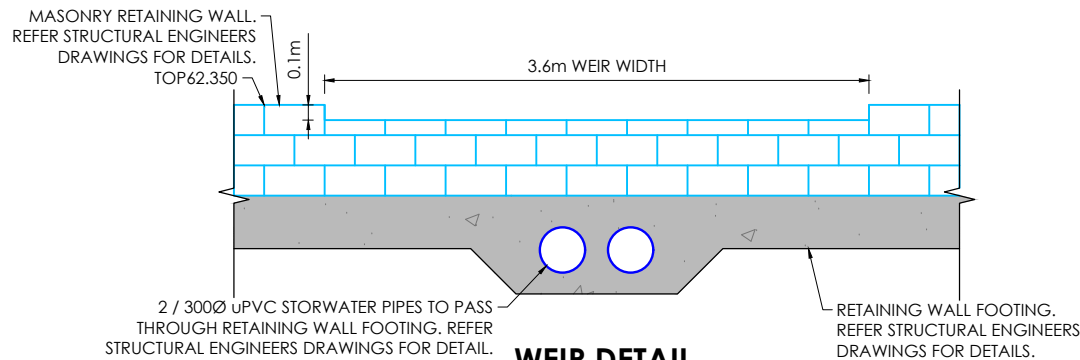


WEIR DETAIL
SCALE 1:50

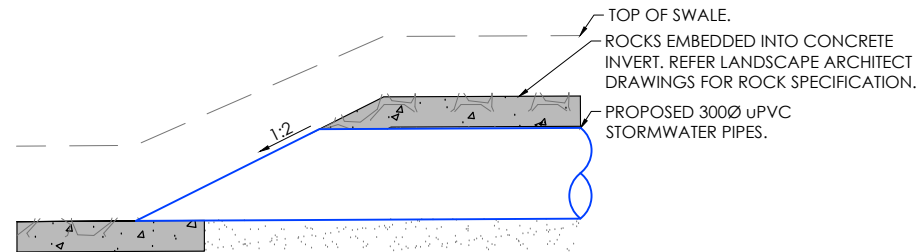

STORMWATER PIPE OUTLET SECTION
SCALE 1:25

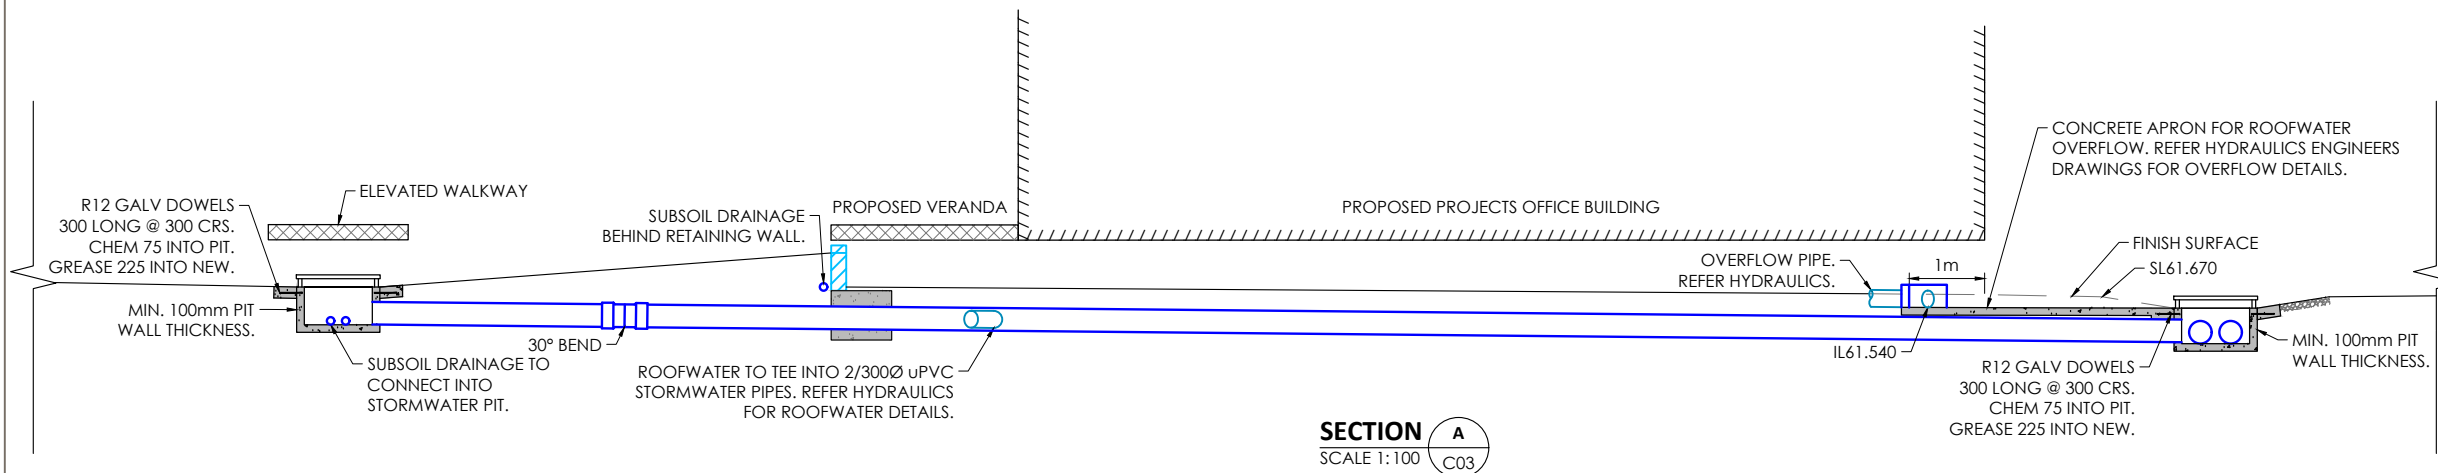

SECTION A
SCALE 1:100
C03

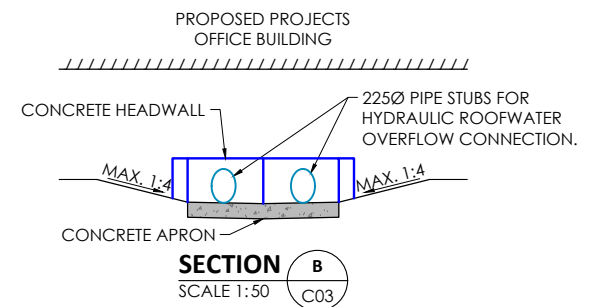

SECTION B
SCALE 1:50
C03

Revision	Date	Revision Description	Drawn	Design	Checked
1	03/09/2025	PRELIMINARY	JC	JC	MD
2	23/09/2025	DD ISSUE	JC	JC	MD
3	03/11/2025	50% CD ISSUE	JC	JC	MD
4	28/11/2025	90% CD ISSUE	JC	JC	MD
5	19/12/2025	100% CD ISSUE	JC	JC	MD
A	09/03/2026	FOR TENDER	JC	JC	MD

MATTHEW DENNIS R.P.E.Q. 24862
APPROVAL FOR ISSUE FOR AND ON BEHALF OF
JANES AND STEWART STRUCTURES PTY LTD

AS SHOWN

A3 SHEET - DO NOT SCALE

Client
STANWELL

Janes and Stewart Structures Pty Ltd
120 William Street | Po Box 1072
Rockhampton 4700
07 4922 1948
janes.and.stewart@jsstructures.com.au
ABN 30 620 233 025

JS² Janes and Stewart
Structural+Civil
CONSULTANTS

Project
STANWELL NEW PROJECTS OFFICE

**SWITCHYARD ROAD,
STANWELL, QLD, 4702**

TENDER
NOT FOR CONSTRUCTION PURPOSES

CIVIL DETAILS

Project Number
25052

Drawing
C04

Revision
A