


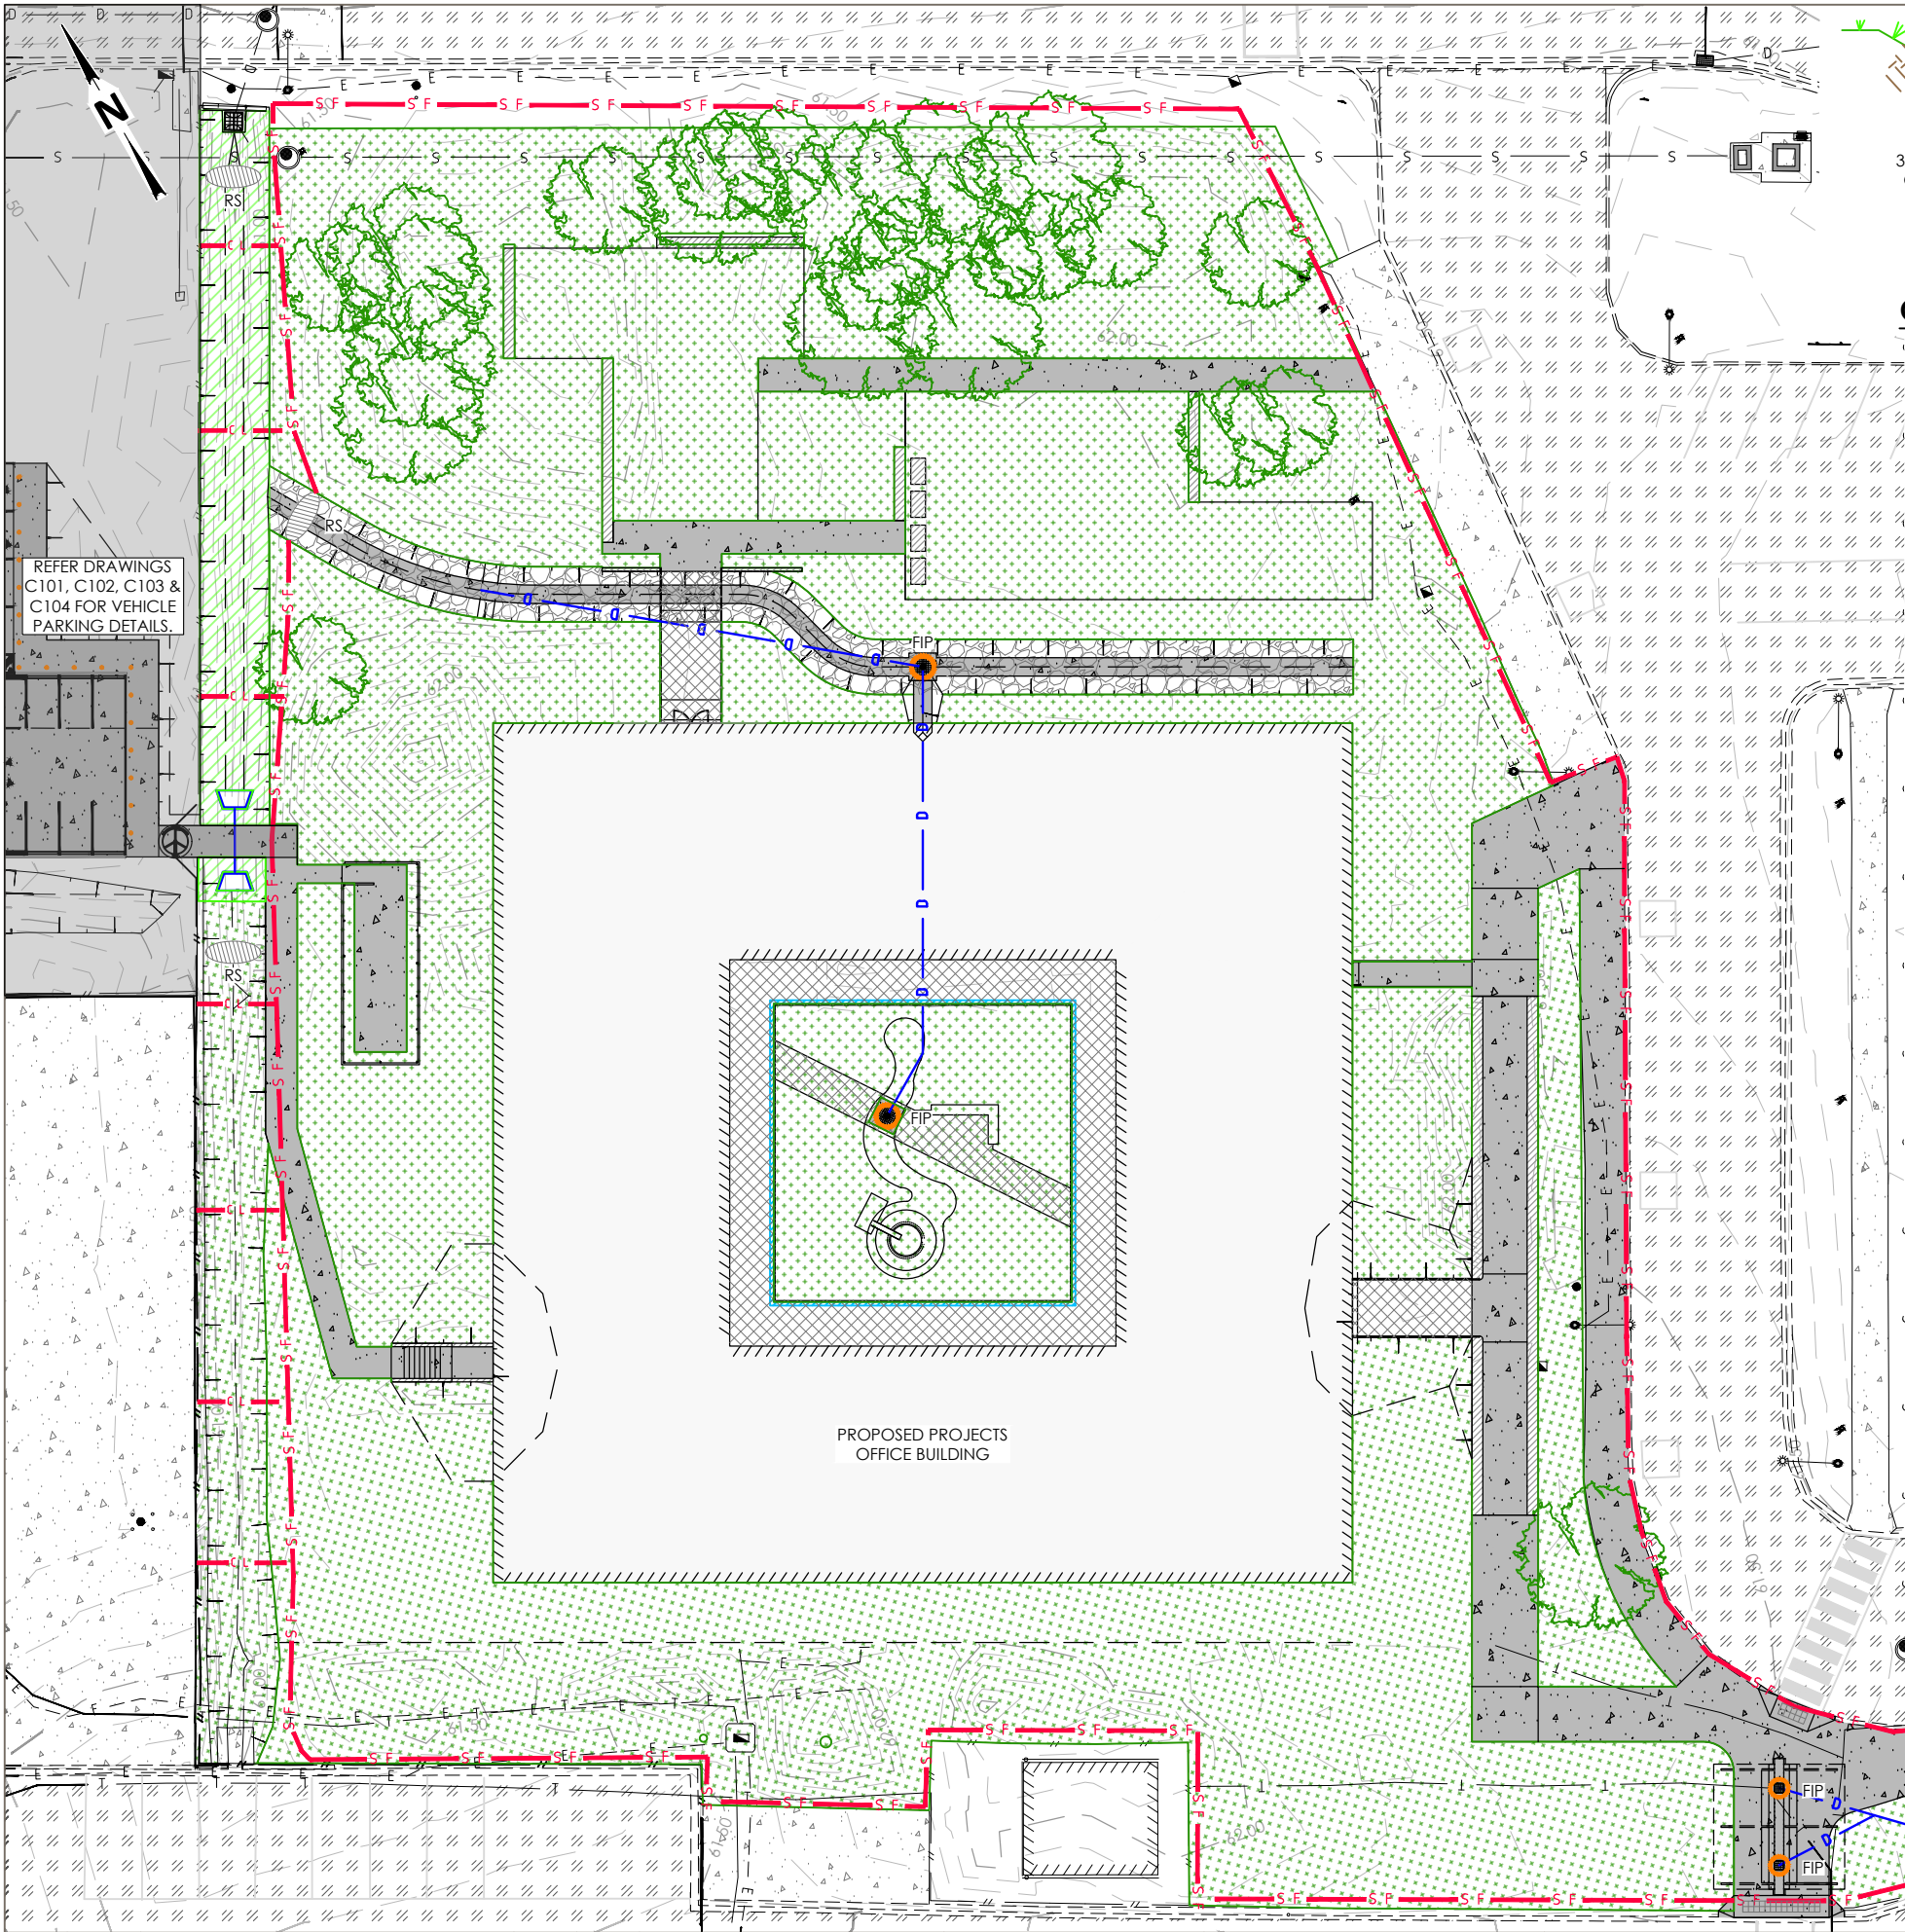

REFER DRAWINGS
C101, C102, C103 &
C104 FOR VEHICLE
PARKING DETAILS.

Revision	Date	Revision Description	Drawn	Design	Checked
1	03/09/2025	PRELIMINARY	JC	JC	MD
2	23/09/2025	DD ISSUE	JC	JC	MD
3	03/11/2025	50% CD ISSUE	JC	JC	MD
4	28/11/2025	90% CD ISSUE	JC	JC	MD
5	19/12/2025	100% CD ISSUE	JC	JC	MD
A	09/03/2026	FOR TENDER	JC	JC	MD

MATTHEW DENNIS R.P.E.Q.24862
APPROVAL FOR ISSUE FOR AND ON BEHALF OF
JANES AND STEWART STRUCTURES PTY LTD

0 2.0 8.0m 1:400

A3 SHEET - DO NOT SCALE

Client
STANWELL


Janes and Stewart Structures Pty Ltd
120 William Street | Po Box 1072
Rockhampton 4700
07 4922 1948
janes.and.stewart@jsstructures.com.au
ABN 30 620 233 025

JS² Janes and Stewart
Structural+Civil
CONSULTANTS


Project
STANWELL NEW PROJECTS OFFICE
Switchyard Road,
Stanwell, QLD, 4702

TENDER
NOT FOR CONSTRUCTION PURPOSES
Title
**EROSION AND SEDIMENT CONTROL
PLAN AND DETAILS**
Project Number
25052
Drawing
C05
Revision
A


COIR LOG (TYPICAL PLACEMENT)
GENERALLY IN ACCORDANCE WITH IEECA GUIDELINES.
SCALE 1:20

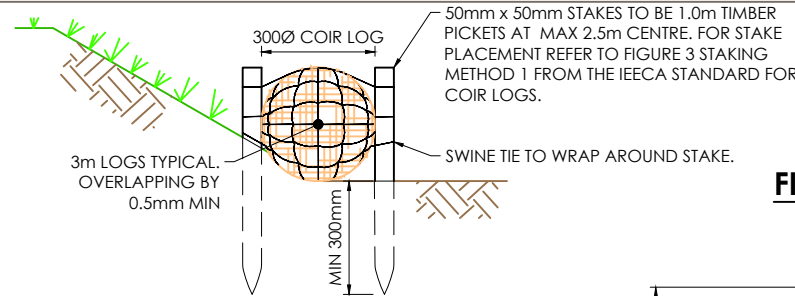

FIELD INLET PROTECTION (FIP)

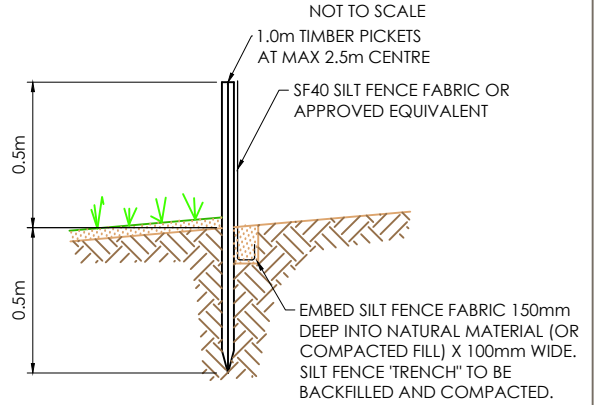

SILT FENCE (SF)
NOT TO SCALE

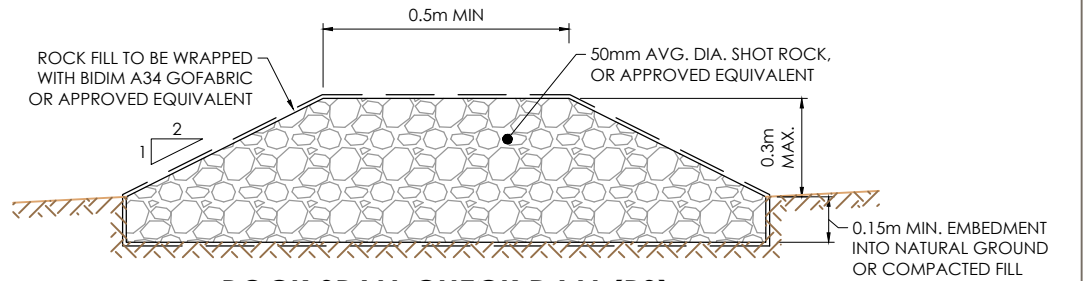

ROCK SPALL CHECK DAM (RS)
NOT TO SCALE

LEGEND

	EXISTING SEAL AREA
	EXISTING CONCRETE AREA
	PROPOSED TURF AREA
	PROPOSED LANDSCAPING (DETAILED BY OTHERS)
	PROPOSED ROCK AREA - REFER LANDSCAPE ARCHITECT
	PROPOSED VERANDA AREA
	TEMP. ROCK SPALL CHECK DAM (RS)
	PROPOSED TOE OF BATTER
	PROPOSED TOP OF BATTER
	TEMP. COIR LOG (CL)
	TEMP. SILT FENCE (SF)
	TEMP. FIELD INLET PROTECTION (FIP)

NOTES

- REFER TO SPECIFICATION NOTES ON DRAWING C01 FOR EROSION AND SEDIMENT CONTROL REQUIREMENTS.
- PROVIDE ENTRY / EXIT SEDIMENT TRAPS AT ALL VEHICLE ENTRY/EXIT POINTS
- FOR EXTENTS AND DETAILS OF PERMANENT EROSION CONTROL SURFACE TREATMENTS, REFER LANDSCAPE ARCHITECT DRAWINGS.