


LEGEND	
	EXISTING SEAL AREA
	EXISTING CONCRETE AREA
	PROPOSED CONCRETE AREA
	EXISTING SURFACE LEVEL
	PROPOSED FINISHED CONCRETE LEVEL
	PROPOSED SURFACE LEVEL
	EXISTING TOE OF BATTER
	EXISTING TOP OF BATTER
	EXISTING KERB
	PROPOSED TOE OF BATTER
	PROPOSED TOP OF BATTER
	PROPOSED CROWN LINE
	PROPOSED STORMWATER DRAINAGE
	EXISTING CONTOUR

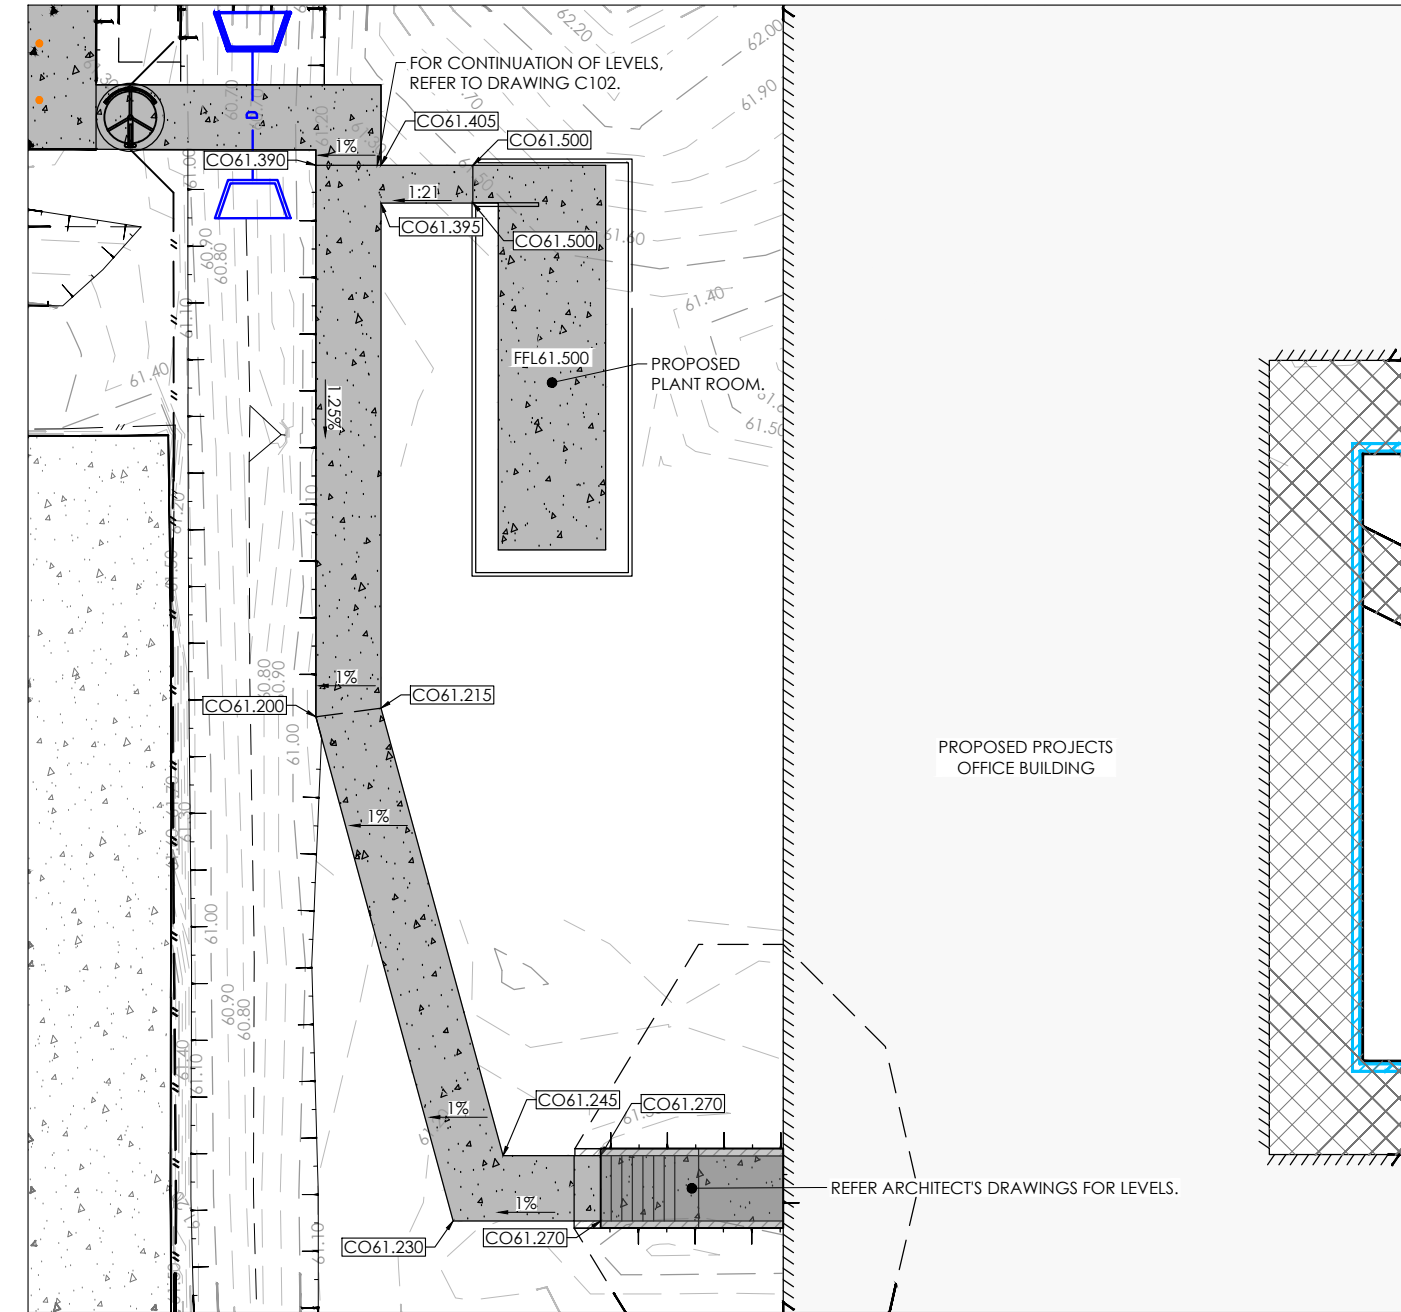


WESTERN PATHWAY LEVELS

SCALE 1:200


Revision	Date	Revision Description	Drawn	Design	Checked
1	19/12/2025	100% CD ISSUE	JC	JC	MD
A	09/03/2026	FOR TENDER	JC	JC	MD

MATTHEW DENNIS R.P.E.Q.24862

APPROVAL FOR ISSUE FOR AND ON BEHALF OF
JANES AND STEWART STRUCTURES PTY LTD

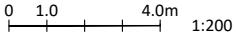


A3 SHEET - DO NOT SCALE

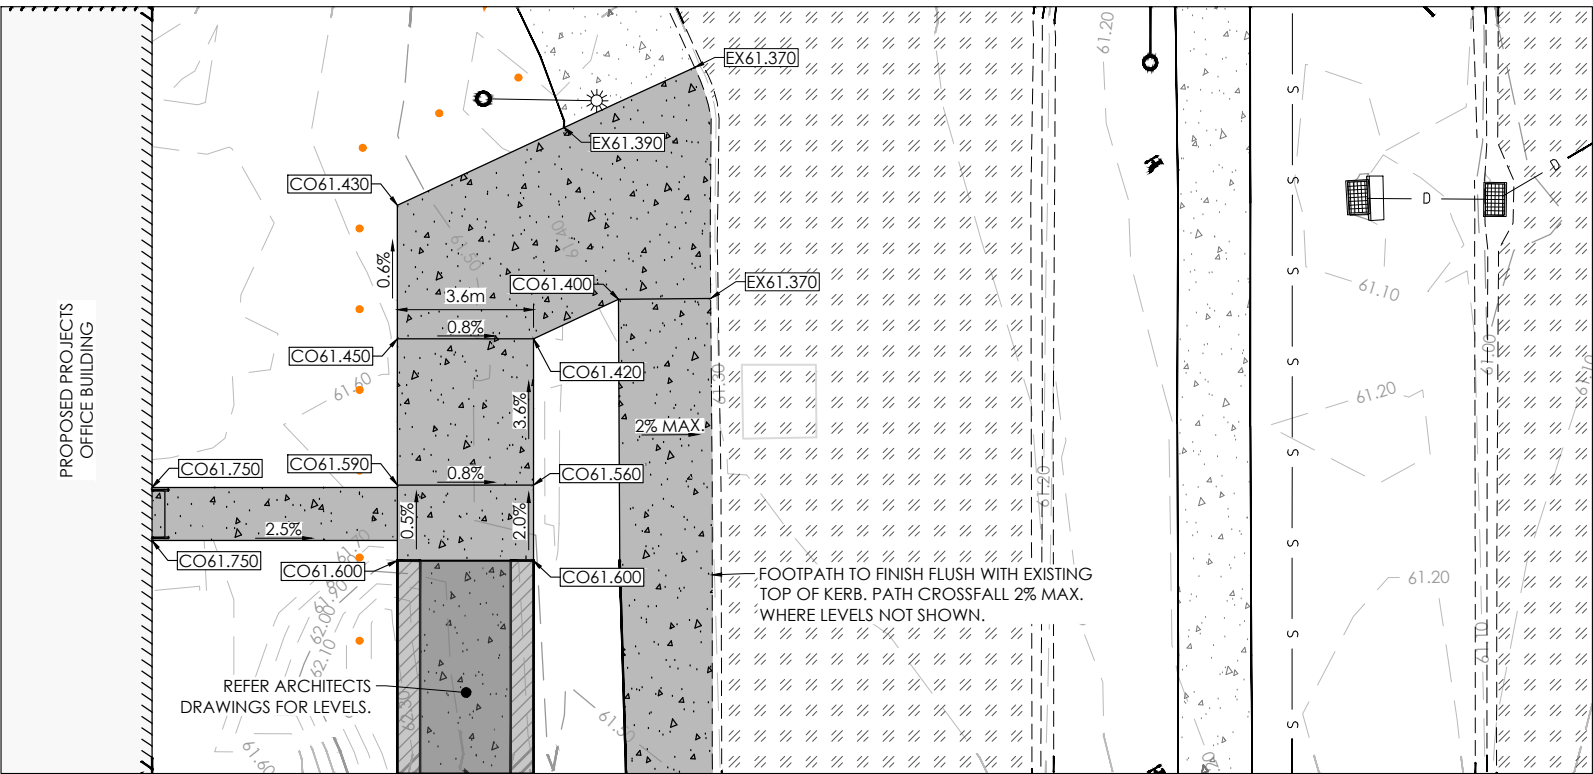

EASTERN PATHWAY LEVELS

SCALE 1:200

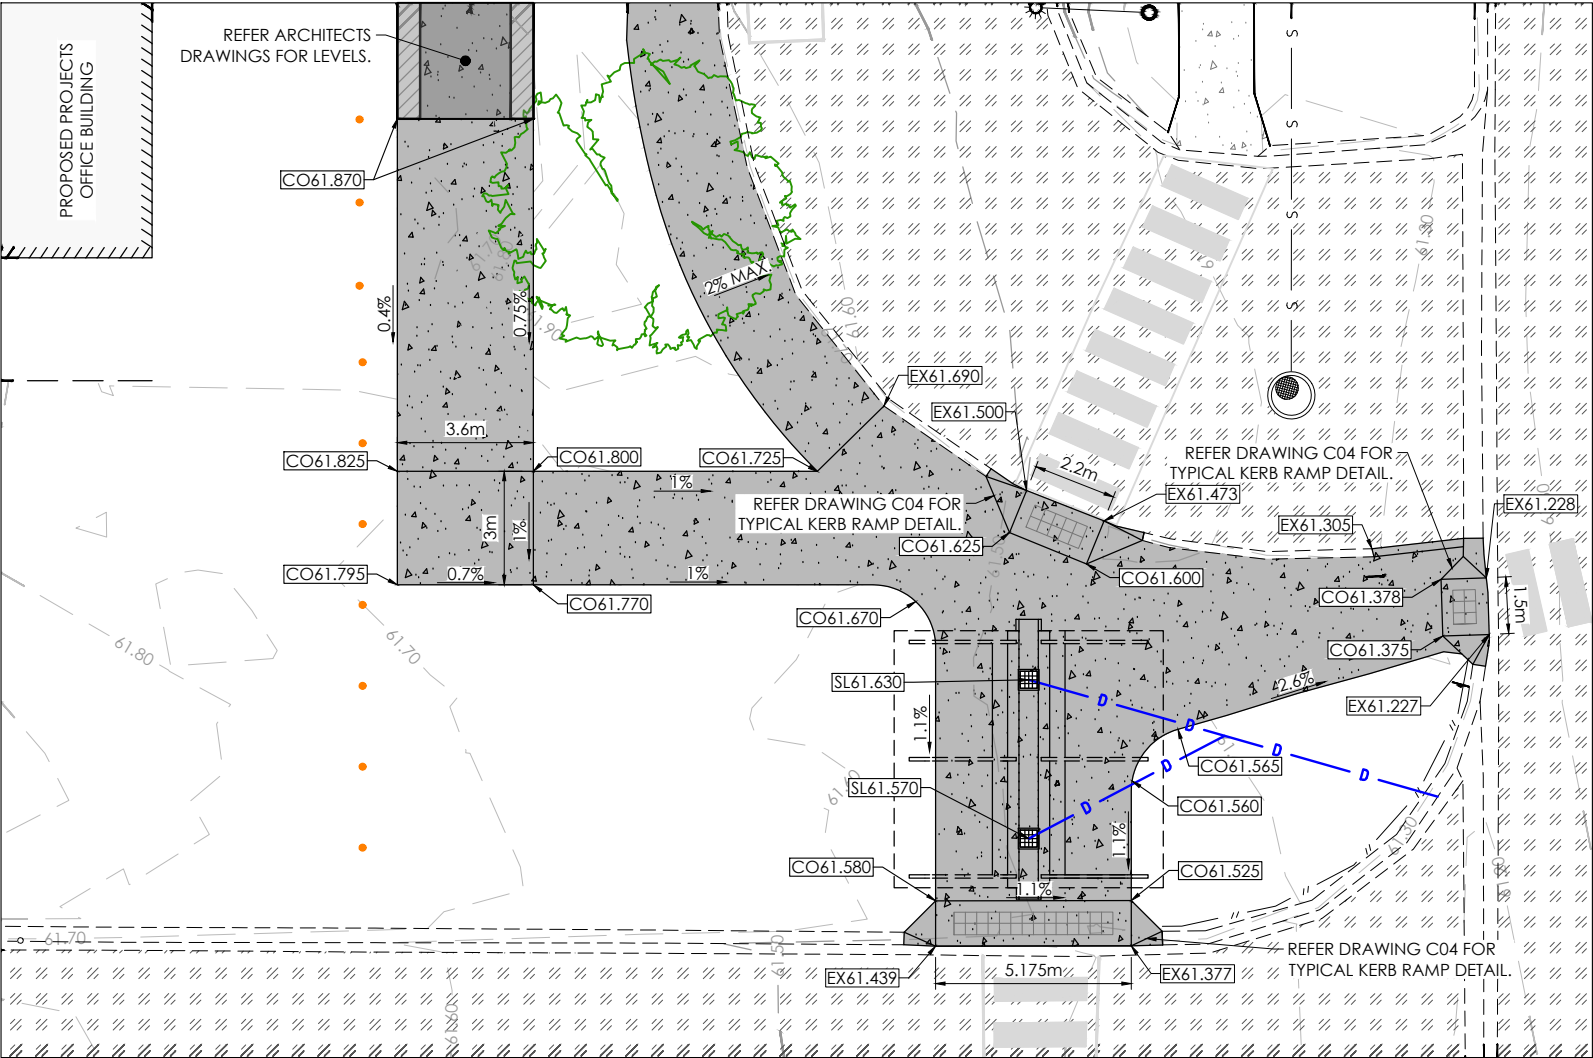

HAT STAND AREA LEVELS

SCALE 1:200

Client
STANWELL

Janes and Stewart Structures Pty Ltd
120 William Street | Po Box 1072
Rockhampton 4700
07 4922 1948
janes.and.stewart@jsstructures.com.au
ABN 30 620 233 025

JS² Janes and Stewart
Structural+Civil
CONSULTANTS

Project
STANWELL NEW PROJECTS OFFICE

SWITCHYARD ROAD,
STANWELL, QLD, 4702

TENDER
NOT FOR CONSTRUCTION PURPOSES

CONCRETE PATHWAY LEVELS PLAN

Project Number
25052

Title
Drawing
C06

Revision
A