

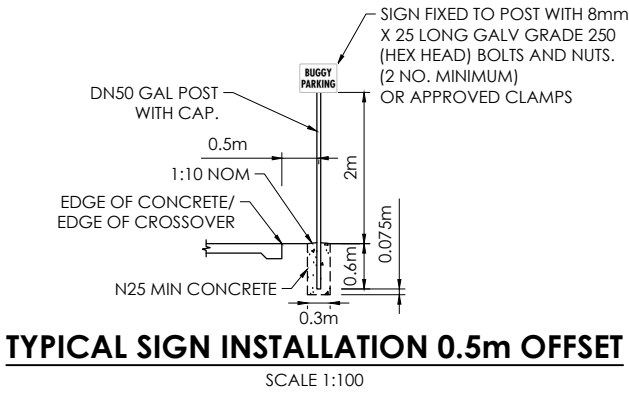
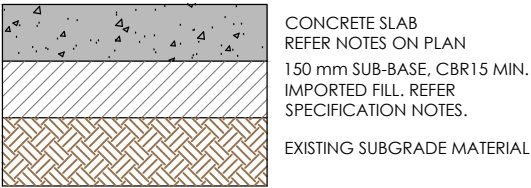
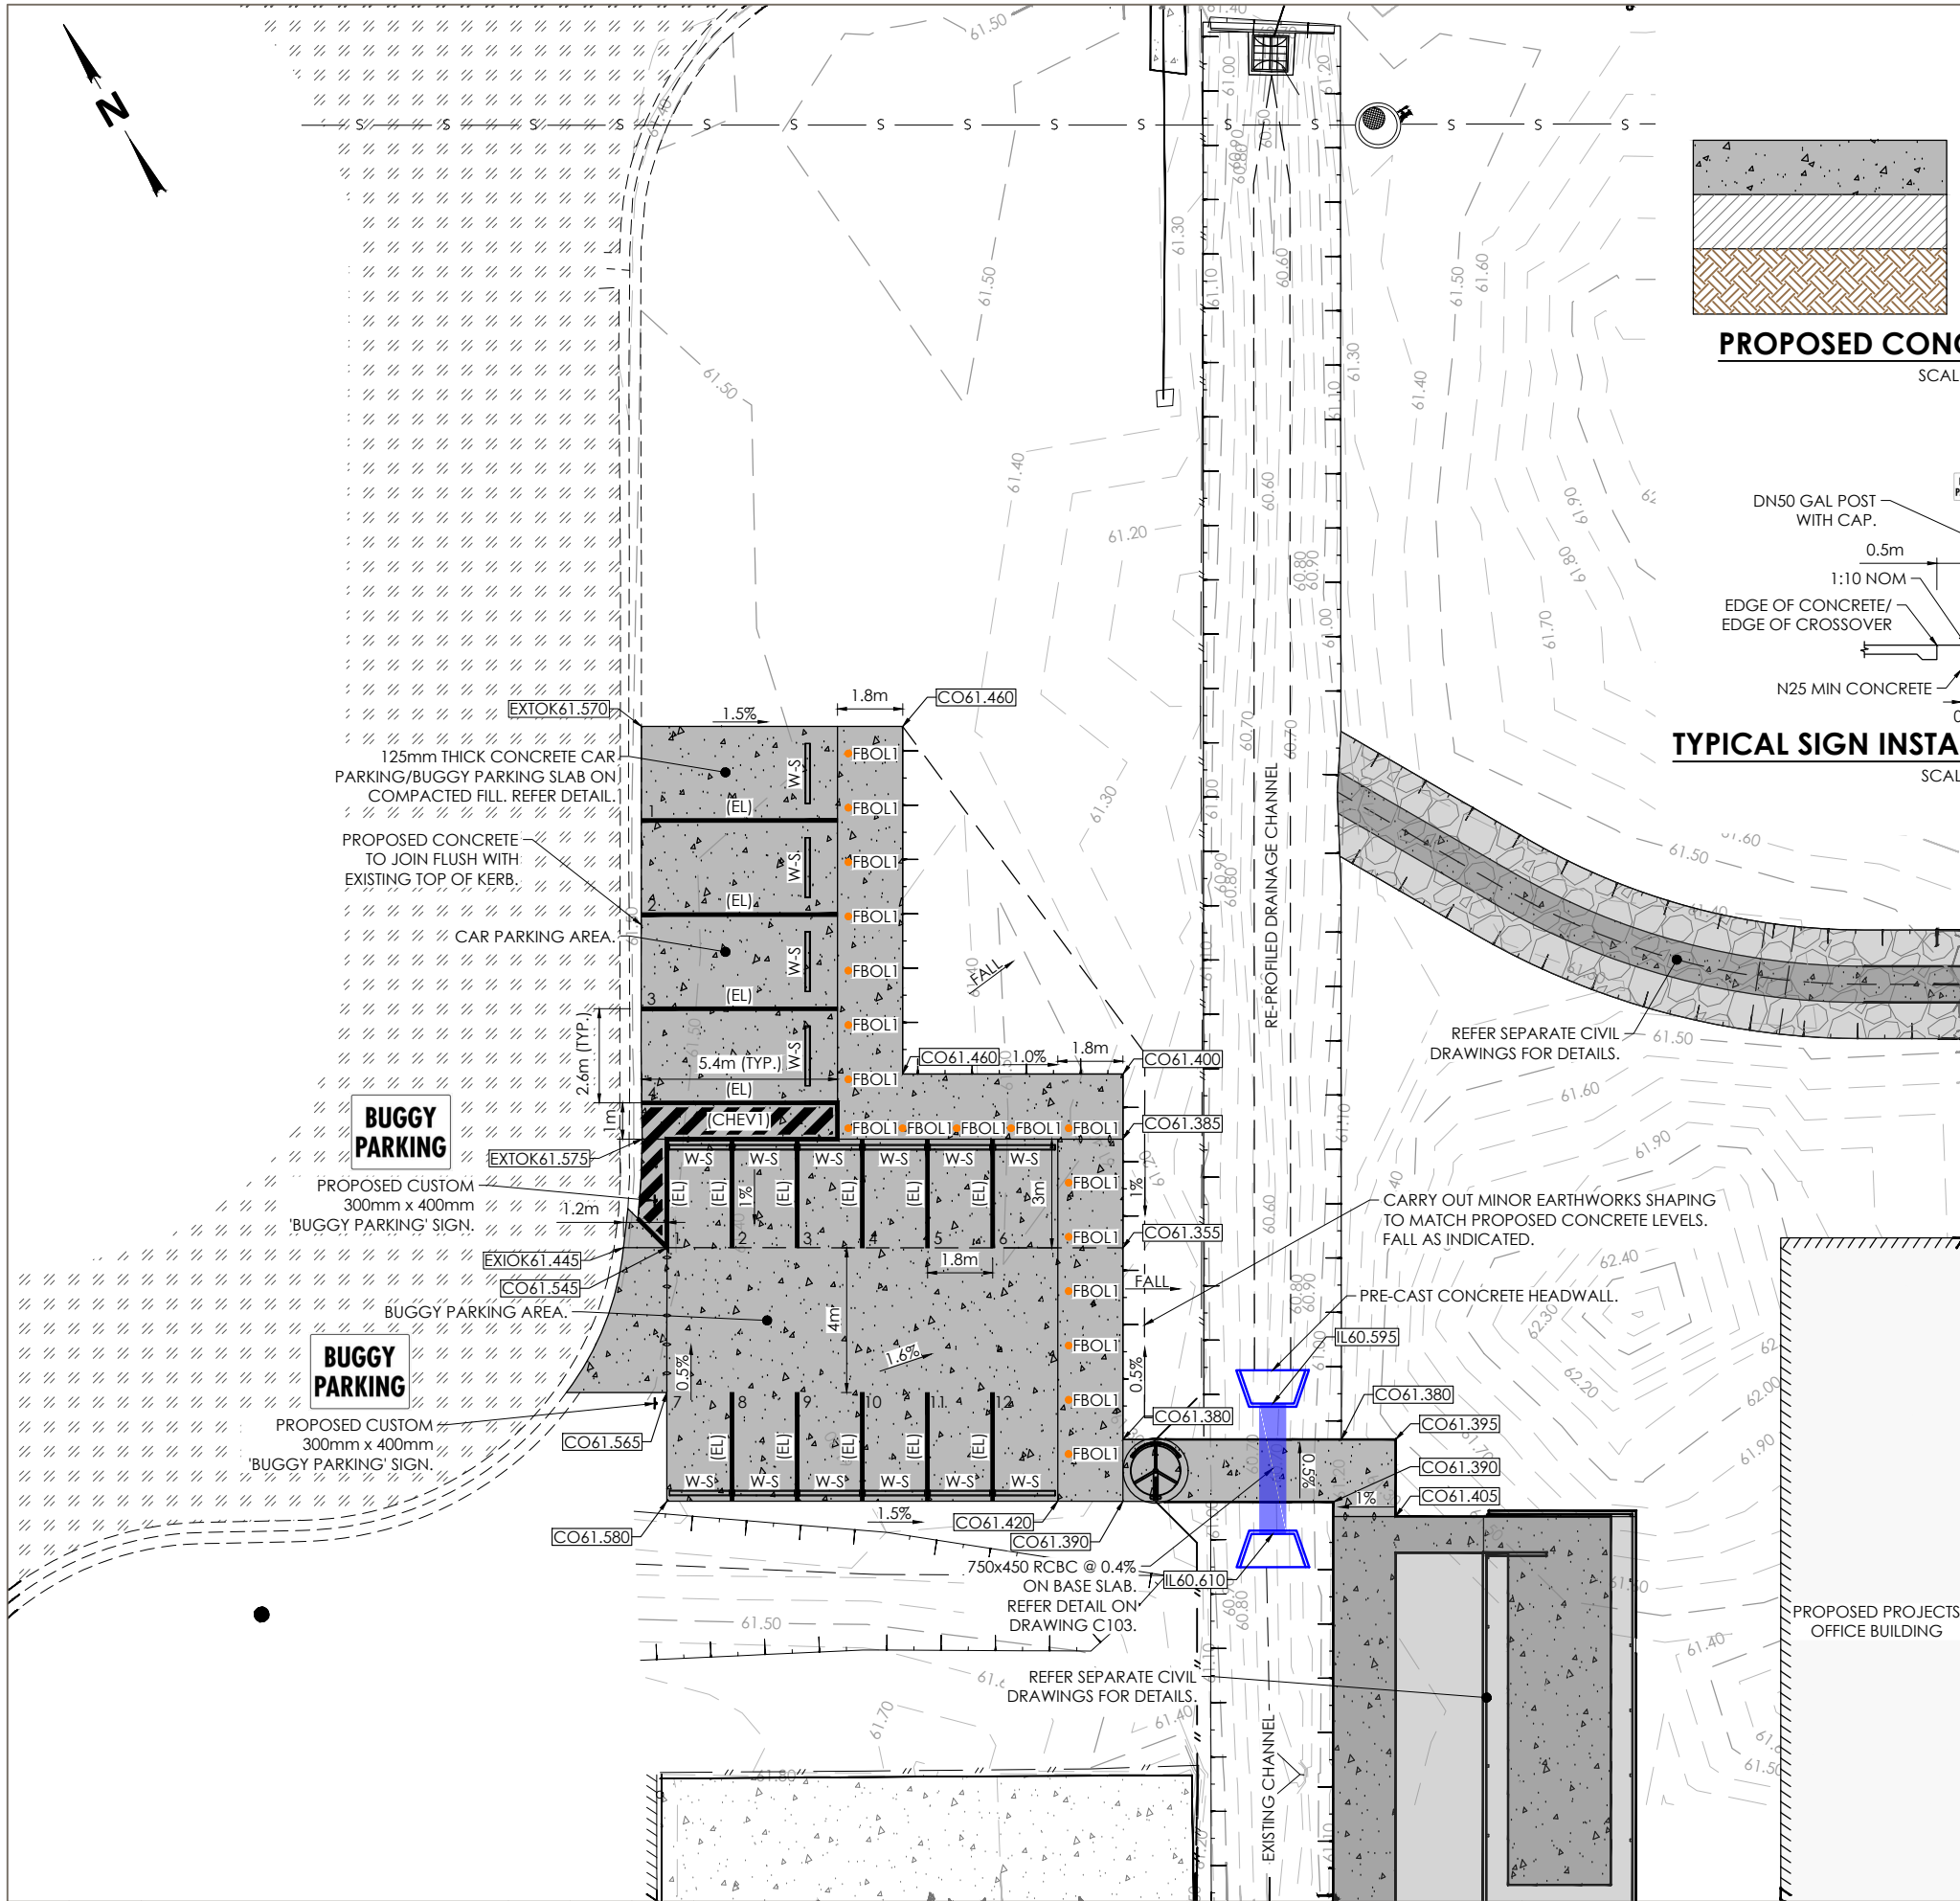
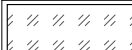
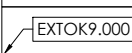
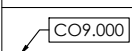
 
 
 
 
 
 
 
 
 
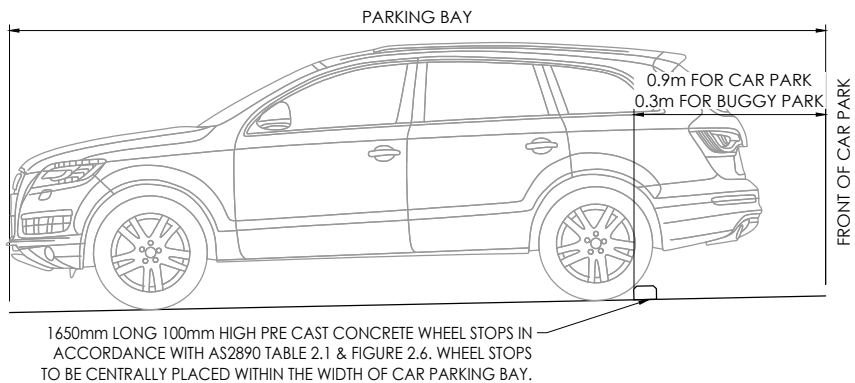


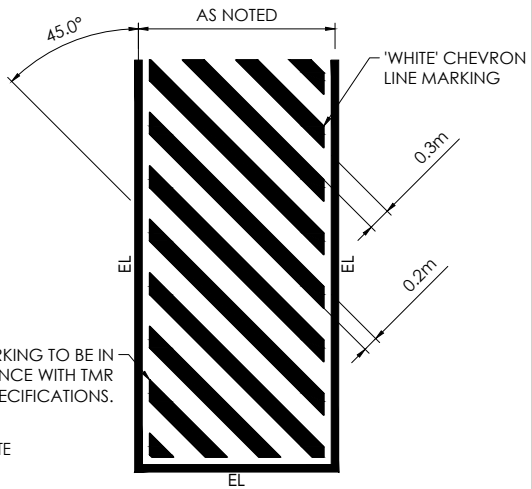


LEGEND		
	EXISTING SEAL AREA	
	EXISTING CONCRETE AREA	
	PROPOSED CONCRETE AREA	
	EXISTING INVERT OF KERB LEVEL	
	EXISTING TOP OF KERB LEVEL	
	PROPOSED FINISHED CONCRETE LEVEL	
	EXISTING SEWER MAIN & MANHOLE	
	EXISTING FENCE	
	EXISTING TOE OF BATTER	
	EXISTING TOP OF BATTER	
	EXISTING KERB	
	PROPOSED FENCE	
	PROPOSED TOE OF BATTER	
	PROPOSED TOP OF BATTER	
	PROPOSED CROWN LINE	
	PROPOSED STORMWATER DRAINAGE (SIZE AS NOTED)	
	EXISTING CONTOUR	
PAVEMENT MARKING LEGEND		
CODE	DESCRIPTION & DIMENSIONS	LINE WIDTH
(EL)	EDGE LINE 	100mm

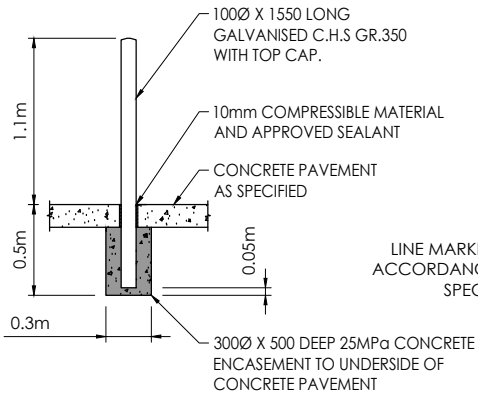

Revision	Date	Revision Description	Drawn	Design	Checked
1	03/09/2025	PRELIMINARY	JC	JC	MD
2	23/09/2025	DD ISSUE	JC	JC	MD
3	03/11/2025	50% CD ISSUE	JC	JC	MD
4	28/11/2025	90% CD ISSUE	JC	JC	MD
5	19/12/2025	100% CD ISSUE	JC	JC	MD
A	09/03/2026	FOR TENDER	JC	JC	MD

MATTHEW DENNIS R.P.E.Q.24862	
APPROVAL FOR ISSUE FOR AND ON BEHALF OF JANES AND STEWART STRUCTURES PTY LTD	

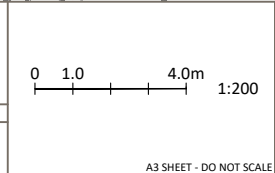

Client
STANWELL

Janes and Stewart Structures Pty Ltd
120 William Street | Po Box 1072
Rockhampton 4700
07 4922 1948
janes.and.stewart@jsstructures.com.au
ABN 30 620 233 025

REFER DRAWINGS C101, C102, C103 & C104 FOR VEHICLE PARKING DETAILS.

JS² Janes and Stewart Structural+Civil CONSULTANTS

Project
STANWELL NEW PROJECTS OFFICE

SWITCHYARD ROAD,
STANWELL, QLD, 4702

TENDER		Project Number
NOT FOR CONSTRUCTION PURPOSES		25052
Title		Drawing
Revision		C102
VEHICLE PARKING LAYOUT AND LINEMARKING PLAN AND DETAILS		A