


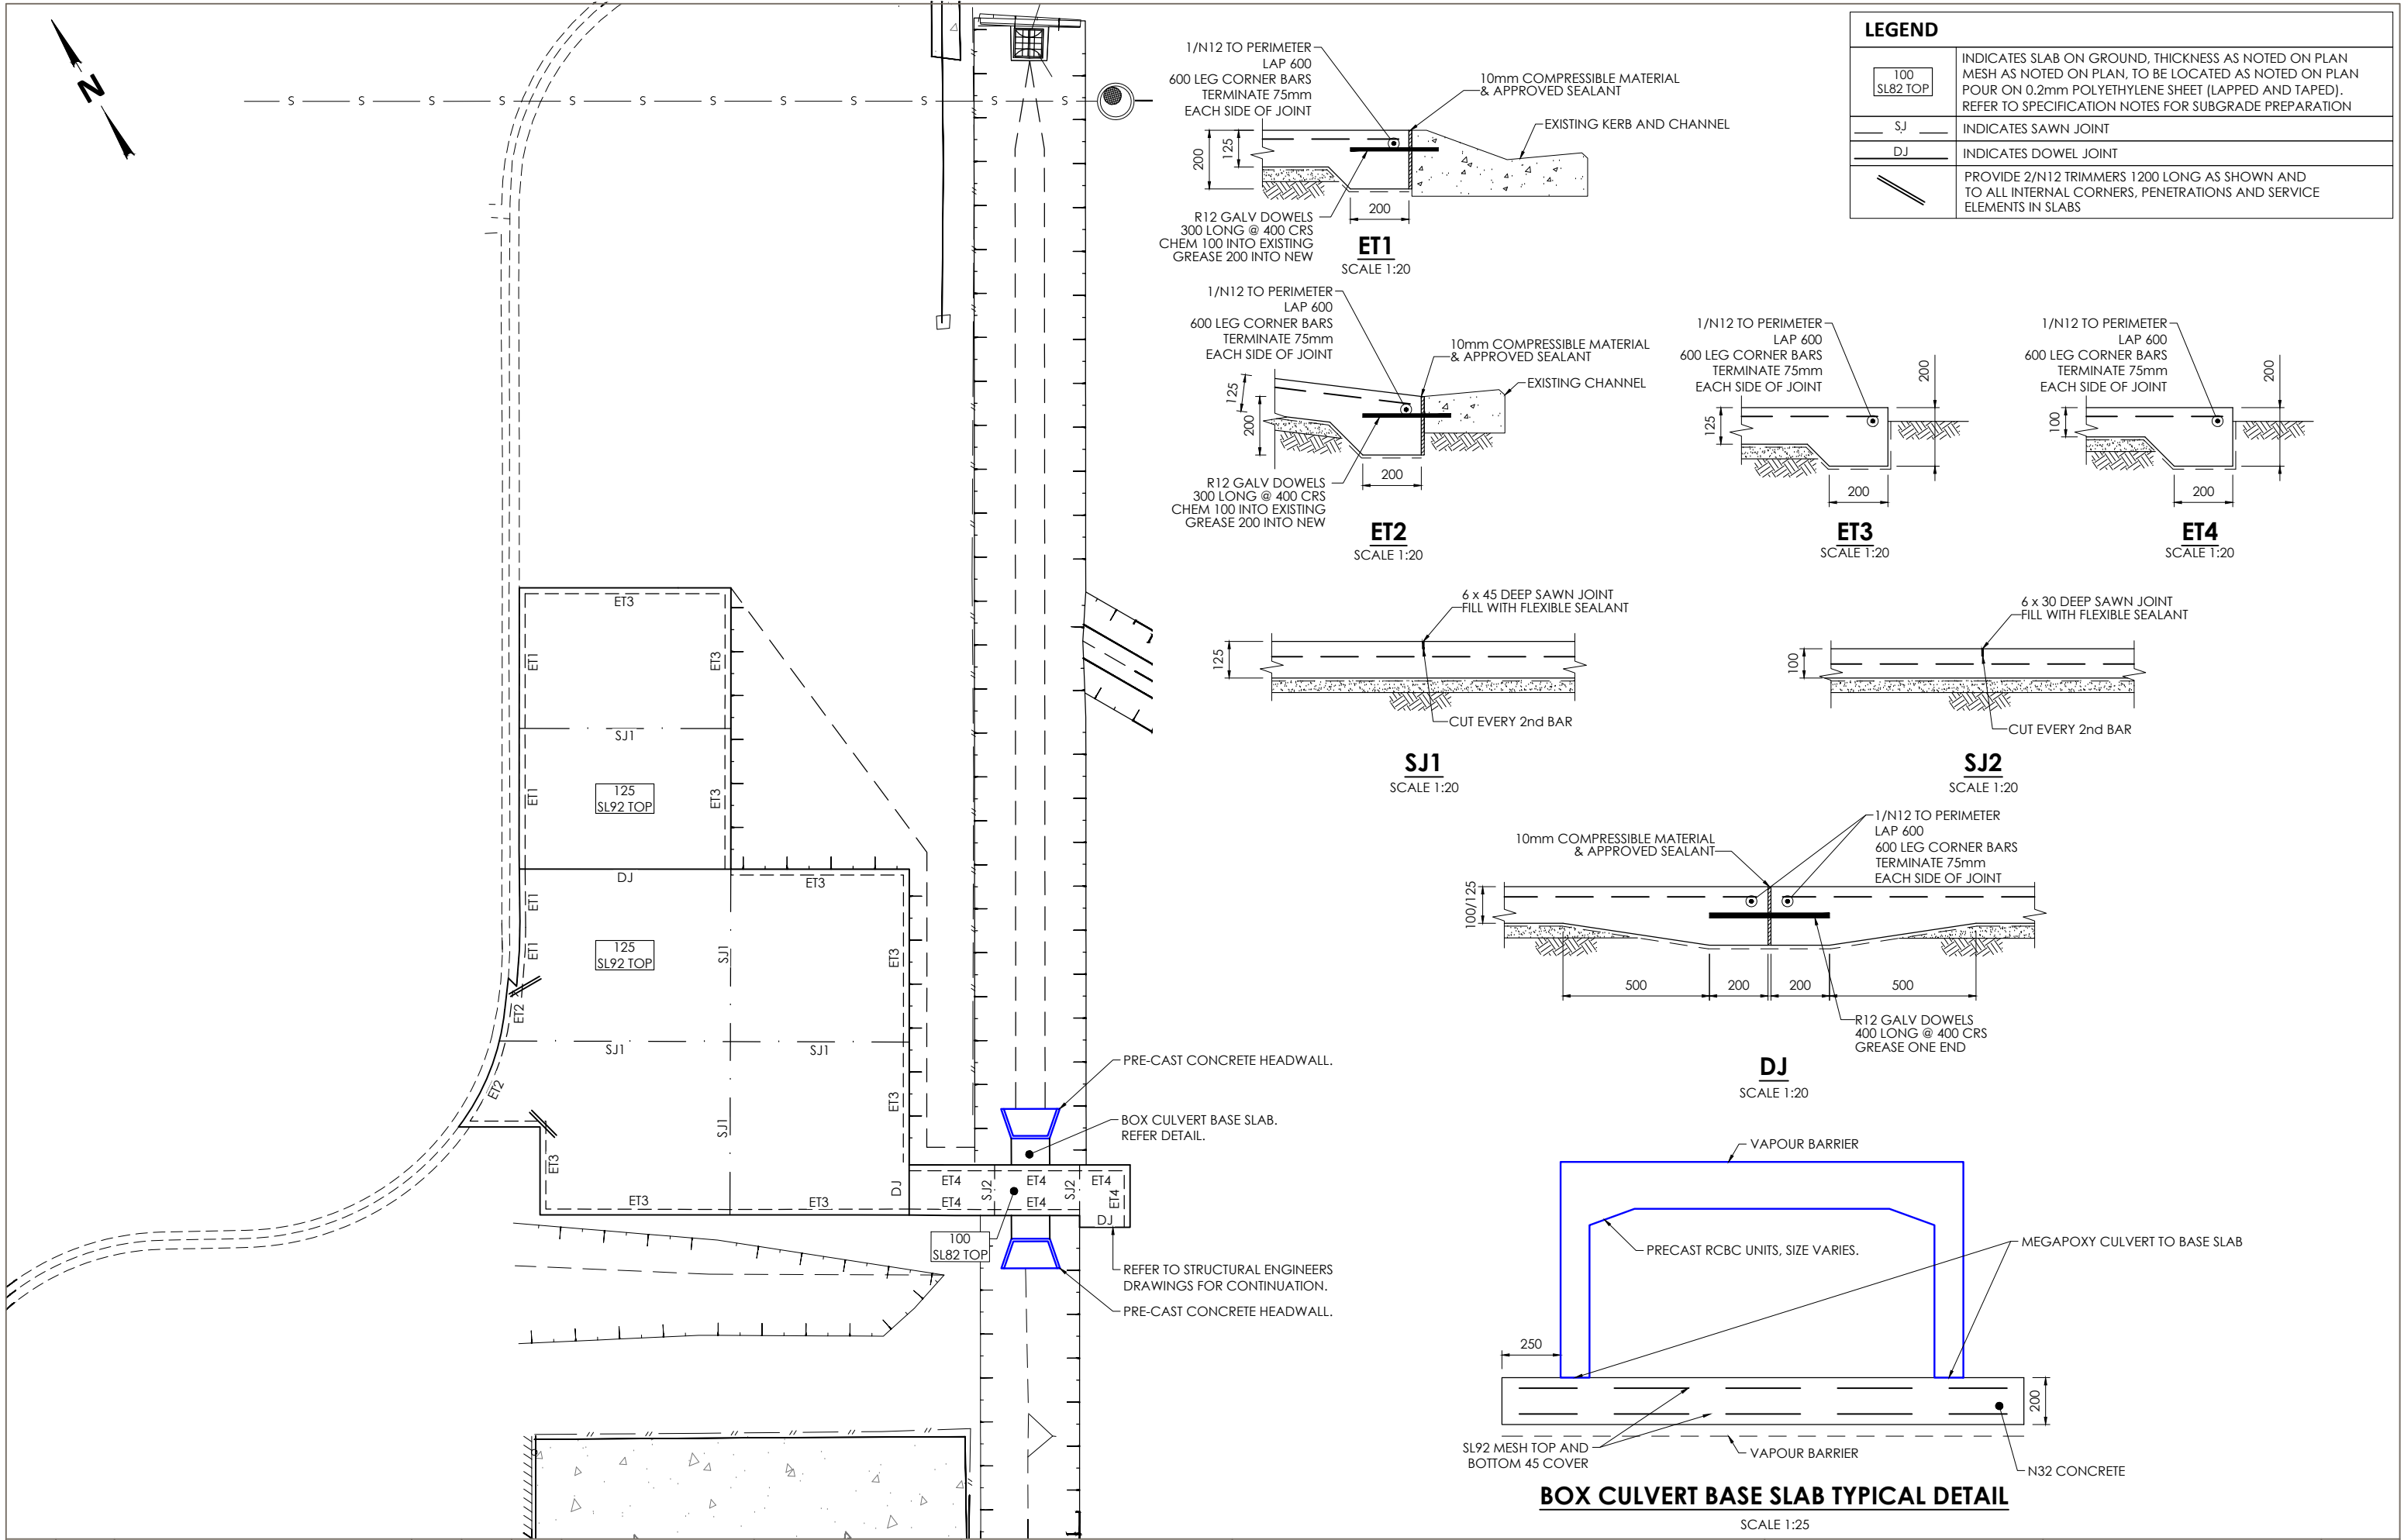

Revision	Date	Revision Description	Drawn	Design	Checked	Client STANWELL		Project STANWELL NEW PROJECTS OFFICE		TENDER NOT FOR CONSTRUCTION PURPOSES		Project Number 25052
1	03/11/2025	50% CD ISSUE	JC	JC	MD							
2	28/11/2025	90% CD ISSUE	JC	JC	MD							
3	19/12/2025	100% CD ISSUE	JC	JC	MD							
A	09/03/2026	FOR TENDER	JC	JC	MD							
						MATTHEW DENNIS R.P.E.Q.24862		SWITCHYARD ROAD, STANWELL, QLD, 4702		VEHICLE PARKING CONCRETE SLAB PLAN AND DETAILS		Drawing C103
						APPROVAL FOR ISSUE FOR AND ON BEHALF OF JANES AND STEWART STRUCTURES PTY LTD						
												Revision A

01.04.2025

1.04.2025

4.0m

1:200

A3 SHEET - DO NOT SCALE

Janes and Stewart Structures Pty Ltd

120 William Street | Po Box 1072

Rockhampton 4700

07 4922 1948

janes.and.stewart@jsstructures.com.au

ABN 30 620 233 025

JS²

Janes and Stewart
Structural+Civil
CONSULTANTS