


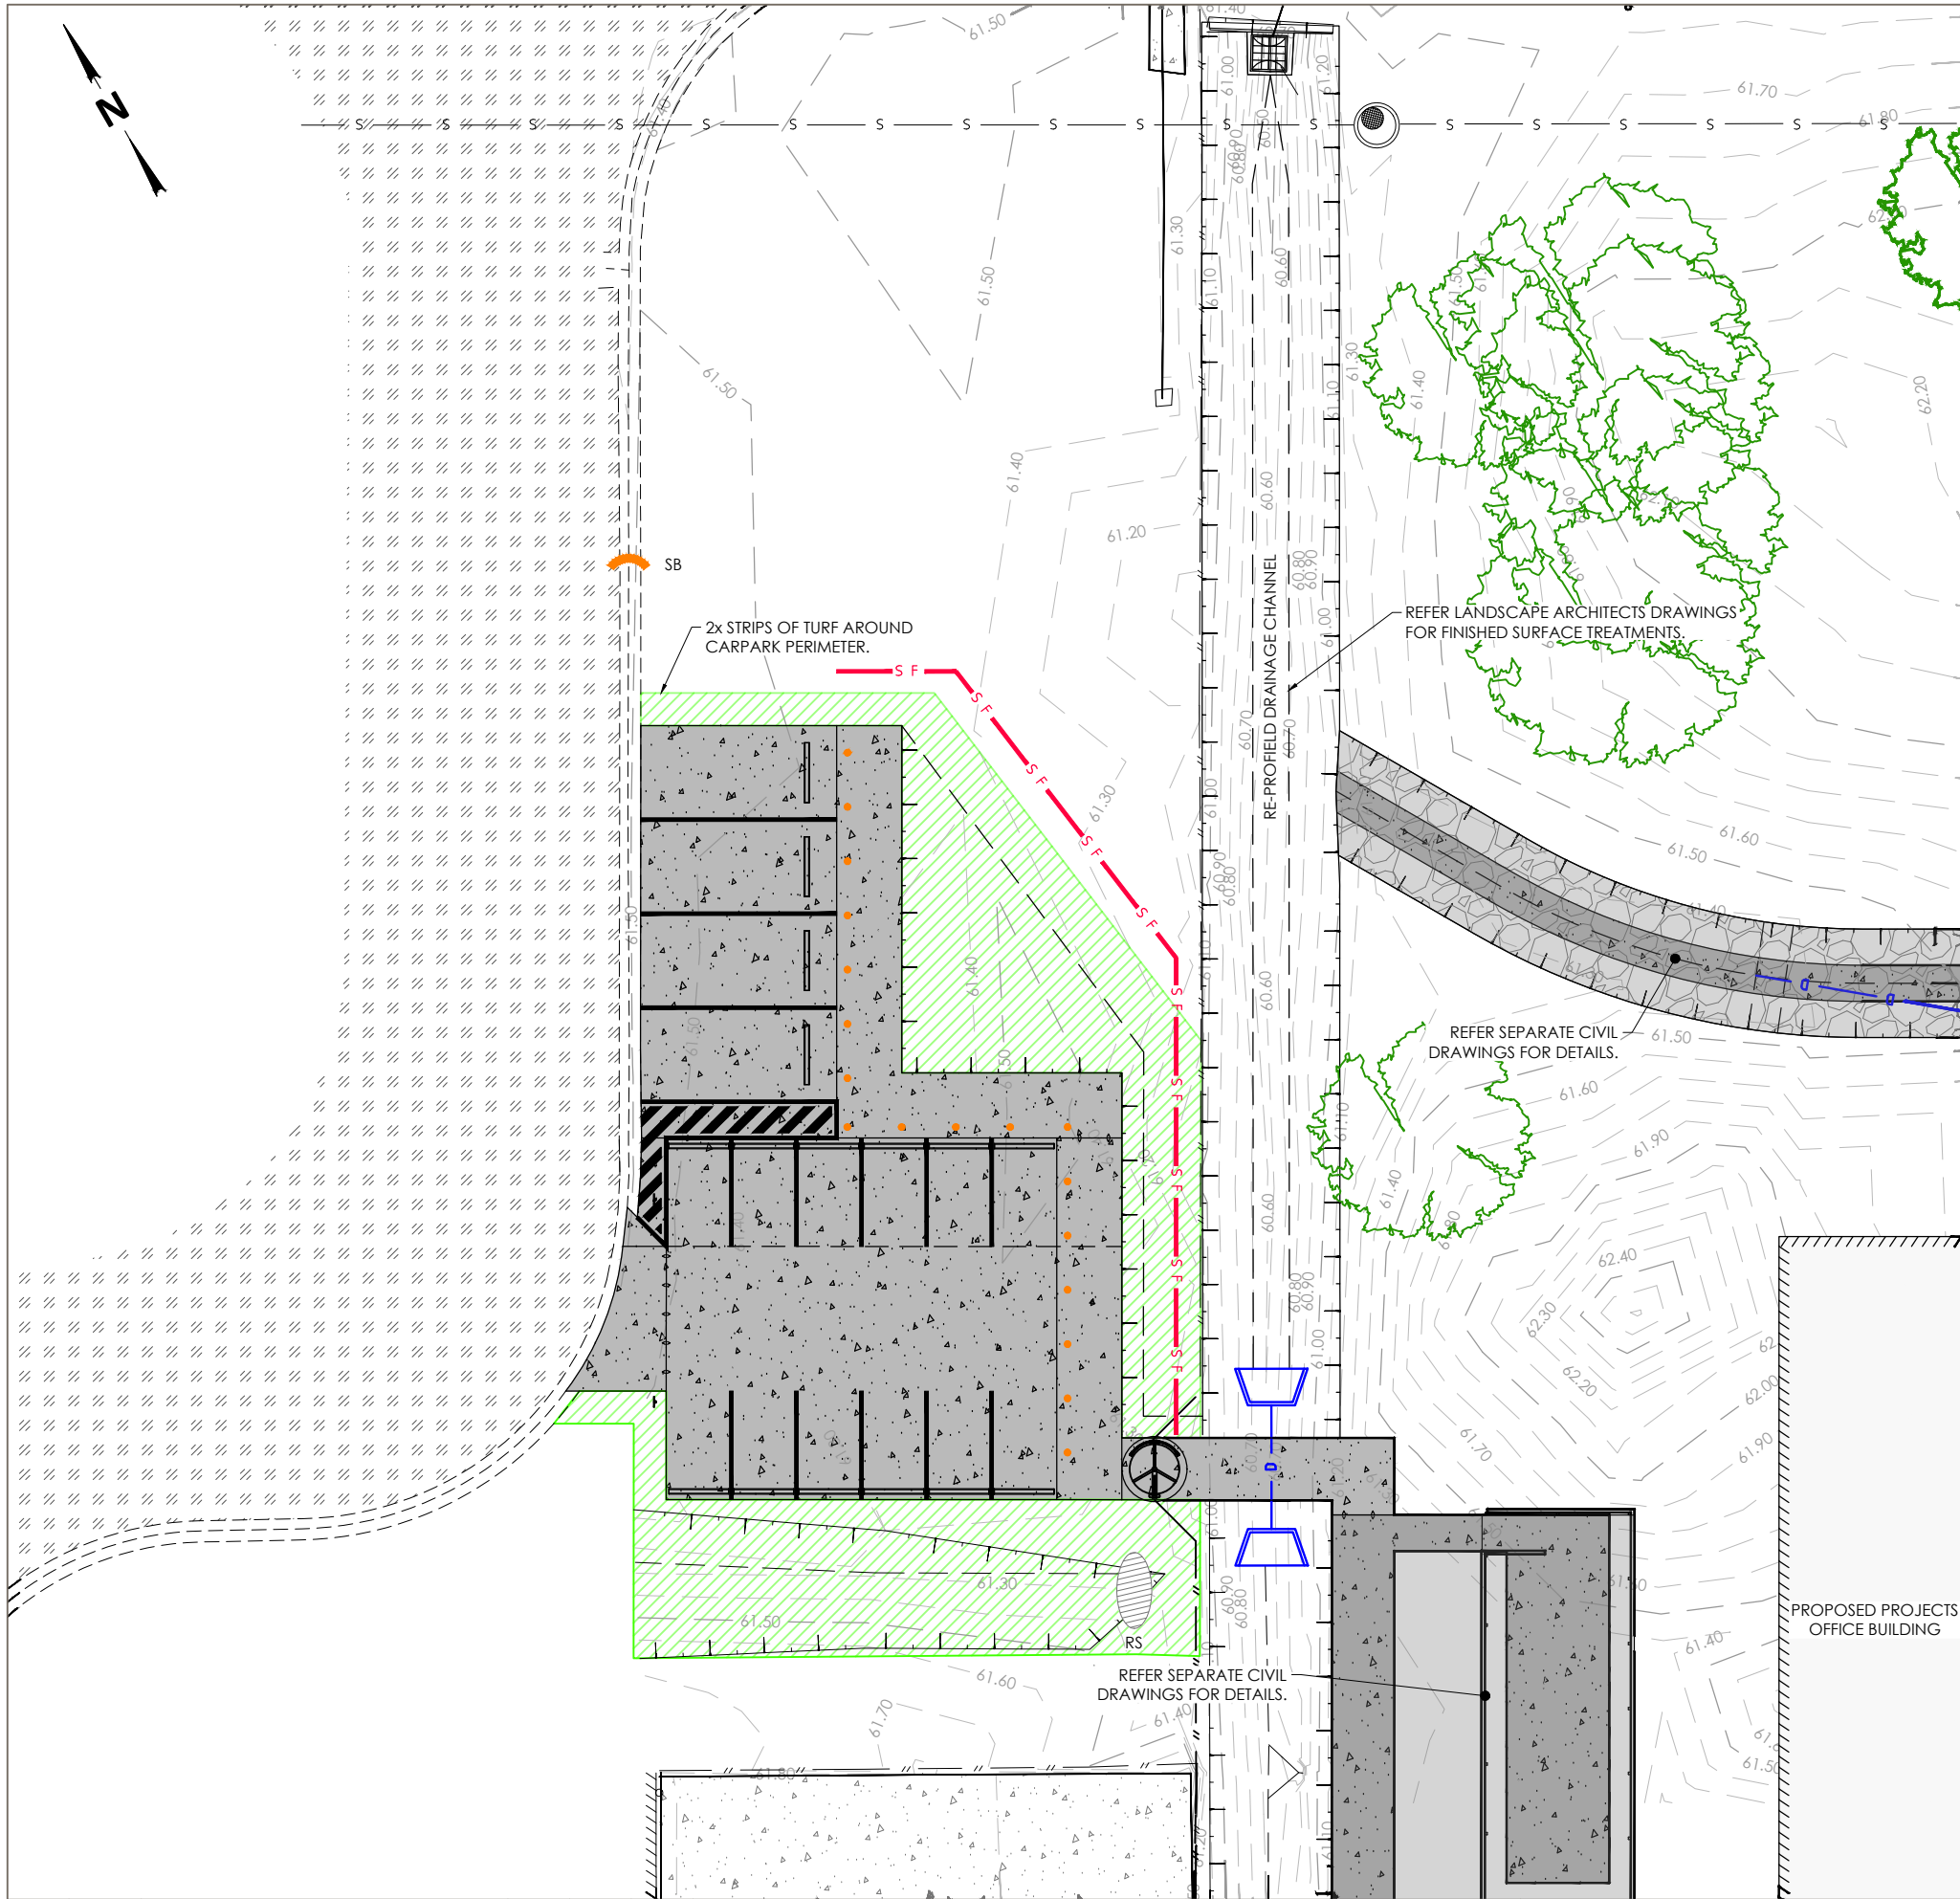


LEGEND

	EXISTING SEAL AREA
	EXISTING CONCRETE AREA
	PROPOSED TURF AREA
	TEMP. ROCK SPALL CHECK DAM (RS)
	EXISTING TOE OF BATTER
	EXISTING TOP OF BATTER
	PROPOSED TOE OF BATTER
	PROPOSED TOP OF BATTER
	TEMP. COIR LOG (CL)
	TEMP. SILT FENCE (SF)
	TEMP. SAND BAG SEDIMENT TRAP (SB)
	EXISTING CONTOUR


NOTES

- REFER TO SPECIFICATION NOTES ON DRAWING C101 FOR EROSION AND SEDIMENT CONTROL REQUIREMENTS.
- PROVIDE ENTRY / EXIT SEDIMENT TRAPS AT ALL VEHICLE ENTRY/EXIT POINTS

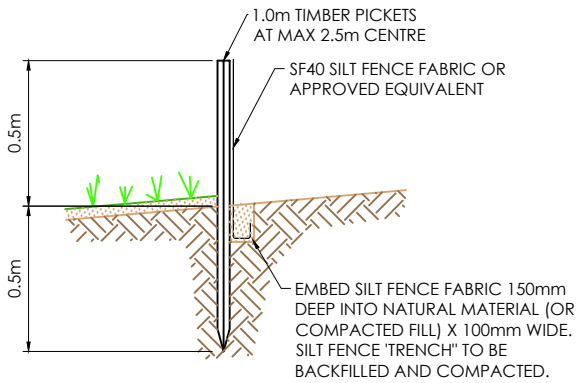


SILT FENCE (SF)

NOT TO SCALE

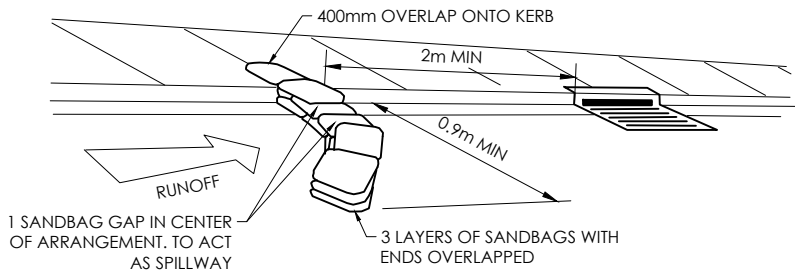

SANDBAG KERB INLET SEDIMENT TRAP (SB)

NOT TO SCALE

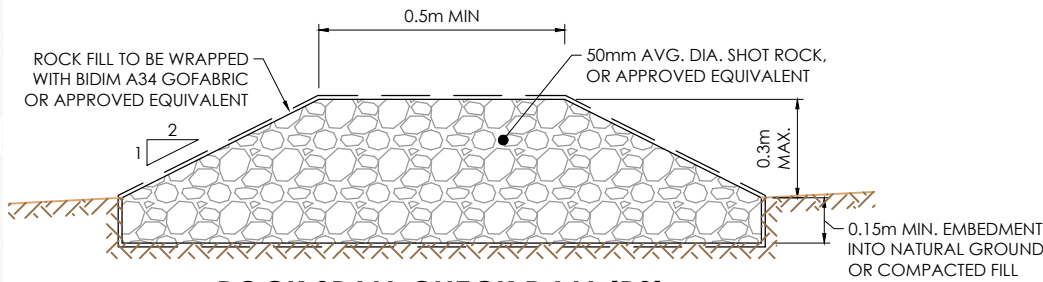

ROCK SPALL CHECK DAM (RS)

NOT TO SCALE

Revision	Date	Revision Description	Drawn	Design	Checked
1	03/09/2025	PRELIMINARY	JC	JC	MD
2	23/09/2025	DD ISSUE	JC	JC	MD
3	03/11/2025	50% CD ISSUE	JC	JC	MD
4	28/11/2025	90% CD ISSUE	JC	JC	MD
5	19/12/2025	100% CD ISSUE	JC	JC	MD
A	09/03/2026	FOR TENDER	JC	JC	MD

MATTHEW DENNIS R.P.E.Q.24862
APPROVAL FOR ISSUE FOR AND ON BEHALF OF
JANES AND STEWART STRUCTURES PTY LTD

0 1.0 4.0m 1:200

A3 SHEET - DO NOT SCALE

Client
STANWELL

Janes and Stewart Structures Pty Ltd
120 William Street | Po Box 1072
Rockhampton 4700
07 4922 1948
janes.and.stewart@jsstructures.com.au
ABN 30 620 233 025

JS² Janes and Stewart
Structural+Civil
CONSULTANTS

Project
STANWELL NEW PROJECTS OFFICE

**SWITCHYARD ROAD,
STANWELL, QLD, 4702**

TENDER
NOT FOR CONSTRUCTION PURPOSES

VEHICLE PARKING EROSION AND
SEDIMENT CONTROL PLAN AND DETAILS

Project Number
25052

Title
C104

Revision
A