

STANWELL POWER STATION
STANWELL, QLD 4702
NEW OFFICE CONSTRUCTION
CIVIL WORKS

SHEET LIST TABLE

Sheet Number	Sheet Title
100	COVER SHEET AND LOCALITY
101	EXISTING LAYOUT AND SERVICES
102	GENERAL DESIGN LAYOUT
103	ANNOTATED SECTIONS AND PAVEMENT DETAIL
104	BULK EARTHWORKS AND SUBGRADE SURFACE
105	DRAINAGE LAYOUT
106	LANEWAY (MC01) SETOUT AND LONGSECTION
107	CONCRETE FEATURES SETOUT PLAN
108	LINEMARKING AND SIGNAGE

GENERAL NOTES

1. ALL PROFESSIONAL ACTIVITIES TO BE IN ACCORDANCE WITH THE RELEVANT SECTIONS OF THE; QUEENSLAND BUILDING ACT, QUEENSLAND WORKPLACE HEALTH AND SAFETY ACT AND CODES, RELEVANT CODES OF PRACTICE, NATIONAL CONSTRUCTION CODE AND AUSTRALIAN STANDARDS AS WELL AS ACCEPTED INDUSTRY BEST PRACTICES AND THESE STRUCTURAL DRAWINGS.
2. ALL PROFESSIONAL ACTIVITIES TO BE PERFORMED IN A SAFE AND RESPONSIBLE MANNER BY SUITABLY QUALIFIED AND LICENSED SUB CONTRACTORS AND CONTRACTORS.
3. THESE CIVIL DRAWINGS HAVE BEEN BASED ON THE BEST INFORMATION AVAILABLE DURING THE DESIGN PROCESS HOWEVER ALL EXISTING CIVIL ELEMENTS SHOULD BE VERIFIED BY THE CONTRACTOR PRIOR TO COMMENCING WORKS. ANY DISCREPANCIES SHALL BE REFERRED THE CIVIL ENGINEER.
4. THESE CIVIL DRAWINGS SHALL BE READ IN CONJUNCTION WITH ALL OTHER CONSULTANTS DRAWINGS AND SPECIFICATIONS FOR RELEVANT INFORMATION. ANY DISCREPANCIES SHALL BE REFERRED TO THE CIVIL ENGINEER PRIOR TO COMMENCING RELEVANT WORKS.
5. ALL SET OUT, LEVELS AND DIMENSIONS SHALL BE IN ACCORDANCE WITH THE THESE DRAWINGS AND SITE CONFIRMED.
6. ALL PROPRIETARY PRODUCTS ARE TO BE USED, APPLIED AND/OR INSTALLED IN ACCORDANCE WITH MANUFACTURER'S SPECIFICATIONS, DETAILS AND GUIDELINES.
7. LOCATION OF ALL EXISTING IN-GROUND AND ABOVE GROUND SERVICES TO BE CONFIRMED BY THE CONTRACTOR. ALL EXISTING SERVICES SHOWN IN THESE DRAWINGS ARE INDICATIVE ONLY.
8. ANY DEVIATIONS OR ALTERATIONS TO THESE DRAWINGS SHALL BE APPROVED BY CERTIFYING ENGINEER.

SURVEY

1. GROUND FEATURE SURVEY BY OTHERS. PATCOL GROUP PTY LTD SHALL NOT ACCEPT LIABILITY RELATED TO ACCURACY OF DATA PROVIDED.
2. THIS DESIGN IS BASED ON INCOMPLETE SURVEY; REFER TO PLAN 101 FOR LOCATION OF SURVEY EXTENT.
3. SURVEY GRID IS MGA20 ZONE 56. AHD DATUM.

SUPERVISION

1. SUPERVISION TO BE DETERMINED BY CLIENT SUPERVISOR AND CERTIFYING RPEQ ENGINEER. THE CONTRACTOR SHALL MAINTAIN SUFFICIENT DOCUMENTATION TO RECORD THE CONSTRUCTION & QUALITY OF THE WORKS, INCLUDING BUT NOT LIMITED TO:
 - 1.1. SURVEY
 - 1.1. INSPECTION TEST PLANS
 - 1.2. MATERIAL TESTING
 - 1.3. AS BUILT REDLINE MARKUPS AND AS BUILT SURVEY LEVELS
2. THE CONTRACTOR SHALL CONFIRM AN INSPECTION REGIME WITH THE CIVIL ENGINEER PRIOR TO COMMENCING WORKS. ADEQUATE NOTICE SHALL BE GIVEN FOR CONSTRUCTION HOLD AND WITNESS POINTS REQUIRED THROUGH CONSTRUCTION,

REFERENCE SPECIFICATION


1. CMDG-D-010 EXCAVATION, BEDDING AND BACKFILLING OF CONCRETE/REINFORCED FIBRE FLEXIBLE DRAINAGE PIPES
2. CMDG-D-020 PRECAST STORMWATER INLET INSTALLATION DETAILS
4. CMDG-R-042 COMMERCIAL ACCESS
5. CMDG-R-050 KERB RAMP DETAILS
6. CMDG-R-060 STANDARD KERB AND CHANNEL PROFILES
7. MEGAFLW INSTALLATION GUIDE (GEOFABRICS AUSTRALIA)

SITE PREPARATION.

1. AN EROSION & SEDIMENT CONTROL PLAN IS THE RESPONSIBILITY OF THE CONTRACTOR AND MUST BE APPROVED PRIOR TO COMMENCEMENT OF WORKS.
2. EROSION & SEDIMENT CONTROLS SUCH AS SILT FENCES, CUT-OFF & CONTOUR DRAINS, SEDIMENT TRAPS ARE TO BE INSTALLED. CHANGES IN WORK OR ENVIRONMENTAL CONDITIONS SHOULD SEE THE MANAGEMENT PLAN REVIEWED.
3. ALL STOCKPILES ARE TO BE LOCATED AWAY FROM NATURAL OVERLAND FLOW PATHS.



LOCALITY
SCALE 1:2000

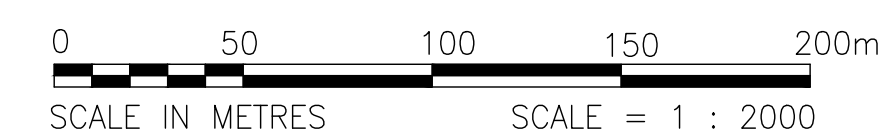[illegible]

	FINISHED SURFACE DESIGN CONTOURS (0.2 m)
	NEW SURFACE DRAIN
	NEW SUBSOIL DRAIN
	NEW STORMWATER PIPE
	EXISTING STORMWATER PIPE
	NEW CONCRETE PATH
	NEW CONCRETE MOW STRIP
	NEW CONCRETE KERB / APRON / FLOOR SLAB
	NEW ASPHALT
	NEW GRASS / LANDSCAPING

MAKE ALL SERVICE COVERS FLUSH WITH
FINISHED SURFACE.
CHECK ENTIRE SITE FOR EXISTING
SERVICES AND DISCUSS OPTIONS WITH
SITE SUPERINTENDENT.

NEW PAINTED
LEVEL CROSSING

NEW ASPHALT PARKING
AREA. 12 BAYS.

REFER STRUCTURAL
DRAWING 25-592_A4
FOR EXTERNAL
CONCRETE DETAILS

COAL ROAD

MOUNTABLE
KERB

- EXTENT OF GROUND SURVEY DATA

NEW MOUNTABLE
KERB & CHANNEL

NEW ROAD GULLY
PIT

NEW 375ø
STORMWATER RCP

NOTE

1. THIS SHEET IS PROVIDED FOR A GENERAL OVERVIEW OF NEW CIVIL WORKS. PROCEED TO DETAILED PLANS FOR DIMENSIONS, SETOUT, AND SPECIFIC WORK INSTRUCTION.

FFI 62.100 mRI

MEGAFLO® 170mm —
PAVEMENT DRAIN

ALIGNMENT MC01—
LANEWAY

V-DRAIN —
SURFACE
CHANNEL

CONCRETE MOW STRIP

CONCRETE MOW STRIP

MCO

CURVE WIDENED -
FOR VEHICLE
TURN PATH

EXTENT OF GROUND SURVEY DATA

MEGAFLO® 170mm
PAVEMENT DRAIN
UNDER KERB

TURBINE ROAD





GENERAL DESIGN LAYOUT



SCALE 1:150

0 1 2.5 5 10 15m
SCALE IN METRES SCALE = 1 : 150

[illegible]

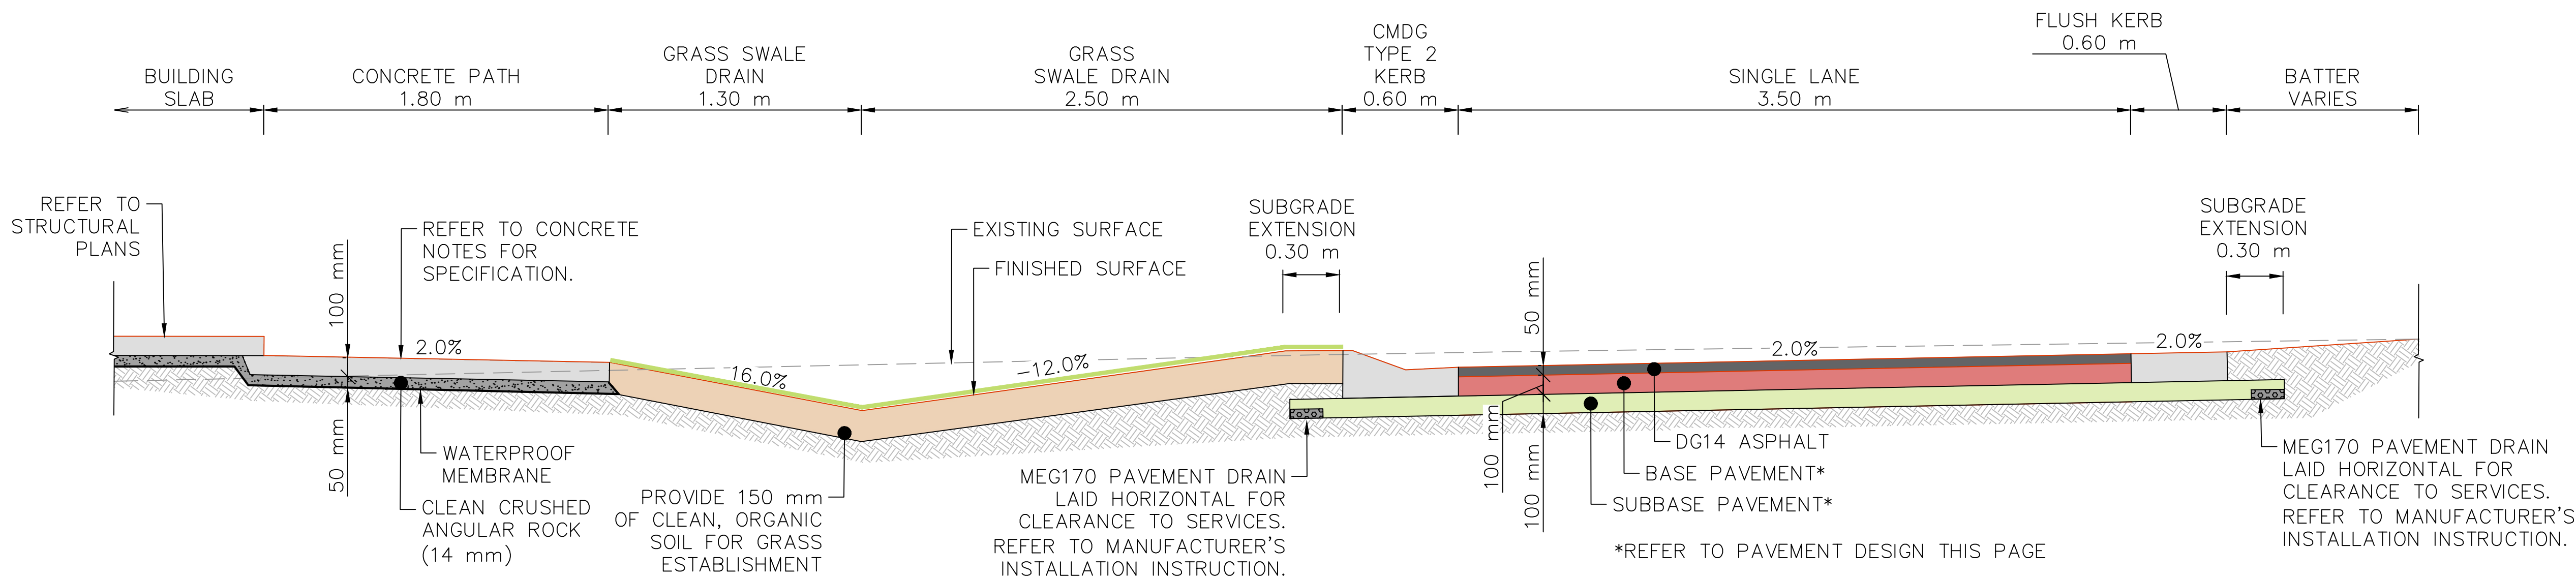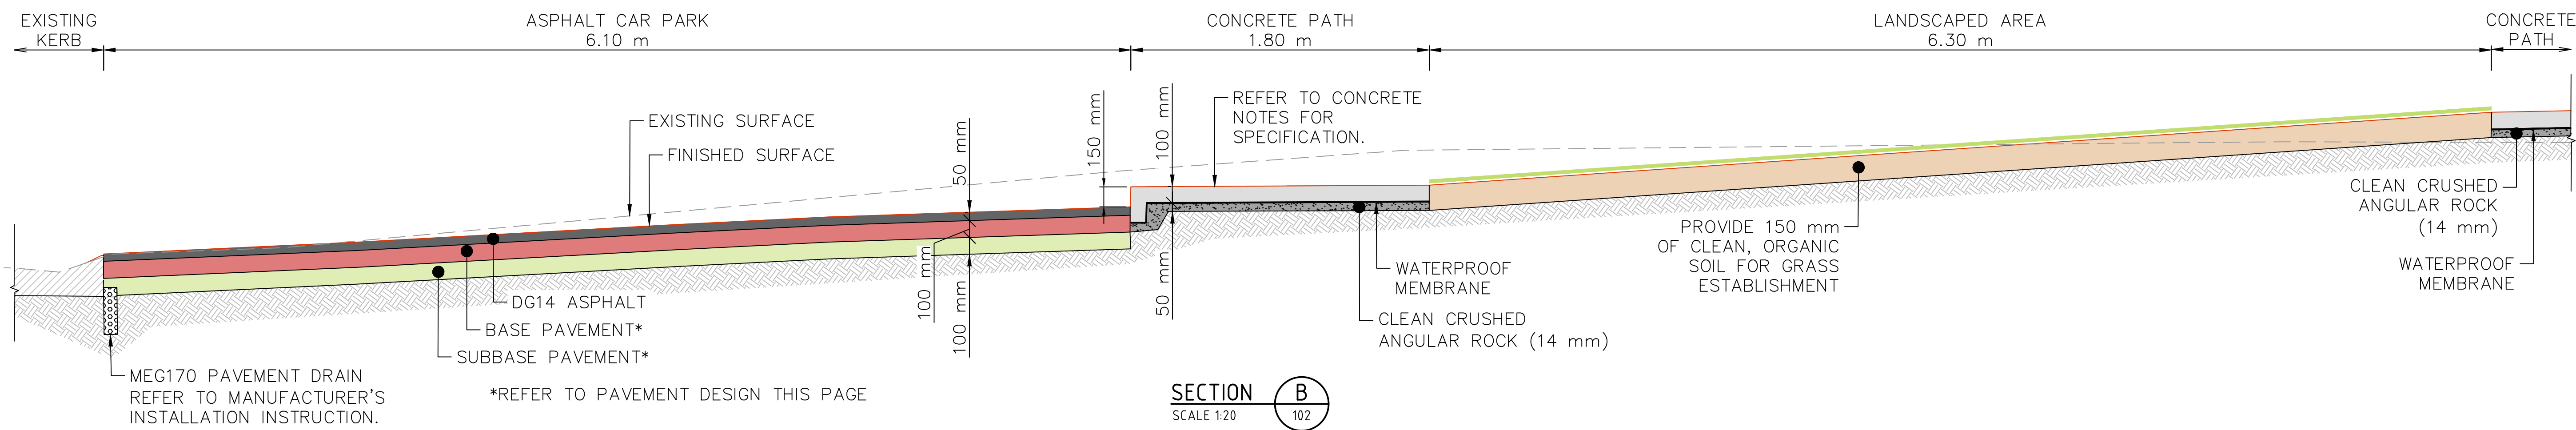

PAVEMENT VOLUMES		
ROAD BASE	54	m³
ROAD SUB BASE	71	m³

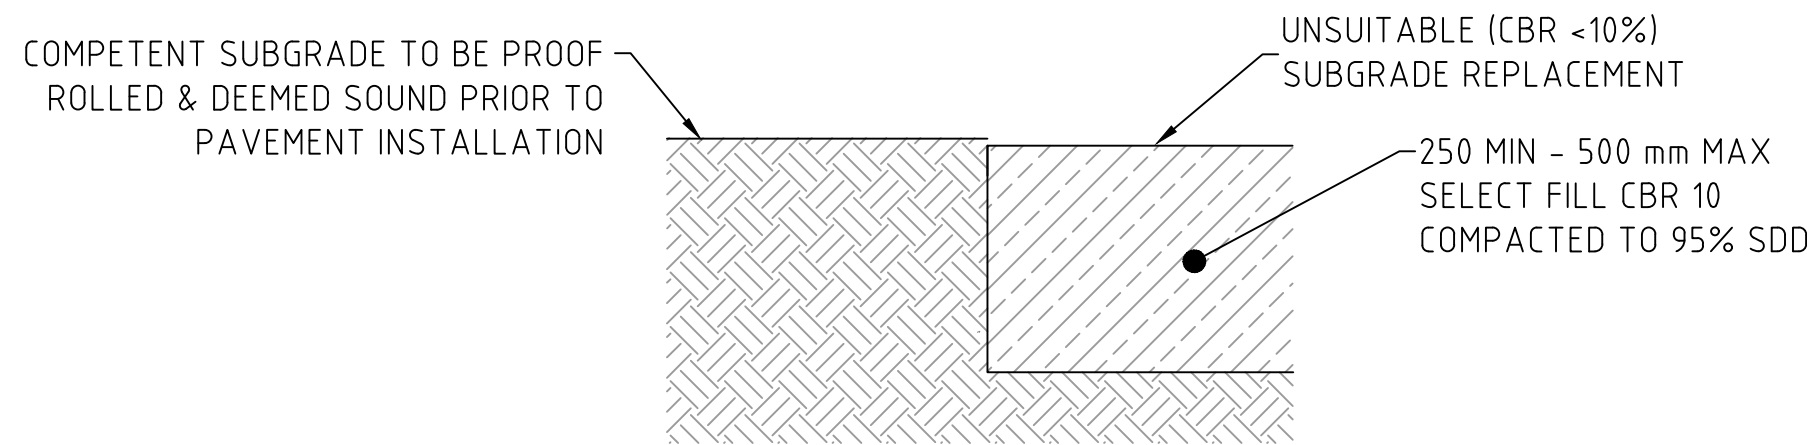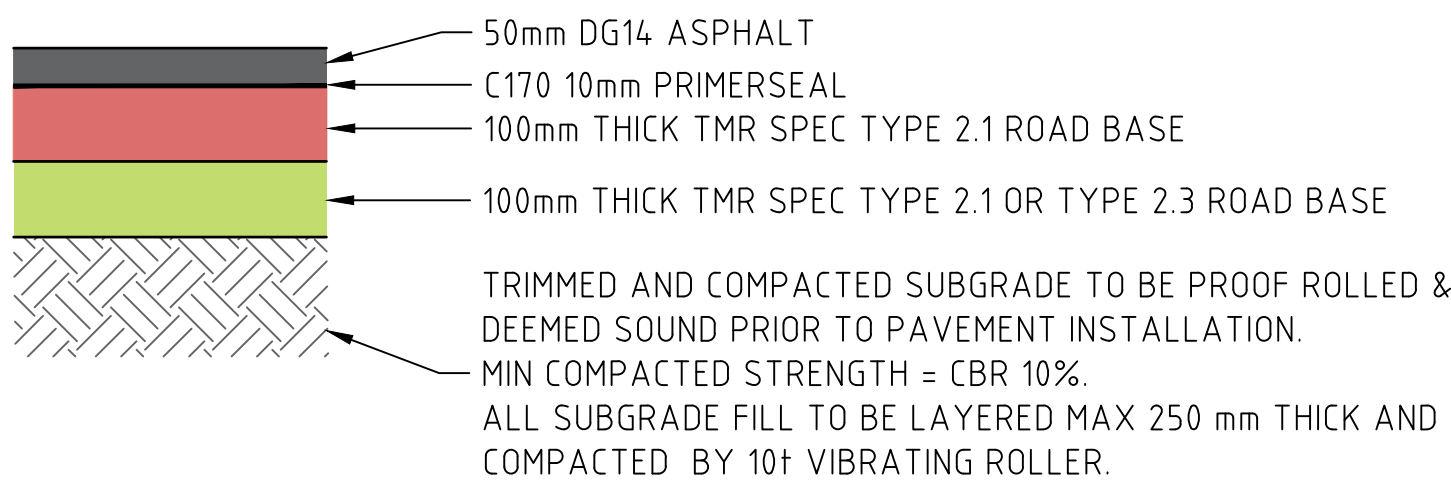


NEW ROAD PAVEMENT - DETAIL

N.T.S.

UNSUITABLE SUBGRADE DETAIL

N.T.S.

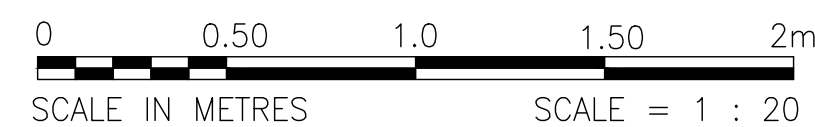

REF. DRG. No.	REFERENCE DRAWING TITLE	REV	DRWN	DSN'D	APP'D	DATE
		C				12.03.2026
		B				25.02.2026
		A				12.02.2026

REGISTERED PROFESSIONAL ENGINEER QUEENSLAND

RPEQ No: 16203
SCOTT MATTHEW THOMAS

SIGNATURE: DATE: 12/03/2026.....

SCALE (A1)

IF IN DOUBT ASK
THIS DOCUMENT
BECOMES
UNCONTROLLED
WHEN PRINTED -
CHECK THE REVISION
IS CURRENT

PATCOL
GROUP

info@patcol.com.au
www.patcol.com.au

186 Denham Street,
Rockhampton QLD 4700

dezinelements
BUILDING DESIGNERS


STANWELL POWER STATION
SWITCHYARD ROAD, STANWELL QLD 4702
NEW OFFICE BUILDING - CIVIL WORKS
ANNOTATED SECTIONS AND PAVEMENT DETAIL



DRAWING No.
25-595_A4 / 103

ISSUED FOR TENDER

REV.
C

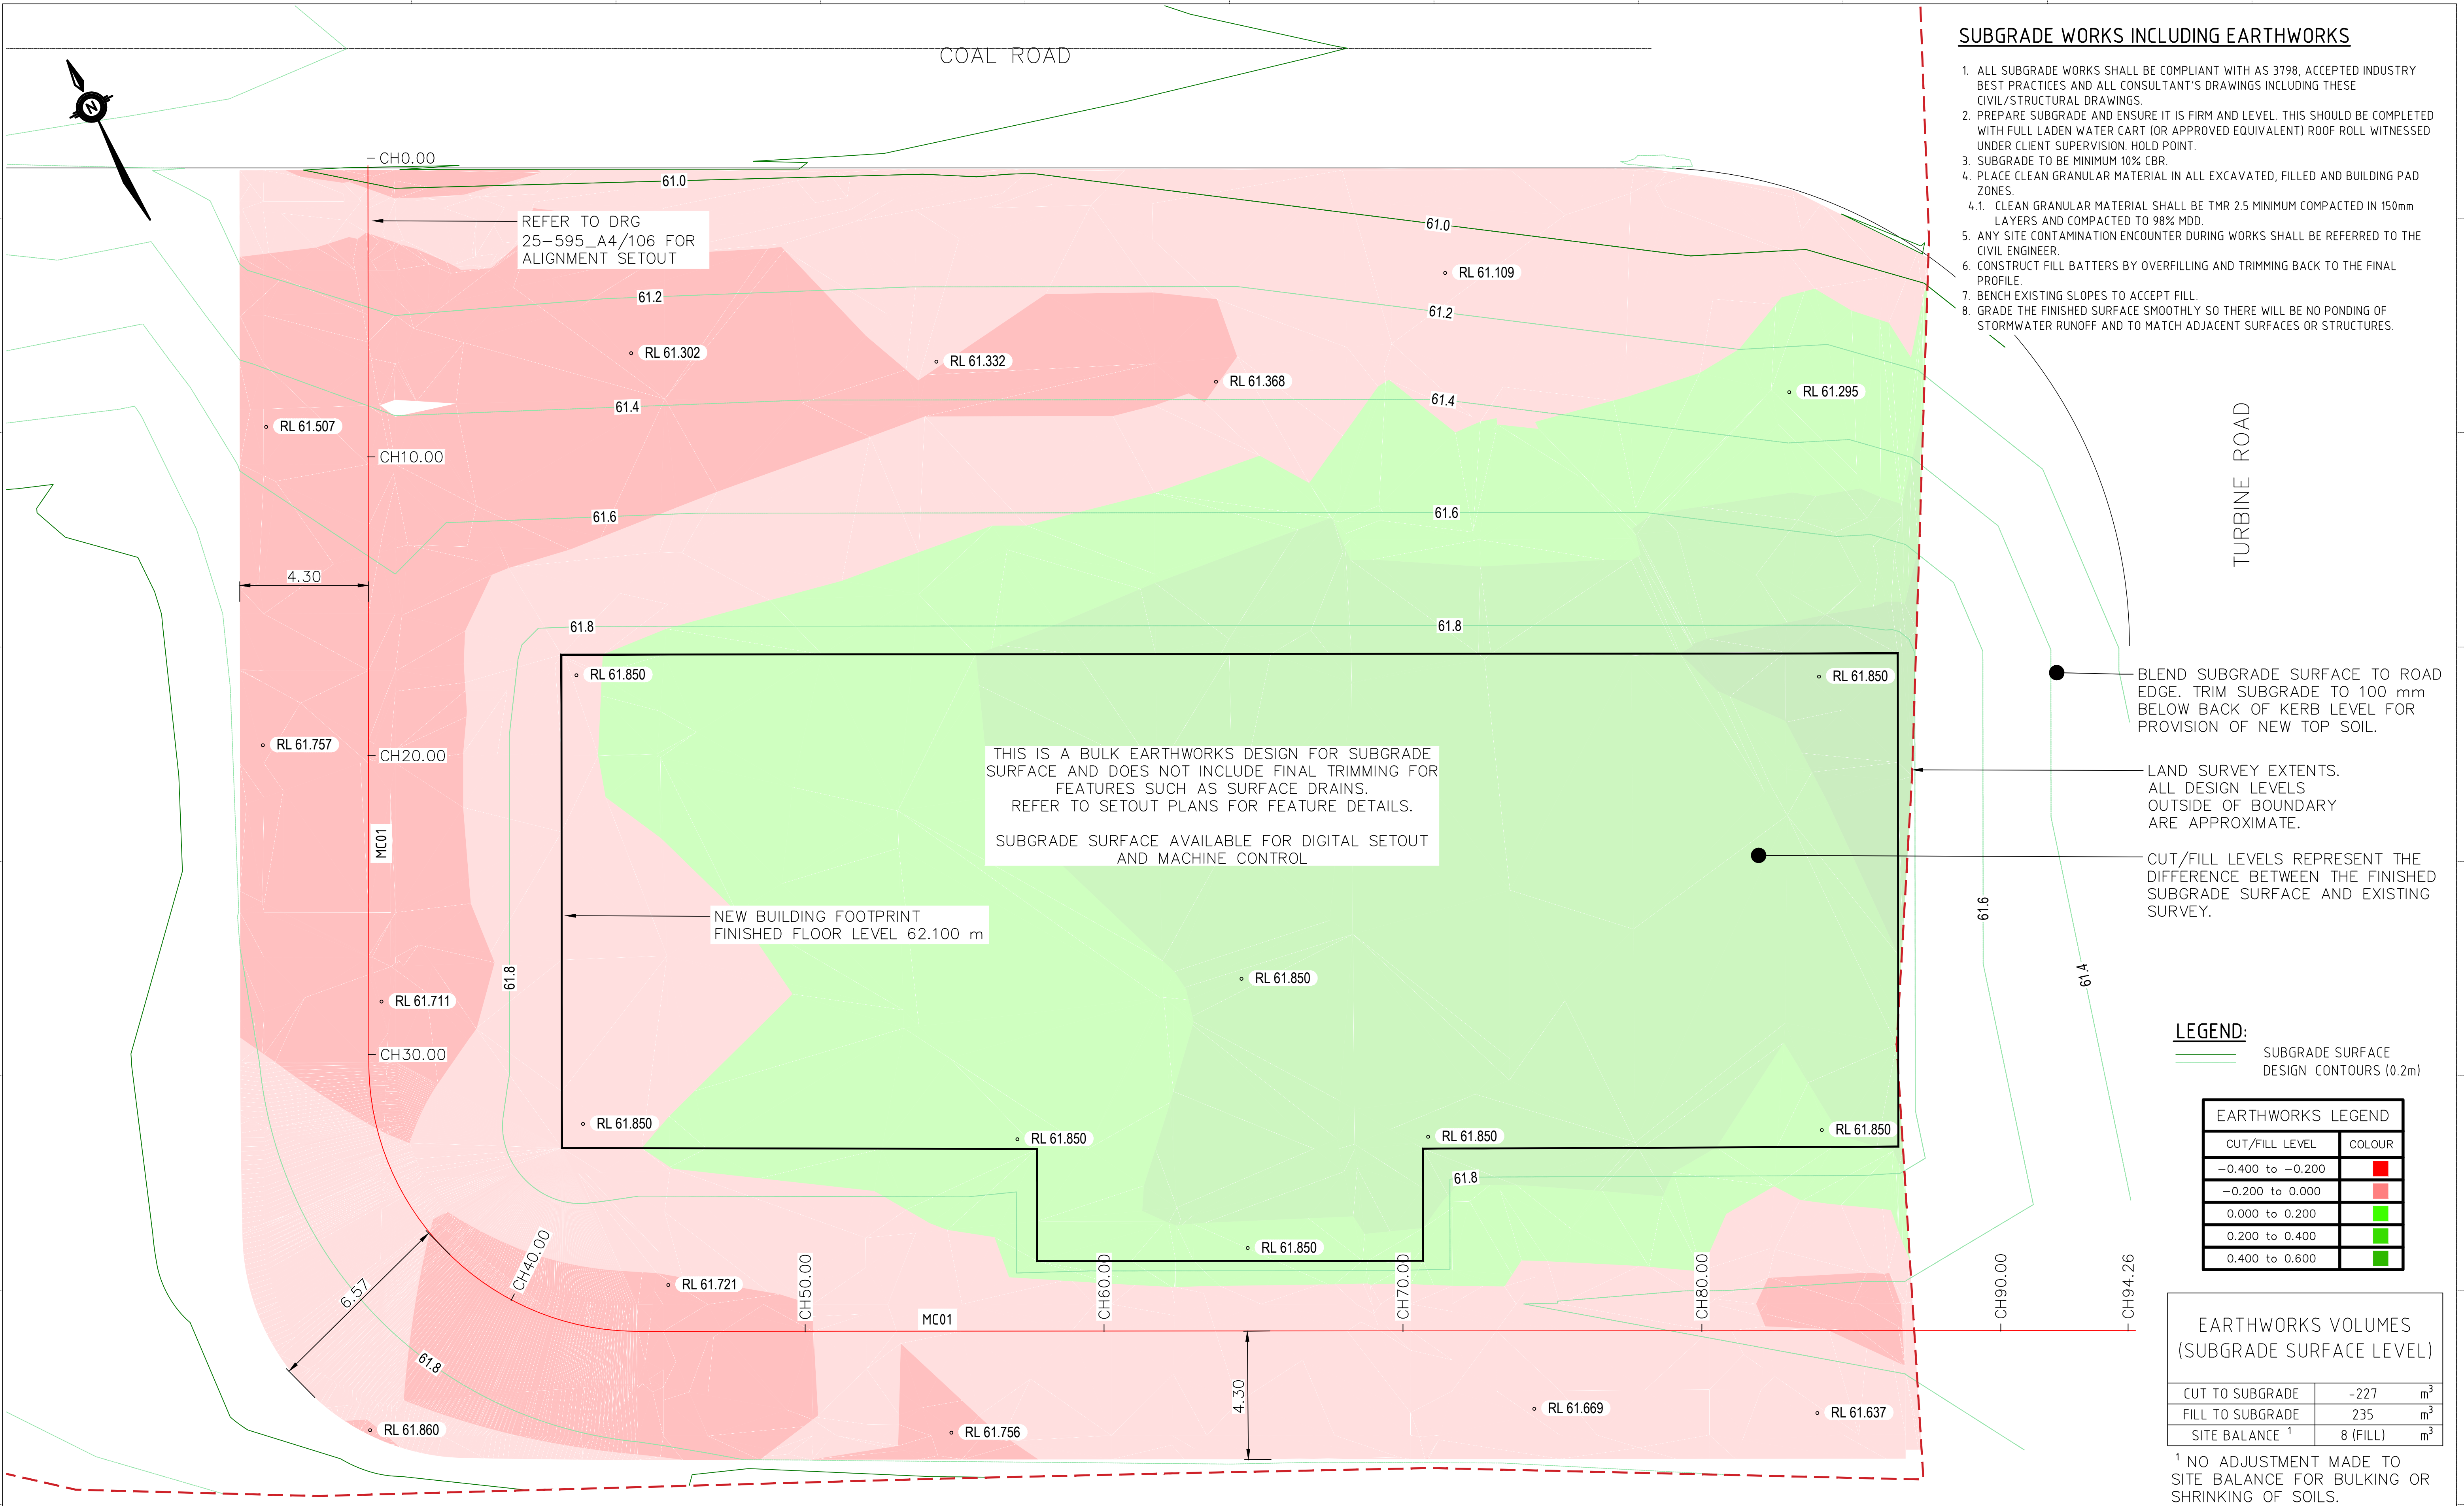

SUBGRADE WORKS INCLUDING EARTHWORKS

- 1. ALL SUBGRADE WORKS SHALL BE COMPLIANT WITH AS 3798, ACCEPTED INDUSTRY BEST PRACTICES AND ALL CONSULTANT'S DRAWINGS INCLUDING THESE CIVIL/STRUCTURAL DRAWINGS.
- 2. PREPARE SUBGRADE AND ENSURE IT IS FIRM AND LEVEL. THIS SHOULD BE COMPLETED WITH FULL LADEN WATER CART (OR APPROVED EQUIVALENT) ROOF ROLL WITNESSED UNDER CLIENT SUPERVISION. HOLD POINT.
- 3. SUBGRADE TO BE MINIMUM 10% CBR.
- 4. PLACE CLEAN GRANULAR MATERIAL IN ALL EXCAVATED, FILLED AND BUILDING PAD ZONES.
- 4.1. CLEAN GRANULAR MATERIAL SHALL BE TMR 2.5 MINIMUM COMPACTED IN 150mm LAYERS AND COMPACTED TO 98% MDD.
- 5. ANY SITE CONTAMINATION ENCOUNTER DURING WORKS SHALL BE REFERRED TO THE CIVIL ENGINEER.
- 6. CONSTRUCT FILL BATTERS BY OVERFILLING AND TRIMMING BACK TO THE FINAL PROFILE.
- 7. BENCH EXISTING SLOPES TO ACCEPT FILL.
- 8. GRADE THE FINISHED SURFACE SMOOTHLY SO THERE WILL BE NO PONDING OF STORMWATER RUNOFF AND TO MATCH ADJACENT SURFACES OR STRUCTURES.

BLEND SUBGRADE SURFACE TO ROAD EDGE. TRIM SUBGRADE TO 100 mm BELOW BACK OF KERB LEVEL FOR PROVISION OF NEW TOP SOIL.

LAND SURVEY EXTENTS. ALL DESIGN LEVELS OUTSIDE OF BOUNDARY ARE APPROXIMATE.

CUT/FILL LEVELS REPRESENT THE DIFFERENCE BETWEEN THE FINISHED SUBGRADE SURFACE AND EXISTING SURVEY.

LEGEND:

SUBGRADE SURFACE DESIGN CONTOURS (0.2m)


EARTHWORKS LEGEND	
CUT/FILL LEVEL	COLOUR
-0.400 to -0.200	
-0.200 to 0.000	
0.000 to 0.200	
0.200 to 0.400	
0.400 to 0.600	

EARTHWORKS VOLUMES (SUBGRADE SURFACE LEVEL)

CUT TO SUBGRADE	-227	m³
FILL TO SUBGRADE	235	m³
SITE BALANCE ¹	8 (FILL)	m³

¹ NO ADJUSTMENT MADE TO SITE BALANCE FOR BULKING OR SHRINKING OF SOILS.


EARTHWORKS CUT/FILL PLAN
SCALE 1:100

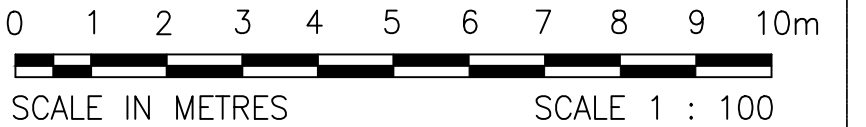

								REGISTERED PROFESSIONAL ENGINEER QUEENSLAND				SCALE		(A1)		 info@patcol.com.au www.patcol.com.au 186 Denham Street, Rockhampton QLD 4700  BUILDING DESIGNERS		STANWELL POWER STATION SWITCHYARD ROAD, STANWELL QLD 4702 NEW OFFICE BUILDING – CIVIL WORKS BULK EARTHWORKS AND SUBGRADE SURFACE					DRAWING No. 25-595_A4 / 104	ISSUED FOR TENDER	REV.	

DRAINAGE SETOUT				
POINT #	EASTING	NORTHING	LEVEL	DESC
1	226177.067	7397267.337	61.955	DRAIN
2	226167.769	7397272.682	61.850	DRAIN
3	226166.020	7397274.988	61.818	DRAIN
4	226166.314	7397277.954	61.787	DRAIN
5	226172.000	7397287.985	61.729	DRAIN
6	226178.241	7397298.994	61.635	DRAIN
10	226183.025	7397305.664	61.111	KA
11	226178.021	7397303.173	61.126	SS
12	226175.137	7397298.178	61.435	SS
13	226170.145	7397289.513	61.629	SS
14	226165.154	7397280.848	61.667	SS
15	226164.459	7397275.098	61.753	IO
16	226167.983	7397269.897	61.670	SS
17	226172.659	7397267.239	61.647	SS
18	226181.307	7397262.217	61.612	SS
19	226189.986	7397257.249	61.574	SS
20	226198.734	7397252.185	61.537	SS
21	226208.140	7397246.751		SS #
22	226205.787	7397242.486		SS #
23	226196.858	7397247.639	61.621	SS
24	226188.420	7397252.499	61.657	SS
25	226179.290	7397257.758	61.696	SS
26	226170.762	7397262.671	61.732	SS
27	226160.924	7397268.401	61.783	SS
28	226157.318	7397273.209	61.761	IO
29	226158.195	7397278.691	61.780	SS
30	226161.252	7397283.920	61.753	SS
31	226165.964	7397292.207	61.716	SS
32	226170.872	7397300.655	61.544	SS
33	226173.473	7397305.181	61.245	SS
34	226173.858	7397310.929	61.172	KA
35	226208.073	7397238.724		KA #
36	226217.985	7397255.285		PIT #


NO DESIGN SURVEY AVAILABLE. CONFIRM LEVEL WITH SITE SUPERINTENDENT.

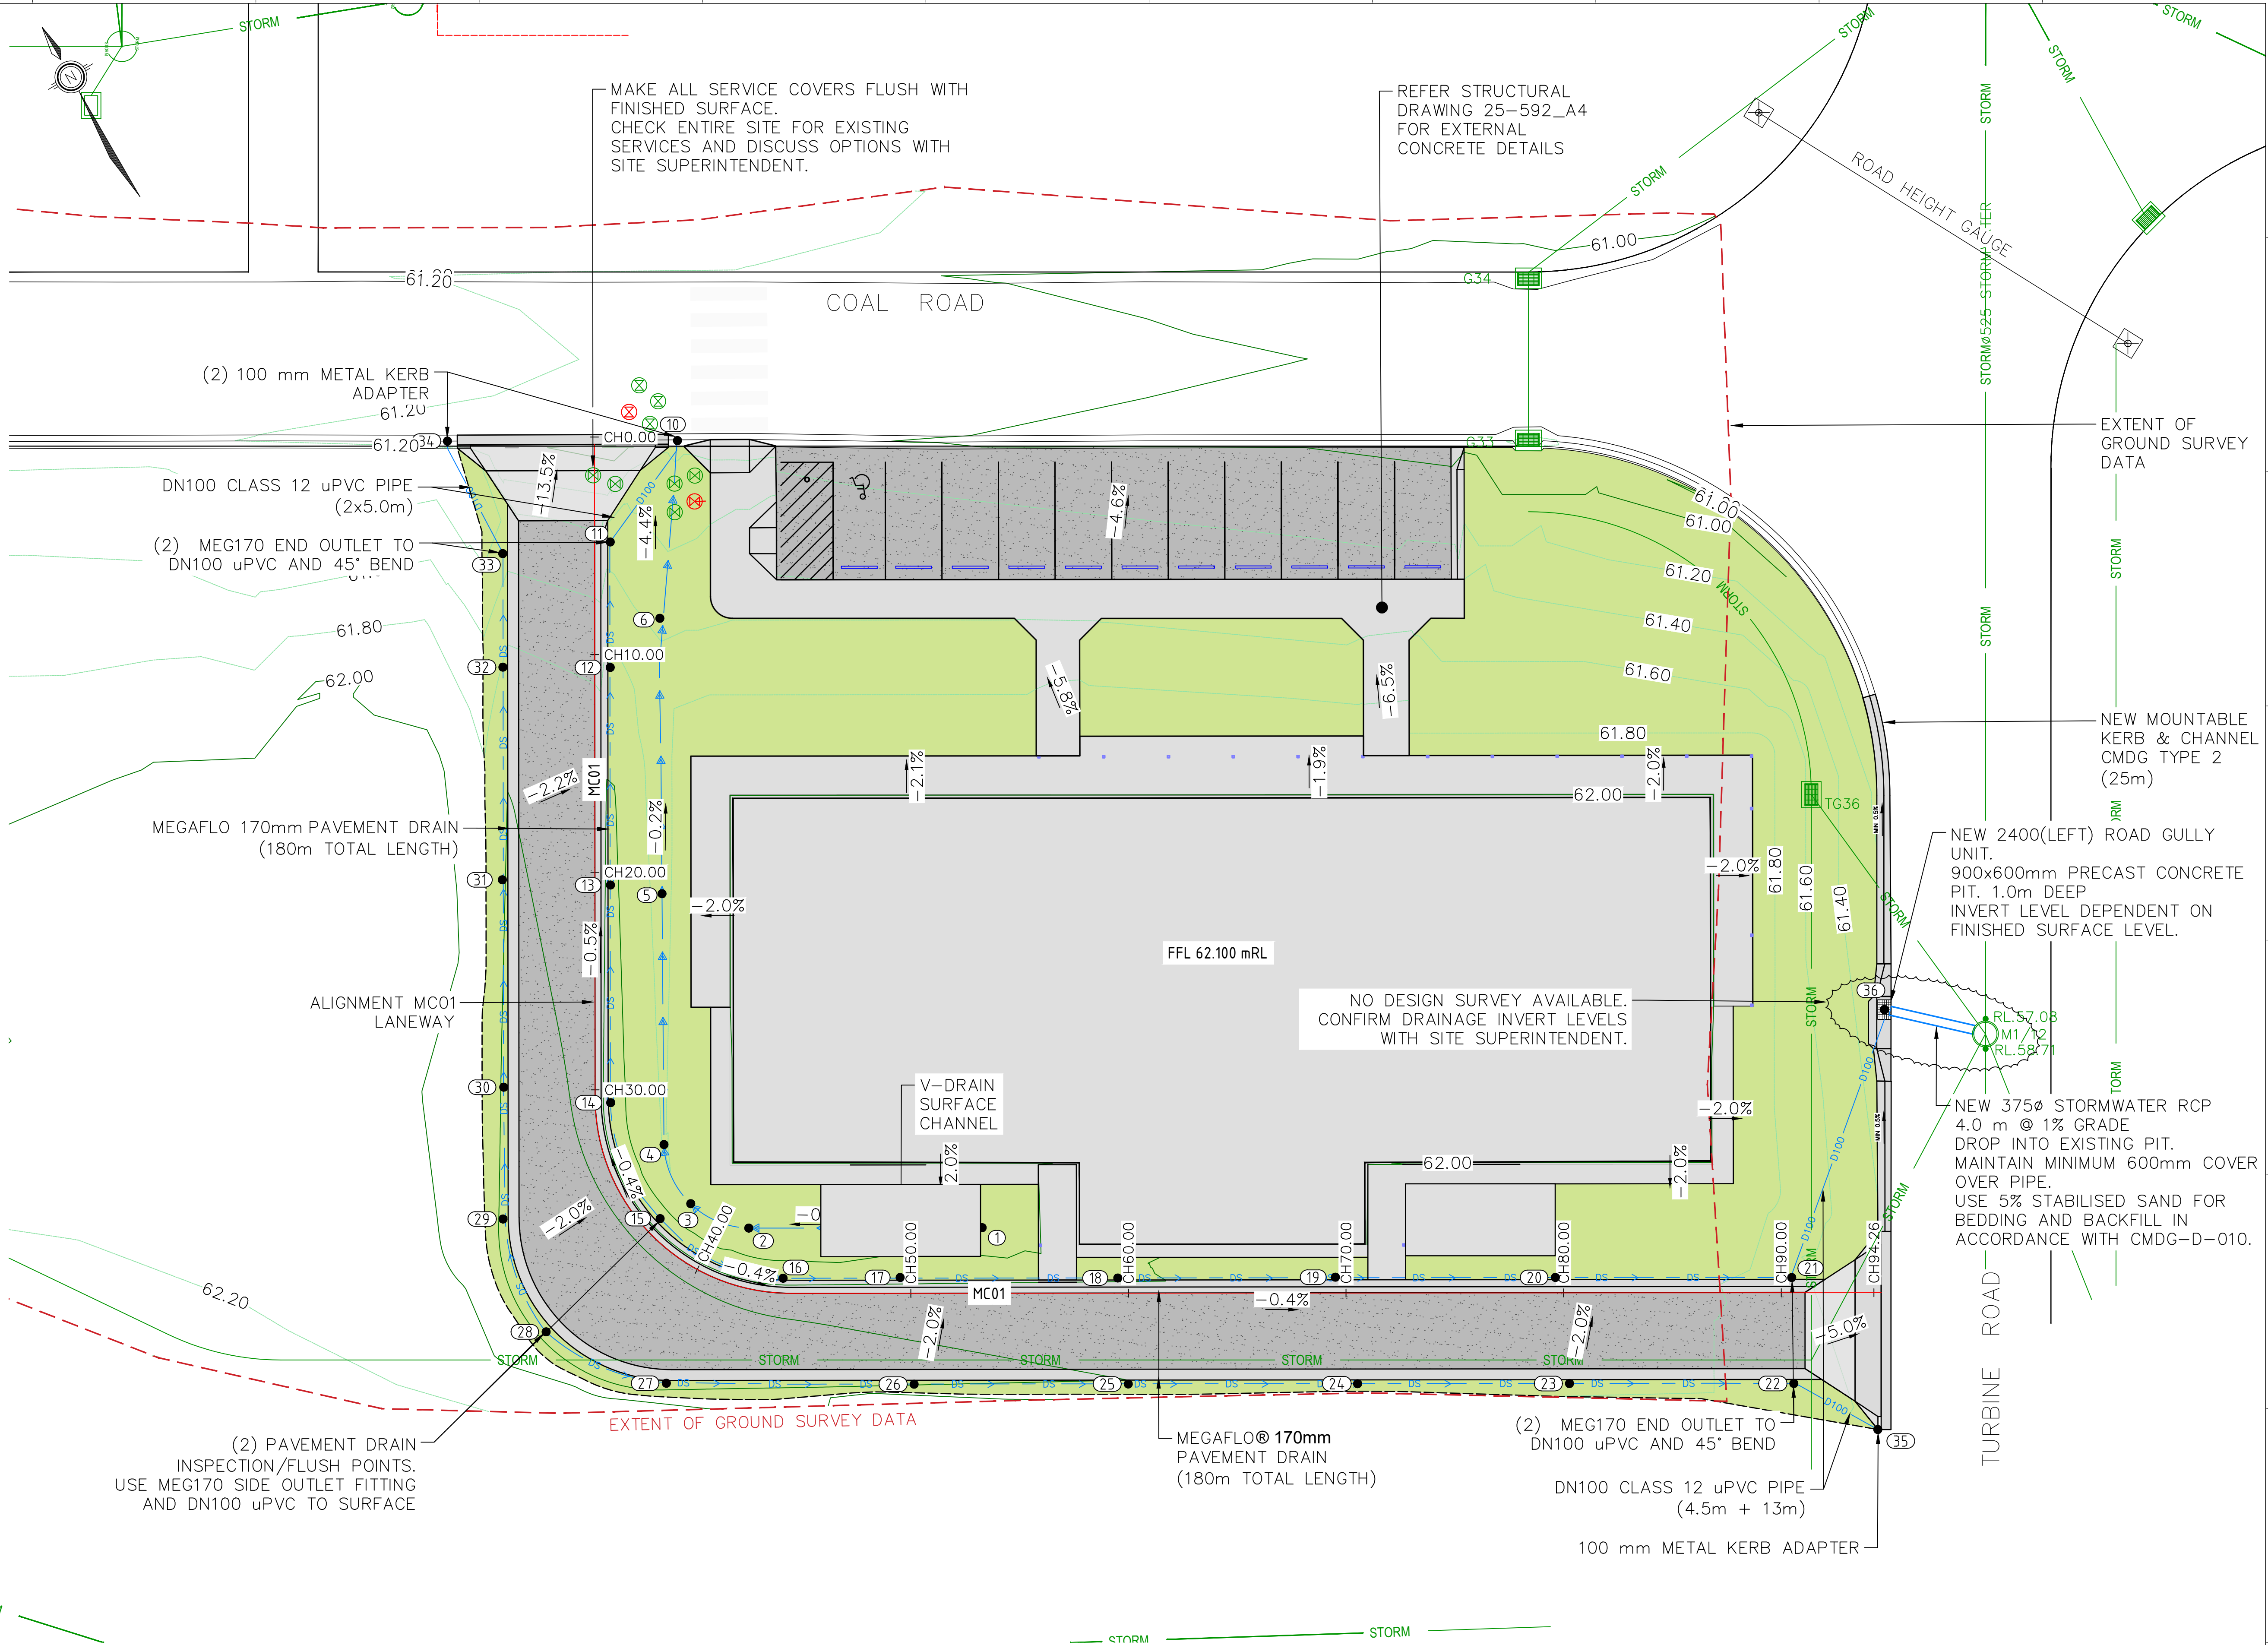



DRAINAGE DESIGN LAYOUT
SCALE 1:150



--	--	

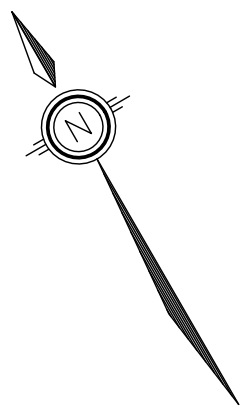


LEGEND:
FINISHED SURFACE DESIGN CONTOURS (0.2 m)

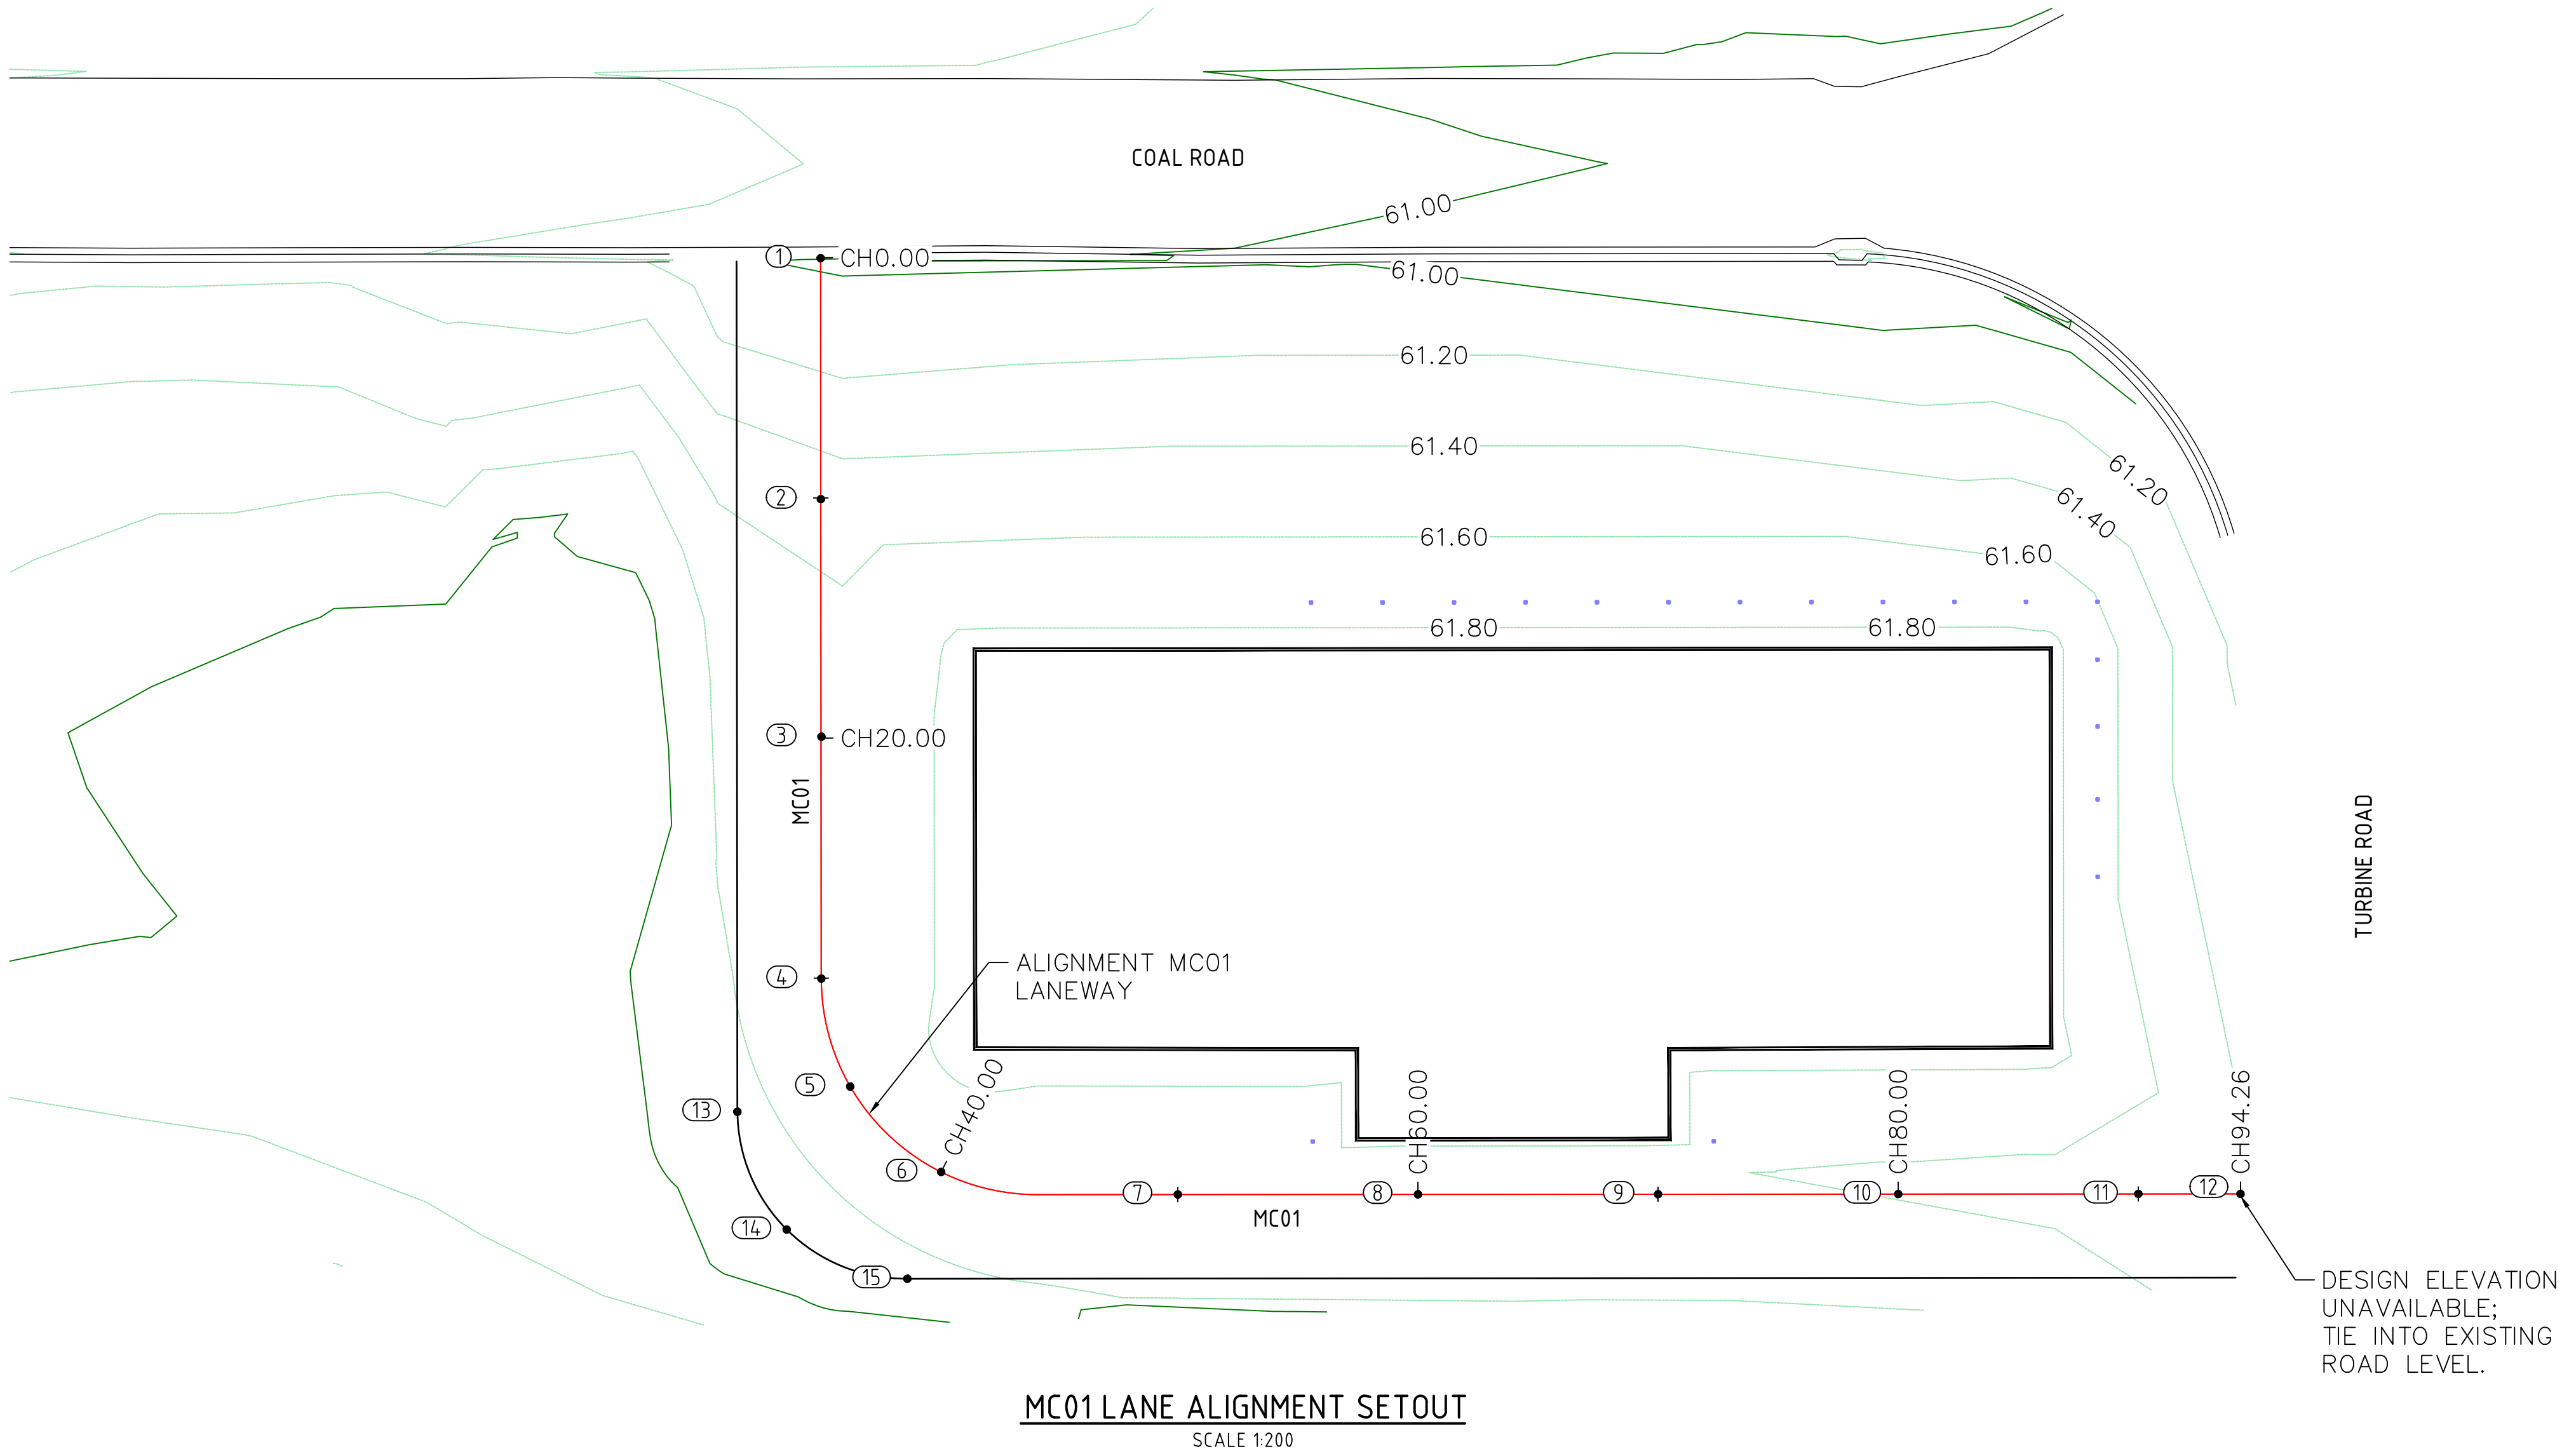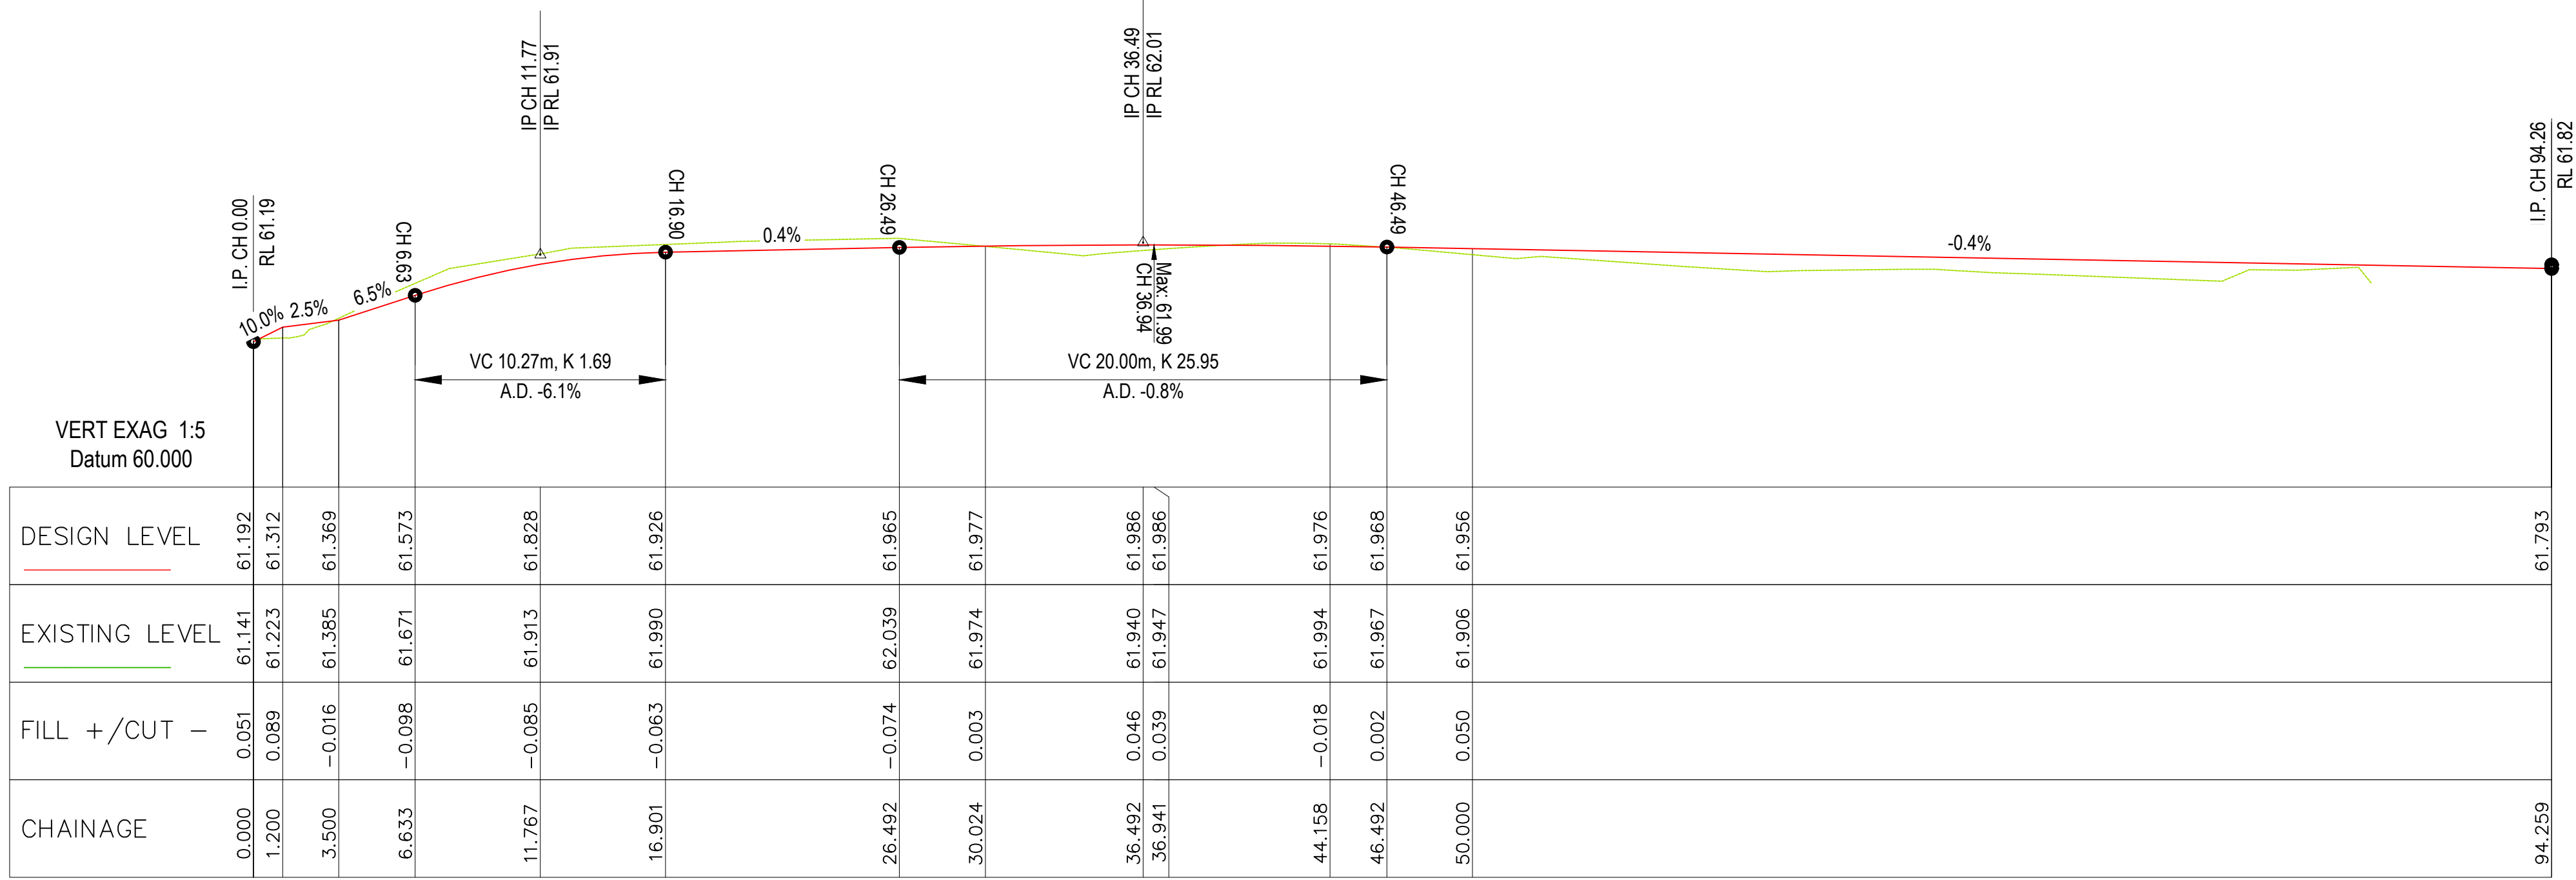

MC01 SETOUT POINTS				
POINT #	EASTING	NORTHING	FS RL	DESC
1	226179.627	7397307.403	61.177	CH 0
2	226174.620	7397298.710	61.760	CH 10
3	226169.694	7397290.129	61.939	CH 20
4	226164.652	7397281.407	61.977	CH 30
5	226163.448	7397276.911	61.985	MID
6	226164.948	7397271.935	61.984	CH 40
7	226173.014	7397266.196	61.956	CH 50
8	226181.677	7397261.201	61.919	CH 60
9	226190.340	7397256.206	61.882	CH 70
10	226199.003	7397251.211	61.845	CH 80
11	226207.666	7397246.216	61.659	CH 90
12	226211.352	7397244.091		END #
13	226158.853	7397278.352	62.078	KERB_TOE
14	226158.177	7397273.073	62.102	KERB_TOE
15	226161.506	7397268.788	62.076	KERB_TOE

DESIGN ELEVATION UNAVAILABLE

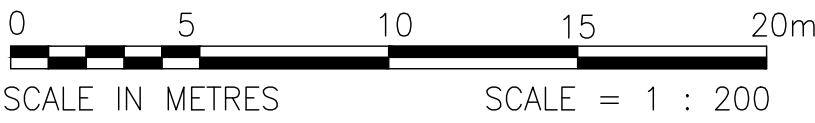

REFER TO STANDARD DRAWING
CMDG-R-042 FOR COMMERCIAL
ACCESS MATERIAL SPECIFICATIONS


PEDESTRIAN RAMPS TO COMPLY
WITH CMDG-R-050.
NO TACTILE SURFACE INDICATORS
UNLESS ORDERED BY STANWELL PM

REFER STRUCTURAL DRAWING 25-592_A4
FOR EXTERNAL CONCRETE DETAILS

LEGEND:
FINISHED SURFACE DESIGN CONTOURS (0.2 m)

MOW STRIP SETOUT				
POINT #	EASTING	NORTHING	LEVEL	DESC
30	226171.324	7397282.338	61.932	MOW STRIP
31	226167.273	7397275.288	61.932	MOW STRIP
32	226180.283	7397267.784	61.932	MOW STRIP
33	226194.948	7397259.338	61.932	MOW STRIP
34	226207.970	7397251.852	61.932	MOW STRIP
35	226212.026	7397258.869	61.932	MOW STRIP

PATH SETOUT				
POINT #	EASTING	NORTHING	LEVEL	DESC
40	226170.580	7397282.801	61.965	PATH
41	226176.315	7397292.769	61.964	PATH
42	226190.068	7397284.860	61.964	PATH
43	226192.251	7397284.623	61.960	PATH
44	226203.495	7397278.134	61.897	PATH
45	226204.830	7397276.344	61.965	PATH
46	226218.558	7397268.427	61.964	PATH
47	226212.821	7397258.444	61.964	PATH
48	226207.563	7397280.916	61.620	PATH
49	226208.928	7397281.282	61.528	PATH
50	226210.256	7397280.510	61.513	PATH
51	226211.153	7397282.067	61.477	PATH
52	226207.979	7397283.871	61.500	PATH
53	226201.191	7397287.795	61.539	PATH
54	226194.823	7397291.453	61.564	PATH
55	226188.233	7397295.249	61.564	PATH
56	226183.776	7397297.847	61.410	PATH
57	226180.710	7397298.610	61.552	PATH
58	226205.738	7397281.960	61.609	PATH
59	226181.122	7397297.331	61.595	PATH
60	226187.338	7397293.736	61.596	PATH
61	226192.346	7397290.845	61.596	PATH
62	226192.713	7397289.479	61.680	PATH
63	226205.371	7397283.326	61.511	PATH
64	226195.810	7397288.846	61.588	PATH
65	226194.445	7397288.479	61.687	PATH

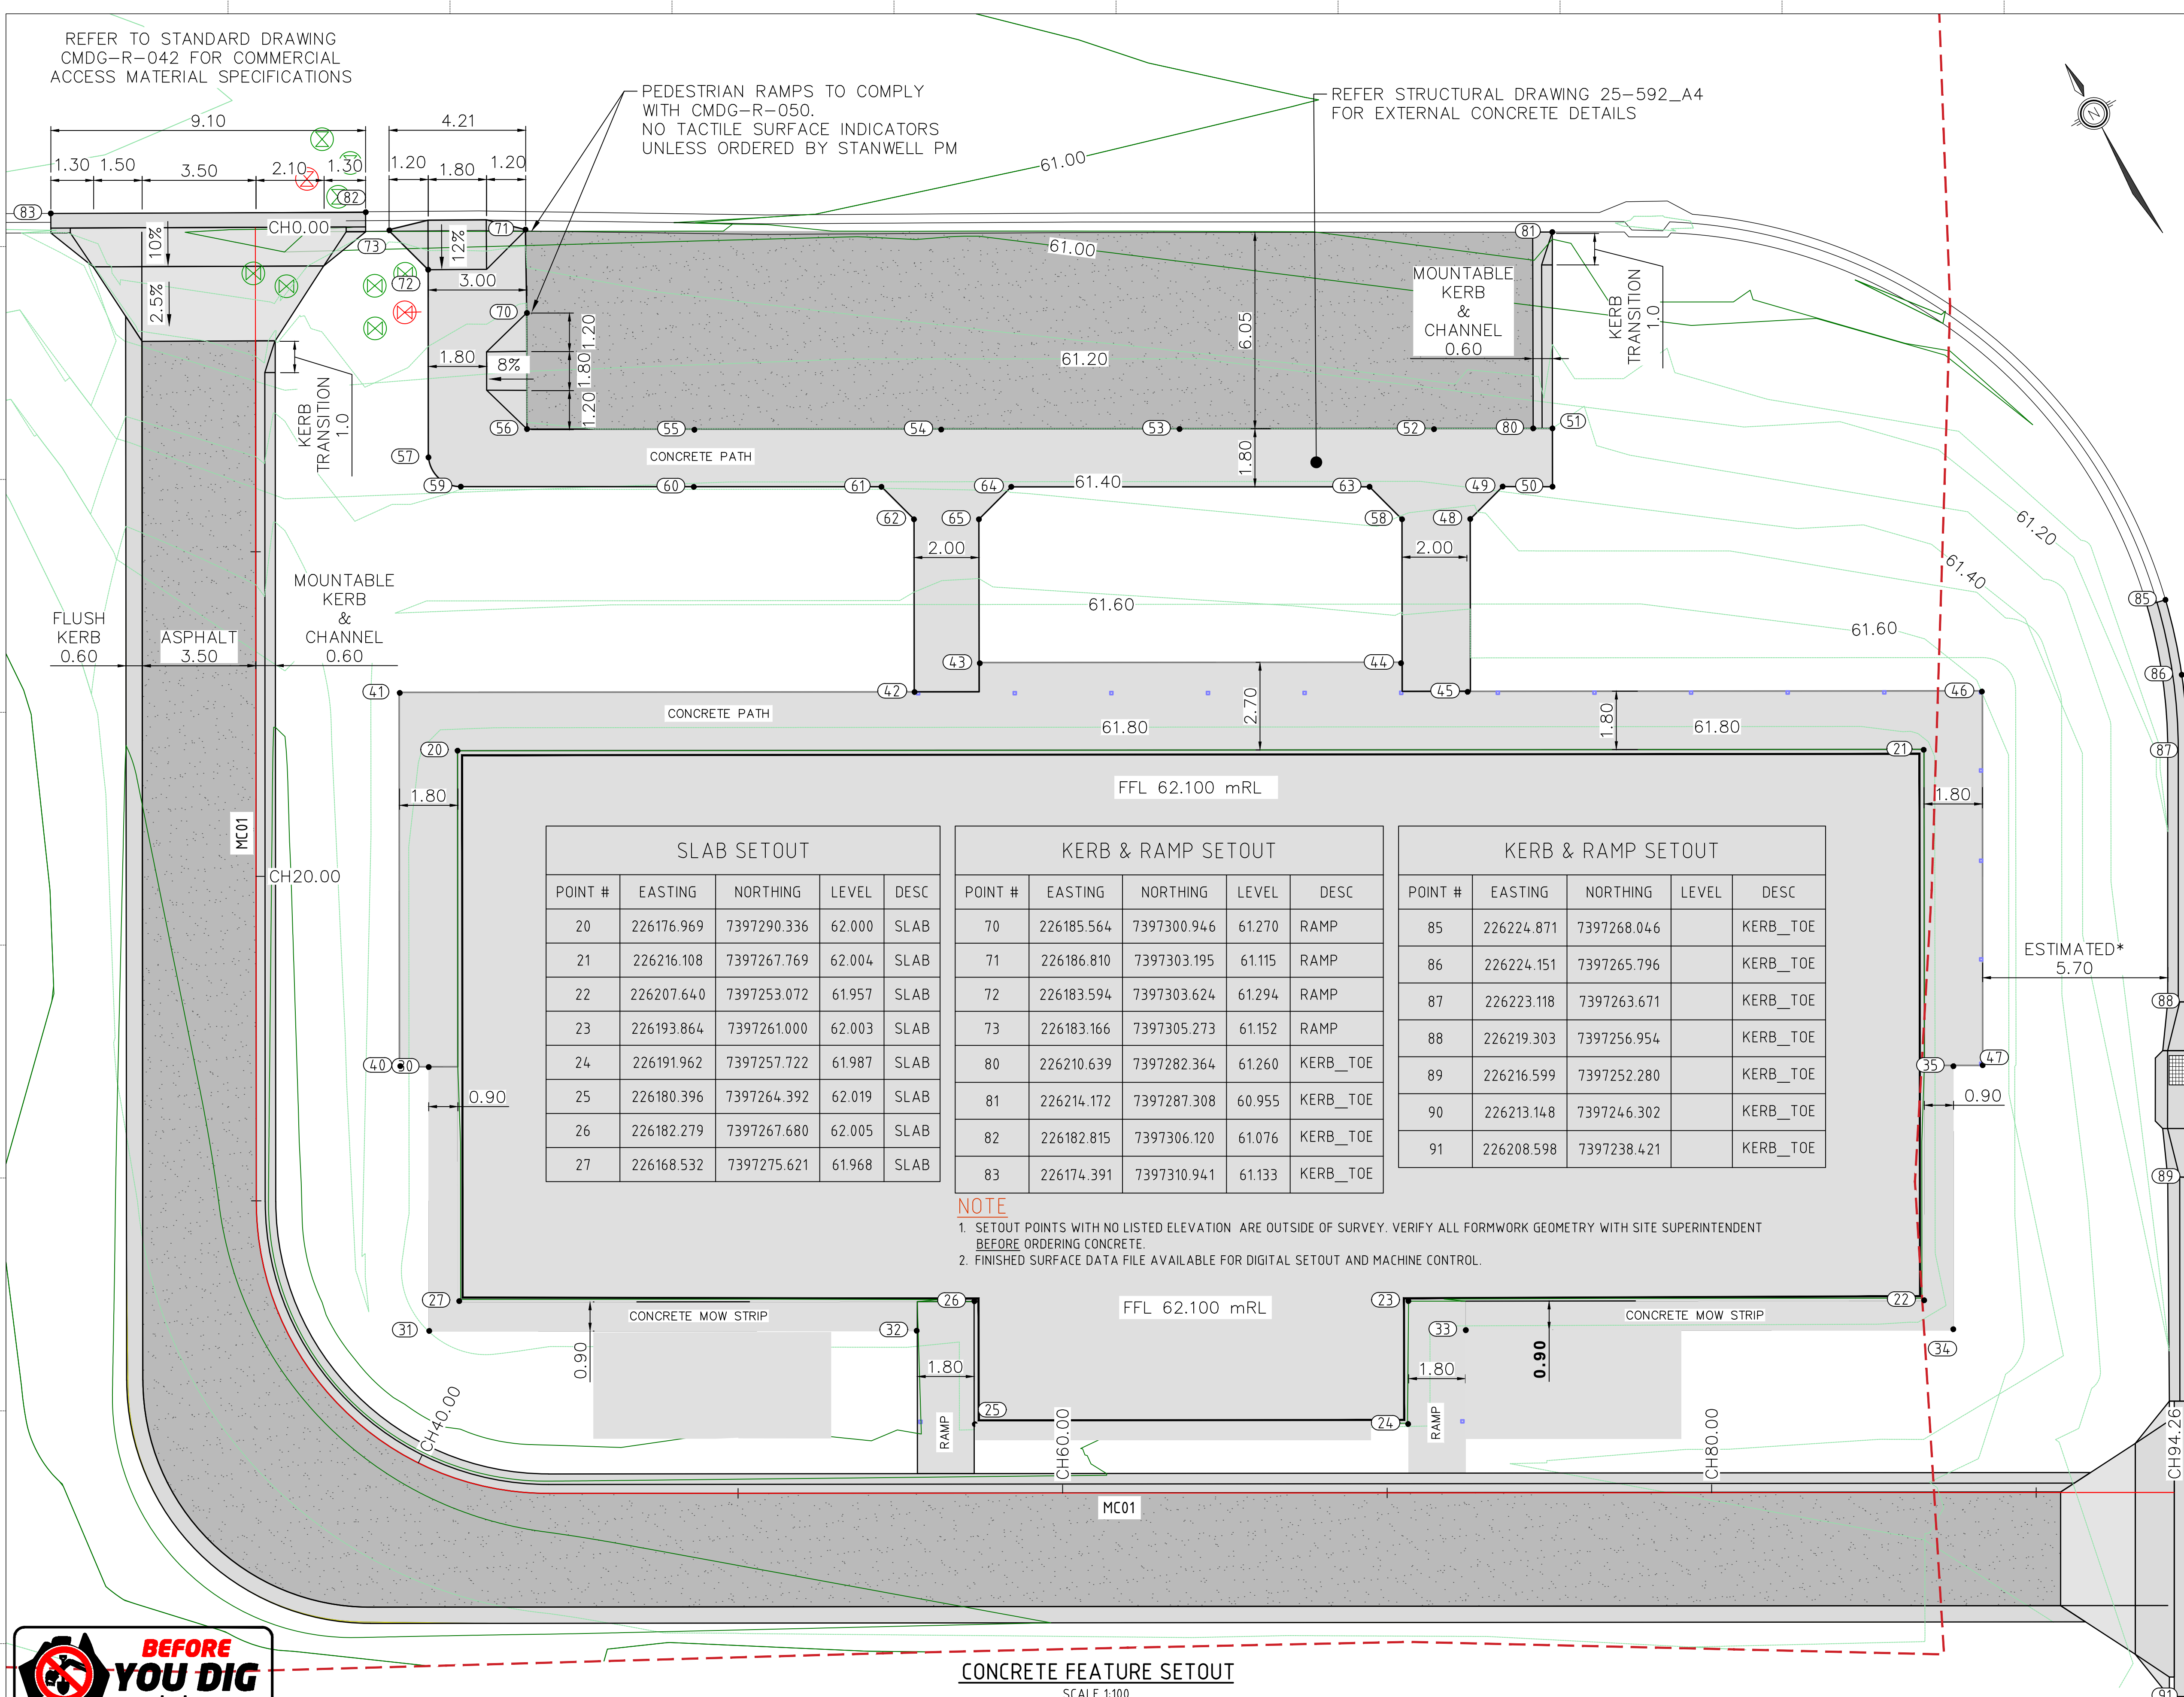

SLAB SETOUT				
POINT #	EASTING	NORTHING	LEVEL	DESC
20	226176.969	7397290.336	62.000	SLAB
21	226216.108	7397267.769	62.004	SLAB
22	226207.640	7397253.072	61.957	SLAB
23	226193.864	7397261.000	62.003	SLAB
24	226191.962	7397257.722	61.987	SLAB
25	226180.396	7397264.392	62.019	SLAB
26	226182.279	7397267.680	62.005	SLAB
27	226168.532	7397275.621	61.968	SLAB

KERB & RAMP SETOUT				
POINT #	EASTING	NORTHING	LEVEL	DESC
70	226185.564	7397300.946	61.270	RAMP
71	226186.810	7397303.195	61.115	RAMP
72	226183.594	7397303.624	61.294	RAMP
73	226183.166	7397305.273	61.152	RAMP
80	226210.639	7397282.364	61.260	KERB_TOE
81	226214.172	7397287.308	60.955	KERB_TOE
82	226182.815	7397306.120	61.076	KERB_TOE
83	226174.391	7397310.941	61.133	KERB_TOE

KERB & RAMP SETOUT				
POINT #	EASTING	NORTHING	LEVEL	DESC
85	226224.871	7397268.046		KERB_TOE
86	226224.151	7397265.796		KERB_TOE
87	226223.118	7397263.671		KERB_TOE
88	226219.303	7397256.954		KERB_TOE
89	226216.599	7397252.280		KERB_TOE
90	226213.148	7397246.302		KERB_TOE
91	226208.598	7397238.421		KERB_TOE

NOTE
1. SETOUT POINTS WITH NO LISTED ELEVATION ARE OUTSIDE OF SURVEY. VERIFY ALL FORMWORK GEOMETRY WITH SITE SUPERINTENDENT BEFORE ORDERING CONCRETE.
2. FINISHED SURFACE DATA FILE AVAILABLE FOR DIGITAL SETOUT AND MACHINE CONTROL.

REFER TO STANDARD DRAWING
CMDG-R-042 FOR COMMERCIAL
ACCESS MATERIAL SPECIFICATIONS



CONCRETE FEATURE SETOUT
SCALE 1:100

0 1 2 3 4 5 6 7 8 9 10m
SCALE IN METRES SCALE 1 : 100

REF. DRG. No.	REFERENCE DRAWING TITLE	REV	DRWN	DSN'D	APP'D	DATE
		C				12.03.2026
		B				25.02.2026
		A				12.02.2026

REGISTERED PROFESSIONAL ENGINEER QUEENSLAND
RPEQ No: 16203
SCOTT MATTHEW THOMAS
SIGNATURE: DATE: 12/03/2026.....

SCALE (A1)
IF IN DOUBT ASK
THIS DOCUMENT
BECOMES
UNCONTROLLED
WHEN PRINTED -
CHECK THE REVISION
IS CURRENT


PATCOL
GROUP
info@patcol.com.au
www.patcol.com.au
186 Denham Street,
Rockhampton QLD 4700

dezi
nelements
BUILDING DESIGNERS


STANWELL POWER STATION
SWITCHYARD ROAD, STANWELL QLD 4702
NEW OFFICE BUILDING - CIVIL WORKS
CONCRETE FEATURES SETOUT



DRAWING No. 25-595_A4 / 107
ISSUED FOR TENDER
REV. C

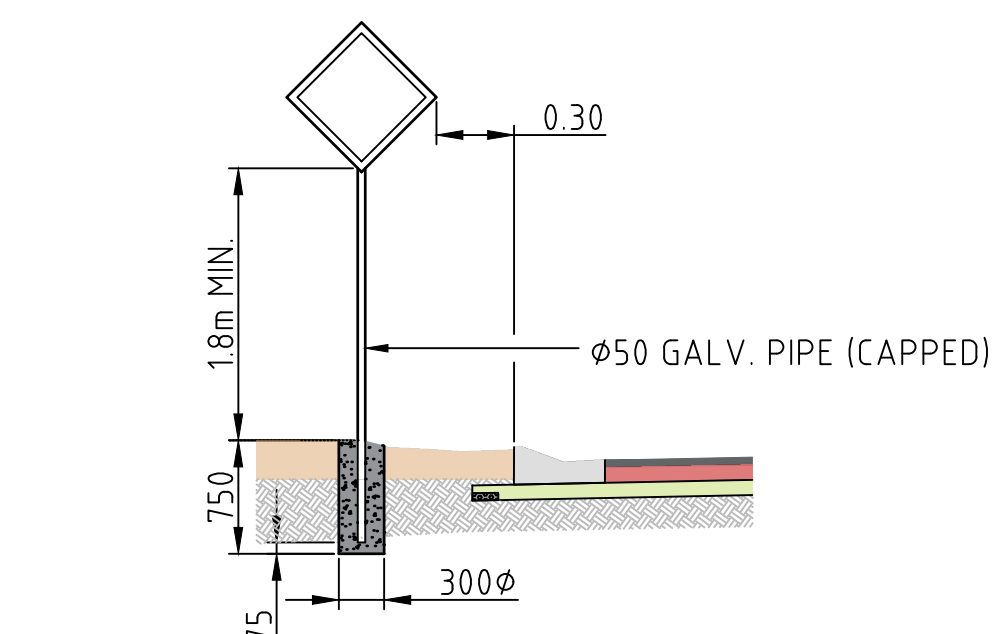

ROAD EDGE SIGN POST TYPICAL DETAIL

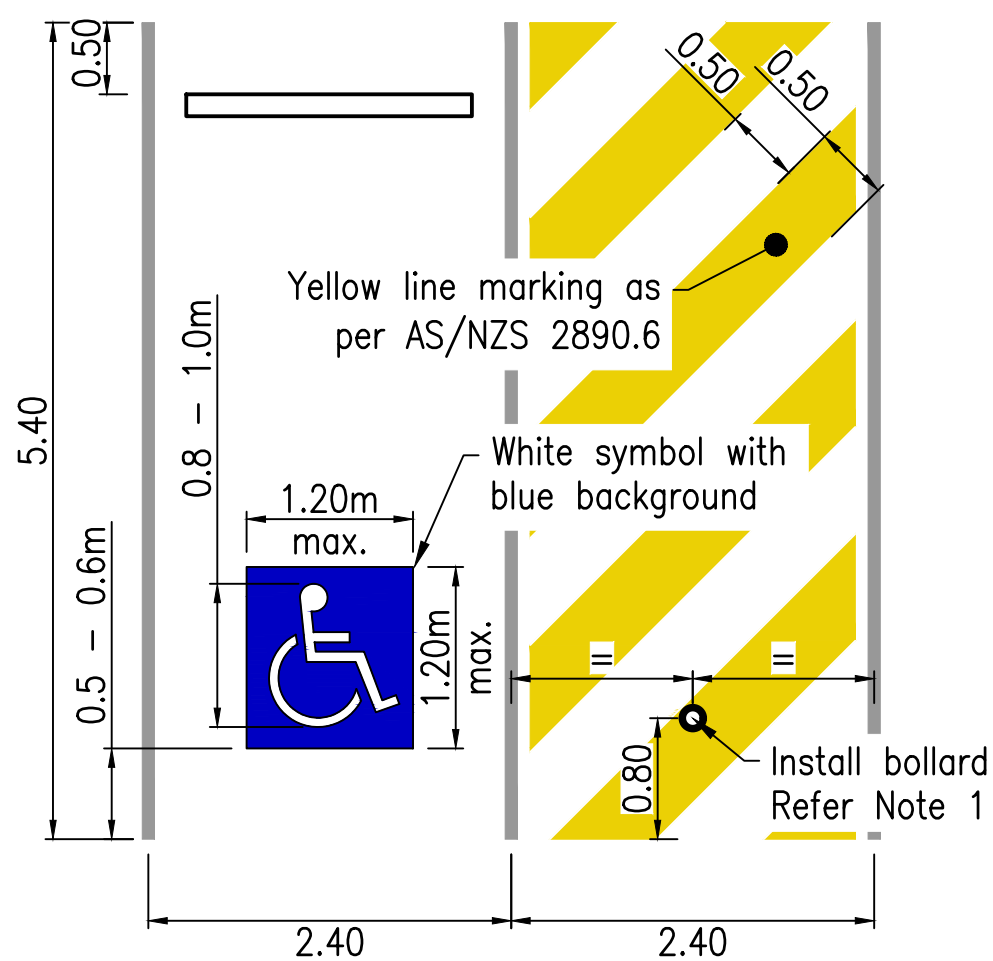

ACCESSIBLE PARKING BAY

TYPICAL DETAIL
SCALE 1:50

LINEMARKING NOTES

1. BOLLARD IN DISABLED PARKING SHARED AREA (139.7 X 5.0 CHS HOT DIPPED GALVANIZED BOLLARD - 1.0M ABOVE GROUND, 1.2M BELOW GROUND, 450DIA. X 1.3M 20MPA CONCRETE FOOTING COMPLETE WITH 25MPA CONCRETE INFILL).
2. PARKING BAY MARKINGS SHALL BE YELLOW AND SHALL HAVE A SLIP RESISTANT SURFACE.
3. REFER TO AS/NZS 1742.2 FOR GENERAL LINE MARKING STANDARDS.

LINEMARKING LAYOUT

SCALE 1:150

[illegible]

0 1 2.5 5 10 15m
SCALE IN METRES SCALE = 1 : 150