rev	date	description	initial
T1	11/03/2026	For Tender	JB

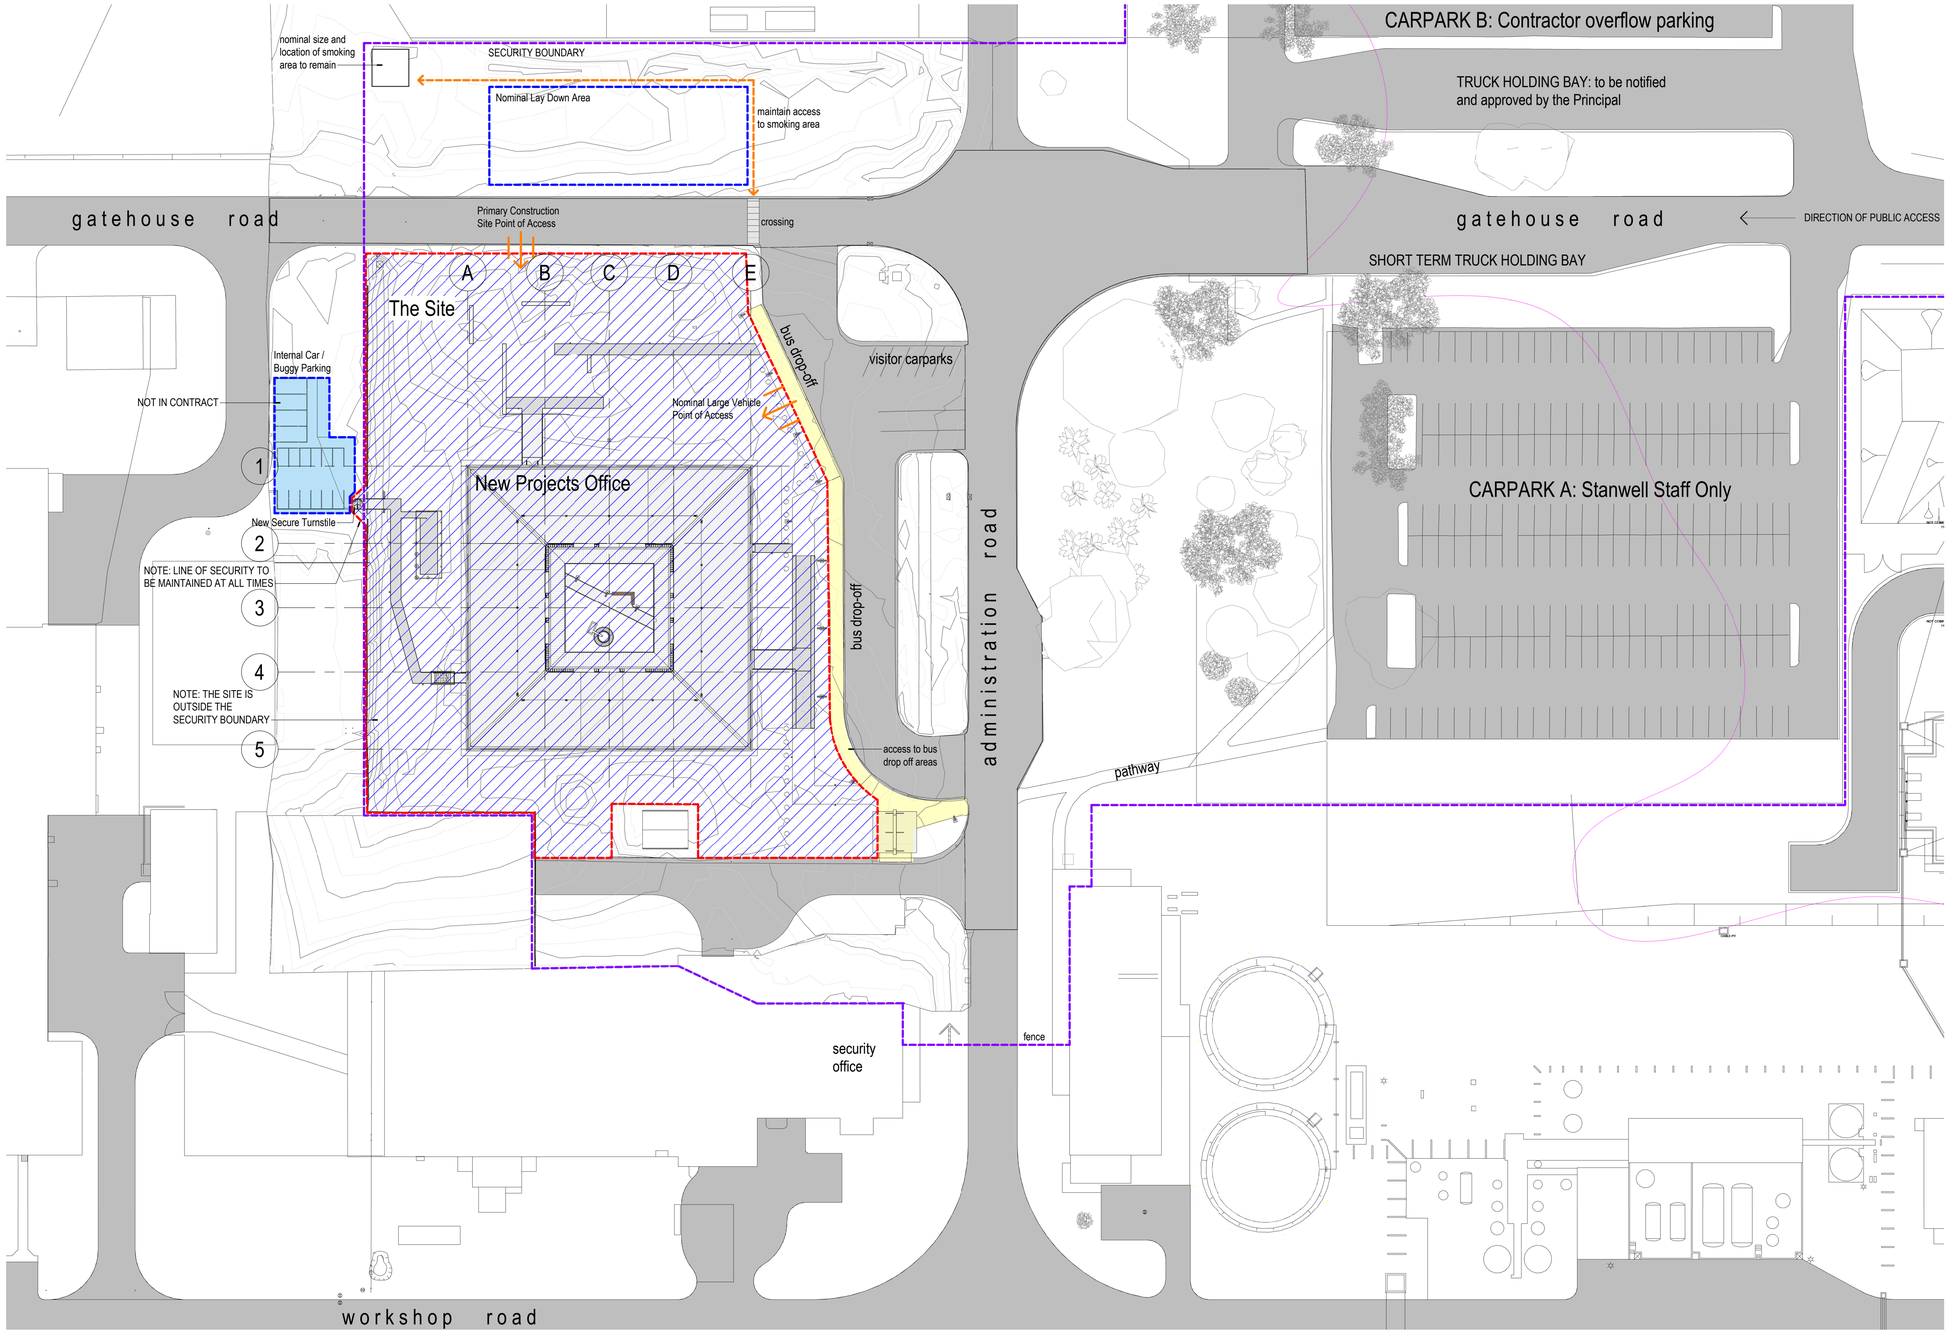

1 Precinct Plan
1 : 500

Site Notes

1. Refer to Architectural Specification for site related preliminaries.
2. Construction Site shown; dashed red.
3. Access to be maintained to bus drop off areas highlighted yellow. For works in this areas altenative access is to be arranged with the Principal.
4. Nominal lay down area shown dashed blue. Confirm full extents of available area with the Principal.

Site Legend

The Site -

Laydown Area -

Secure Area Boundary -

PRELIMINARY NOT FOR CONSTRUCTION

Drawings include colour information. A black & white copy may not have all the information. This background is coloured blue.

brian hooperarchitect
m3architecture
ph: +61 7 3831 4644
11 saint james street petrie tce q 4000
info@m3architecture.com
www.m3architecture.com

client stanwell

project Stanwell New Projects Office
Switchyard Road,
Stanwell, QLD, 4702

title Site Precinct Plan

drawn bg
checked jb
date March 2026
scale As indicated at A1
drawing 25010 / cd A-040001 / T1

copyright ©
These designs, plans, specifications and the copyright herein are the property of the architect and must not be used, reproduced, or copied wholly or in part without the written permission of m3architecture pty ltd abn 23 079 044 545.
Use figured dimensions in preference to scale.
If there are any questions contact the architect.

1:500 at A1

0 5 10 15 20 25m

9/03/2026 12:14:14 PM C:\~Projects\STANWELL-BuildingNPO-CentralFile_jaydn.b.rvt