


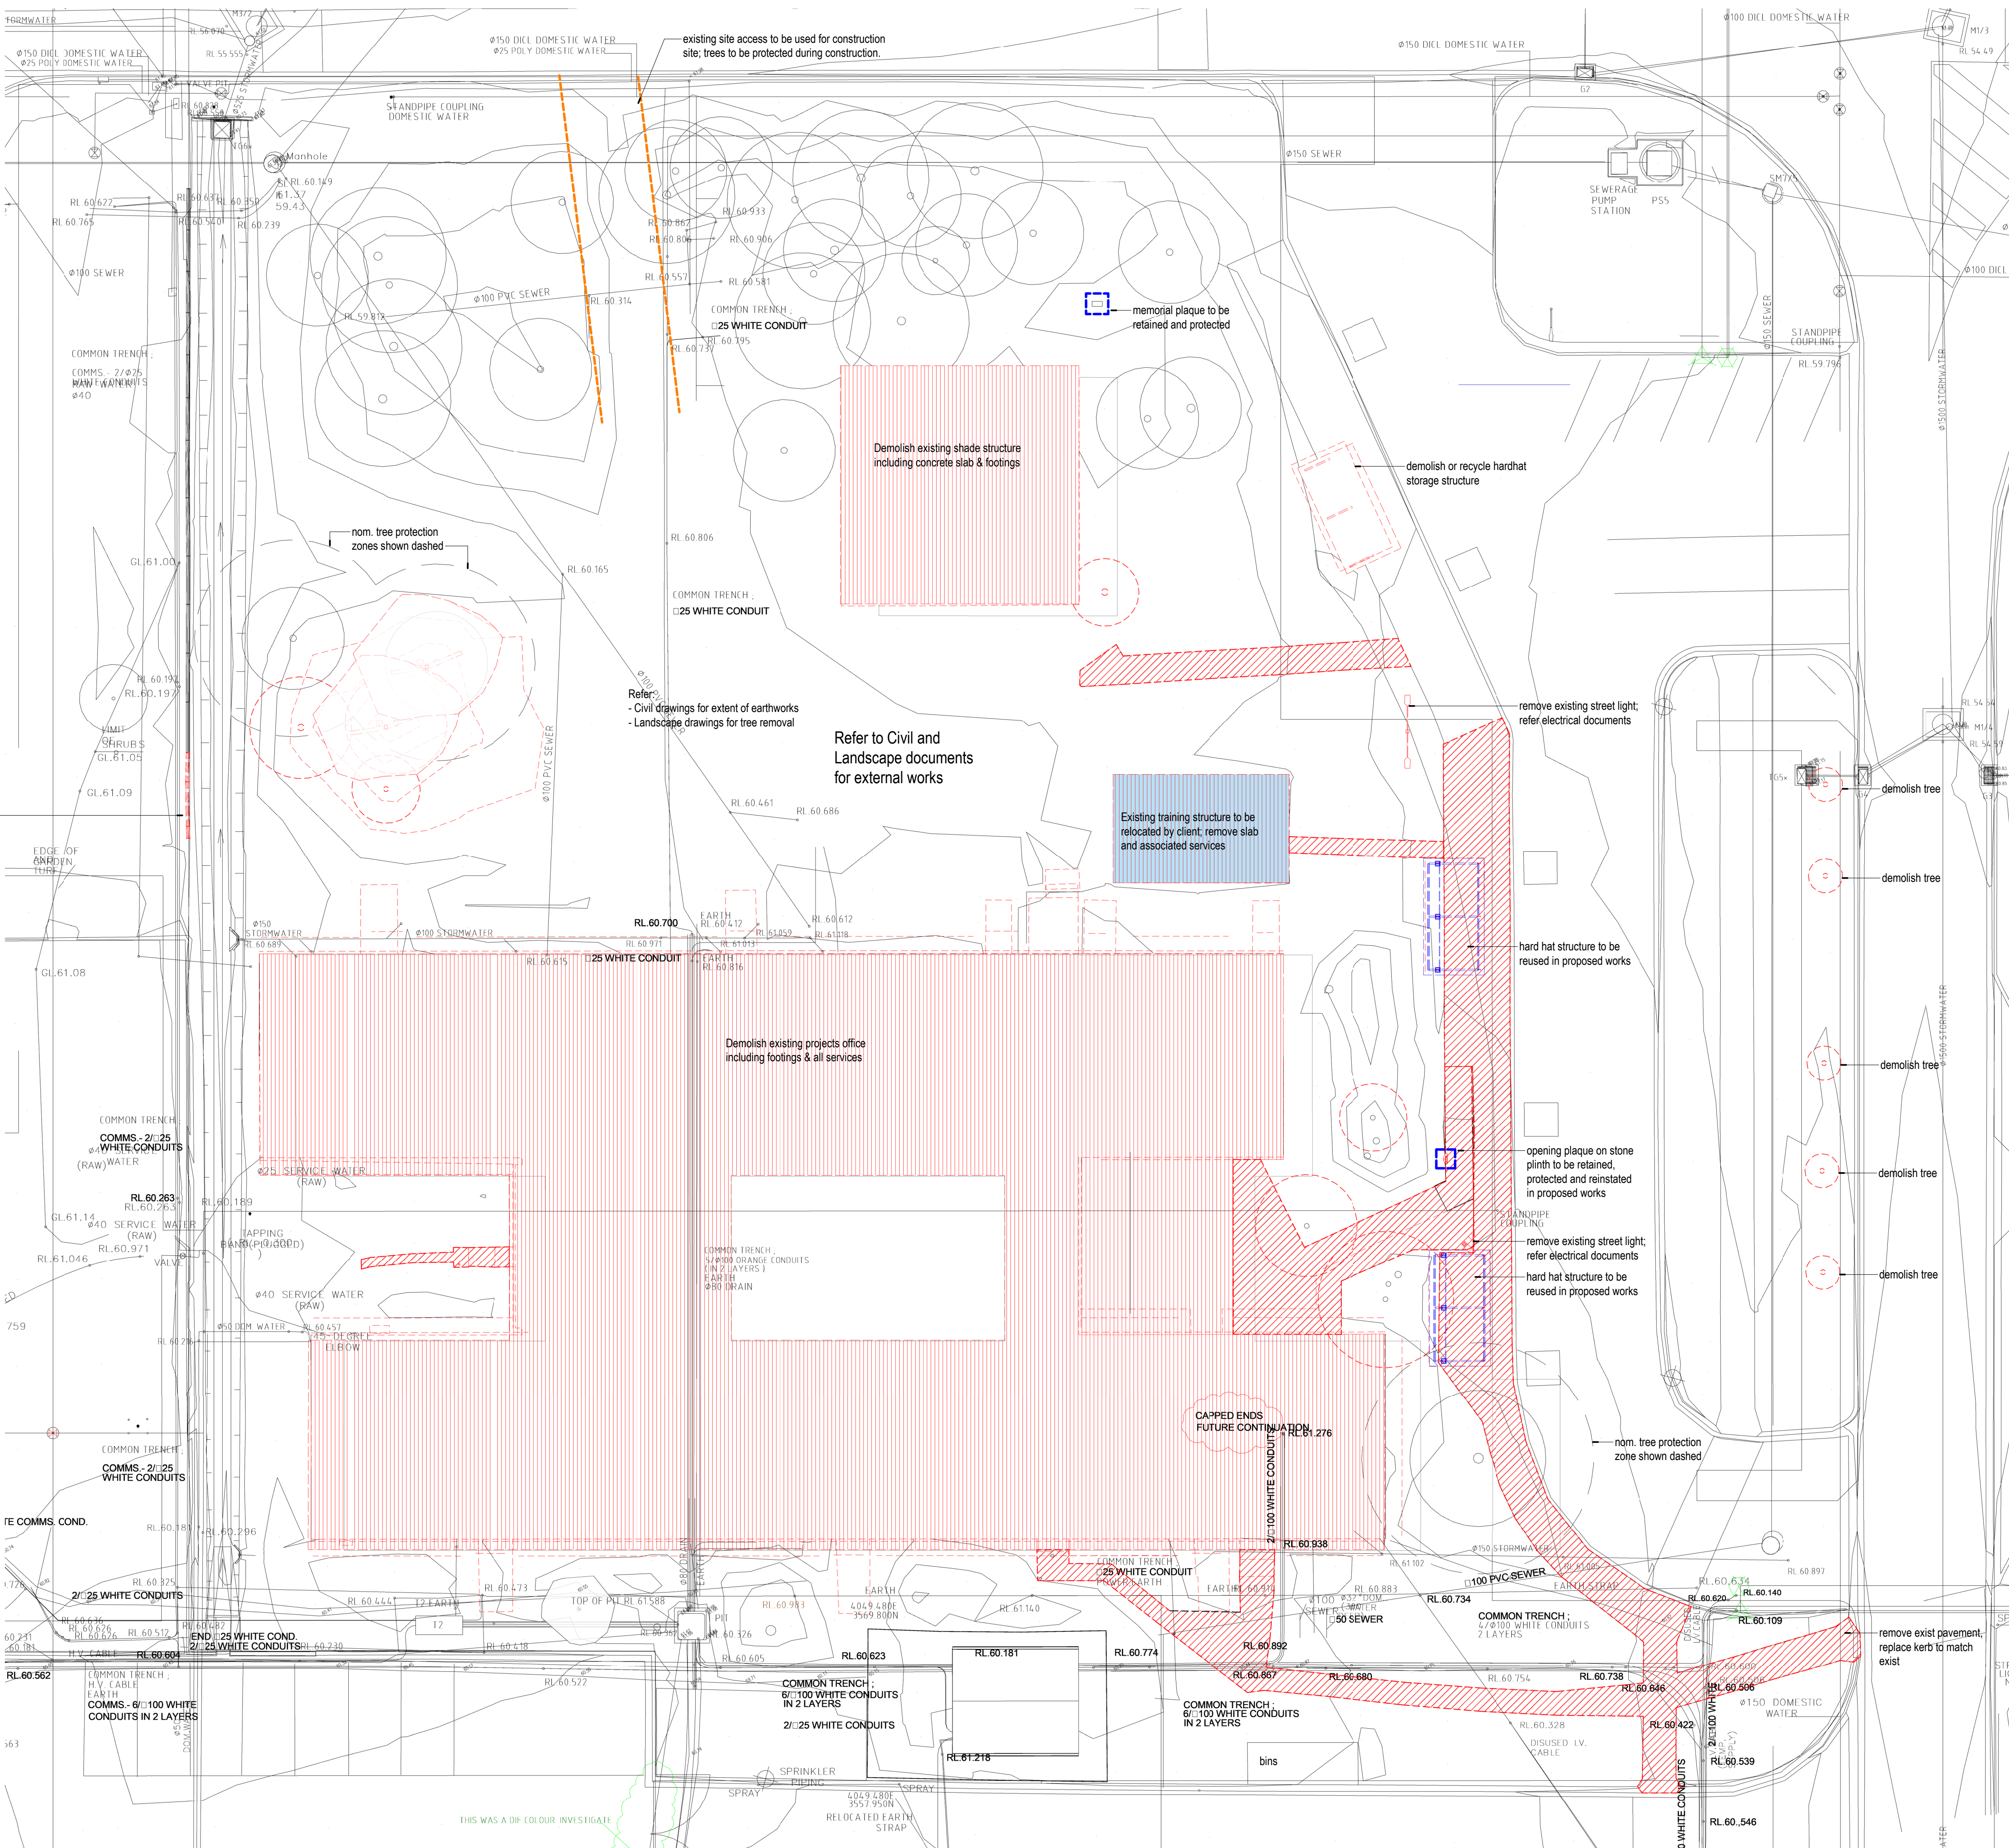

DEMOLITION LEGEND

Notional extent of demolition -
demolished items shown dashed

DEMOLITION NOTES

DN.01 This plan is notional only and does not indicate full extent of demolition. The Contractor is to familiarise themselves with the building to understand extent of demolition.

DN.02 All existing surfaces and finishes to remain that are damaged, modified or affected by the demolition works are to be made good and smooth in finish.

DN.03 Remove all services not required back to point of origin in accordance with the relevant codes and local authority requirements. Refer also consultants documents.

DN.04 If the contractor finds asbestos on site, notify the superintendent immediately.

DN.05 "Hard Hat" structures to be dismantled and retained for re-use. Refer to A-810001 for details of re-build.

DN.06 Trees to remain are to be protected;
refer ot the Architectural Specification.

PRELIMINARY
NOT FOR CONSTRUCTION

Drawings include colour information. A black & white copy may not have all the information. This background is coloured blue.

brian hooperarchitect
m3architecture

ph: +61 7 3831 4644
11 saint james street petrie tce q 4000
info@m3architecture.com
www.m3architecture.com

client  stanwell

project Stanwell New Projects Office
Switchyard Road,
Stanwell, QLD, 4702

title	Site Plan - Existing + Demolition
-------	-----------------------------------

drawn bg
checked jb
date March 2026
scale As indicated at A1
drawing 25010 / cd A-040002 / T1



copyright ©
These designs, plans, specifications and the copyright herein are the property of the architect and must not be used, reproduced, or copied wholly or in part without the written permission of m3architecture pty ltd abn 23 079 044 545.
Use figured dimensions in preference to scale.

0 1 2 3 4 5 6 7 8 9 10m