


9/03/2026 12:21:18 PM C:\Projects\STANWELL-Building\HPC-Central\Files\_jaydn.b.rvt

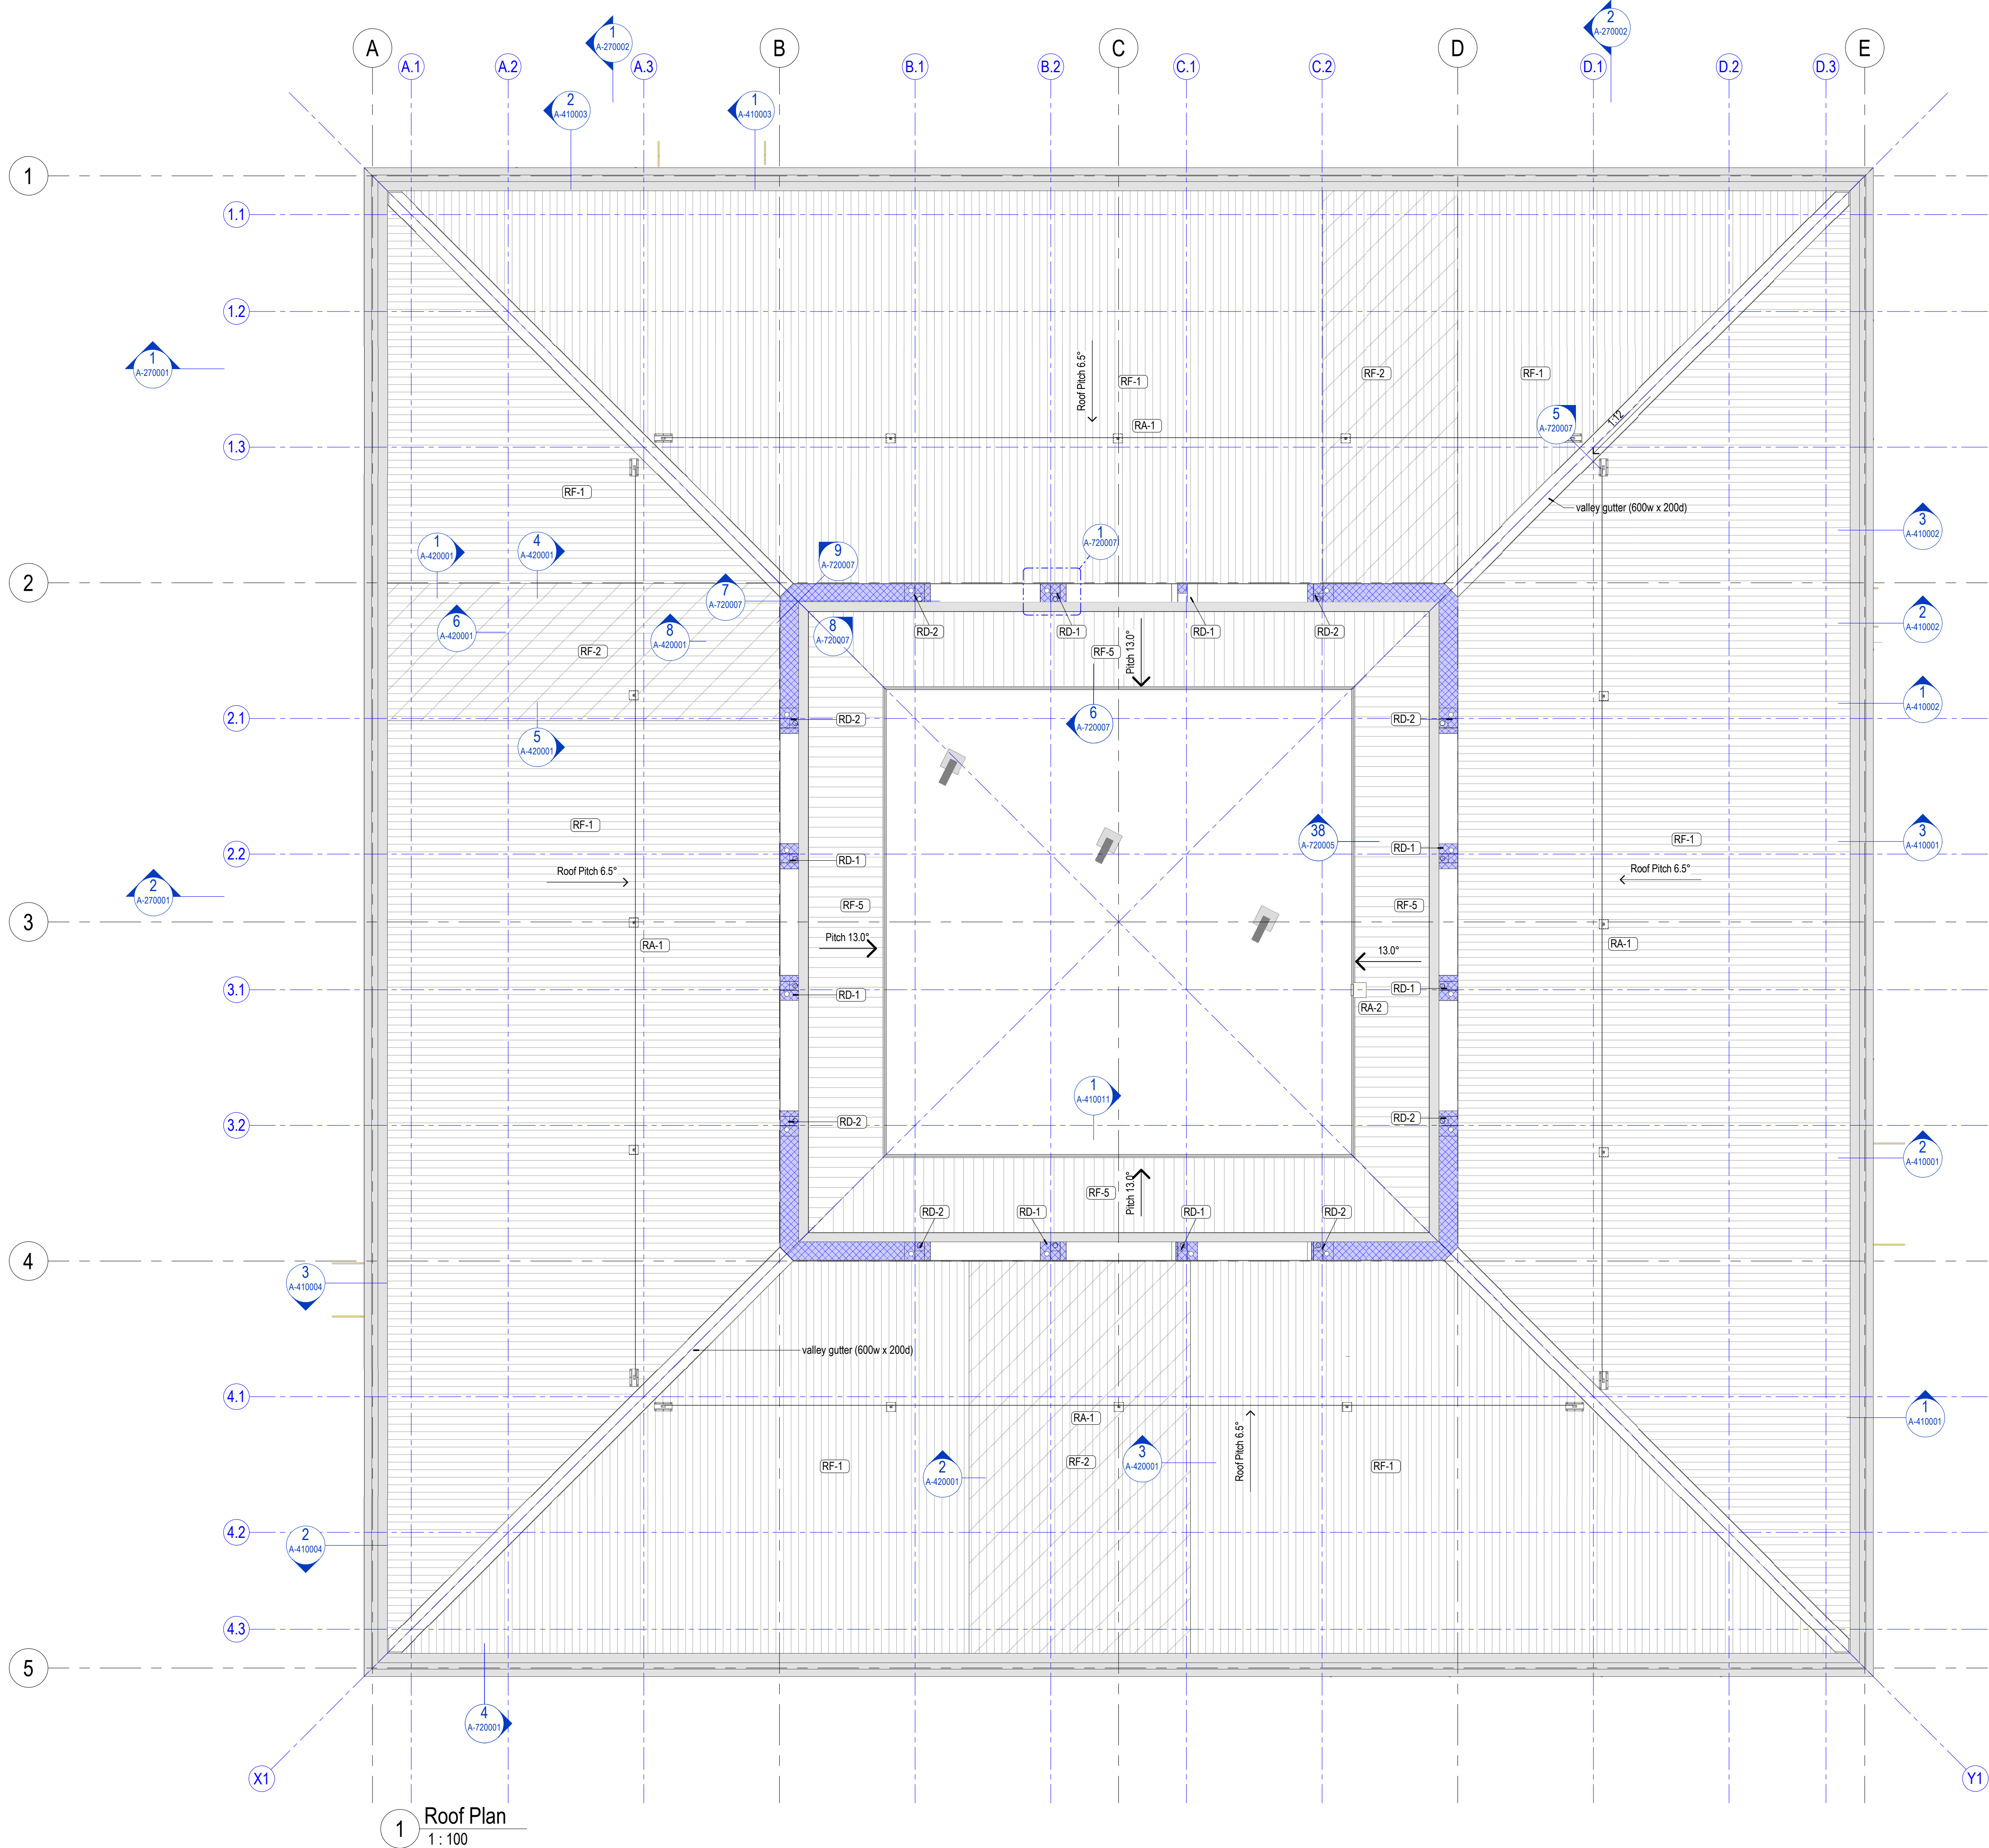

1 Roof Plan  
1 : 100

## ROOF NOTES

- rev date description initial  
T1 11/03/2026 For Tender JB
- RN.01 UNO all roof flashings to match roof sheeting.
- RN.02 Provide roof access system to relevant australian standards. Provide a design construct certification of the proposed system.
- RN.03 Design, construct & install all flashings, cappings etc to make roof weatherproof
- RN.04 Trusses shown are indicative only. Actual sizes, configurations & spacings to be designed and certified by the truss supplier. Refer to structural documents for design parameters.
- RN.05 Refer also to Mechanical and Hydraulic Services documents for roof penetrations.
- RN.06 AC voids are penetrations through plant space floors for mechanical supply and return; refer to mechanical and acoustic documents.

## ROOF LEGEND

-  box gutter sump - refer to hydraulic docs for performance based brief

PRELIMINARY  
NOT FOR CONSTRUCTION

Drawings include colour information. A black & white copy may not have all the information. This background is coloured blue.

brian hooper**architect**  
**m3architecture**  
ph: +61 7 3831 4644  
11 saint james street petrie tce q 4000  
info@m3architecture.com  
www.m3architecture.com

client  **stanwell**

project **Stanwell New Projects Office**  
Switchyard Road,  
Stanwell, QLD, 4702

title **Roof Plan**

drawn bg  
checked jb  
date March 2026  
scale 1 : 100 at A1  
drawing **25010 / cd A-200002 / T1**

copyright ©  
These designs, plans, specifications and the copyright herein are the property of the architect and must not be used, reproduced, or copied wholly or in part without the written permission of m3architecture Pty Ltd abn 23 079 044 545. Use figured dimensions in preference to scale. If there are any questions contact the architect.

1:100 at A1  
0 1 2 3 4 5m