


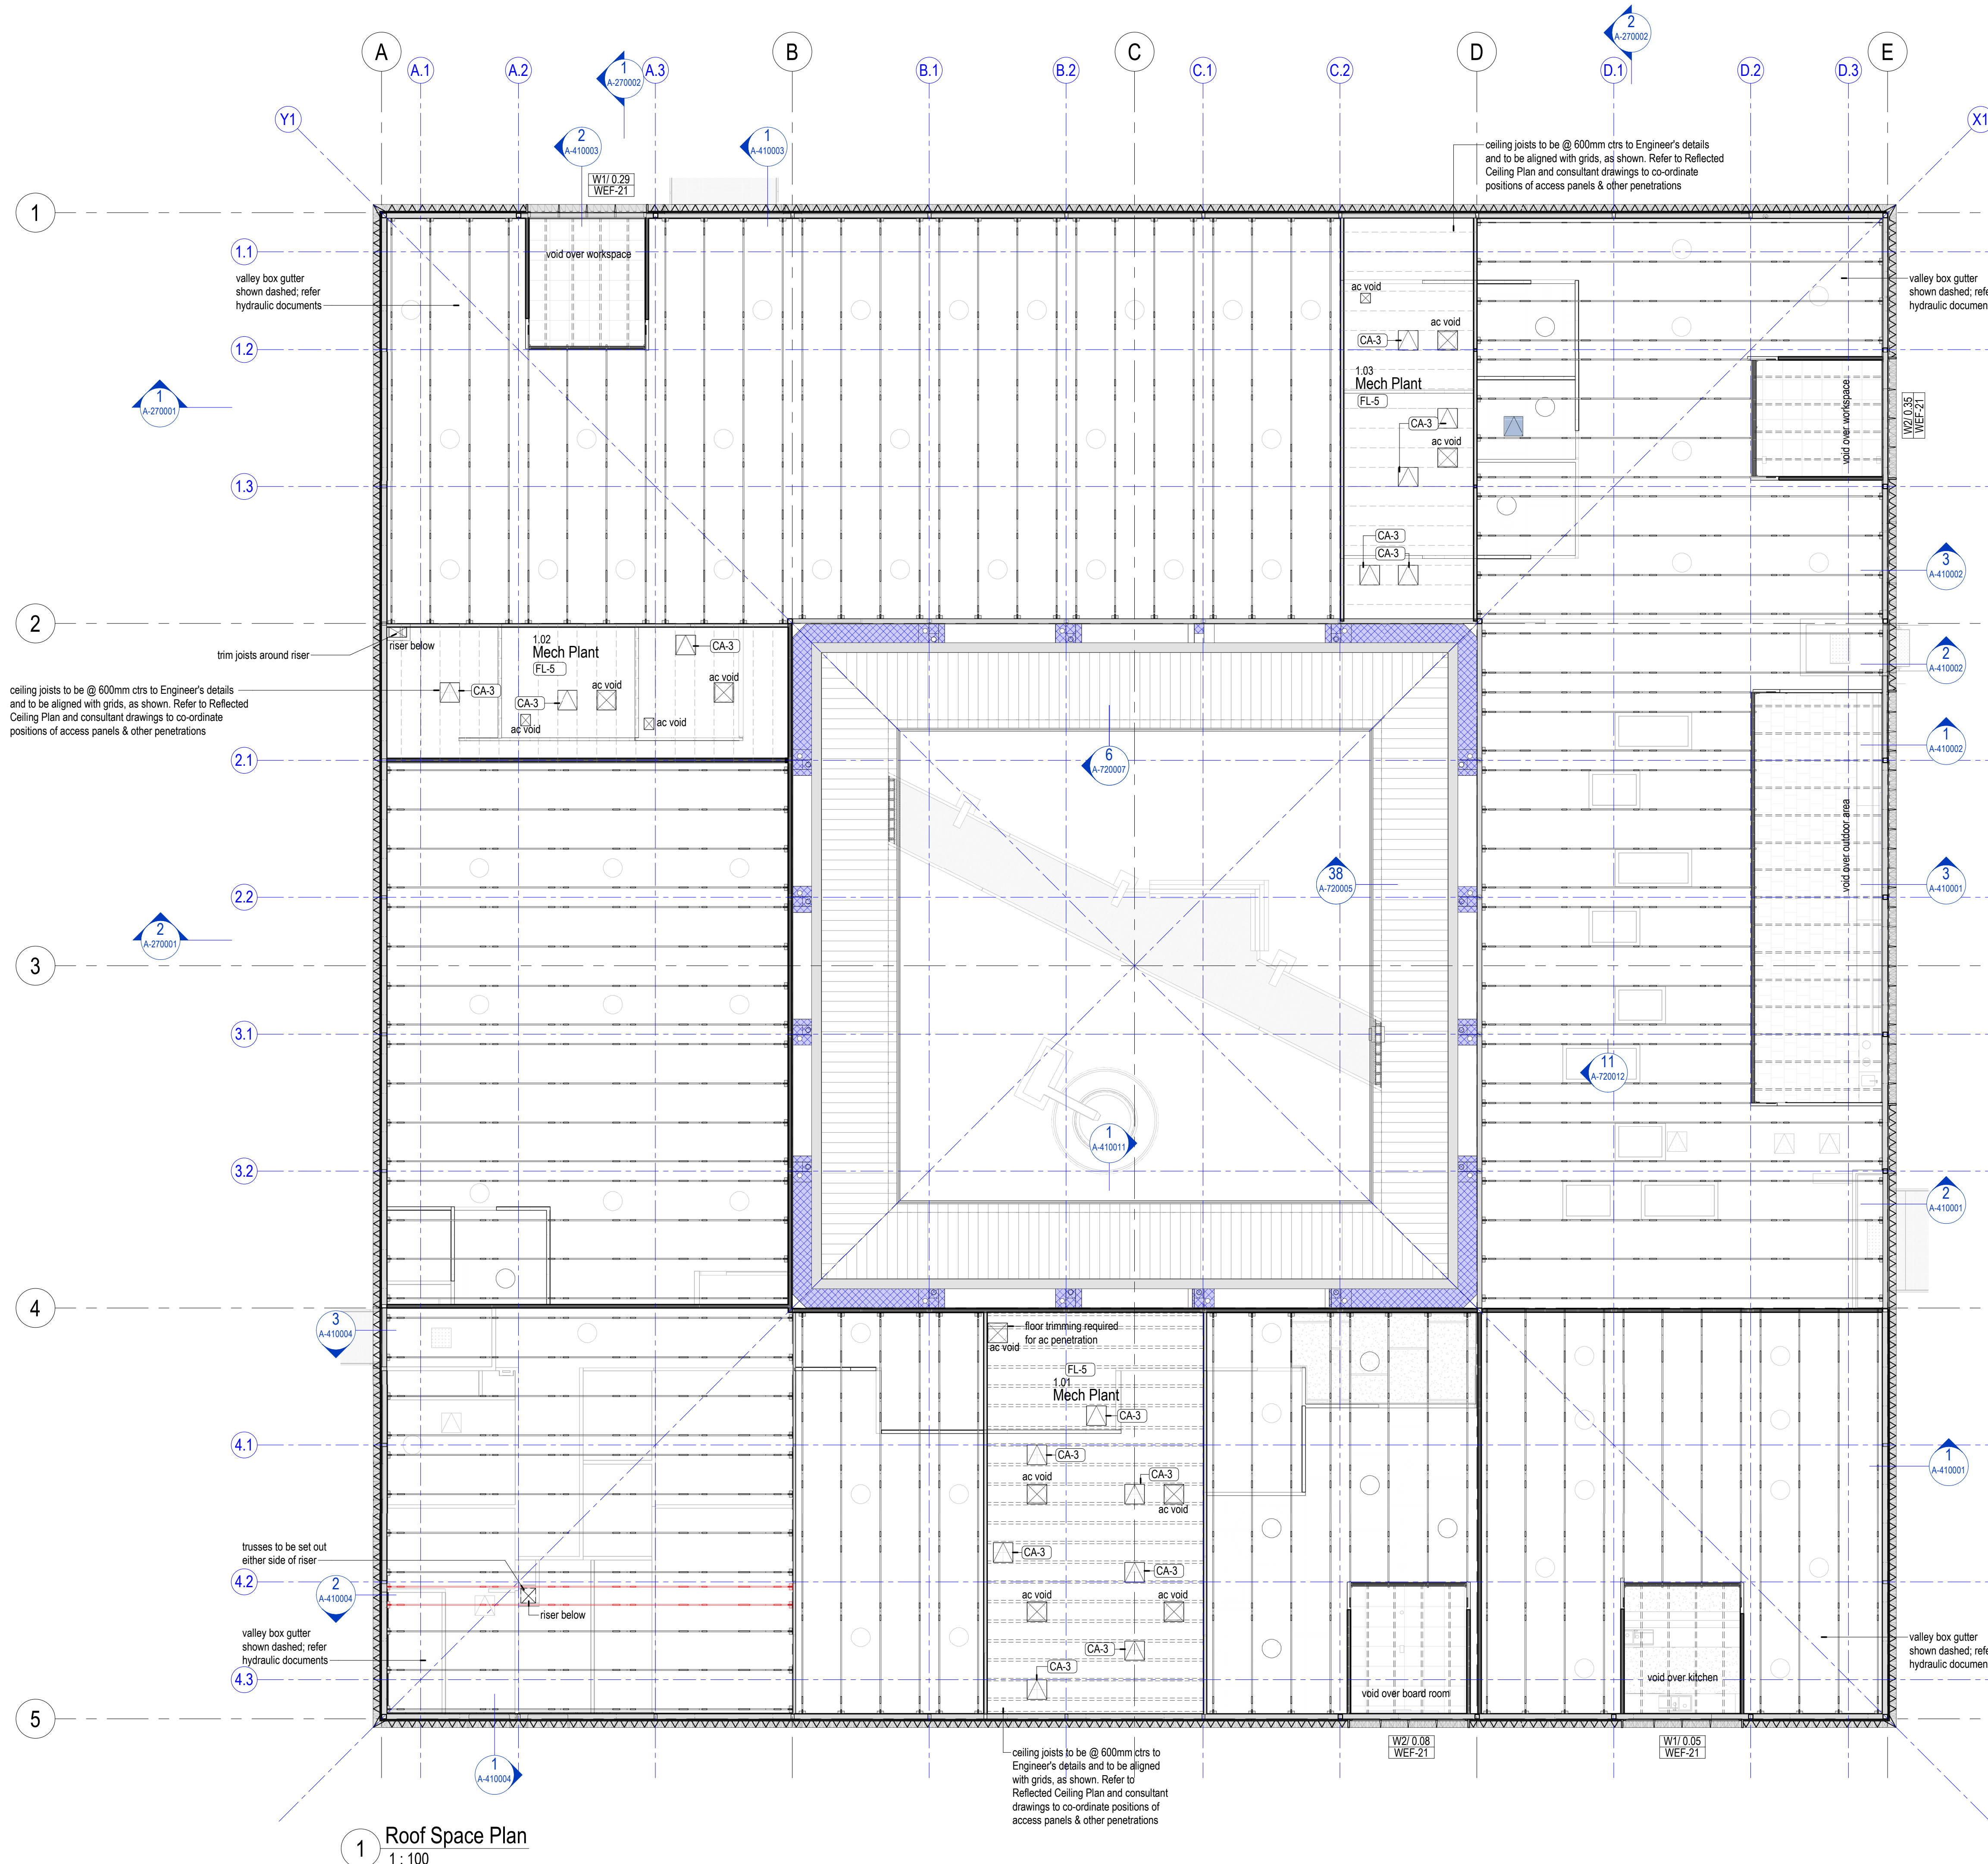

## ROOF NOTES

- |       |   |
|-------|---|
| RN.01 | UNO all roof flashings to match roof sheeting.   |
| RN.02 | Provide roof access system to relevant Australian standards. Provide a design construct certification of the proposed system.                                                       |
| RN.03 | Design, construct & install all flashings, capings etc to make roof weathertight   |
| RN.04 | Trusses shown are indicative only. Actual sizes, configurations & spacings to be designed and certified by the truss supplier. Refer to structural documents for design parameters. |
| RN.05 | Refer also to Mechanical and Hydraulic Services documents for roof penetrations.   |
| RN.06 | AC voids are penetrations through plant space floors for mechanical supply and return; refer to mechanical and acoustic documents.                                                  |

### ROOF LEGEND

-  box gutter sump - refer to hydraulic docs for performance based brief

PRELIMINARY  
NOT FOR CONSTRUCTION

Drawings include colour information. A black & white copy may not have all the information  
This background is coloured blue.

**brian hooperarchitect**  
**m3architecture**  
ph: +61 7 3831 4644  
11 saint james street petrie tce q 4000  
info@m3architecture.com  
www.m3architecture.com

client  stanwell

project Stanwell New Projects Office  
Switchyard Road,  
Stanwell, QLD, 4702

title Roof Cavity Plan

drawn bg  
checked jb  
date March 2026  
scale 1 : 100 at A1  
drawing 25010 / cd A-200003 / T1

**copyright ©**  
These designs, plans, specifications and the  
copyright herein are the property of the architect  
and must not be used, reproduced, or copied  
wholly or in part without the written permission of  
m3architecture pty ltd abn 23 079 044 545.  
Use figured dimensions in preference to scale.  
If there are any questions contact the architect.

0 1 2 3 4 5m