


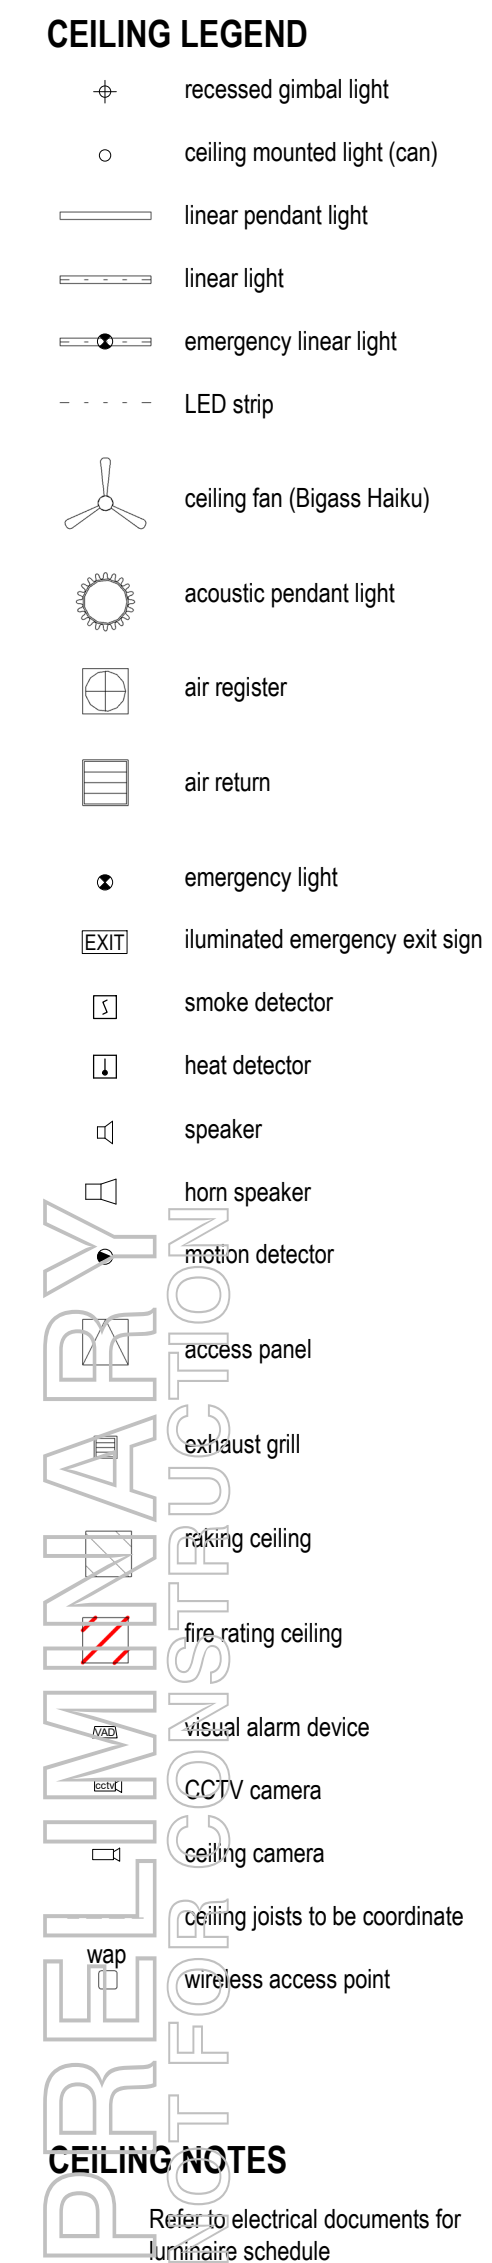

brian hooperarchitect
m3architecture

ph: +61 7 3831 4644
11 saint james street petrie tce q 4000
info@m3architecture.com
www.m3architecture.com

project Stanwell New Projects Office
Switchyard Road,
Stanwell, QLD, 4702

rawn mk
cked jb
date March 2026
scale 1 : 100 at A1
wing 25010 / cd A-210001 / T1

copyright ©
These designs, plans, specifications and the copyright herein are the property of the architect and must not be used, reproduced, or copied wholly or in part without the written permission of m3architecture Pty Ltd abn 23 079 044 545.
Use figured dimensions in preference to scale.

