


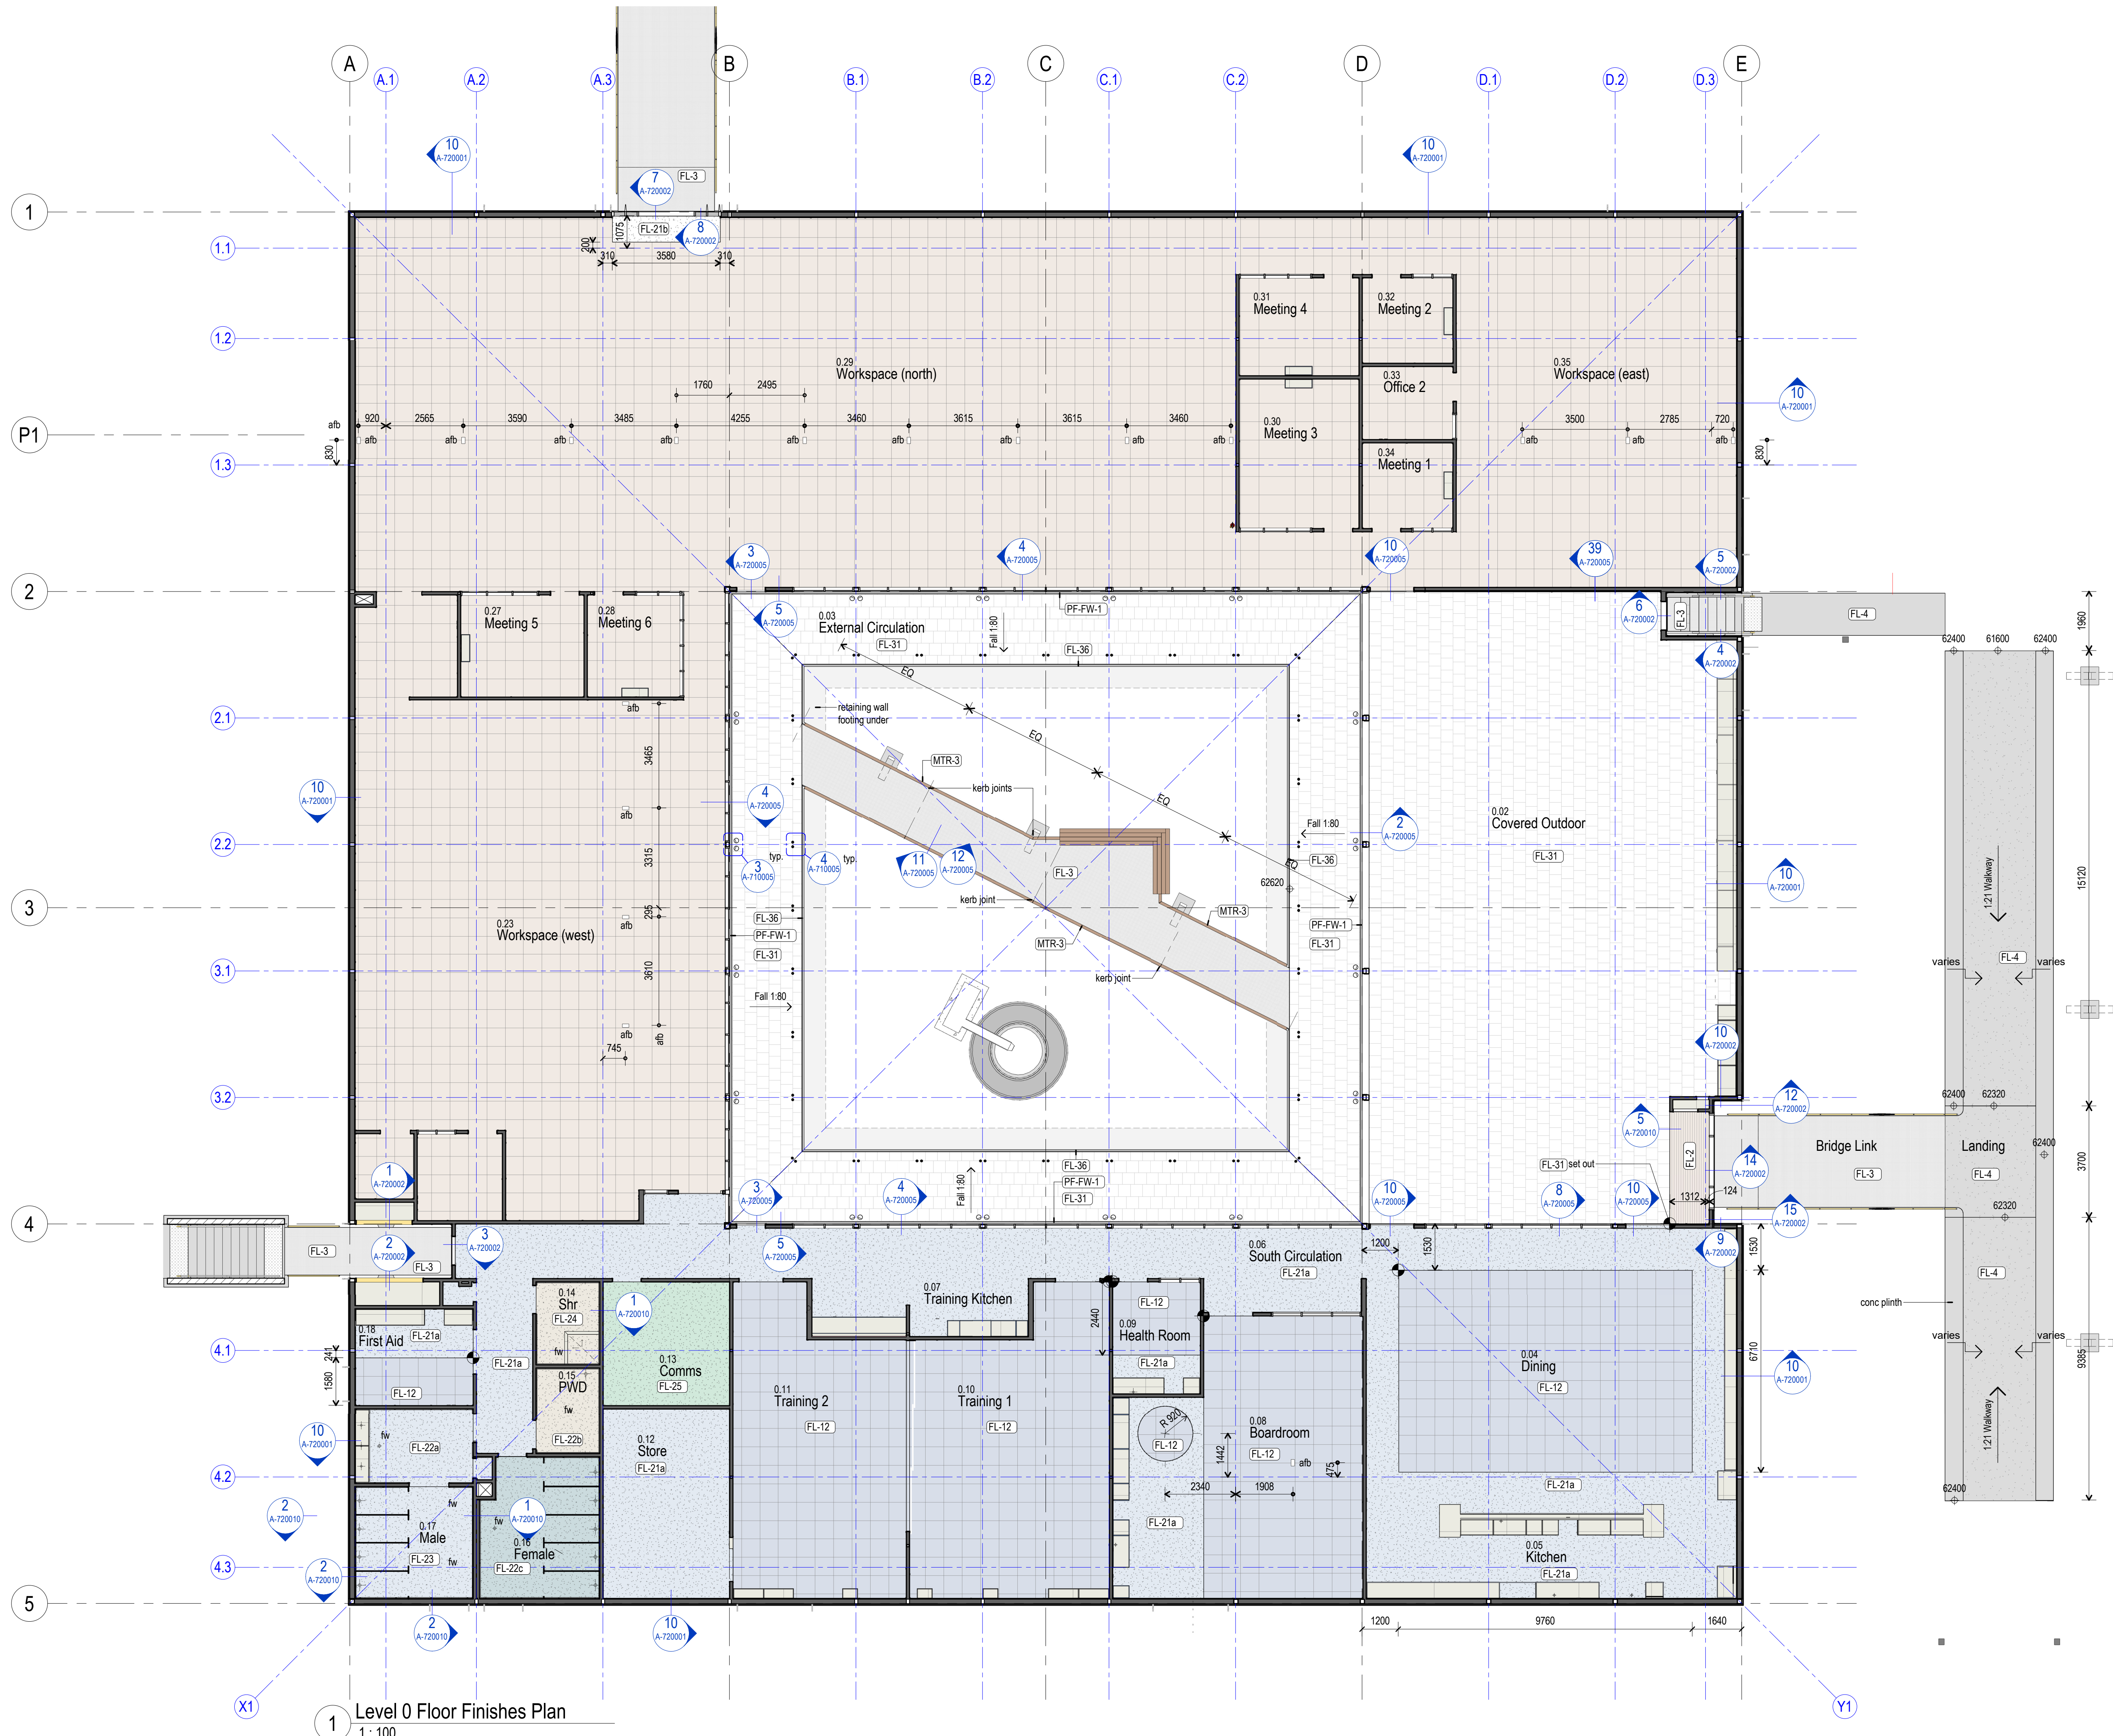

FLOOR FINISHES NOTES

- FN.01 The A-23 series Floor Finishes plans show applied finished only - refer A-30 series drawings for concrete floor finishes.
- FN.02 Refer T-sheet & internal elevations for extent and type of skirtings.
- FN.03 UNO all changes in floor finishes at doorways to be centred on door leaf, refer to door schedule and detail references.
- FN.04 For finishes of stair and ramps including nosings & tactile indicators refer to A-50 series drawings.
- FN.05 Ensure adjacent floor finishes are flush in accordance with AS1428.1 Section 7: Continuous Accessible Path of Travel. Adjust concrete substrate and/or fill to suit.
- FN.06 For threshold details between different floor finishes, refer to details on A-660001.
- FN.07 Pressure clean existing exposed slabs within scope area.
- FN.08 Protect existing flooring to be retained during construction.

PRELIMINARY
NOT FOR CONSTRUCTION

Drawings include colour information. A black & white copy may not have all the information. This background is coloured blue.

brian hooperarchitect
m3architecture
ph: +61 7 3831 4644
11 saint james street petrie tce q 4000
info@m3architecture.com
www.m3architecture.com

client **stanwell**

project **Stanwell New Projects Office**
Switchyard Road,
Stanwell, QLD, 4702

title **Floor Finishes Plan**

drawn mk
checked jb
date March 2026
scale 1:100 at A1
drawing **25010 / cd A-230001 / T1**

copyright ©
These designs, plans, specifications and the copyright herein are the property of the architect and must not be used, reproduced, or copied wholly or in part without the written permission of m3architecture Pty Ltd abn 23 079 044 545. Use figured dimensions in preference to scale. If there are any questions contact the architect.

1:1 at A1
0 10 20 30 40 50mm