
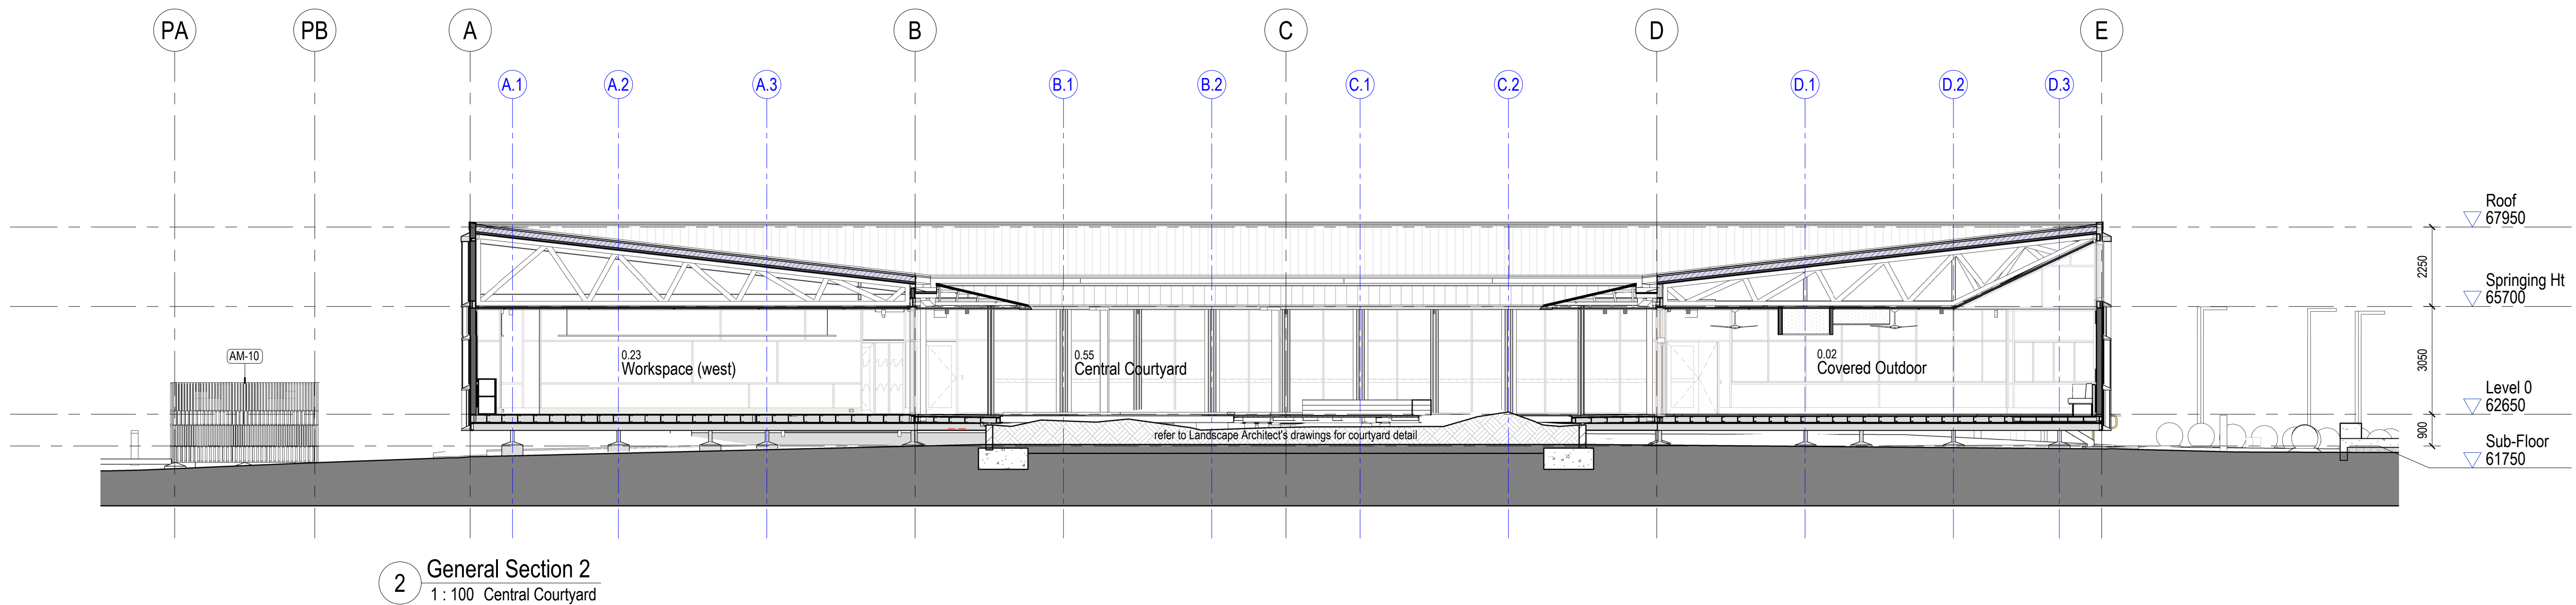


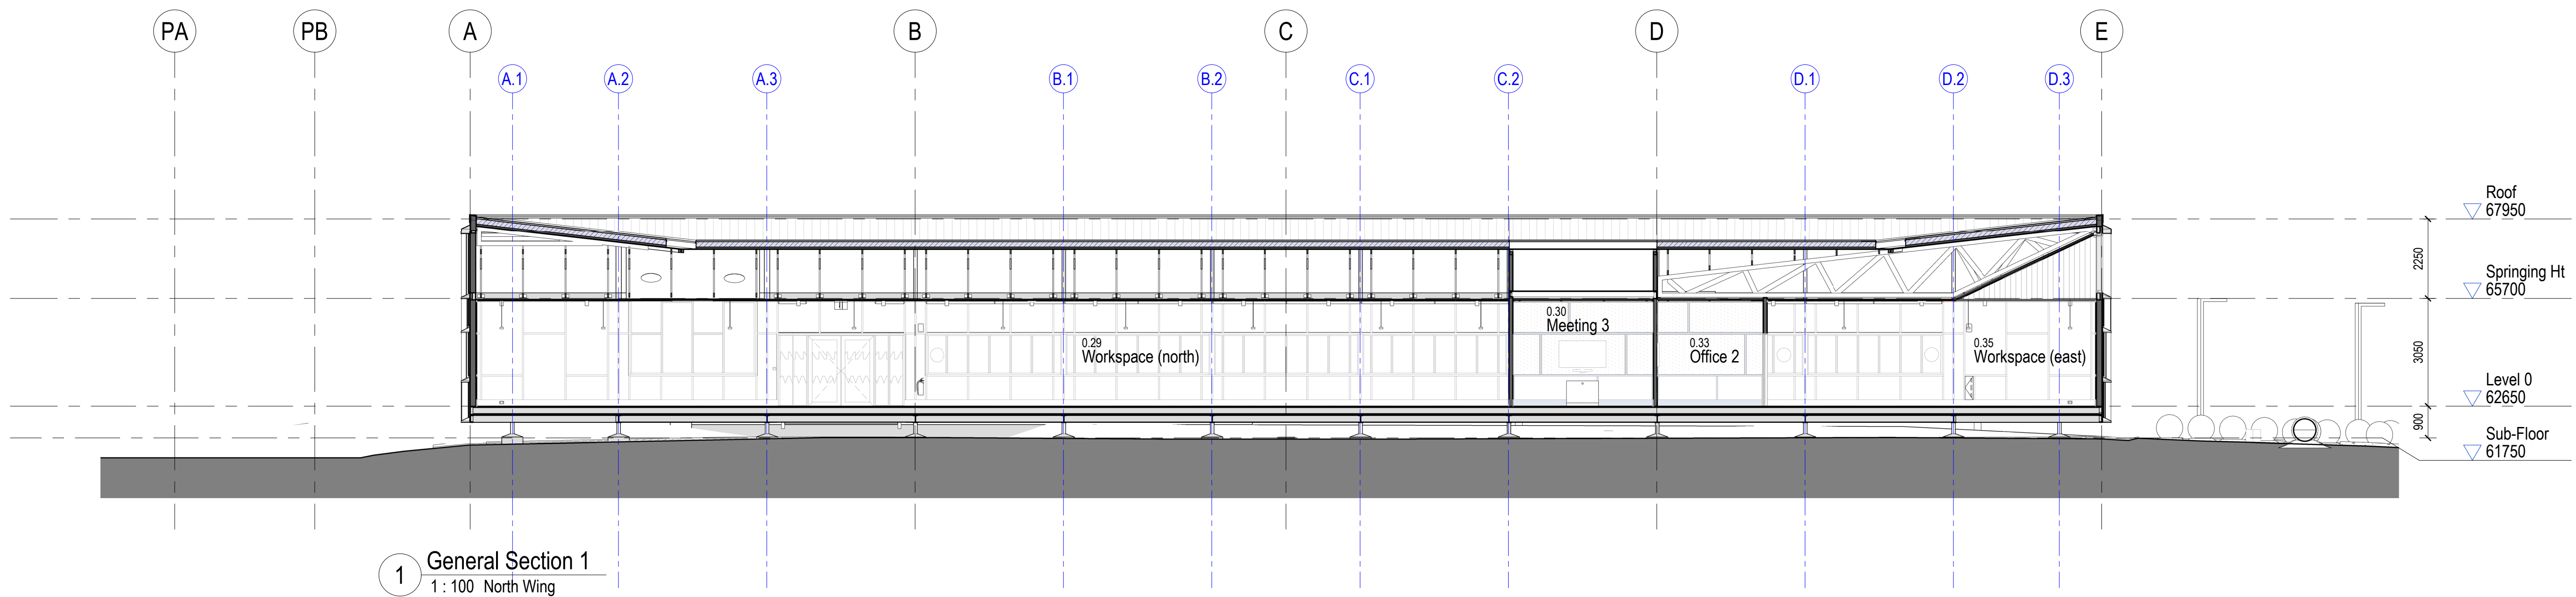

GA NOTES

- GN.01 UNO all partitions and glazing to go to u/s ceiling. Provide bracing / propping to u/s of trusses as required.
- GN.02 Services not shown in ceiling space for clarity. Framing in ceiling space is indicative only.
- GN.03 Confirm all dimensions on site prior to starting work.
- GN.04 Internal planters shown grey nic.
- GN.05 For trusses refer to structural drawings. Trusses are shown indicatively. Truss set out is critical for mechanical servicing. Changes to the truss set out to be approved by the superintendent, contractor to coordinate services.

PRELIMINARY
NOT FOR CONSTRUCTION

Drawings include colour information. A black & white copy may not have all the information. This background is coloured blue.

brian hooper**architect**
m3architecture
ph: +61 7 3831 4644
11 saint james street petrie tce q 4000
info@m3architecture.com
www.m3architecture.com

client  **stanwell**

project **Stanwell New Projects Office**
Switchyard Road,
Stanwell, QLD, 4702

title **General Sections**

drawn bg
checked jb
date March 2026
scale 1:100 at A1
drawing 25010 / cd A-270001 / T1

copyright ©
These designs, plans, specifications and the copyright herein are the property of the architect and must not be used, reproduced, or copied wholly or in part without the written permission of m3architecture Pty Ltd abn 23 079 044 545. Use figured dimensions in preference to scale. If there are any questions contact the architect.

1:100 at A1
0 1 2 3 4 5m