


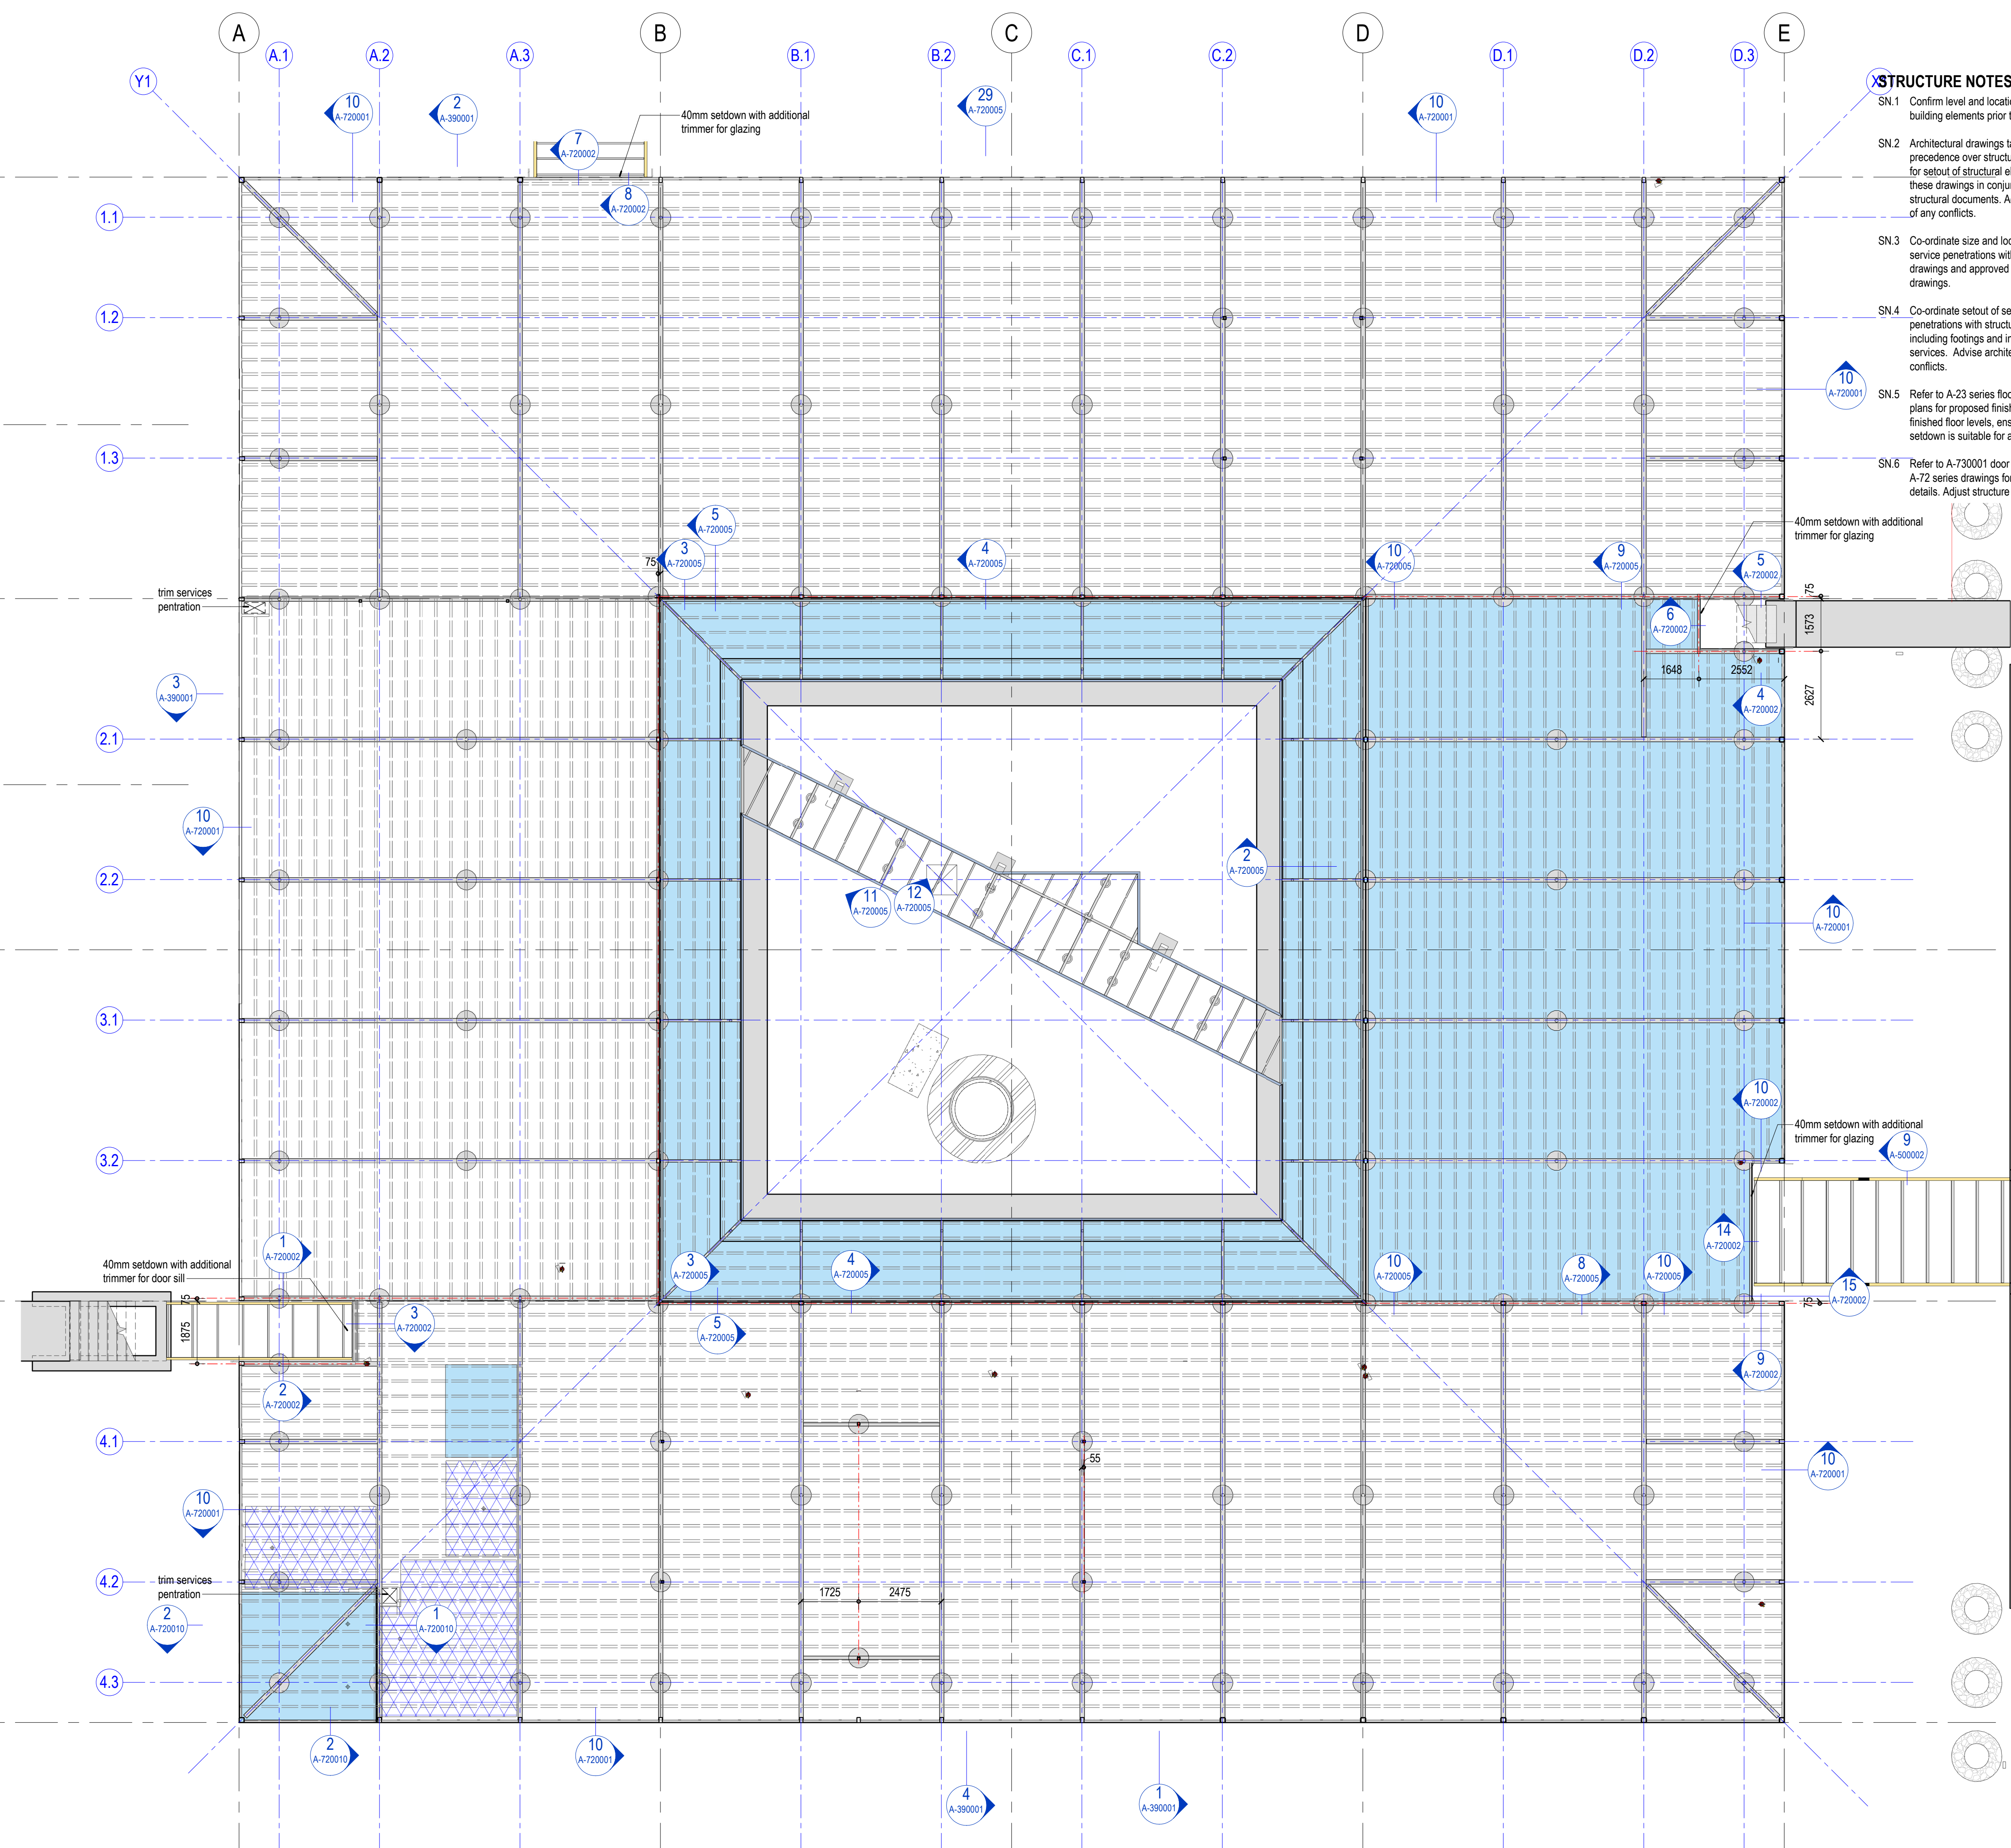

STRUCTURE NOTES

- SN.1 Confirm level and location of existing building elements prior to construction.
- SN.2 Architectural drawings take precedence over structural documents for setout of structural elements. Read these drawings in conjunction with structural documents. Advise architect of any conflicts.
- SN.3 Co-ordinate size and location of service penetrations with consultant drawings and approved shop drawings.
- SN.4 Co-ordinate setout of service penetrations with structural documents including footings and in-ground services. Advise architect of any conflicts.
- SN.5 Refer to A-23 series floor finishes plans for proposed finishes and finished floor levels. ensure finish and setback is suitable for applied finish.
- SN.6 Refer to A-730001 door schedule and A-72 series drawings for threshold details. Adjust structure setout to suit.

STRUCTURE NOTES cont.

- SN.7 Refer to A-05 series architectural setout drawings for setout of grids. All external steel work to be hot dip galvanised.
- SN.8 UNO Columns dimensioned to centre-line, where no dimension, centre on grid line.
- SN.9 Refer A-40 series Façade Elevations for setout of secondary steel associated with the façade.
- SN.10 Coordinate all SHS and RHS secondary steel within stud walls to have base plates contained within stud wall plane i.e. no visible base plates
- SN.11 For trusses refer to structural drawings. Trusses are shown indicatively. Truss set out is critical for mechanical servicing. Changes to the truss set out to be approved by the superintendent; contractor to coordinate services.

STRUCTURE LEGEND

- BOS Bottom of Structure
CHS Circular Hollow Section
EA Equal Angle
FFL Finished Floor Level
FSL Finished Structural Level
FW Floor Waste
GD Grated Drain
GP Gully Pit
HS Hydraulic Stack
IOS Inspection Opening to Surface
SHS Square Hollow Section
SSL Structural Slab Level
TOH Top of Concrete Hob
TOS Top of Structure
WCB Concrete Block Wall
WB Wall Beam
WO Waste Outlet (refer hydraulic spec)

- STEP**
Step in slab, number indicates difference between levels (mm)
Existing concrete
New concrete slab
New suspended FC deck
New suspended FC deck with Waterproof membrane
New suspended FC deck, setback
New suspended FC deck, setback with Waterproof membrane (as coded)
New concrete block wall built on concrete slab/footing

- I O**
Steel columns
Dashed line indicates footings / pile caps / beams below
Saw Dowel Joint
Dowel Expansion Joint
CLT Joint Line
Waterproof Membrane
Waterproof Membrane (Below)

- Steel setout dimensions
Hob setout dimensions
Penetration setout dimensions
Centre-line of steel structure

Drawings include colour information. A black & white copy may not have all the information. This background is coloured blue.

**brian hooperarchitect
m3architecture**
ph: +61 7 3831 4644
11 saint james street petrie tce q 4000
info@m3architecture.com
www.m3architecture.com

client **stanwell**

project **Stanwell New Projects Office
Switchyard Road,
Stanwell, QLD, 4702**

title **Structure Outline Sub-Floor
Plan**

drawn bg
checked jb
date March 2026
scale 1:100 at A1
drawing 25010 / cd A-300002 / T1

copyright ©
These designs, plans, specifications and the copyright herein are the property of the architect and must not be used, reproduced, or copied wholly or in part without the written permission of m3architecture Pty Ltd abn 23 079 044 545.
Use figured dimensions in preference to scale. If there are any questions contact the architect.

1 Sub-Floor Plan
1:100