


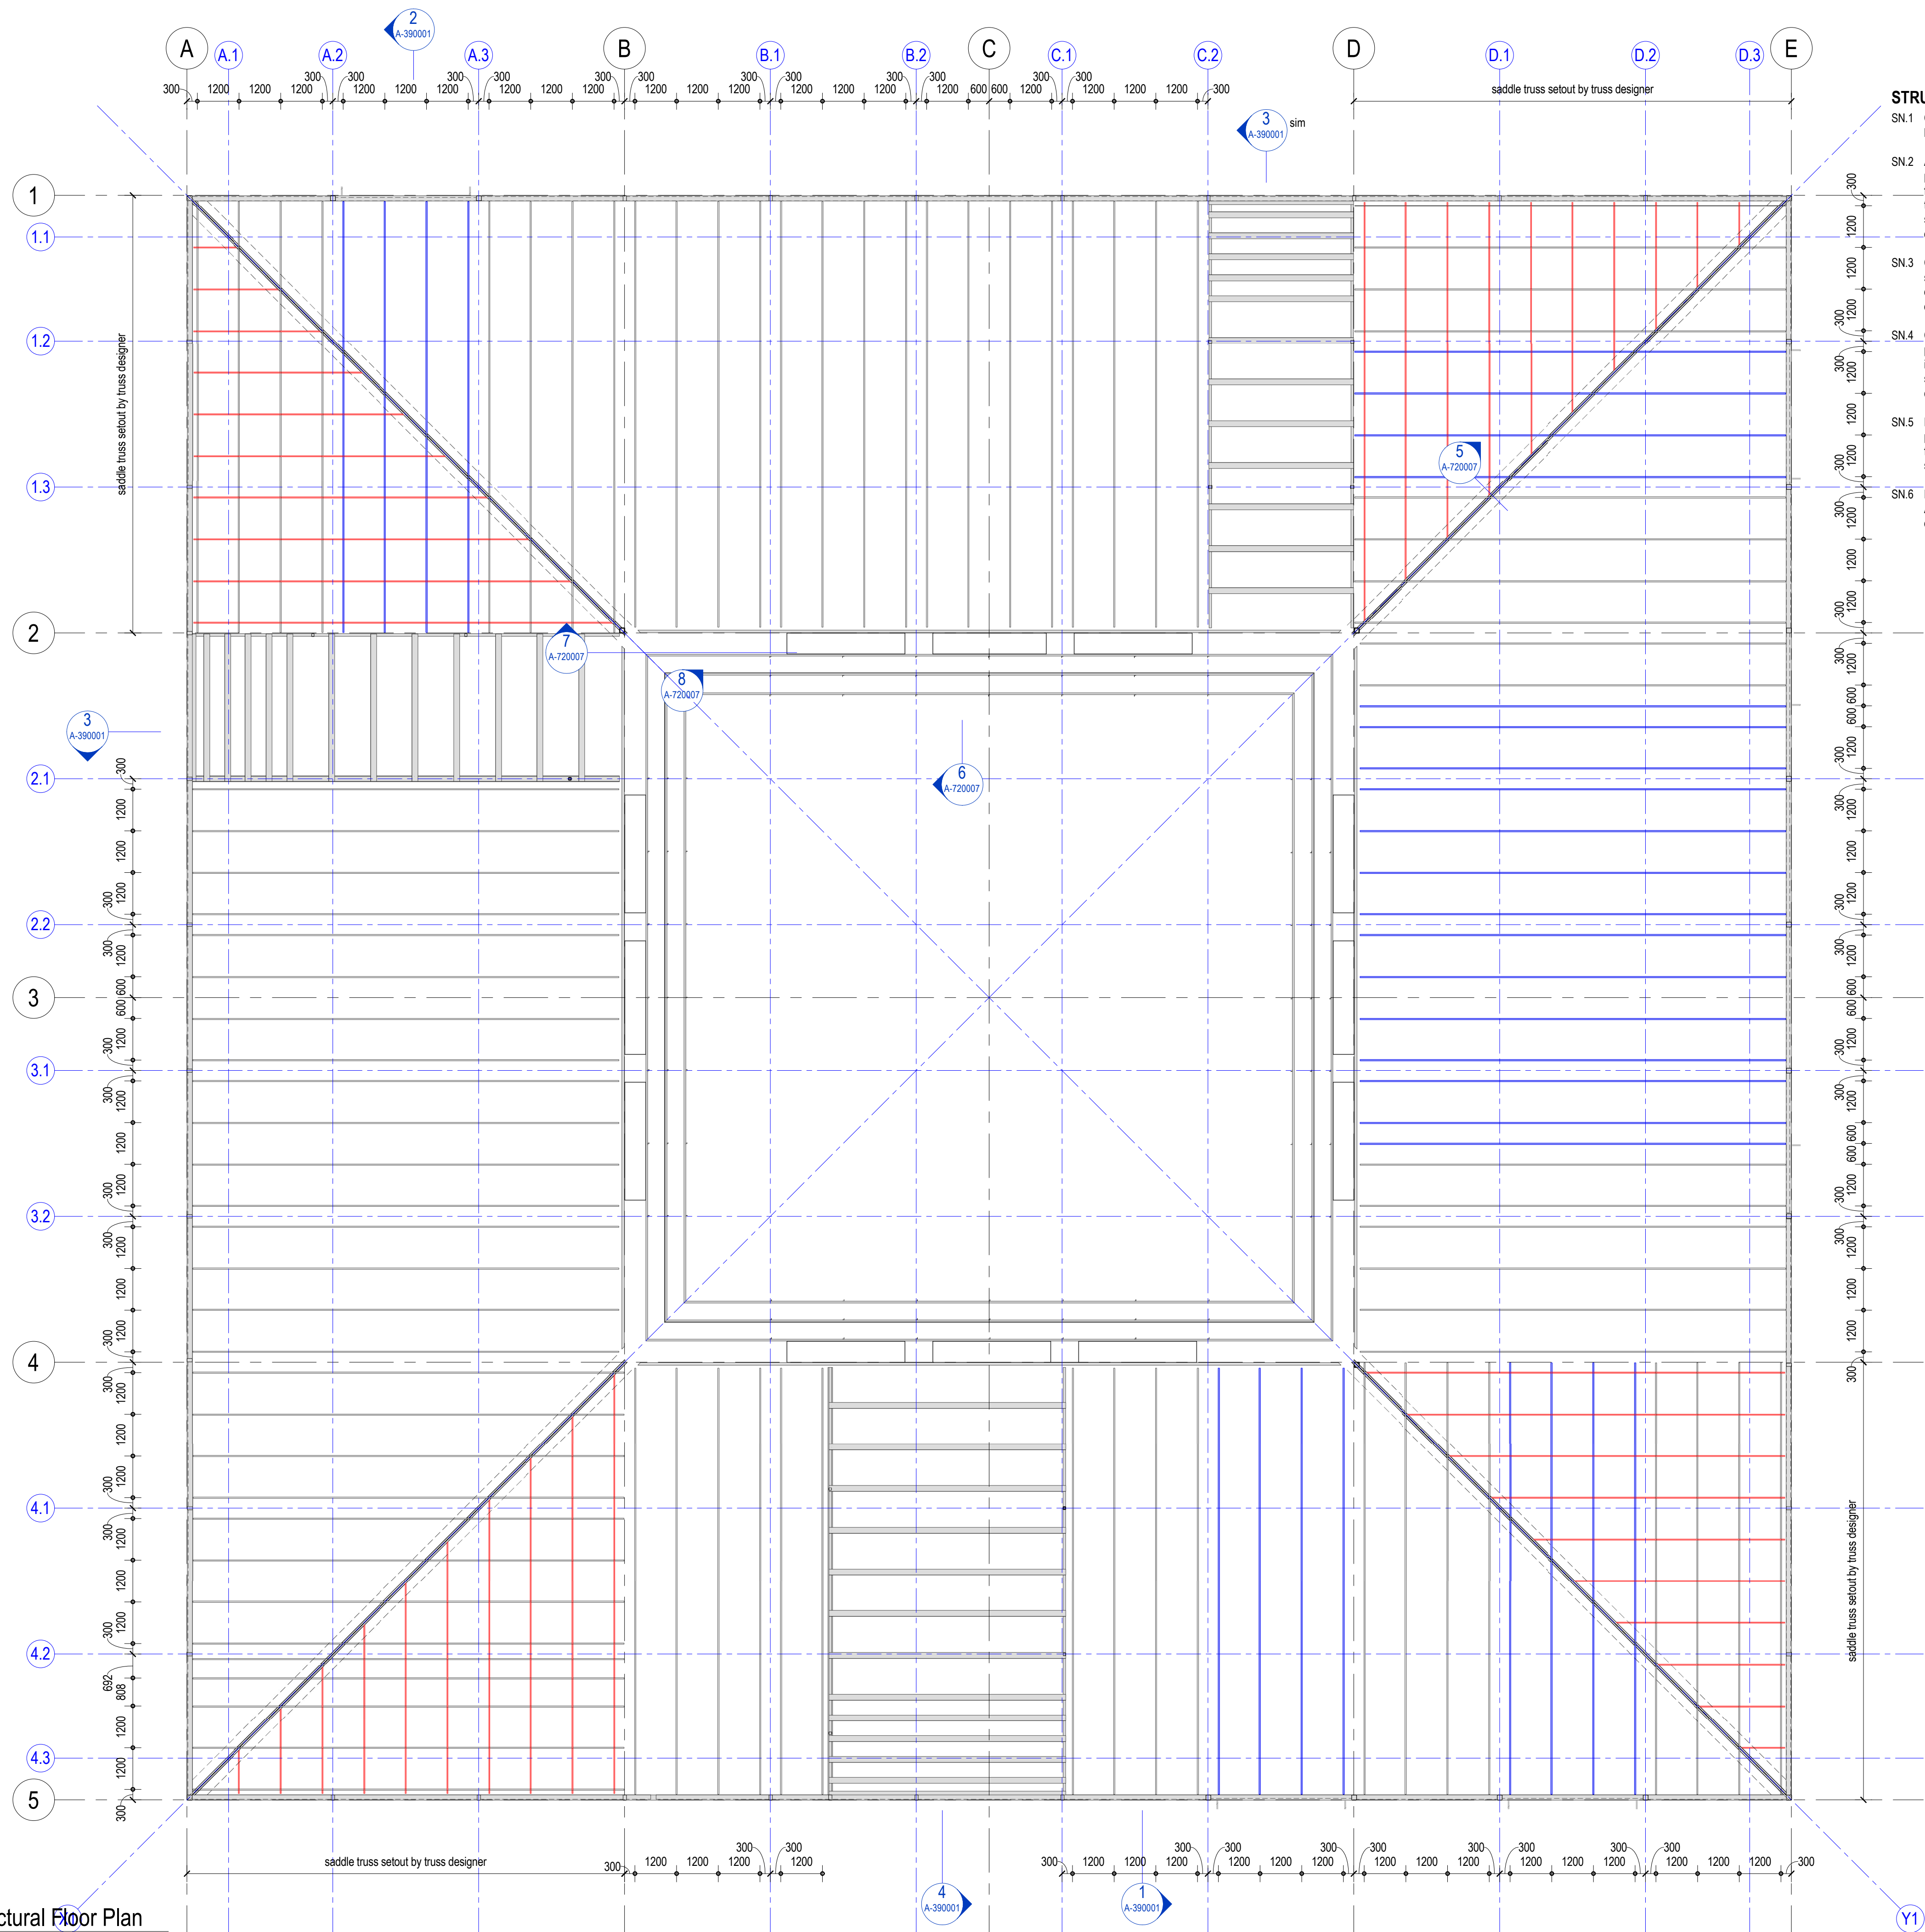

STRUCTURE NOTES

- SN.1 Confirm level and location of existing building elements prior to construction.
- SN.2 Architectural drawings take precedence over structural documents for setout of structural elements. Read these drawings in conjunction with structural documents. Advise architect of any conflicts.
- SN.3 Co-ordinate size and location of service penetrations with consultant drawings and approved shop drawings.
- SN.4 Co-ordinate setout of service penetrations with structural documents including footings and in-ground services. Advise architect of any conflicts.
- SN.5 Refer to A-23 series floor finishes plans for proposed finishes and finished floor levels, ensure finish and setdown is suitable for applied finish.
- SN.6 Refer to A-730001 door schedule and A-72 series drawings for threshold details. Adjust structure setout to suit.

STRUCTURE NOTES cont.

- SN.7 Refer to A-05 series architectural setout drawings for setout of grids. All external steel work to be hot dip galvanised.
- SN.8 UNO Columns dimensioned to centre-line, where no dimension, centre on grid line.
- SN.9 Refer A-40 series Façade Elevations for setout of secondary steel associated with the façade.
- SN.10 Coordinate all SHS and RHS secondary steel within stud walls to have base plates contained within stud wall plane i.e. no visible base plates.
- SN.11 For trusses refer to structural drawings. Trusses are shown indicatively. Truss set out is critical for mechanical servicing. Changes to the truss set out to be approved by the superintendent; contractor to coordinate services.

STRUCTURE LEGEND

BOS	Bottom of Structure
CHS	Circular Hollow Section
EA	Equal Angle
FFL	Finished Floor Level
FSL	Finished Structural Level
FW	Floor Waste
GD	Grated Drain
GP	Gully Pit
HS	Hydraulic Stack
IOS	Inspection Opening to Surface
SHS	Square Hollow Section
SSL	Structural Slab Level
TOH	Top of Concrete Hob
TOS	Top of Structure
WCB	Concrete Block Wall
WB	Wall Beam
WO	Waste Outlet (refer hydraulic spec)

STEP	Step in slab, number indicates difference between levels (mm)
Existing concrete	
New concrete slab	
New suspended FC deck	
New suspended FC deck with Waterproof membrane	
New suspended FC deck, setdown	
New suspended FC deck, setdown with Waterproof membrane (as coded)	
New concrete block wall built on concrete slab/footing	
Steel columns	
Dashed line indicates footings / pile caps / beams below	
Saw Dowel Joint	
Dowel Expansion Joint	
Cl.T-Joint Line	
Waterproof Membrane	
Waterproof Membrane (Below)	
Steel setout dimensions	1500
Hob setout dimensions	1500
Penetration setout dimensions	1500
Centre-line of steel structure	
Standard Truss	
Truncated (angled) Truss	
Saddle Truss	

Drawings include colour information. A black & white copy may not have all the information. This background is coloured blue.

brian hooperarchitect
m3architecture
ph: +61 7 3831 4644
11 saint james street petrie tce q 4000
info@m3architecture.com
www.m3architecture.com

client **stanwell**

project **Stanwell New Projects Office**
Switchyard Road,
Stanwell, QLD, 4702

title **Structure Outline Roof Plan**

drawn bg
checked jb
date March 2026
scale 1:100 at A1
drawing 25010 / cd A-300003 / T1

copyright ©
These designs, plans, specifications and the copyright herein are the property of the architect and must not be used, reproduced, or copied wholly or in part without the written permission of m3architecture Pty Ltd abn 23 079 044 545. Use figured dimensions in preference to scale. If there are any questions contact the architect.

1:1 at A1
0 10 20 30 40 50mm