

FACADE NOTES

FN.01 Refer to Appendix B - Wall Schedule for wall types.

FN.02 Refer to Window Schedule on A-740001 & Appendix B - Wall Schedule for window types.

FN.03 Refer to T-Sheet for AM codes

FN.04 Confirm positions on site for AM-3 vertical flashings to suit adjoining wall locations

GLASS TYPES

	LV - Glass louvres, refer to Wall
	Schedule for selection

FG - Fixed clear single glazed, refer to Wall Schedule for selection

IGU - Fixed clear double glazed,
refer to Wall Schedule for selection

Joint in AM-2 horizontal flashing

WINDOW SCHEDULE				
Room		Window		
No.	Name	No	Code	Ht x Width Location
0.02	Covered Outdoor	W2	WEF-22	1655h x 12632w East-Row 4
0.02	Covered Outdoor	W1	WEF-22	1235h x 1836w East-Row 2
0.05	Kitchen	W1	WEF-21	1655h x 3640w South-Row 4
0.08	Boardroom	W1	WEF-21	1235h x 3845w South-Row 2
0.08	Boardroom	W2	WEF-21	1655h x 3654w South-Row 4
0.11	Training Kitchen	W1	WEF-21	1235h x 2439w South-Row 2
0.16	Female Amenities	W1	WEF-21	740h x 1240w South-Row 3
0.17	Male Amenities	W1	WEF-21	725h x 1240w South-Row 3
0.18	First Aid	W1	WEF-21	1235h x 1084w West-Row 2
0.29	Workspace (North)	W1	WEF-21	4019h x 3640w North-Rows 2, 3 & 4
0.29	Workspace (North)	W2	WEF-21	2135h x 3640w North-Rows 1 & 2
0.29	Workspace (North)	W3	WEF-21	1235h x 28840w North-Row 2
0.35	Workspace (East)	W1	WEF-21	1235h x 1810w East-Row 2
0.35	Workspace (East)	W2	WEF-21	1655h x 3640w East-Row 4

PRELIMINARY
NOT FOR CONSTRUCTION

Drawings include colour information. A black & white copy may not have all the information. This background is coloured blue.

brian hooperarchitect
m3architecture
ph: +61 7 3831 4644
11 saint james street petrie tce q 4000
info@m3architecture.com
www.m3architecture.com

client  stanwell

project Stanwell New Projects Office
Switchyard Road,
Stanwell, QLD, 4702

title	Facade Plans & Elevation - North
-------	----------------------------------


drawn bg
checked jb
date March 2026
scale As indicated at A1
drawing 25010 / cd A-400001 / T1

copyright ©
These designs, plans, specifications and the copyright herein are the property of the architect and must not be used, reproduced, or copied wholly or in part without the written permission of m3architecture pty ltd abn 23 079 044 545.
Use figured dimensions in preference to scale.
If there are any questions contact the architect.


1:100 at A1




0 1 2 3 4 5m

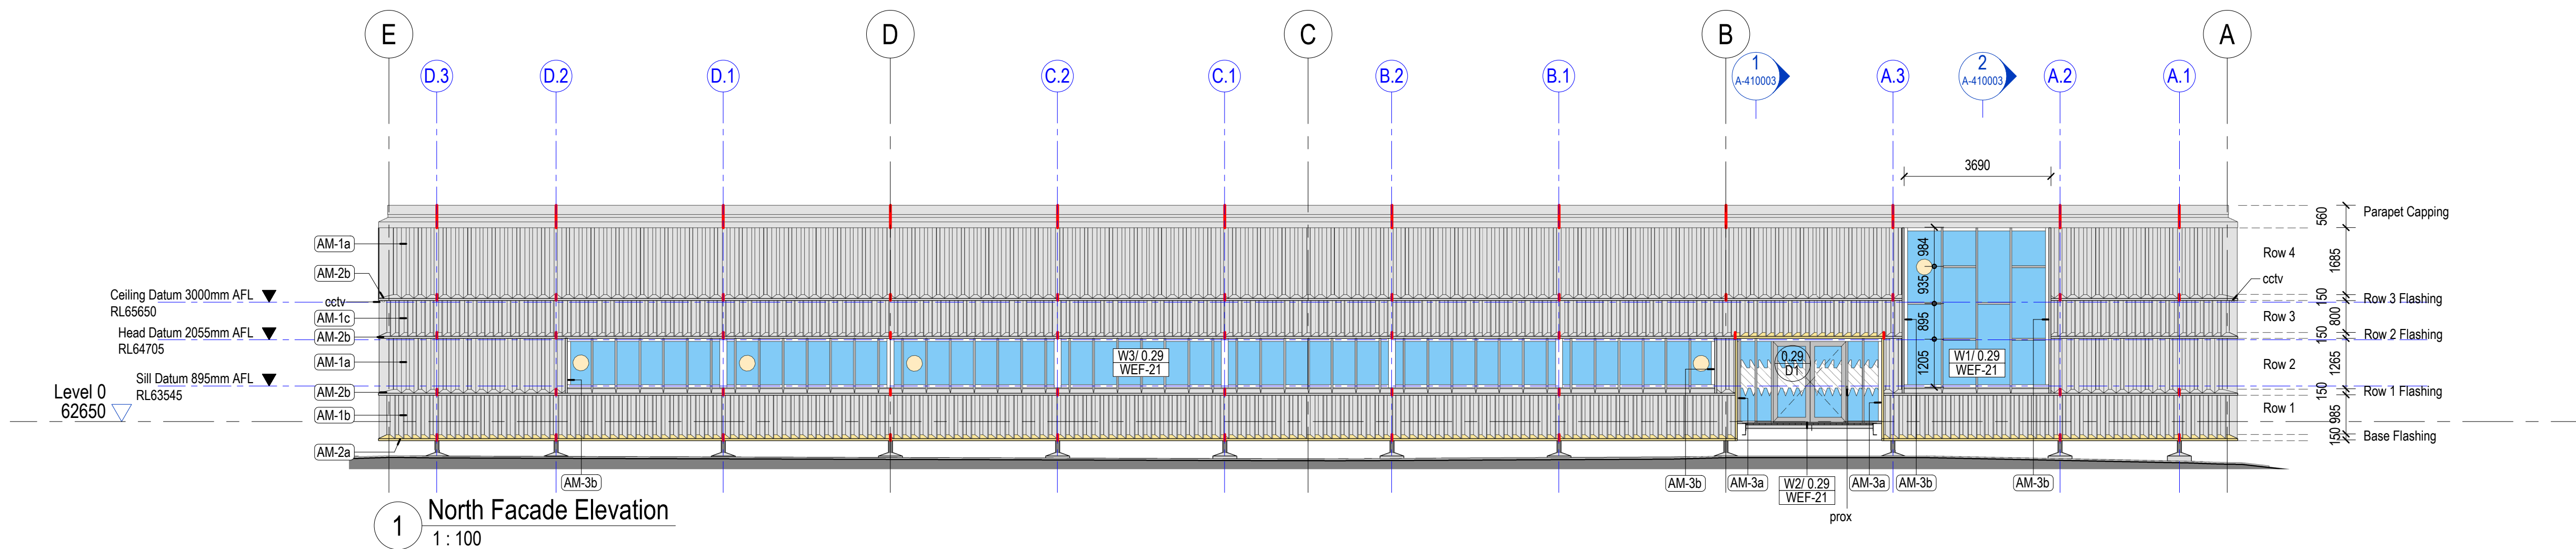


1 North Facade Elevation
1 : 100

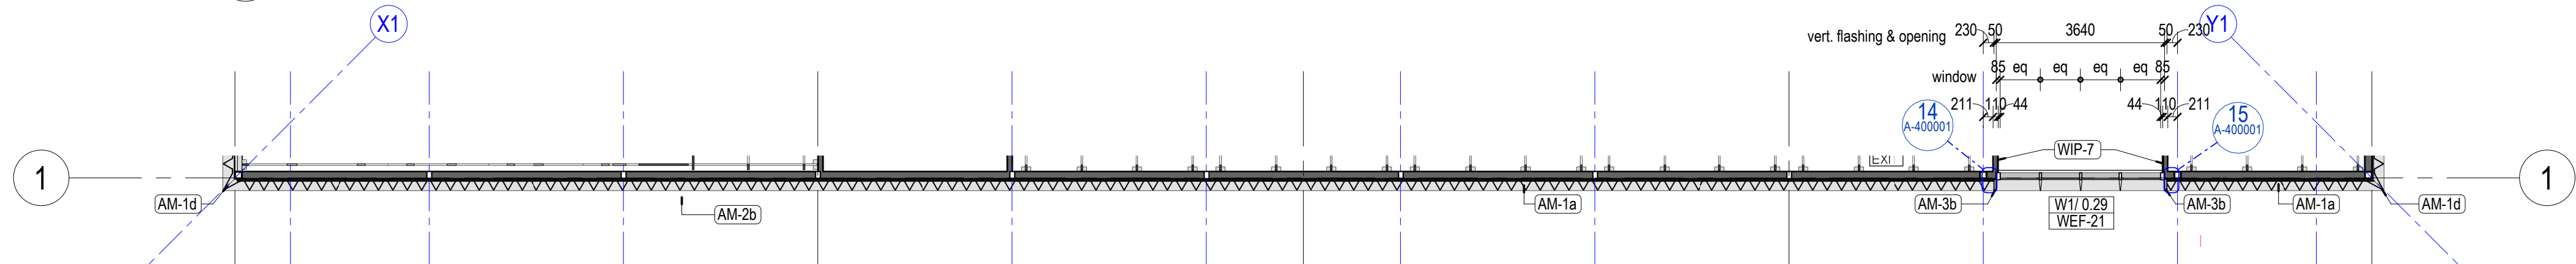


2 North Wall Setout Plan - Row 4 (plan rotated)
1 : 100 Cut @ 3900 AFL

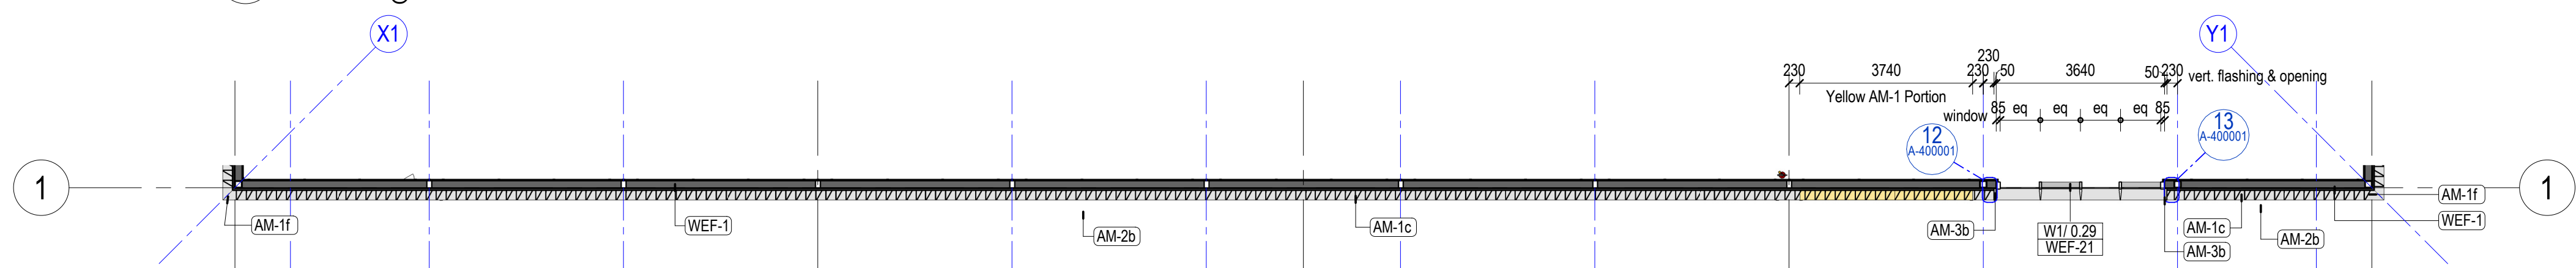


3 North Wall Setout Plan - Row 3 (plan rotated)
1 : 100 Cut @ 2550 AFL

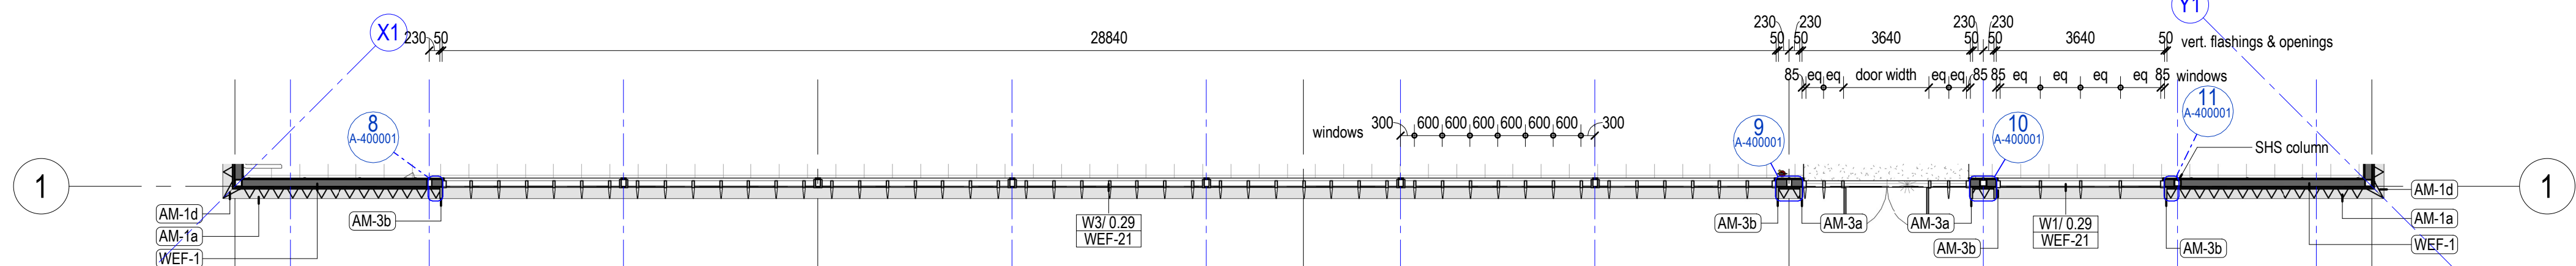

4 North Wall Setout Plan - Row 2 - (plan rotated)
1 : 100 Cut @ 1400 AFL

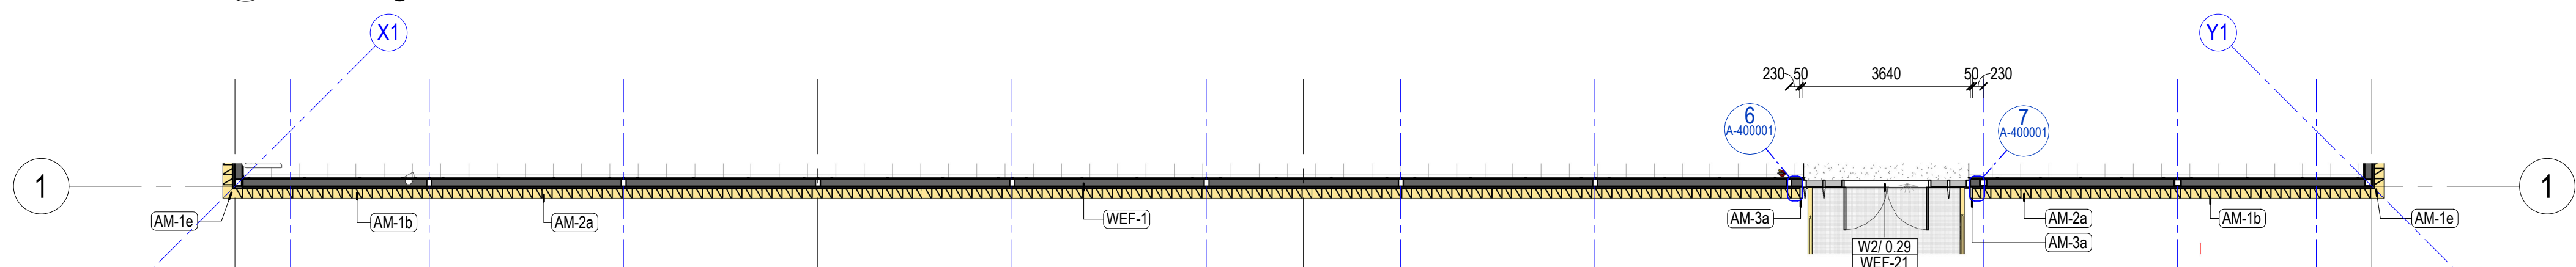

5 North Wall Setout Plan - Row 1 (plan rotated)
1 : 100 Cut @ 300 AFL

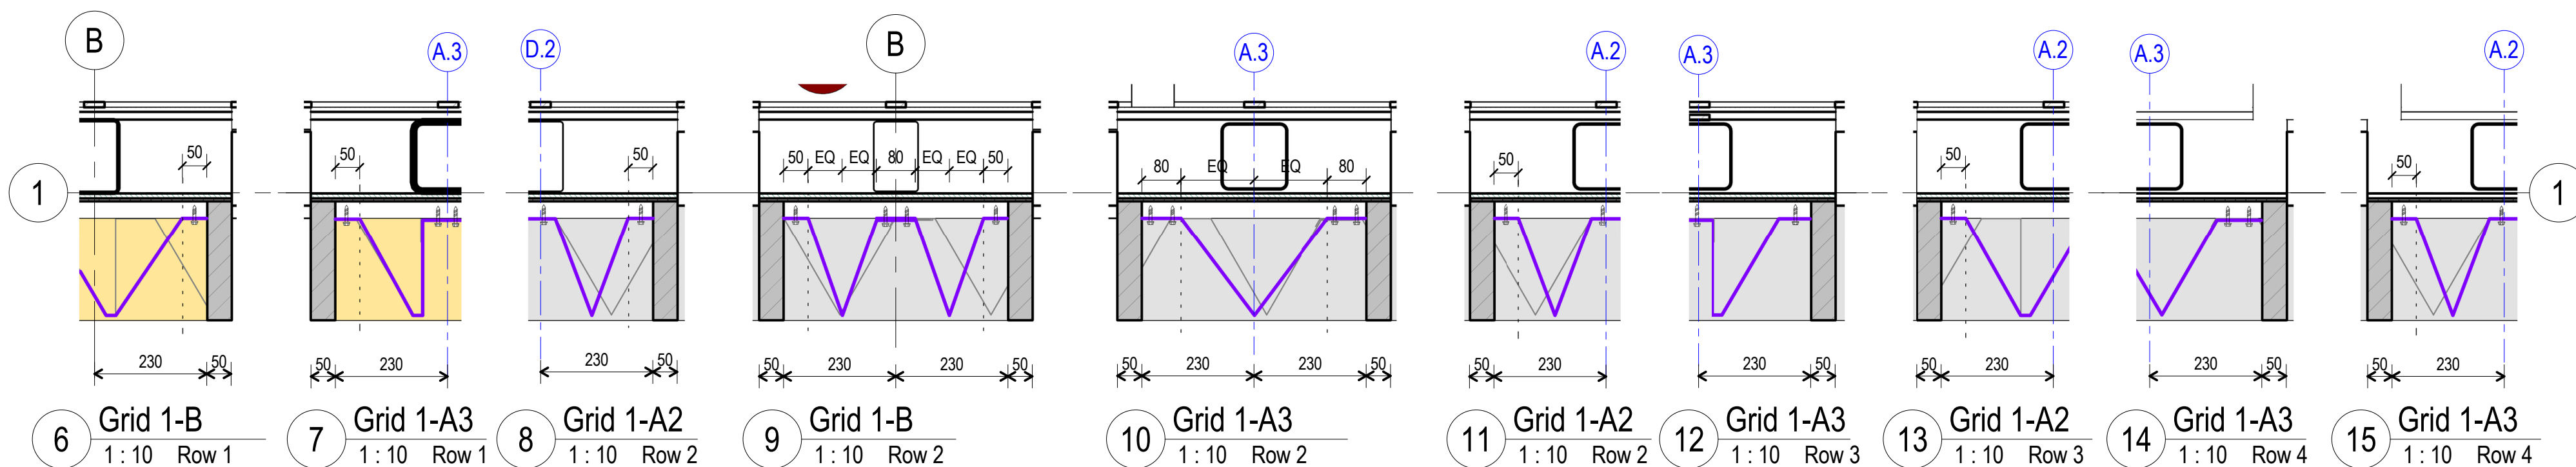

6 Grid 1-B 1:10 Row 1 7 Grid 1-A3 1:10 Row 1 8 Grid 1-A2 1:10 Row 2 9 Grid 1-B 1:10 Row 2 10 Grid 1-A3 1:10 Row 2 11 Grid 1-A2 1:10 Row 2 12 Grid 1-A3 1:10 Row 3 13 Grid 1-A2 1:10 Row 3 14 Grid 1-A3 1:10 Row 4 15 Grid 1-A3 1:10 Row 4