

FACADE NOTES

- FN.01 Refer to Appendix B - Wall Schedule for wall types.
- FN.02 Refer to Window Schedule on A-740001 & Appendix B - Wall Schedule for window types.
- FN.03 Refer to T-Sheet for AM codes
- FN.04 Confirm positions on site for AM-3 vertical flashings to suit adjoining wall locations

GLASS TYPES

- LV - Glass louvres, refer to Wall Schedule for selection
- FG - Fixed clear single glazed, refer to Wall Schedule for selection
- IGU - Fixed clear double glazed, refer to Wall Schedule for selection
- Joint in AM-2 horizontal flashing

ROOM COLOUR SCHEME (UNO):

- Walls PT-ELa
- Walls skirtings and battens PT-EGa
- Ceiling PT-EMc
- Ceiling battens PT-EGc

PRELIMINARY
NOT FOR CONSTRUCTION

Drawings include colour information. A black & white copy may not have all the information. This background is coloured blue.

brian hooperarchitect
m3architecture
ph: +61 7 3831 4644
11 saint james street petrie tce q 4000
info@m3architecture.com
www.m3architecture.com

client  **stanwell**


project **Stanwell New Projects Office**
Switchyard Road,
Stanwell, QLD, 4702

title **Facade Elevation - Courtyard**


drawn bg
checked jb
date March 2026
scale As indicated at A1
drawing **25010 / cd A-400101 / T1**

copyright ©
These designs, plans, specifications and the copyright herein are the property of the architect and must not be used, reproduced, or copied wholly or in part without the written permission of m3architecture Pty Ltd abn 23 079 044 545. Use figured dimensions in preference to scale. If there are any questions contact the architect.


1:100 at A1
0 1 2 3 4 5m

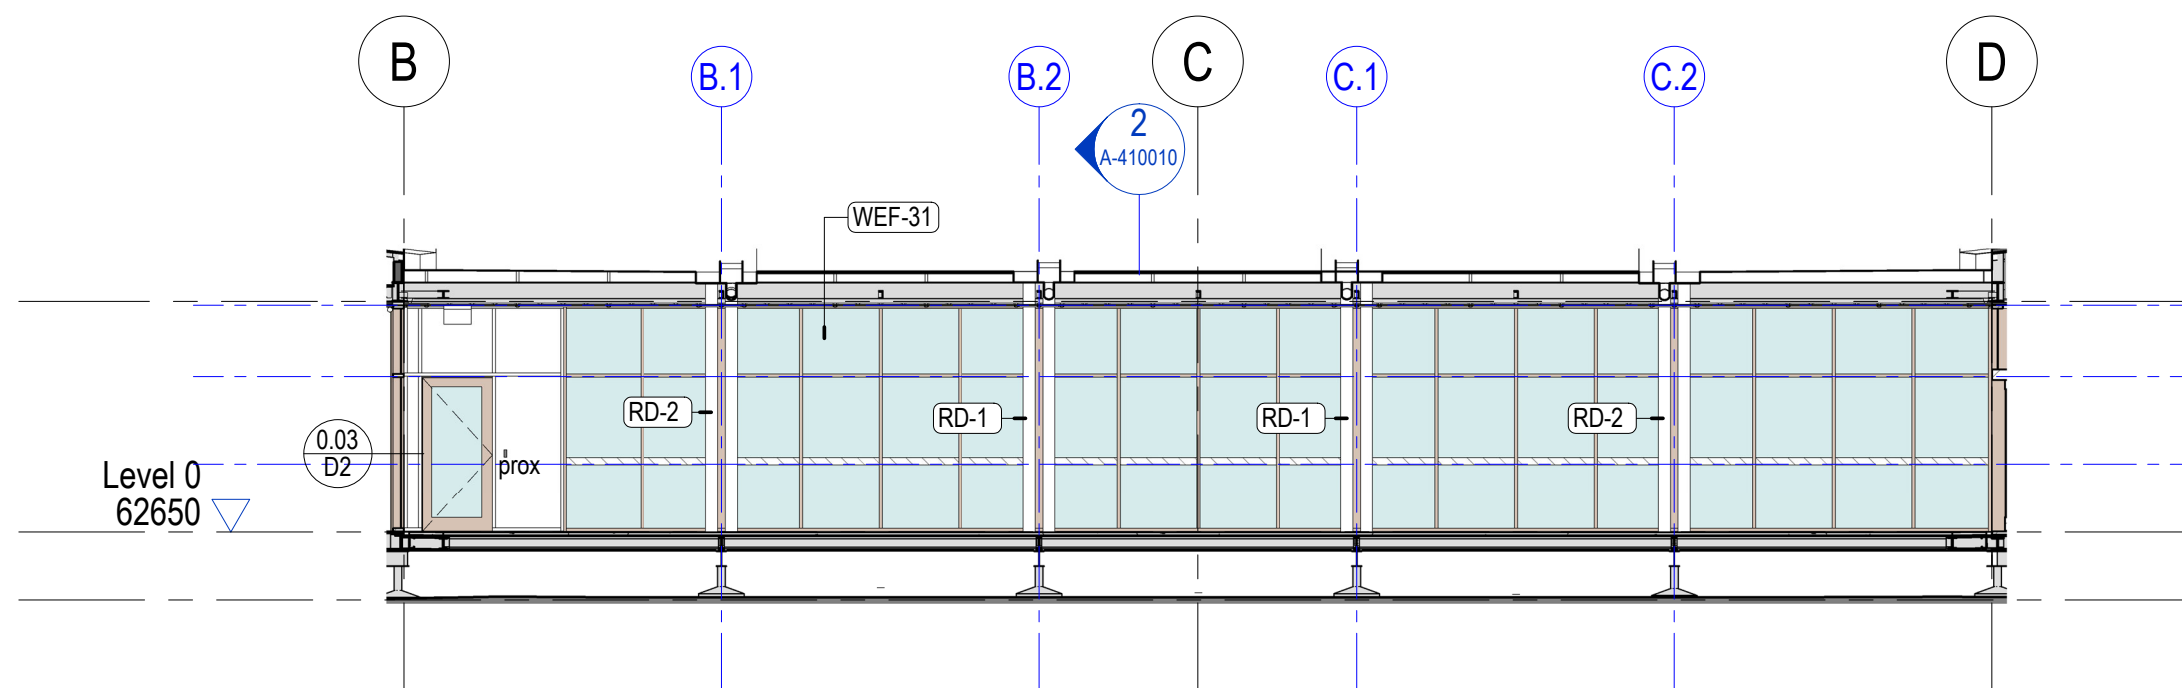


1 Courtyard North Elevation
1:100 Glazing

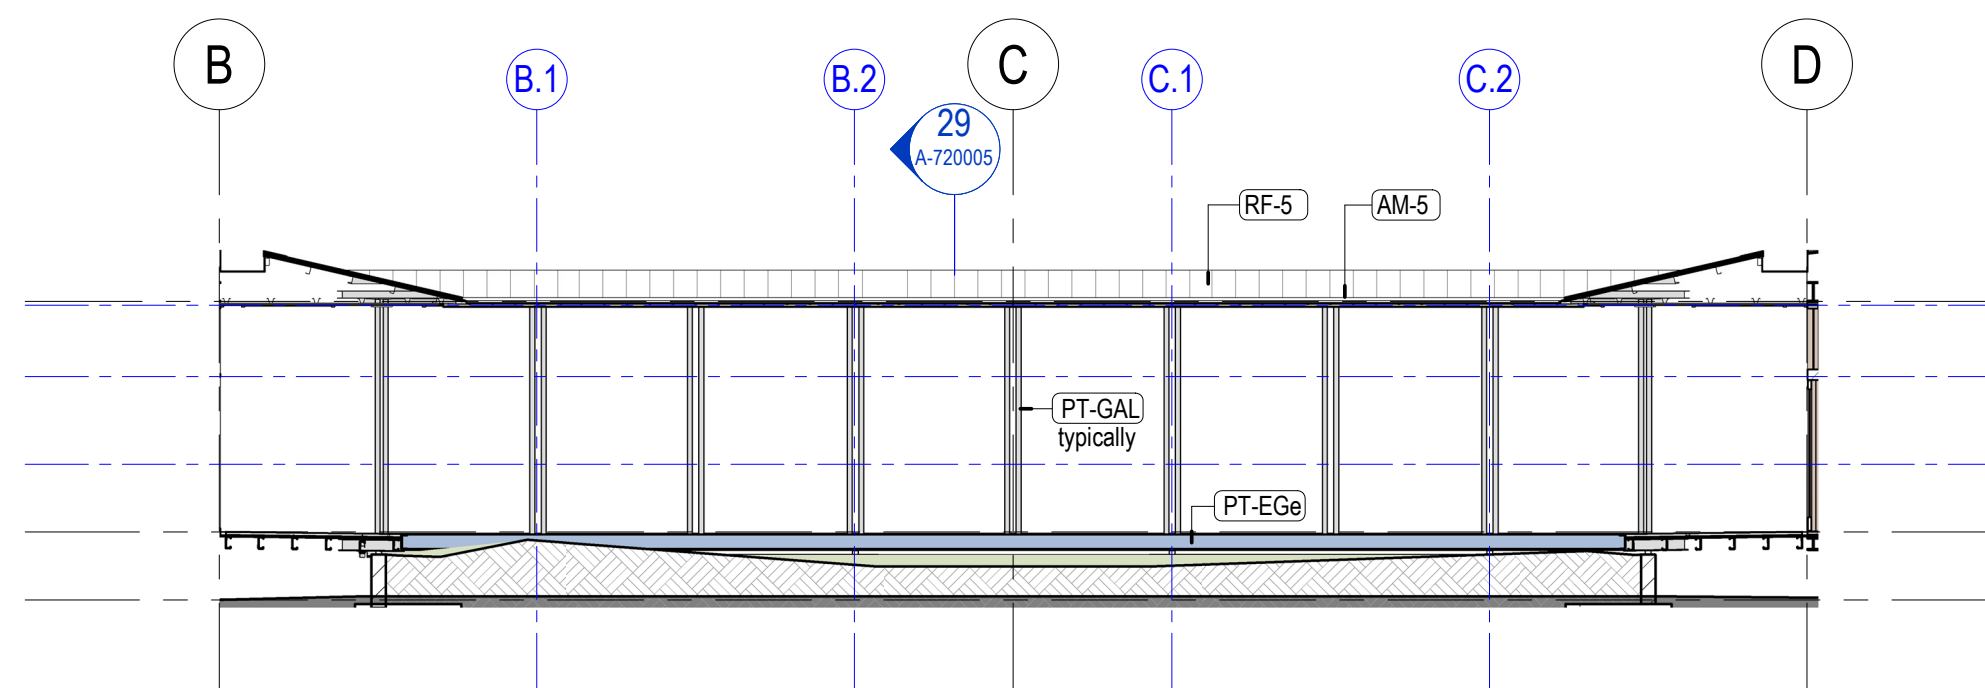


2 Courtyard North Elevation
1:100 Perimeter

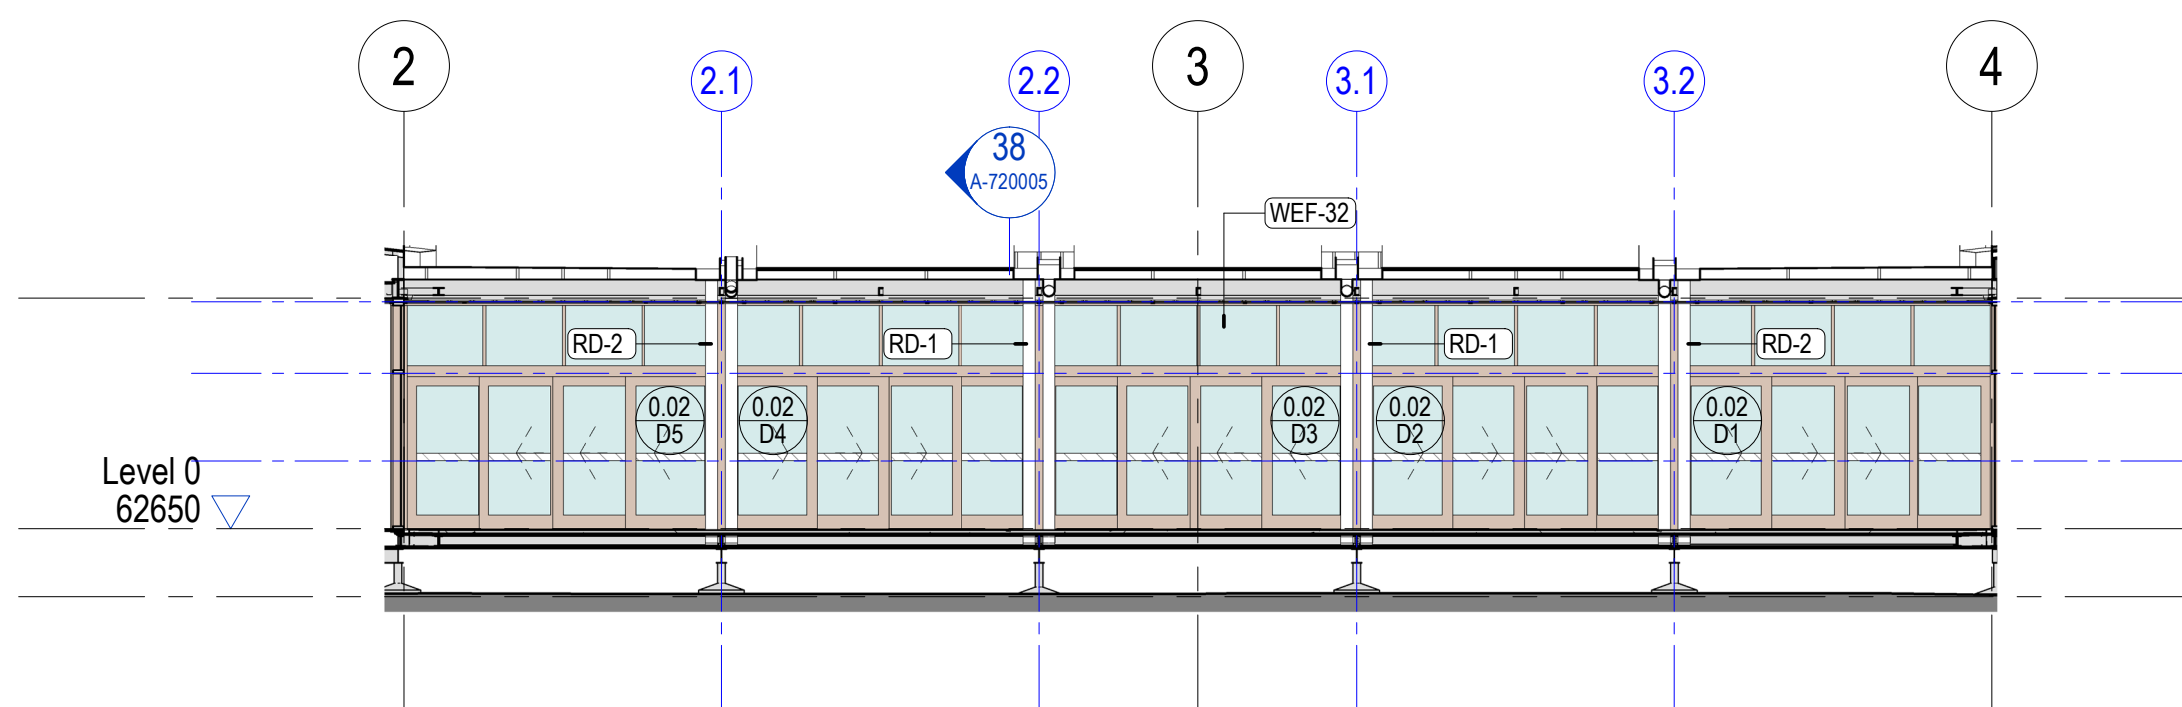


3 Courtyard East Elevation
1:100 Glazing

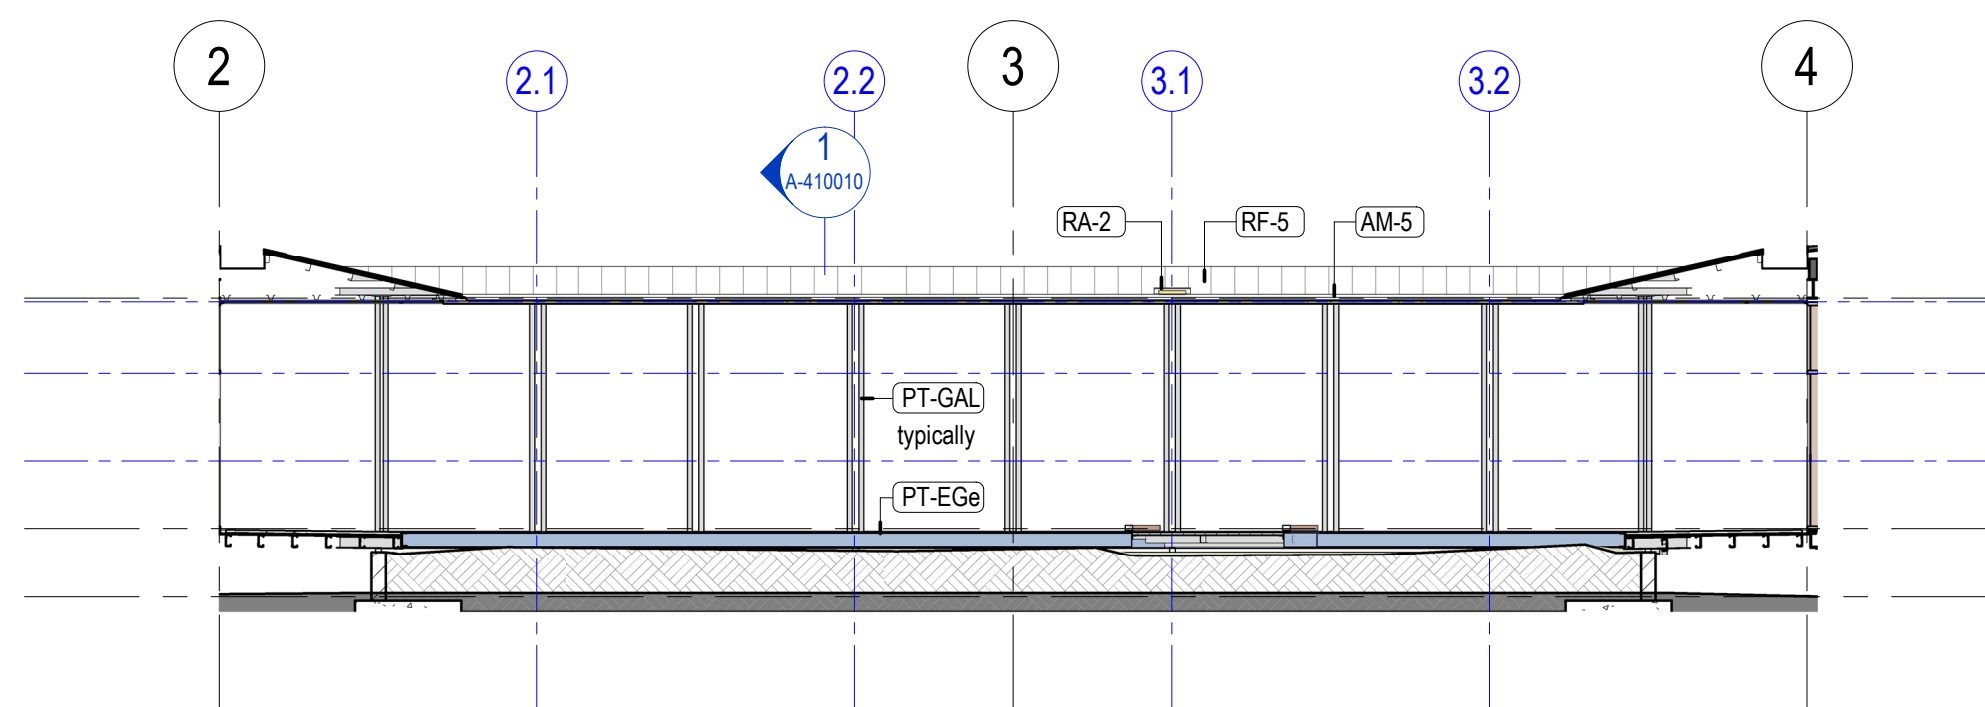


4 Courtyard East Elevation
1:100 Perimeter

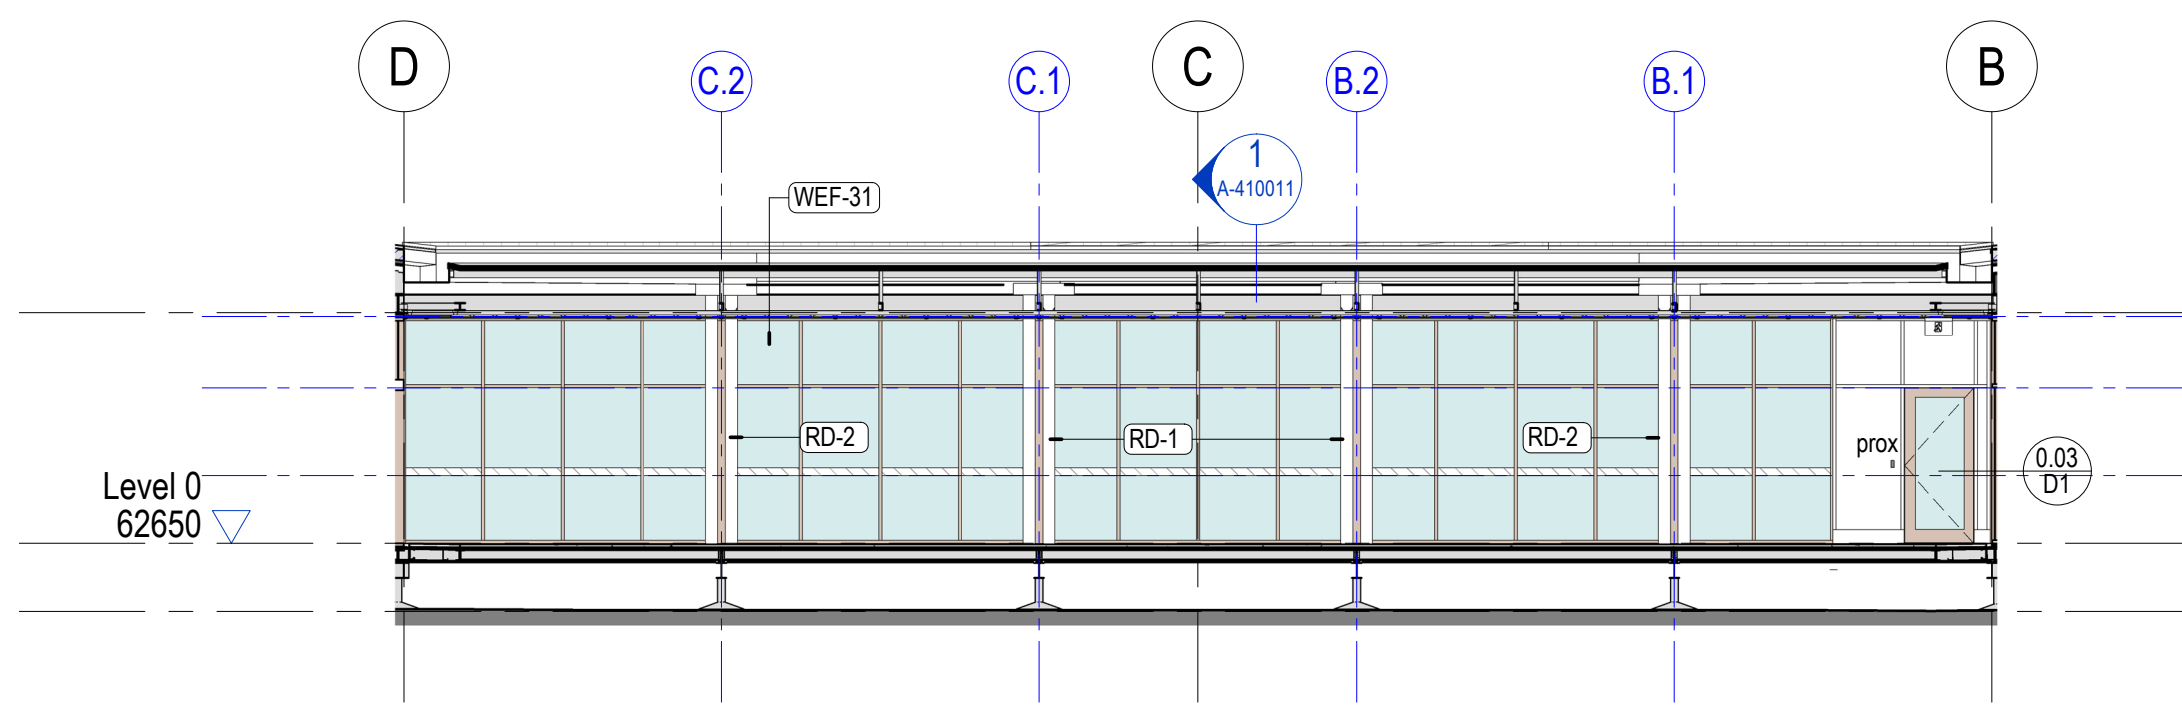


5 Courtyard South Elevation
1:100 Glazing

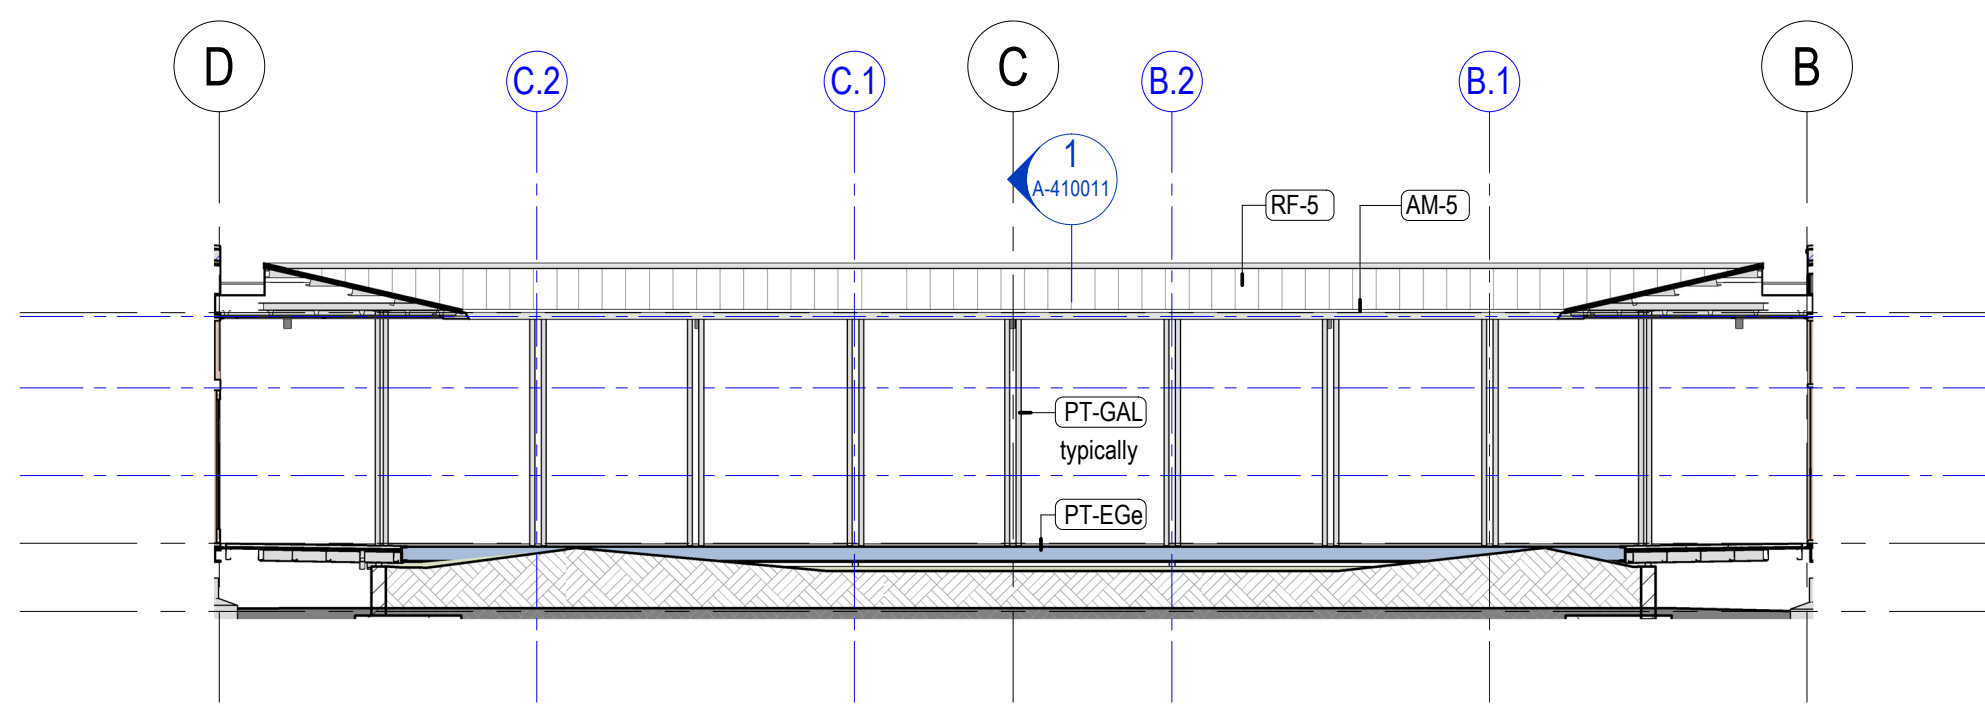

6 Courtyard South Elevation
1:100 Perimeter

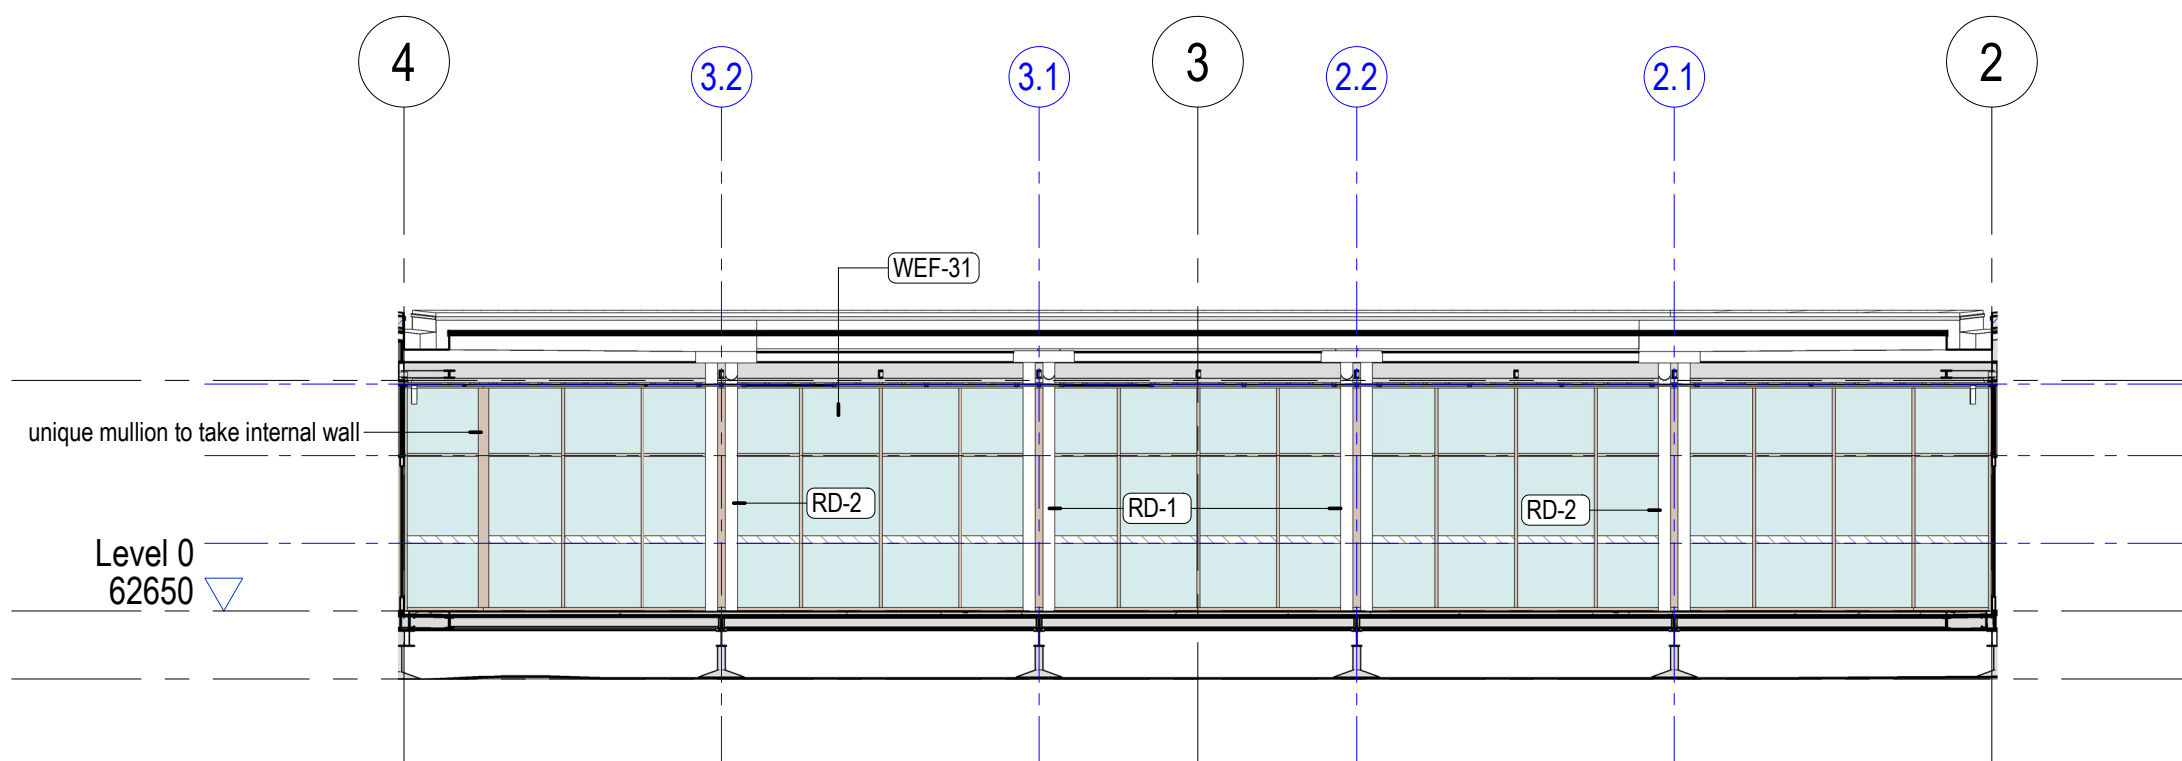

7 Courtyard West Elevation
1:100 Glazing

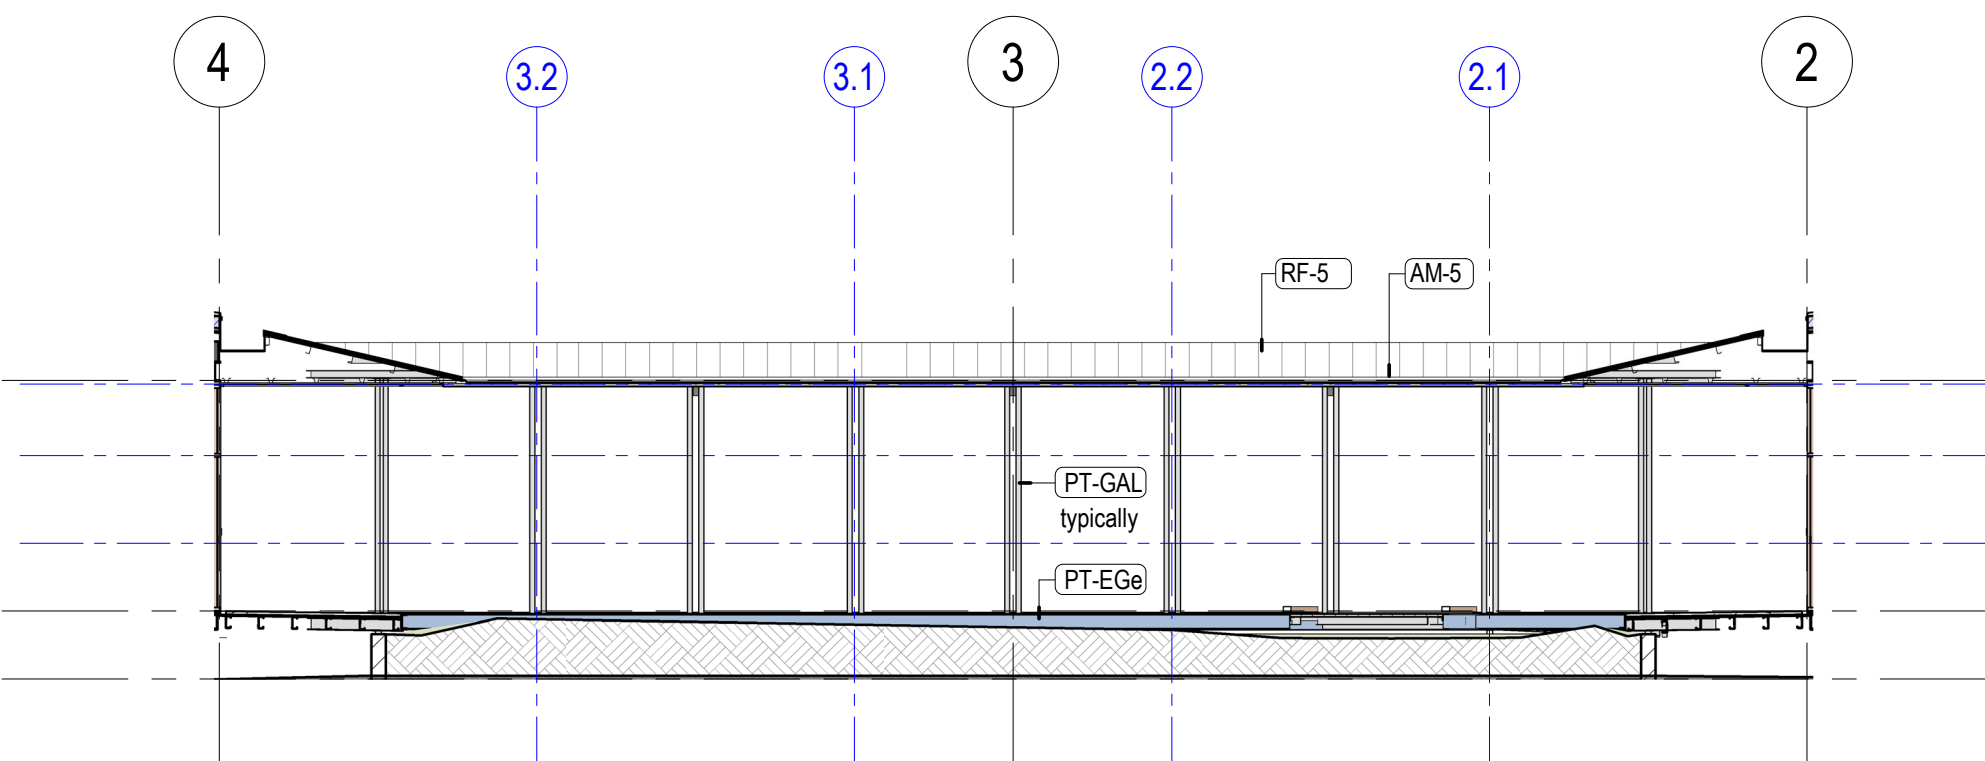

8 Courtyard West Elevation
1:100 Perimeter