


DETAILS NOTES

1. XXX  
2. Xxx

| rev | date       | description | initial |
|-----|------------|-------------|---------|
| T1  | 11/03/2026 | For Tender  | JB      |

FACADE LEGEND

- (WP-2) Weather Resistive Wrap  
Alum Flashing  
(WP-1 or 3) Floor Waterproof Membrane  
(WP-4) Ext. Wall Sarking

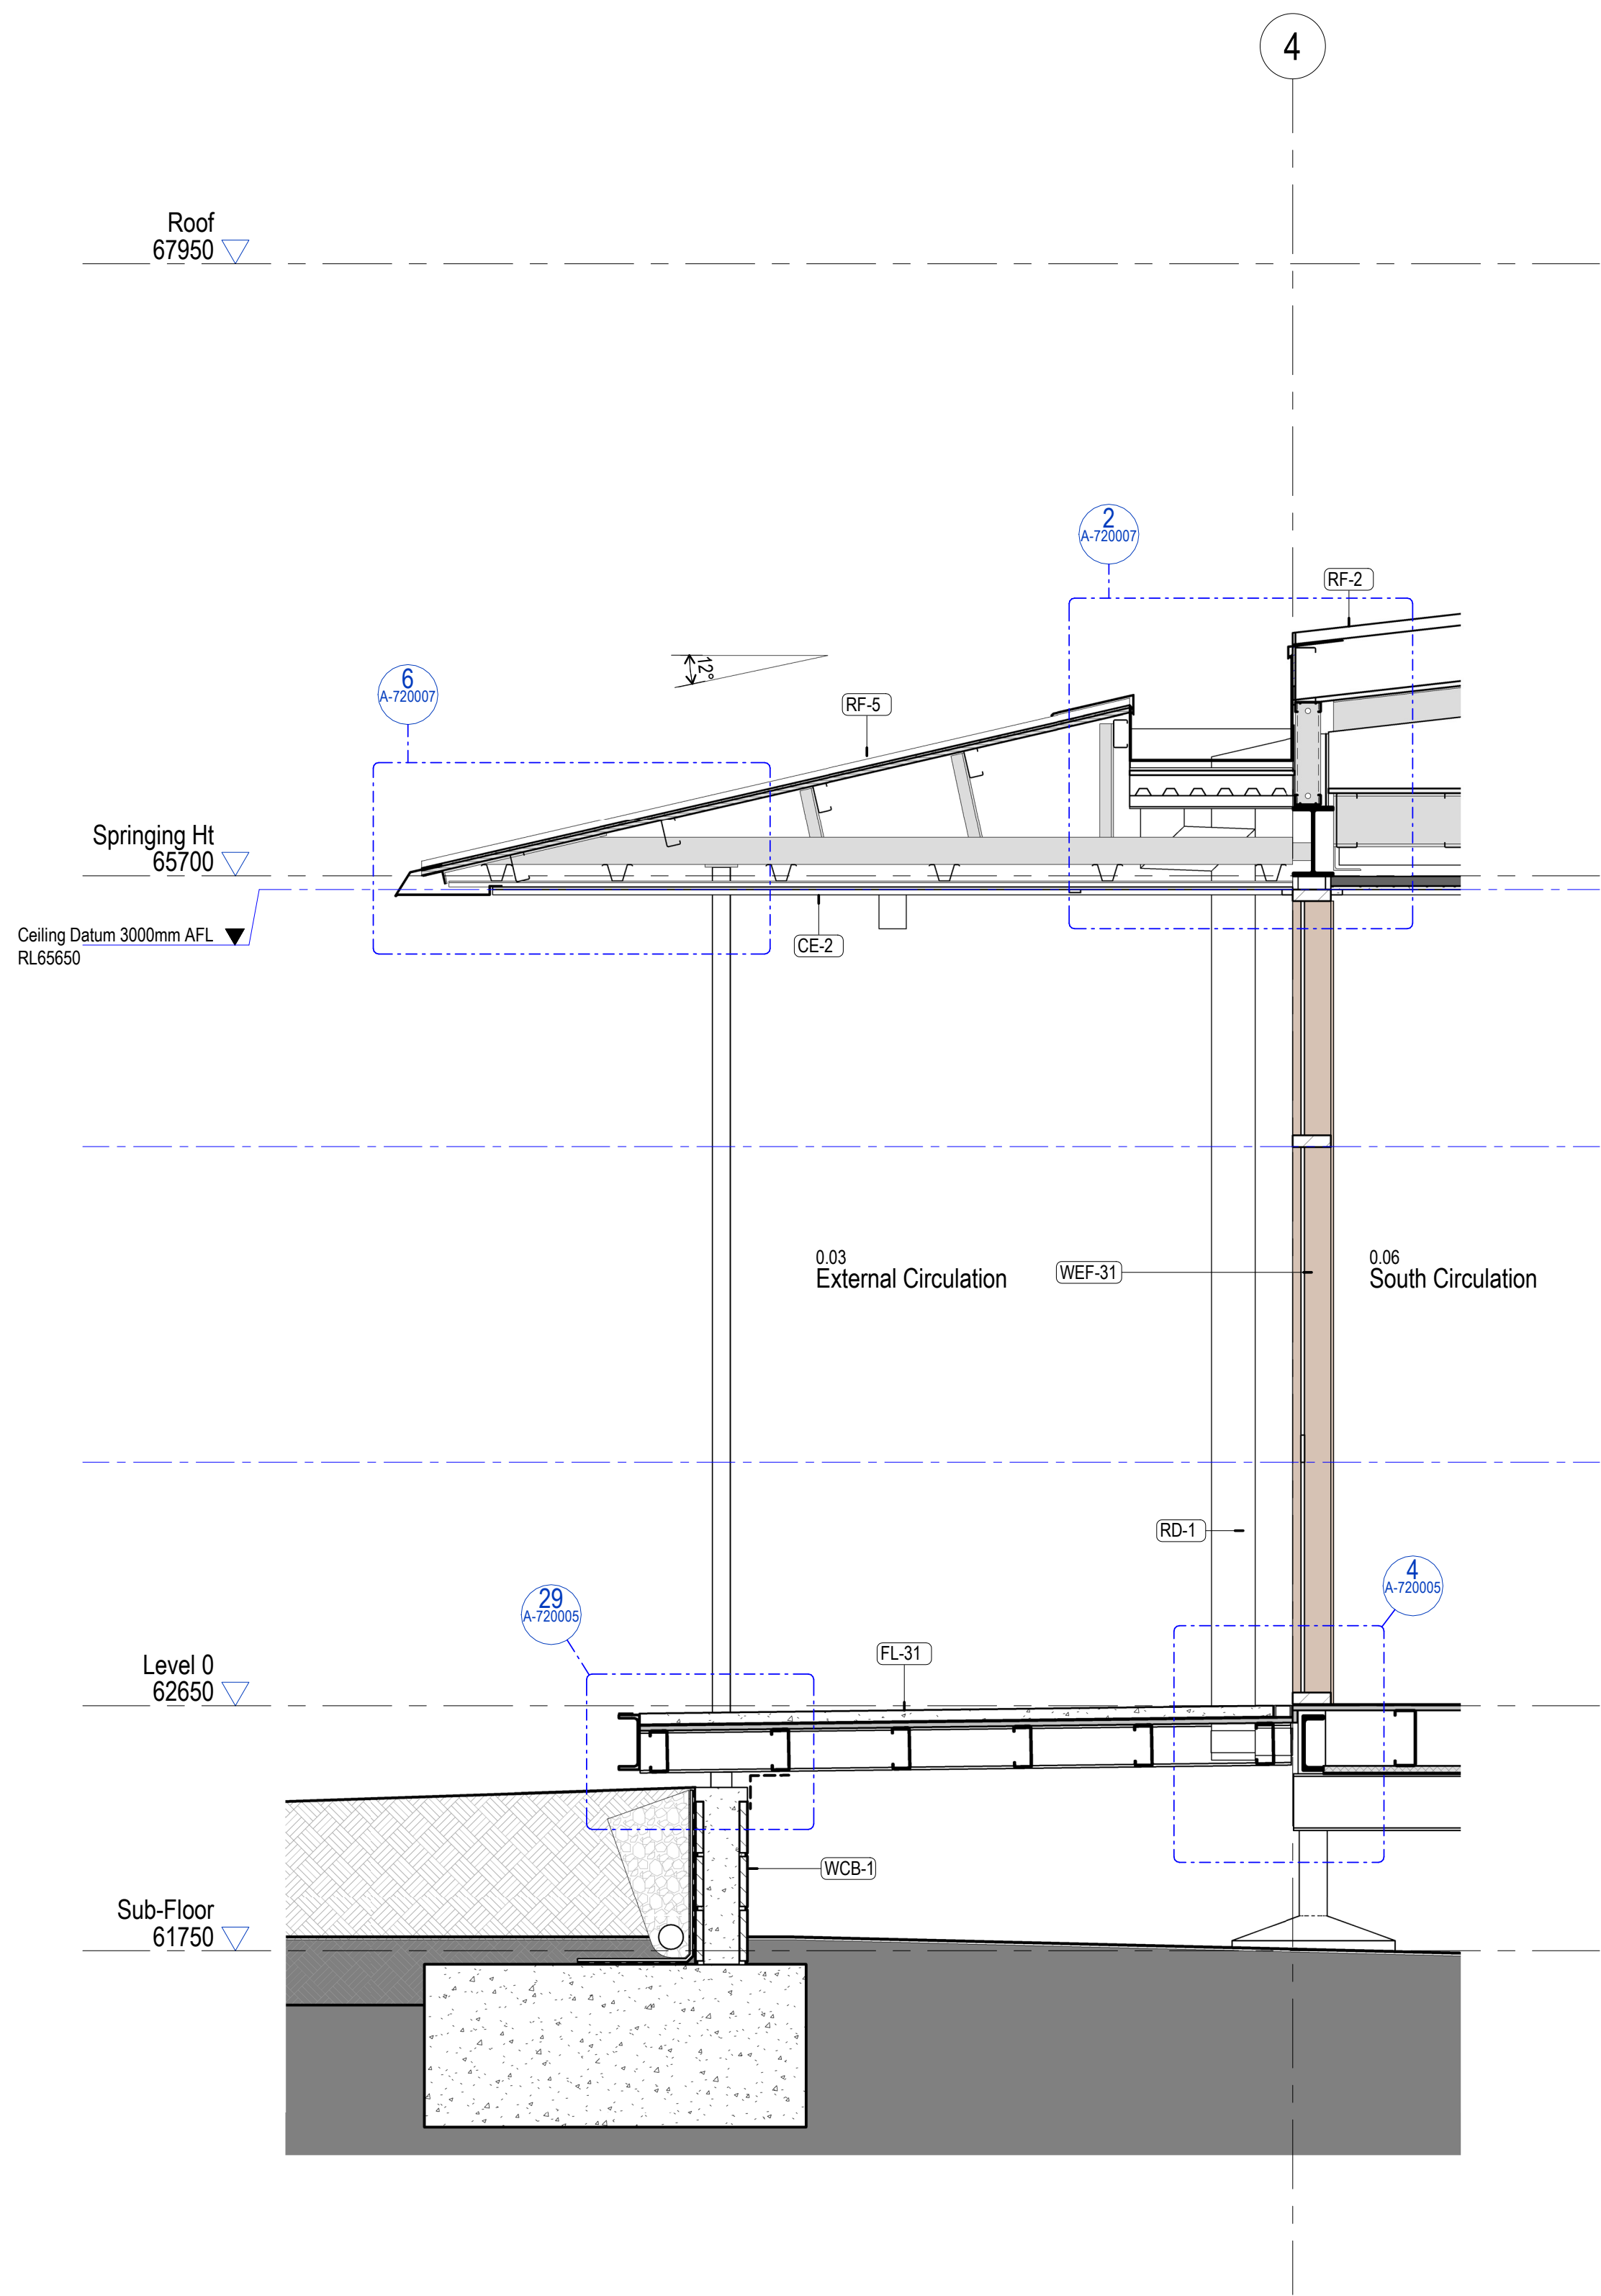

1 Courtyard South Facade Section  
1 : 20

PRELIMINARY  
NOT FOR CONSTRUCTION

Drawings include colour information. A black & white copy may not have all the information. This background is coloured blue.

brian hooperarchitect  
**m3architecture**  
ph: +61 7 3831 4644  
11 saint james street petrie tce q 4000  
info@m3architecture.com  
www.m3architecture.com

client  **stanwell**

project **Stanwell New Projects Office**  
Switchyard Road,  
Stanwell, QLD, 4702

title **Facade Sections - Courtyard**

drawn JB  
checked bh  
date March 2026  
scale As indicated at A1  
drawing 25010 / cd A-410011 / T1

copyright ©  
These designs, plans, specifications and the copyright herein are the property of the architect and must not be used, reproduced, or copied wholly or in part without the written permission of m3architecture Pty Ltd abn 23 079 044 545. Use figured dimensions in preference to scale. If there are any questions contact the architect.

1:1 at A1  
0 10 20 30 40 50mm