




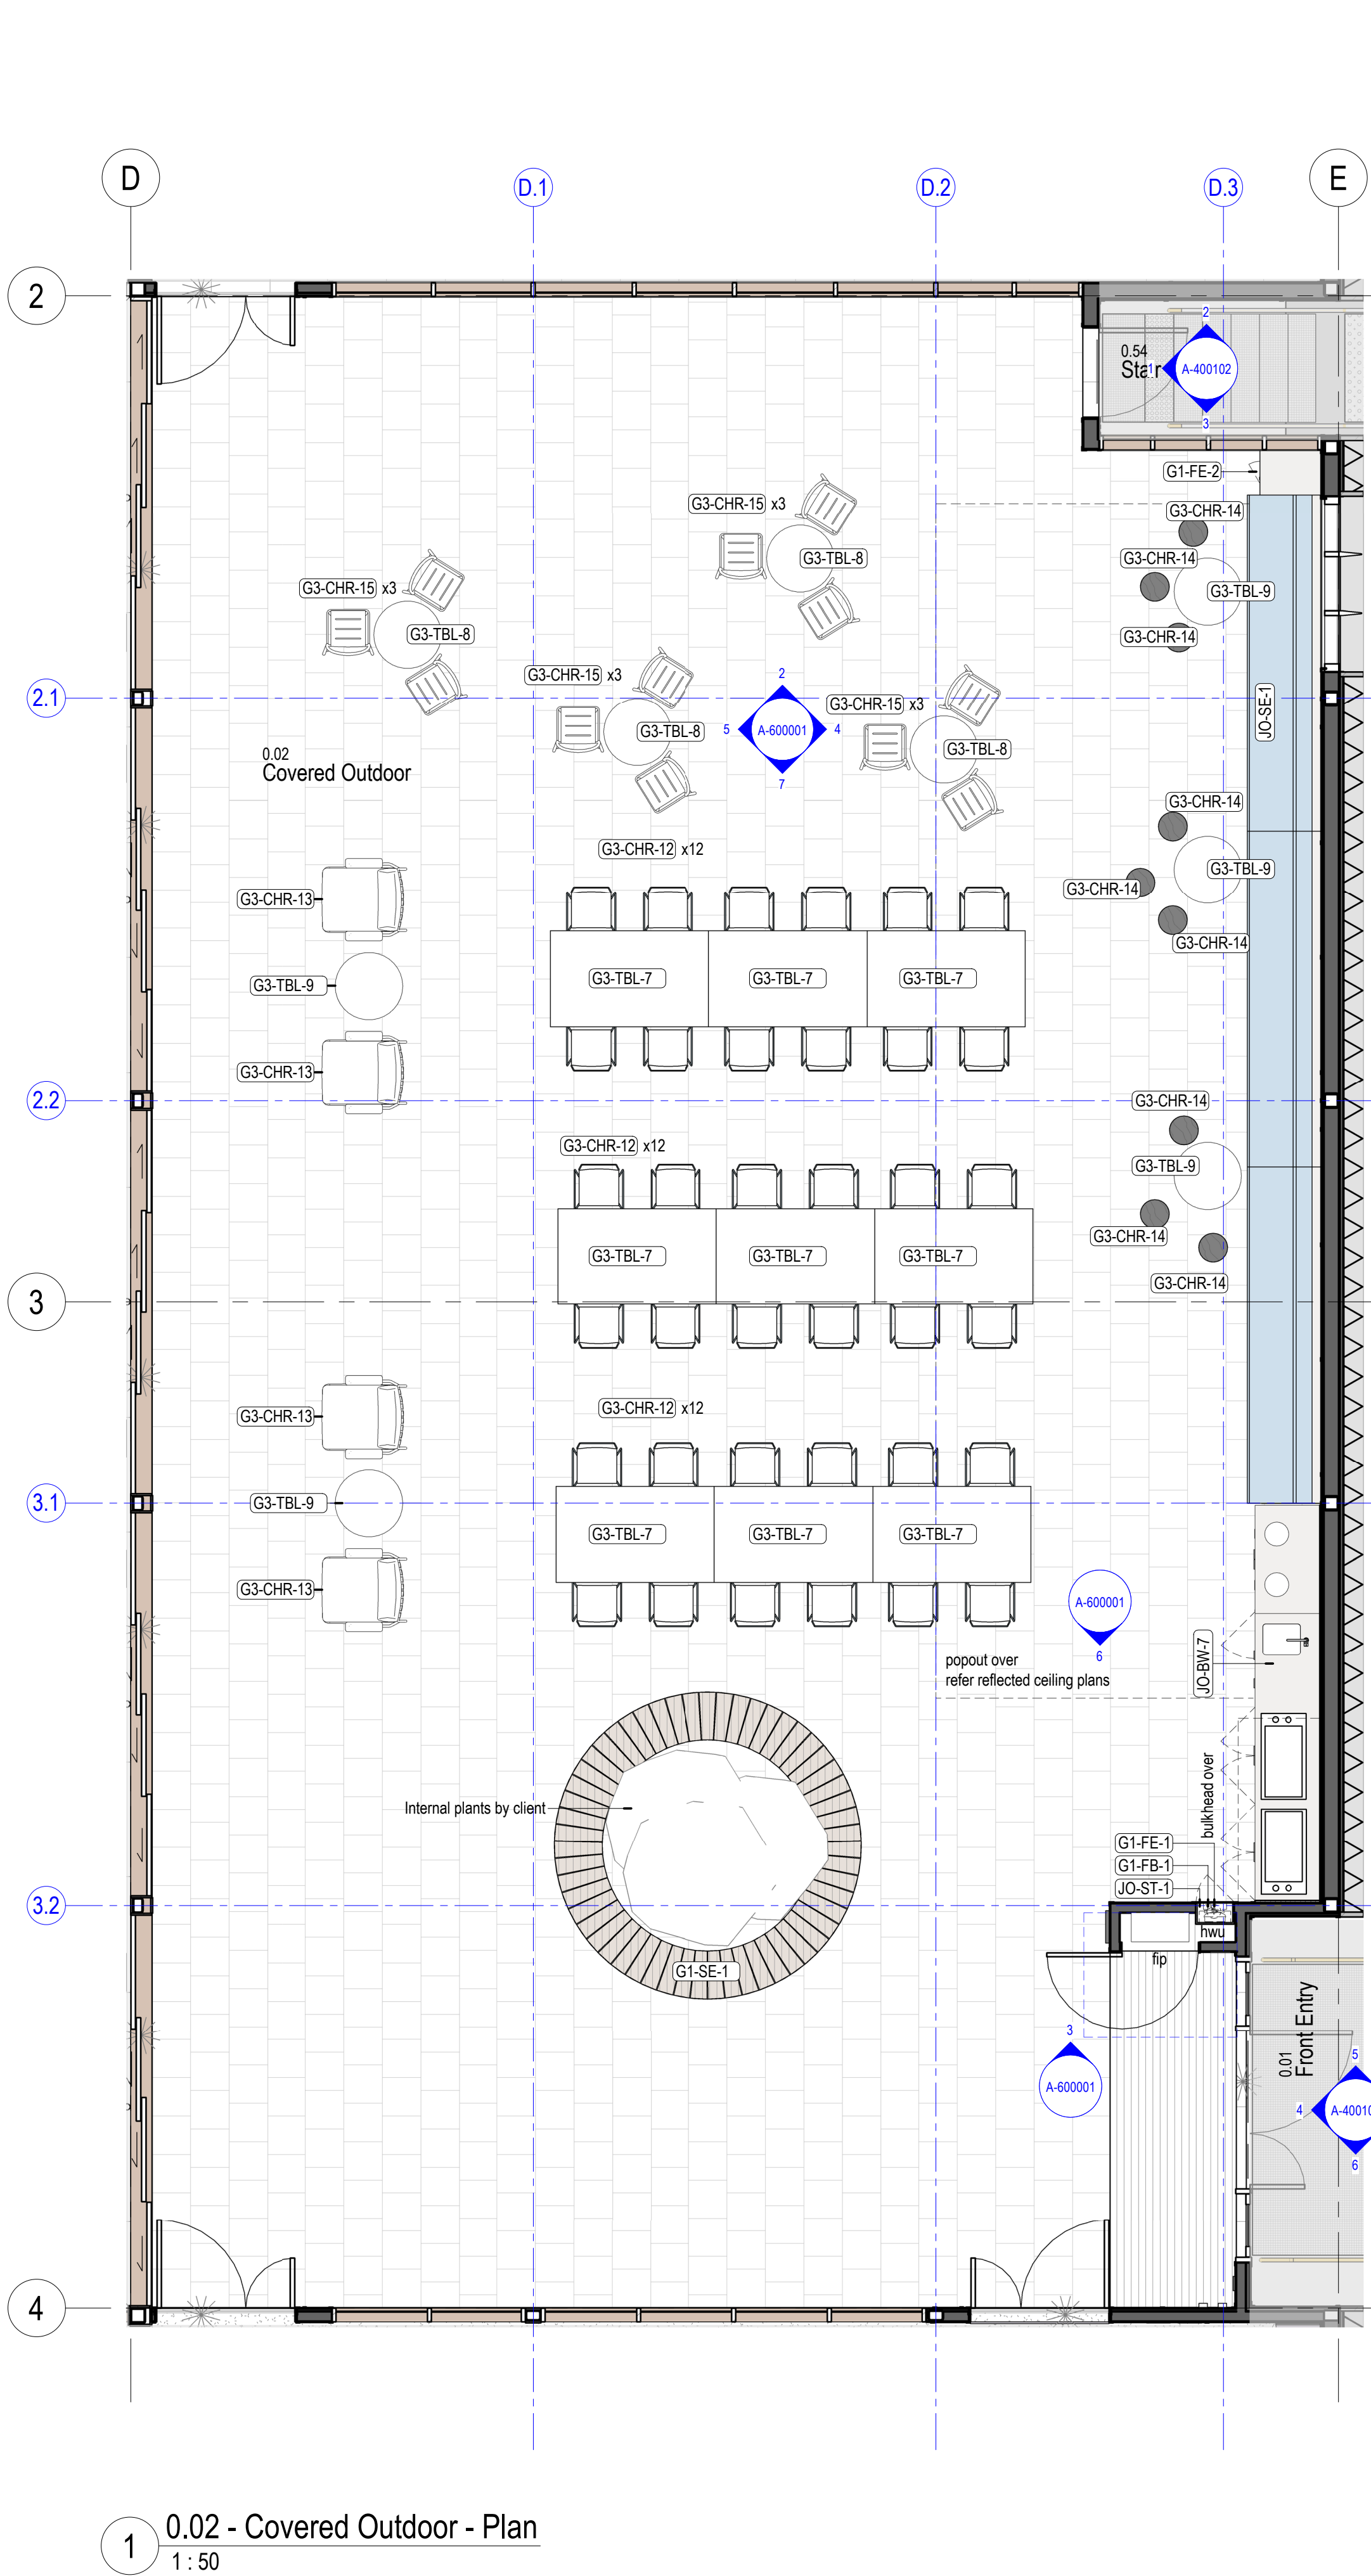


1 0.02 - Covered Outdoor - Plan
1 : 50

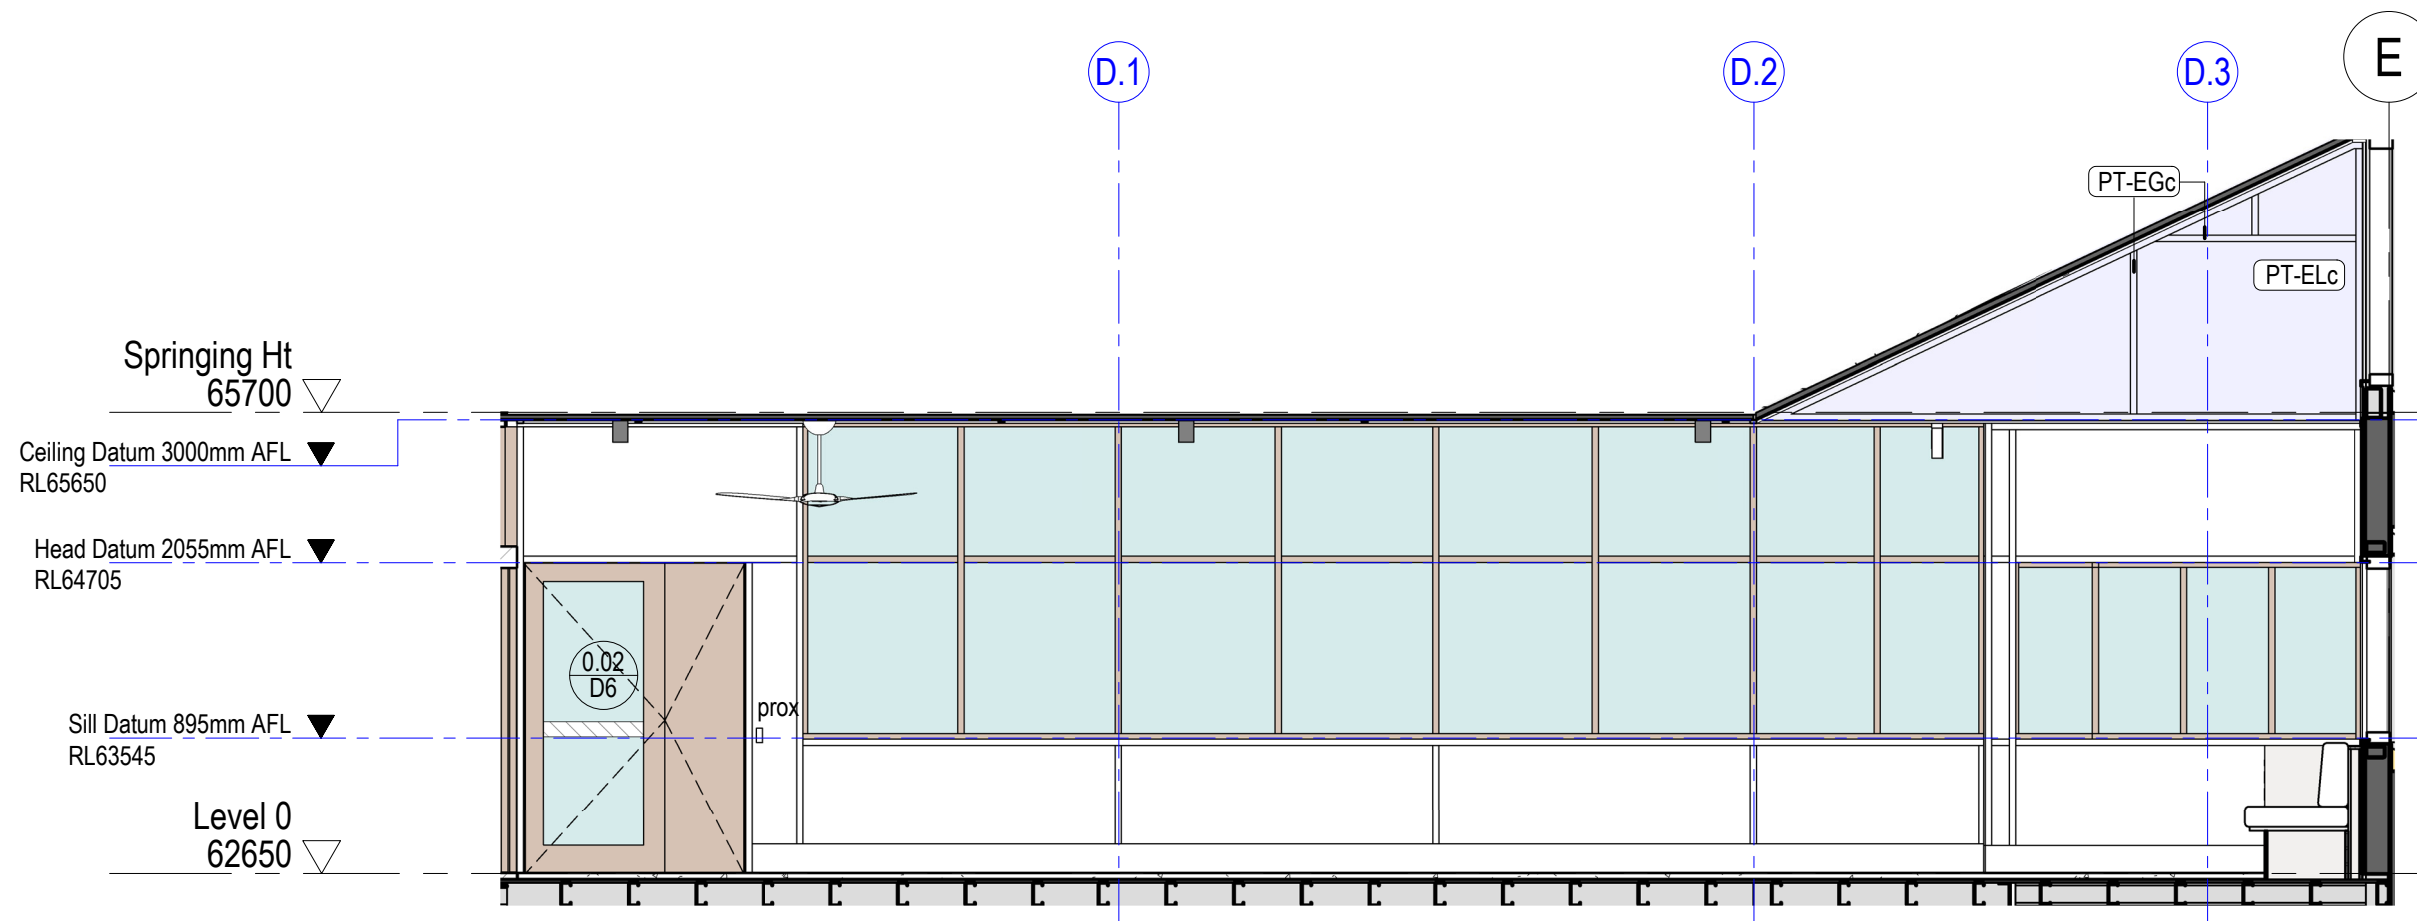


2 0.02 - Covered Outdoor - North Elevation 1
1 : 50

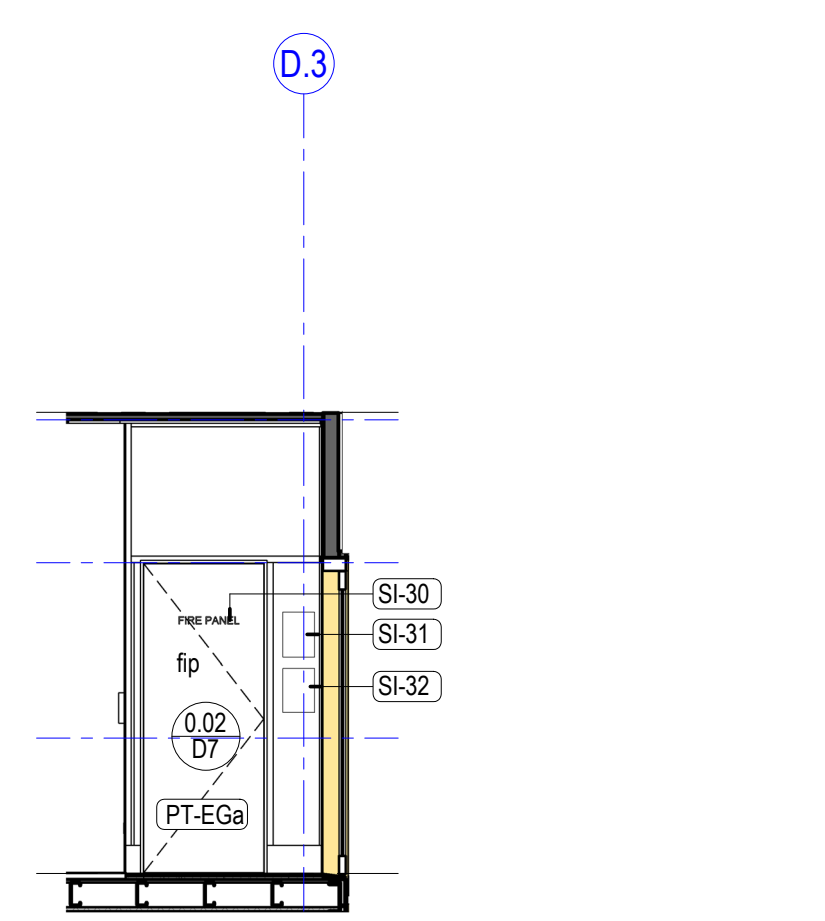


3 0.02 - Covered Outdoor - North Elevation 2
1 : 50

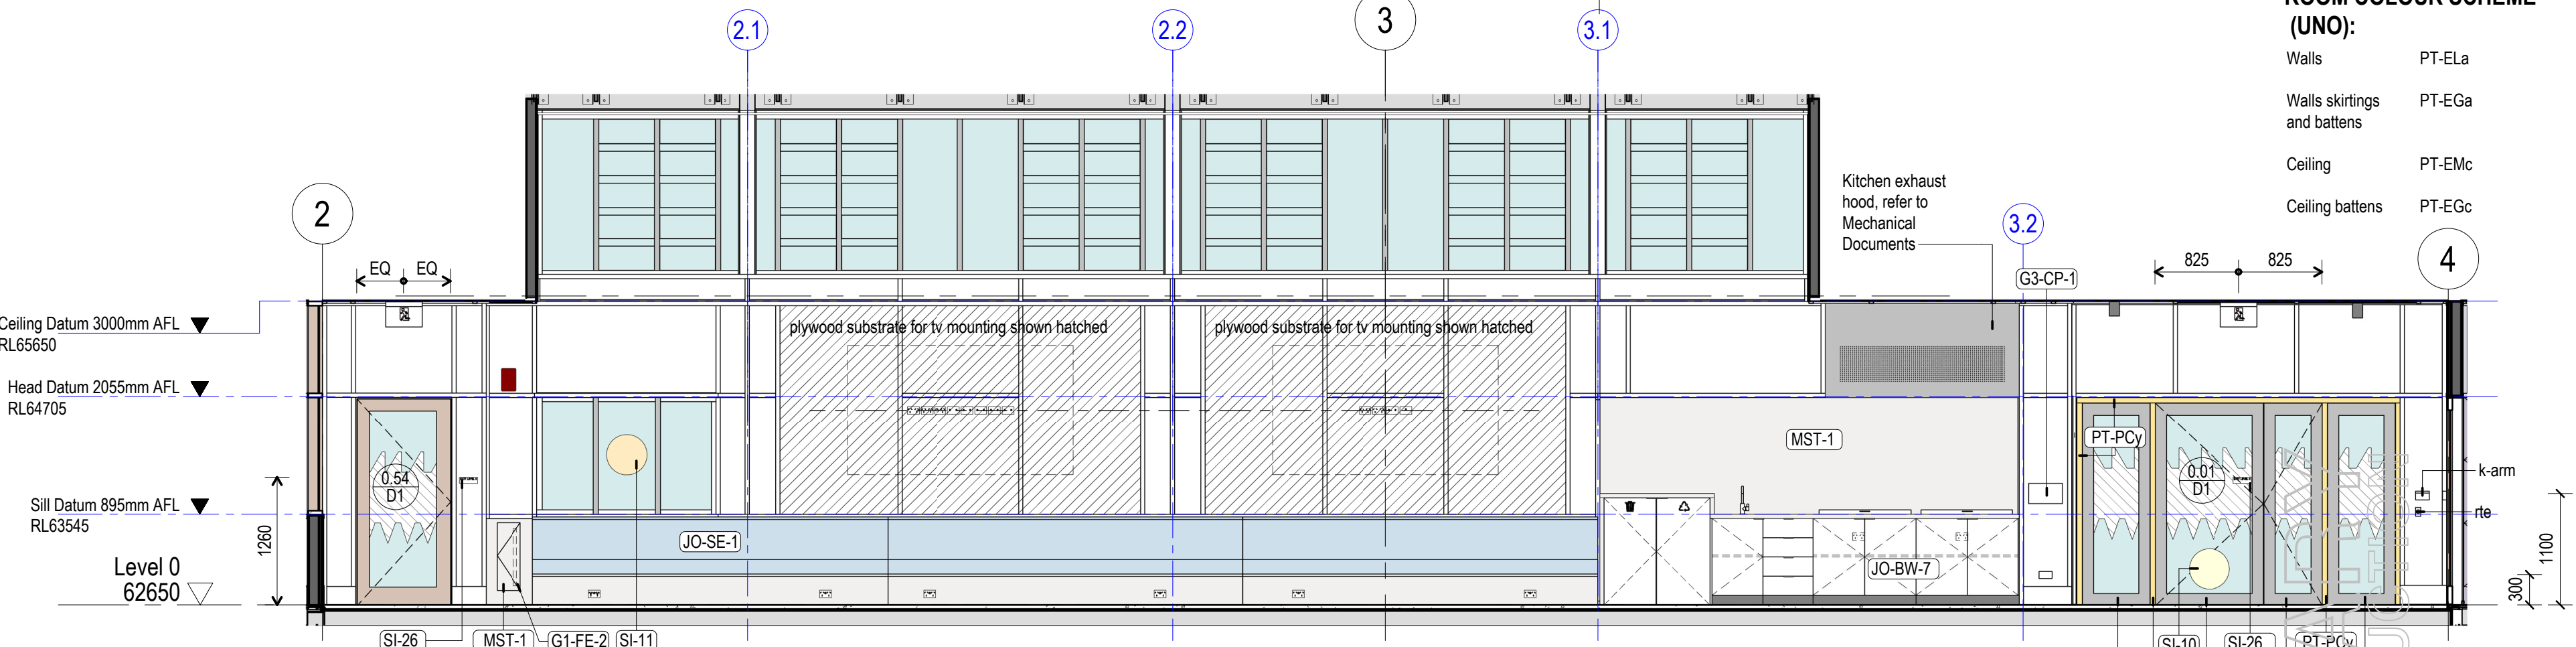


4 0.02 - Covered Outdoor - East Elevation
1 : 50

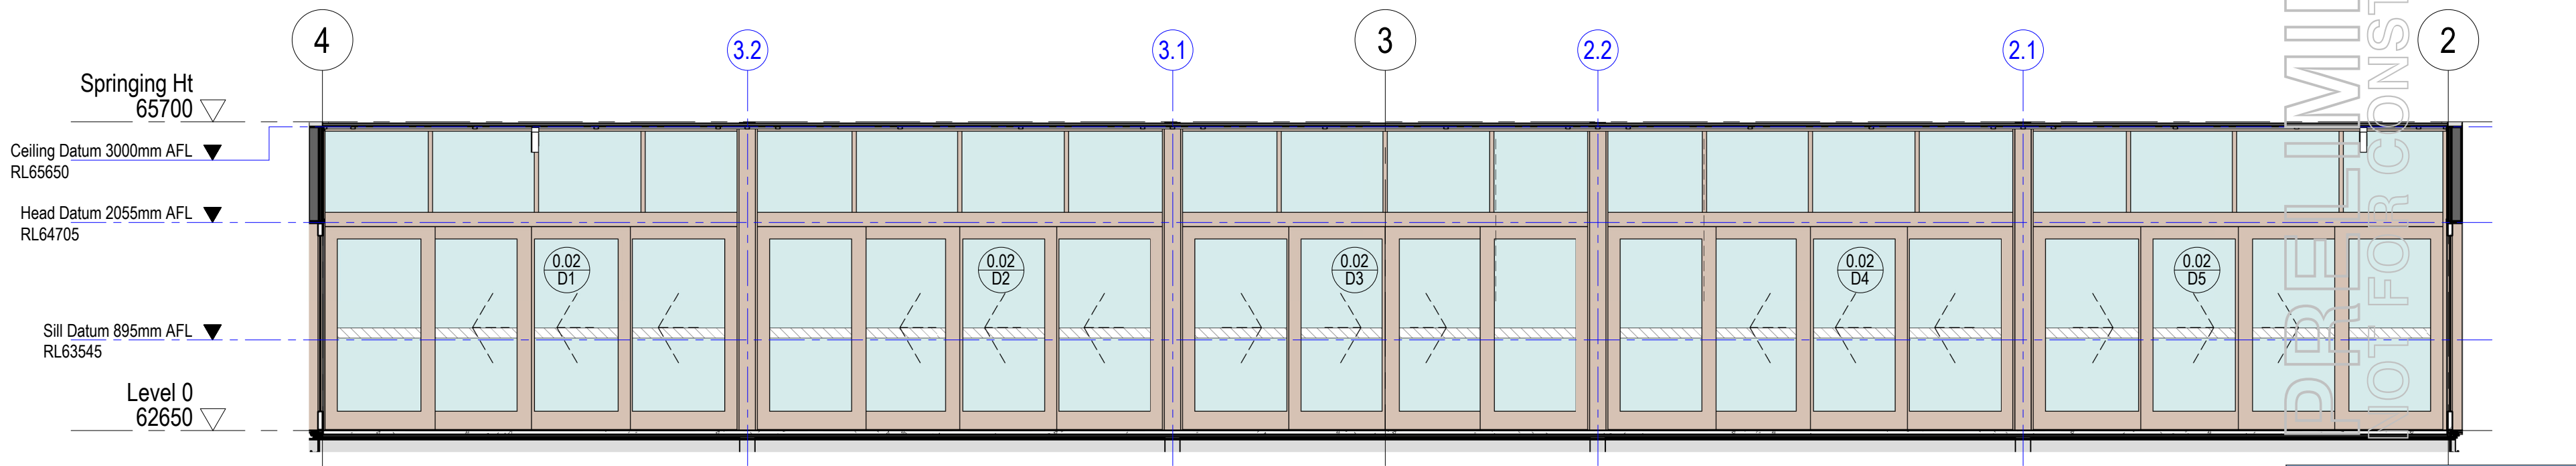

5 0.02 - Covered Outdoor - West Elevation
1 : 50

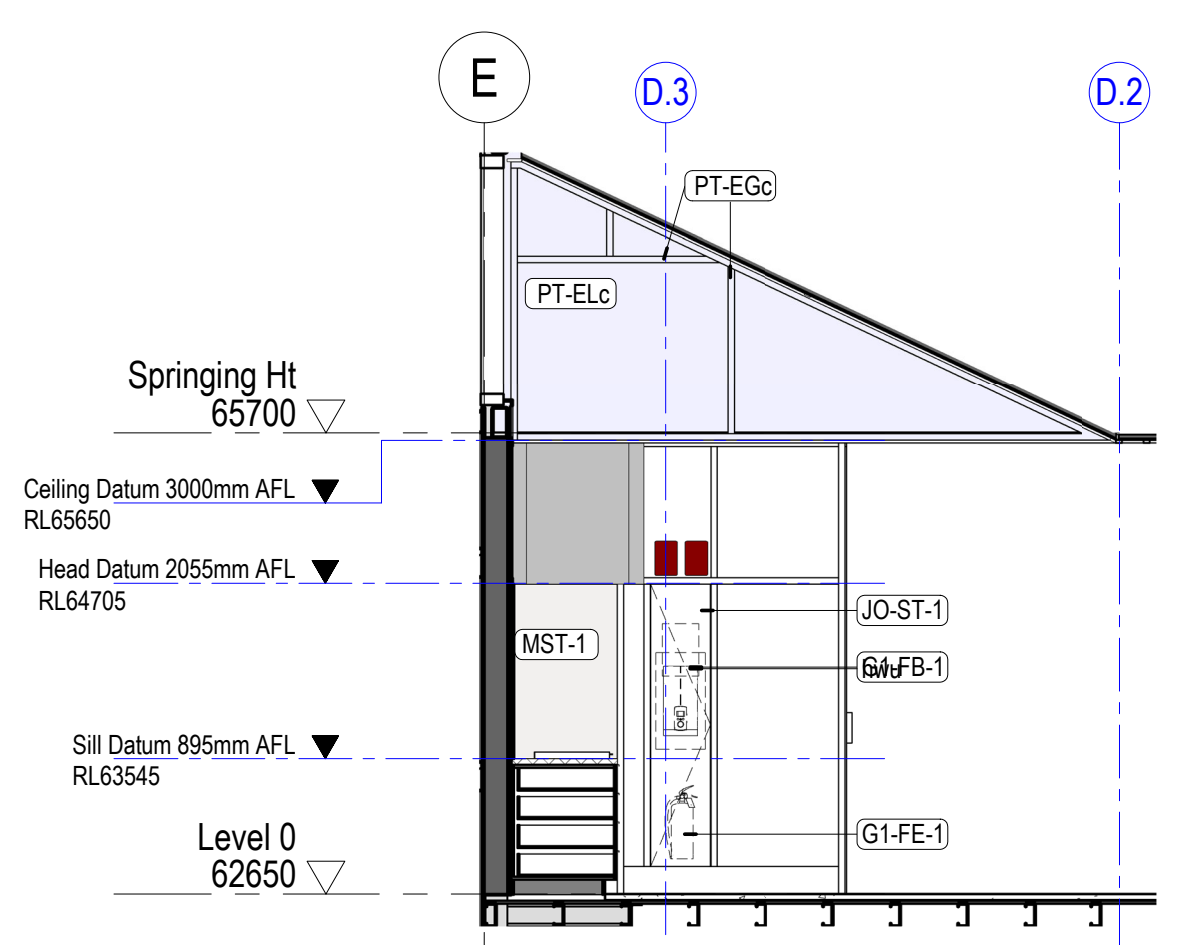

6 0.02 - Covered Outdoor - South Elevation 2
1 : 50

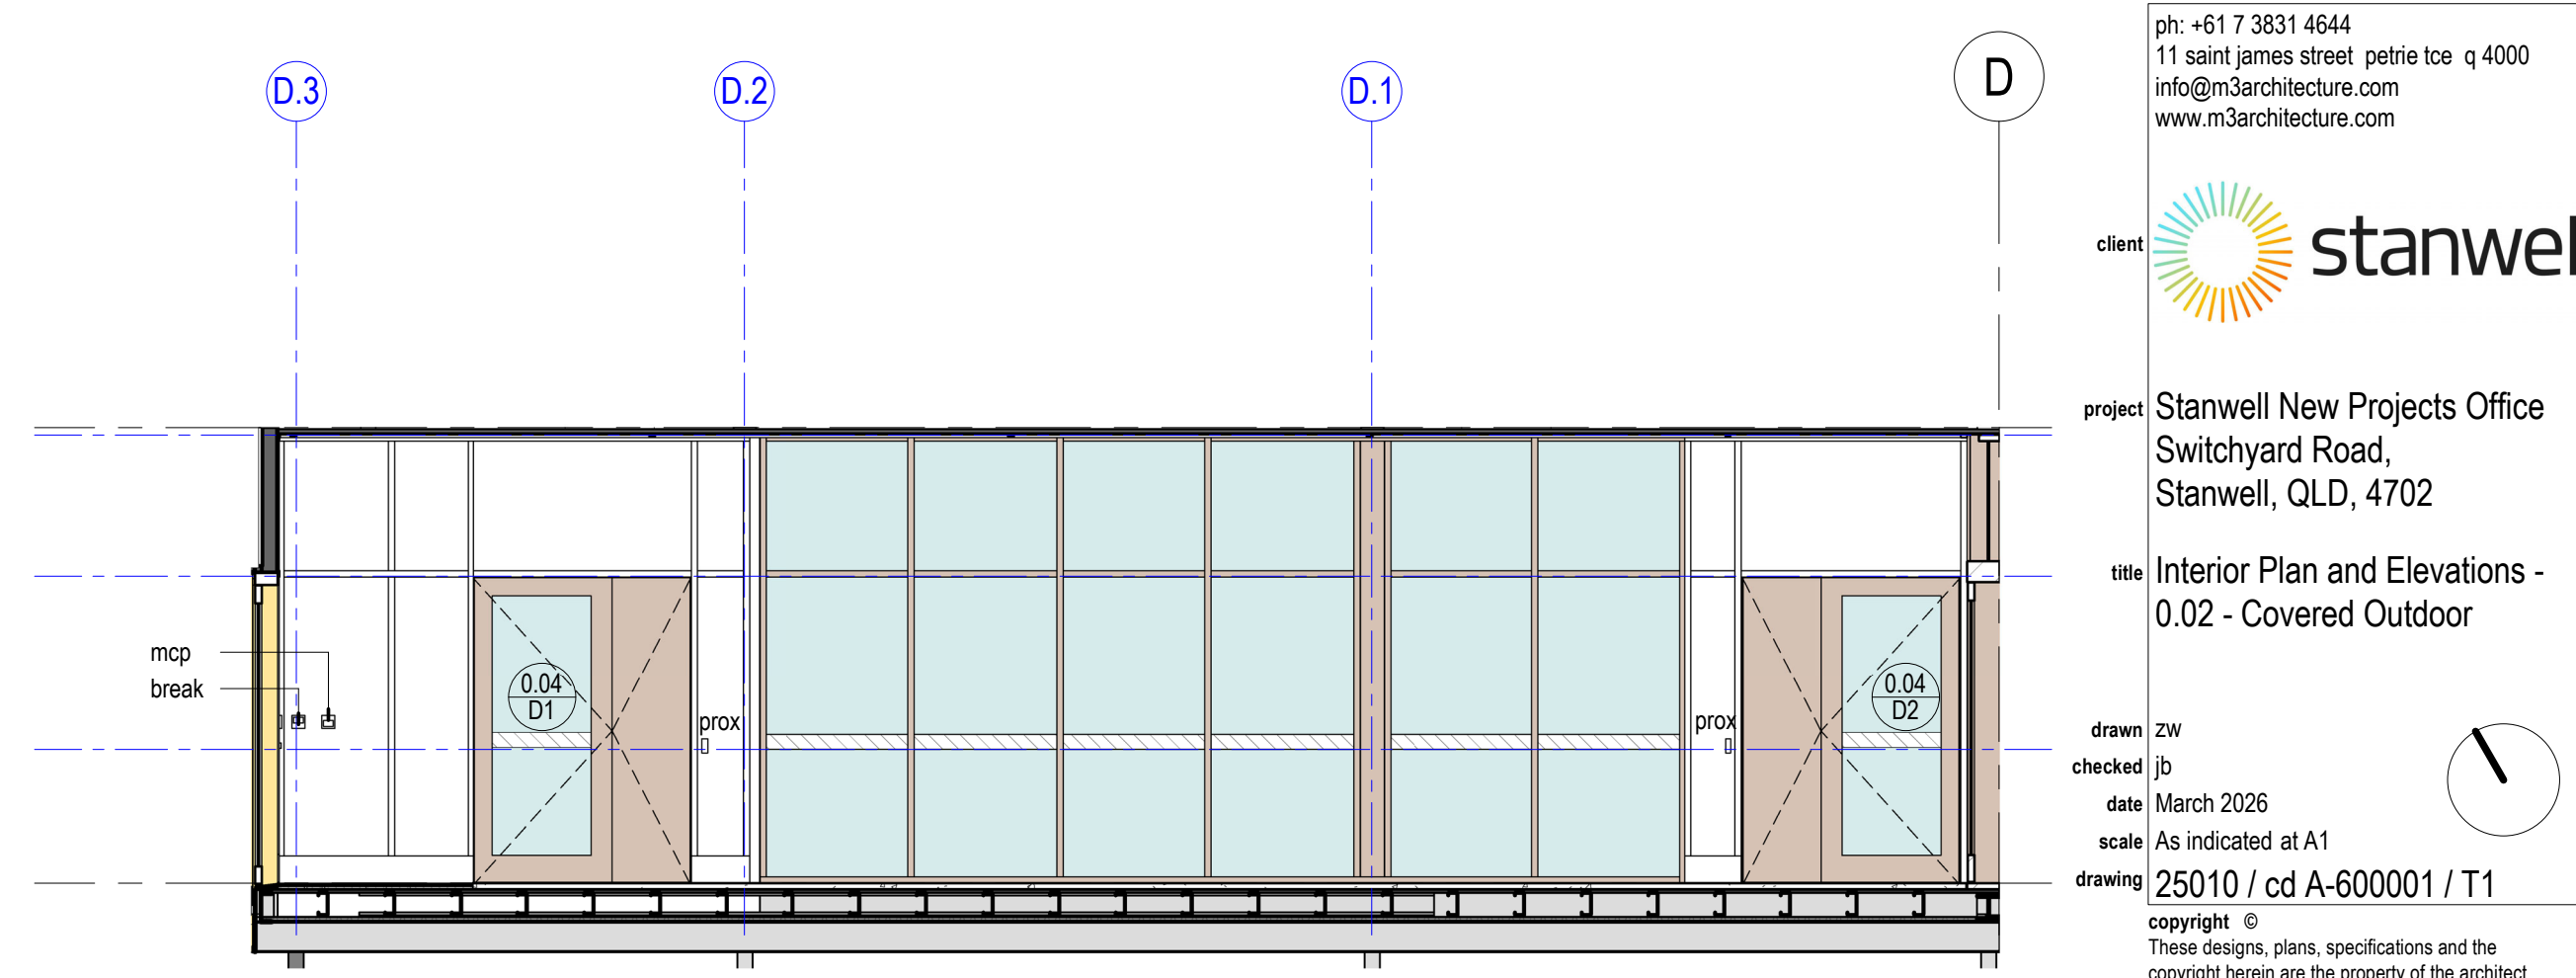

7 0.02 - Covered Outdoor - South Elevation 1
1 : 50

WALL NOTES:

1. Walls are painted typically. Refer to Colour Scheme below for paint system & colour.
2. Tags are used for materials other than painted walls.
3. Decals shown where required on glazing, MDE-1.
4. Install FC wall lining sheets to match cover batten setout, and install cover battens to conceal joints.
5. GPOs on architectural drawings are for setout purposes only. For selections refer to Electrical Engineer's documents.

Typical
Wall Battens: MTR-1a UNO
Skirting: MTR-d UNO

ROOM COLOUR SCHEME (UNO):

Walls	PT-ELa
Walls skirtings and battens	PT-EGa
Ceiling	PT-EMc
Ceiling battens	PT-EGc

Drawings include colour information. A black & white copy may not have all the information. This background is coloured blue.

brian hooperarchitect
m3architecture
ph: +61 7 3831 4644
11 saint james street petrie tce q 4000
info@m3architecture.com
www.m3architecture.com

client stanwell

project Stanwell New Projects Office
Switchyard Road,
Stanwell, QLD, 4702

title Interior Plan and Elevations -
0.02 - Covered Outdoor

drawn ZW
checked JB
date March 2026
scale As indicated at A1
drawing 25010 / cd A-600001 / T1

copyright ©
These designs, plans, specifications and the copyright herein are the property of the architect and must not be used, reproduced, or copied wholly or in part without the written permission of m3architecture Pty Ltd abn 23 079 044 545.
Use figured dimensions in preference to scale. If there are any questions contact the architect.

1:50 at A1
0 0.5 1.0 1.5 2.0 2.5m