




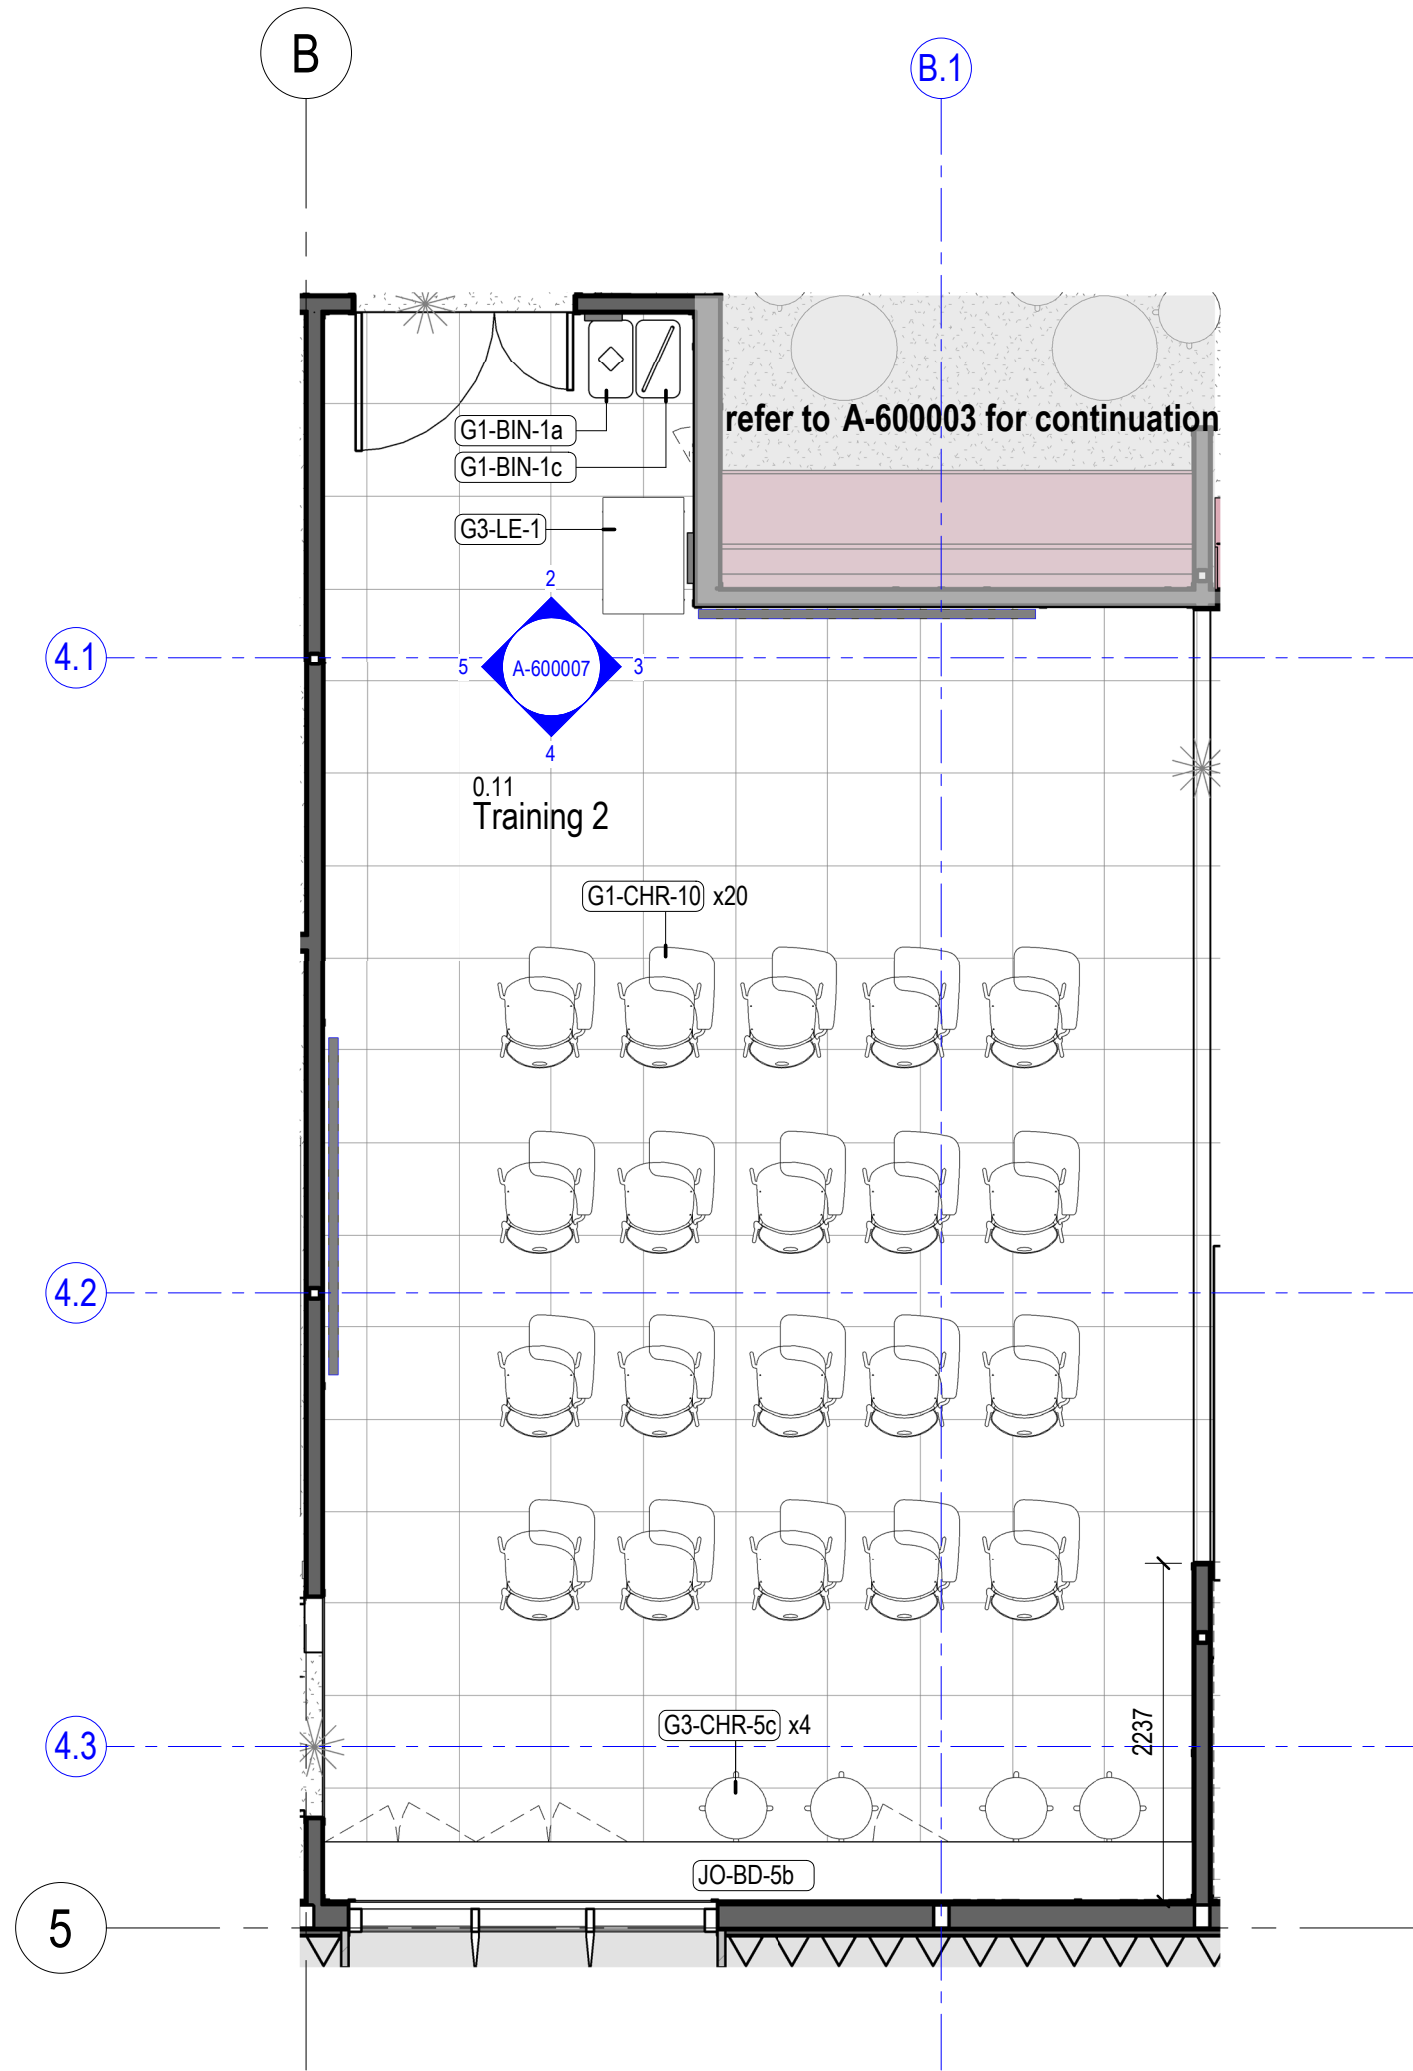


1 0.11 - Training Kitchen - Plan
1 : 50

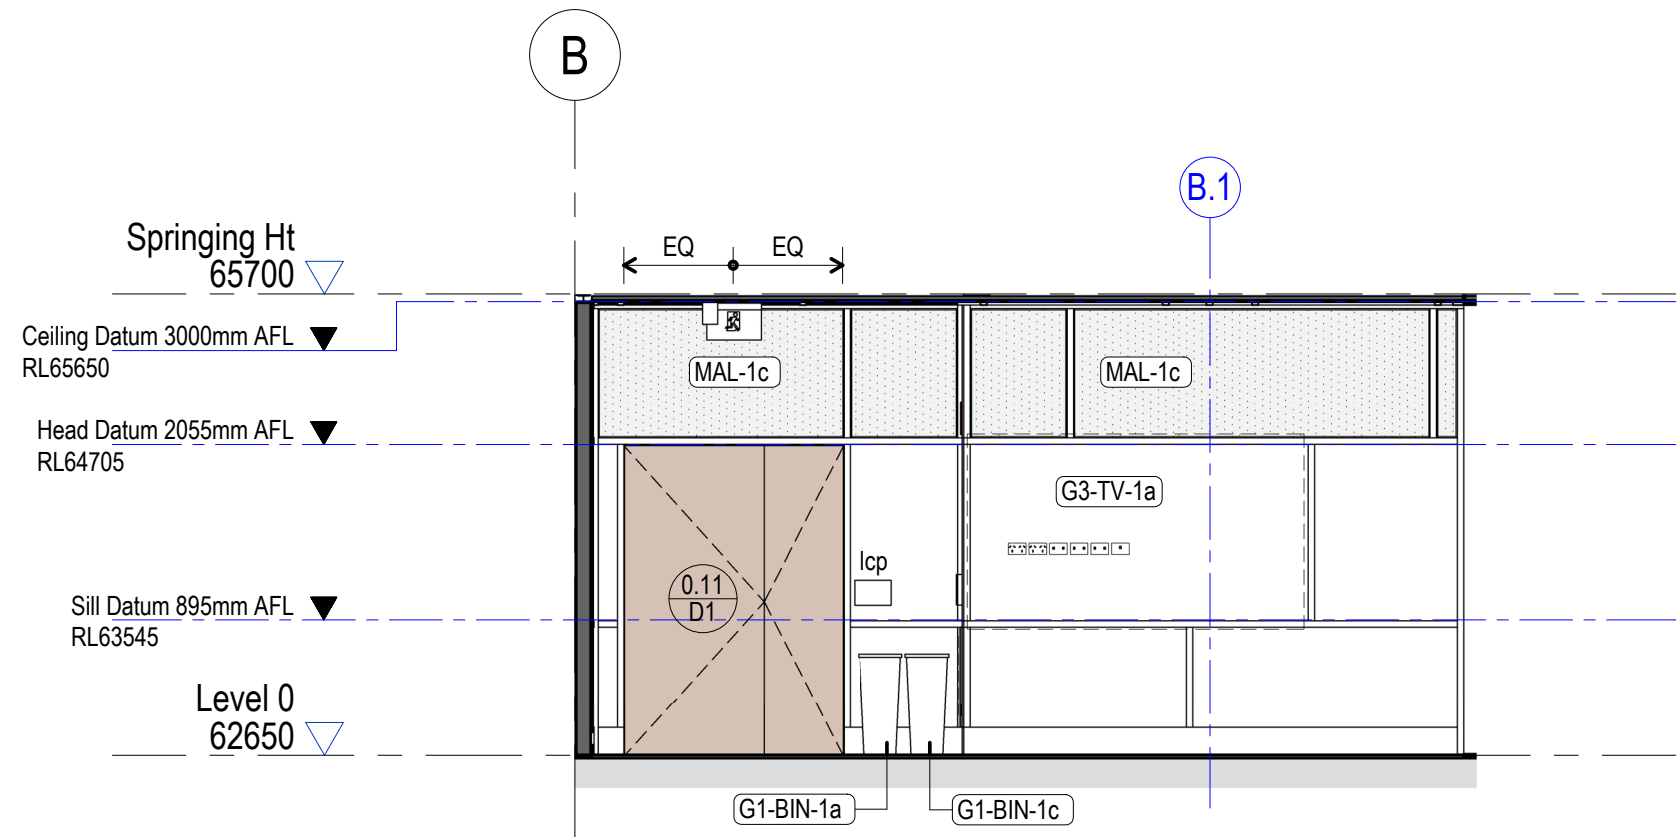


2 0.11 - Training 02 - North Elevation
1 : 50

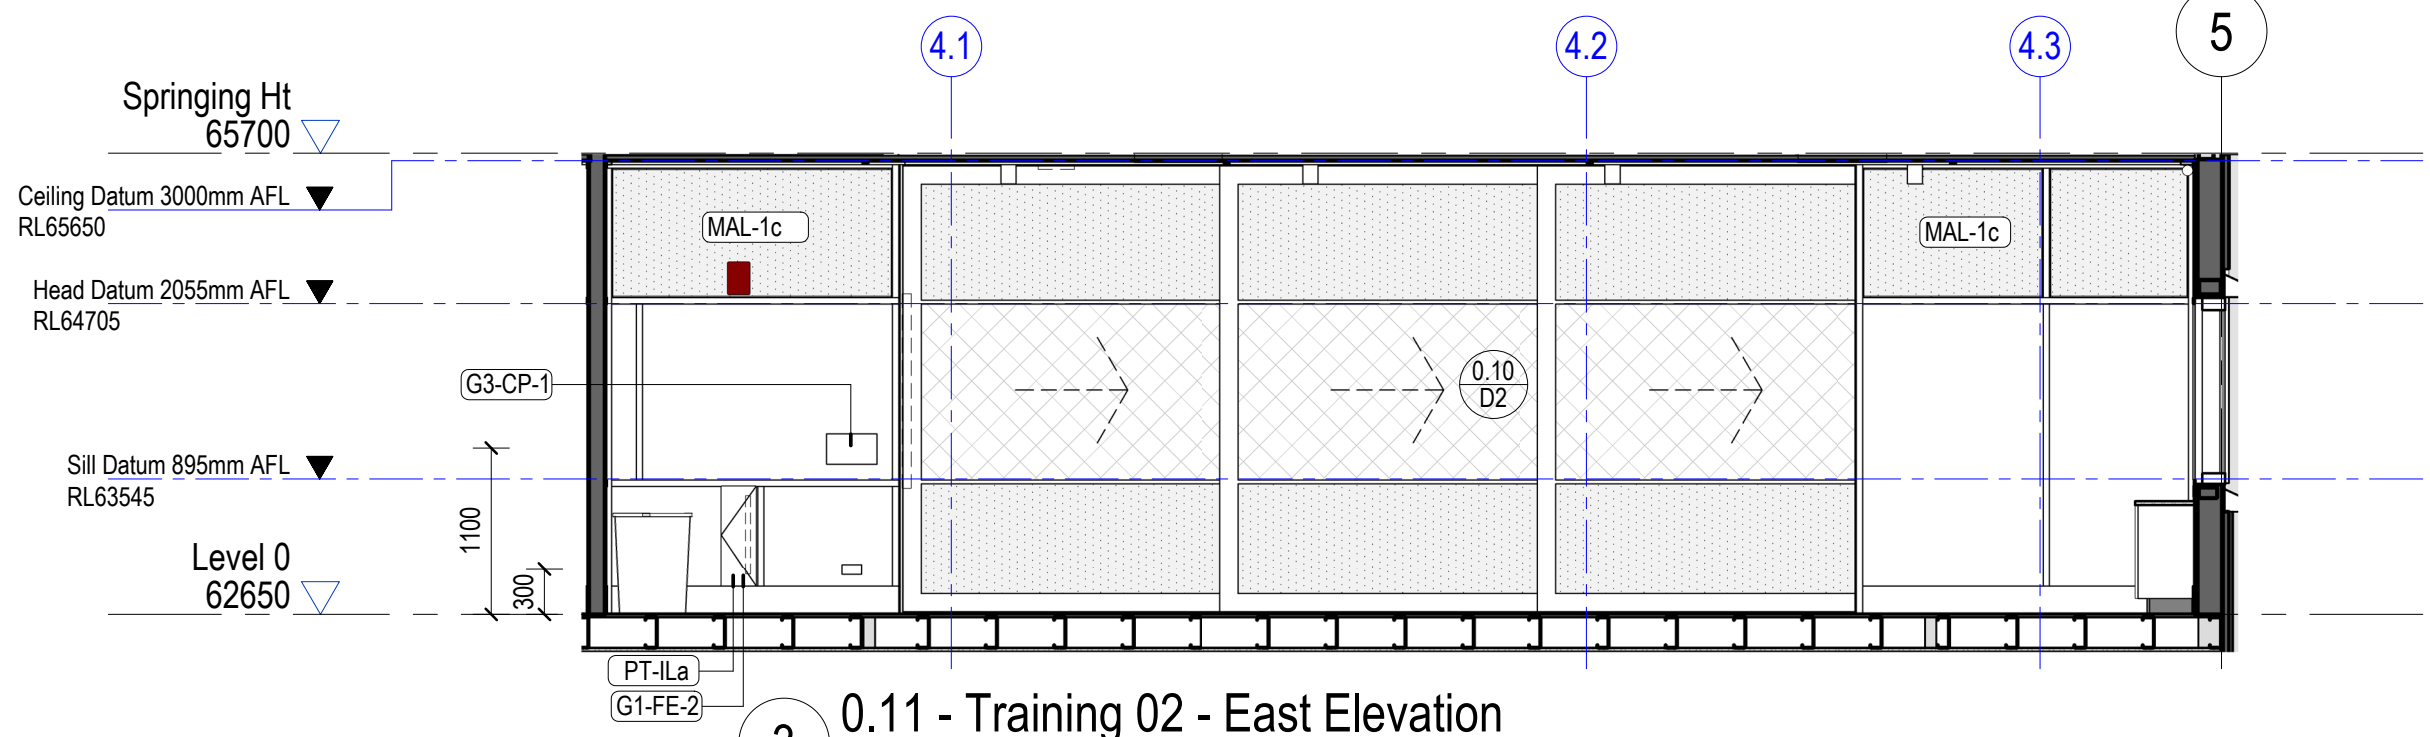

3 0.11 - Training 02 - East Elevation
1 : 50

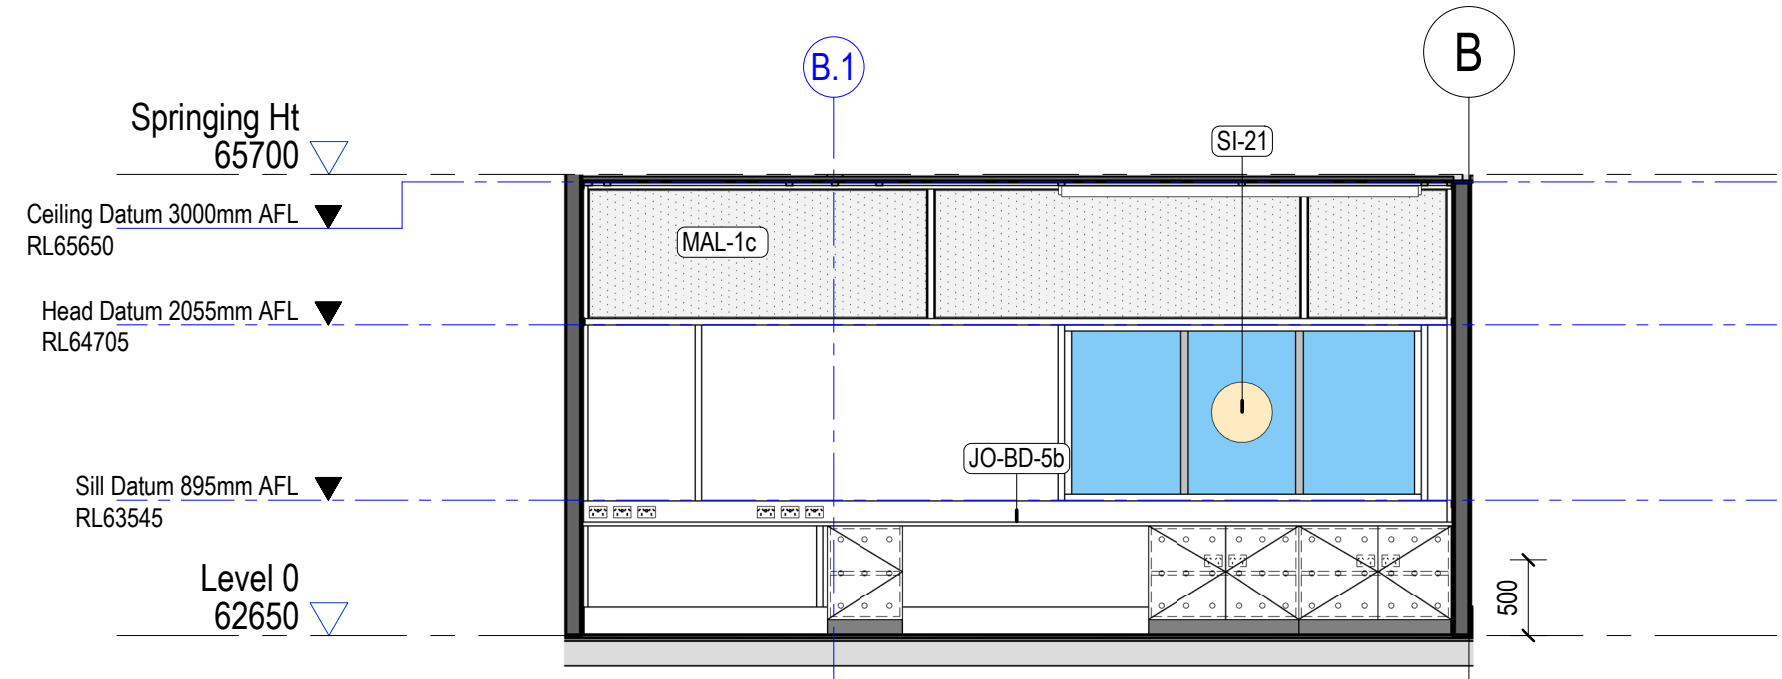

4 0.11 - Training 02 - South Elevation
1 : 50

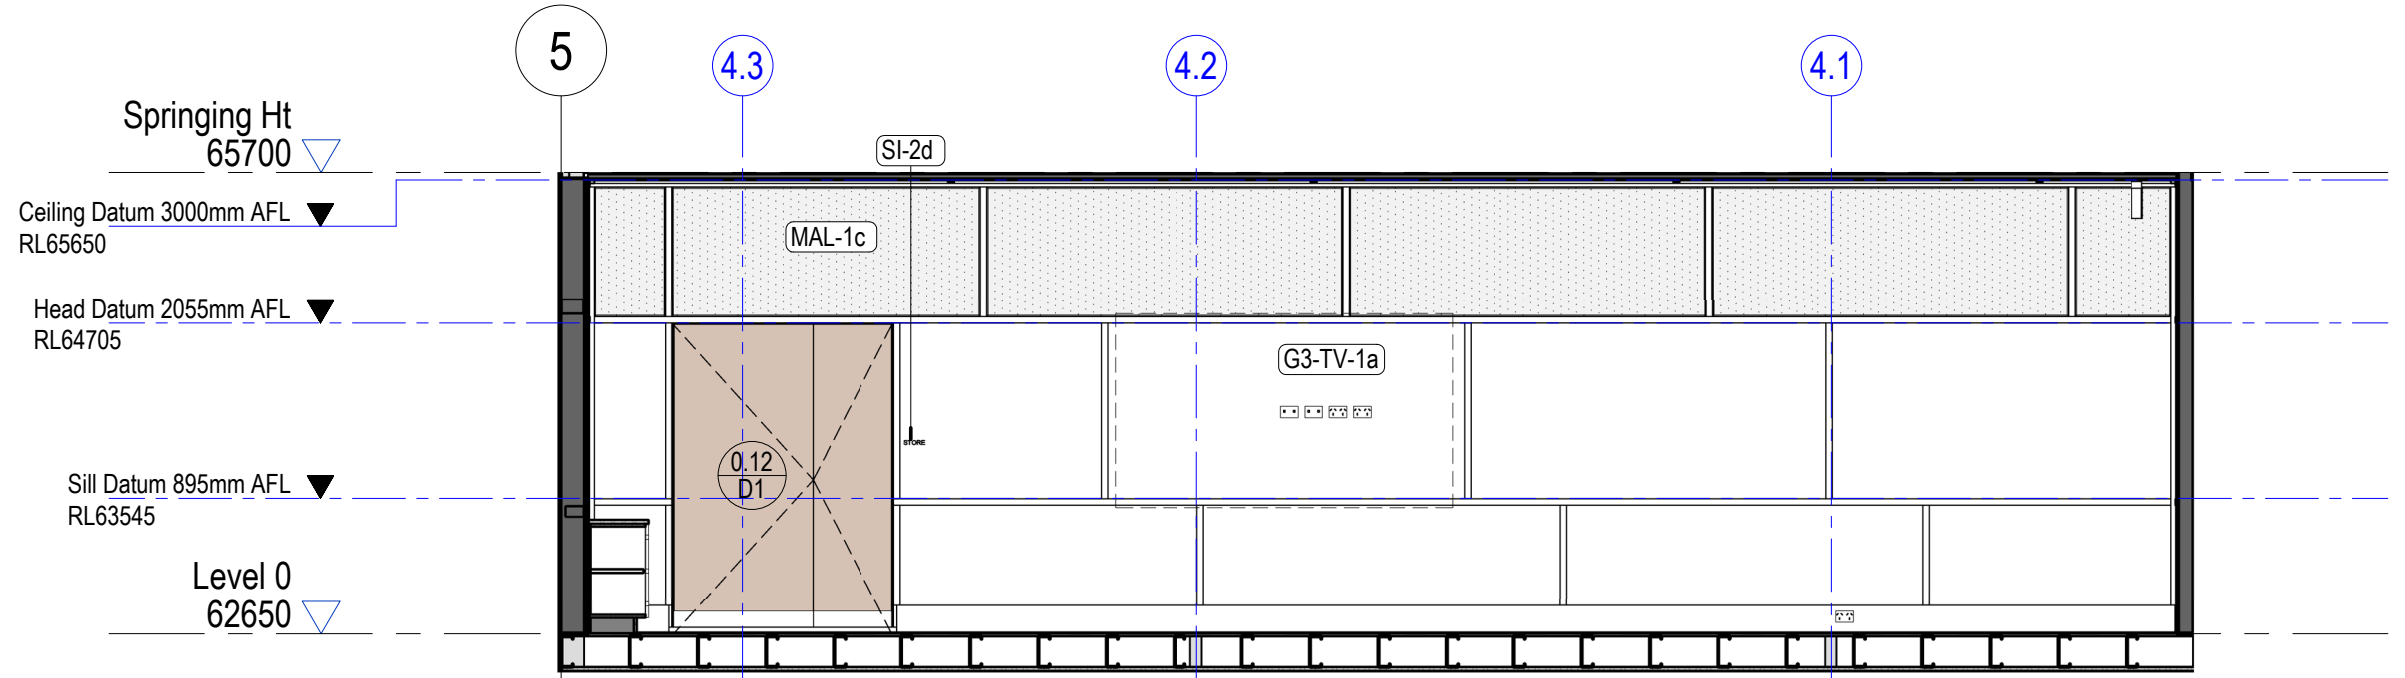

5 0.11 - Training 02 - West Elevation
1 : 50

WALL NOTES:

- Walls are painted typically. Refer to Colour Scheme below for paint system & colour.
- Tags are used for materials other than painted walls.
- Decals shown where required on glazing, MDE-1.
- Install FC wall lining sheets to match cover batten setout, and install cover battens to conceal joints.
- GPOs on architectural drawings are for setout purposes only. For selections refer to Electrical Engineer's documents.

Typical
Wall Battens: MTR-1a UNO
Skirting: MTR-d UNO

ROOM COLOUR
SCHEME WHITE (UNO):

Walls PT-1La
Walls skirtings and battens PT-IGa
Ceiling PT-1Ma
Ceiling battens PT-IGa

GLASS TYPES

LJV - Glass louvres, refer to Wall Schedule for selection
FG - Fixed clear single glazed, refer to Wall Schedule for selection
IGL - Fixed clear double glazed, refer to Wall Schedule for selection

Drawings include colour information. A black & white copy may not have all the information. This background is coloured blue.

brian hooperarchitect
m3architecture
ph: +61 7 3831 4644
11 saint james street petrie tce q 4000
info@m3architecture.com
www.m3architecture.com

client stanwell

project Stanwell New Projects Office
Switchyard Road,
Stanwell, QLD, 4702

title Interior Plan and Elevations -
0.11 - Training 02

drawn ZW
checked JB
date March 2026
scale As indicated at A1
drawing 25010 / cd A-600007 / T1

copyright ©
These designs, plans, specifications and the copyright herein are the property of the architect and must not be used, reproduced, or copied wholly or in part without the written permission of m3architecture Pty Ltd abn 23 079 044 545. Use figured dimensions in preference to scale. If there are any questions contact the architect.

1:50 at A1
0 0.5 1.0 1.5 2.0 2.5m