




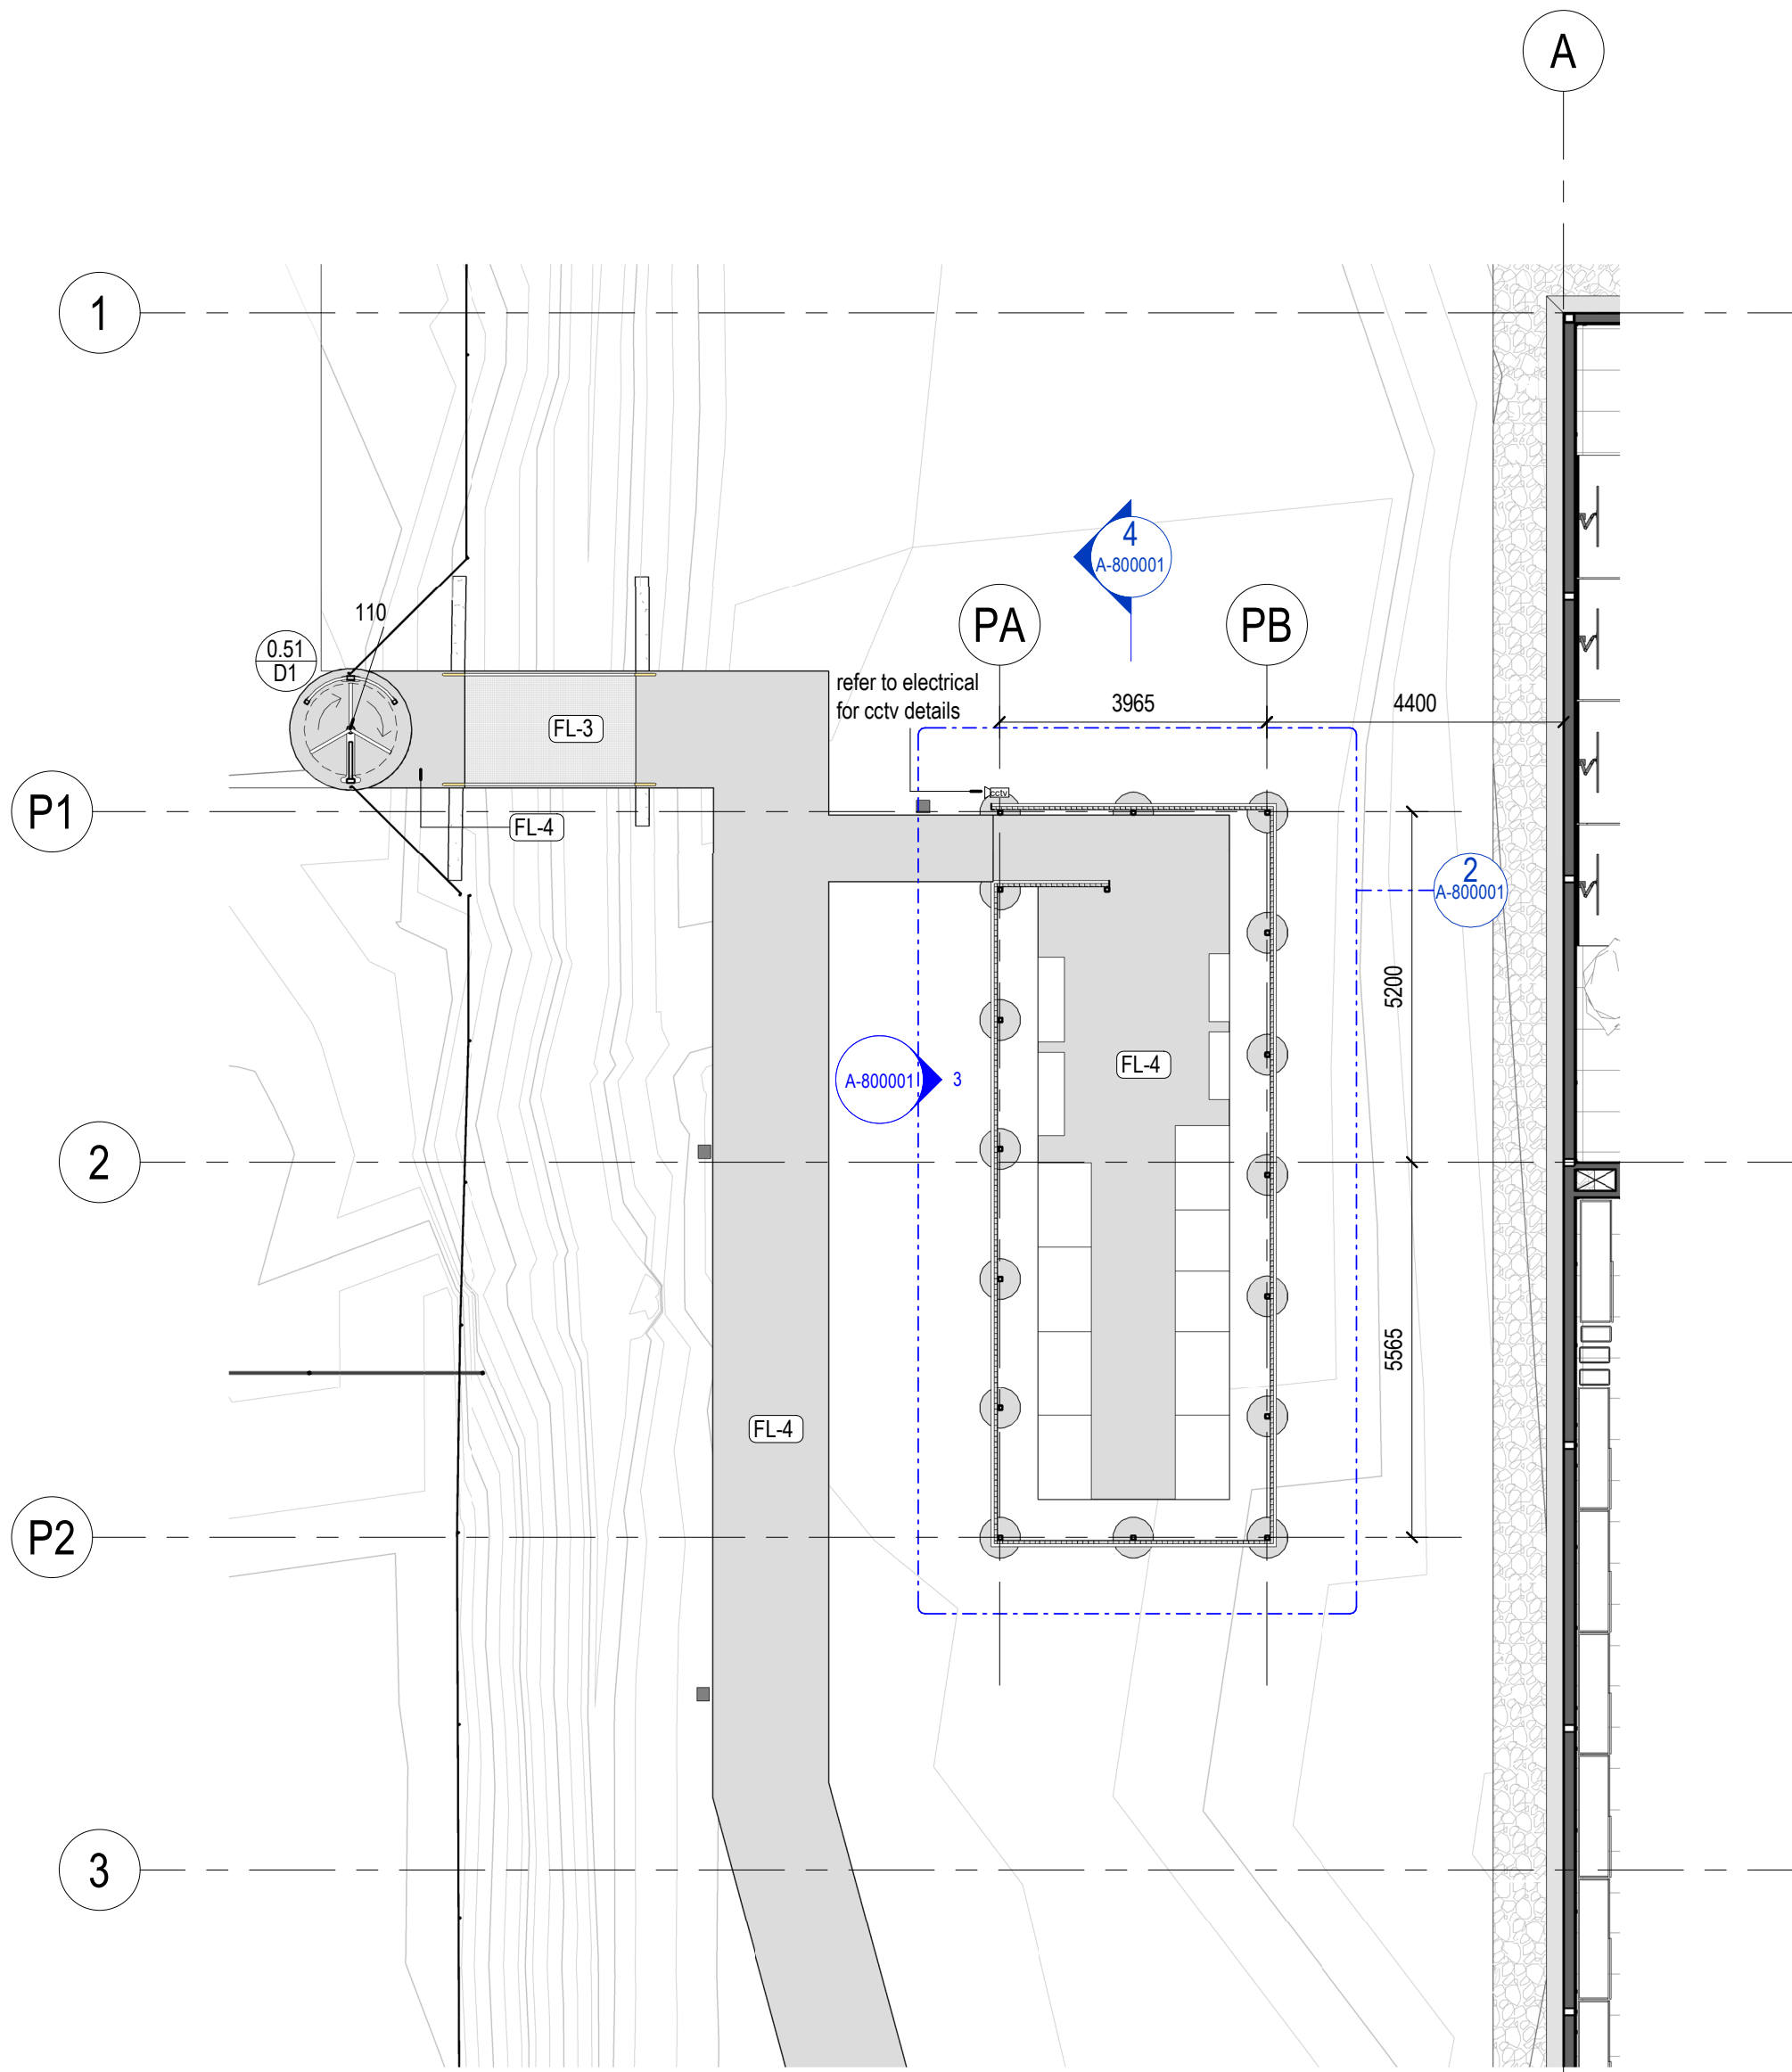


1 Plant Room Site Plan
1 : 100

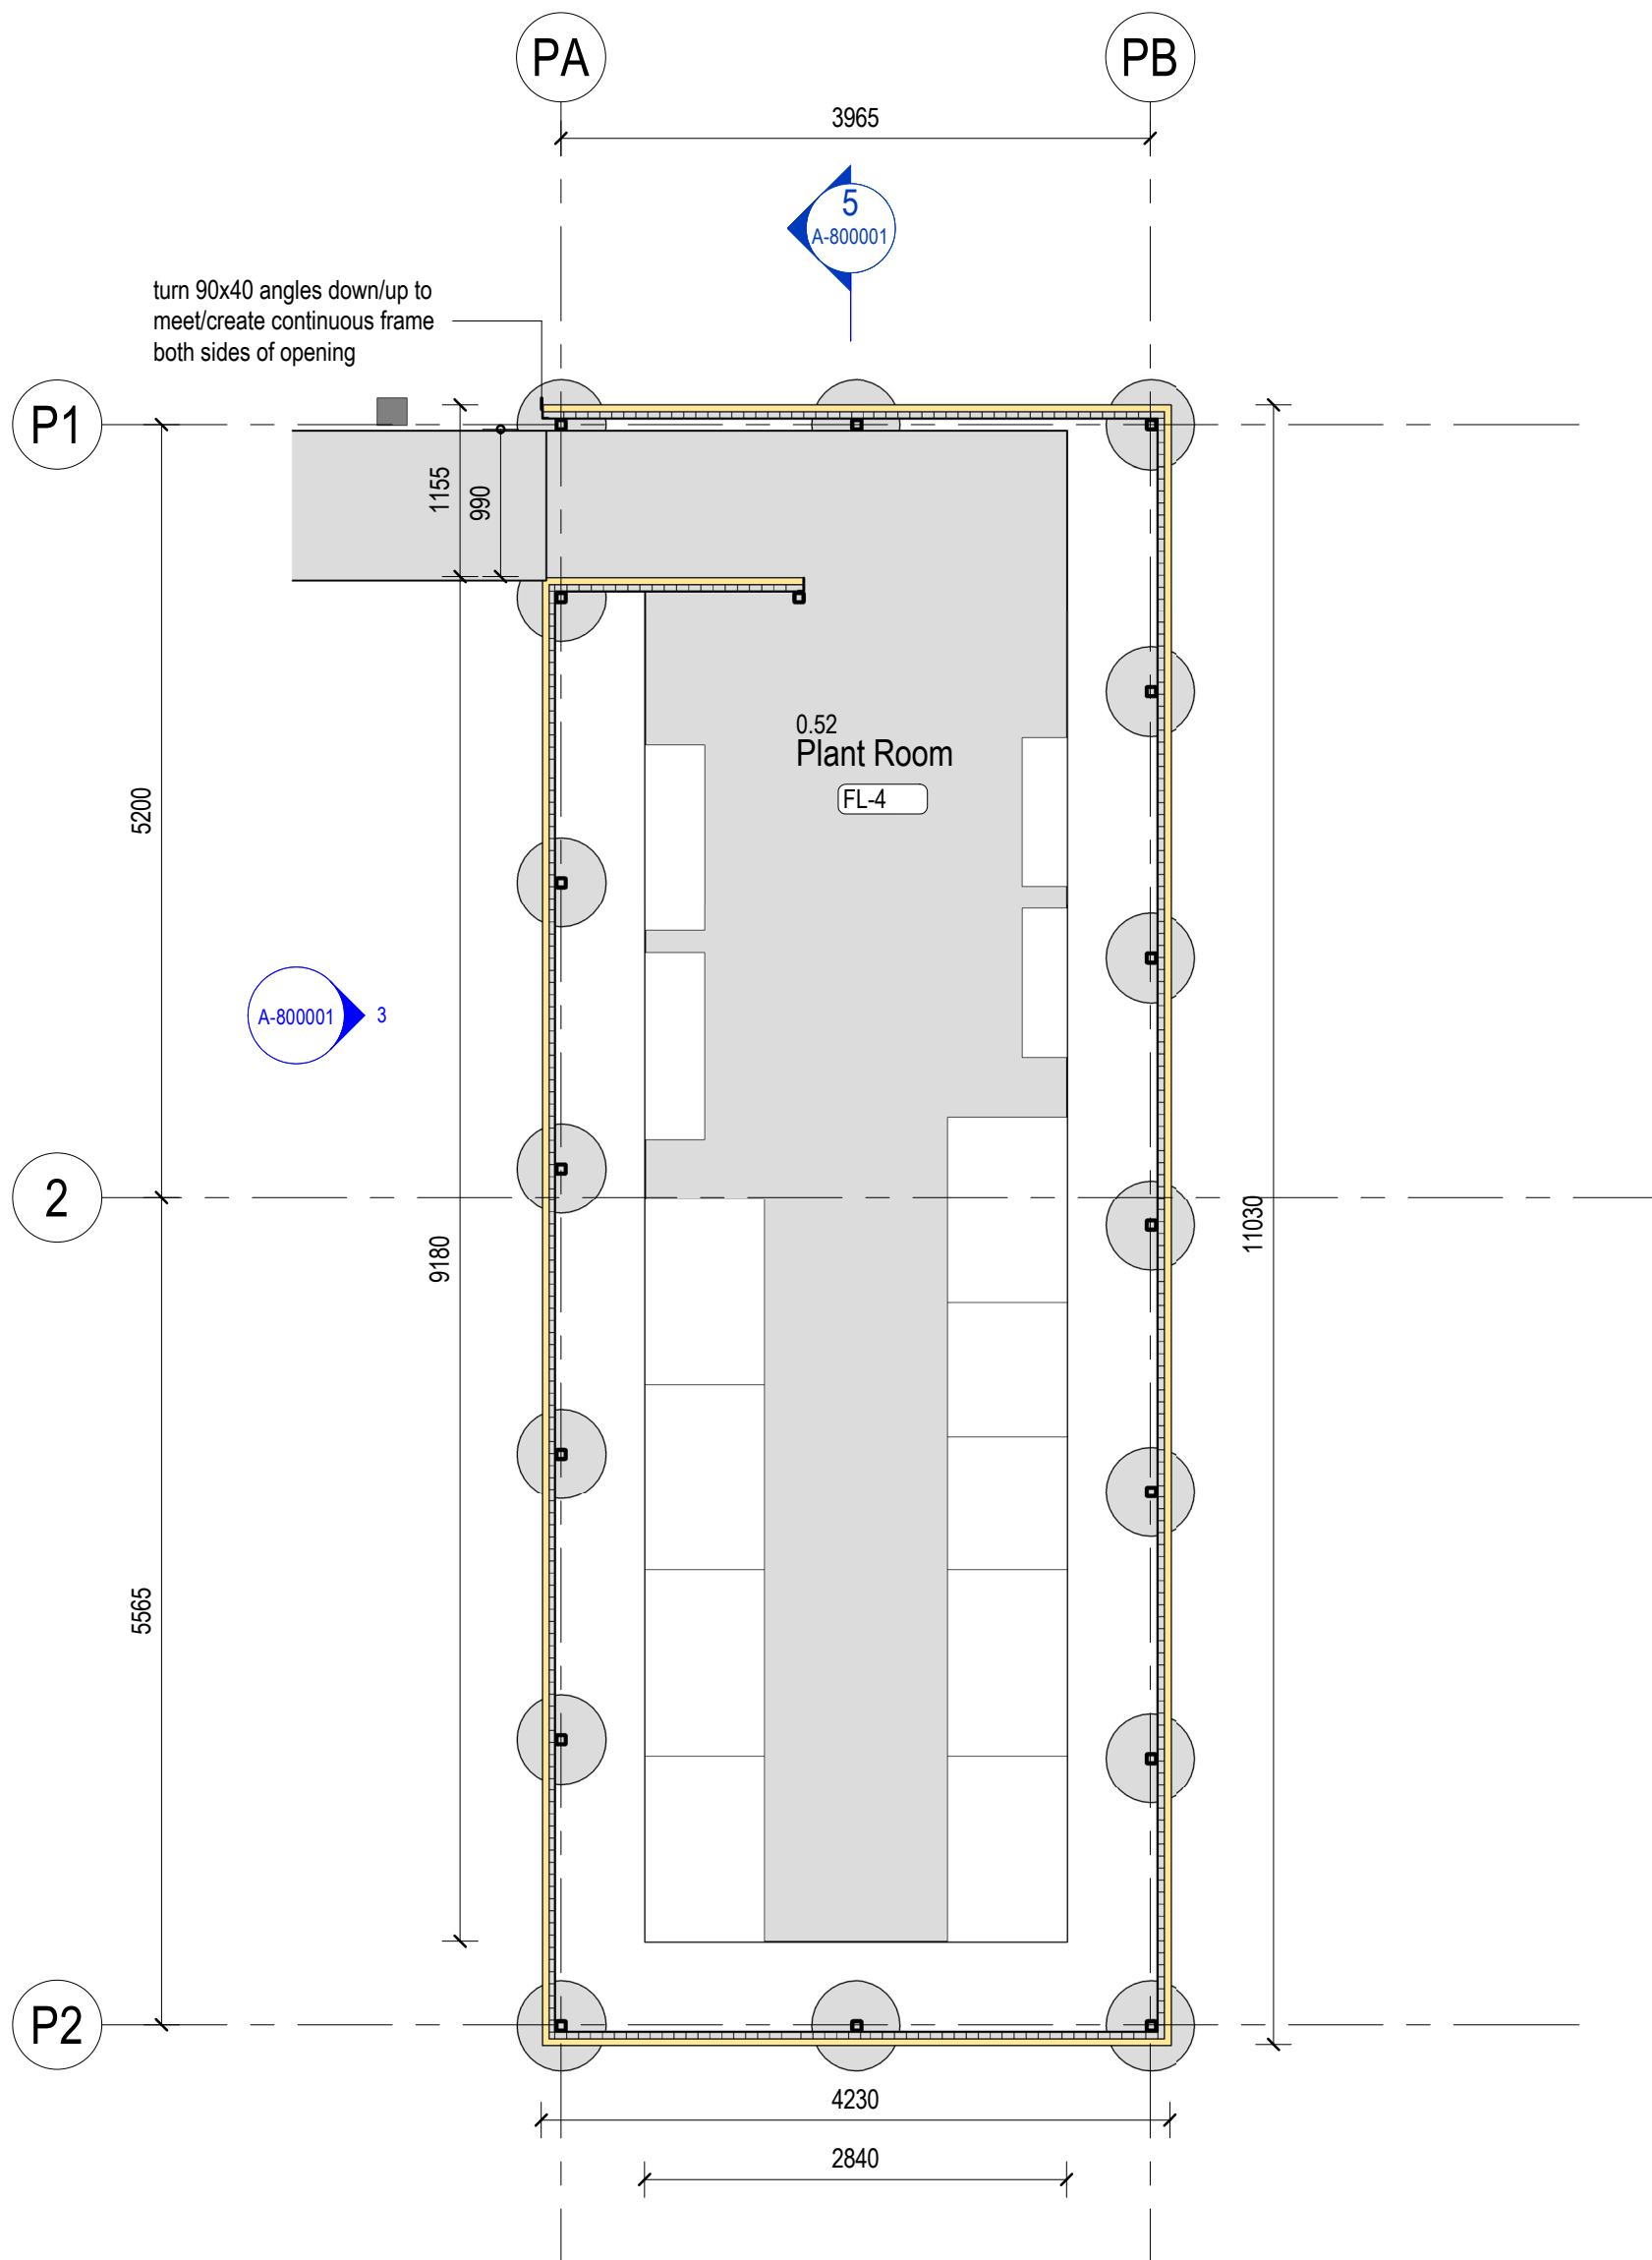


2 Plant Room Floor Plan
1 : 50

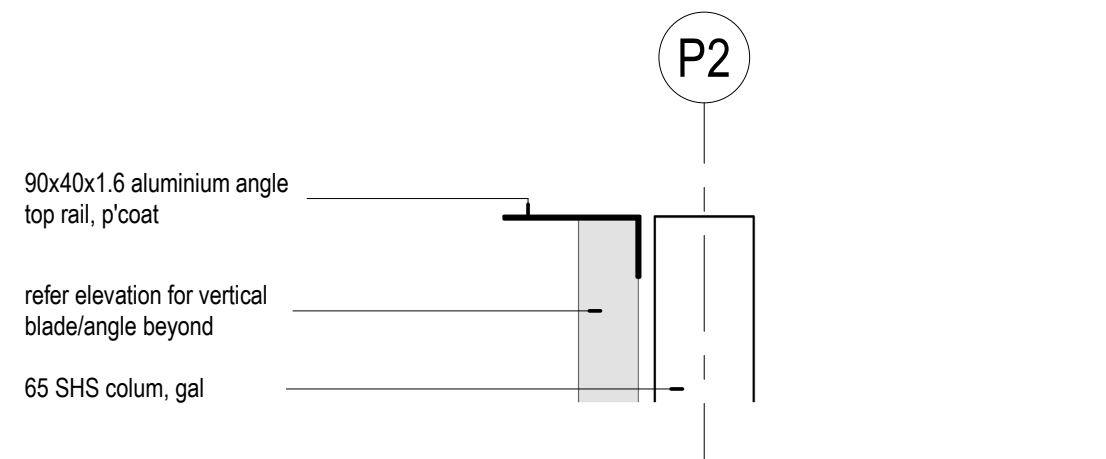


5 Plant Room Detail Section A
1 : 5

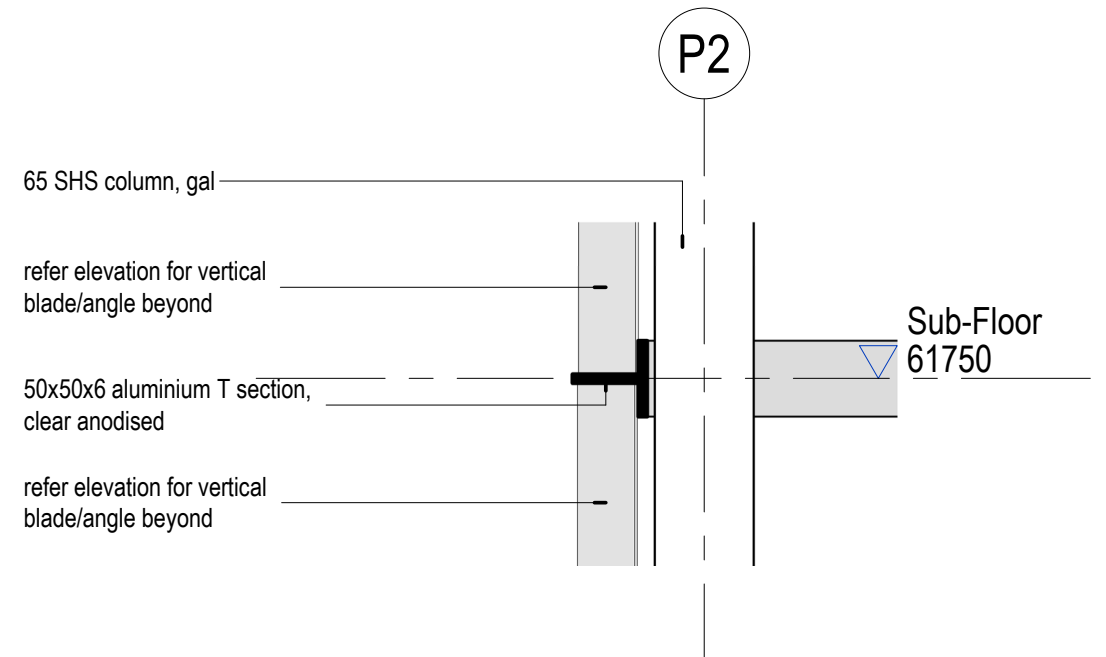


6 Plant Room Detail Section B
1 : 5

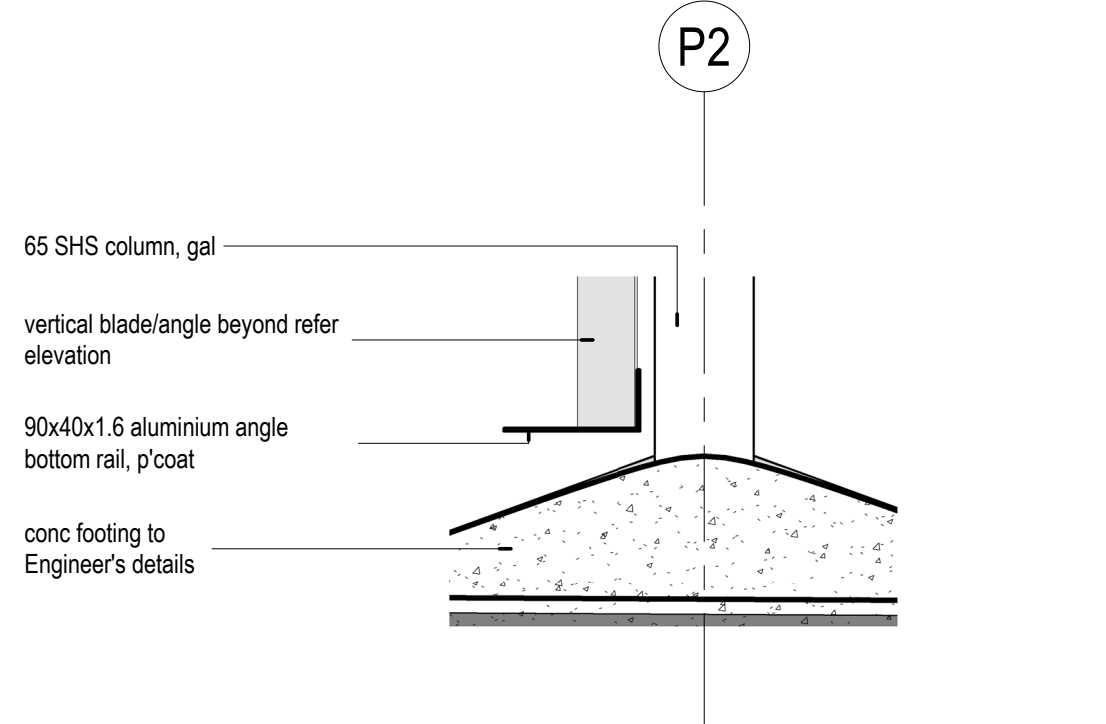

7 Plant Room Detail Section C
1 : 5

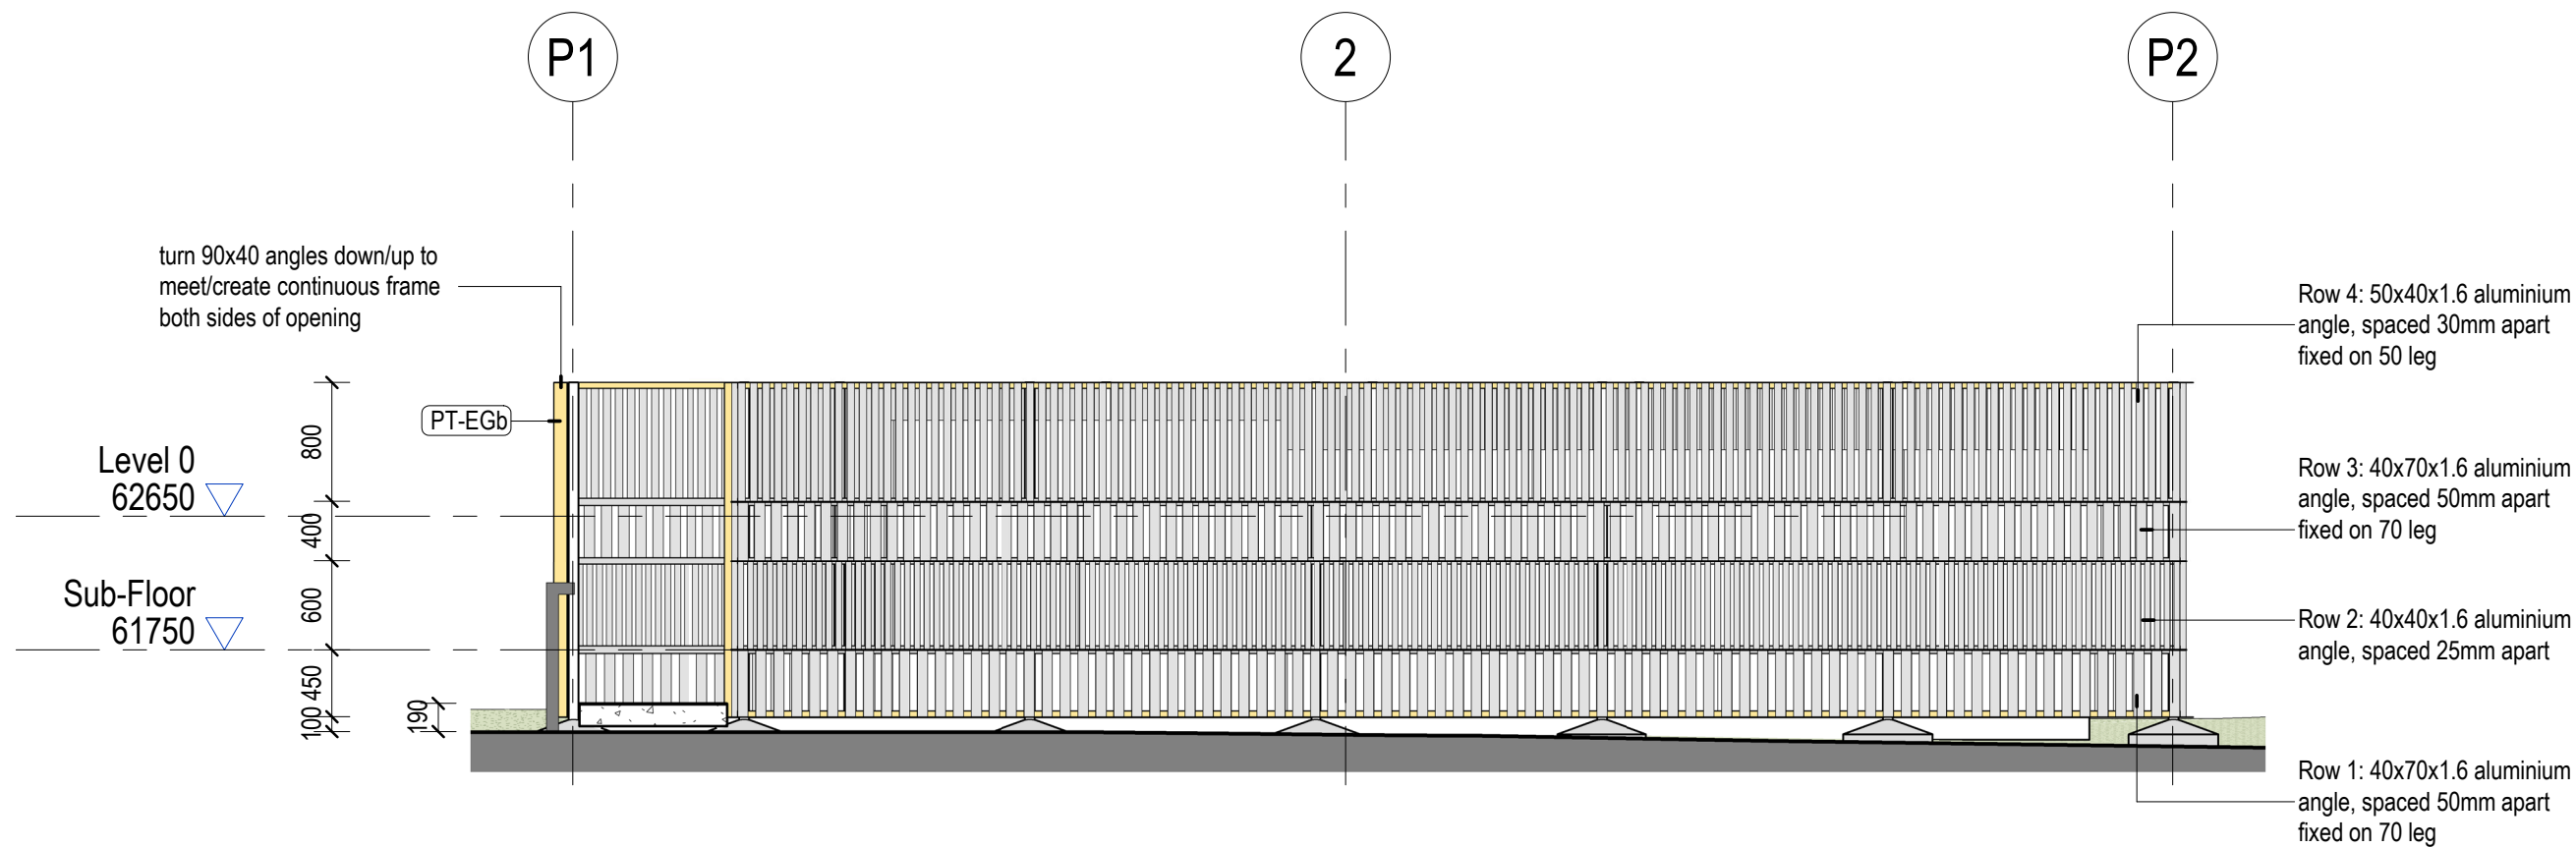

3 80 N Plant Room Elevation
1 : 50

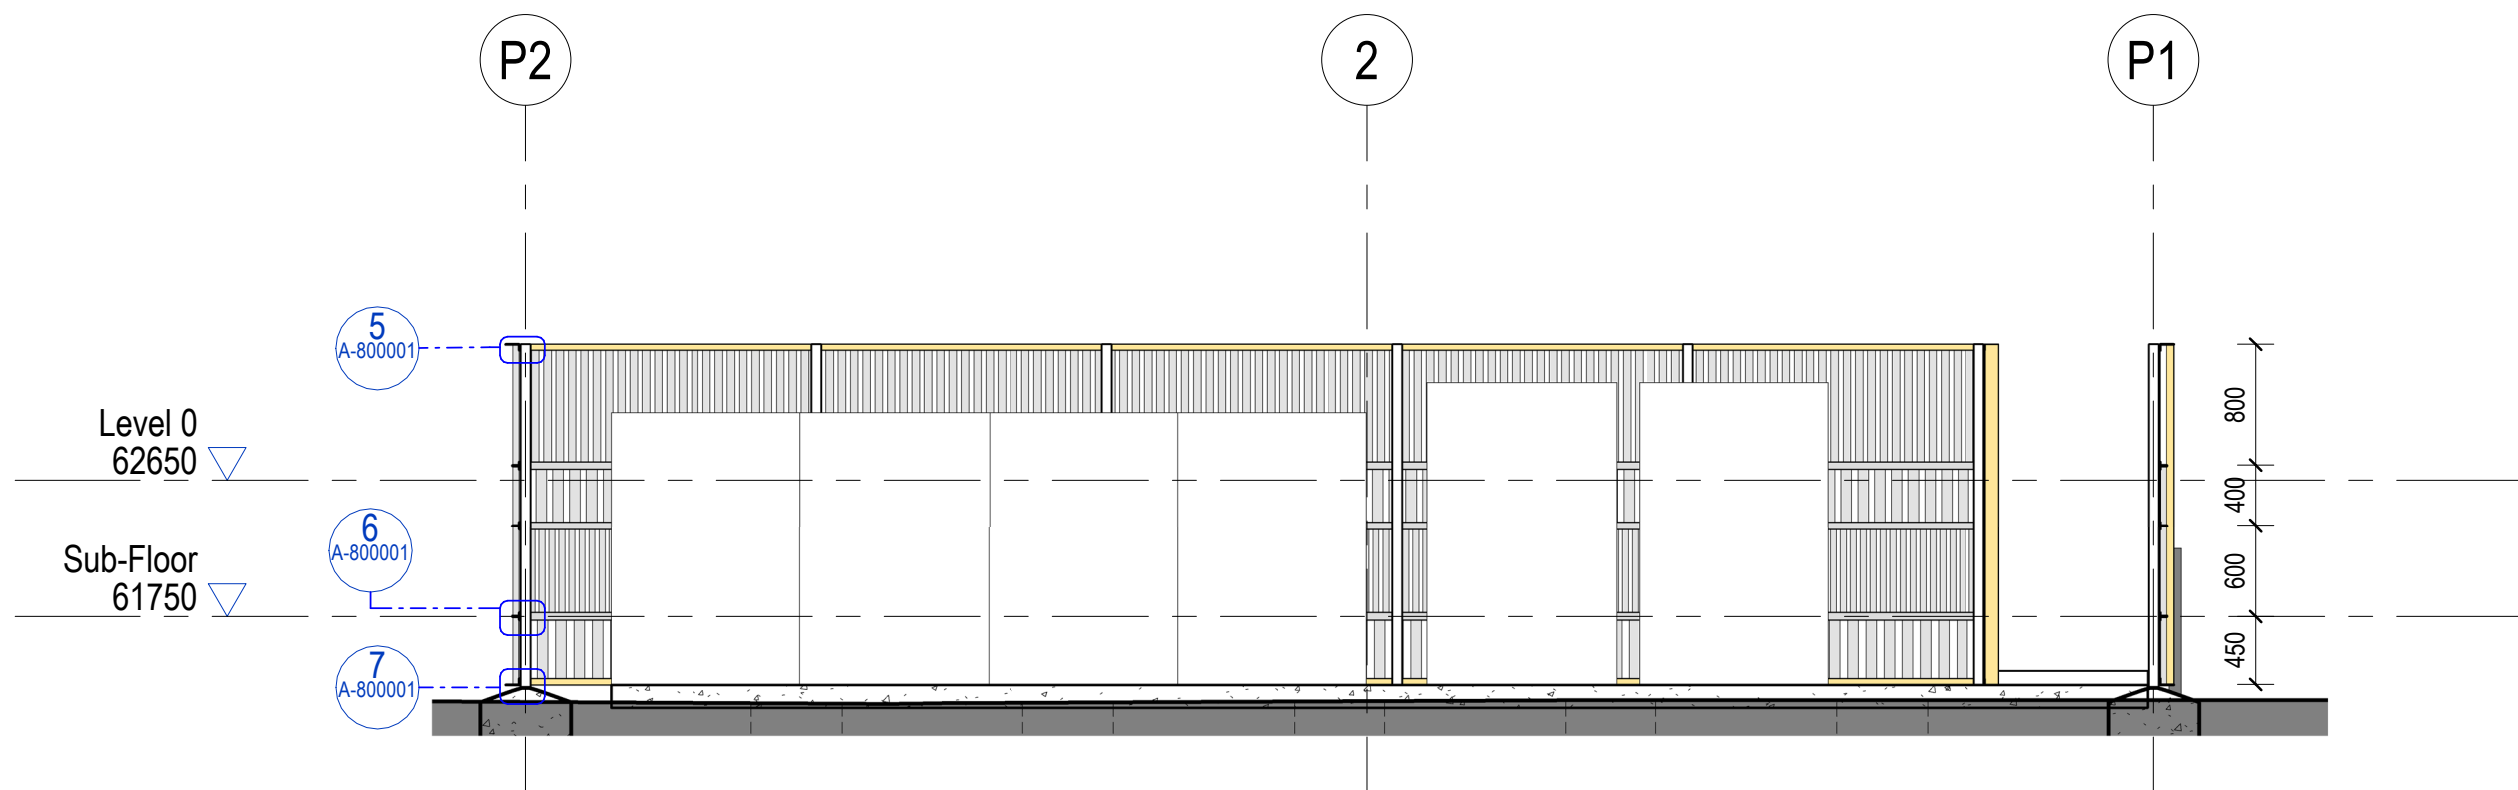

4 Plant Room Section
1 : 50

PRELIMINARY
NOT FOR CONSTRUCTION

Drawings include colour information. A black & white copy may not have all the information. This background is coloured blue.

brian hooper**architect**
m3architecture
ph: +61 7 3831 4644
11 saint james street petrie tce q 4000
info@m3architecture.com
www.m3architecture.com

client **stanwell**

project **Stanwell New Projects Office**
Switchyard Road,
Stanwell, QLD, 4702

title **Plant Room**

drawn **ZW**
checked **JB**
date **March 2026**
scale **As indicated at A1**
drawing **25010 / cd A-800001 / T1**

copyright ©
These designs, plans, specifications and the copyright herein are the property of the architect and must not be used, reproduced, or copied wholly or in part without the written permission of m3architecture Pty Ltd abn 23 079 044 545. Use figured dimensions in preference to scale. If there are any questions contact the architect.

1:1 at A1
0 10 20 30 40 50mm