

Stanwell

Stanwell New Projects Office
Switchyard Road,
Stanwell, QLD, 4702

25010 / cd Spec G / T1

Appendix G - Building Access System

Revision	Date	Description	Issued by
T1	11/03/2026	For Tender	JB

PRELIMINARY
NOT FOR CONSTRUCTION

Kattsafe

Height access
and fall protection

+61 3 8727 9000
design@Kattsafe.com.au
kattsafe.com.au

1029 Mountain Highway
Boronia Victoria 3155
Australia

PROJECT PROPOSAL

SWITCHYARD ROAD, STANWELL (QLD) – STANWELL NEW PROJECTS OFFICE

Project Reference No.
28079

Revision No.
EST94104

Date
16-Dec-25



Introduction

Project: **SWITCHYARD ROAD, STANWELL (QLD) – STANWELL NEW PROJECTS OFFICE**
Project Ref No: **28079**
Revision No: **EST94104**
Project Stage: **PLANNING STAGE**

Welcome to Kattsafe, thank you for the opportunity to present this proposal.

Our experienced design consultants work with you to design fully compliant, cost-effective height safety solutions. We take a collaborative approach to help you document the correct access and fall protection strategies customised to your project's needs.

We know the regulations

Our experts ensure all legal requirements are met with our project design, so you can have complete peace of mind.

We work with a network of approved installers to ensure fully compliant, fit-for-purpose solutions.

After sales care and service


Effective management, use and maintenance of any height access and fall protection system is essential to keeping personnel safe.

Our documentation and after-sales service ensures every step of a height access and fall protection system's lifecycle has been looked after.

World-class product design and manufacturing

Every Kattsafe component, product, and system is designed to the highest specification for complete confidence that people's lives will be protected.

All our components and products integrate seamlessly for modular systems that minimise rework.

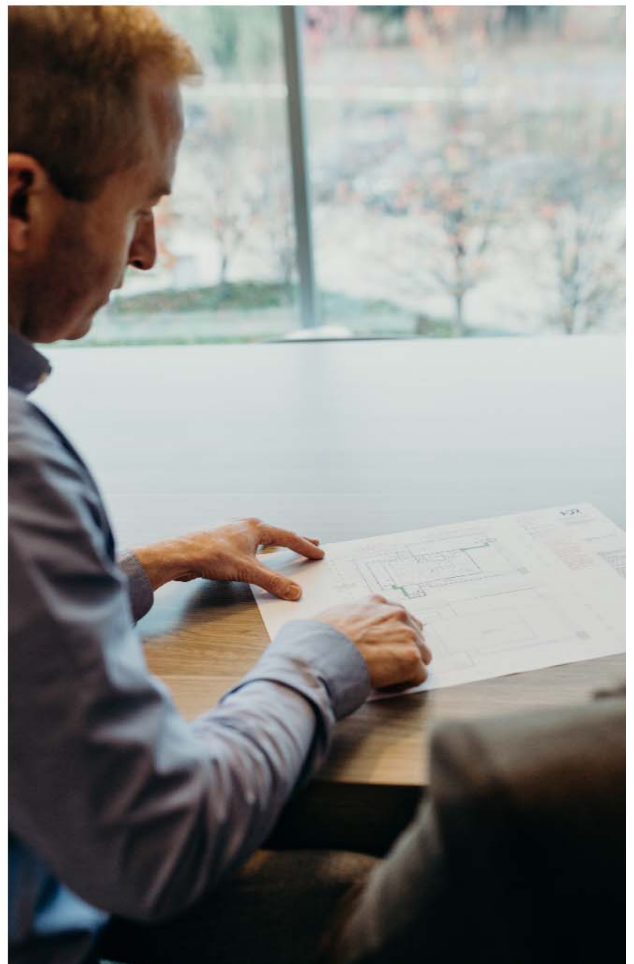

Regards,

Kattsafe Design Team

Rick Voss -Projects Co-ordinator
rick.voss@kattsafe.com.au

Michael Soth - Design Co-ordinator
design@kattsafe.com.au

Leng Kuoch - Estimating Co-ordinator
leng.kuoch@kattsafe.com.au

Scope Of Works

Project: **SWITCHYARD ROAD, STANWELL (QLD) – STANWELL NEW PROJECTS OFFICE**
 Project Ref No: **28079**
 Revision No: **EST94104**
 Project Stage: **PLANNING STAGE**

Qty	Code	Description	NO Prices
-----	------	-------------	-----------

MAIN BUILDING

1	AP115.1500	1.5m Anchor Point Strop with Quicklink
5	AP135A	Top Mount Fall Arrest Anchors
2	SL1.056 + SL223A	50.5m Top Mount Static Lines (1 x 90° Corner)
2	SL227	Horizontal Static Line Travellers
1	LD402	Portable Ladder Support Bracket
1	SD975	System Information Signboard

ACCESSORIES

2	HR040.15	Multipurpose Roofers Harness Kits (15m Rope Line)
1	HR048	Lockable Harness Equipment Cabinet (Large)

Design Criteria

Project: **SWITCHYARD ROAD, STANWELL (QLD) – STANWELL NEW PROJECTS OFFICE**
Project Ref No: **28079**
Revision No: **EST94104**
Project Stage: **PLANNING STAGE**

DESIGN REVISION

Date	Project Stage	Project Issued By:	Written	Drawn	System Design By:
04/12/2025	Planning	M3 Architecture		✓	Kattsafe Group
15/12/2025	Planning	M3 Architecture		✓	Kattsafe Group

DESIGN NOTES

- Based on current regulations, Kattsafe recommends fall protection to all fall edges.
- WORKSAFE classifies skylights as fall hazards, therefore the investment of skylight protectors is strongly recommended by KATTSafe GROUP.
- System Design has been based on criteria provided by the project coordinator. Any changes made to the system design must be authorised by Kattsafe prior to commencement of installation. Failure to do this may result in a non-compliant installation and possible litigation exposure.
- Any changes made to the system design must be authorised by Kattsafe prior to commencement of installation. Failure to do this may result in a non-compliant installation and possible litigation exposure.

This Scope of Works is based on:

System design request form based on Drawing No: A-200002 Rev. 8

Methods of Access & Fall Protection is based on the following:

- ACCESS - Portable ladder using a ladder support bracket
- FALL PROTECTION - To all fall edges

AUSTRALIAN STANDARDS

Installation of proprietary Access & Fall Protection equipment must comply with the following:

AS/NZS5532:2013 Manufacturing requirements for single point anchor point used for harness based work at height
AS/NZS1891.1:2009 Industrial fall arrest systems and devices/harnesses and ancillary equipment
AS/NZS1891.2:2001 Industrial fall arrest systems and devices/horizontal lifeline and rail systems
AS/NZS1891.3:1997 Industrial fall arrest systems and devices/fall arrest devices
AS/NZS1891.4:2009 Industrial fall arrest systems and devices/selection, use and maintenance
AS1657:2018 Fixed platforms, walkways, stairways and ladders/design, construction, installation

Project Notes

Project:	SWITCHYARD ROAD, STANWELL (QLD) – STANWELL NEW PROJECTS OFFICE
Project Ref No:	28079
Revision No:	EST94104
Project Stage:	PLANNING STAGE

Installation Notes

- Pricing for installation of equipment defined in this proposal must be confirmed with a recommended Kattsafe Installer.
- Installation of Roof Access, Fall Protection and Abseil Systems must be carried out by a recommended Kattsafe Installer who is competent and conversant with the relevant Australian Standards and Compliance Codes.
- Exact component locations, support structure integrity, suitability for use and the fixing method must be assessed and approved by a competent person prior to commencement of installation.
- Elevated work platforms or crange may be required for safe installation of the system.

Certification Notes


- On completion of installation, certification must be carried out by an recommended **Kattsafe Installer** in accordance with Kattsafe's installation guidelines.
- A System Handover Manual must be provided on completion of installation of Roof Access, Fall Protection and Abseil Systems. This manual will include the following:
 - Product Specifications
 - As-built layout plan
 - Installation Certification
 - System Operating Instructions
 - Annual Recertification Schedule
 - Product Warranties
 - Product Certificate
 - Working at heights management template

Safe Use and Maintenance Notes

- Fall Arrest systems and equipment must only be operated by competent persons trained to use and maintain fall arrest equipment.
- All Fall Arrest and Abseil equipment requires periodical maintenance by a competent person in accordance with Kattsafe's specifications and the requirement of Australian Standard AS/NZS1891.4.2009 (Section 9), and AS/NZS4488.
- If you are unsure or require help regarding this proposal, you can contact our help line on **1300 301 755** or EMAIL **info@kattsafe.com.au**
- Any attempt to change the design during installation renders both our compliance and responsibility null and void. The person who authorises any changes holds himself responsible for all actions and decisions made.

Project Co-ordinators:	Architect:	M3 ARCHITECTURE
	Tel No:	07 3831 4644

2/11/2025 4:12:23 PM C:\Projects\STANWELL\Building\BPC-CentralFile_BromieG.rvt

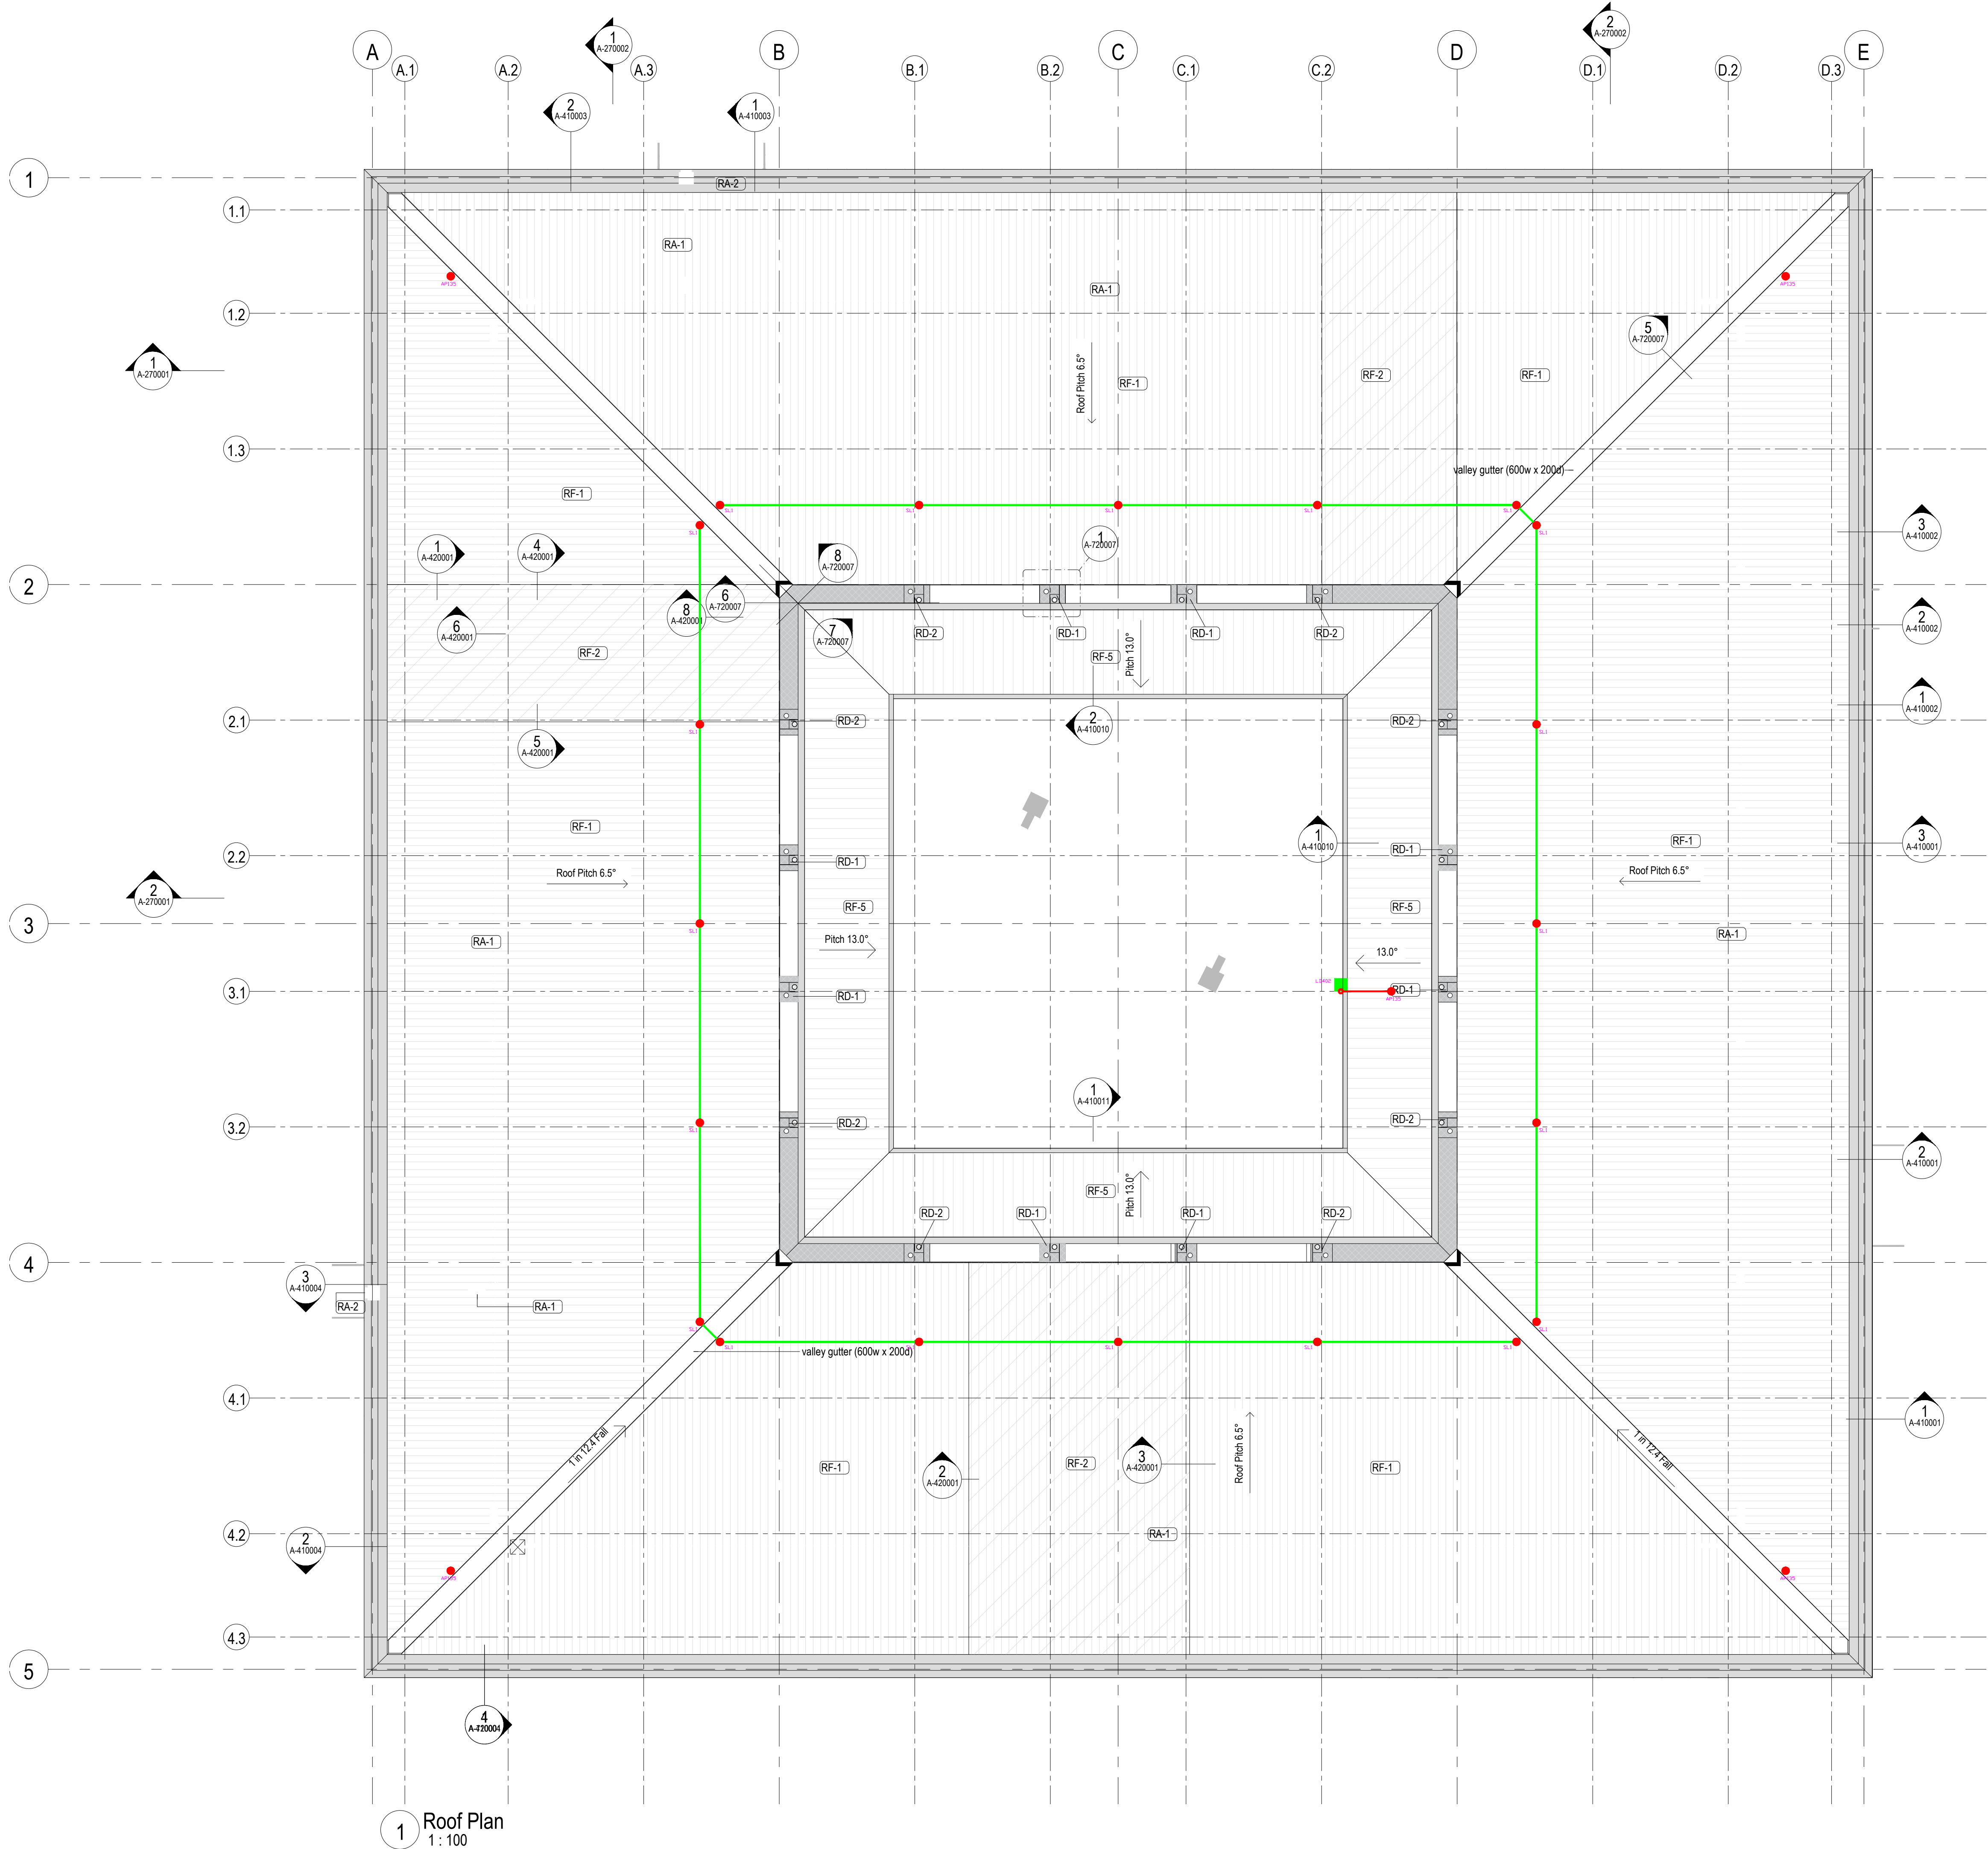

1 Roof Plan
1 : 100

ROOF NOTES

- | rev | date | description | initial |
|-------|--------------|---|---------|
| RN.01 | 1 17/06/25 | QS Issue #1 | |
| | 2 08/07/2025 | Background Issue | |
| RN.02 | 3 11/08/2025 | Coordination Issue | JB |
| | 4 29/08/2025 | Coordination Issue | JB |
| | 5 08/09/2025 | QS Issue | JB |
| | 6 19/09/2025 | 100% CD Issue | JB |
| | 7 27/10/2025 | 50% CD Issue | JB |
| | 8 21/11/2025 | CD Coordination Issue | JB |
| RN.03 | | Design, construct & install all flashings, cappings etc to make roof weatherproof | |
| RN.04 | | Trusses shown are indicative only. Actual sizes, configurations & spacings to be designed and certified by the truss supplier. Refer to structural documents for design parameters. | |
| RN.05 | | Refer also to Mechanical and Hydraulic Services documents for roof penetrations. | |

ROOF LEGEND

box gutter sump - refer to hydraulic docs for performance based brief

KATTSafe LAYOUT LEGEND

- Anchor Strop
- Fall Arrest Anchor
- Static Line System
- Ladder Support Bracket

PROJ REF NO: 28079.ES794104 DATE: 15/12/2025

PRELIMINARY
NOT FOR CONSTRUCTION

Drawings include colour information. A black & white copy may not have all the information. This background is coloured blue.

brian hooperarchitect

ph: +61 7 3831 4644
11 saint james street petrie tce q 4000
info@m3architecture.com
www.m3architecture.com

client: _____

project: Stanwell New Projects Office
Switchyard Road,
Stanwell, QLD, 4702

title: Roof Plan

drawn: bg

checked: jb

date: Nov 2025

scale: 1 : 100 at A1

drawing: 25010 / cd A-200002 / 8

copyright ©

These designs, plans, specifications and the copyright herein are the property of the architect and must not be used, reproduced, or copied wholly or in part without the written permission of m3architecture Pty Ltd abn 23 079 044 545. Use figured dimensions in preference to scale. If there are any questions contact the architect.

1:100 at A1
0 1 2 3 4 5m