


3 x OFFICE REFURBISHMENTS, 1 x NEW BUILD

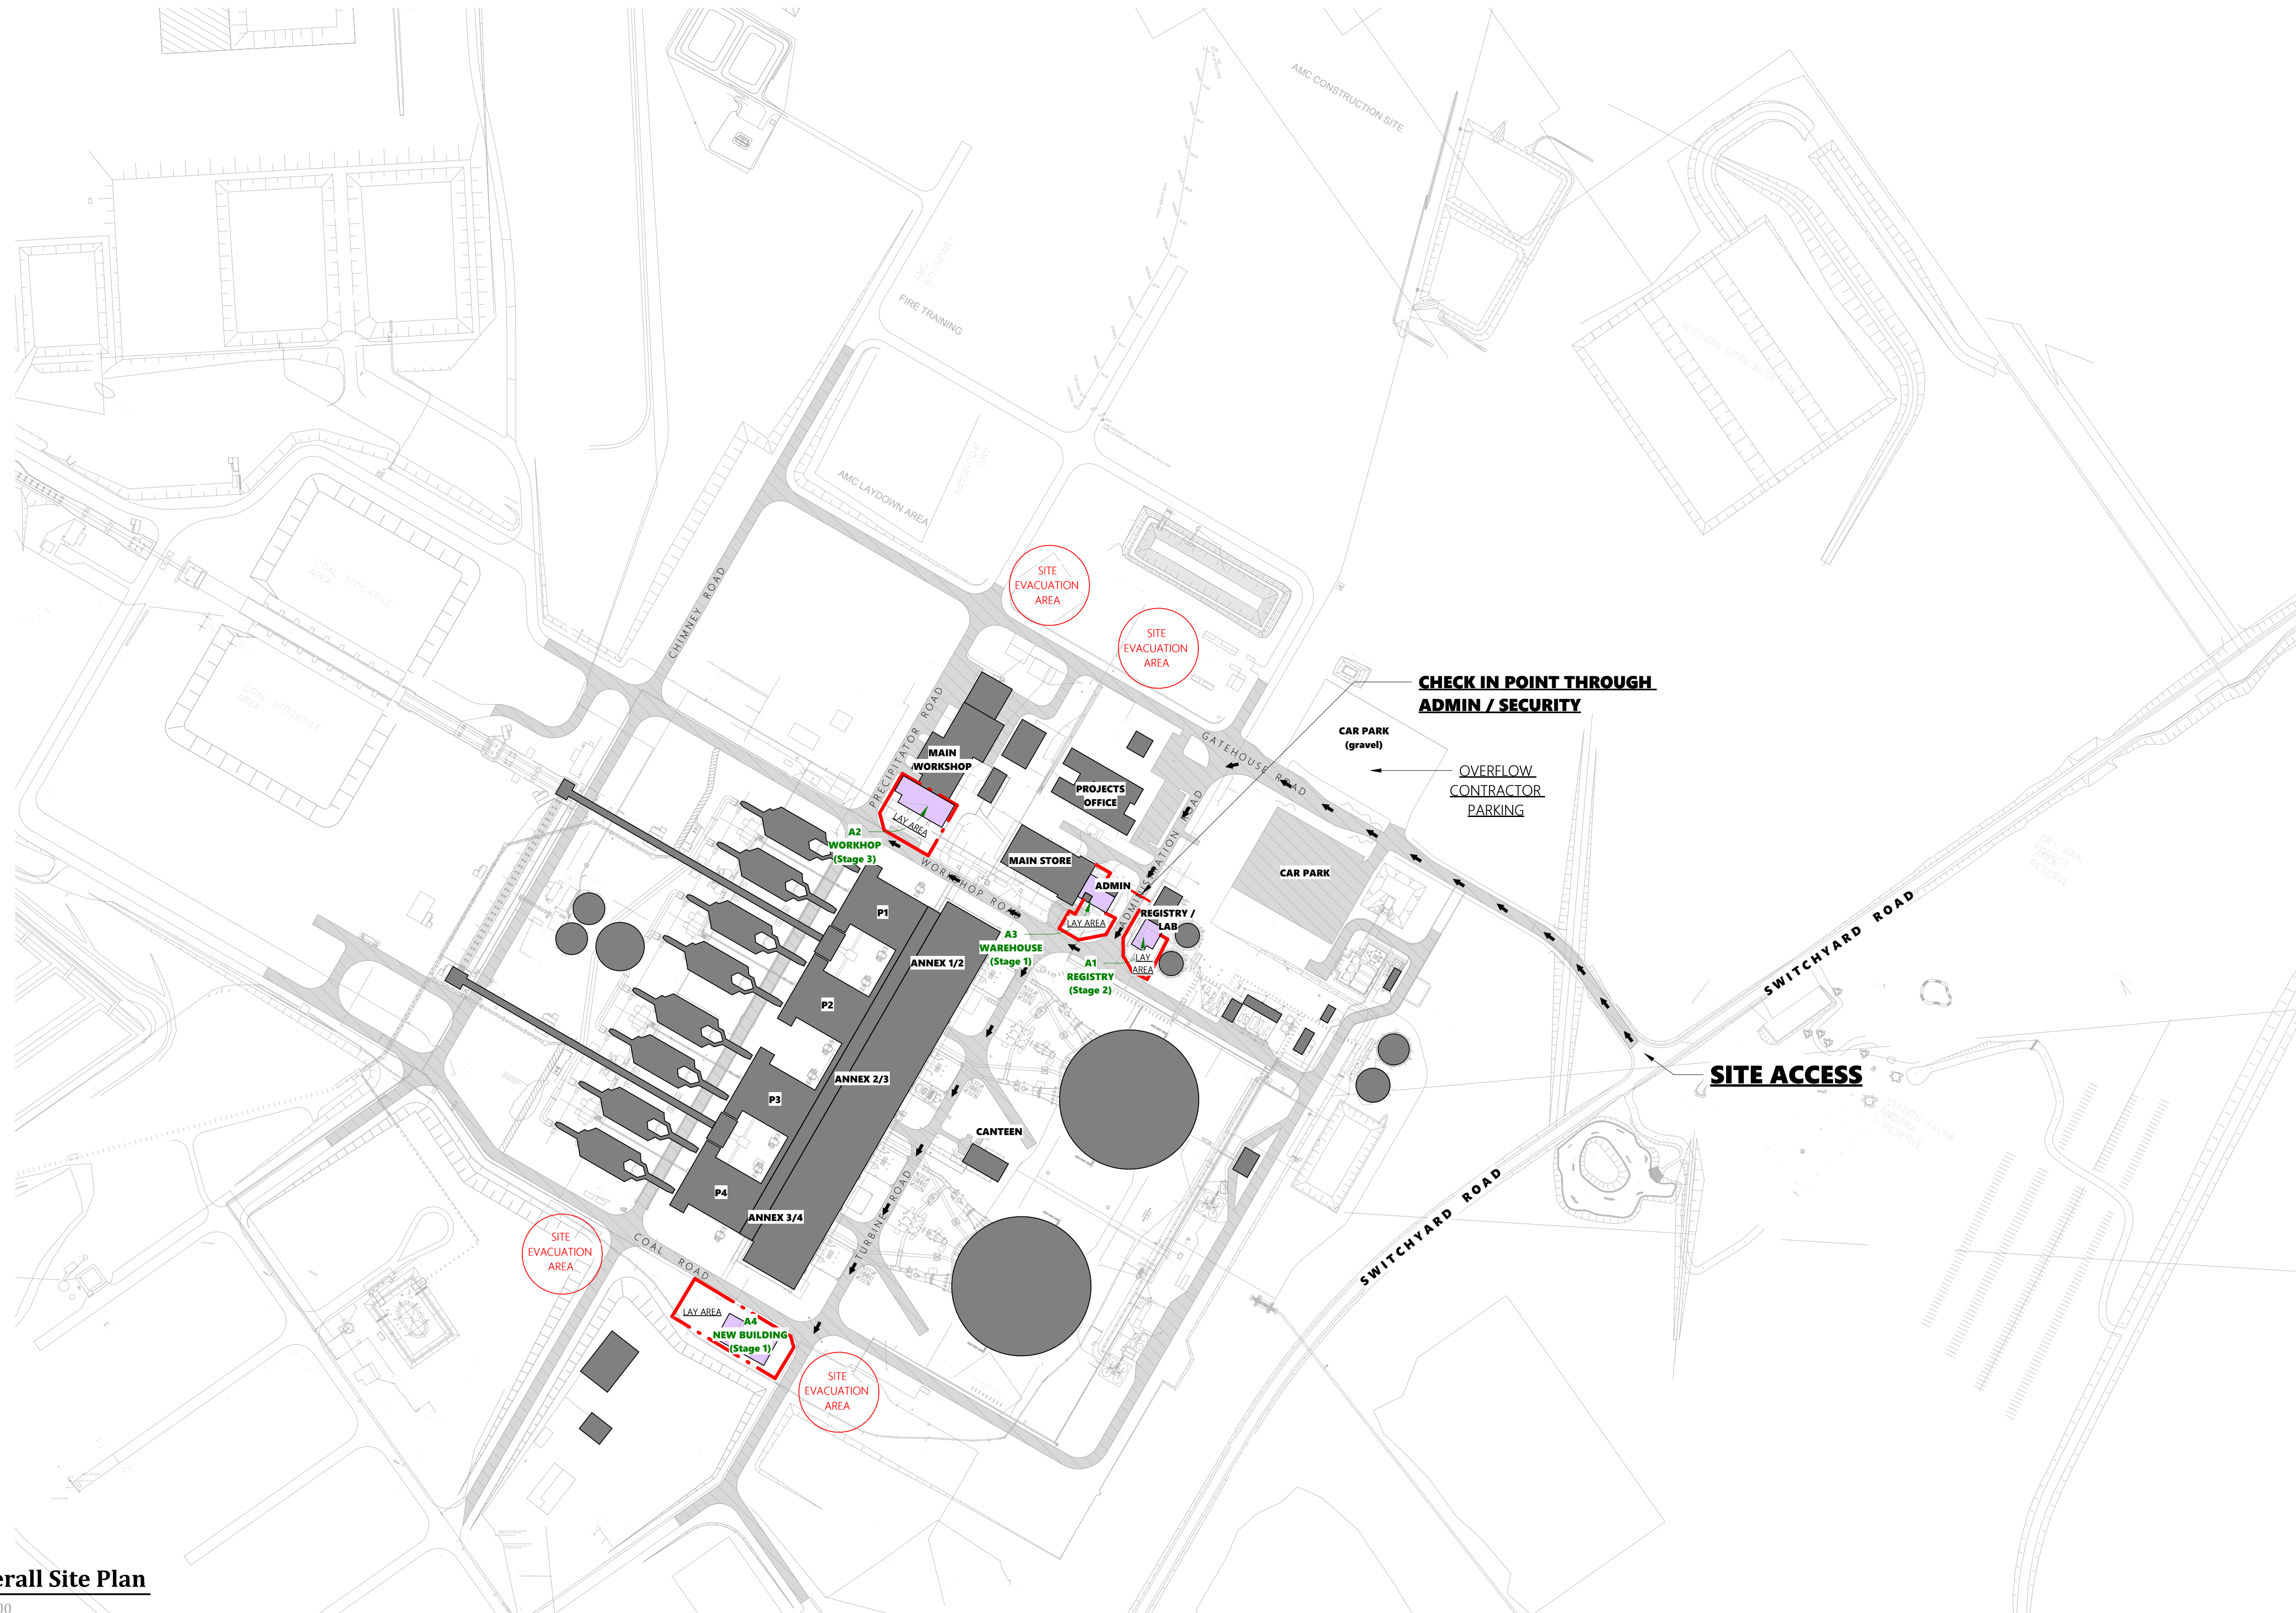

1 : 2500

STAGE 1 -
A3 WAREHOUSE
A4 NEW BUILD

STAGE 2 -
A1 - REGISTRY

STAGE 3 -
A2 WORKSHOP

Project No: **25_003** Drawing No: **A0-000**

DO NOT SCALE THIS DRAWINGS

Service Legend

Electrical Line

Industrial Waste

Gas

Sewer

Stormwater

Comms

Water

Fire Hydrant

Eu

IW

G

S

SW

C

W

HYD

Exp

W

G

S

SW

C

W

HYD

ALL SERVICE LINES SHOWN ON THE PLAN ARE APPROXIMATE LOCATIONS. CONTRACTOR TO LOCATE ALL SERVICES ON SITE PRIOR TO COMMENCING WORKS.

THE CONTRACTOR SHALL ENSURE THAT AT ALL TIMES SERVICES TO ALL SURROUNDING BUILDINGS ARE NOT AFFECTED BY THE WORKS.

CAP VAC AREAS TO IDENTIFY LOCATION OF SERVICES

TENDER ISSUE

Client

stanwell

Project Details

NEW OFFICE, REFURB PROJECT

Address

SWITCHYARD ROAD, STANWELL, 4702

Drawing Title

A1 - REGISTRY - EXISTING & PROPOSED SITE PLAN

dezi

nelements

BUILDING DESIGNERS

0483 988 655 M

info@dezi nelements.com.au E

QBCC No: 1247120 BDAQ No: 0001677

Scale: 1 : 100

Date: MARCH 2026

Drawn: NJB

Rev:

T1

Project No:

Drawing No:

25_003 A0-001

These drawings, designs and the Copyright thereof are the property of Design Group Qld Pty Ltd (T/A Design Elements) and are not to be used, retained or copied by either physical or electronic means without the written permission of Nathan Burke (Director). Conditions stated in the terms and conditions. Design Elements accepts no responsibility for the completeness, accuracy or compatibility of electronically transferred documents.

REVISIONS		
Rev	Description	Date
T1	TENDER ISSUE	19.03.2026

DO NOT SCALE THIS DRAWINGS

SERVICE LEGEND

Eu

Eu

Electrical Line

W

W

Industrial Waste

G

G

Gas

S

S

Sewer

SW

SW

Stormwater

C

C

Comms

W

W

Water

HYD


HYD

Fire Hydrant

ALL SERVICE LINES SHOWN ON THE PLAN ARE APPROXIMATE LOCATIONS. CONTRACTOR TO LOCATE ALL SERVICES ON SITE PRIOR TO COMMENCING WORKS.

THE CONTRACTOR SHALL ENSURE THAT AT ALL TIMES SERVICES TO ALL SURROUNDING BUILDINGS ARE NOT AFFECTED BY THE WORKS.

CAP VAC AREAS TO IDENTIFY LOCATION OF SERVICES

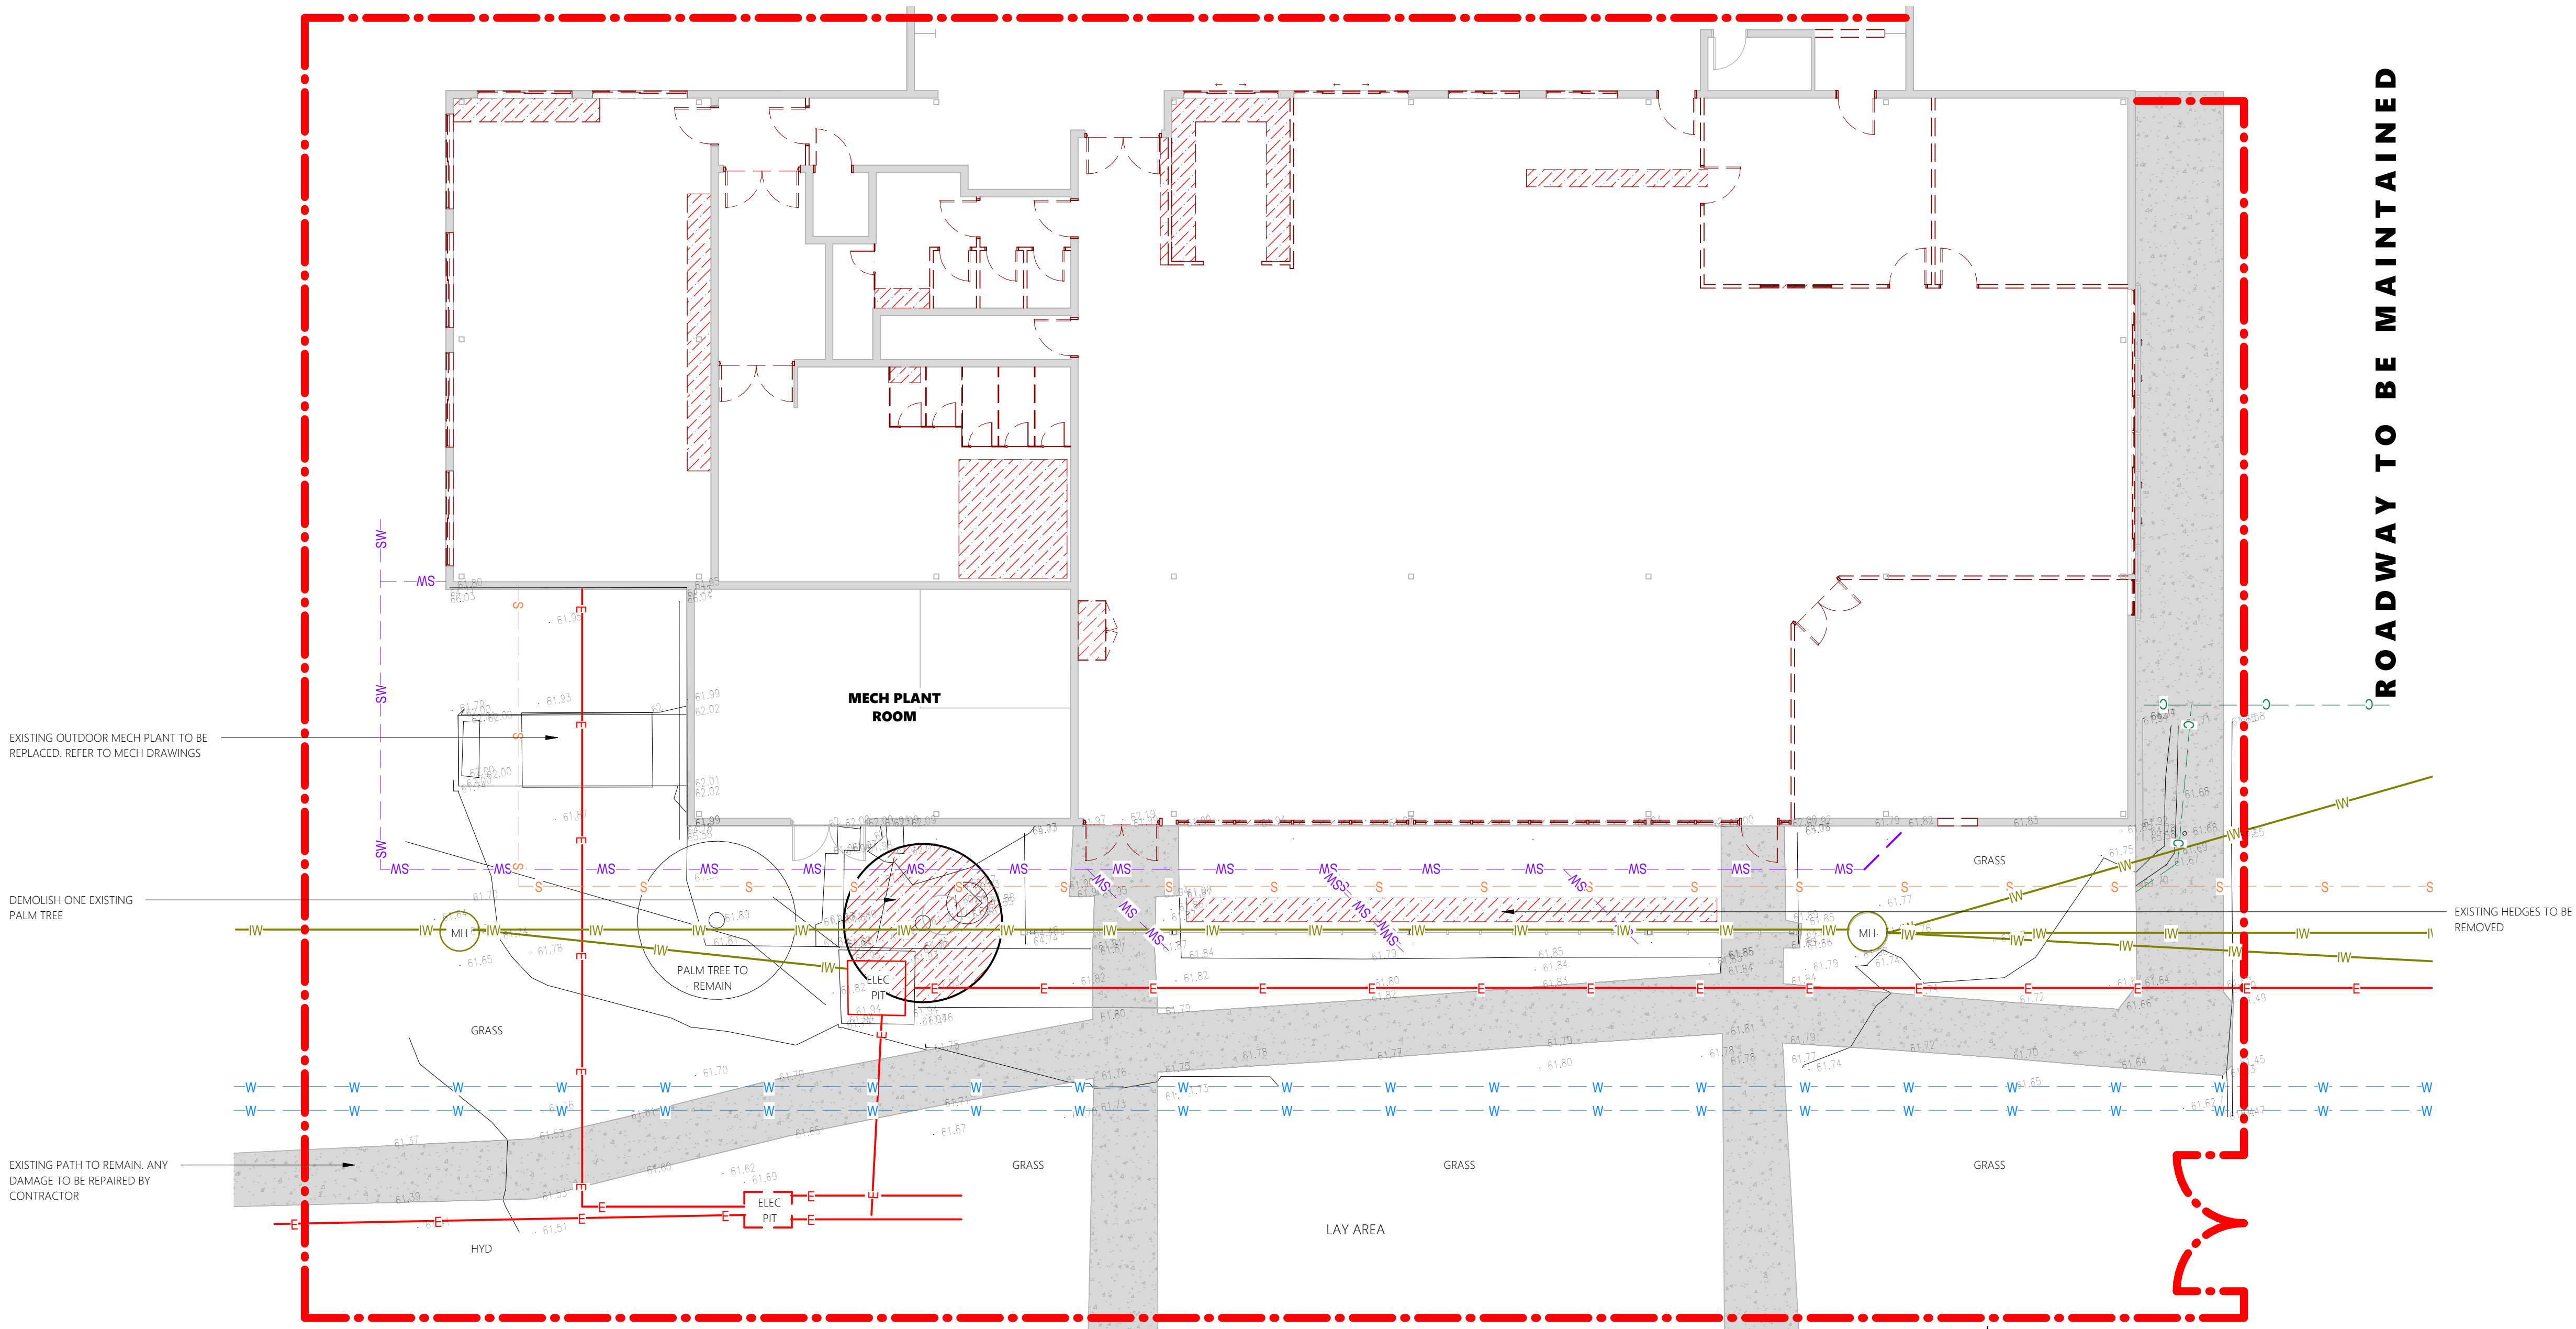

TENDER ISSUE

Client

Project Details

NEW OFFICE, REFURB PROJECT

Address

**SWITCHYARD ROAD,
STANWELL, 4702**

Drawing Title

**A2 - WORKSHOP -
EXISTING SITE PLAN**

dezi elements
BUILDING DESIGNERS

0483 988 655

info@dezi elements.com.au

QBCC No: 1247120 BDAQ No: 0001677

Scale: 1 : 100 Rev: **T1**

Date: MARCH 2026

Drawn: NJB

Project No: Drawing No:

25_003 A0-002

19/03/2026 11:52:17 AM

A2 - WORKSHOP Existing Site

1 : 100

REVISIONS		
Rev	Description	Date
T1	TENDER ISSUE	19.03.2026

DO NOT SCALE THIS DRAWINGS

SERVICE LEGEND

---Eu---

---W---

---G---

---S---

---SW---

---C---

---W---

---HYD---

Electrical Line

Industrial Waste

Gas

Sewer

Stormwater

Comms


Water

Fire Hydrant

ALL SERVICE LINES SHOWN ON THE PLAN ARE APPROXIMATE LOCATIONS. CONTRACTOR TO LOCATE ALL SERVICES ON SITE PRIOR TO COMMENCING WORKS.

THE CONTRACTOR SHALL ENSURE THAT AT ALL TIMES SERVICES TO ALL SURROUNDING BUILDINGS ARE NOT AFFECTED BY THE WORKS.

CAP VAC AREAS TO IDENTIFY LOCATION OF SERVICES

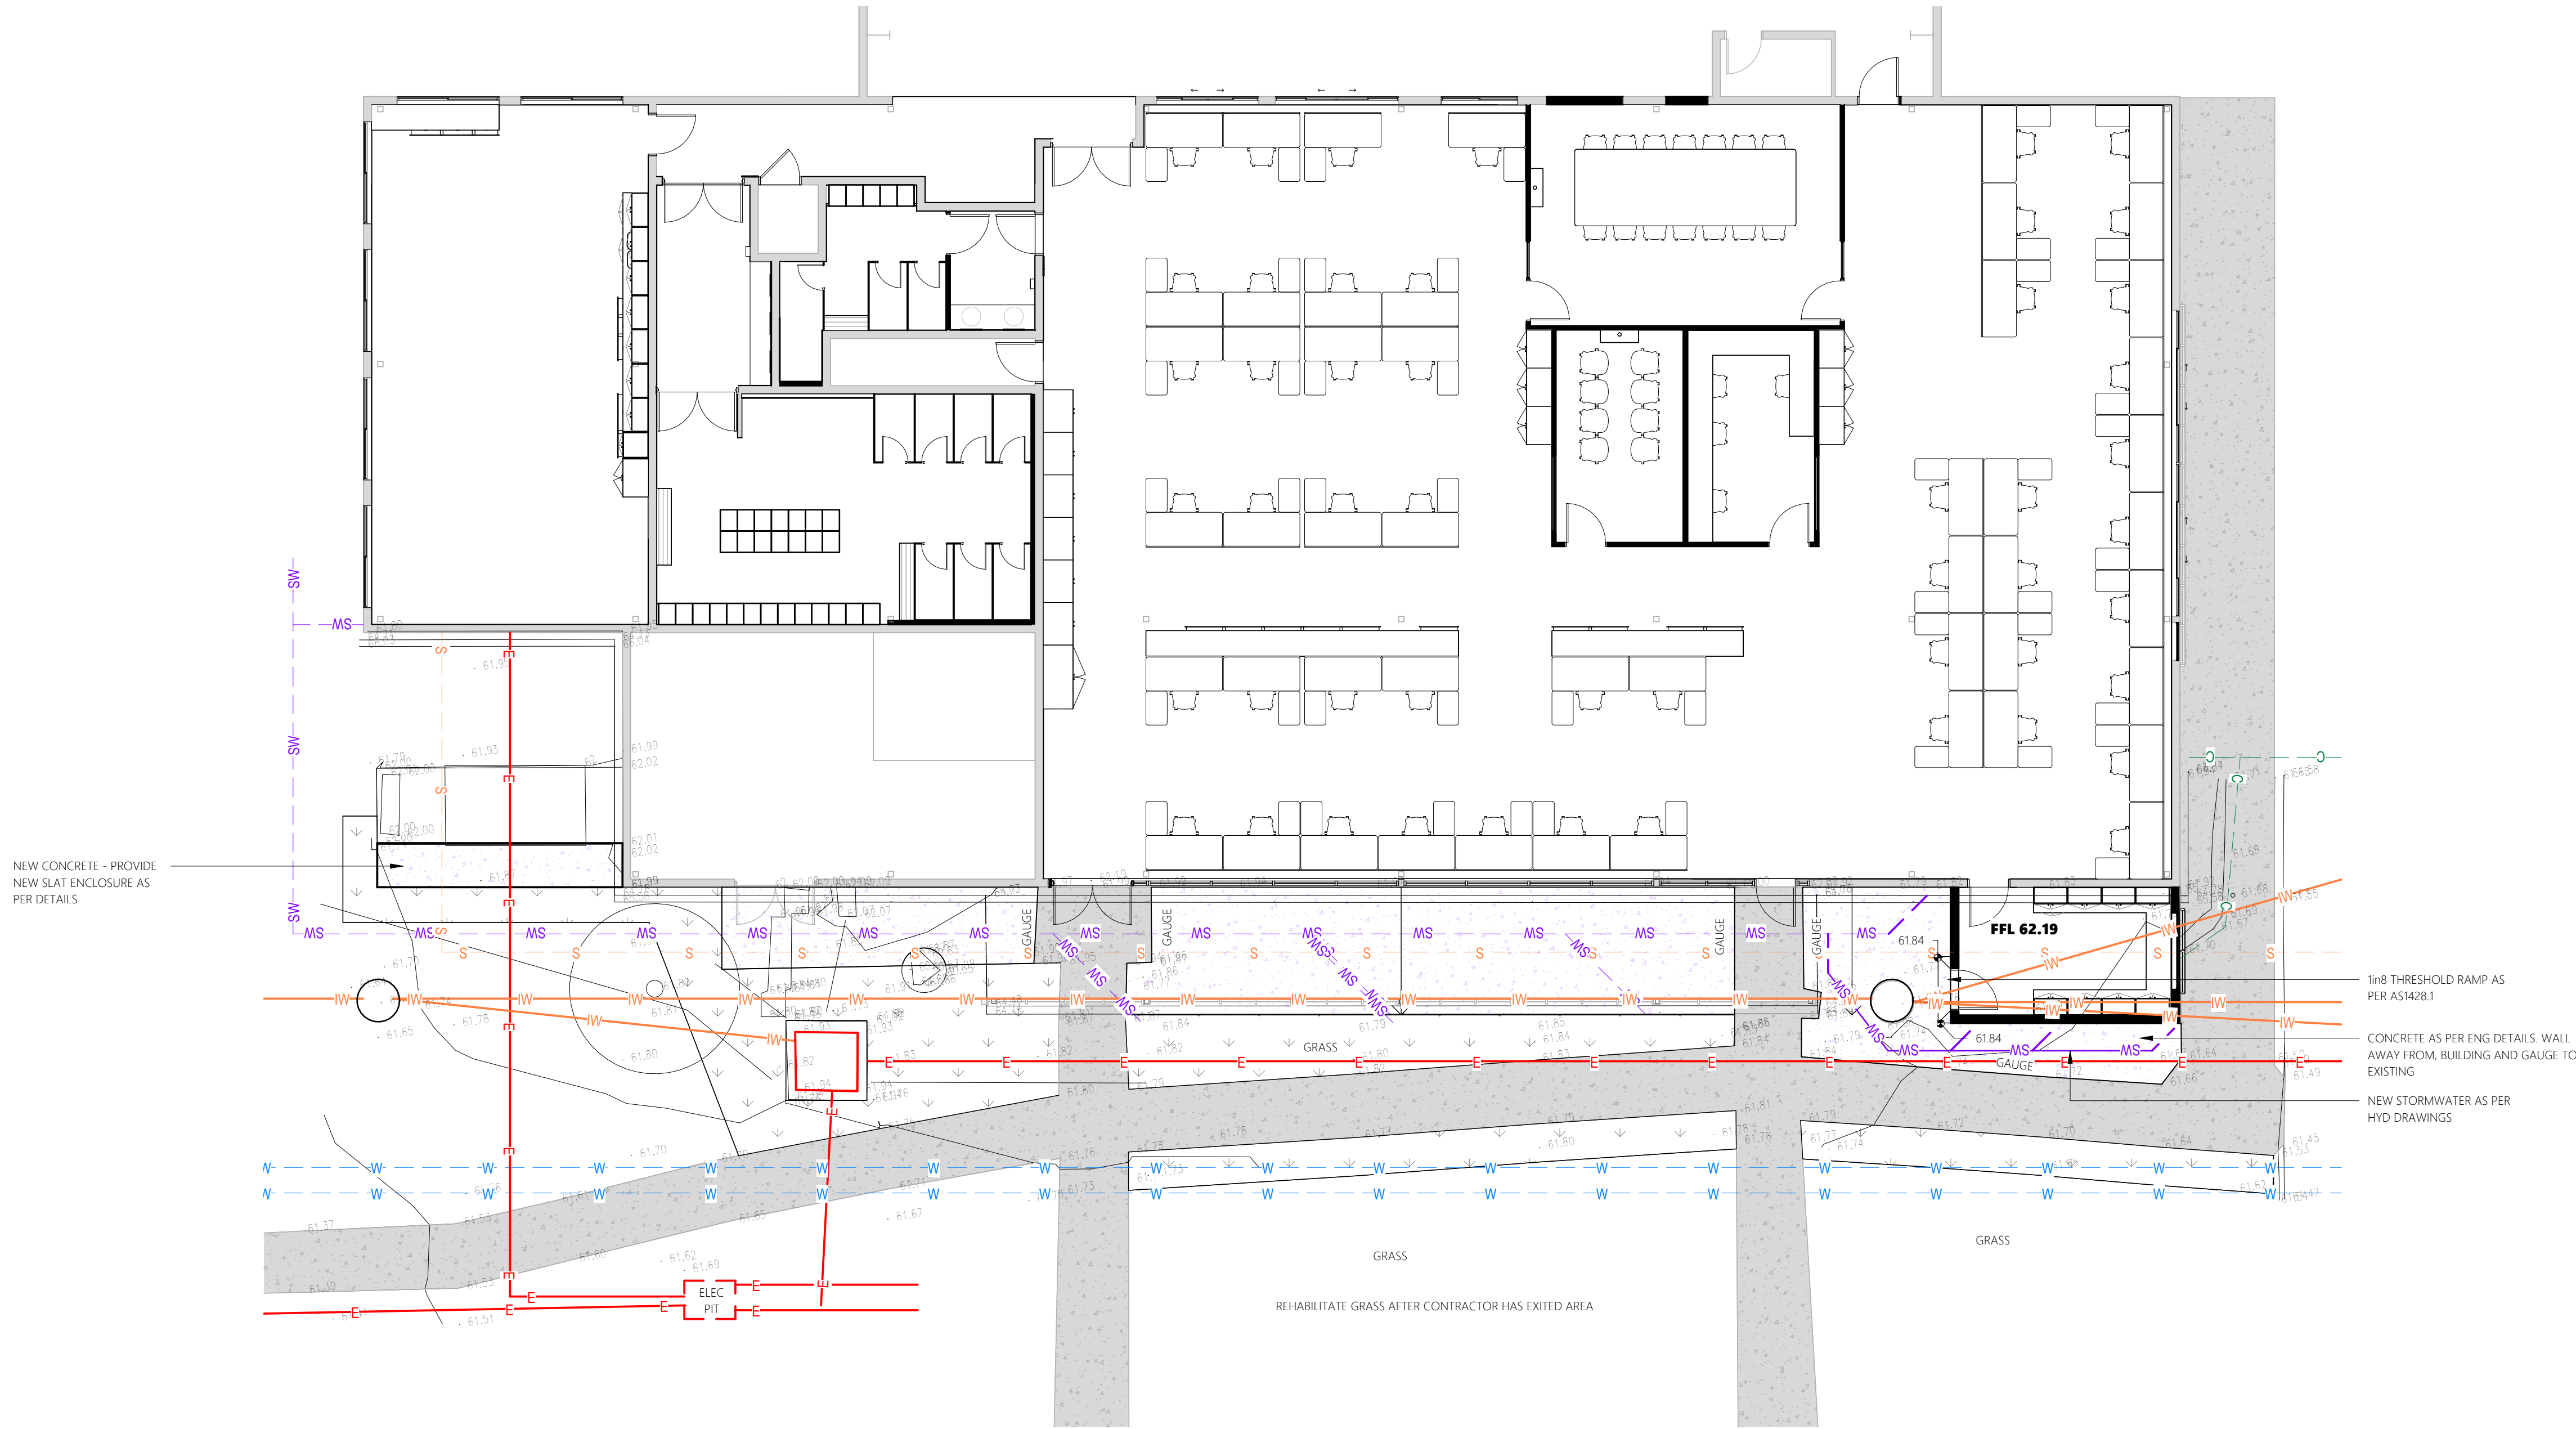

EXTENT OF CONTRACTORS SITE AREA. PROVIDE TEMPORARY FENCING TO WORKPLACE HEALTH AND SAFETY REQUIREMENTS AND MAINTAIN DURING CONTRACT PERIOD.

EXISTING GARDEN TO REMAIN. TO BE RE MULCHED AT END OF CONSTRUCTION WORKS. ANY DAMAGED TO GARDEN EDGING TO BE REPAIRED BY CONTRACTOR

TREE TO BE REMOVED FOR CONSTRUCTION WORKS

CLOSE ACCESS TO BUILDING

ACCESS TO FIRST AID TO BE MAINTAINED AT ALL TIMES, PARKING SPACES AVAILABLE FOR FIRST AID ONLY

ANY BITUMEN / KERBING DAMAGE TO BE REPAIRED

ACCESS TO FIRST AID TO BE MAINTAINED

RECEPTION / SECURITY

FIRST AID

MECH PLANT

EXISTING BITUMEN CARPARK

ELEC PIT

ANY DAMAGE TO CONCRETE PATHS TO BE REPAIRED BY CONTRACTOR

REHABILITATE GRASS AFTER CONTRACTOR HAS EXITED AREA

EXTENT OF CONTRACTORS SITE AREA. PROVIDE TEMPORARY FENCING TO WORKPLACE HEALTH AND SAFETY REQUIREMENTS AND MAINTAIN DURING CONTRACT PERIOD.

EXTENT OF CONTRACTORS SITE AREA. PROVIDE TEMPORARY FENCING TO WORKPLACE HEALTH AND SAFETY REQUIREMENTS AND MAINTAIN DURING CONTRACT PERIOD.

REVISIONS

Rev	Description	Date
T1	TENDER ISSUE	19.03.2026

DO NOT SCALE THIS DRAWINGS

SERVICE LEGEND

---E---E---	Electrical Line
---W---W---	Industrial Waste
---G---G---	Gas
---S---S---	Sewer
---SW---SW---	Stormwater
---C---C---	Comms
---W---W---	Water
---HYD---HYD---	Fire Hydrant

ALL SERVICE LINES SHOWN ON THE PLAN ARE APPROXIMATE LOCATIONS. CONTRACTOR TO LOCATE ALL SERVICES ON SITE PRIOR TO COMMENCING WORKS.

THE CONTRACTOR SHALL ENSURE THAT AT ALL TIMES SERVICES TO ALL SURROUNDING BUILDINGS ARE NOT AFFECTED BY THE WORKS.

CAP VAC AREAS TO IDENTIFY LOCATION OF SERVICES

TENDER ISSUE

Client



Project Details

NEW OFFICE, REFURB PROJECT

Address

SWITCHYARD ROAD, STANWELL, 4702

Drawing Title

A3 - WAREHOUSE - EXISTING & PROPOSED SITE PLAN



0483 988 655 M

info@designelements.com.au E

QBCC No: 1247120 BDAQ No: 0001677

Scale: 1 : 100

Date: MARCH 2026

Drawn: NJB


Project No:

25_003

Drawing No:

A0-004

19/03/2026 11:52:33 AM

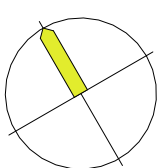

A3 - WAREHOUSE Existing Site

1 : 100

REVISIONS		
Rev	Description	Date
T1	TENDER ISSUE	19.03.2026

DO NOT SCALE THIS DRAWINGS

SERVICE LEGEND

- Electrical Line
- Industrial Waste
- Gas
- Sewer
- Stormwater
- Comms
- Water
- Fire Hydrant

ALL SERVICE LINES SHOWN ON THE PLAN ARE APPROXIMATE LOCATIONS. CONTRACTOR TO LOCATE ALL SERVICES ON SITE PRIOR TO COMMENCING WORKS.

THE CONTRACTOR SHALL ENSURE THAT AT ALL TIMES SERVICES TO ALL SURROUNDING BUILDINGS ARE NOT AFFECTED BY THE WORKS.

CAP VAC AREAS TO IDENTIFY LOCATION OF SERVICES

TENDER ISSUE

Client



Project Details

NEW OFFICE, REFURB PROJECT

Address

SWITCHYARD ROAD, STANWELL, 4702



Drawing Title

A3 - WAREHOUSE - PROPOSED SITE PLAN




0483 988 655 
info@dezi nelements.com.au 
QBCC No: 1247120 BDAQ No: 0001677

Scale: 1 : 100 Rev: **T1**
Date: MARCH 2026
Drawn: NJB
Project No: Drawing No:
25_003 A0-005

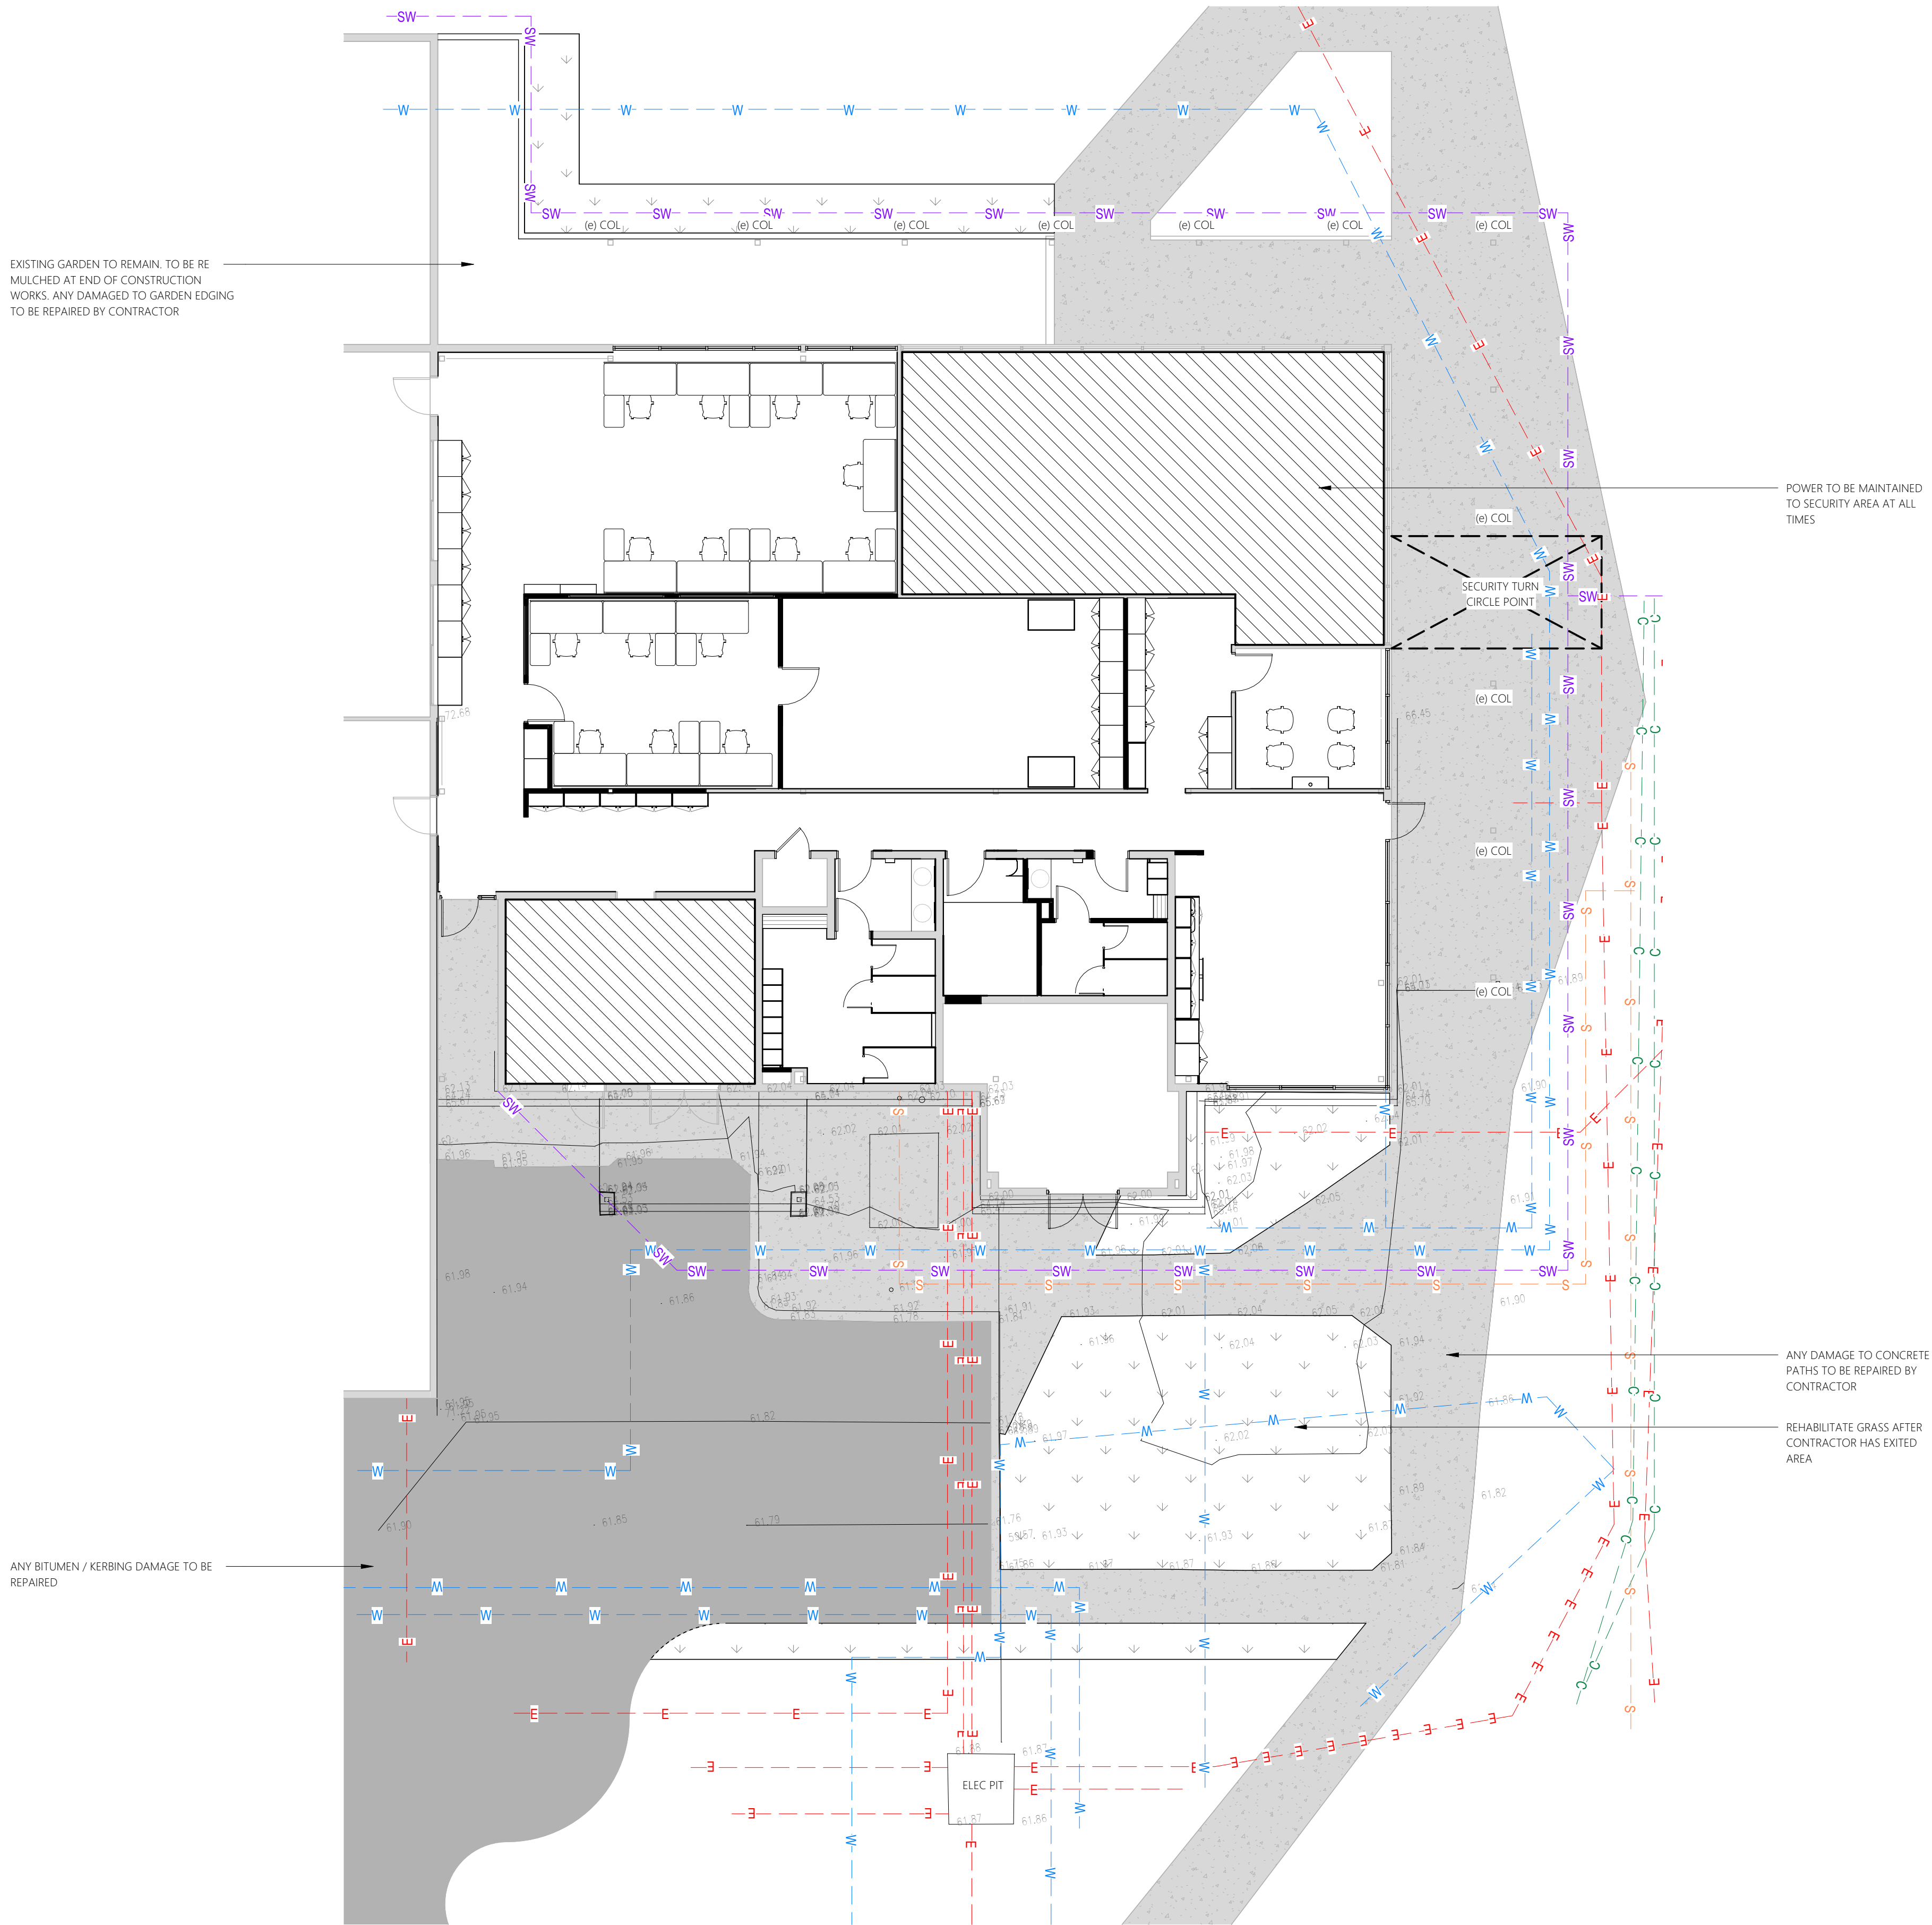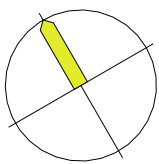

A3 - WAREHOUSE Proposed Site

1 : 100

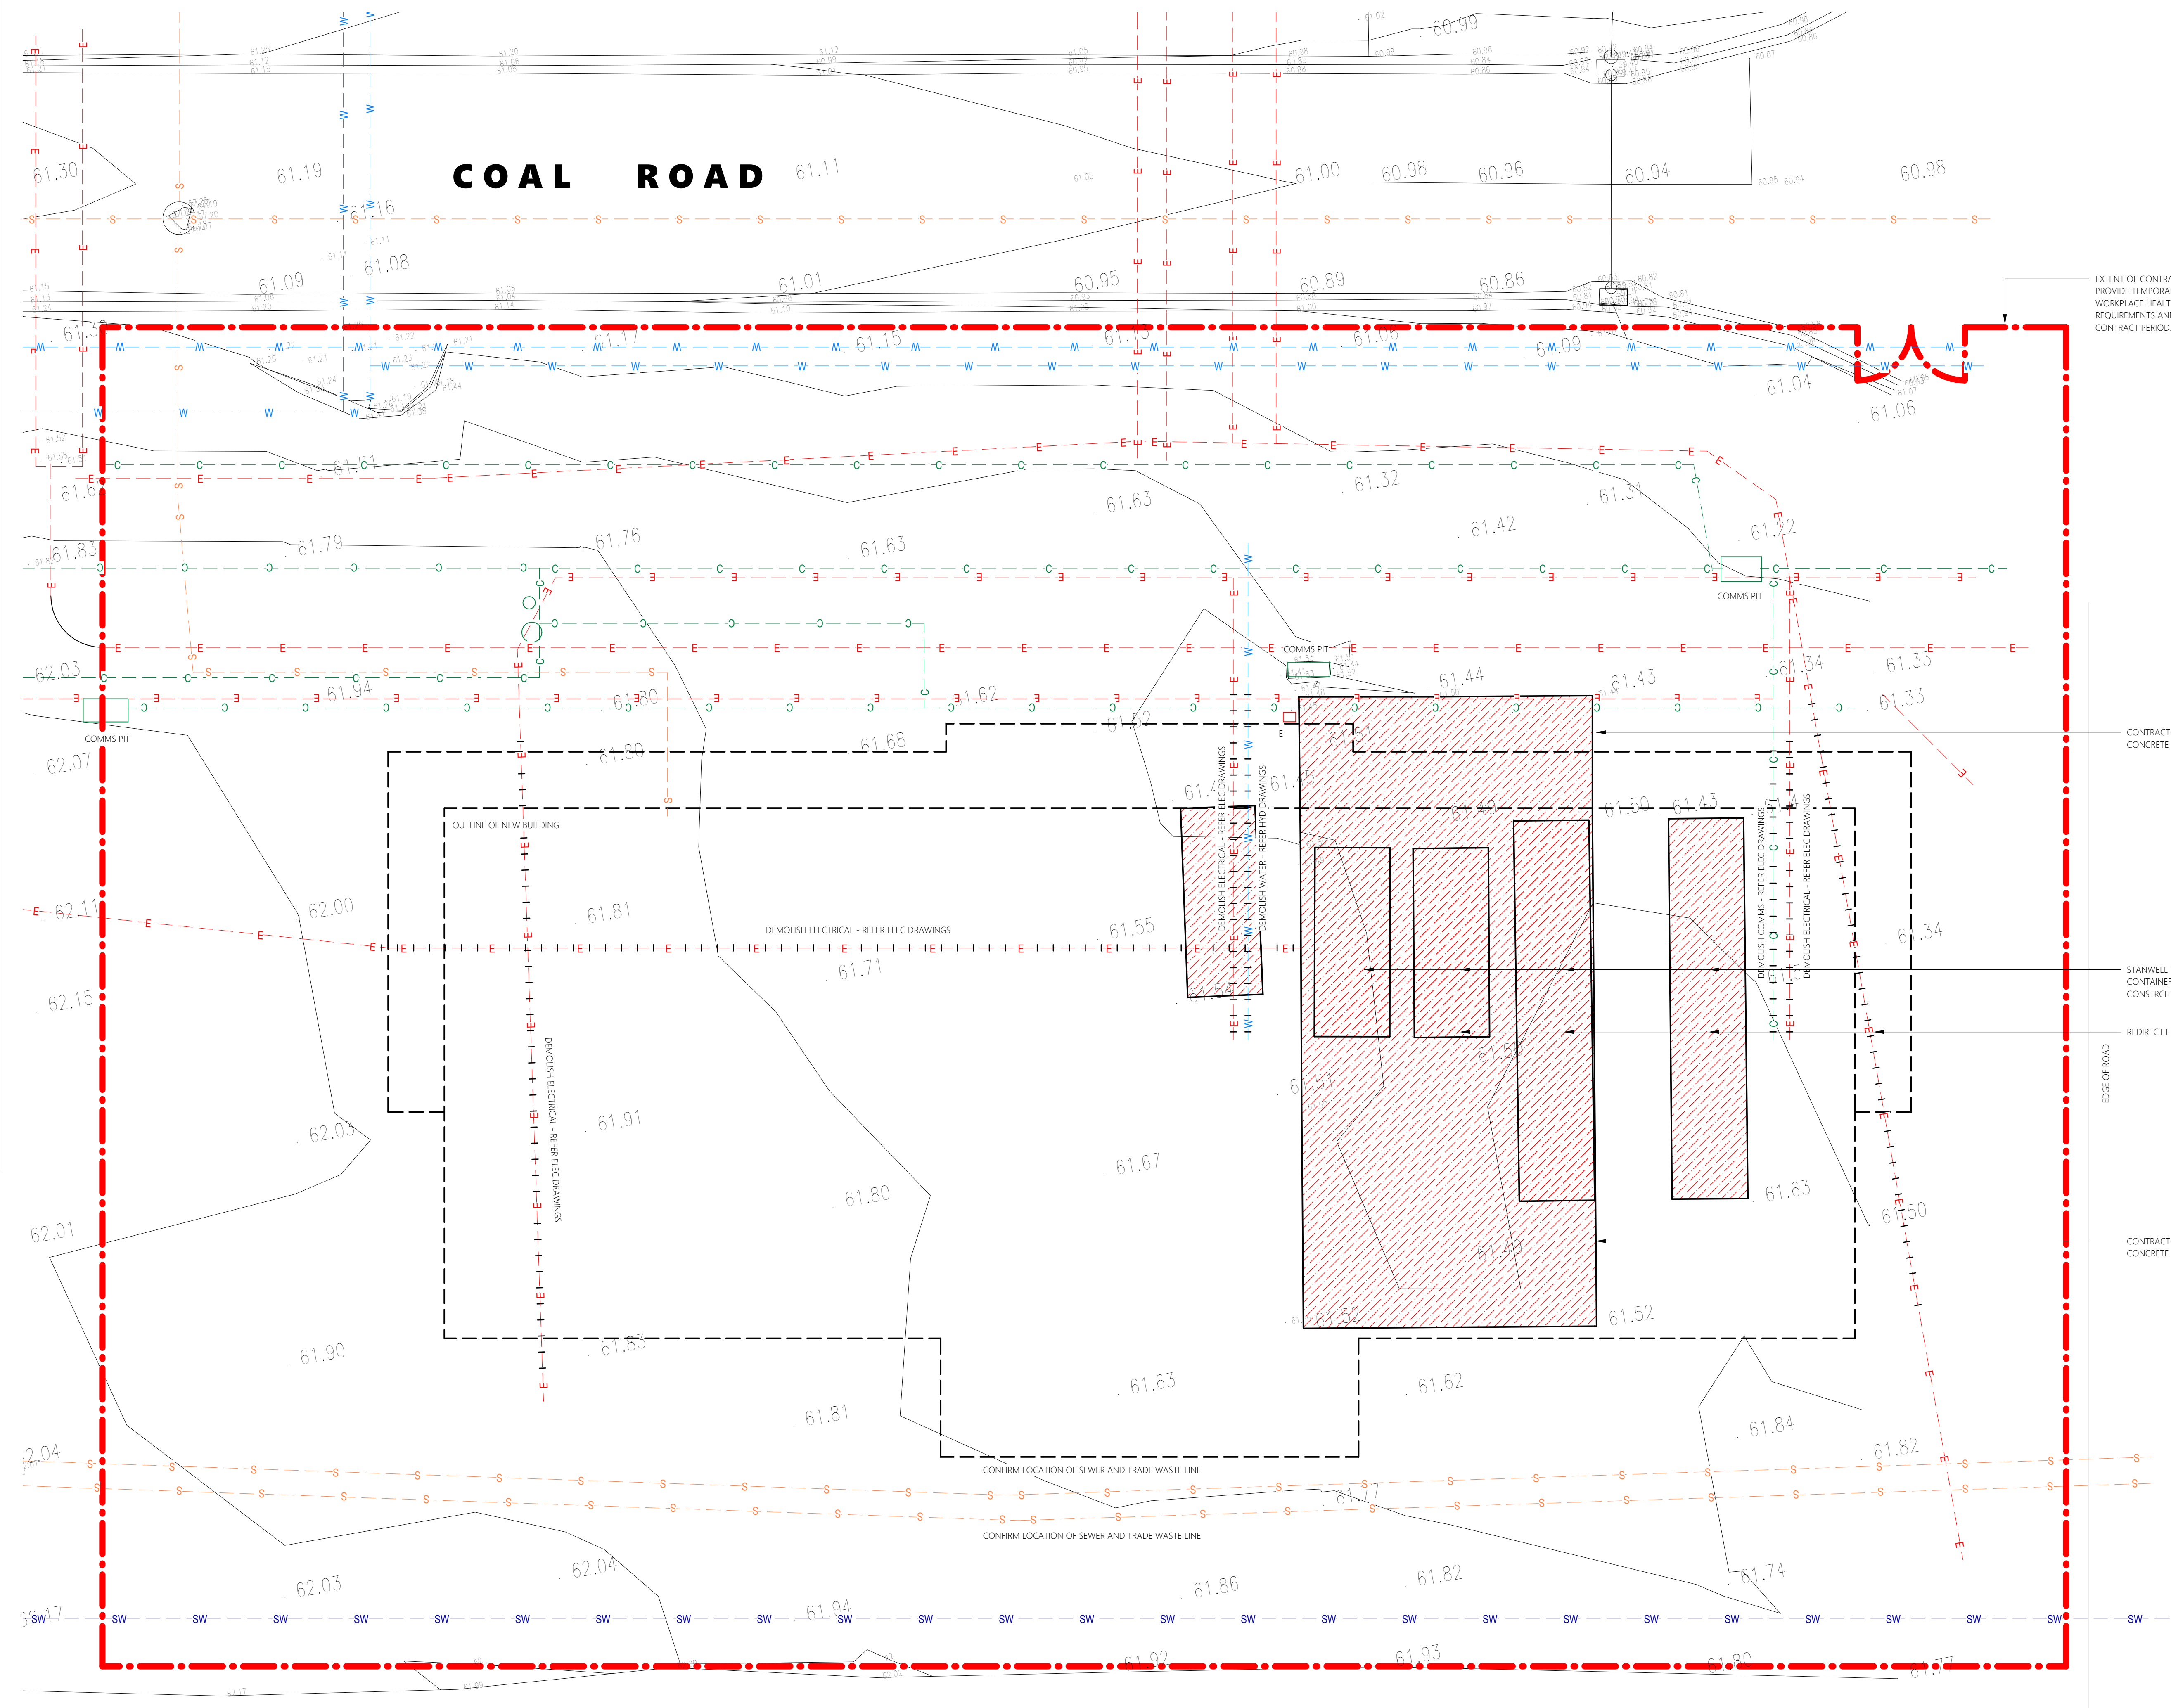

A4 - NEW BUILD - Existing Site

1:100

REVISIONS		
Rev	Description	Date
T1	TENDER ISSUE	19.03.2026

DO NOT SCALE THIS DRAWINGS

SERVICE LEGEND

---Eu---	Electrical Line
---IW---	Industrial Waste
---G---	Gas
---S---	Sewer
---SW---	Stormwater
---C---	Comms
---W---	Water
---HYD---	Fire Hydrant

ALL SERVICE LINES SHOWN ON THE PLAN ARE APPROXIMATE LOCATIONS. CONTRACTOR TO LOCATE ALL SERVICES ON SITE PRIOR TO COMMENCING WORKS.

THE CONTRACTOR SHALL ENSURE THAT AT ALL TIMES SERVICES TO ALL SURROUNDING BUILDINGS ARE NOT AFFECTED BY THE WORKS.

CAP VAC AREAS TO IDENTIFY LOCATION OF SERVICES

EXTENT OF CONTRACTORS SITE AREA. PROVIDE TEMPORARY FENCING TO WORKPLACE HEALTH AND SAFETY REQUIREMENTS AND MAINTAIN DURING CONTRACT PERIOD.

CONTRACTOR TO DEMOLISH CONCRETE

STANWELL TO REMOVE CONTAINERS PRIOR TO CONSTRUCTION

REDIRECT ELECTRICAL LINE

CONTRACTOR TO DEMOLISH CONCRETE

TENDER ISSUE

Client



Project Details

NEW OFFICE, REFURB PROJECT

Address

SWITCHYARD ROAD, STANWELL, 4702

Drawing Title

A4 - NEW BUILD - EXISTING SITE PLAN



0483 988 655 **M**
info@designelements.com.au **E**
QBCC No: 1247120 BDAQ No: 0001677

Scale: 1:100


Rev: **T1**

Date: MARCH 2026

Drawn: NJB

Project No: **25_003**

Drawing No: **A0-006**

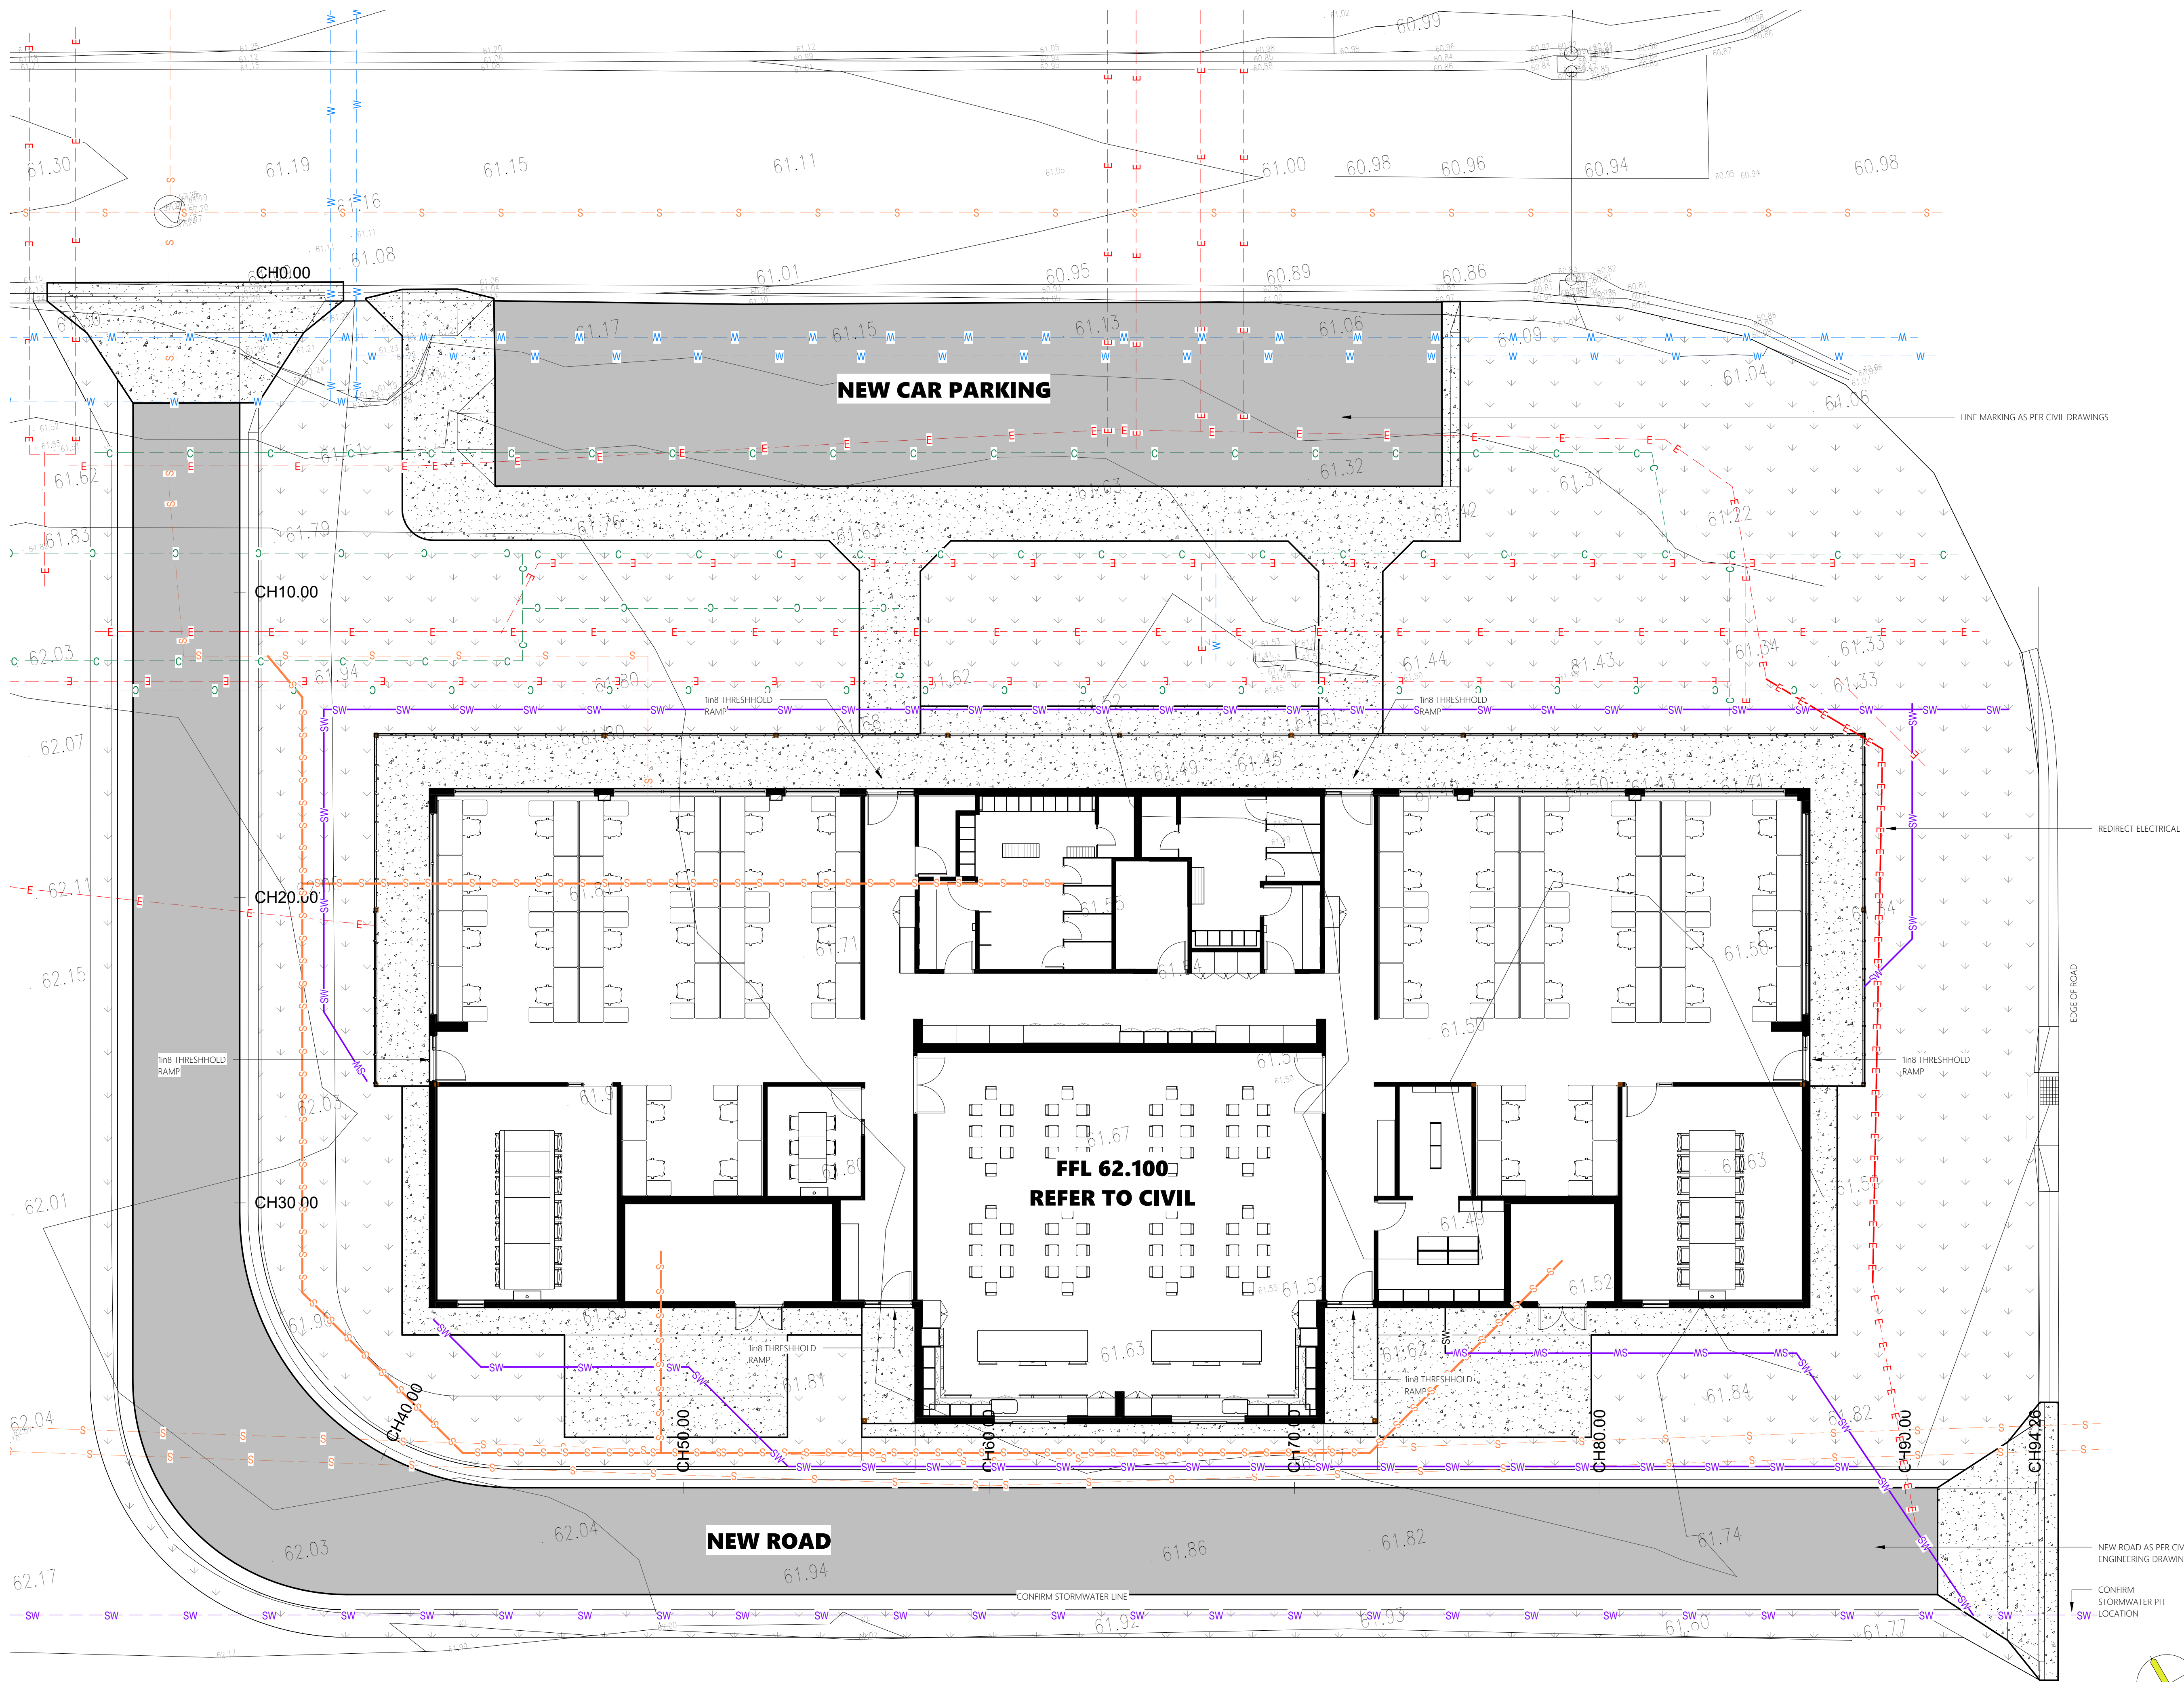

REVISIONS		
Rev	Description	Date
T1	TENDER ISSUE	19.03.2026

DO NOT SCALE THIS DRAWINGS

SERVICE LEGEND

---Eu---	Electrical Line
---IW---	Industrial Waste
---G---	Gas
---S---	Sewer
---SW---	Stormwater
---C---	Comms
---W---	Water
---HYD---	Fire Hydrant

ALL SERVICE LINES SHOWN ON THE PLAN ARE APPROXIMATE LOCATIONS. CONTRACTOR TO LOCATE ALL SERVICES ON SITE PRIOR TO COMMENCING WORKS.

THE CONTRACTOR SHALL ENSURE THAT AT ALL TIMES SERVICES TO ALL SURROUNDING BUILDINGS ARE NOT AFFECTED BY THE WORKS.

CAP VAC AREAS TO IDENTIFY LOCATION OF SERVICES

TENDER ISSUE

Client

Project Details

NEW OFFICE, REFURB PROJECT

Address

SWITCHYARD ROAD, STANWELL, 4702

Drawing Title

A4 - NEW BUILD - PROPOSED SITE PLAN

0483 988 655 M
info@deziignelements.com.au E
QBCC No: 1247120 BDAQ No: 0001677

Scale: 1 : 100 Rev: **T1**
Date: MARCH 2026
Drawn: NJB
Project No: Drawing No:
25_003 A0-007

19/03/2026 11:52:58 AM

A4 - NEW BUILD - Proposed Site

1 : 100