


ADDRESS

SWITCHYARD ROAD, STANWELL, QLD, 4702

PROJECT

3 x OFFICE REFURBISHMENTS, 1 x NEW BUILD

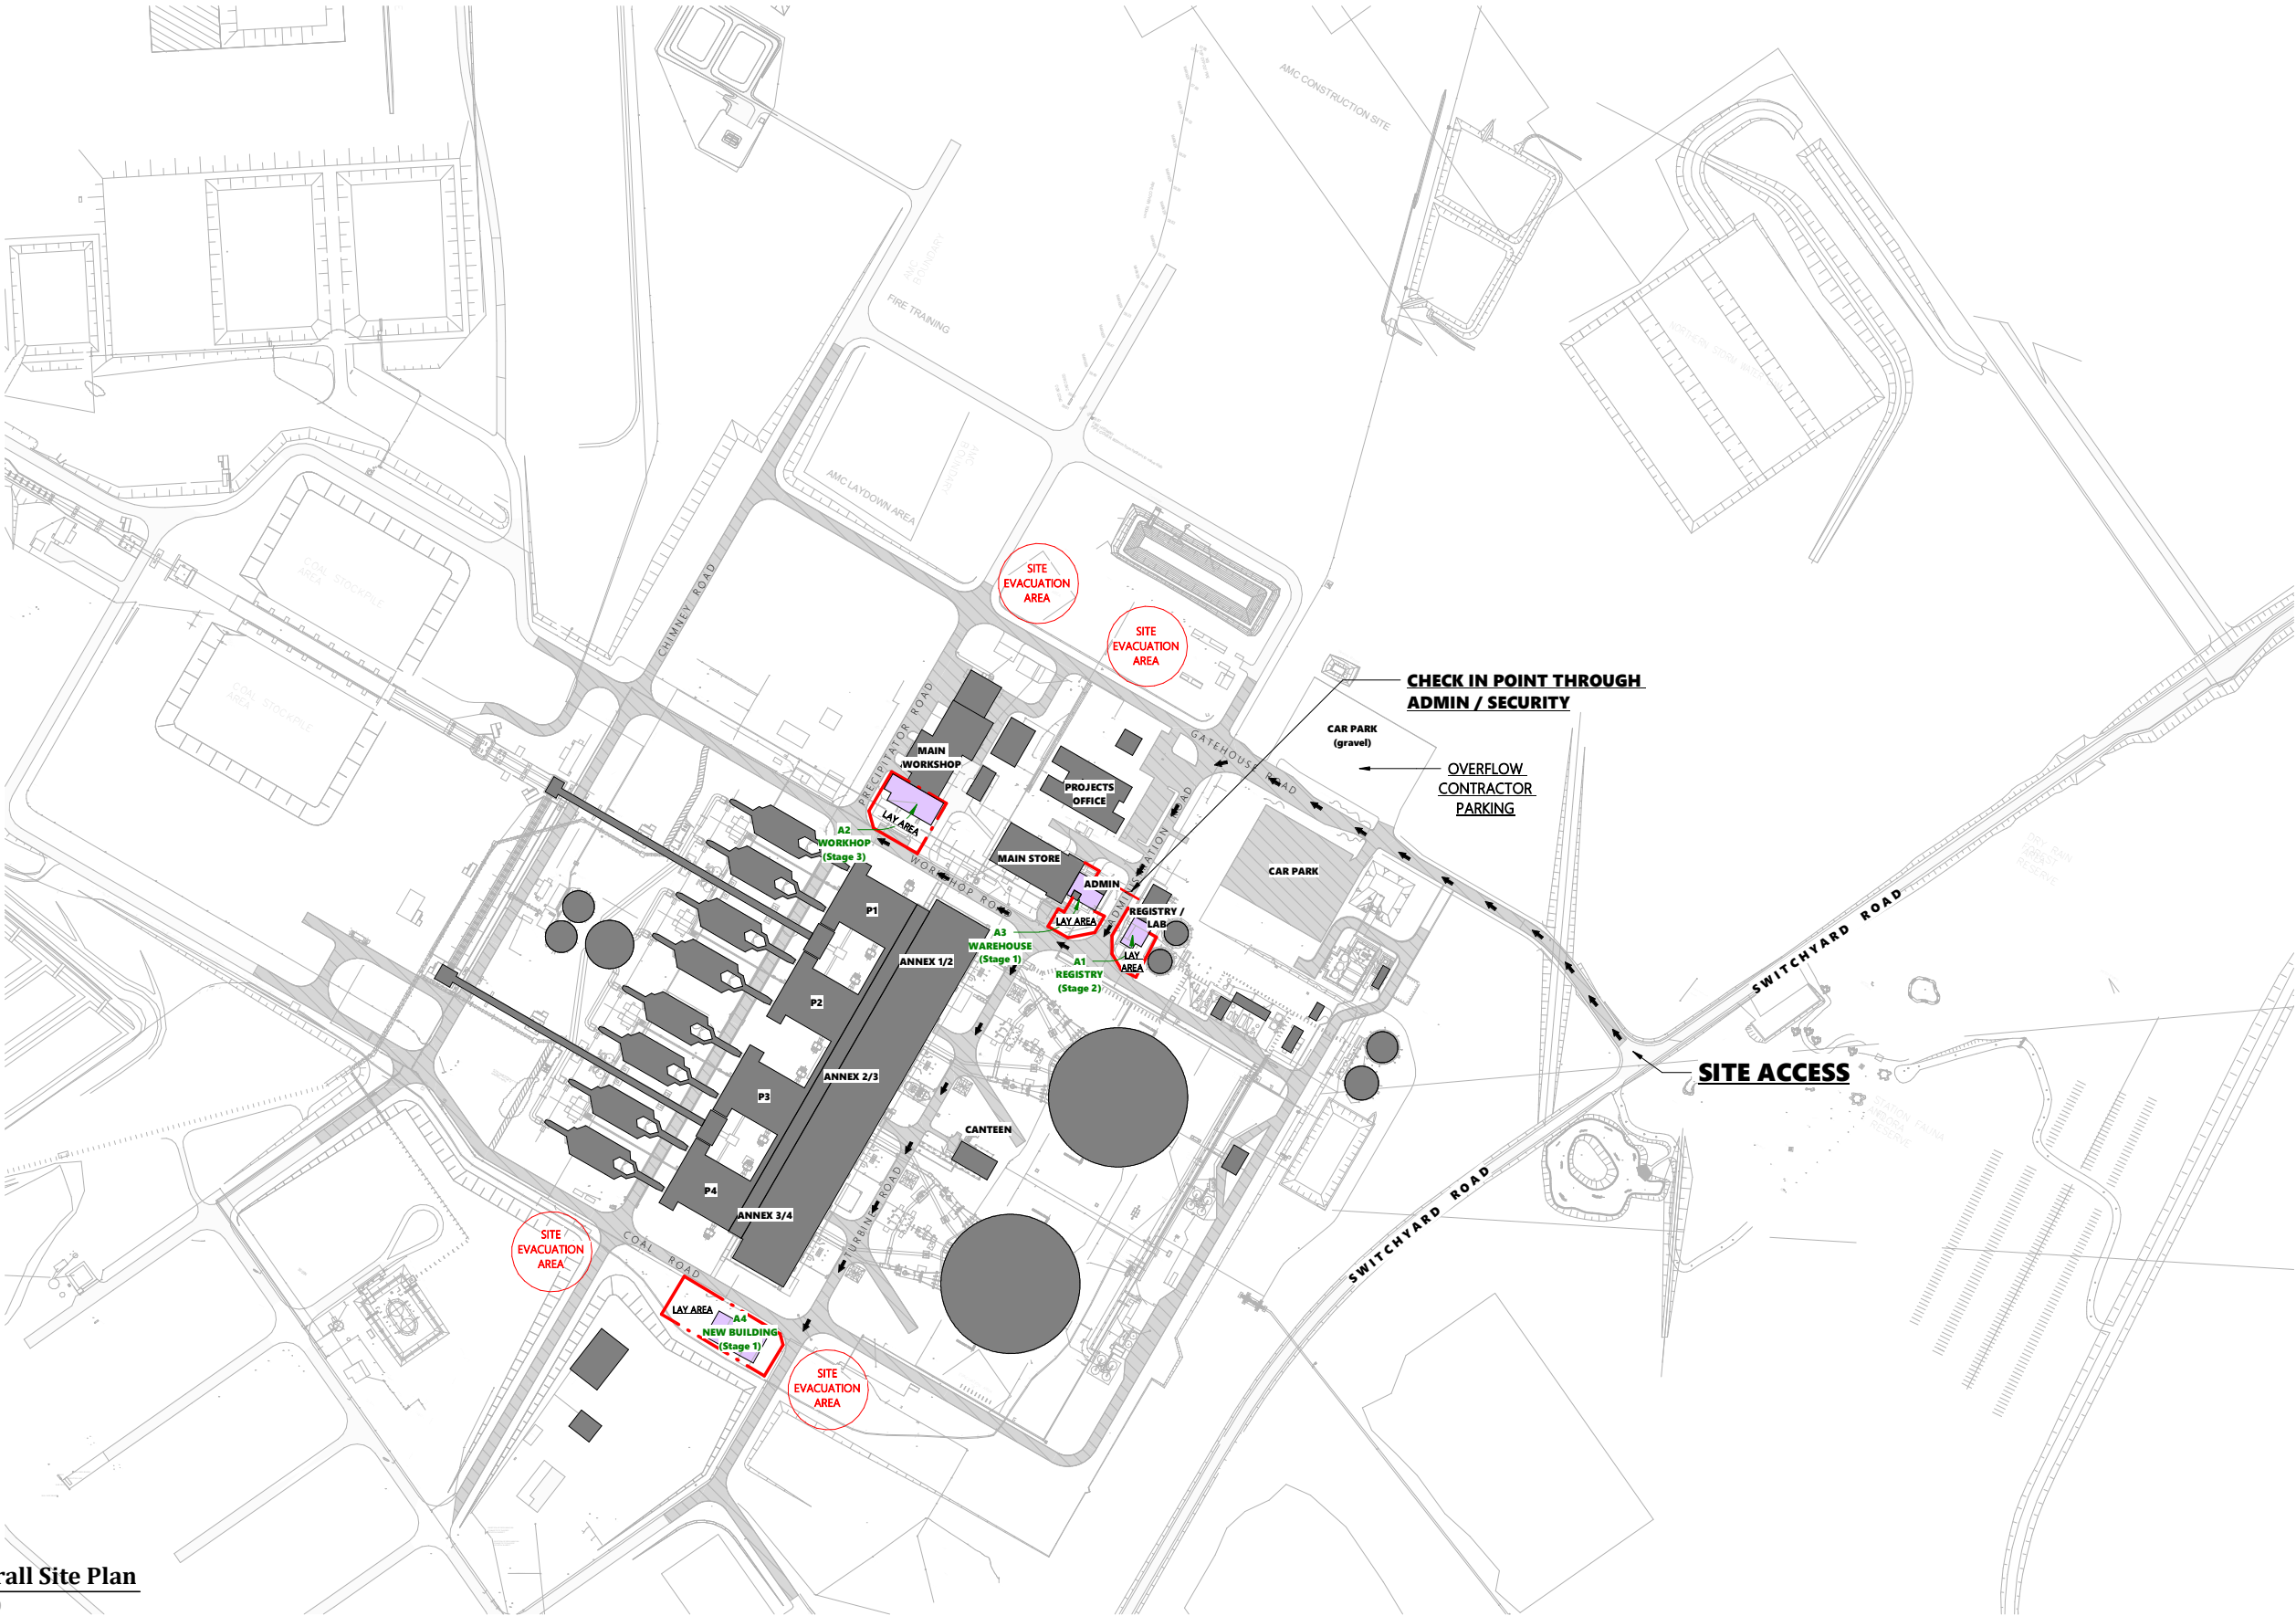

Overall Site Plan
1 : 2500

REVISIONS

Rev	Description	Date
T1	TENDER ISSUE	19.03.2026

DO NOT SCALE THIS DRAWINGS

REAL PROPERTY DESCRIPTION

Lot Number

44

Reg/Survey Plan Number

SP 140 243

Local Authority

ROCKHAMPTON

STAGE OF WORKS

STAGE 1 -

A3 WAREHOUSE

A4 NEW BUILD

STAGE 2 -

A1 - REGISTRY

STAGE 3 -

A2 WORKSHOP

TENDER ISSUE

Client

Project Details

NEW OFFICE, REFURB PROJECT

Address

SWITCHYARD ROAD,

STANWELL, 4702

Drawing Title

OVERALL SITE PLAN

0483 988 655

M

info@dezi elements.com.au

E

QBCC No: 1247120

BDAQ No: 0001677

Scale: As indicated

Date: MARCH 2026

Drawn: NJB

Rev: T1

Project No: 25_003

Drawing No: A0-000

19/03/2026 11:49:42 AM

These drawings, designs and the Copyright thereof are the property of Dezi Group Qld Pty Ltd (T/A Dezi Elements) and are not to be used, retained or copied by either physical or electronic means without the written permission of Nathan Burke (Director). Conditions stated in the terms and conditions. Dezi Elements accepts no responsibility for the completeness, accuracy or compatibility of electronically transferred documents.

DO NOT SCALE THIS DRAWINGS

SERVICE LEGEND

- | | |
|-----------|------------------|
| ---Eu--- | Electrical Line |
| ---W--- | Industrial Waste |
| ---G--- | Gas |
| ---S--- | Sewer |
| ---SW--- | Stormwater |
| ---C--- | Comms |
| ---W--- | Water |
| ---HYD--- | Fire Hydrant |

ALL SERVICE LINES SHOWN ON THE PLAN ARE APPROXIMATE LOCATIONS. CONTRACTOR TO LOCATE ALL SERVICES ON SITE PRIOR TO COMMENCING WORKS.

THE CONTRACTOR SHALL ENSURE THAT AT ALL TIMES SERVICES TO ALL SURROUNDING BUILDINGS ARE NOT AFFECTED BY THE WORKS.

CAP VAC AREAS TO IDENTIFY LOCATION OF SERVICES

TENDER ISSUE



Project Details

NEW OFFICE, REFURB PROJECT

Address

**SWITCHYARD ROAD,
STANWELL, 4702**

Drawing Title

**A1 - REGISTRY - EXISTING &
PROPOSED SITE PLAN**



0483 988 655 M

info@dezi nelements.com.au E

QBCC No: 1247120 BDAQ No: 0001677

Scale: 1 : 100

Date: MARCH 2026

Drawn: NJB

Project No:

25_003

Rev:



T1

Drawing No:

A0-001



19/03/2026 11:49:45 AM

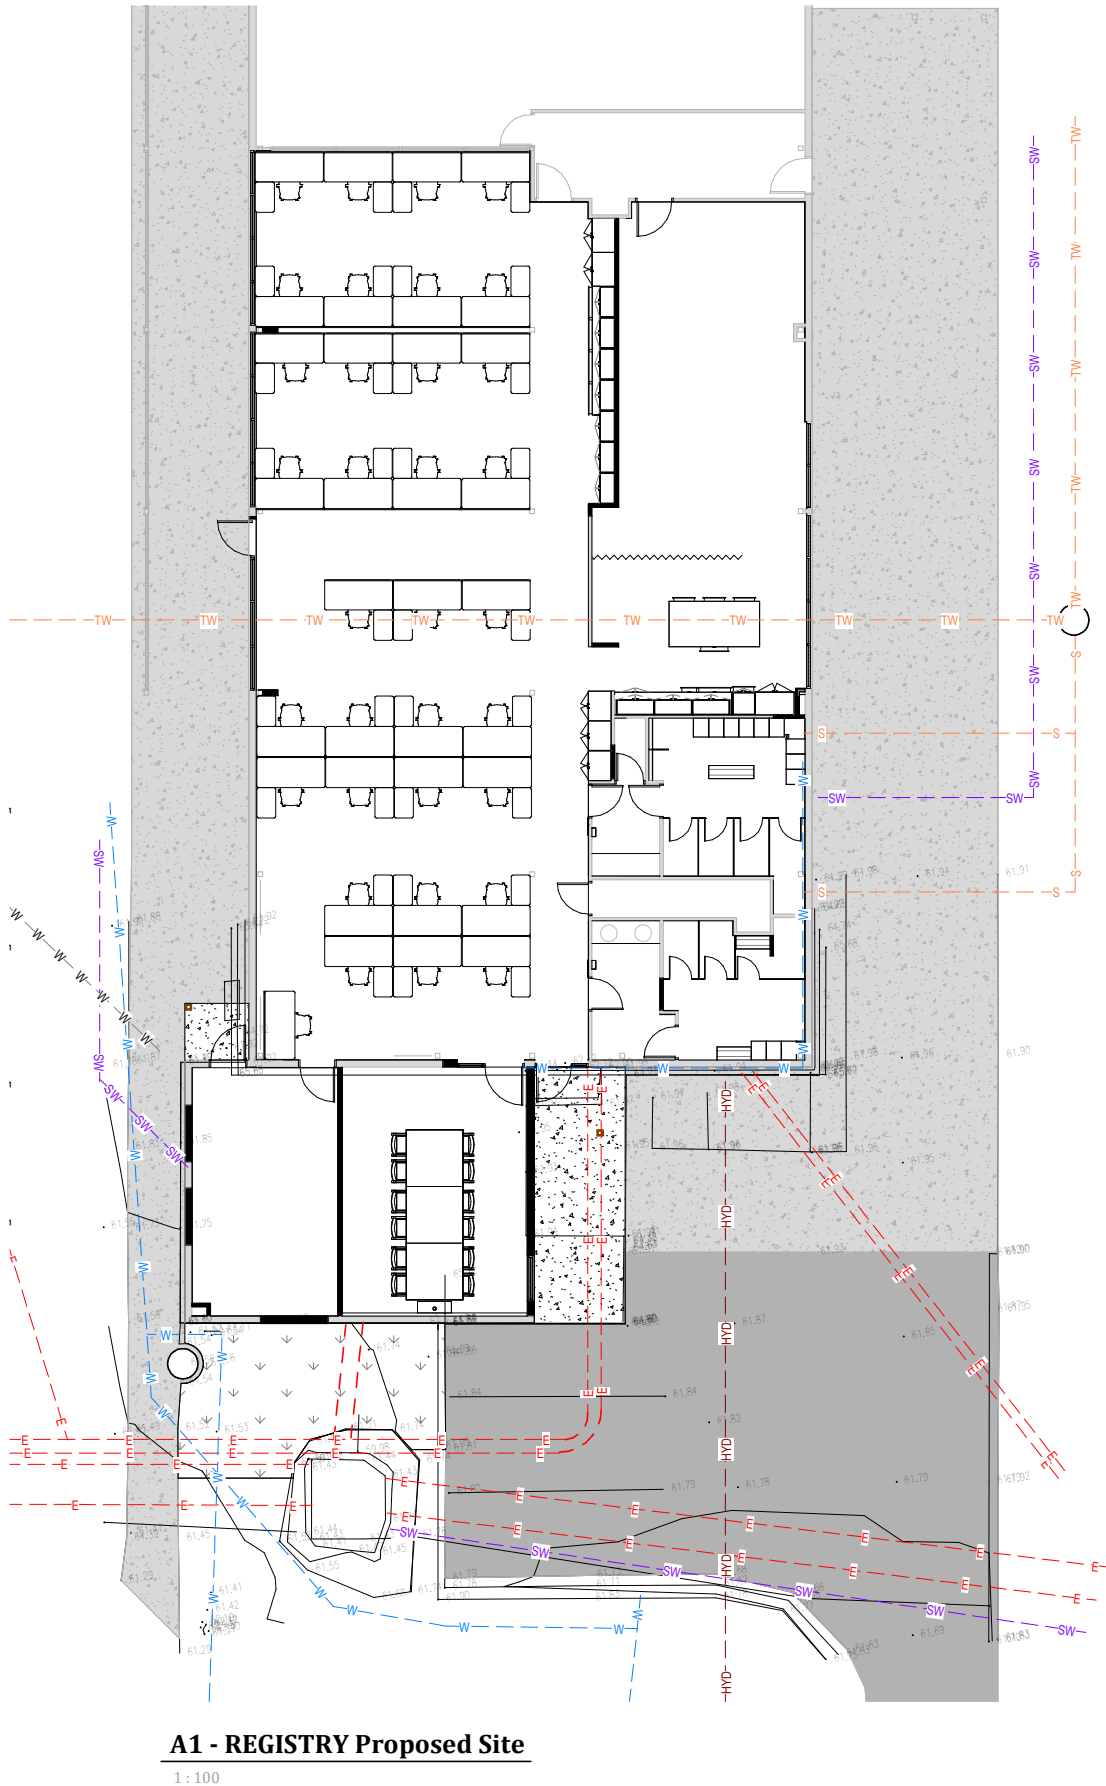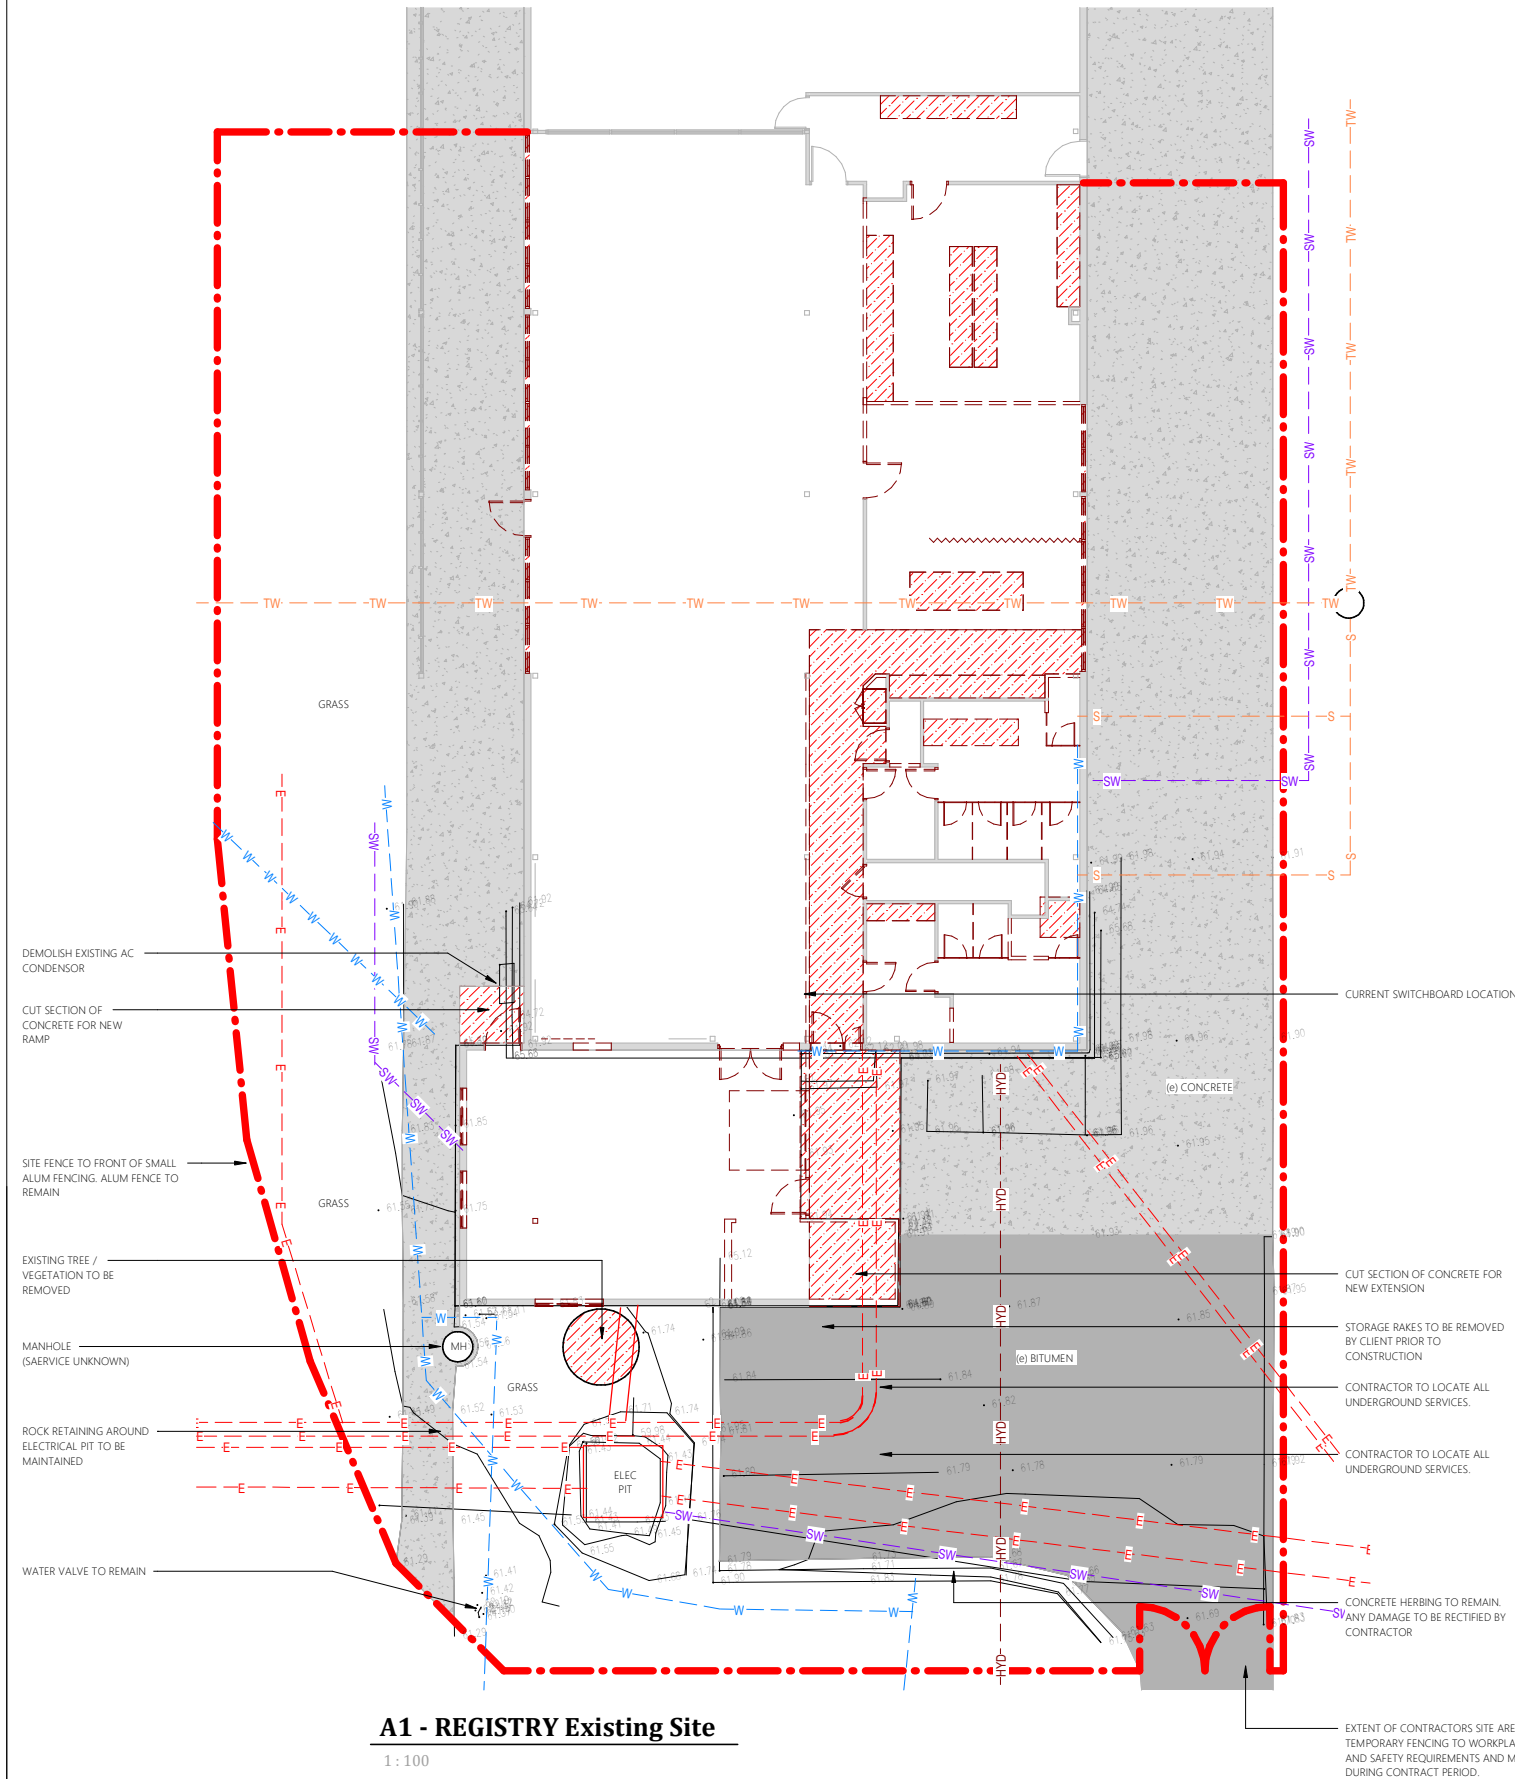

REVISIONS		
Rev	Description	Date
T1	TENDER ISSUE	19.03.2026

DO NOT SCALE THIS DRAWINGS

SERVICE LEGEND

---Eu---

---W---

---G---

---S---

---SW---

---C---

---W---

---HYD---

Electrical Line

Industrial Waste

Gas

Sewer

Stormwater

Comms


Water

Fire Hydrant

ALL SERVICE LINES SHOWN ON THE PLAN ARE APPROXIMATE LOCATIONS. CONTRACTOR TO LOCATE ALL SERVICES ON SITE PRIOR TO COMMENCING WORKS.

THE CONTRACTOR SHALL ENSURE THAT AT ALL TIMES SERVICES TO ALL SURROUNDING BUILDINGS ARE NOT AFFECTED BY THE WORKS.

CAP VAC AREAS TO IDENTIFY LOCATION OF SERVICES

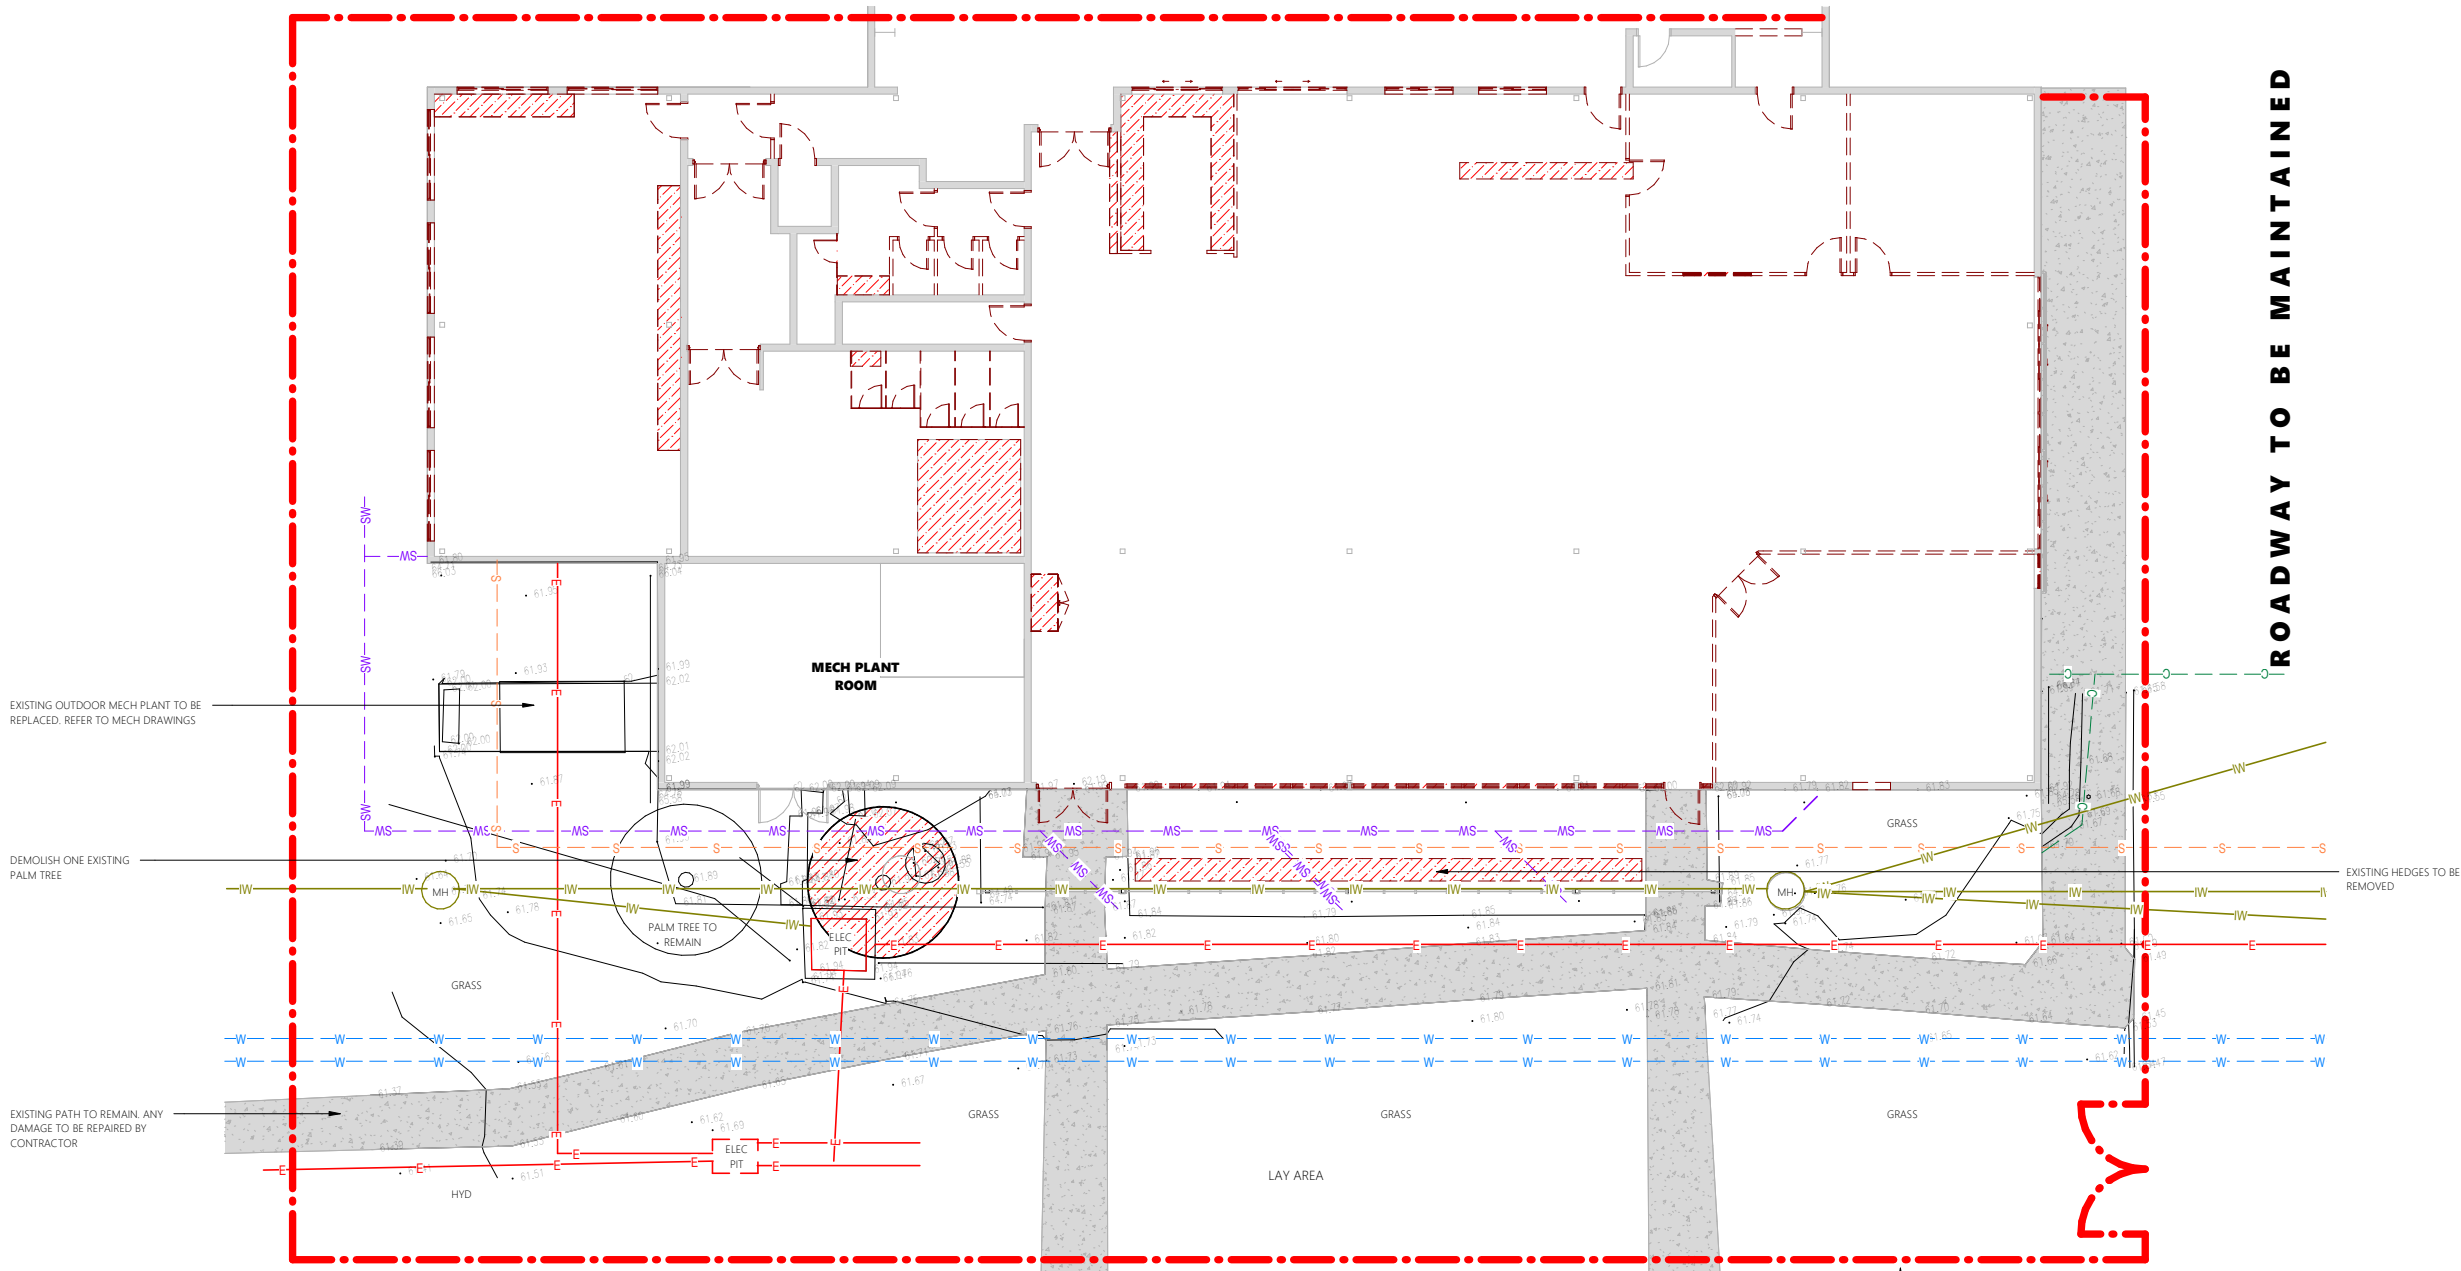

TENDER ISSUE

Client

Project Details

NEW OFFICE, REFURB PROJECT

Address

**SWITCHYARD ROAD,
STANWELL, 4702**

Drawing Title

**A2 - WORKSHOP -
EXISTING SITE PLAN**

0483 988 655 M

info@deziignelements.com.au E

QBCC No: 1247120 BDAQ No: 0001677

Scale: 1 : 100 Rev:

Date: MARCH 2026 T1

Drawn: NJB

Project No: Drawing No:

25_003 A0-002

19/03/2026 11:49:47 AM



A2 - WORKSHOP Existing Site

1 : 100

REVISIONS

Rev	Description	Date
T1	TENDER ISSUE	19.03.2026

DO NOT SCALE THIS DRAWINGS

SERVICE LEGEND

---Eu---	Electrical Line
---W---	Industrial Waste
---G---	Gas
---S---	Sewer
---SW---	Stormwater
---C---	Comms
---W---	Water
---HYD---	Fire Hydrant

ALL SERVICE LINES SHOWN ON THE PLAN ARE APPROXIMATE LOCATIONS. CONTRACTOR TO LOCATE ALL SERVICES ON SITE PRIOR TO COMMENCING WORKS.

THE CONTRACTOR SHALL ENSURE THAT AT ALL TIMES SERVICES TO ALL SURROUNDING BUILDINGS ARE NOT AFFECTED BY THE WORKS.

CAP VAC AREAS TO IDENTIFY LOCATION OF SERVICES



TENDER ISSUE



Project Details
NEW OFFICE, REFURB PROJECT

Address
**SWITCHYARD ROAD,
STANWELL, 4702**


Drawing Title
**A2 - WORKSHOP -
PROPOSED SITE PLAN**



0483 988 655 M
info@designelements.com.au E
QBCC No: 1247120 BDAQ No: 0001677

Scale: 1 : 100 Rev:
Date: MARCH 2026 T1
Drawn: NJB

Project No: Drawing No:
25_003 A0-003

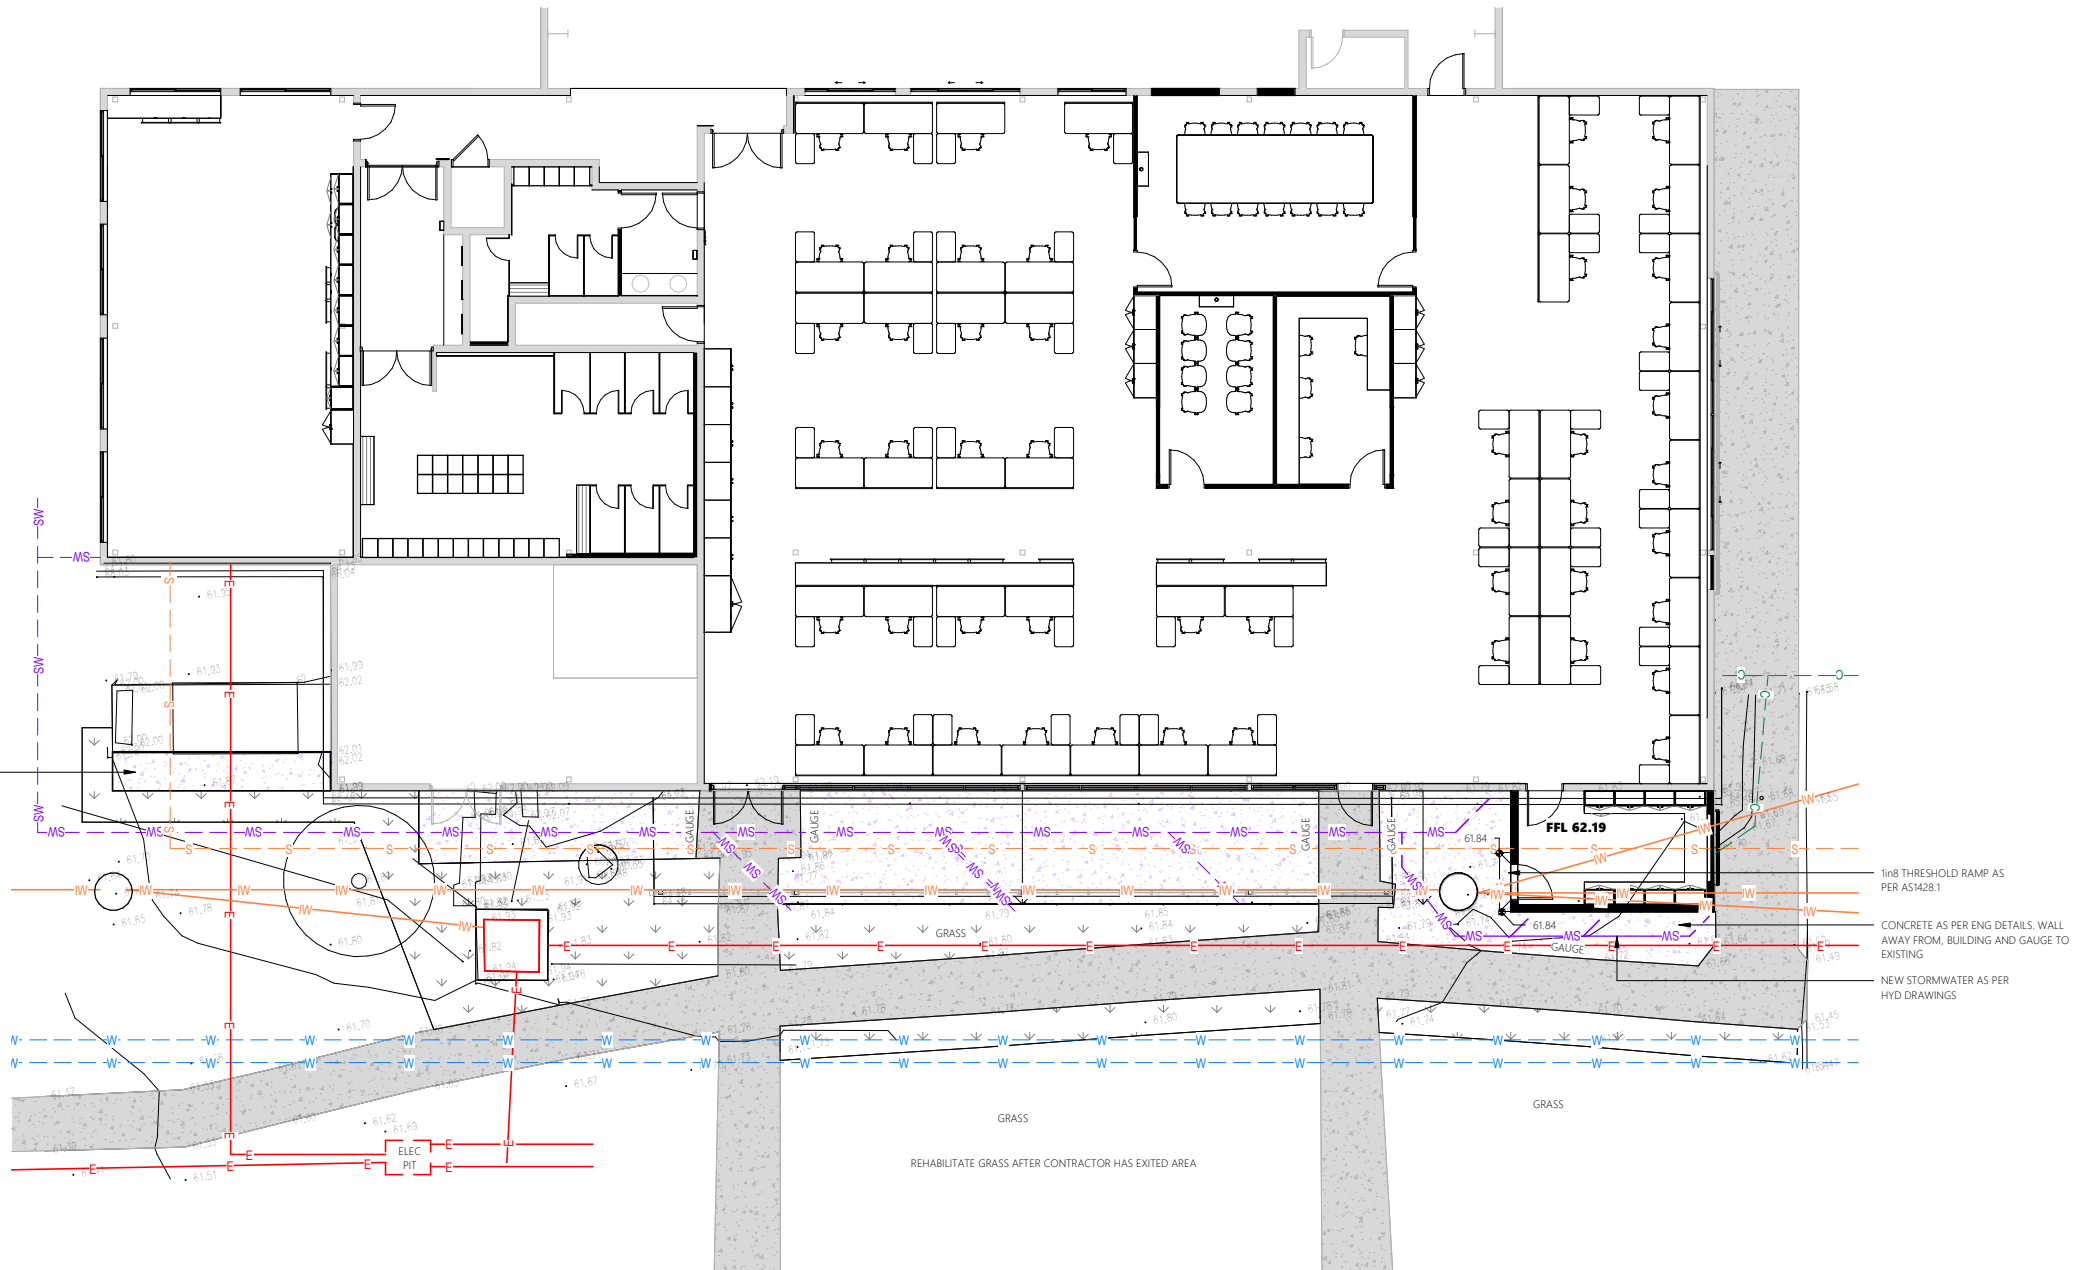

A2 - WORKSHOP Proposed Site

1 : 100

EXTENT OF CONTRACTORS SITE AREA. PROVIDE TEMPORARY FENCING TO WORKPLACE HEALTH AND SAFETY REQUIREMENTS AND MAINTAIN DURING CONTRACT PERIOD.

EXISTING GARDEN TO REMAIN. TO BE RE MULCHED AT END OF CONSTRUCTION WORKS. ANY DAMAGED TO GARDEN EDGING TO BE REPAIRED BY CONTRACTOR

TREE TO BE REMOVED FOR CONSTRUCTION WORKS

CLOSE ACCESS TO BUILDING

ACCESS TO FIRST AID TO BE MAINTAINED AT ALL TIMES. PARKING SPACES AVAILABLE FOR FIRST AID ONLY

ANY BITUMEN / KERBING DAMAGE TO BE REPAIRED

ACCESS TO FIRST AID TO BE MAINTAINED

RECEPTION / SECURITY

FIRST AID

MECH PLANT

EXISTING BITUMEN CARPARK

ELEC PIT

ANY DAMAGE TO CONCRETE PATHS TO BE REPAIRED BY CONTRACTOR

REHABILITATE GRASS AFTER CONTRACTOR HAS EXITED AREA

EXTENT OF CONTRACTORS SITE AREA. PROVIDE TEMPORARY FENCING TO WORKPLACE HEALTH AND SAFETY REQUIREMENTS AND MAINTAIN DURING CONTRACT PERIOD.

EXTENT OF CONTRACTORS SITE AREA. PROVIDE TEMPORARY FENCING TO WORKPLACE HEALTH AND SAFETY REQUIREMENTS AND MAINTAIN DURING CONTRACT PERIOD.

REVISIONS

Rev	Description	Date
T1	TENDER ISSUE	19.03.2026

DO NOT SCALE THIS DRAWINGS

SERVICE LEGEND

---Eg---	Electrical Line
---W---	Industrial Waste
---G---	Gas
---S---	Sewer
---SW---	Stormwater
---C---	Comms
---W---	Water
---HYD---	Fire Hydrant

ALL SERVICE LINES SHOWN ON THE PLAN ARE APPROXIMATE LOCATIONS. CONTRACTOR TO LOCATE ALL SERVICES ON SITE PRIOR TO COMMENCING WORKS.

THE CONTRACTOR SHALL ENSURE THAT AT ALL TIMES SERVICES TO ALL SURROUNDING BUILDINGS ARE NOT AFFECTED BY THE WORKS.

CAP VAC AREAS TO IDENTIFY LOCATION OF SERVICES

TENDER ISSUE

Client



Project Details

NEW OFFICE, REFURB PROJECT

Address

SWITCHYARD ROAD, STANWELL, 4702

Drawing Title

A3 - WAREHOUSE - EXISTING & PROPOSED SITE PLAN



0483 988 655 M

info@designelements.com.au E

QBCC No: 1247120 BDAQ No: 0001677

Scale: 1 : 100

Date: MARCH 2026

Drawn: NJB

Project No:

25_003

Rev:

T1

Drawing No:

A0-004



A3 - WAREHOUSE Existing Site

1 : 100

REVISIONS

Rev	Description	Date
T1	TENDER ISSUE	19.03.2026

DO NOT SCALE THIS DRAWINGS

SERVICE LEGEND

-Ea-	-Ea-	Electrical Line
-W-	-W-	Industrial Waste
-G-	-G-	Gas
-S-	-S-	Sewer
-SW-	-SW-	Stormwater
-C-	-C-	Comms
-W-	-W-	Water
-HYD-	-HYD-	Fire Hydrant

ALL SERVICE LINES SHOWN ON THE PLAN ARE APPROXIMATE LOCATIONS. CONTRACTOR TO LOCATE ALL SERVICES ON SITE PRIOR TO COMMENCING WORKS.

THE CONTRACTOR SHALL ENSURE THAT AT ALL TIMES SERVICES TO ALL SURROUNDING BUILDINGS ARE NOT AFFECTED BY THE WORKS.

CAP VAC AREAS TO IDENTIFY LOCATION OF SERVICES

TENDER ISSUE

Client



Project Details

NEW OFFICE, REFURB PROJECT

Address

SWITCHYARD ROAD, STANWELL, 4702

Drawing Title


A3 - WAREHOUSE - PROPOSED SITE PLAN

 **dezi elements**
BUILDING DESIGNERS

0483 988 655 M
info@dezi elements.com.au E


QBCC No: 1247120 BDAQ No: 0001677

Scale: 1 : 100 Rev: T1
Date: MARCH 2026
Drawn: NJB
Project No: Drawing No:
25_003 A0-005

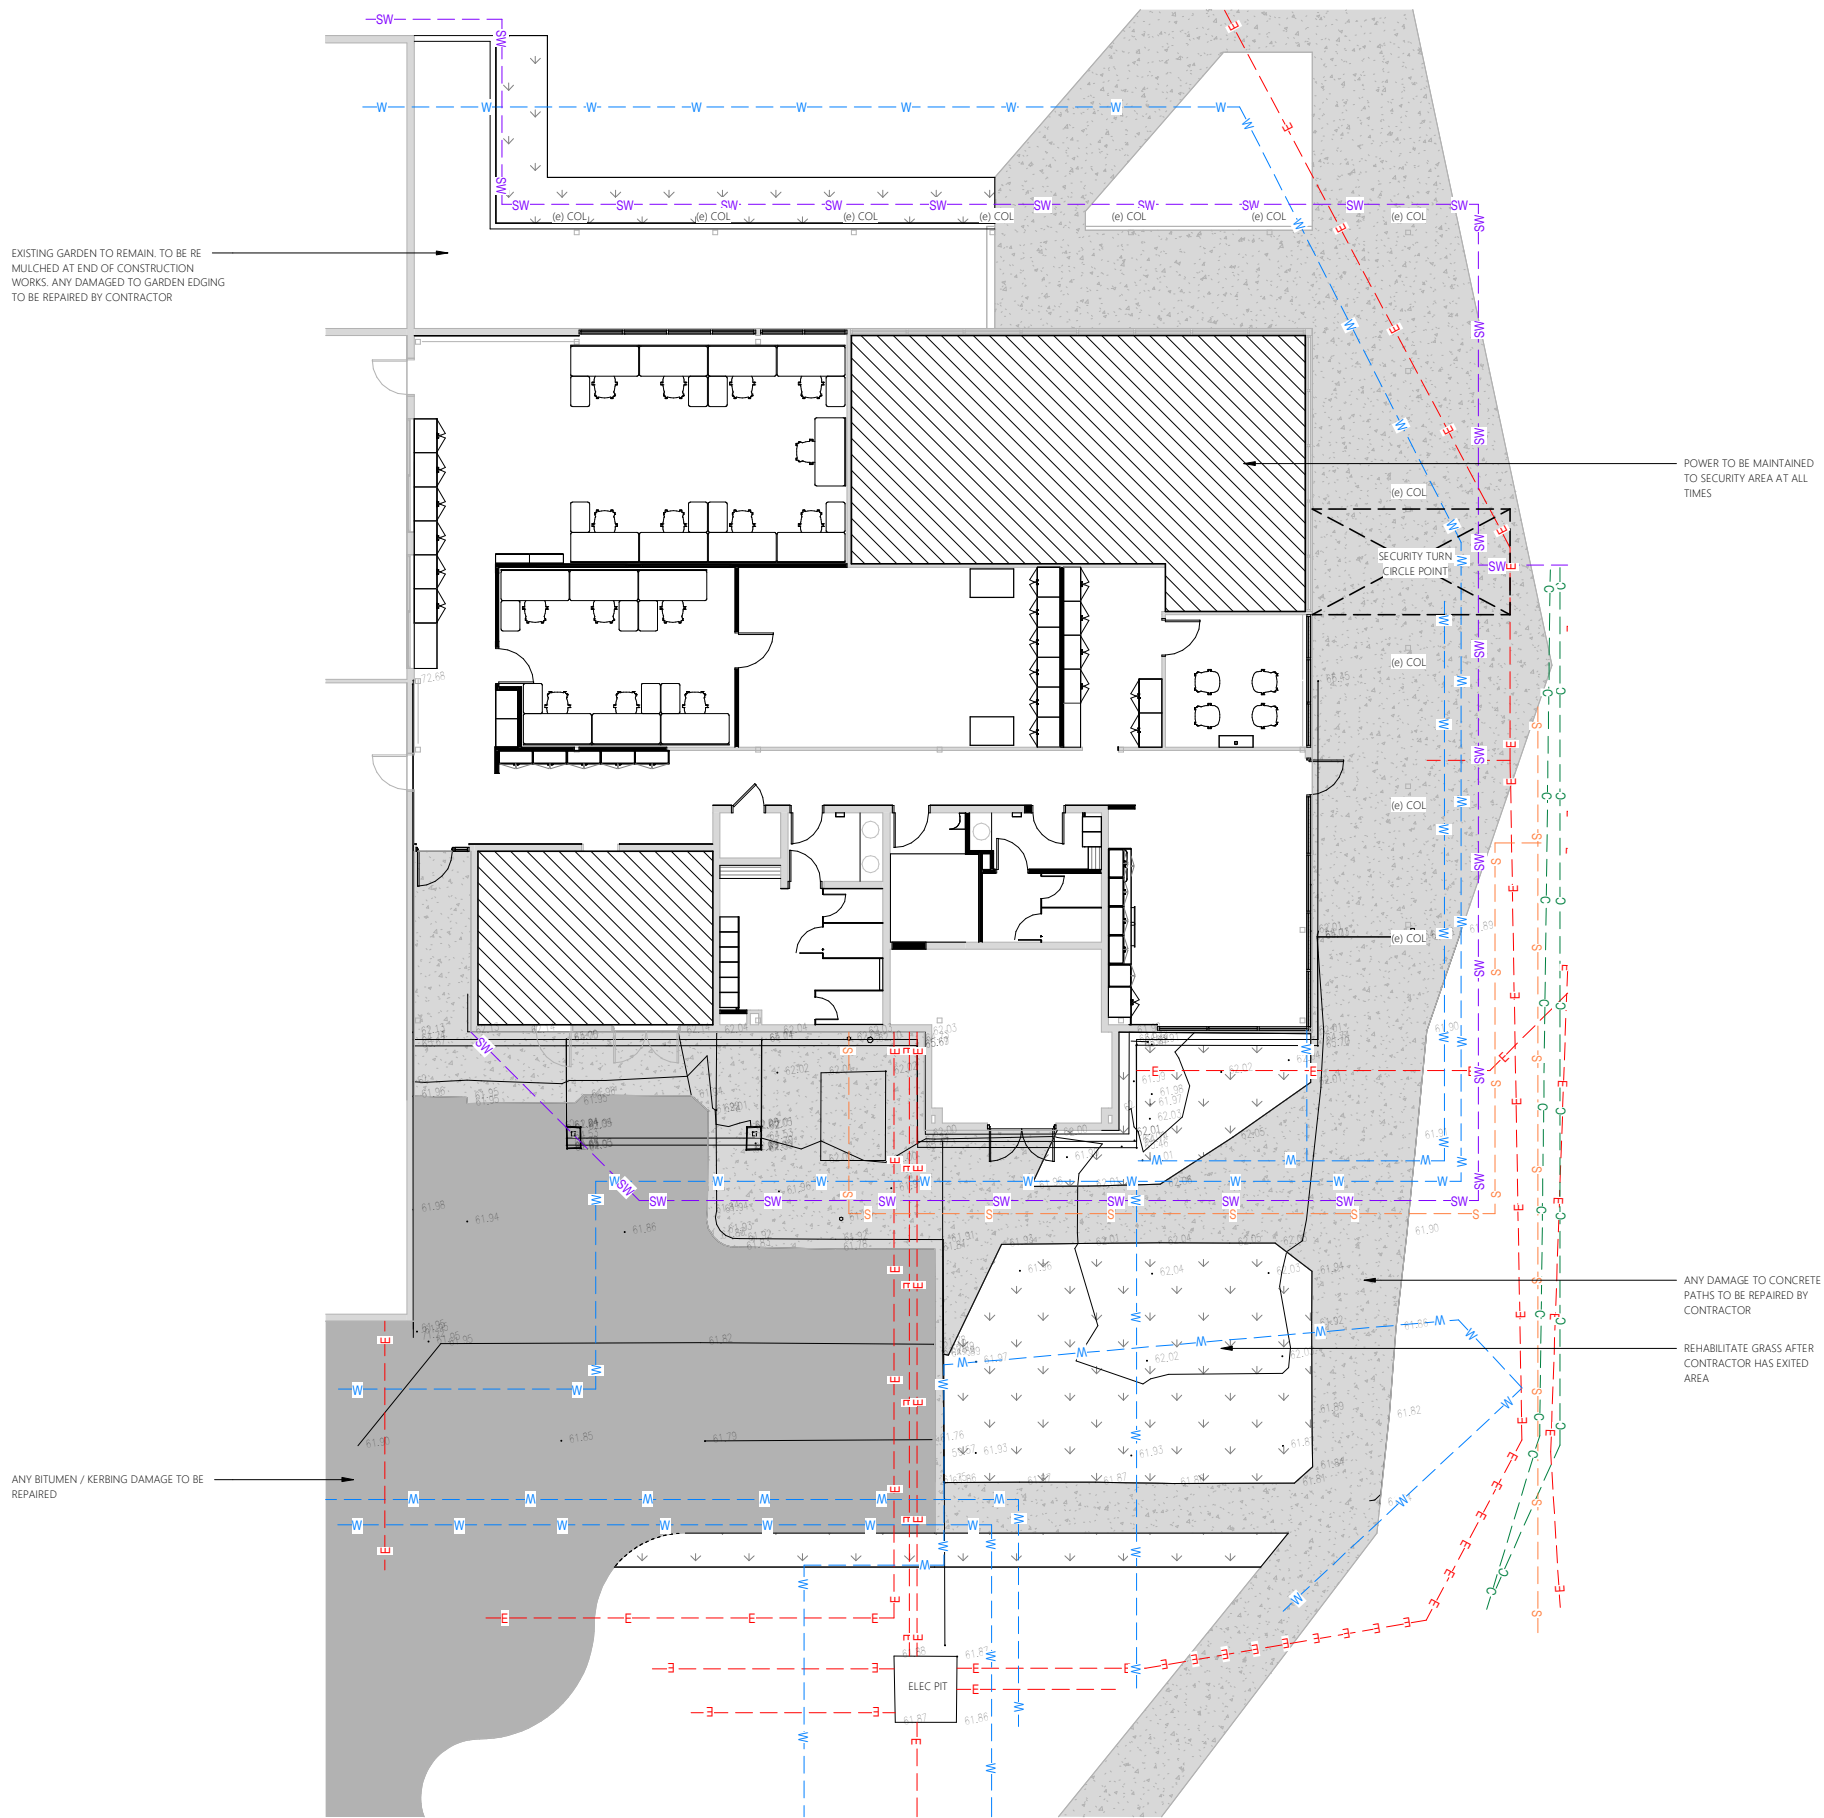

A3 - WAREHOUSE Proposed Site

1 : 100

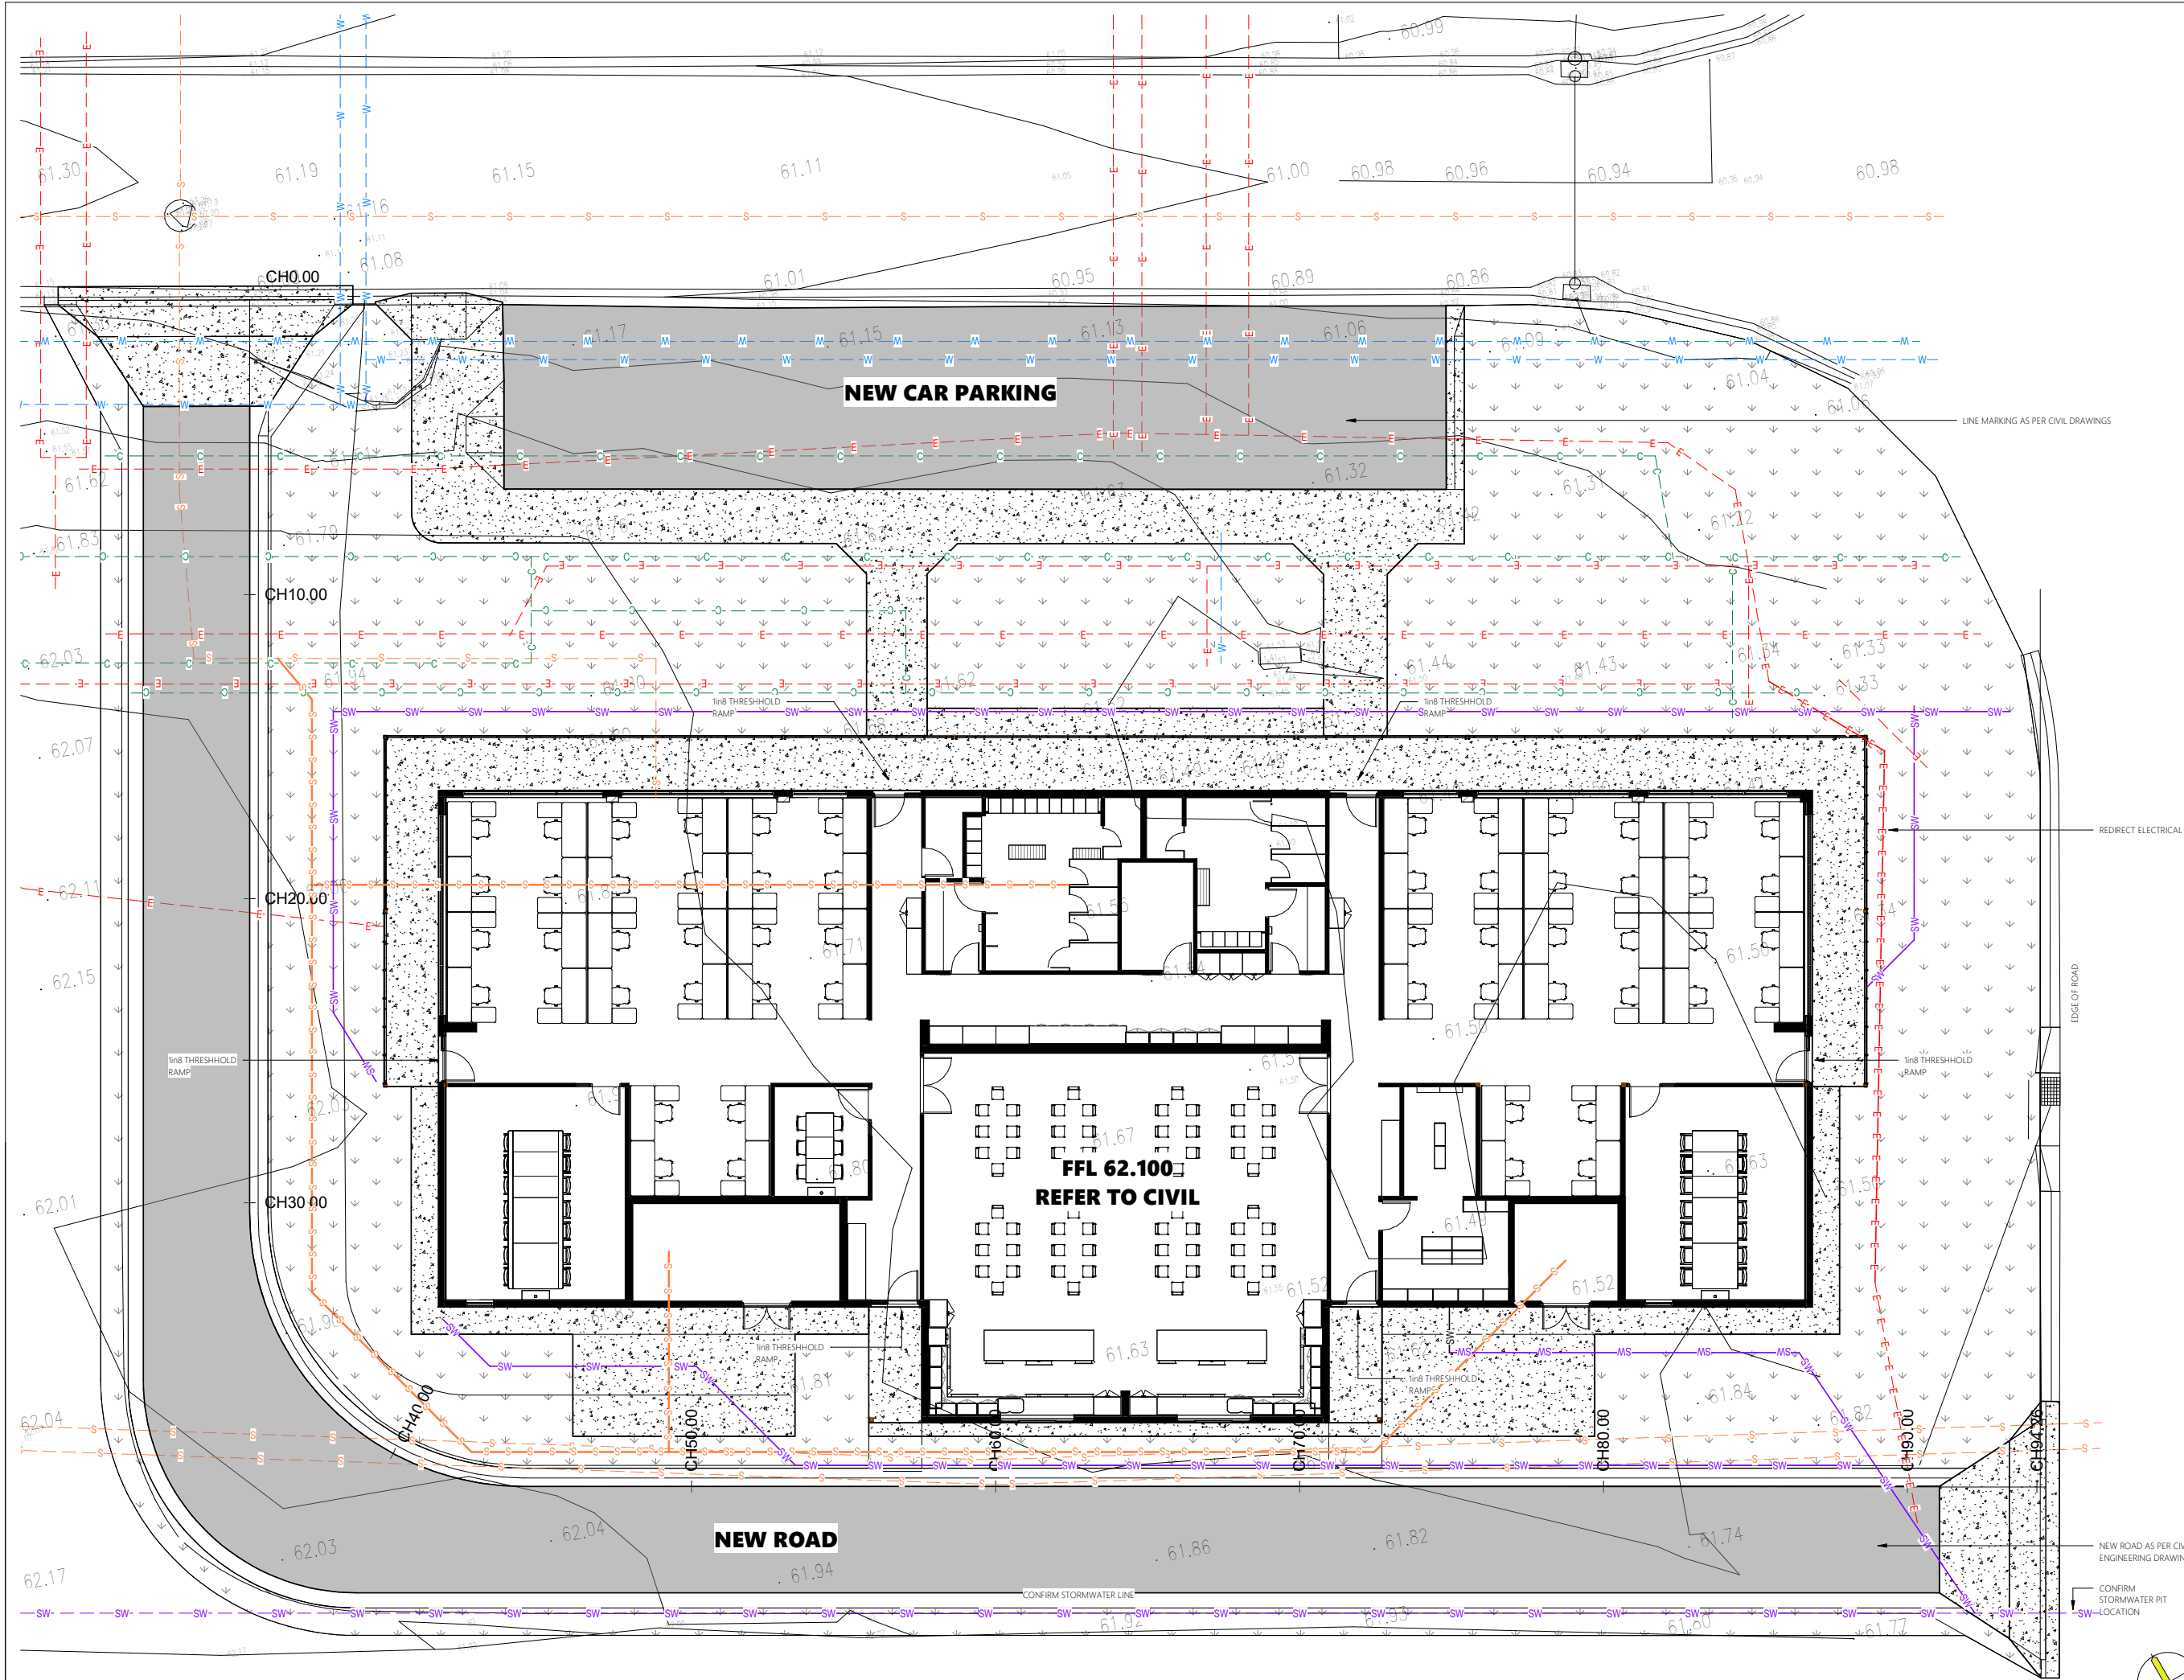

REVISIONS

Rev	Description	Date
T1	TENDER ISSUE	19.03.2026

DO NOT SCALE THIS DRAWINGS

SERVICE LEGEND

---E---E---	Electrical Line
---W---W---	Industrial Waste
---G---G---	Gas
---S---S---	Sewer
---SW---SW---	Stormwater
---C---C---	Comms
---W---W---	Water
---HYD---HYD---	Fire Hydrant

ALL SERVICE LINES SHOWN ON THE PLAN ARE APPROXIMATE LOCATIONS. CONTRACTOR TO LOCATE ALL SERVICES ON SITE PRIOR TO COMMENCING WORKS.

THE CONTRACTOR SHALL ENSURE THAT AT ALL TIMES SERVICES TO ALL SURROUNDING BUILDINGS ARE NOT AFFECTED BY THE WORKS.

CAP VAC AREAS TO IDENTIFY LOCATION OF SERVICES

TENDER ISSUE

Client

stanwell

Project Details

NEW OFFICE, REFURB PROJECT

Address

SWITCHYARD ROAD, STANWELL, 4702

Drawing Title

A4 - NEW BUILD - PROPOSED SITE PLAN

dezinelements
BUILDING DESIGNERS

0483 988 655 M
info@dezi

QBCC No: 1247120 BDAQ No: 0001677

Scale: 1 : 100
Date: MARCH 2026
Drawn: NJB

Rev: **T1**
Project No: Drawing No:
25_003 A0-007

19/03/2026 11:49:55 AM

1 : 100

These drawings, designs and the Copyright thereof are the property of Design Group Qld Pty Ltd (T/A Design Elements) and are not to be used, retained or copied by either physical or electronic means without the written permission of Nathan Burke (Director). Conditions stated in the terms and conditions.

Design Elements accepts no responsibility for the completeness, accuracy or compatibility of electronically transferred documents.