



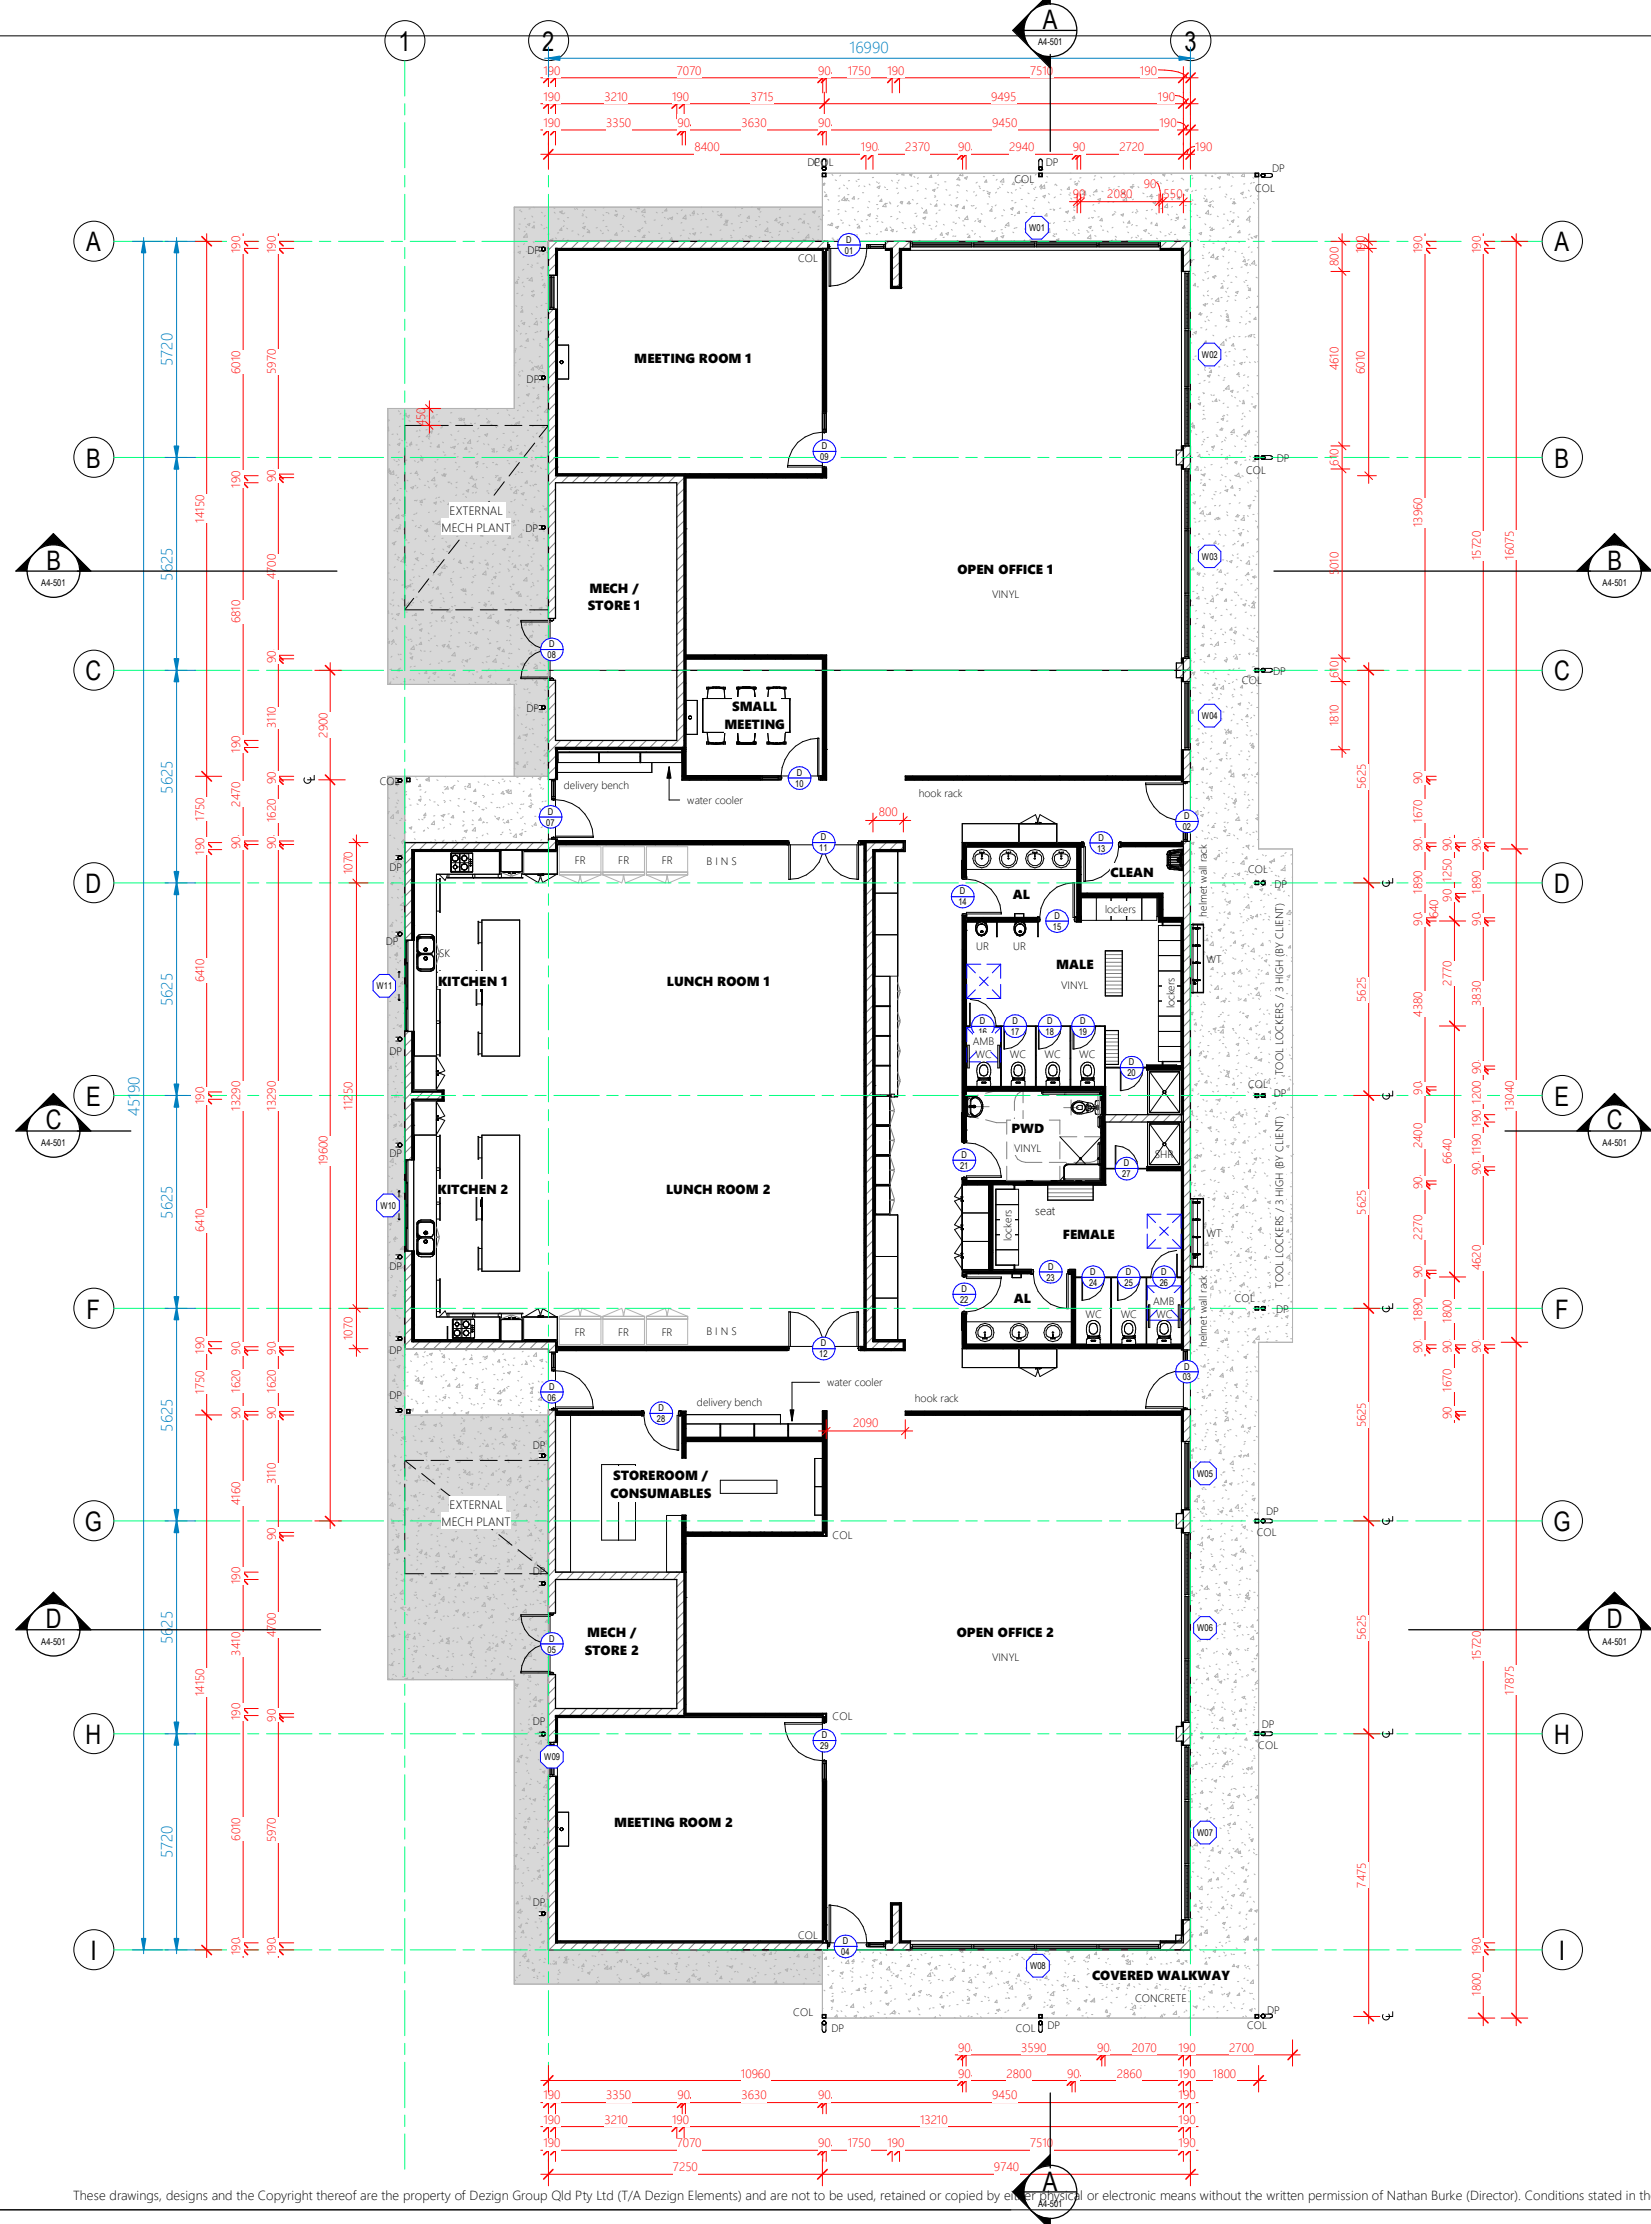

Proposed Floor Plan

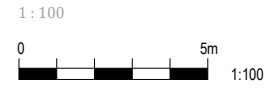

REVISIONS		
Rev	Description	Date
T1	TENDER ISSUE	12.03.2026

DO NOT SCALE THIS DRAWINGS

KEYNOTE LEGEND	
BSN	Basin
COL	Column
CON	Condenser
CPD	Cupboard
CS	Cleaners Sink
CT	Cooktop
DP	Downpipe
DW	Dish Washer
FAP	Fire Alarm Panel
FHR	Fire Hose Reel
FR	Fridge (By Client)
HD	Hand Driver (Air Blade)
L	Locker
OV	Oven
RH	Range Hood
DW	Dish Washer
SK	Sink
SB	Switch Board
UR	Urinal

TENDER ISSUE

Client

Project Details

OFFICE REFURBS

Address

STANWELL POWER STATION

Drawing Title


PROPOSED FLOOR PLAN

0483 988 655 M
info@deziignelements.com.au E
QBCC No: 1247120 BDAQ No: 0001677

Scale: 1 : 100 Rev: T1
Date: MAR 2026
Drawn: Author


Project No: Drawing No:
25_003 A4-300

12/03/2026 7:52:04 PM

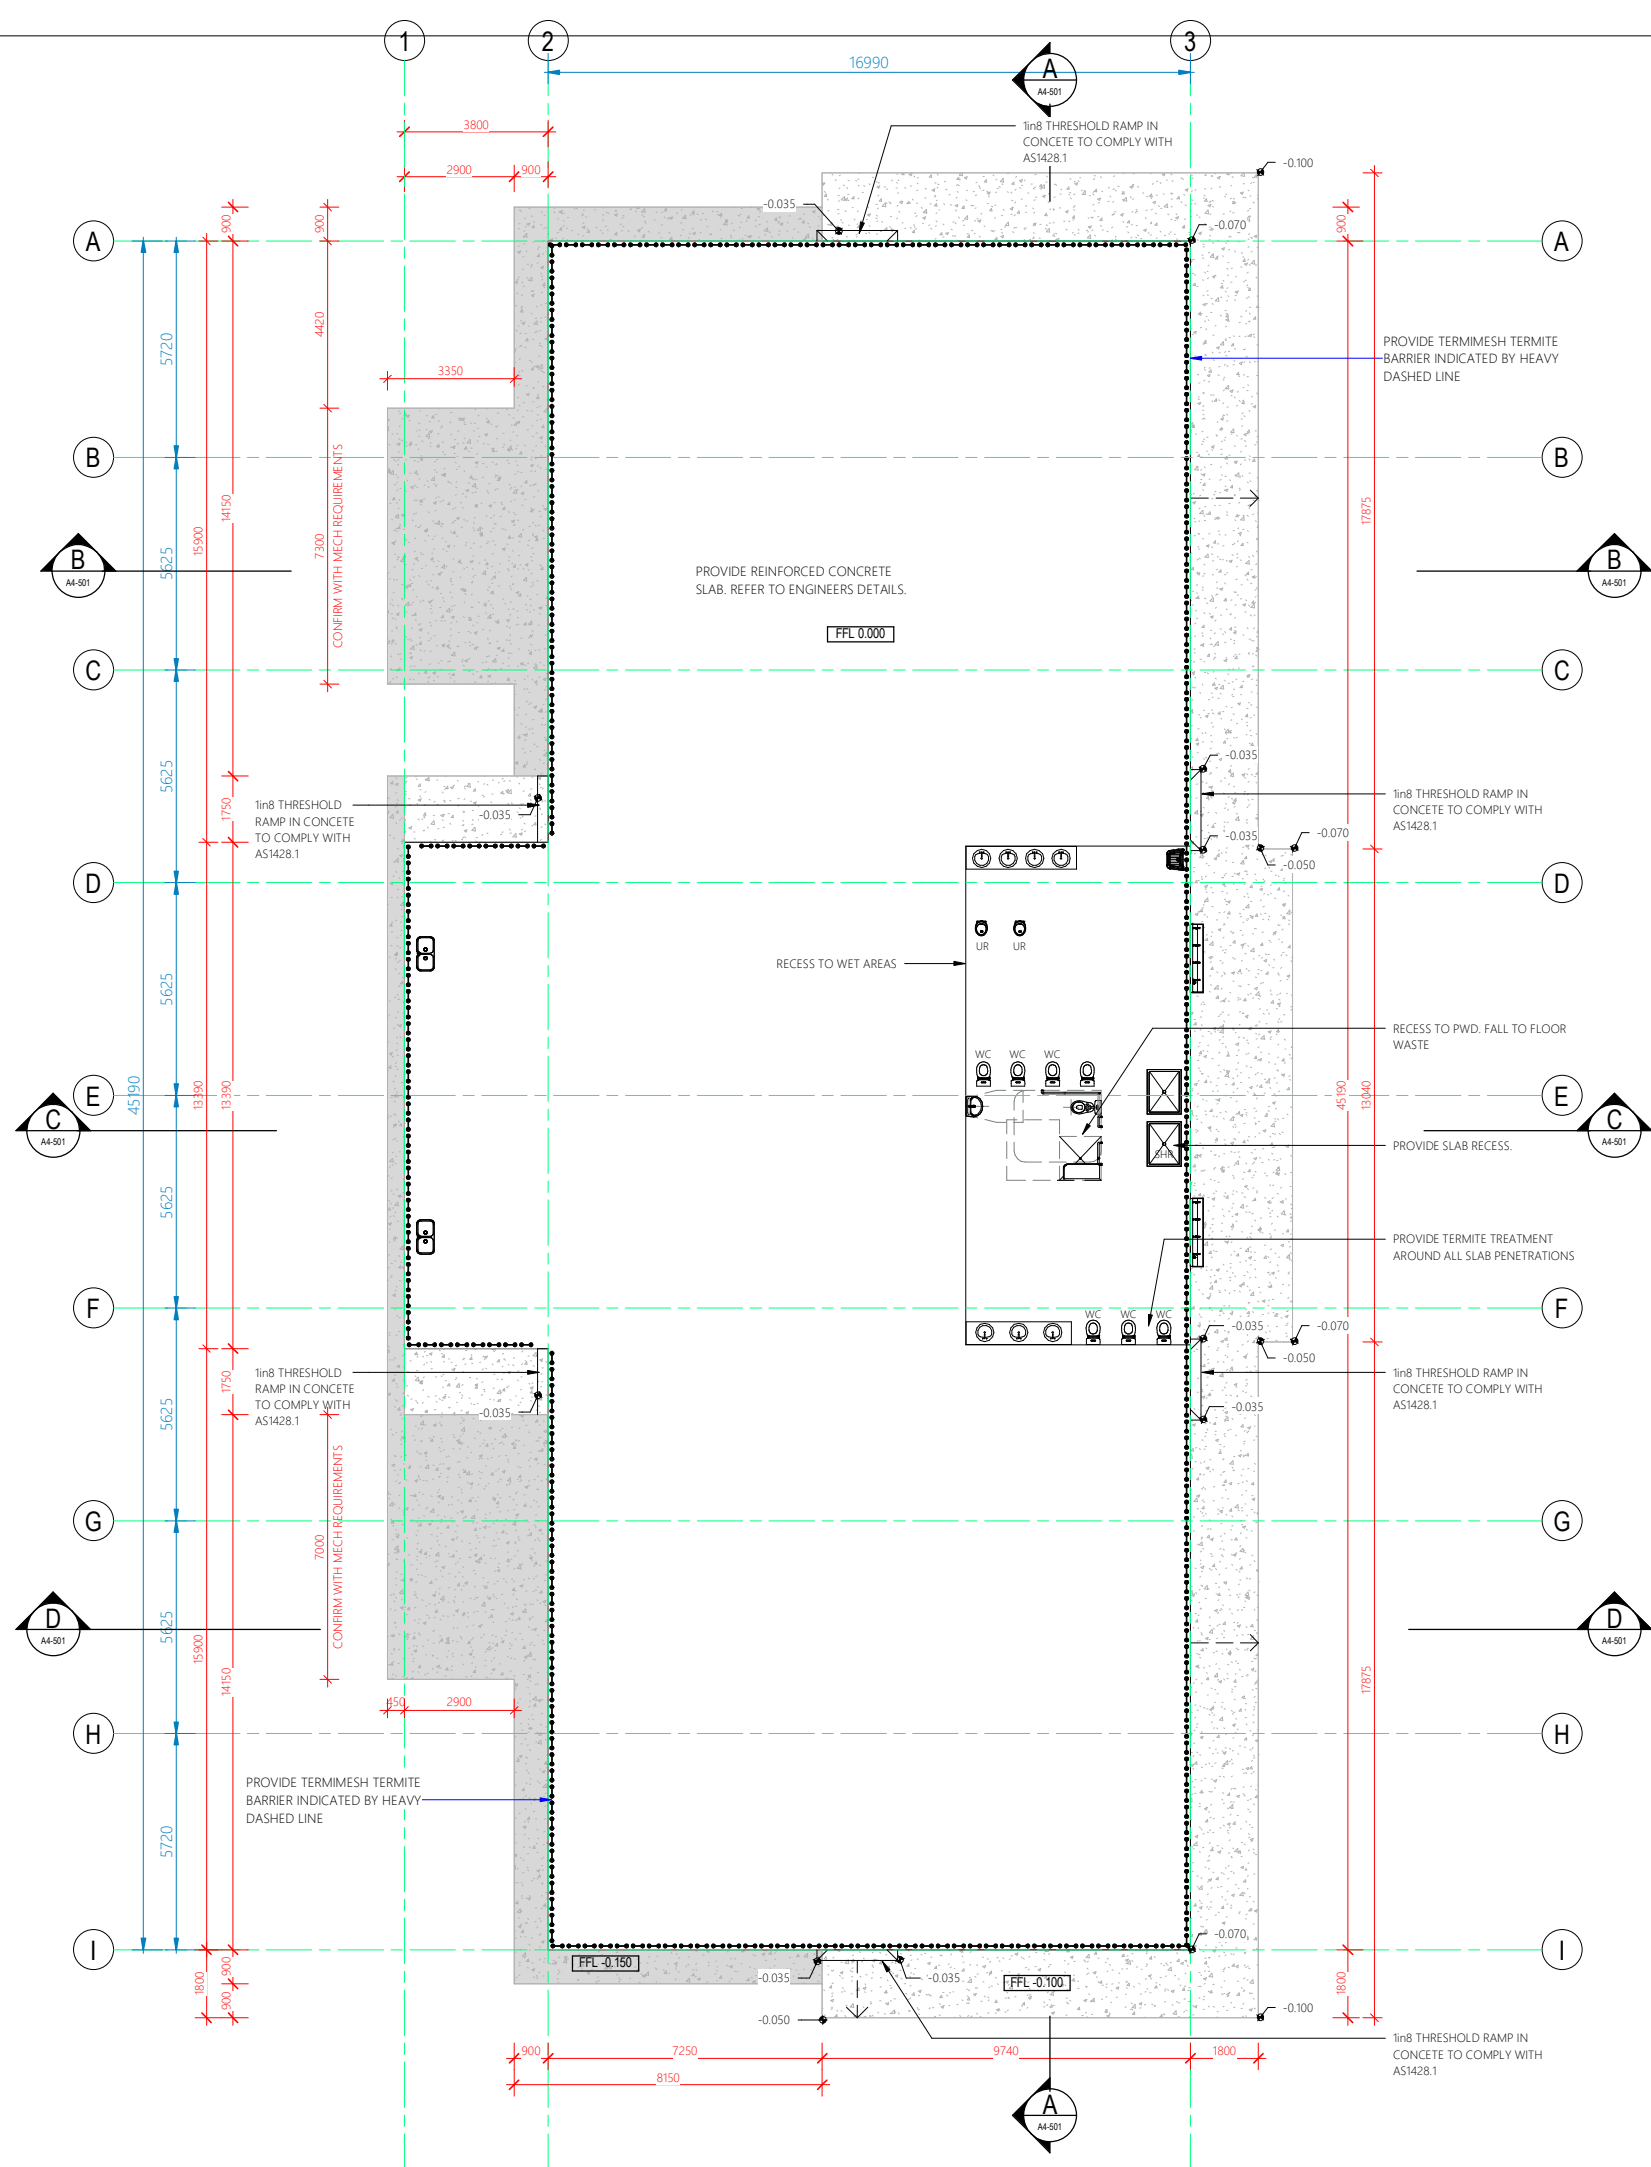

REVISIONS		
Rev	Description	Date
T1	TENDER ISSUE	12.03.2026

DO NOT SCALE THIS DRAWINGS

 

TENDER ISSUE

Client

 stanwell

Project Details

OFFICE REFURBS

Address

STANWELL POWER STATION

Drawing Title

PROPOSED SLAB SETOUT PLAN

 **designelements**
BUILDING DESIGNERS

0483 988 655 M
info@designelements.com.au E
QBCC No: 1247120 BDAQ No: 0001677

Scale: 1 : 100 Rev: **T1**
Date: MAR 2026
Drawn: Author

Project No: Drawing No:
25_003 A4-301



Slab Plan


1 : 100

0 5m 1:100

CONFIRM EXISTING GRID SETOUT ON SITE


NEW CEILING INSULATION THROUGHOUT
SHADED AREA - REFER SPEC

- CEILING LEGEND
- 1200 x 600 APEX ACOUSTIC CEILING TILES (OR APPROVED EQUAL - NEW TILES THROUGH RENOVATED AREA)
 - INSULATED PANELING WITH FLAT COLORBOND SOFFIT LINING
 - INSULATION ABOVE CEILING TILES

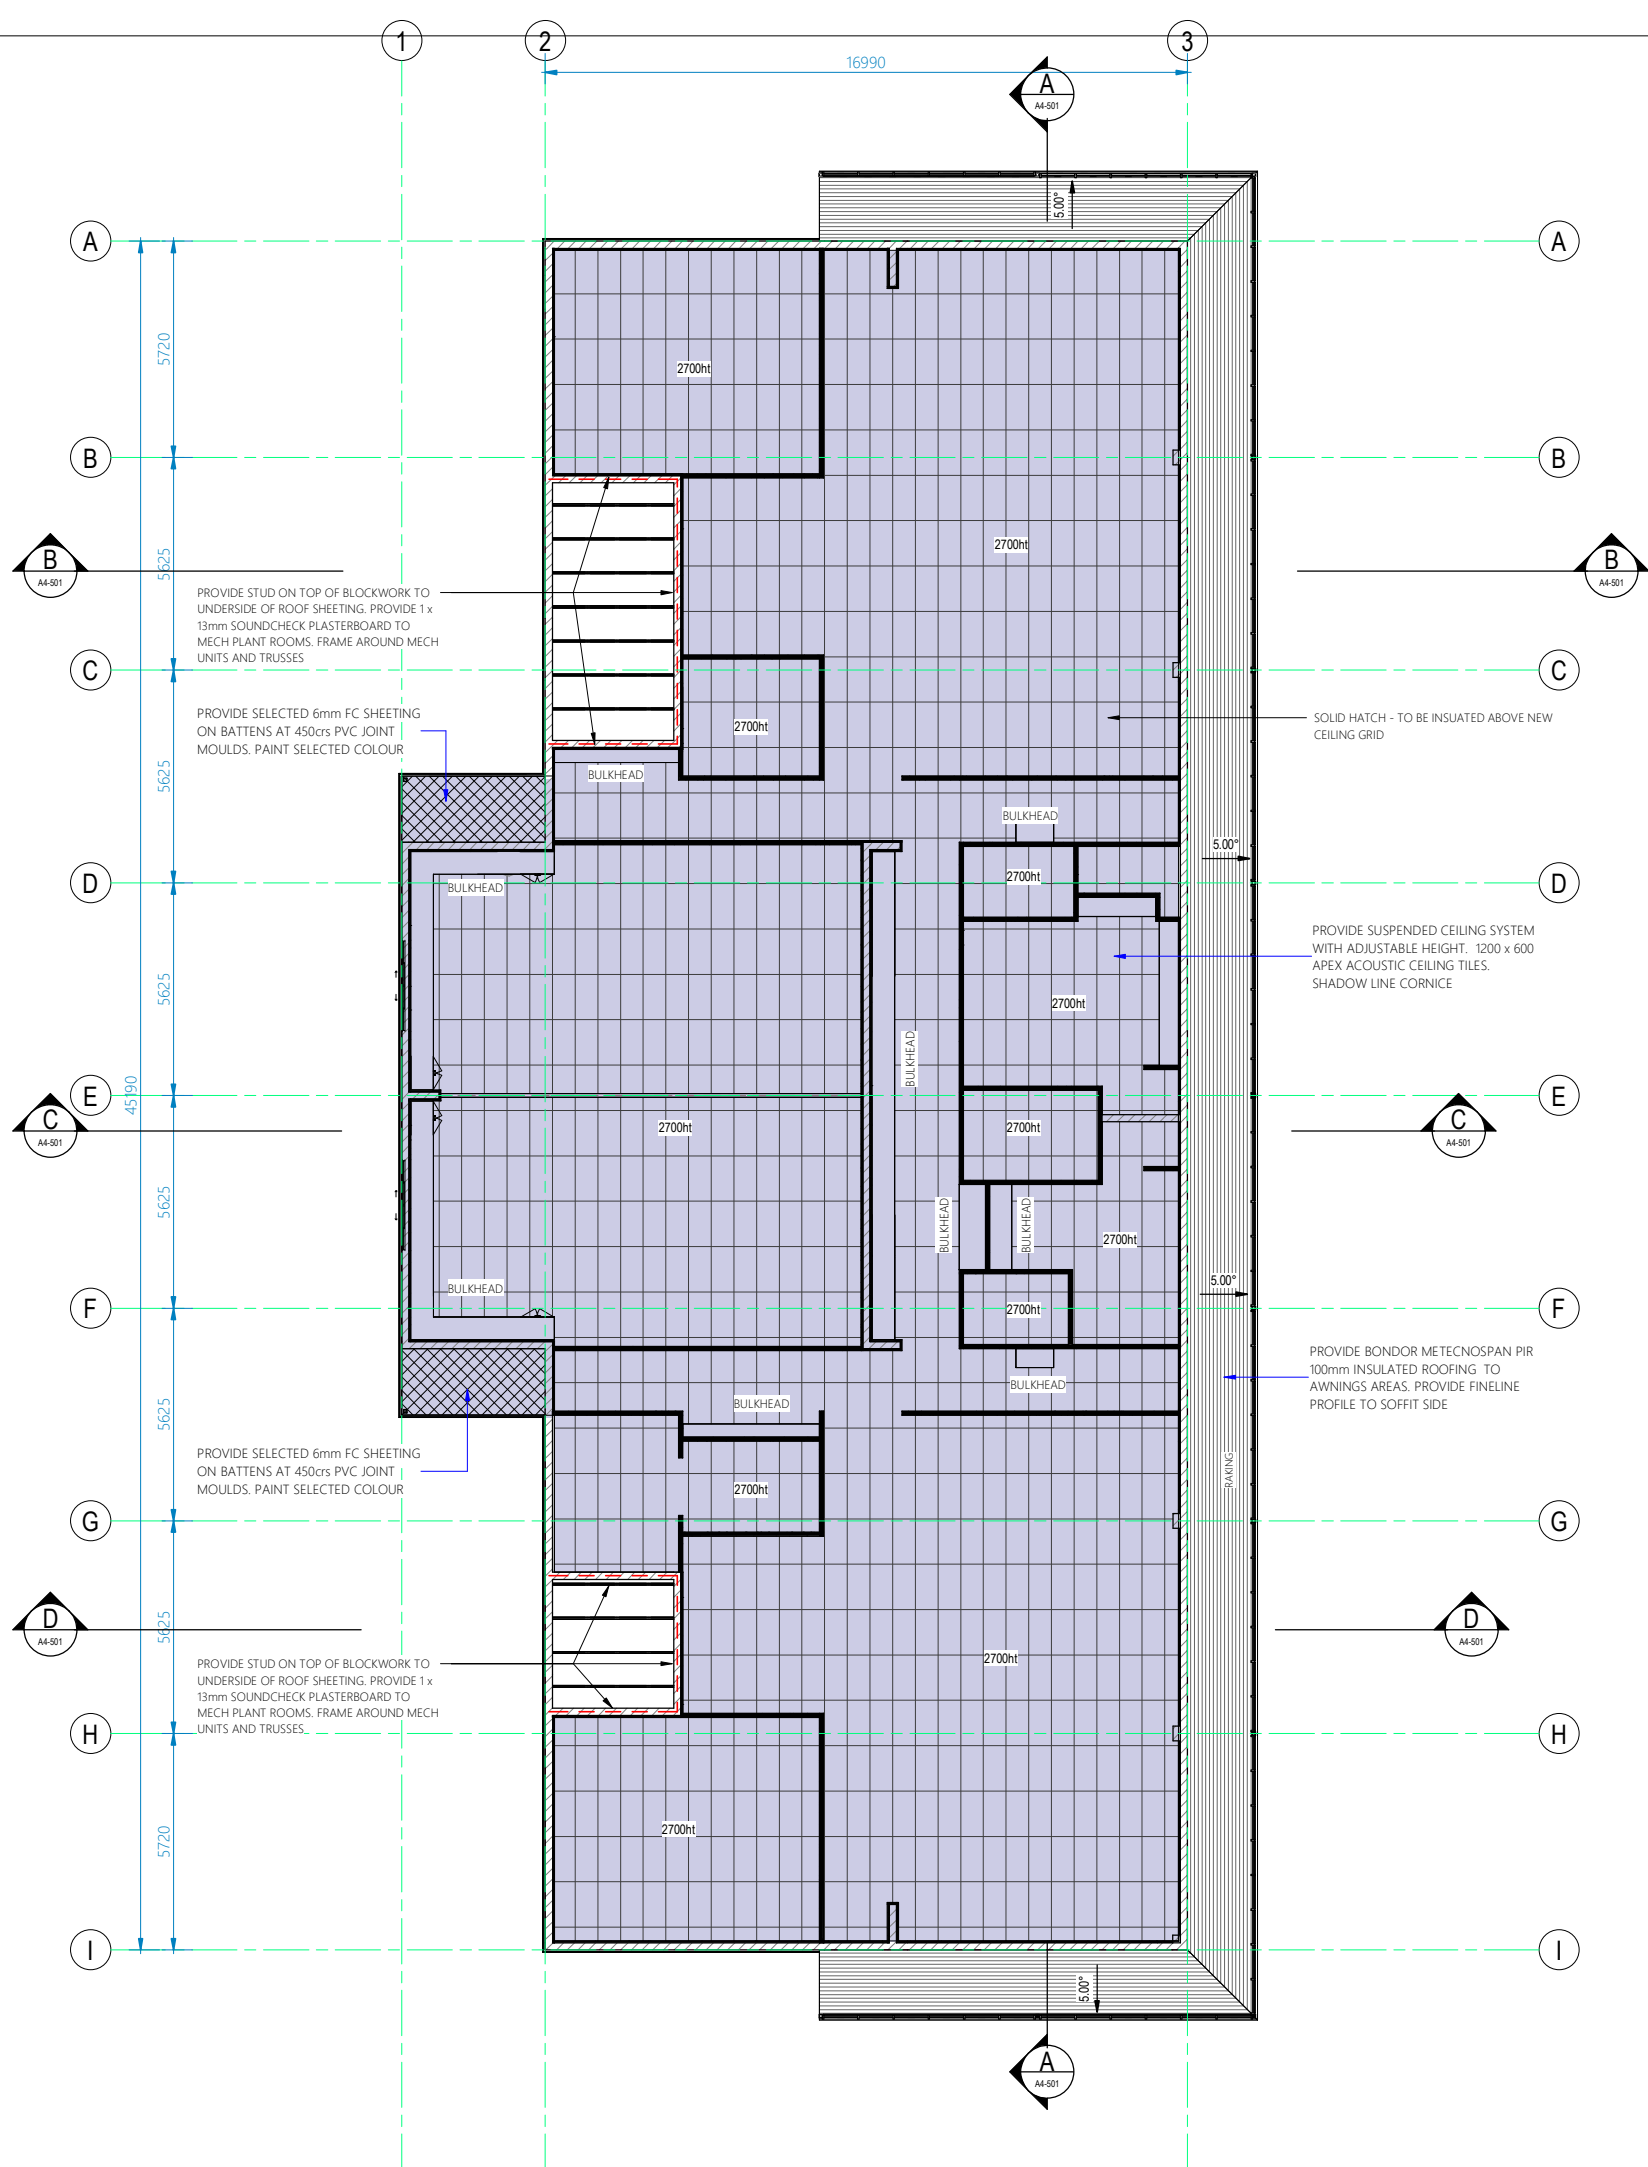

REVISIONS		
Rev	Description	Date
T1	TENDER ISSUE	12.03.2026

DO NOT SCALE THIS DRAWINGS

 


TENDER ISSUE



Project Details
OFFICE REFURBS
Address
STANWELL POWER STATION
Drawing Title
PROPOSED CEILING PLAN




Scale: 1 : 100	Rev: T1
Date: MAR 2026	
Drawn: Author	
Project No: 25_003	Drawing No: A4-303

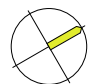


Ceiling Plan



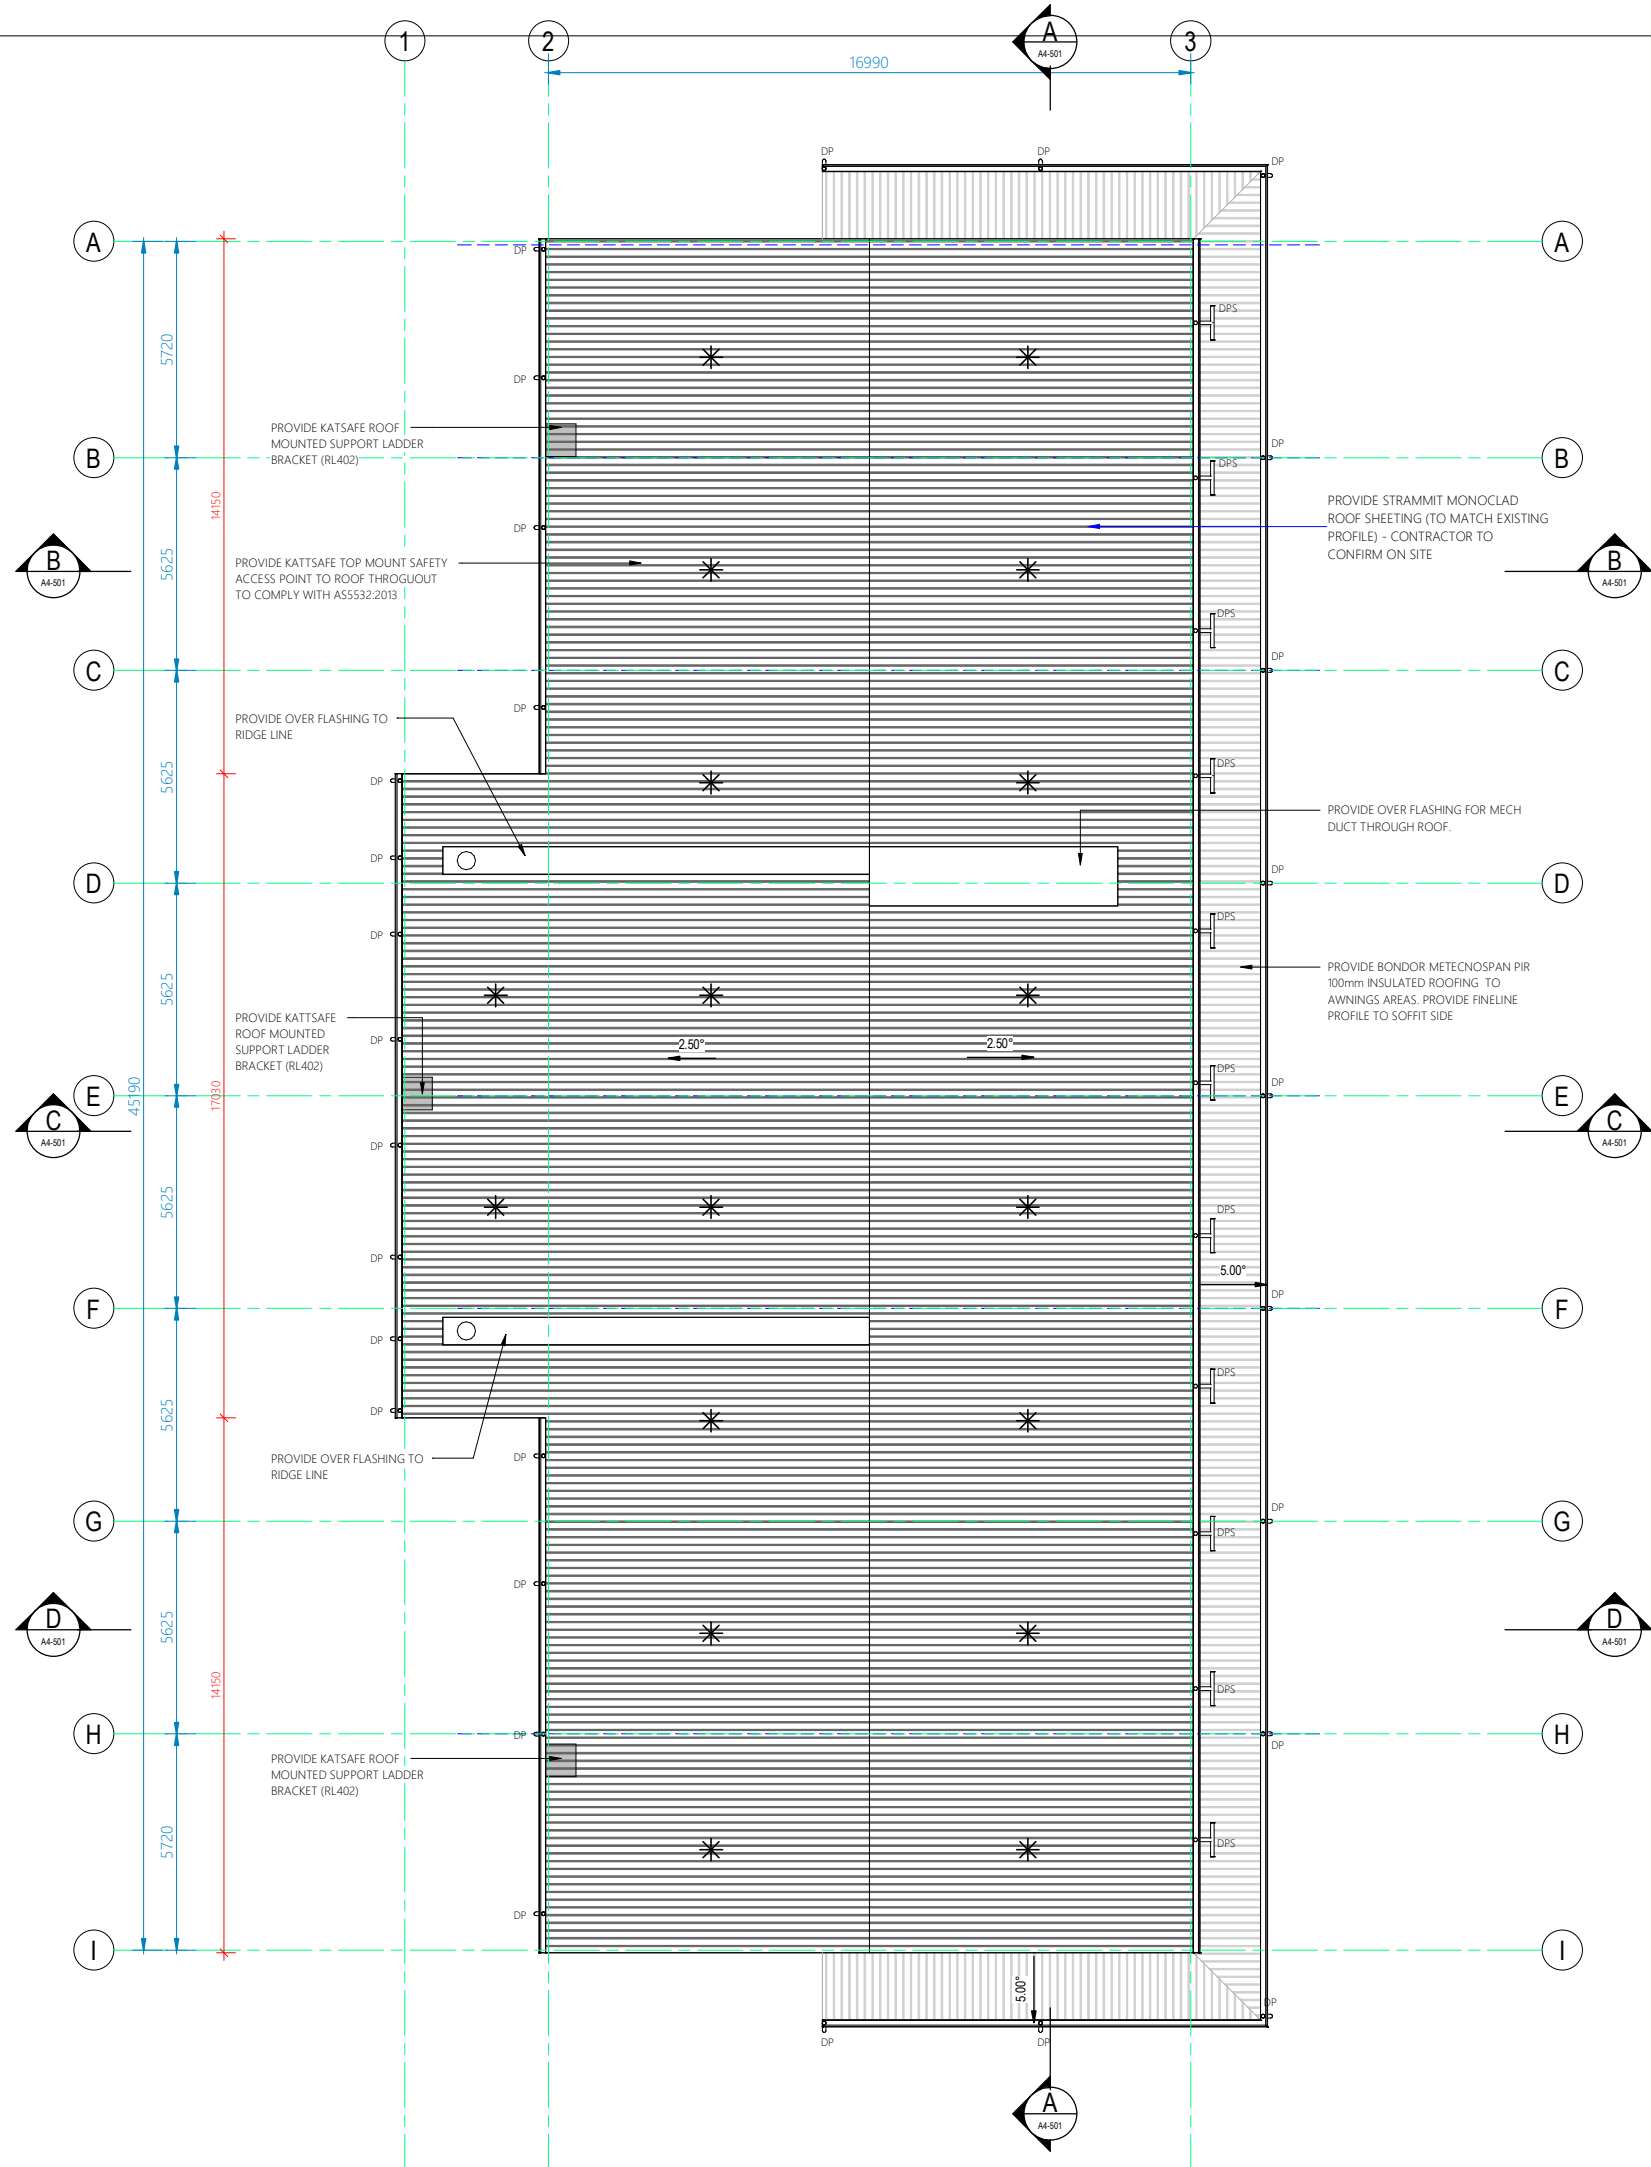

Proposed Roof Plan

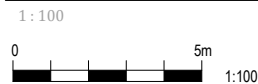

REVISIONS		
Rev	Description	Date
T1	TENDER ISSUE	12.03.2026

DO NOT SCALE THIS DRAWINGS



TENDER ISSUE

Client



Project Details

OFFICE REFURBS

Address

STANWELL POWER STATION

Drawing Title

PROPOSED ROOF PLAN


BUILDING DESIGNERS









0483 988 655 M
info@dezignelements.com.au E

QBCC No: 1247120 BDAQ No: 0001677


Scale: 1 : 100 Rev: T1
Date: MAR 2026
Drawn: Author

Project No: 25_003 Drawing No: A4-304



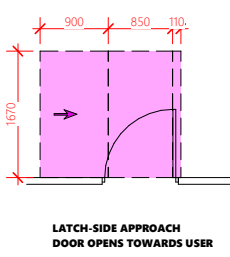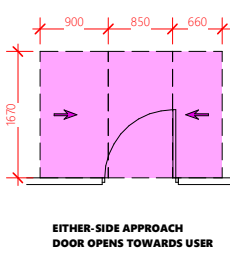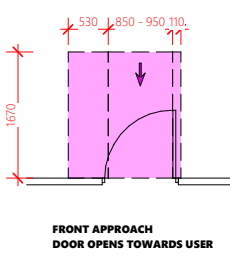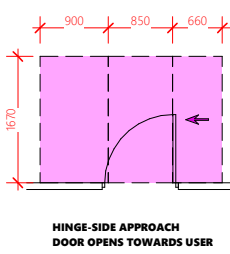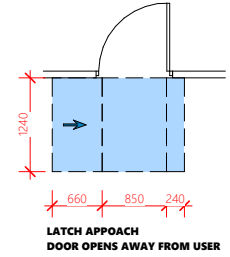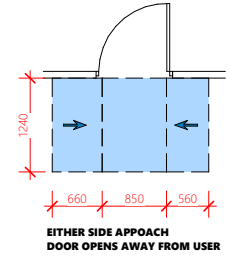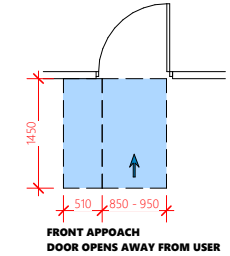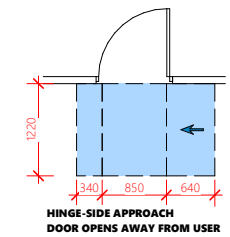

AS1428.1 - Clearance Plan

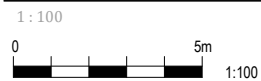

REVISIONS

Rev	Description	Date
T1	TENDER ISSUE	12.03.2026

DO NOT SCALE THIS DRAWINGS



TENDER ISSUE

Client

Project Details

OFFICE REFURBS

Address

STANWELL POWER STATION


Drawing Title

AS1428.1 - CLEARANCE PLAN

0483 988 655 M
info@designelements.com.au E
QBCC No: 1247120 BDAQ No: 0001677

Scale: As indicated	Rev: T1
Date: MAR 2026	
Drawn: Author	
Project No: 25_003	Drawing No: A4-305



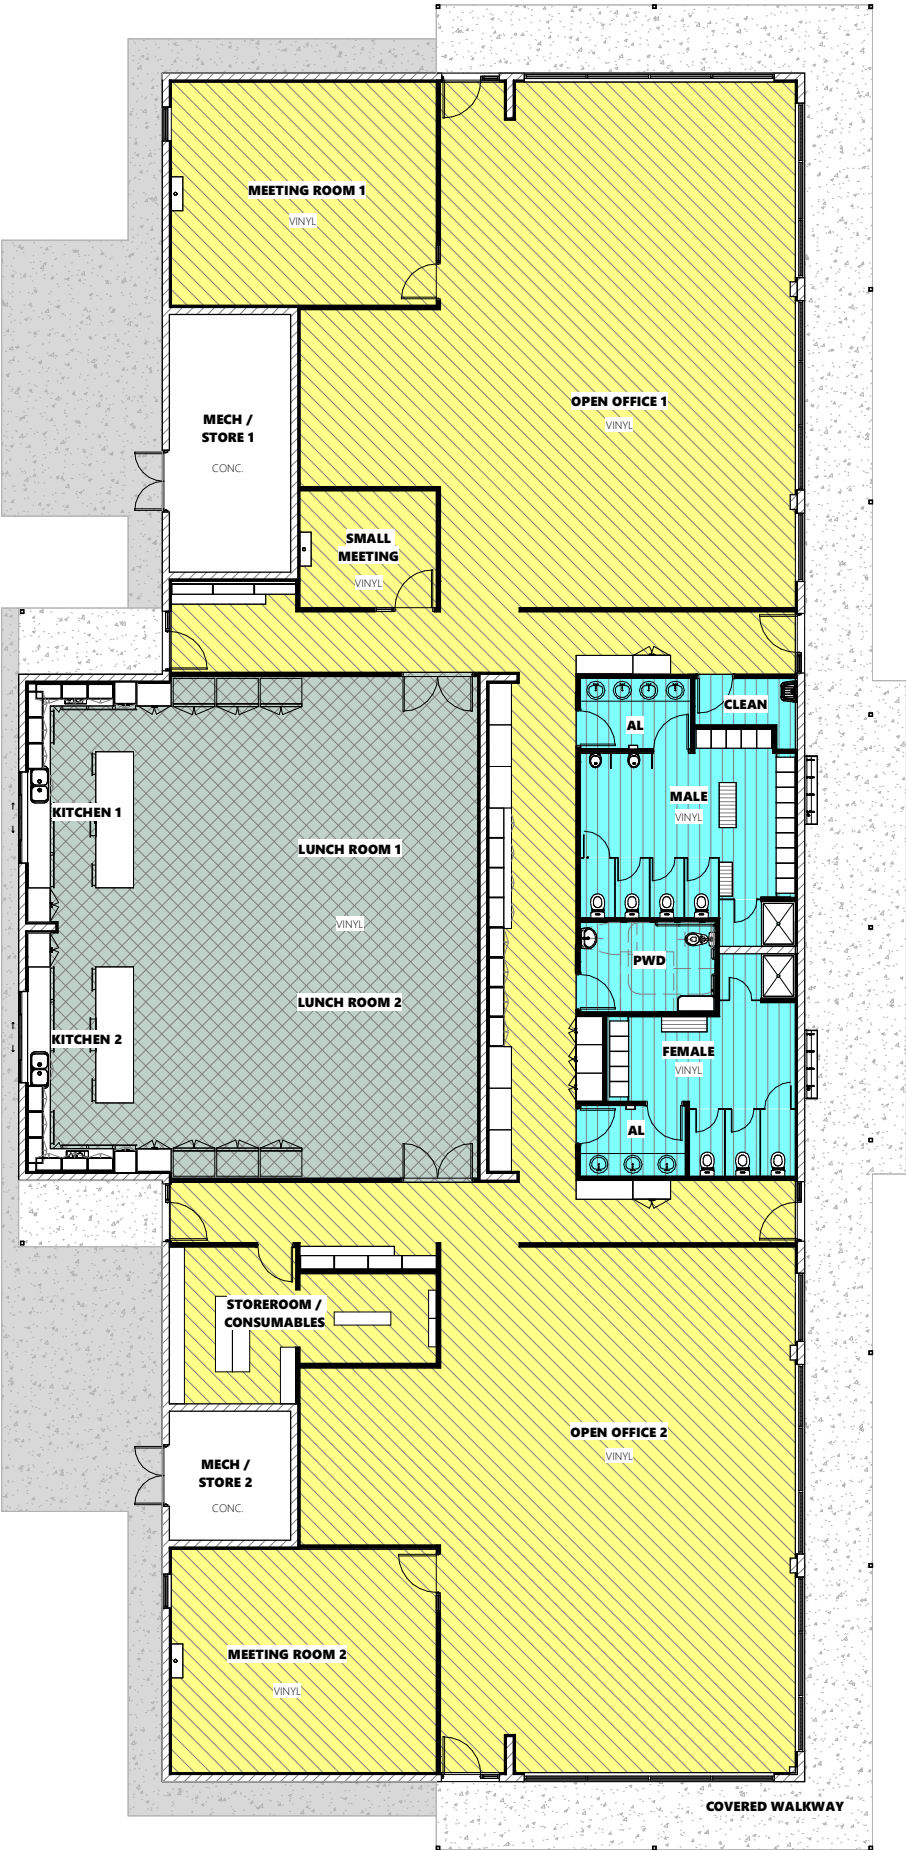

Floor Covering Plan



REVISIONS		
Rev	Description	Date
T1	TENDER ISSUE	12.03.2026

DO NOT SCALE THIS DRAWINGS

FLOOR COVERING PLAN

	SHEET VINYL - TYPE 1 100mm FEATHER EDGE SKIRTING - BLACK
	SHEET VINYL - TYPE 2 100mm COVERED UP SKIRTING
	SHEET VINYL - TYPE 3 100mm FEATHER EDGE SKIRTING - BLACK

TENDER ISSUE

Client

Project Details

OFFICE REFURBS

Address

STANWELL POWER STATION

Drawing Title

FLOOR COVERING PLAN


0483 988 655 M
info@dezignelements.com.au E
QBCC No: 1247120 BDAQ No: 0001677

Scale:	1 : 100	Rev:	T1
Date:	MAR 2026		
Drawn:	Author		
Project No:	25_003	Drawing No:	A4-306



REVISIONS		
Rev	Description	Date
T1	TENDER ISSUE	12.03.2026

DO NOT SCALE THIS DRAWINGS

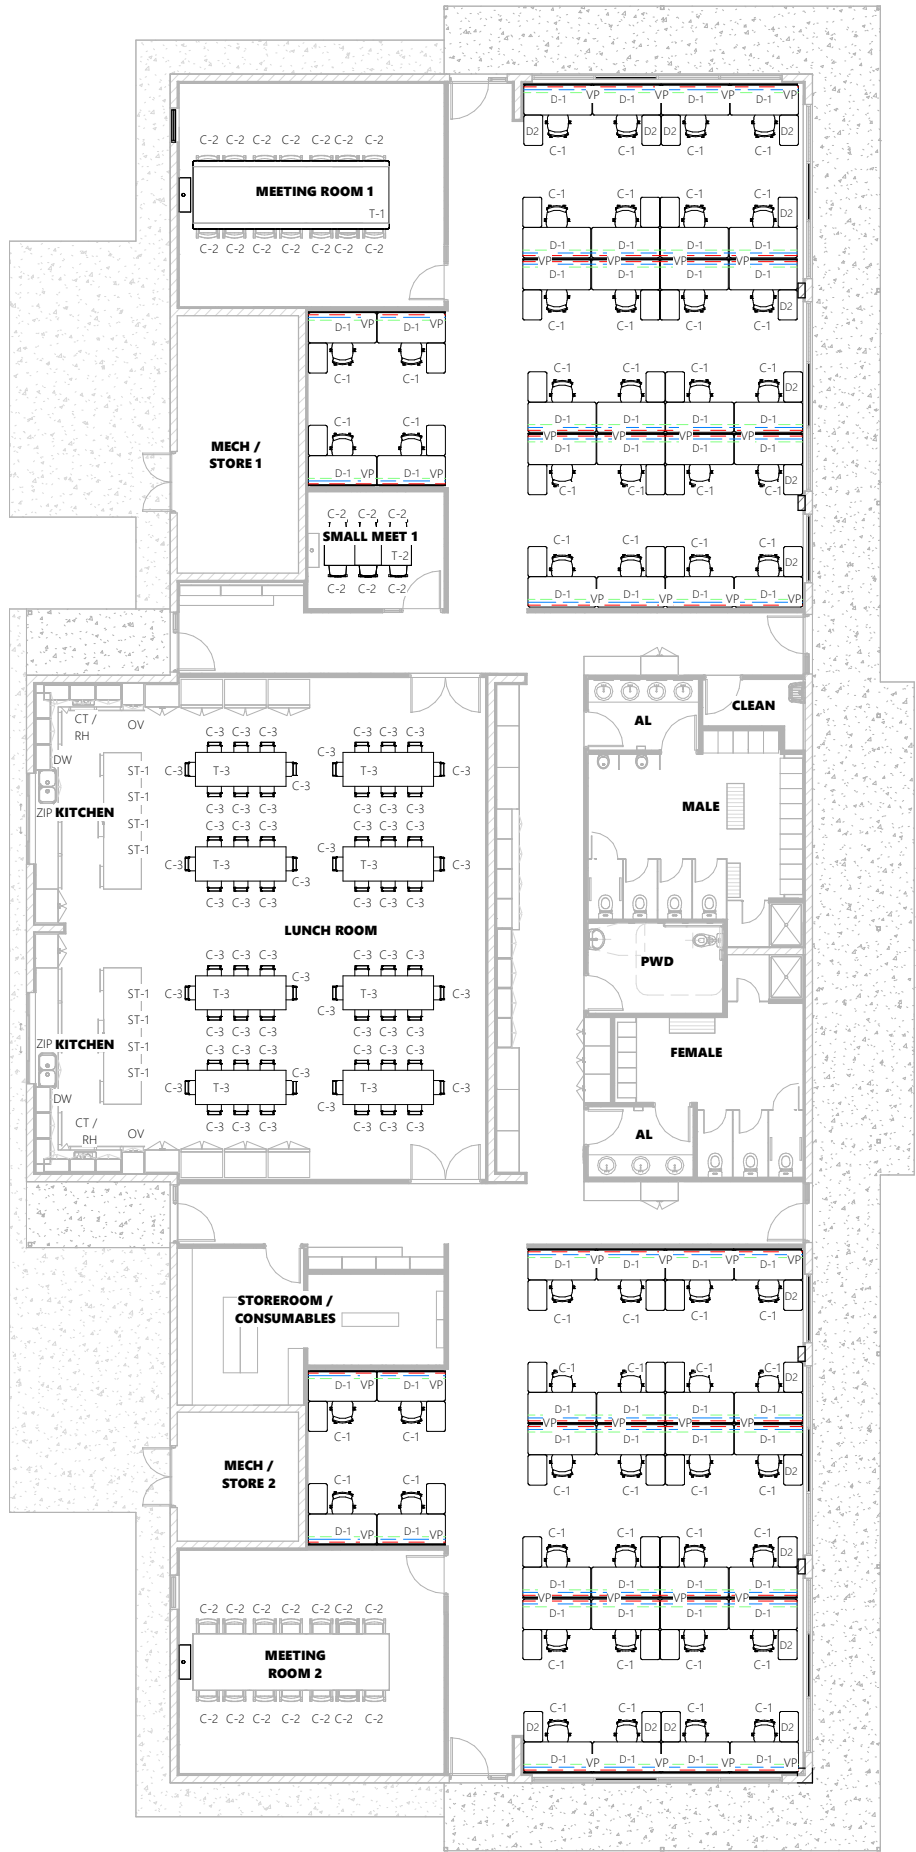

FURNITURE & APPLIANCE SCHEDULE

CODE	TYPE	SIZE	QTY	SUPPLIER
D-1	DESK	1800 x 800	56	SCHIAVELLA CLIMATE RECTANGLE WORK STATION
D-2	DESK	800 x 500	56	SCHIAVELLA CLIMATE RECTANGLE WORK STATION RETURN
C-1	CHAIR (workstation)	-	56	SCHIAVELLA HIGH BACK CHAIR BY OKAMURA, BLACK BODY, BLACK MESH BLACK AND UPHOLSTERED SEAT
C-2	CHAIR (meeting)	-	34	SHIBUSA HIGH BACK BY OKAMURA (BLACK)
C-3	CHAIR (dining)	-	64	MEXICA CHAIR (plywood with natural oak finish / no arms)
T-1	TABLE (large meet)	1800 x 5200	2	MEETING TABLE EONA - 25mm LAMINEX CHARCOAL NATURAL FINISH WITH ABS EDGING
T-2	TABLE (small meet)	900 x 2000	1	MEETING TABLE EONA - 25mm LAMINEX CHARCOAL NATURAL FINISH WITH ABS EDGING
T-3	TABLE (dining)	900 x 2400	8	JOGGLE TABLE BY IMPOSTER - 25mm LAMINEX WHITE. STEEL FRAME WHITE POWDERCOAT
ST-1	STOOL (kitchen)	-	8	MEXICA STOOL (plywood with natural oak finish)
—	CABLE CATCHER	AS REQUIRED	-	SCHIAVELLA
- - -	CABLE ARTICULATOR	AS REQUIRED	-	SCHIAVELLA
- - -	CABLE CHANNEL	AS REQUIRED	-	SCHIAVELLA
VP	VIDE SUSP. PANEL	1800 (600mm ABOVE DESK)	40	SCHIAVELLA - PROVIDE SUSPENDED BRACKETS TO EACH DESK
OV	OVEN	598 x 596	2	FISHER & PAYKEL 60CM SERIES 7 CONTEMPORARY PYROLYTIC OVEN 9 FUNCTION - BLACK
DW	DISHWASHER	597 x 600	2	FISHER & PAYKEL SERIES 7 CONTEMPORARY DISHWASHER - BLACK STEEL
CT	COOK TOP	600	2	FISHER & PAYKEL 60CM SERIES 7 4 ZONE INDUCTION COOKTOP 2 SMARTZONES - BLACK
RH	RANGE HOOD	600	2	FISHER & PAYKEL 60CM SERIES 7 INTEGRATED INSERT WALL RANGEHOOD EXTERNAL MOTOR - STEEL GLASS
ZIP	ZIP UNIT	-	2	HYDROTAP G5 BCSHA100 5-IN-1 CLASSIC TAP WITH CLASSIC MIXER BLACK

Proposed Furniture Layout



TENDER ISSUE

Client

Project Details

OFFICE REFURBS

Address

STANWELL POWER STATION

Drawing Title

FURNITURE LAYOUT

0483 988 655 M
info@dezignelements.com.au E
QBCC No: 1247120 BDAQ No: 0001677

Scale: 1 : 100 Rev: T1
Date: MAR 2026
Drawn: Author


Project No: Drawing No:
25_003 A4-307

12/03/2026 7:52:13 PM

REVISIONS


Rev	Description	Date
T1	TENDER ISSUE	12.03.2026

DO NOT SCALE THIS DRAWINGS

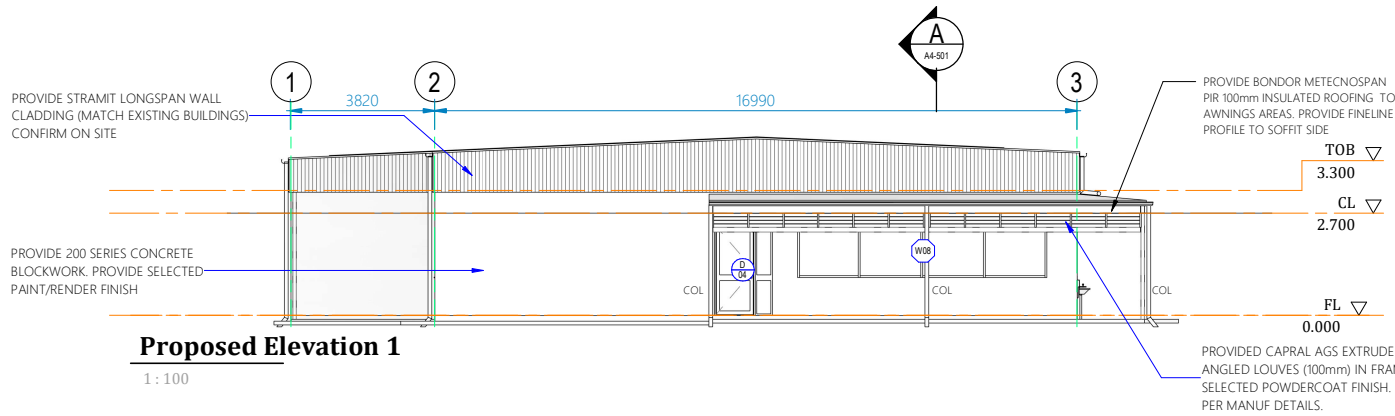


Proposed Elevation 1

1 : 100

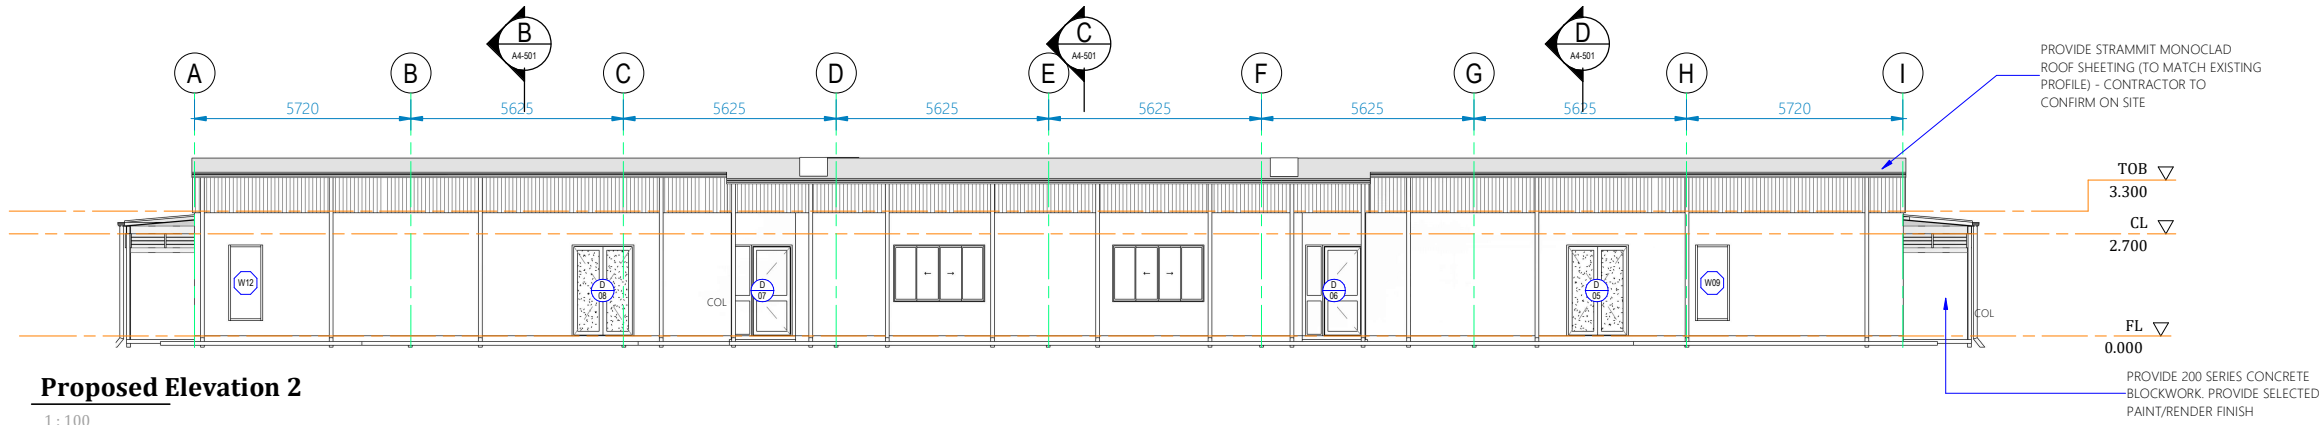


Proposed Elevation 2

1 : 100

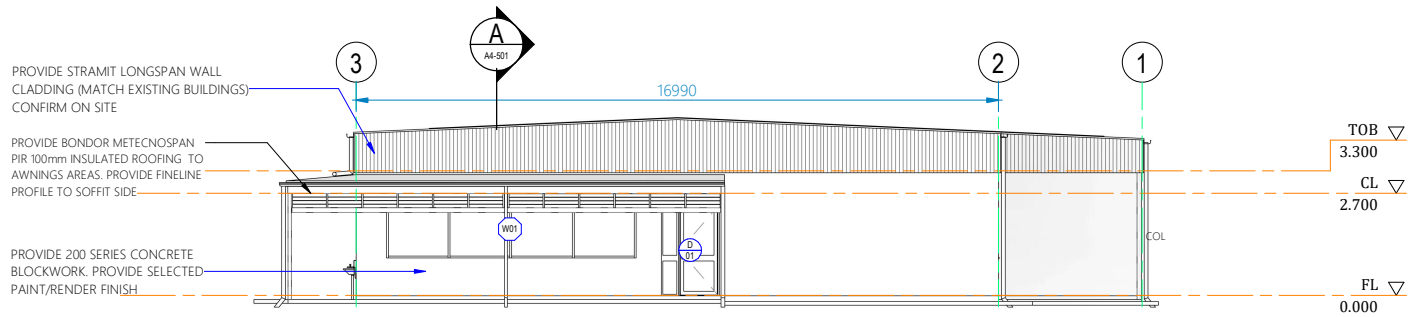

Proposed Elevation 3

1 : 100

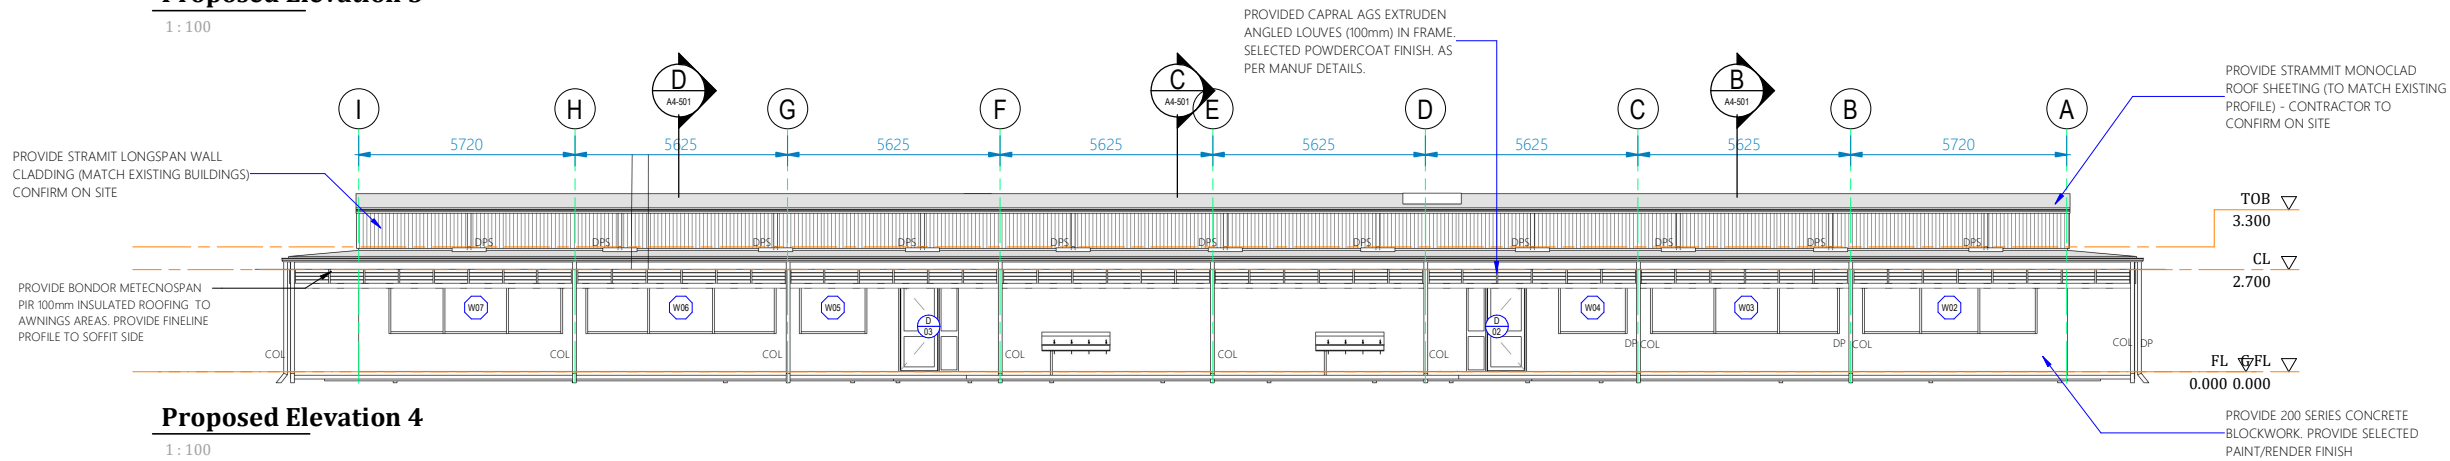

Proposed Elevation 4

1 : 100

TENDER ISSUE



Project Details

OFFICE REFURBS

Address
STANWELL POWER STATION

Drawing Title
PROPOSED ELEVATIONS



0483 988 655 M
info@deignelements.com.au E
QBCC No: 1247120 BDAQ No: 0001677

Scale: 1 : 100 Rev:
Date: MAR 2026 T1
Drawn: Author


Project No: Drawing No:

25_003 A4-401

REVISIONS


Rev	Description	Date
T1	TENDER ISSUE	12.03.2026

DO NOT SCALE THIS DRAWINGS

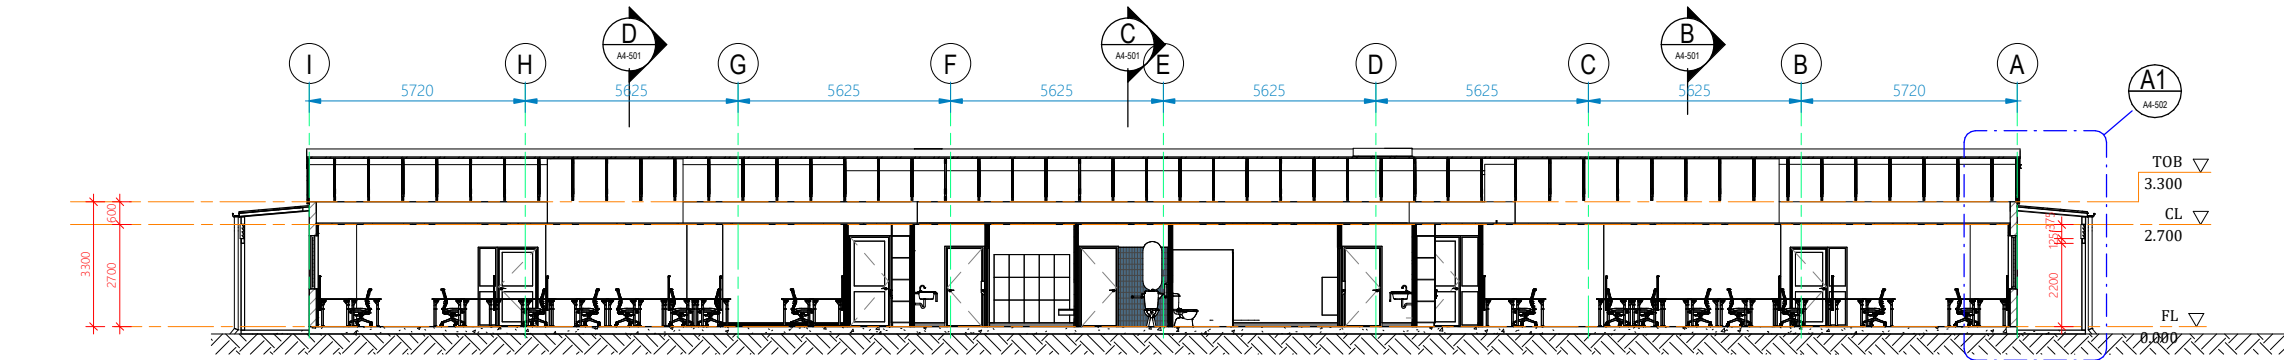


SECTION A

1 : 100

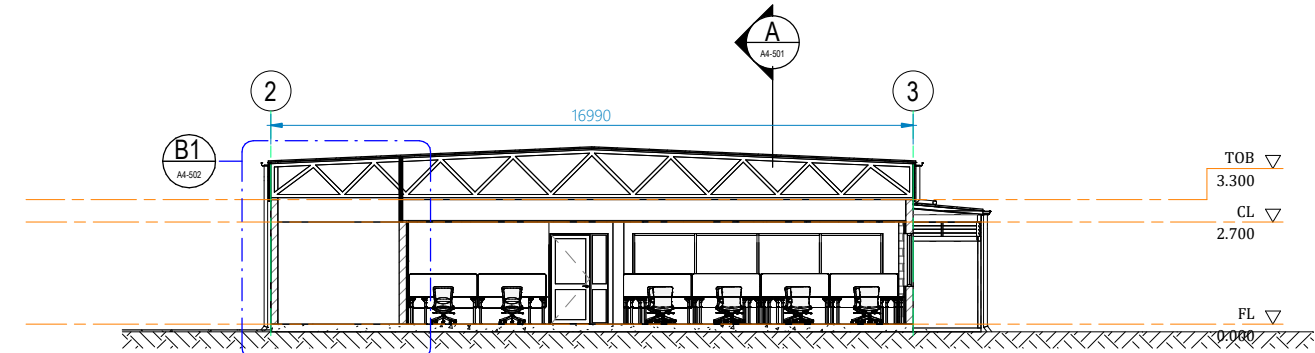


SECTION B

1 : 100

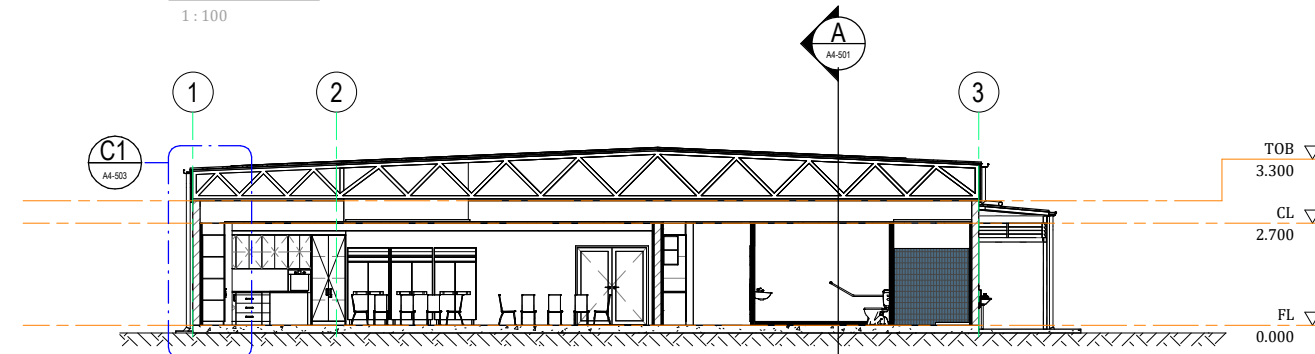

SECTION C

1 : 100

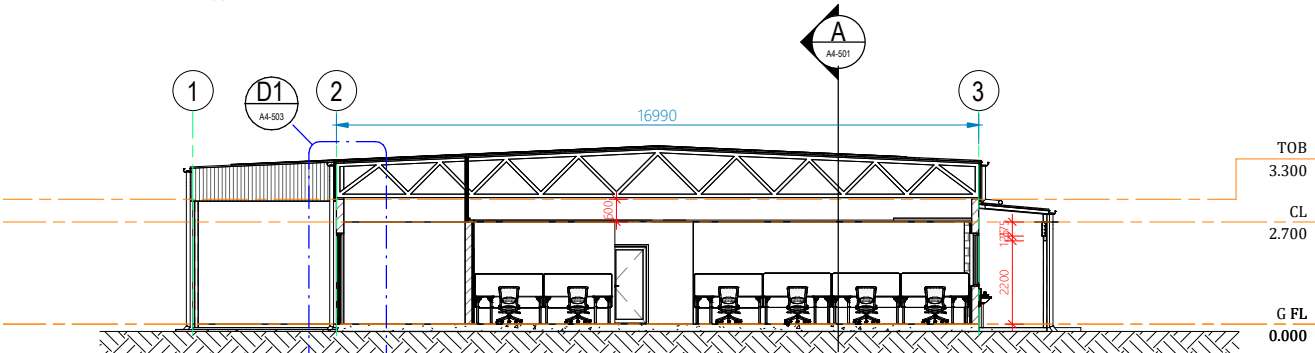

SECTION D

1 : 100

TENDER ISSUE



Project Details

OFFICE REFURBS

Address

STANWELL POWER STATION

Drawing Title

PROPOSED SECTIONS



0483 988 655 M

info@dezi nelements.com.au E

QBCC No: 1247120 BDAQ No: 0001677

Scale: 1 : 100 Rev:

Date: MAR 2026 T1

Drawn: Author


Project No: Drawing No:

25_003 A4-501



REVISIONS		
Rev	Description	Date
T1	TENDER ISSUE	12.03.2026

DO NOT SCALE THIS DRAWINGS

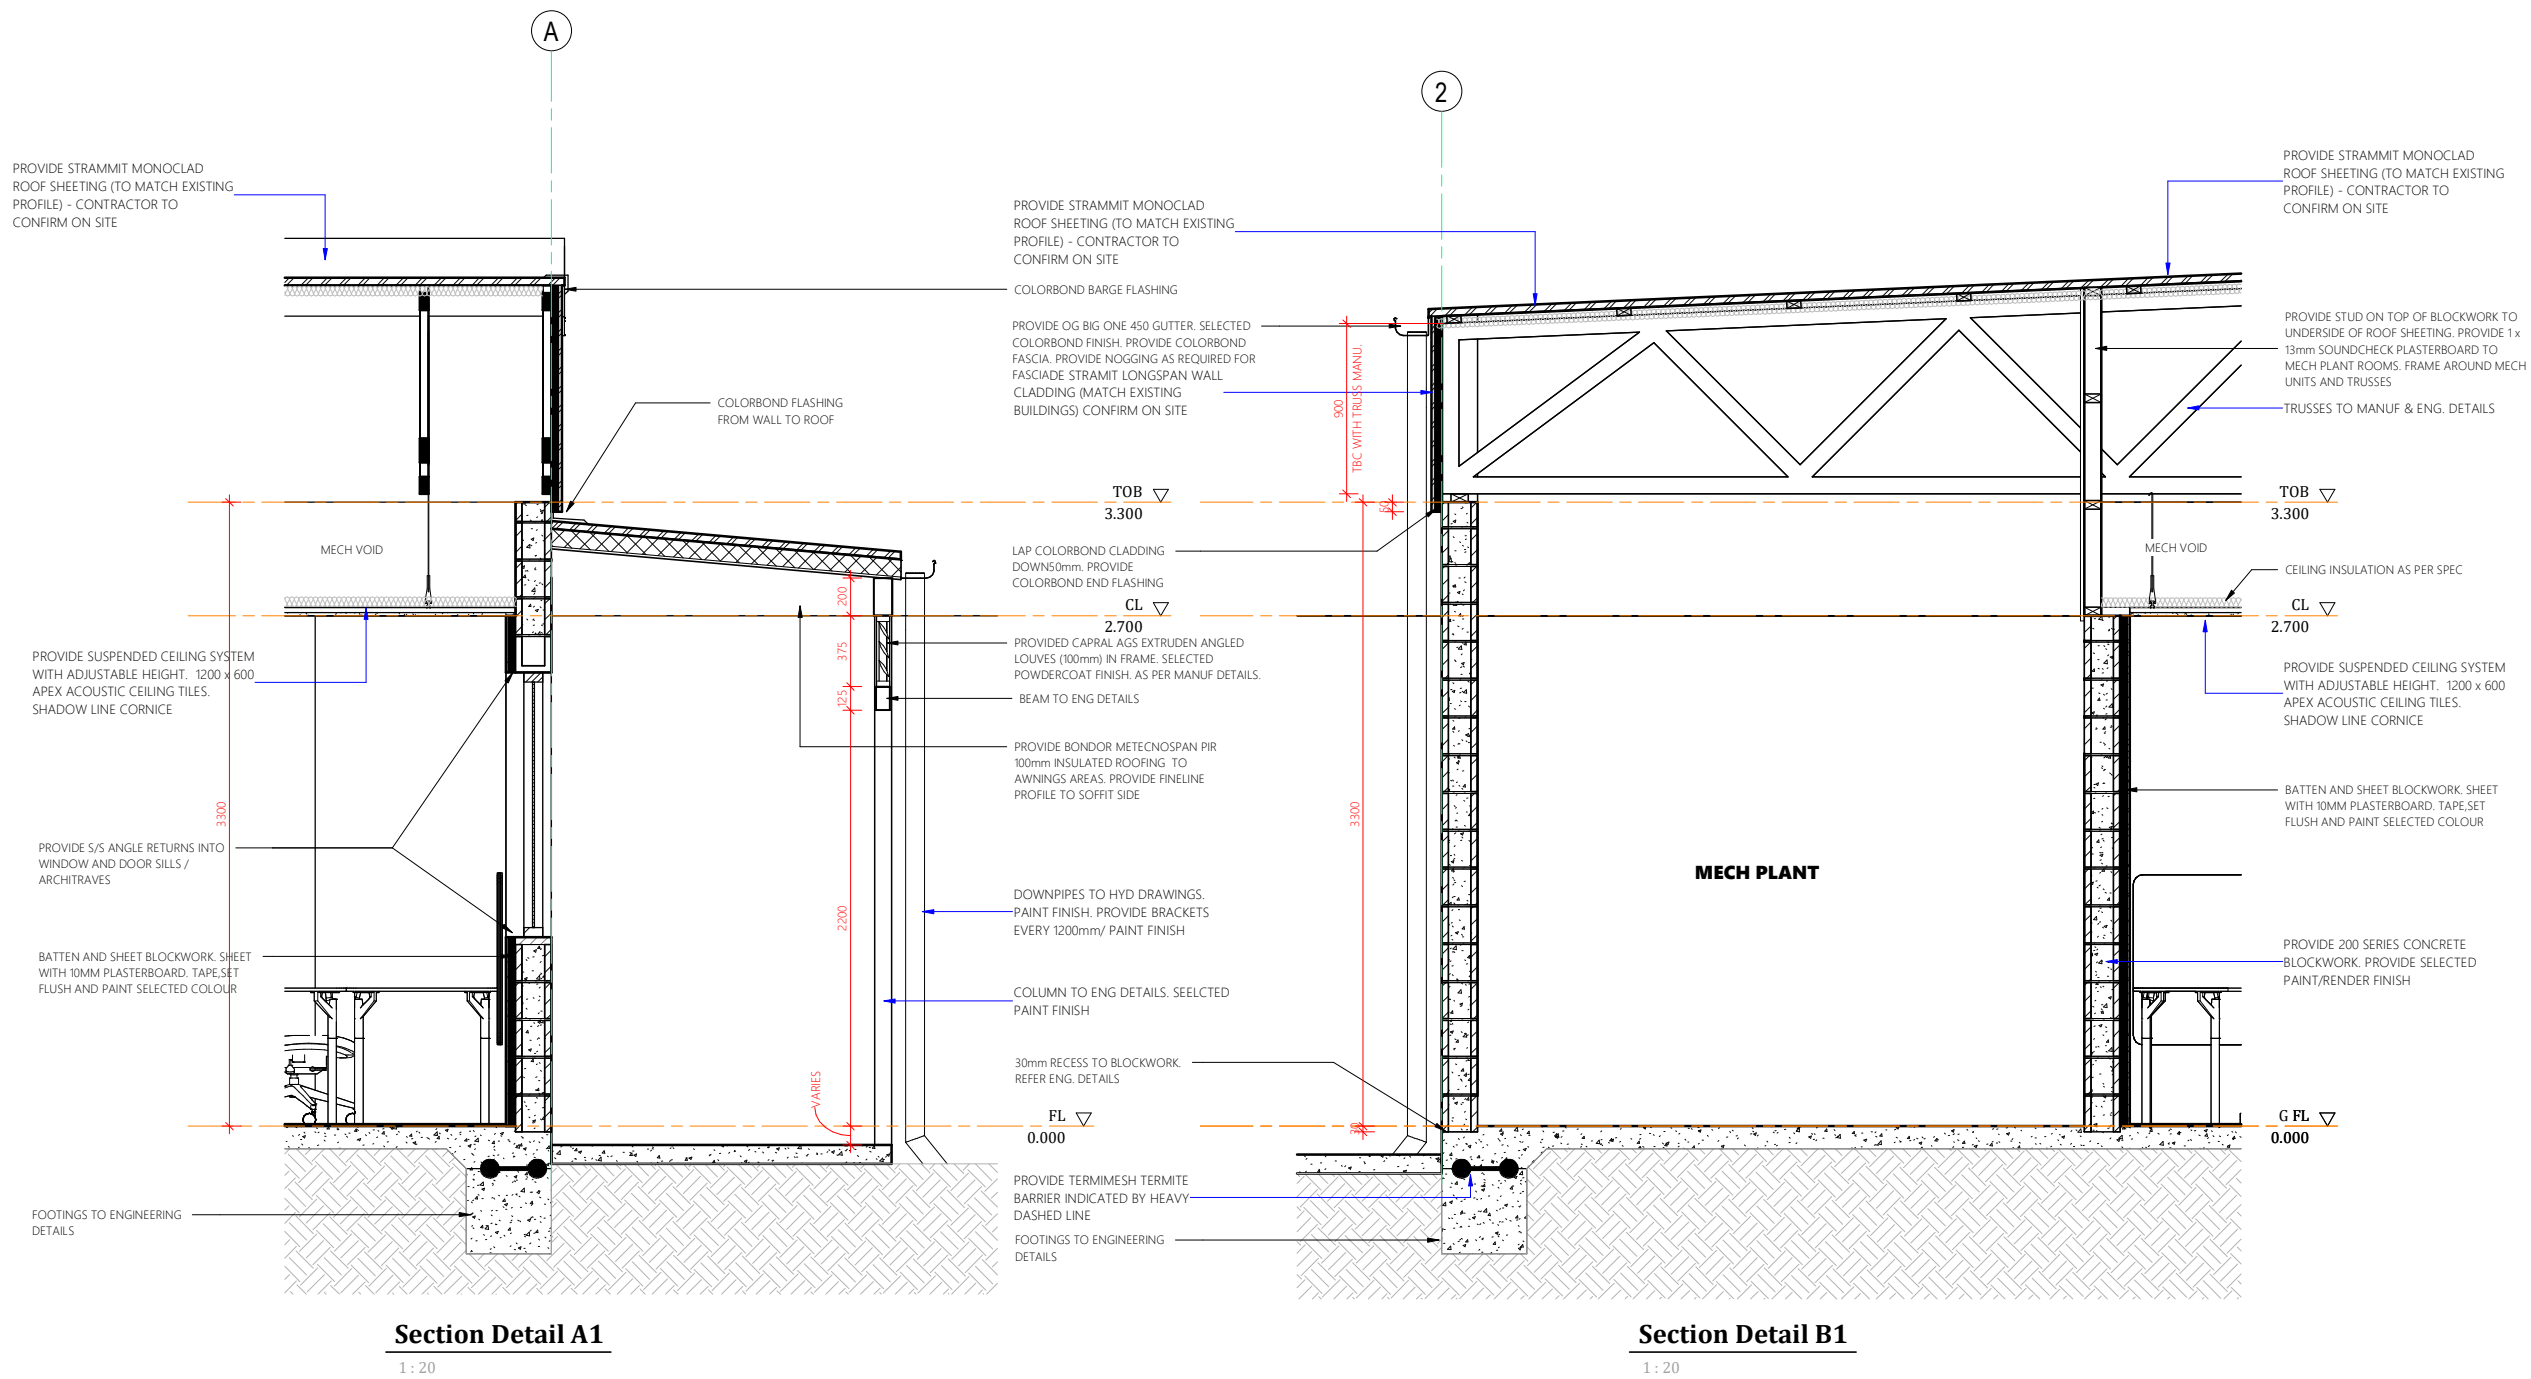

TENDER ISSUE



Project Details
OFFICE REFURBS
Address
STANWELL POWER STATION
Drawing Title
PROPOSED SECTION DETAILS

dezinelements
BUILDING DESIGNERS

0483 988 655 M
info@dezi

QBCC No: 1247120 BDAQ No: 0001677


Scale: 1 : 20 Rev: T1
Date: MAR 2026
Drawn: Author

Project No: Drawing No:
25_003 A4-502

12/03/2026 7:52:33 PM


REVISIONS		
Rev	Description	Date
T1	TENDER ISSUE	12.03.2026

DO NOT SCALE THIS DRAWINGS

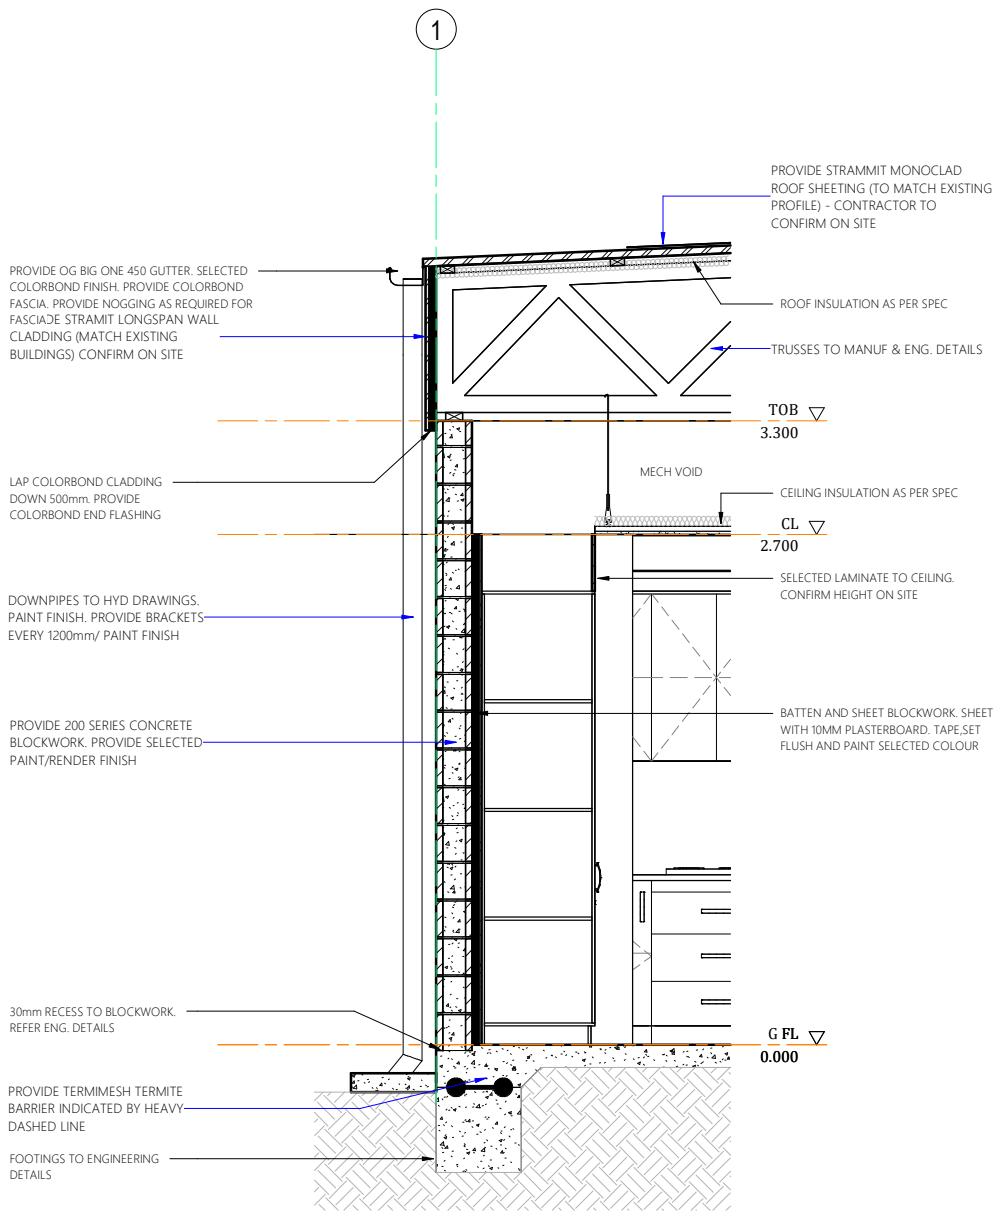


Section Detail C1

1 : 20

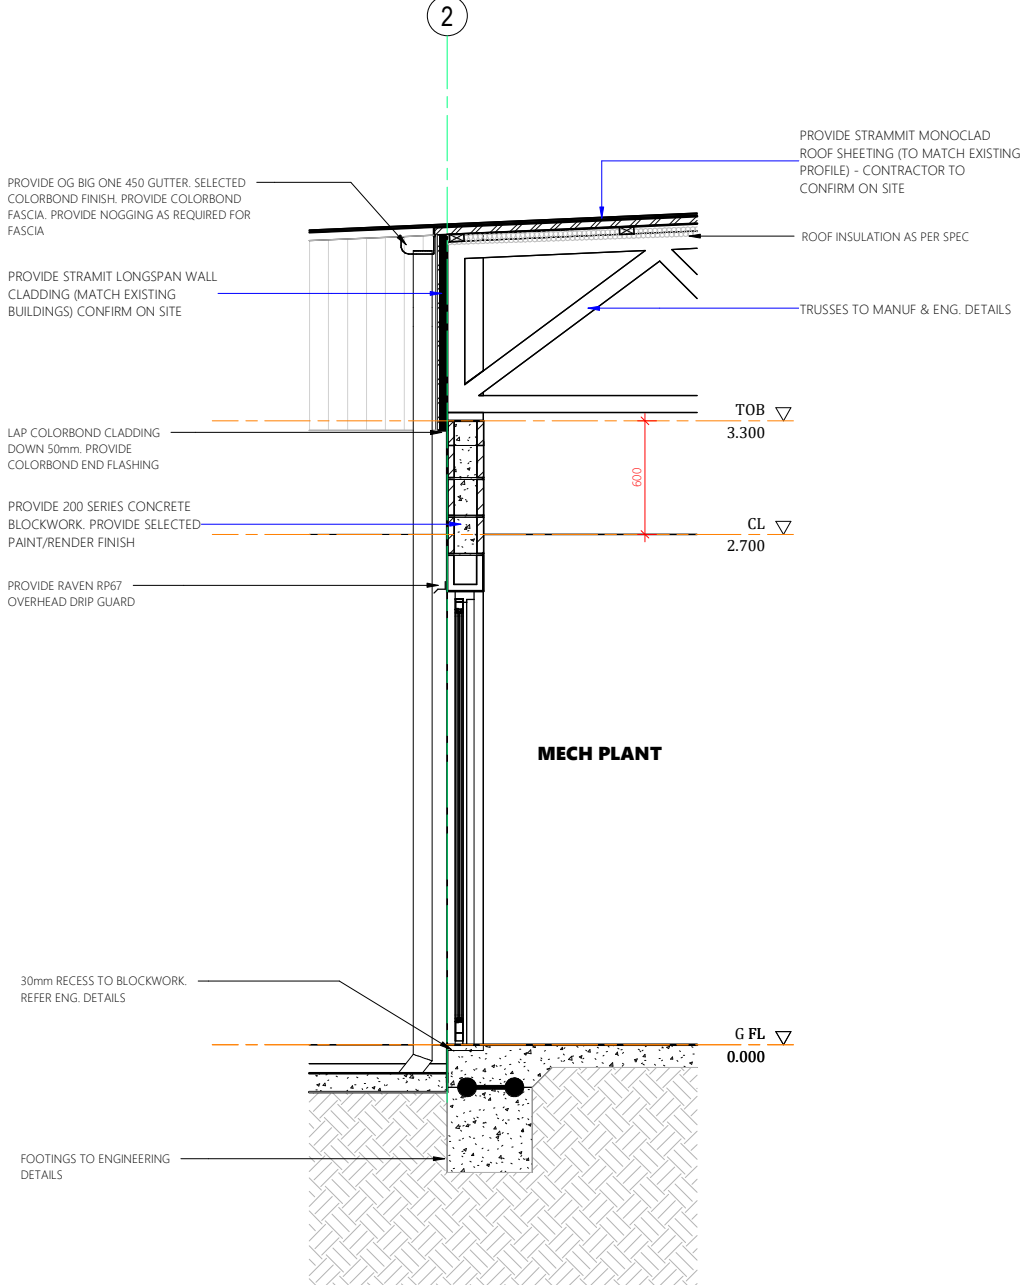



Section Detail D1

1 : 20

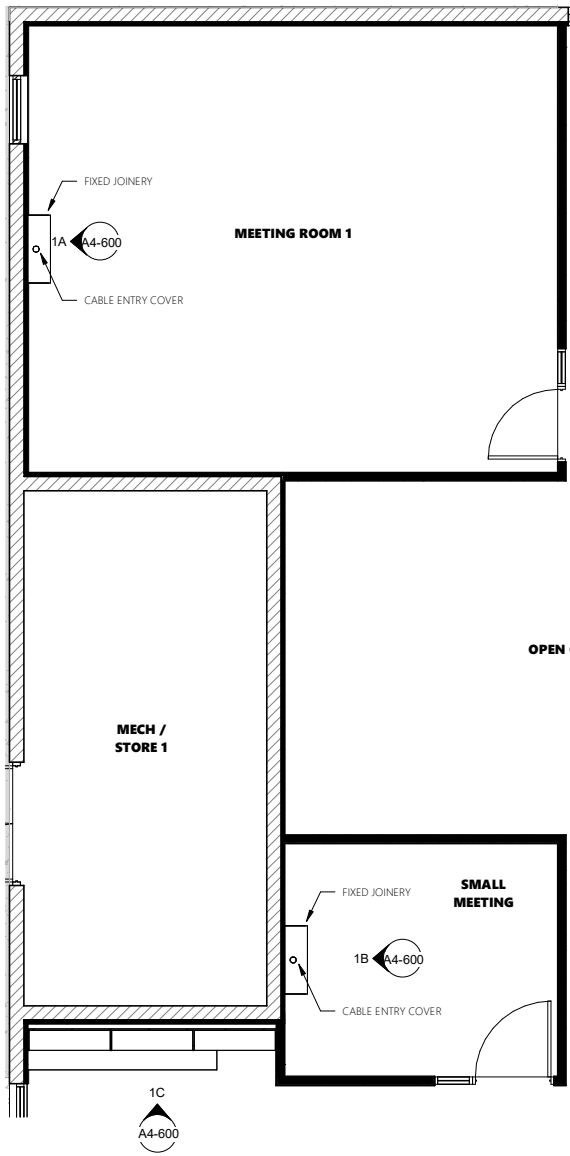

Internal Plan 2 - Consumables

1 : 50

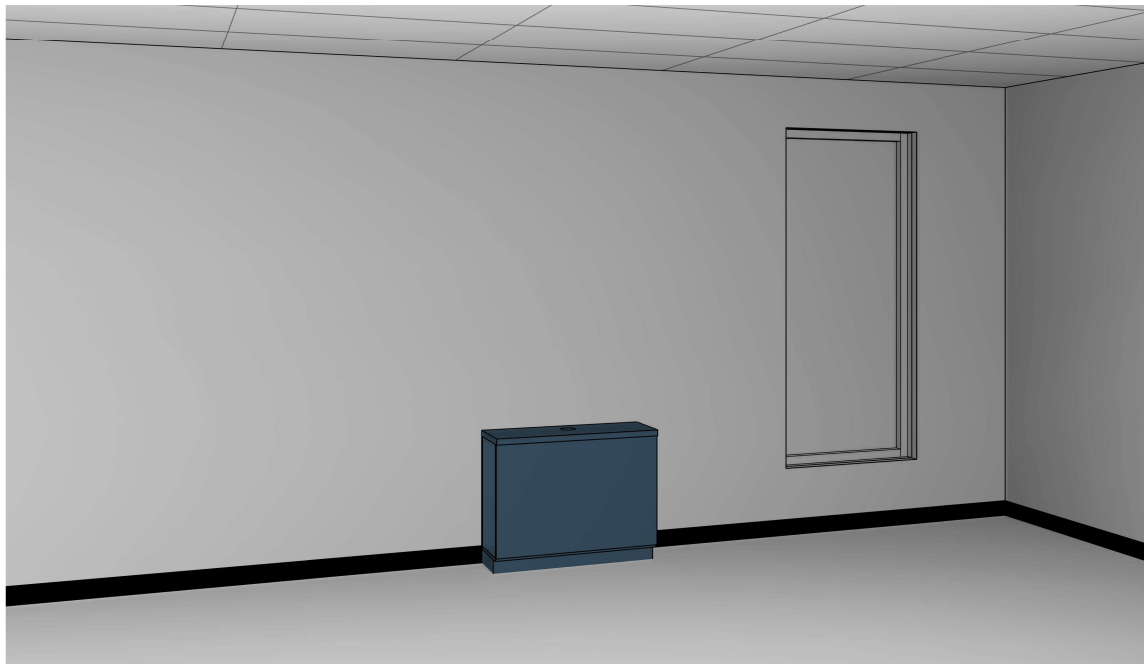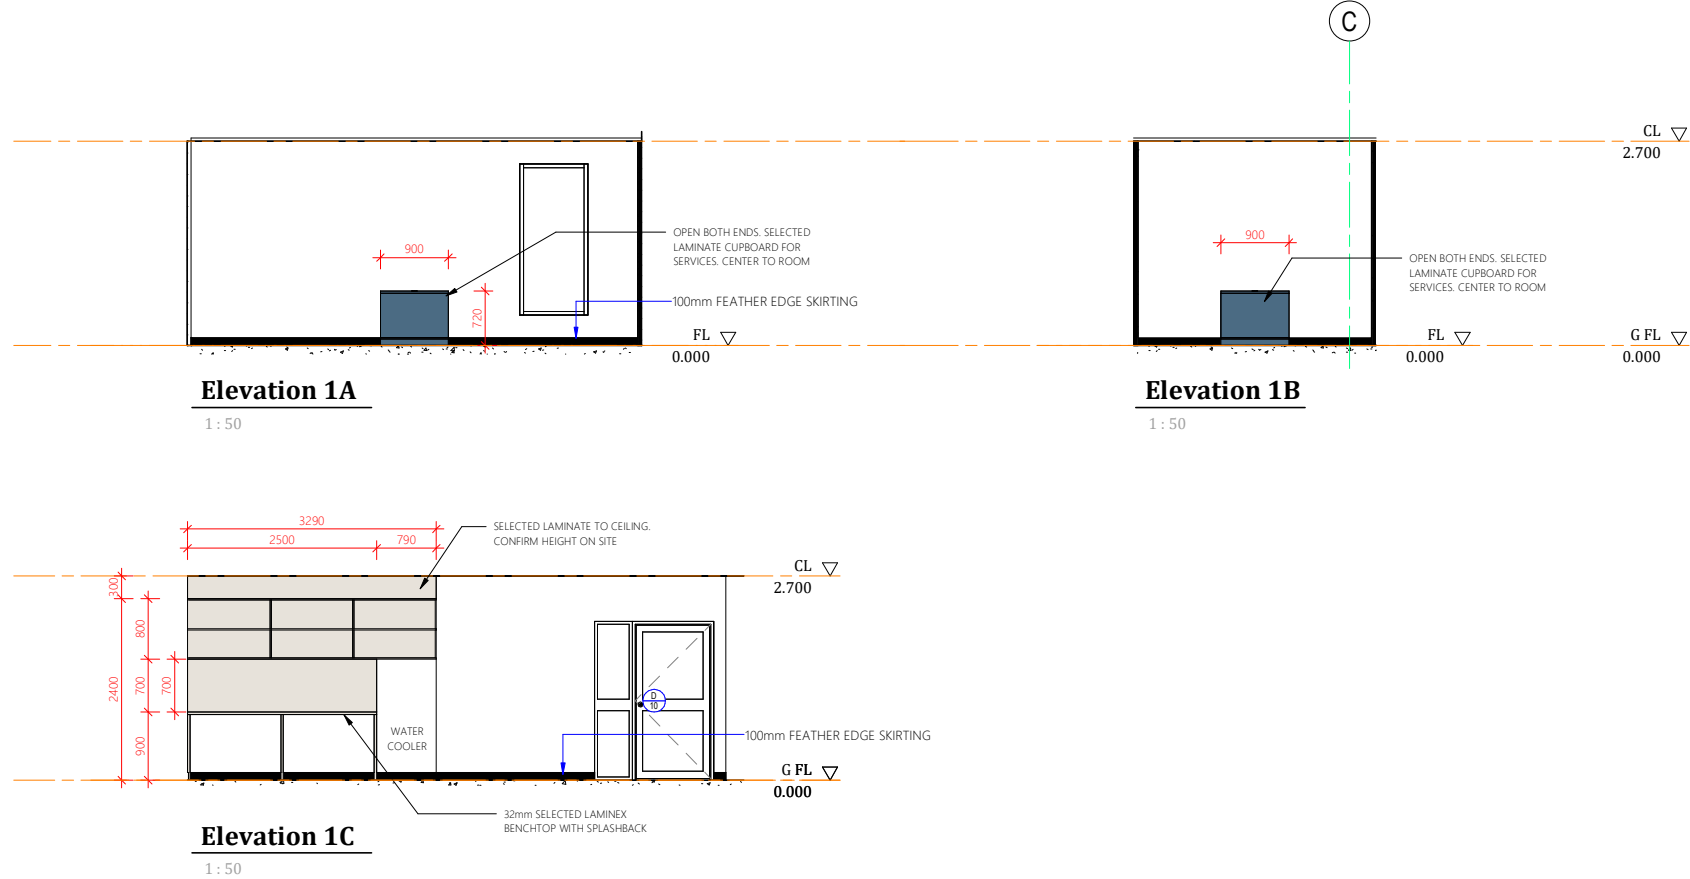

REVISIONS		
Rev	Description	Date
T1	TENDER ISSUE	12.03.2026

DO NOT SCALE THIS DRAWINGS



TENDER ISSUE

Client

 stanwell

Project Details

OFFICE REFURBS

Address

STANWELL POWER STATION

Drawing Title

INTERNAL DETAILS 1 - MEETING ROOM 1, SMALL MEETING

 **designelements**
BUILDING DESIGNERS

0483 988 655 M

info@designelements.com.au E

QBCC No: 1247120 BDAQ No: 0001677

Scale: 1 : 50 Rev: T1

Date: MAR 2026


Drawn: Author

Project No: 25_003 Drawing No: A4-600

12/03/2026 7:52:36 PM



DO NOT SCALE THIS DRAWINGS

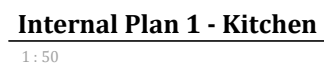[illegible]


Client

 stanwell

Address
**STANWELL POWER
STATION**

 **dezi nelements**
BUILDING DESIGNERS
0483 988 655 **M**
info@dezi nelements.com.au **E**
QBCC No: 1247120 BDAQ No: 0001677

DO NOT SCALE THIS DRAWINGS

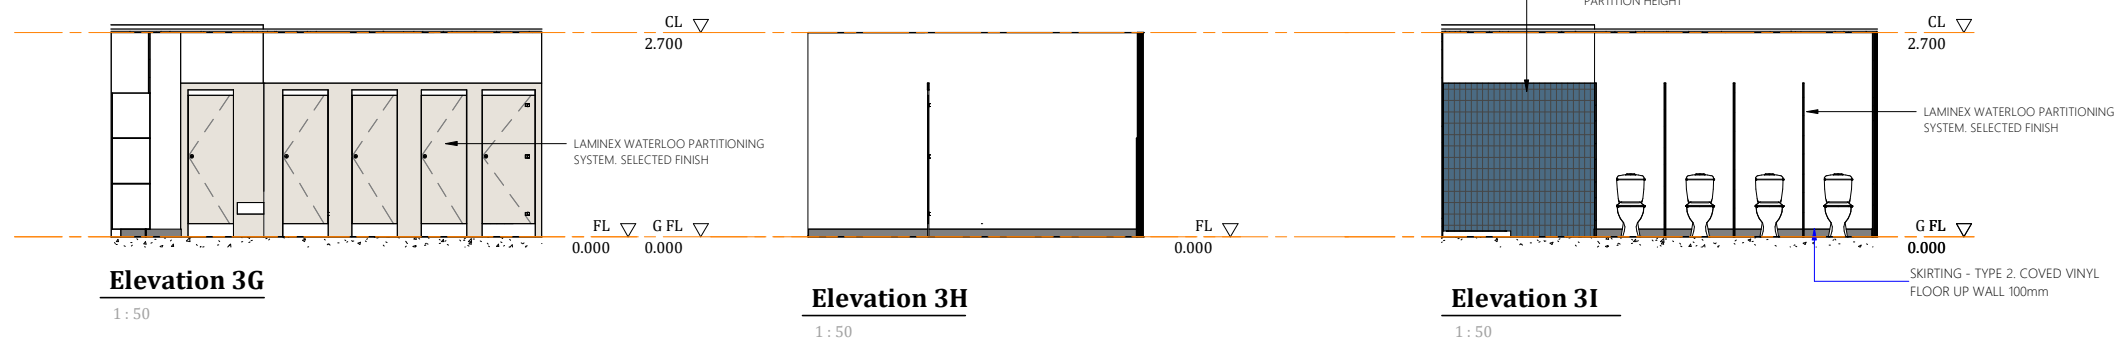[illegible]

Client


 stanwell

Project Details	OFFICE REFURBS
Address	STANWELL POWER STATION
Drawing Title	INTERNAL DETAILS 3 - MALE AMENITIES

 **dezi nelements**
BUILDING DESIGNERS
0483 988 655 **M**
info@dezi nelements.com.au **E**
QBCC No: 1247120 BDAQ No: 0001677


Scale: **1:50** Rev: **T1**
 Date: **MAR 2026**
 Drawn: **Author**
 Project No: **25_003** Drawing No: **A4-602**



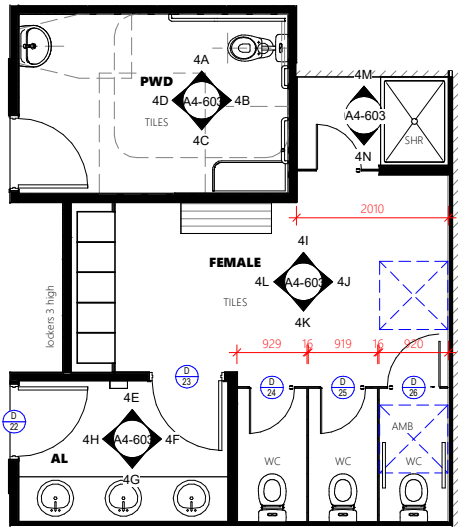

Internal Plan 3 - Amenities

1:50

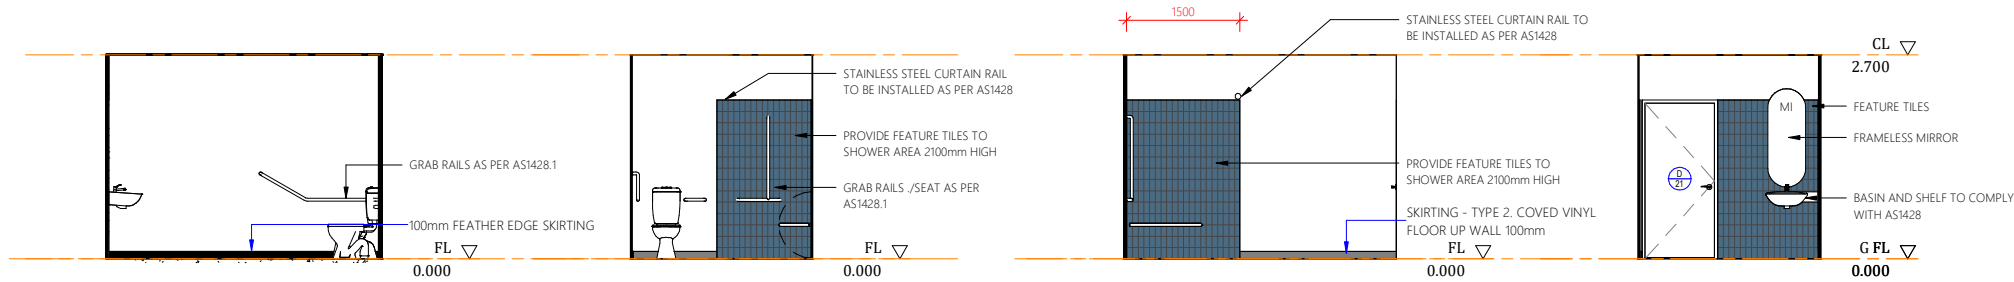

Elevation 4A

1:50

Elevation 4B


1:50

Elevation 4C

1:50

Elevation 4D

1:50

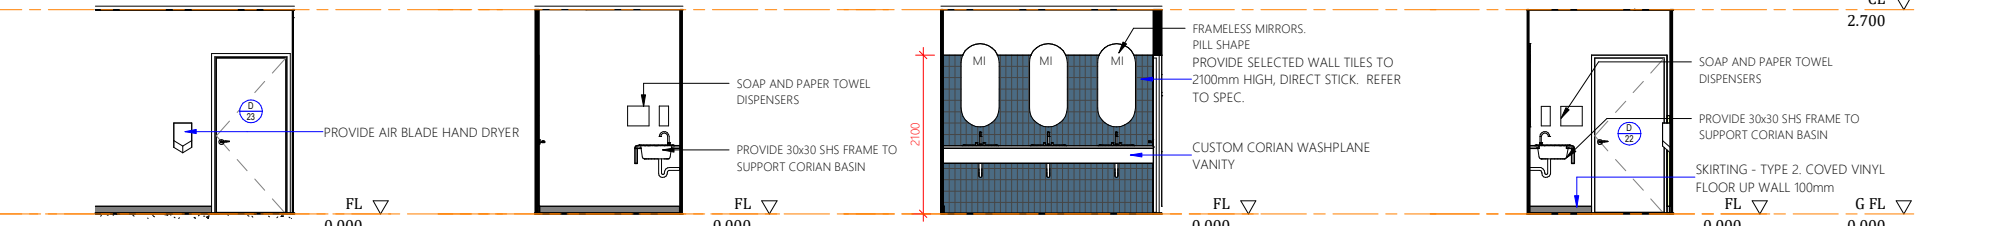

Elevation 4E

1:50

Elevation 4F


1:50

Elevation 4G

1:50

Elevation 4H

1:50

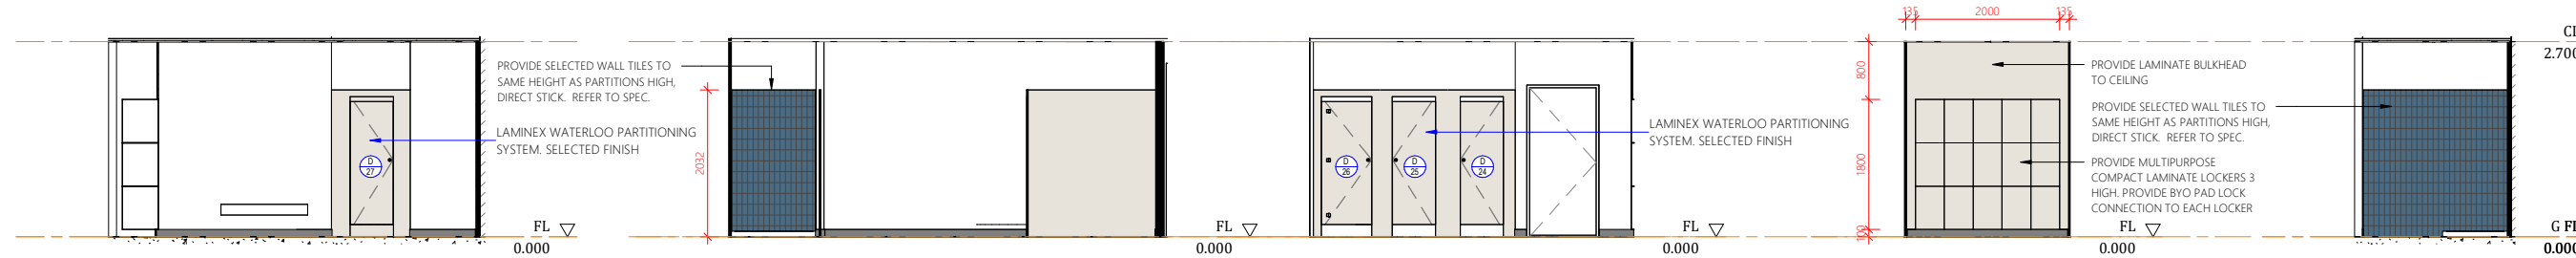

Elevation 4I

1:50

Elevation 4J

1:50

Elevation 4K


1:50

Elevation 4L

1:50


Elevation 4M

1:50

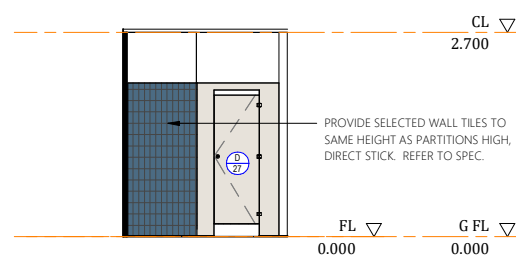


Elevation 4N

1:50

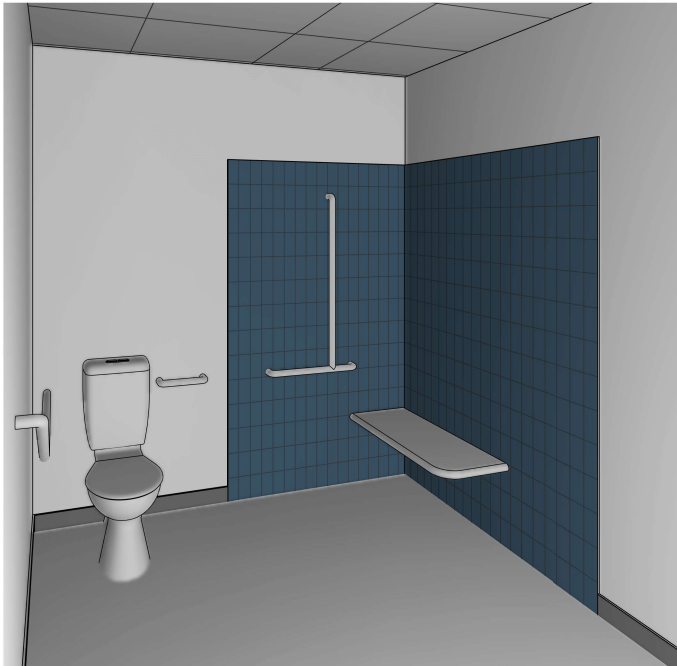

REVISIONS		
Rev	Description	Date
T1	TENDER ISSUE	12.03.2026

DO NOT SCALE THIS DRAWINGS

 


TENDER ISSUE



Project Details	
OFFICE REFURBS	
Address	
STANWELL POWER STATION	
Drawing Title	
INTERNAL DETAILS 3 - FEMALE AMENITIES	



Scale:	1:50	Rev:	T1
Date:	MAR 2026		
Drawn:	Author		
Project No:	25_003	Drawing No:	A4-603

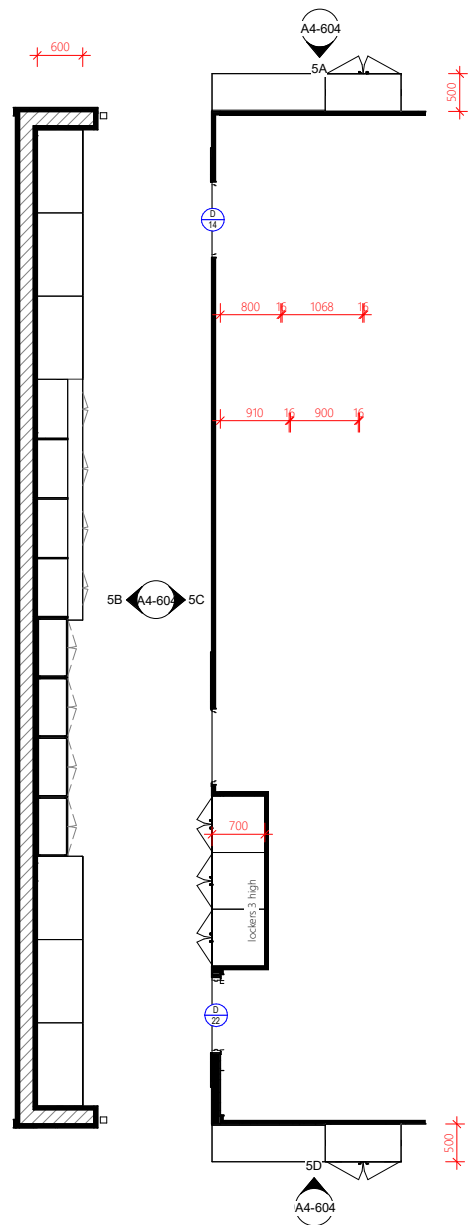

Internal Plan 5 - Central Corridor

1:50



REVISIONS		
Rev	Description	Date
T1	TENDER ISSUE	12.03.2026

DO NOT SCALE THIS DRAWINGS



TENDER ISSUE




Project Details
OFFICE REFURBS
Address
STANWELL POWER STATION
Drawing Title
INTERNAL DETAILS 5 - CENTRAL CORRIDOR




Scale: 1:50	Rev: T1
Date: MAR 2026	
Drawn: Author	
Project No: 25_003	Drawing No: A4-604



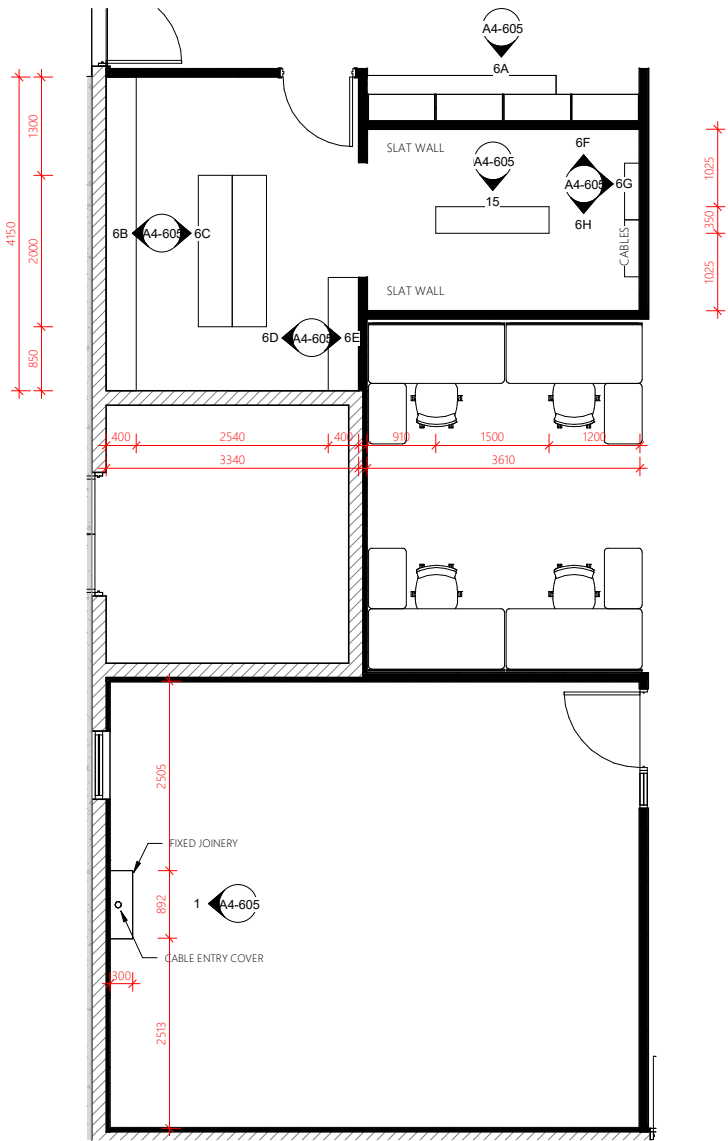

Internal Plan 2 - Consumables

1 : 50

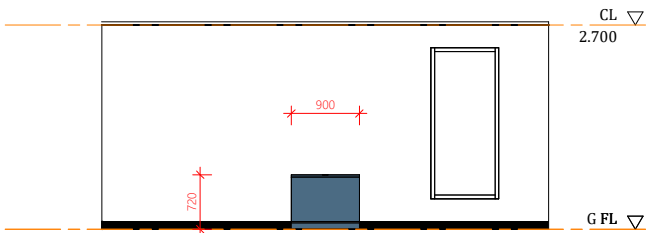


Elevation 6J

1 : 50




PHOTO FOR REFERENCE FOR ELEVATION 6G

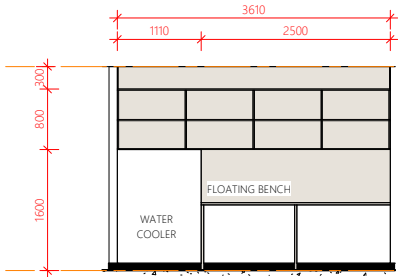


Elevation 6A

1 : 50

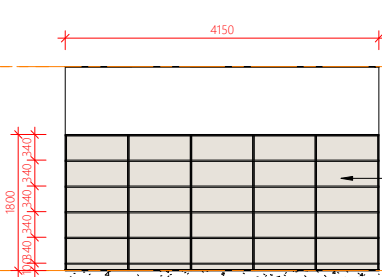


Elevation 6B

1 : 50

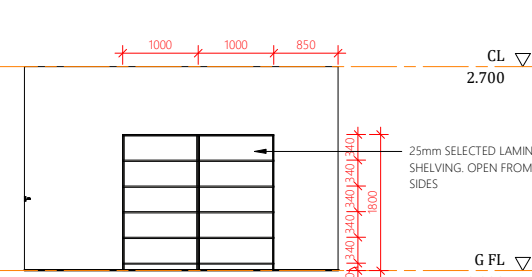


Elevation 6C

1 : 50

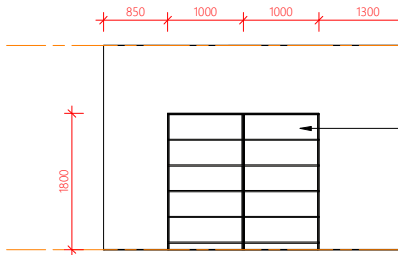


Elevation 6D

1 : 50

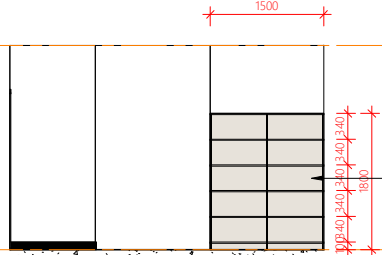


Elevation 6E

1 : 50

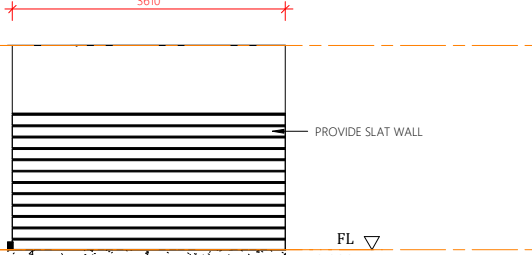


Elevation 6F

1 : 50

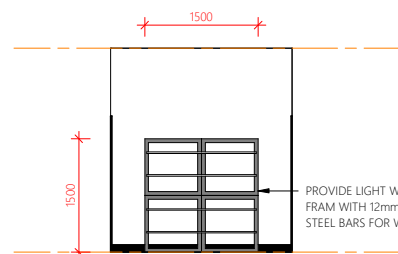


Elevation 6G

1 : 50

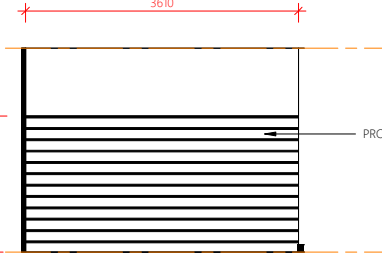



Elevation 6H

1 : 50

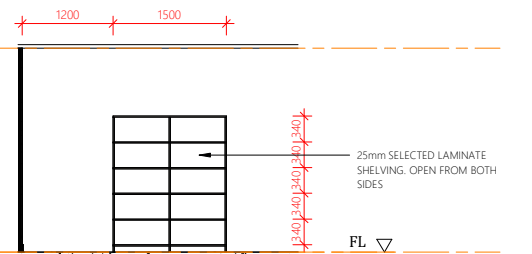


Elevation 6I

1 : 50

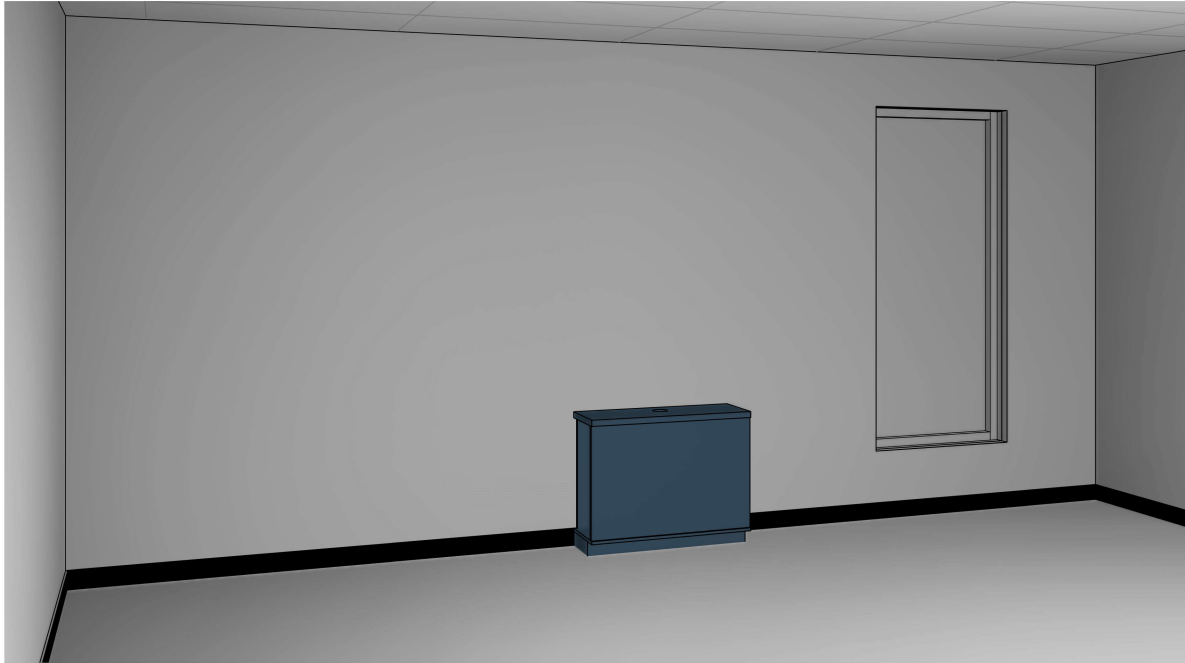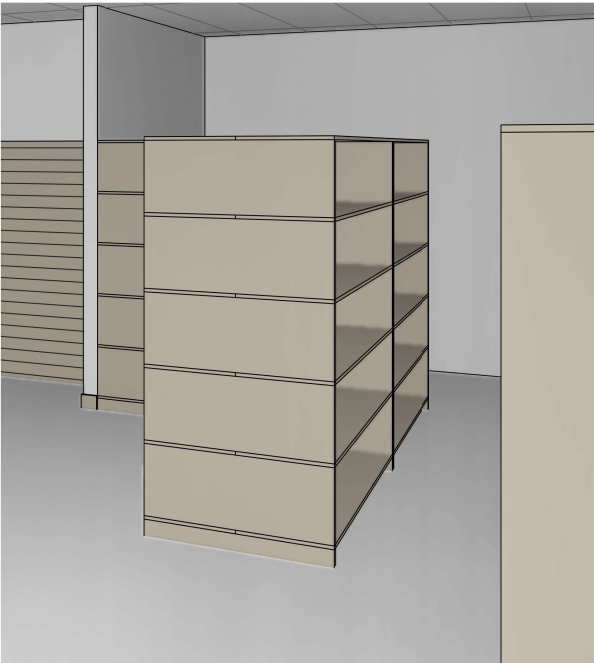

REVISIONS		
Rev	Description	Date
T1	TENDER ISSUE	12.03.2026

DO NOT SCALE THIS DRAWINGS

 

TENDER ISSUE




Project Details
OFFICE REFURBS
Address
STANWELL POWER STATION
Drawing Title
INTERNAL DETAILS 6 - CONSUMABLES



Scale: 1 : 50	Rev: T1
Date: MAR 2026	
Drawn: Author	
Project No: 25_003	Drawing No: A4-605




DOOR SCHEDULE	
DOOR NO.	DOOR TYPE
01	TYPE A
02	TYPE A
03	TYPE A
04	TYPE A
05	TYPE B
06	TYPE A
07	TYPE A
08	TYPE B
09	TYPE D
10	TYPE C
11	TYPE C
12	TYPE C
13	TYPE F
14	TYPE G
15	TYPE G
16	TYPE J
17	TYPE K
18	TYPE K
19	TYPE K
20	TYPE K
21	TYPE H
22	TYPE G
23	TYPE G
24	TYPE K
25	TYPE K
26	TYPE J
27	TYPE K
28	TYPE E
29	TYPE D

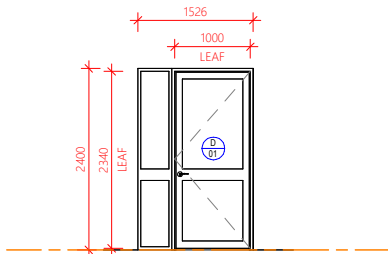


DOOR TYPE A

LOCATION: EXTERNAL
DOOR TYPE: HINGED ALUMINIUM FRAMED SINGLE DOOR
FRAME TYPE: G.JAMES 475 SERIES
FRAME FINISH: SELECTED POWDERCOAT
DOOR FINISH: SELECTED POWDERCOAT
INFILL: GREY SAFETY GLASS
THRESHOLD:
SEALS:
LOCK: VESTIBULE LOCK
HARDWARE: DOOR CLOSER, DOOR STOP

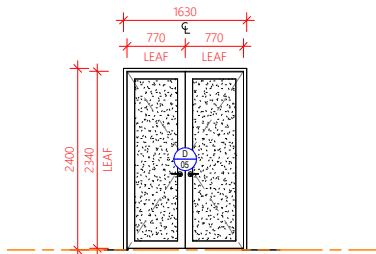


DOOR TYPE B

LOCATION: EXTERNAL, MECH STORES
DOOR TYPE: HINGED ALUMINIUM FRAMED DOUBLE DOOR
FRAME TYPE: G.JAMES 475 SERIES
FRAME FINISH: SELECTED POWDERCOAT
DOOR FINISH: SELECTED POWDERCOAT
INFILL: 9mm CFC, PAINT FINISH
THRESHOLD:
SEALS:
LOCK: VESTIBULE LOCK
HARDWARE:

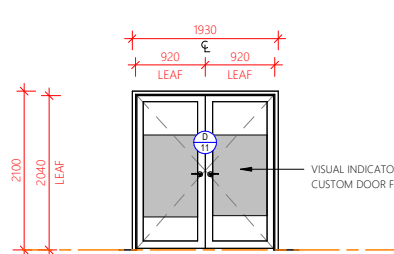


DOOR TYPE C

LOCATION: INTERNAL, LUNCH ROOM
DOOR TYPE: HINGED ALUMINIUM FRAMED DOUBLE DOOR
FRAME TYPE: G.JAMES 475 SERIES
FRAME FINISH: SELECTED POWDERCOAT
DOOR FINISH: SELECTED POWDERCOAT
INFILL: CLEAR SAFETY GLASS
THRESHOLD:
SEALS:
LOCK: VESTIBULE LOCK
HARDWARE:

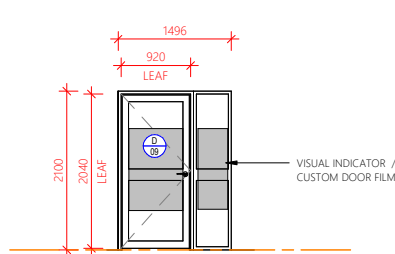


DOOR TYPE D

LOCATION: INTERNAL, MEETING ROOMS
DOOR TYPE: HINGED ALUMINIUM FRAMED SINGLE DOOR
FRAME TYPE: G.JAMES 475 SERIES
FRAME FINISH: SELECTED POWDERCOAT
DOOR FINISH: SELECTED POWDERCOAT
INFILL: GREY SAFETY GLASS
THRESHOLD:
SEALS:
LOCK: VESTIBULE LOCK
HARDWARE: DOOR CLOSER, DOOR STOP

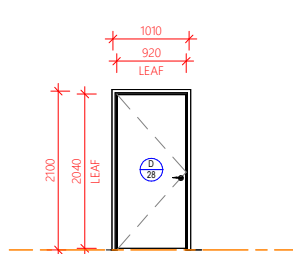


DOOR TYPE E

LOCATION: INTERNAL
DOOR TYPE: 40mm HINGED SOLID CORE SINGLE DOOR
FRAME TYPE: TIMBER
FRAME FINISH: PAINT
DOOR FINISH: PAINT
SEALS: NONE
LOCK: VESTIBULE LOCK
HARDWARE: DOOR CLOSER, DOOR STOP

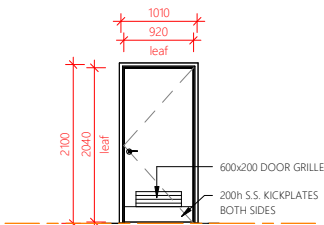


DOOR TYPE F

LOCATION: CLEANER
DOOR TYPE: 40mm HINGED SOLID CORE SINGLE DOOR
FRAME TYPE: TIMBER
FRAME FINISH: PAINT
DOOR FINISH: PAINT
SEALS: NONE
LOCK: VESTIBULE LOCK
HARDWARE: KICK PLATES, DOOR CLOSER, DOOR STOP

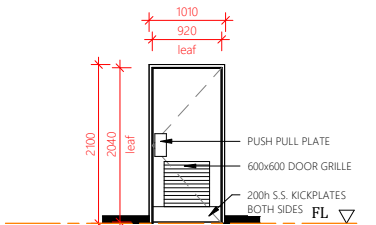


DOOR TYPE G

LOCATION: MALE & FEMALE AMENITIES
DOOR TYPE: 40mm HINGED SOLID CORE SINGLE DOOR
FRAME TYPE: TIMBER
FRAME FINISH: PAINT
DOOR FINISH: PAINT
SEALS: NONE
LOCK: PUSH PULL PLATES (NO LOCKING)
HARDWARE: KICK PLATES, DOOR CLOSER, DOOR STOP

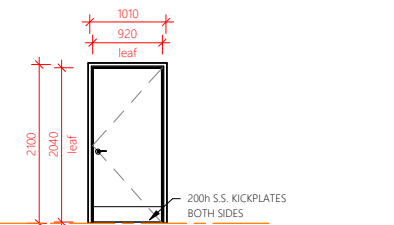


DOOR TYPE H

LOCATION: PWD
DOOR TYPE: 40mm HINGED SOLID CORE SINGLE DOOR
FRAME TYPE: TIMBER
FRAME FINISH: PAINT
DOOR FINISH: PAINT
SEALS: NONE
LOCK: PRIVACY LATCH LEVER HANDLE WITH INDICATOR BOLT
HARDWARE: KICK PLATES, DOOR CLOSER, DOOR STOP

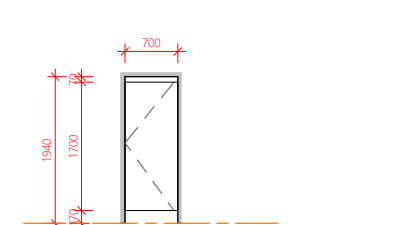


DOOR TYPE J

LOCATION: AMENITIES AMB WC
DOOR TYPE: 13mm COMPACT LAMINATE PARTITION DOOR
FRAME TYPE: PROVIDE 30° PRIVACY BEVEL
DOOR FINISH: SELECTED LAMINATE
SEALS: NONE
LOCK: METLAM XCEL SLIDE LOCK & INDICATOR.
HARDWARE:

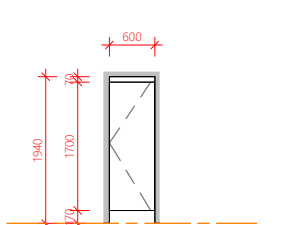


DOOR TYPE K

LOCATION: AMENITIES
DOOR TYPE: 13mm COMPACT LAMINATE PARTITION DOOR
FRAME TYPE: PROVIDE 30° PRIVACY BEVEL
DOOR FINISH: SELECTED LAMINATE
SEALS: NONE
LOCK: METLAM XCEL SLIDE LOCK & INDICATOR.
HARDWARE:

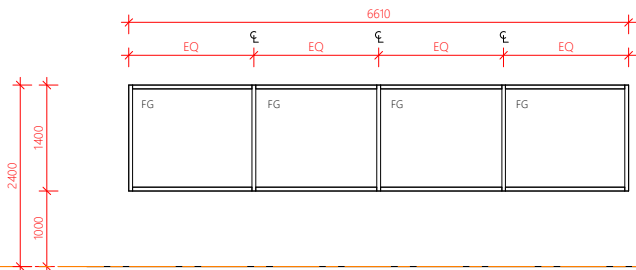


WINDOW TYPE A

LOCATION: EXTERNAL
FRAME TYPE: G.JAMES 475 SERIES
FRAME FINISH: SELECTED POWDERCOAT
WINDOW: FIXED GLASS
GLASS: SAFETY GLASS

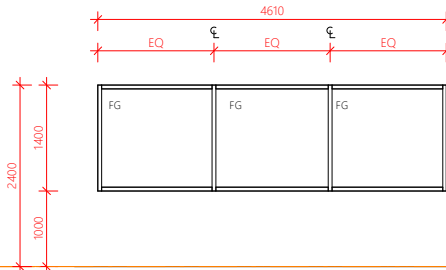


WINDOW TYPE B

LOCATION: EXTERNAL
FRAME TYPE: G.JAMES 475 SERIES
FRAME FINISH: SELECTED POWDERCOAT
WINDOW: FIXED GLASS
GLASS: SAFETY GLASS

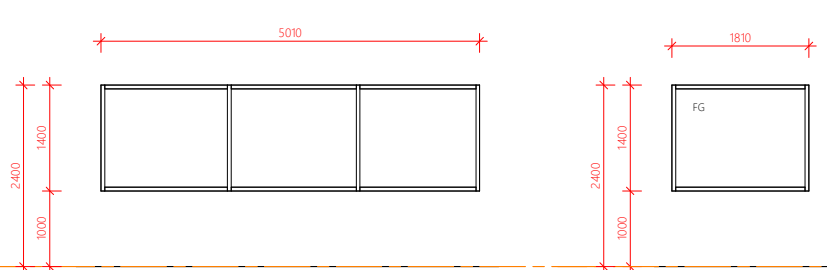


WINDOW TYPE C

LOCATION: EXTERNAL
FRAME TYPE: G.JAMES 475 SERIES
FRAME FINISH: SELECTED POWDERCOAT
WINDOW: FIXED GLASS
GLASS: SAFETY GLASS

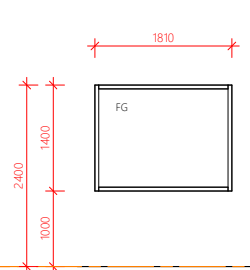

WINDOW TYPE D


LOCATION: EXTERNAL
FRAME TYPE: G.JAMES 475 SERIES
FRAME FINISH: SELECTED POWDERCOAT
WINDOW: FIXED GLASS
GLASS: SAFETY GLASS

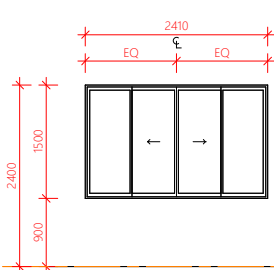

WINDOW TYPE E


LOCATION: EXTERNAL
FRAME TYPE: G.JAMES 475 SERIES
FRAME FINISH: SELECTED POWDERCOAT
WINDOW: G.JAMES 165 SERIES SLIDING WINDOW
GLASS: SAFETY GLASS

WINDOW SCHEDULE	
WINDOW NO.	WINDOW TYPE
01	TYPE A
02	TYPE B
03	TYPE B
04	TYPE C
05	TYPE C
06	TYPE B
07	TYPE B
08	TYPE A
09	TYPE C
10	TYPE E
11	TYPE E
12	TYPE F
13	TYPE G
14	TYPE G
15	TYPE H
16	TYPE I
17	TYPE I
18	TYPE I
19	TYPE I
20	TYPE I
21	TYPE I
22	TYPE H
23	TYPE G
24	TYPE G

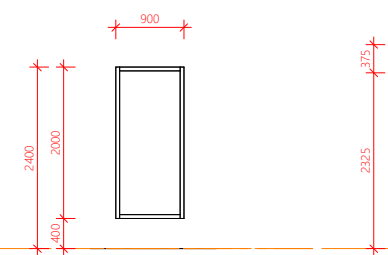


WINDOW TYPE F

LOCATION: EXTERNAL
FRAME TYPE: G.JAMES 475 SERIES
FRAME FINISH: SELECTED POWDERCOAT
WINDOW: FIXED GLASS
GLASS: SAFETY GLASS

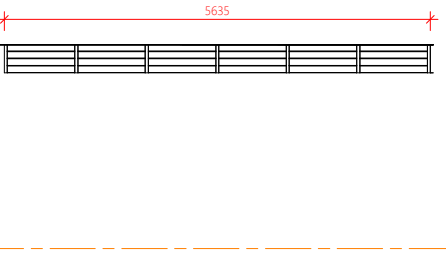


WINDOW TYPE G

LOCATION: EXTERNAL
FRAME TYPE: CAPRAL EXTRUDED LOUVRE BLADES.
FRAME FINISH: SELECTED POWDERCOAT
WINDOW: -
GLASS: -

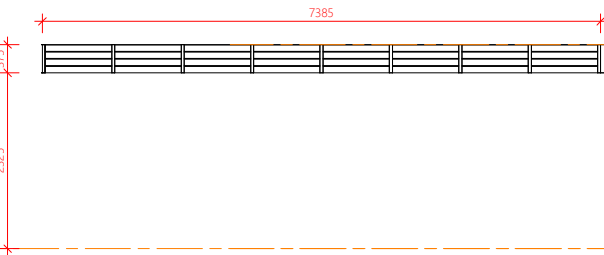

WINDOW TYPE H

LOCATION: EXTERNAL
FRAME TYPE: CAPRAL EXTRUDED LOUVRE BLADES.
FRAME FINISH: SELECTED POWDERCOAT
WINDOW: -
GLASS: -

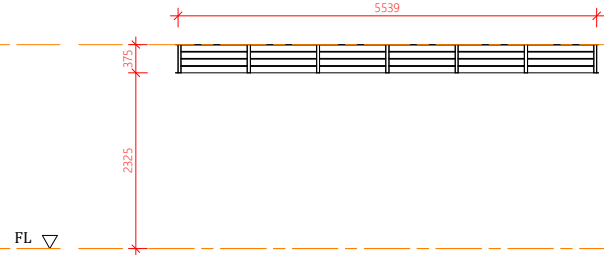

WINDOW TYPE I

LOCATION: EXTERNAL
FRAME TYPE: CAPRAL EXTRUDED LOUVRE BLADES.
FRAME FINISH: SELECTED POWDERCOAT
WINDOW: -
GLASS: -

REVISIONS		
Rev	Description	Date
T1	TENDER ISSUE	12.03.2026

DO NOT SCALE THIS DRAWINGS

TENDER ISSUE



Client
Project Details
OFFICE REFURBS
Address
STANWELL POWER STATION
Drawing Title
DOOR & WINDOW SCHEDULE



Scale: 1 : 50	Rev: T1
Date: MAR 2026	
Drawn: Author	
Project No: 25.003	Drawing No: A4-701