

HYDRAULIC SERVICES LEGEND

PERMIT APPLICATION REF: _____

DESIGNER: HARRISON RALPH
QBCC Lic No. 15125080
SOIL CLASSIFICATION: H1



All dimensions to be verified on site/s prior to commencement of on-site work and/or off-site prefabrication. Figured dimension to be taken in preference to scaled dimensions. This drawing is copyright and remains the property of JHA Consulting Engineers. Reproduction in whole or part of these drawings without written consent constitutes an infringement of copyright.

REVISIONS / AMENDMENTS

Rev	Date	Description	Verified
A	29.08.2025	DRAFT ISSUE	H.R.
B	03.09.2025	QS ISSUE	H.R.
C	19.09.2025	100% CD DETAILED DESIGN	H.R.
D	31.10.2025	90% CD DRAFT ISSUE	H.R.
E	28.11.2025	90% CD ISSUE	H.R.
F	18.12.2025	TENDER ISSUE	H.R.
G	14.01.2026	ISSUE FOR COUNCIL APPROVAL	H.R.

AUTHORITY/CIVIL LINETYPE LEGEND

---	AGM	AUTHORITY GAS MAIN
---	ASM	AUTHORITY SEWER MAIN
---	ASWM	AUTHORITY STORMWATER MAIN
---	AWM	AUTHORITY WATER MAIN
---	CS	CIVIL SEWER
---	CSW	CIVIL STORMWATER
---	CW	CIVIL WATER

FIRE SERVICES LINETYPE LEGEND

---	FHR	FIRE HOSE REEL
---	eFHR	FIRE HOSE REEL - EXISTING
---	FH	FIRE HYDRANT
---	eFH	FIRE HYDRANT - EXISTING
---	FS	FIRE SERVICE
---	eFS	FIRE SERVICE - EXISTING
---	FTD	FIRE TEST DRAIN

GAS SERVICES LINETYPE LEGEND

---	GF	GAS FLUE
---	GAS	GAS SERVICE
---	eGAS	GAS SERVICE - EXISTING

WATER SERVICES LINETYPE LEGEND

---	CW	COLD WATER
---	eCW	COLD WATER - EXISTING
---	FCW	COLD WATER - FILTERED
---	SCW	COLD WATER - SOFTENED
---	WHF	HOT WATER FLOW
---	eWHF	HOT WATER FLOW - EXISTING
---	HWR	HOT WATER RETURN
---	eHWR	HOT WATER RETURN - EXISTING
---	NPCW	NON-POTABLE COLD WATER
---	eNPCW	NON-POTABLE COLD WATER - EXISTING
---	NPHWF	NON-POTABLE HOT WATER
---	eNPHWF	NON-POTABLE HOT WATER - EXISTING
---	NPHWR	NON-POTABLE HOT WATER RETURN
---	RR	RAINWATER RE-USE
---	eRR	RAINWATER RE-USE - EXISTING
---	RW	RECLAIMED WATER
---	eRW	RECLAIMED WATER - EXISTING
---	WWF	WARM WATER FLOW
---	eWWF	WARM WATER FLOW - EXISTING
---	WWR	WARM WATER RETURN
---	eWWR	WARM WATER RETURN - EXISTING

DRAINAGE SERVICES LINETYPE LEGEND

---	CW	CHAMBER VENT
---	CD	CONDENSATE DRAIN
---	eCD	CONDENSATE DRAIN - EXISTING
---	SD	SANITARY DRAINAGE
---	eSD	SANITARY DRAINAGE - EXISTING
---	SP	SANITARY PLUMBING
---	eSP	SANITARY PLUMBING - EXISTING
---	SRM	SANITARY RISING MAIN
---	eSRM	SANITARY RISING MAIN - EXISTING
---	SWC	STORMWATER CATCHMENT
---	SWD	STORMWATER DRAINAGE
---	eSWD	STORMWATER DRAINAGE - EXISTING
---	SWRM	STORMWATER RISING MAIN
---	eSWRM	STORMWATER RISING MAIN - EXISTING
---	SSD	SUBSOIL DRAINAGE
---	eSSD	SUBSOIL DRAINAGE - EXISTING
---	TWD	TRADE WASTE DRAINAGE
---	eTWD	TRADE WASTE DRAINAGE - EXISTING
---	TWVP	TRADE WASTE VENT PIPE
---	eTWVP	TRADE WASTE VENT PIPE - EXISTING
---	VP	VENT PIPE
---	eVP	VENT PIPE - EXISTING

MISC. LINETYPE LEGEND

---	AMENDMENT
---	INSET BORDER
---	DISCONNECTED SERVICE
---	ELECTRICAL SERVICE
---	CASTIN

SYMBOLS

---	RISER
---	DROP / RISE
---	DROPPER
---	TEE DROPPER
---	PIPEWORK CAP
---	PIPEWORK CONTINUATION
---	UNDOCUMENTED CONTINUED LINE
---	PIPEWORK SECTION
---	DIRECTION ARROW
---	NEW CONNECTION
---	NEXT DRAWING
---	DIRECTION OF FLOW
---	SERVICE DESCRIPTION
---	SERVICE TITLE
---	SERVICE SIZE
---	DIRECTION OF FLOW
---	STOP VALVE
---	CHECK VALVE
---	BALANCING VALVE
---	3 - WAY VALVE
---	BALL VALVE
---	REDUCED PRESSURE ZONE DEVICE
---	PRESSURE RELIEF VALVE
---	PRESSURE LIMITING VALVE
---	SOLENOID VALVE
---	DOUBLE CHECK VALVE
---	THERMOSTATIC MIXING VALVE
---	TEMPERING VALVE
---	WATER FILTER
---	REFLUX VALVE
---	REFLUX VALVE IN PIT
---	PATHBOX
---	WATER METER
---	GAS METER
---	STRAINER
---	WATER POINT
---	TAP SET
---	HOSE TAP
---	BAYONET POINT
---	REGULATOR
---	PUMP
---	CONTROL PANEL
---	FIRE HOSE REEL
---	HOT WATER UNIT
---	FIRE HYDRANT
---	DUAL PILLAR FIRE HYDRANT
---	STREET HYDRANT
---	DUAL SUCTION POINT
---	QUAD SUCTION POINT
---	DUAL BOOSTER POINT
---	QUAD BOOSTER POINT

SYMBOLS (cont'd)

---	INDUCT PIPE MICA FLAP
---	KAMLOCK CONNECTION
---	AIR ADMITTANCE VALVE
---	SYPHONIC OUTLET
---	RAINWATER OUTLET
---	SPREADER
---	OVERLAND FLOW ARROW
---	STORMWATER FLOW ARROW
---	PENETRATION / CORE HOLE IN SLAB
---	BEAM PENETRATION
---	REDUCER
---	GREASE ARRESTOR
---	STORMWATER GRATE
---	STORMWATER COVER
---	TRENCH GRATE
---	REVISION
---	KERB ENTRY PIT
---	THRUST BLOCK
---	P.A.P.A. VALVE
---	RAINWATER HEAD
---	MONITORED VALVE
---	PRESSURE GAUGE
---	FLOW SWITCH
---	PRESSURE SWITCH
---	FLOORWASTE
---	TUNDISH
---	BUCKET TRAP FLOORWASTE
---	CLEAROUT TO SURFACE
---	SEWER MANHOLE
---	BOUNDARY TRAP
---	SURCHARGE GULLY
---	INSPECTION SHAFT
---	EXPANTION JOINT
---	SWIVEL JOINT

NOTE:
THIS IS A STANDARD LEGEND. ALL SYMBOLS MAY NOT
NECESSARILY BE USED IN THESE DRAWINGS.

ABBREVIATIONS

A/C	Air Conditioning
AAV	Air Admittance Valve
AHD	Australian Height Datum
B	Basin
BALV	Balancing Valve
BBO	Barbecue
BBV	Brigade Booster Valve
BCA	Building Code Of Australia
BDO	Balcony Drain Outlet
BID	Bidet
BM	Bain Marie
BP	Bayonet Point
BR	Brass
BT	Boundary trap
BTFWG	Bucket Trap Floorwaste Gully
BTH	Bath
BV	Ball Valve
BWL	Bottom Water Level
BWU	Boiling Water Unit
CHV	Check Valve
CHVP	Chamber Vent Pipe
CHWU	Chilled Water Unit
CI	Cast Iron
CIC	Cast In Column
CICL	Cast Iron Cement Lined
CIS	Cast In Slab
CL	Ceiling Level
COS	Clear Out To Surface
CSK	Cleaners Sink
CST	Condensate Stack
CT	Cook Top
CU	Copper
CV	Control Valve
CWM	Cold Water Meter
D	Disabled
DB	Disabled Basin
DCV	Double Check Valve
DCV-A	Double Check Valve Assembly
DF	Drinking Fountain
DG	Disconnector Gully
DIA	Diameter
DICL	Ductile Iron Cement Lined
DP	Downpipe
DPFH	Dual Pillar Fire Hydrant
DR	Drainage Riser
DTU	Drainage Turn Up
DU	Dental Unit
DWC	Disabled Water Closet
DWG	Drawing
DWM	Dish Washing Machine
e	Existing
ECV	Expansion Control valve
EJ	Expansion Joint
ELEC	Electrical Service
EDP	Elevated Drainage Pipe
EIV	Eye Wash
EXT	Extinguisher
FC	Fume Cupboard
FD	Floor Drain
FFL	Finished Floor Level
FD	Fire Hydrant
FHR	Fire Hose Reel
FHV	Fire Hydrant Valve
FIP	Fire Indicator Panel
FR	Fridge
FRC	Fibre Reinforced Concrete
FRS	Flushing Rim Sink
FSL	Finished Surface Level
FSR	Fire Sprinkler Range
FTD	Fire Test Drain
FU	Fixture Units
FV	Flush Valve
FW	Floorwaste (Untrapped)
FWG	Floorwaste Gully (Trapped)
GA	Grease Arrestor
GAL	Galvanised
GD	Grated Drain
GDO	Grated Drain Outlet
GDTU	Grease Drainage Turn Up
GIT	Grease Interceptor Trap
GL	Ground Level
GM	Gas Meter
GMS	Galvanised Mild Steel
GO	Gutter Outlet
GR	Gas Regulator
GST	Grease Stack
GT	Grease Trap
GTU	Grease Turn Up
CTVP	Grease Trap Vent Pipe
GV	Gate Valve
GWM	Glass Washing Machine
GWST	Grease Waste Stack
HIL	High Level

ABBREVIATIONS (cont'd)

HD	Heavy Duty
HDPE	High Density Polyethylene
HP	High Point
HT	Hose Tap
HV	High Voltage
HWM	Hot Water Meter
HWU	Hot Water Unit
ID	Inside Diameter
IL	Invert Level
IM	Ice Machine
IO	Inspection Opening
IS	Inspection Shaft
IV	Isolation Valve
JU	Jump Up
KIP	Kerb Inlet Pit
KPA	Kilopascal
KW	Kilowatt
L	Litres
L/L	Low Level
L/S	Litres Per Second
LD	Light Duty
LPG	Liquid Petroleum Gas
LSK	Laboratory Sink
LT	Laundry Tub
LU	Loading Units
LV	Low Voltage
M	Metre
M.HEAD	Metres Head
M/S	Metres per Second
M3/HR	Cubic Metres per Hour
MDPE	Medium Density Polyethylene
MIN	Minimum
MJ	Megapascals
MM	Millimetres
MS	Mild Steel
NRV	Non-Return Valve
NTS	Not To Scale
NY	Nylon
O/F	Overflow
OD	Outside Diameter
OJ	Oblique Junction
ORG	Overflow Relief Gully
PAPA	Positive Air Pressure Attenuator
PDO	Planter Drain Outlet
PEX	Cross Linked Polyethylene
PFWG	Platroom Floorwaste Gully
PG	Pressure Gauge
PLV	Pressure Limiting Valve
PM	Post Mix
PRV	Pressure Relief Valve
PS	Pan Sanitiser
PSK	Pot Sink
PVC	Polyvinyl Chloride
RCP	Reinforced Concrete Pipe
RHS	Rectangular Hollow Section
RL	Reduced Level
R/PZD	Reduced Pressure Zone Device
RV	Relief Valve
RVP	Relief Vent Pipe
RWH	Rain Water Head
RWO	Rainwater Outlet
S/S	Stainless Steel
S/TR	Safe Tray
SB	Surgeons Basin
SDO	Spoon Drain Outlet
SH	Slop Hopper
SHR	Shower
SP	Sewer Inspection Pit
SK	Sink
SL	Surface Level
SMH	Sewer Manhole
SO	Syphonic Outlet
SOF	Syphonic Overflow
SPD	Spreader
SPR	Sprinkler
SQ	Square
SSHR	Safety Shower
SSL	Structural Slab Level
SST	Soil Stack
ST	Stack
STD	Sprinkler Test Drain
STER	Steriliser
SV	Stop Valve
SWIP	Stormwater Inspection Pit
SWMH	Stormwater Manhole
SWP	Stormwater Pit
SWS	Stormwater Sump
SYN	Syphonic
TA	Test Access
TB	Thrust Block
TBR	To Be Removed
TD	Tundish
TEL	Telecommunication Service
TG	Trench Grate


ABBREVIATIONS (cont'd)

TLV	Temperature Limiting Valve
TMV	Thermosatic Mixing Valve
TPRV	Temperature & Pressure Relief Valve
TTD	Trapped Tundish
TWIP	Trade waste Inspection Pit
TWL	Top Water Level
TWST	Trade waste Stack
TWTU	Tradewaste Turn Up
TWVP	Tradewaste Vent Pipe
TYP	Typical
U/S	Underside
UNO	Unless Noted Otherwise
UPVC	Unplasticised Polyvinyl Chloride
UR	Urinal
UV	Ultra Violet
VB	Vacuum Breaker
VCP	Vitrified Clay Pipe
VP	Vent Pipe
WC	Water Closet
WL	Water Level
WM	Washing Machine (Clothes)
WST	Waste Stack
WT	Wash Trough

WARNING

BEWARE OF UNDERGROUND SERVICES

THE LOCATIONS OF UNDERGROUND SERVICES ARE APPROXIMATE.
ONLY AND THEIR EXACT POSITION SHOULD BE PROVEN ON SITE. NO
GUARANTEE IS GIVEN THAT ALL EXISTING SERVICES ARE SHOWN.

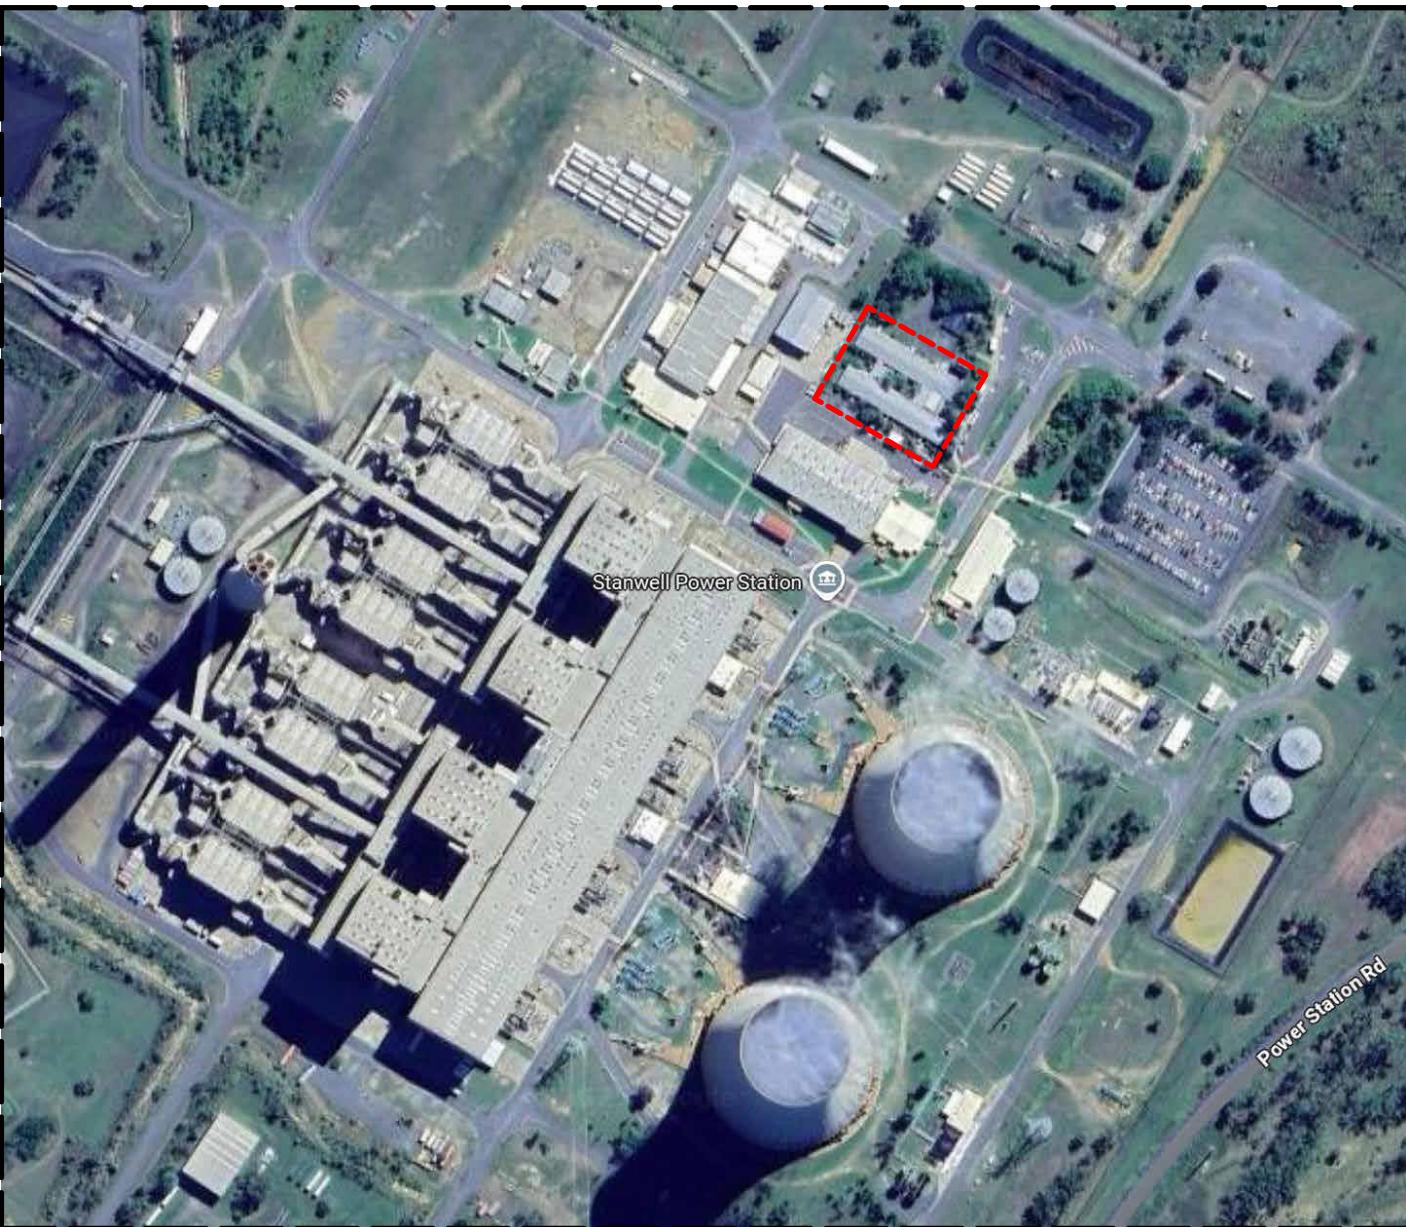

LOCALITY PLAN
SCALE N.T.S.

AUTHORITY
APPROVAL
STAMPS



brian hooperarchitect
m3architecture



PROJECT
**STANWELL NEW PROJECTS
OFFICE**

397 POWER STATION ROAD,
STANWELL, QLD 4702

TITLE
**HYDRAULIC SERVICES
LEGEND, LOCALITY PLAN,
SYMBOLS & LINE TYPES**

APPROVAL ISSUE

NOT TO BE USED FOR CONSTRUCTION

DRAWN	J.P.	SCALE @ A1
CHECKED	H.R.	NTS
APPROVED	H.R.	
CREATED	DEC 25	
JOB No.	DRAWING No.	REV
Q250128	H0001	G