



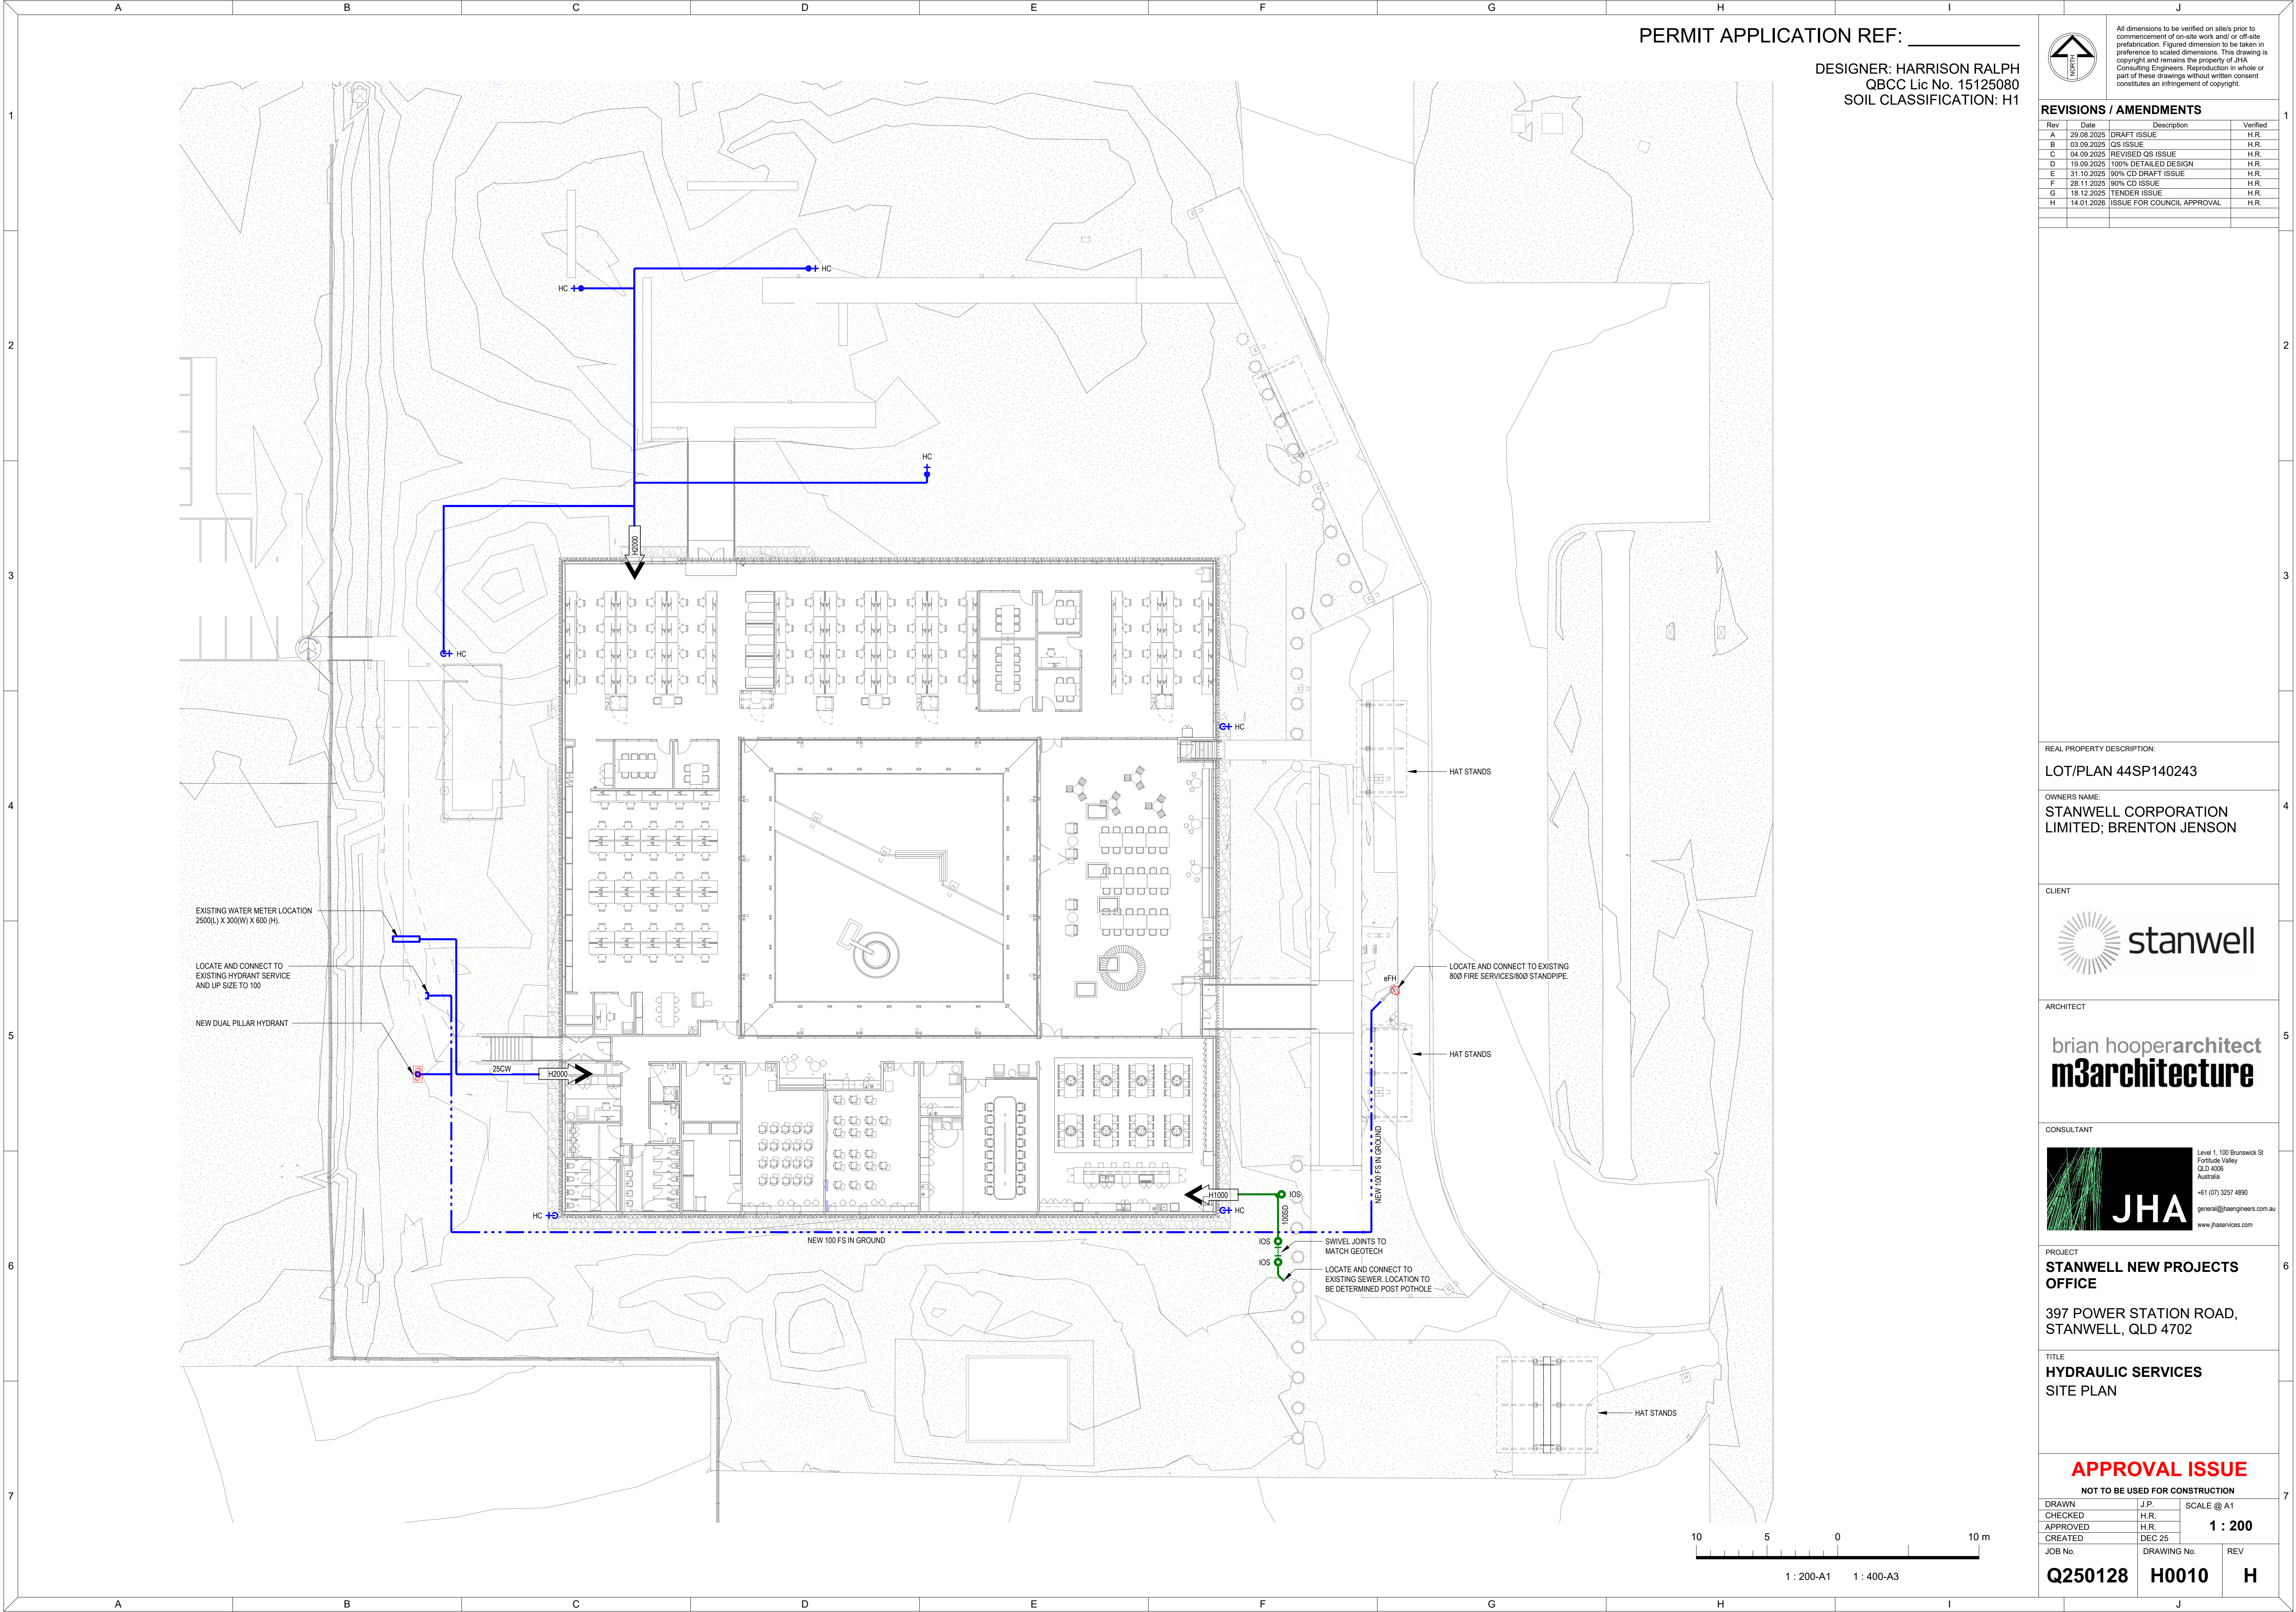

PERMIT APPLICATION REF: _____

DESIGNER: HARRISON RALPH
QBCC Lic No. 15125080
SOIL CLASSIFICATION: H1

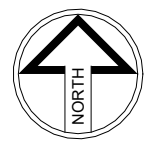

All dimensions to be verified on site/s prior to commencement of on-site work and/or off-site prefabrication. Figured dimension to be taken in preference to scaled dimensions. This drawing is copyright and remains the property of JHA Consulting Engineers. Reproduction in whole or part of these drawings without written consent constitutes an infringement of copyright.

REVISIONS / AMENDMENTS

Rev	Date	Description	Verified
A	29.08.2025	DRAFT ISSUE	H.R.
B	03.09.2025	QS ISSUE	H.R.
C	04.09.2025	REVISED QS ISSUE	H.R.
D	19.09.2025	100% DETAILED DESIGN	H.R.
E	31.10.2025	90% CD DRAFT ISSUE	H.R.
F	28.11.2025	90% CD ISSUE	H.R.
G	18.12.2025	TENDER ISSUE	H.R.
H	14.01.2026	ISSUE FOR COUNCIL APPROVAL	H.R.

REAL PROPERTY DESCRIPTION:

LOT/PLAN 44SP140243

OWNERS NAME:
STANWELL CORPORATION
LIMITED; BRENTON JENSON

CLIENT



ARCHITECT

brian hooper**architect**
m3architecture

CONSULTANT

Level 1, 100 Brunswick St
Fortitude Valley
QLD 4006
Australia
+61 (07) 3257 4890
general@jhaengineers.com.au
www.jhaservices.com

PROJECT

STANWELL NEW PROJECTS
OFFICE

397 POWER STATION ROAD,
STANWELL, QLD 4702

TITLE

HYDRAULIC SERVICES
SITE PLAN

APPROVAL ISSUE

NOT TO BE USED FOR CONSTRUCTION

DRAWN	J.P.	SCALE @ A1
CHECKED	H.R.	1 : 200
APPROVED	H.R.	
CREATED	DEC 25	
JOB No.	DRAWING No.	REV
Q250128	H0010	H