


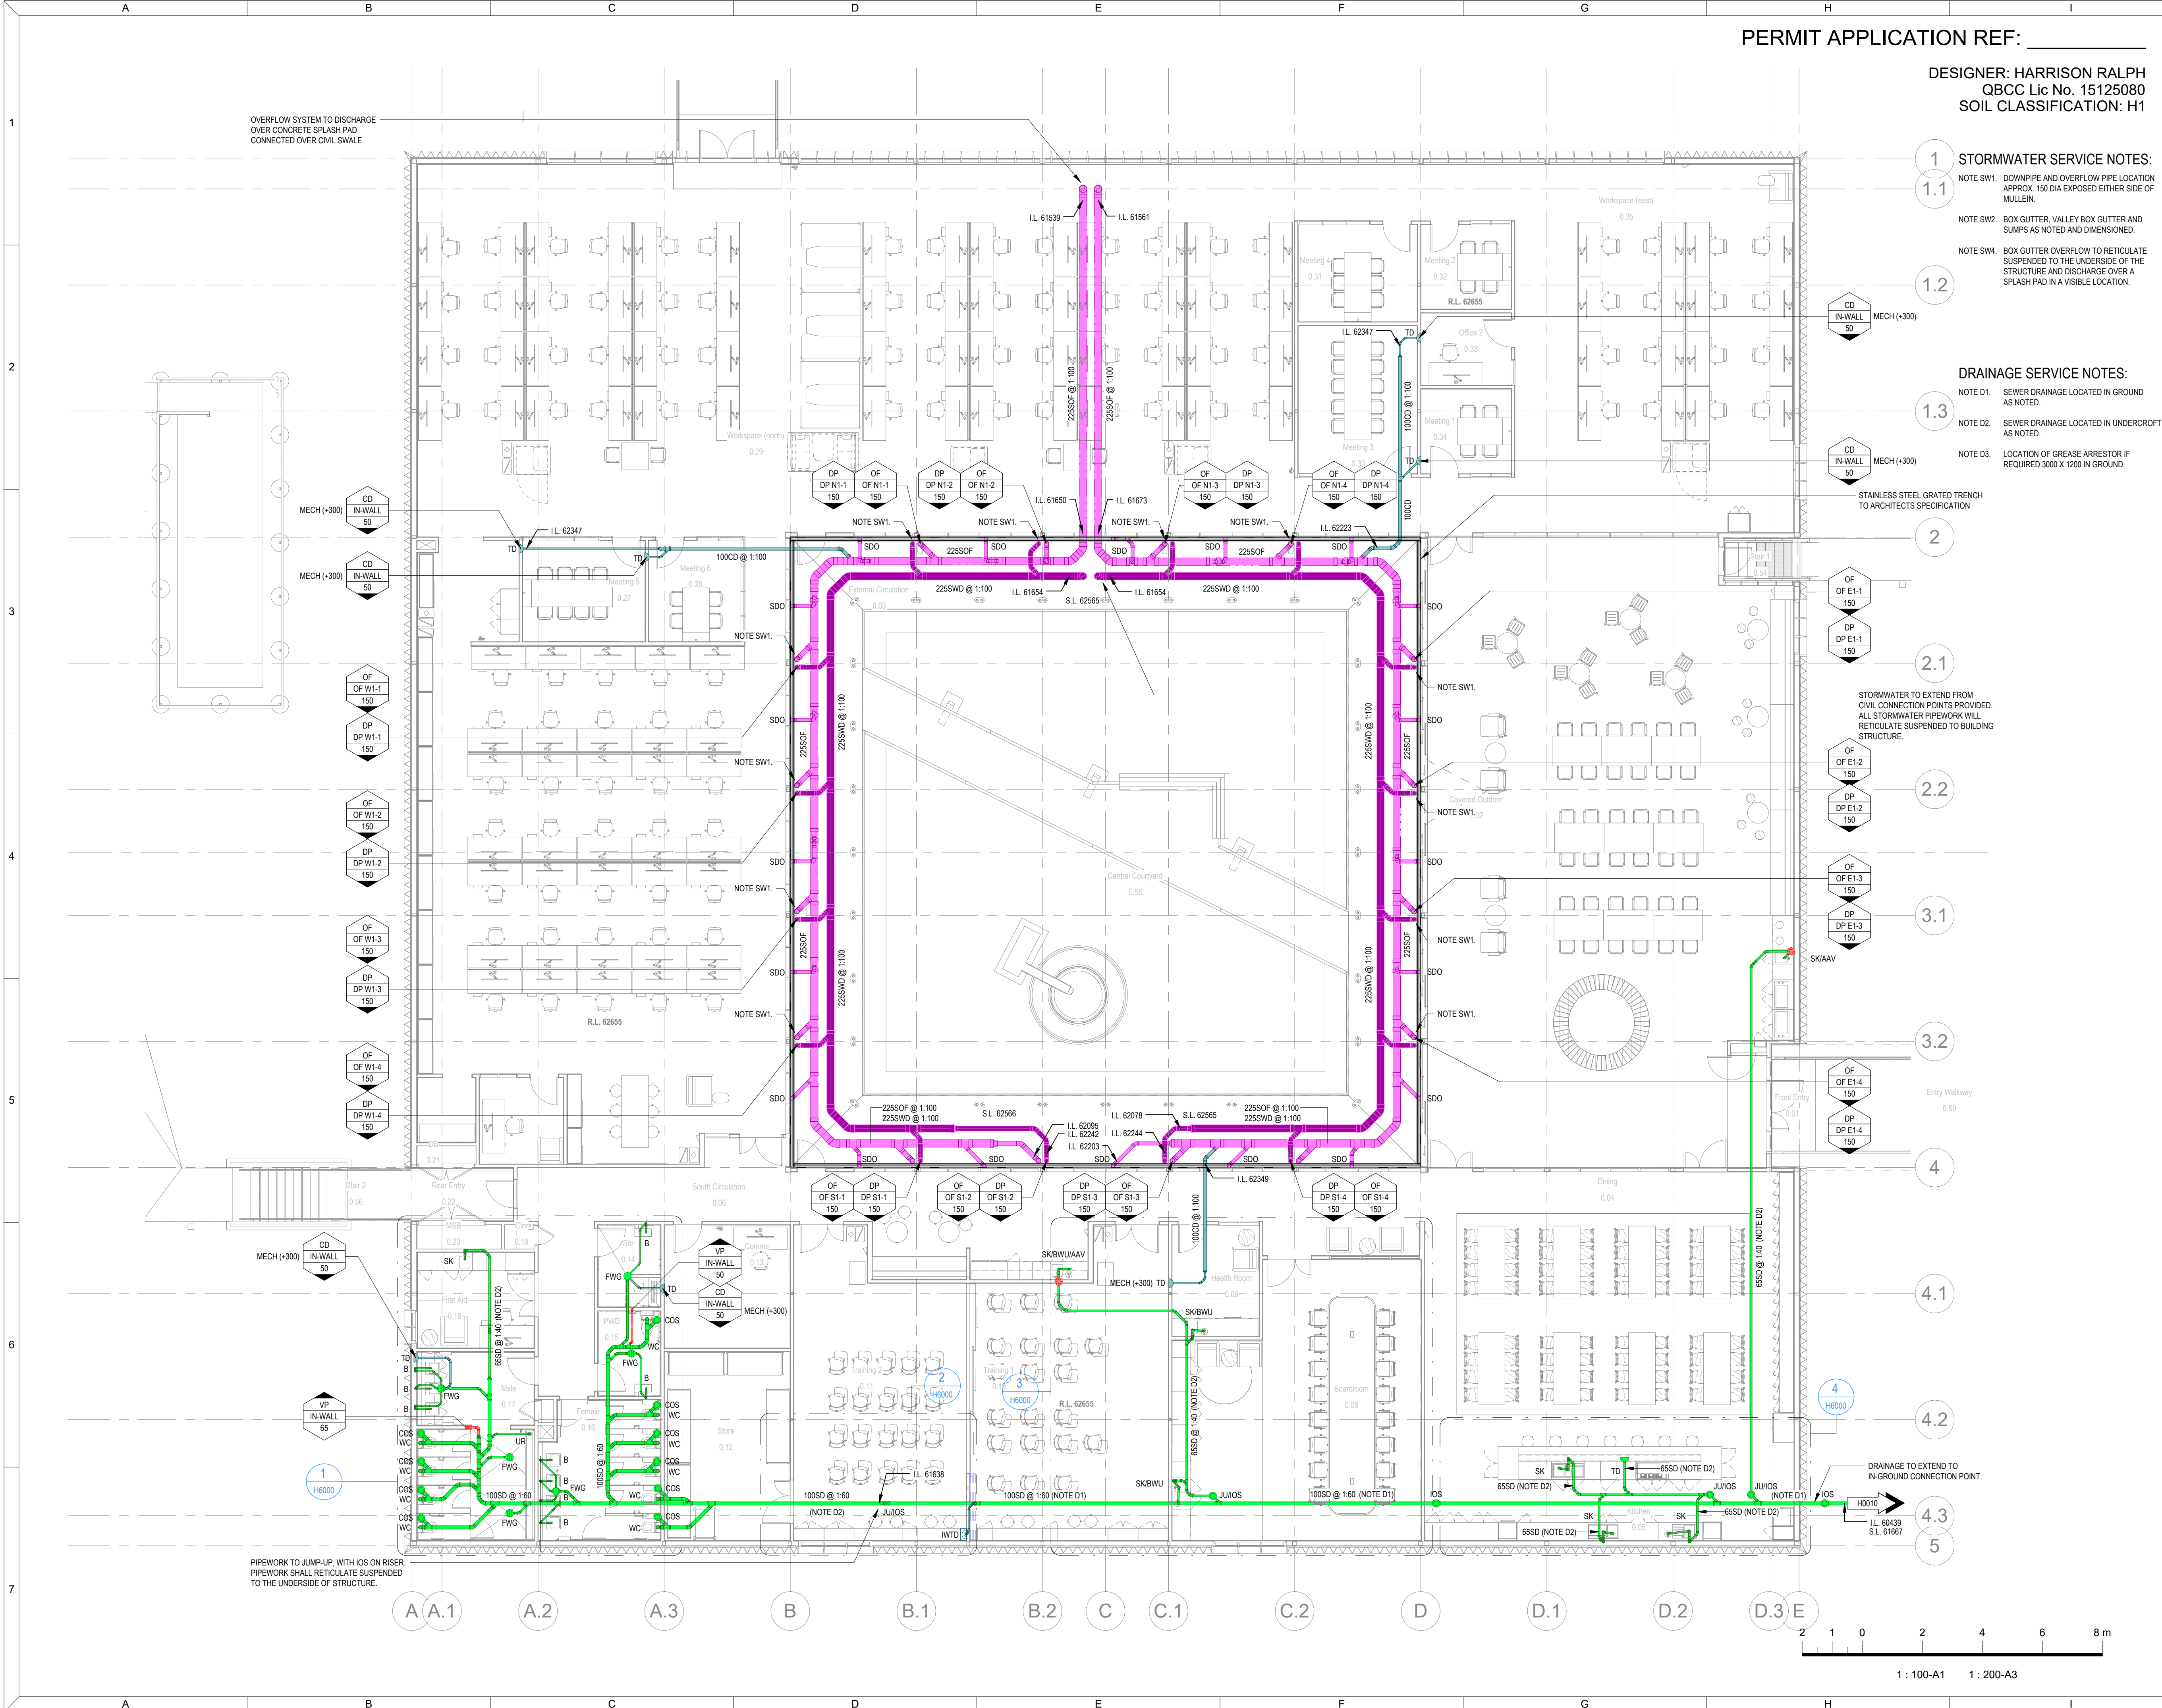

PERMIT APPLICATION REF: _____

DESIGNER: HARRISON RALPH
QBCC Lic No. 15125080
SOIL CLASSIFICATION: H1

All dimensions to be verified on site prior to commencement of on-site work and/or off-site prefabrication. Figured dimension to be taken in preference to scaled dimensions. This drawing is copyright and remains the property of JHA Consulting Engineers. Reproduction in whole or part of these drawings without written consent constitutes an infringement of copyright.

REVISIONS / AMENDMENTS			
Rev	Date	Description	Verified
A	29.08.2025	DRAFT ISSUE	H.R.
B	03.09.2025	QS ISSUE	H.R.
C	04.09.2025	REVISED QS ISSUE	H.R.
D	19.09.2025	100% DETAILED DESIGN	H.R.
E	31.10.2025	90% CD DRAFT ISSUE	H.R.
F	28.11.2025	90% CD ISSUE	H.R.
G	18.12.2025	TENDER ISSUE	H.R.
H	14.01.2026	ISSUE FOR COUNCIL APPROVAL	H.R.

- 1
- 1.1
- 1.2
- 1.3
- 2
- 2.1
- 2.2
- 3.1
- 3.2
- 4
- 4.1
- 4.2
- 4.3
- 5

STORMWATER SERVICE NOTES:

NOTE SW1. DOWNPIPE AND OVERFLOW PIPE LOCATION APPROX. 150 DIA EXPOSED EITHER SIDE OF MULLEIN.

NOTE SW2. BOX GUTTER, VALLEY BOX GUTTER AND SUMPS AS NOTED AND DIMENSIONED.

NOTE SW4. BOX GUTTER OVERFLOW TO RETICULATE SUSPENDED TO THE UNDERSIDE OF THE STRUCTURE AND DISCHARGE OVER A SPLASH PAD IN A VISIBLE LOCATION.

DRAINAGE SERVICE NOTES:

NOTE D1. SEWER DRAINAGE LOCATED IN GROUND AS NOTED.

NOTE D2. SEWER DRAINAGE LOCATED IN UNDERCROFT AS NOTED.

NOTE D3. LOCATION OF GREASE ARRESTOR IF REQUIRED 3000 X 1200 IN GROUND.

REAL PROPERTY DESCRIPTION:
LOT/PLAN 44SP140243

OWNERS NAME:
STANWELL CORPORATION LIMITED; BRENTON JENSON



PROJECT
STANWELL NEW PROJECTS OFFICE

397 POWER STATION ROAD,
STANWELL, QLD 4702

TITLE
**HYDRAULIC SERVICES
GROUND FLOOR DRAINAGE
SERVICES**

APPROVAL ISSUE

NOT TO BE USED FOR CONSTRUCTION

DRAWN	J.P.	SCALE @ A1
CHECKED	H.R.	1 : 100
APPROVED	H.R.	
CREATED	DEC 25	

JOB No.	DRAWING No.	REV
Q250128	H1000	H