


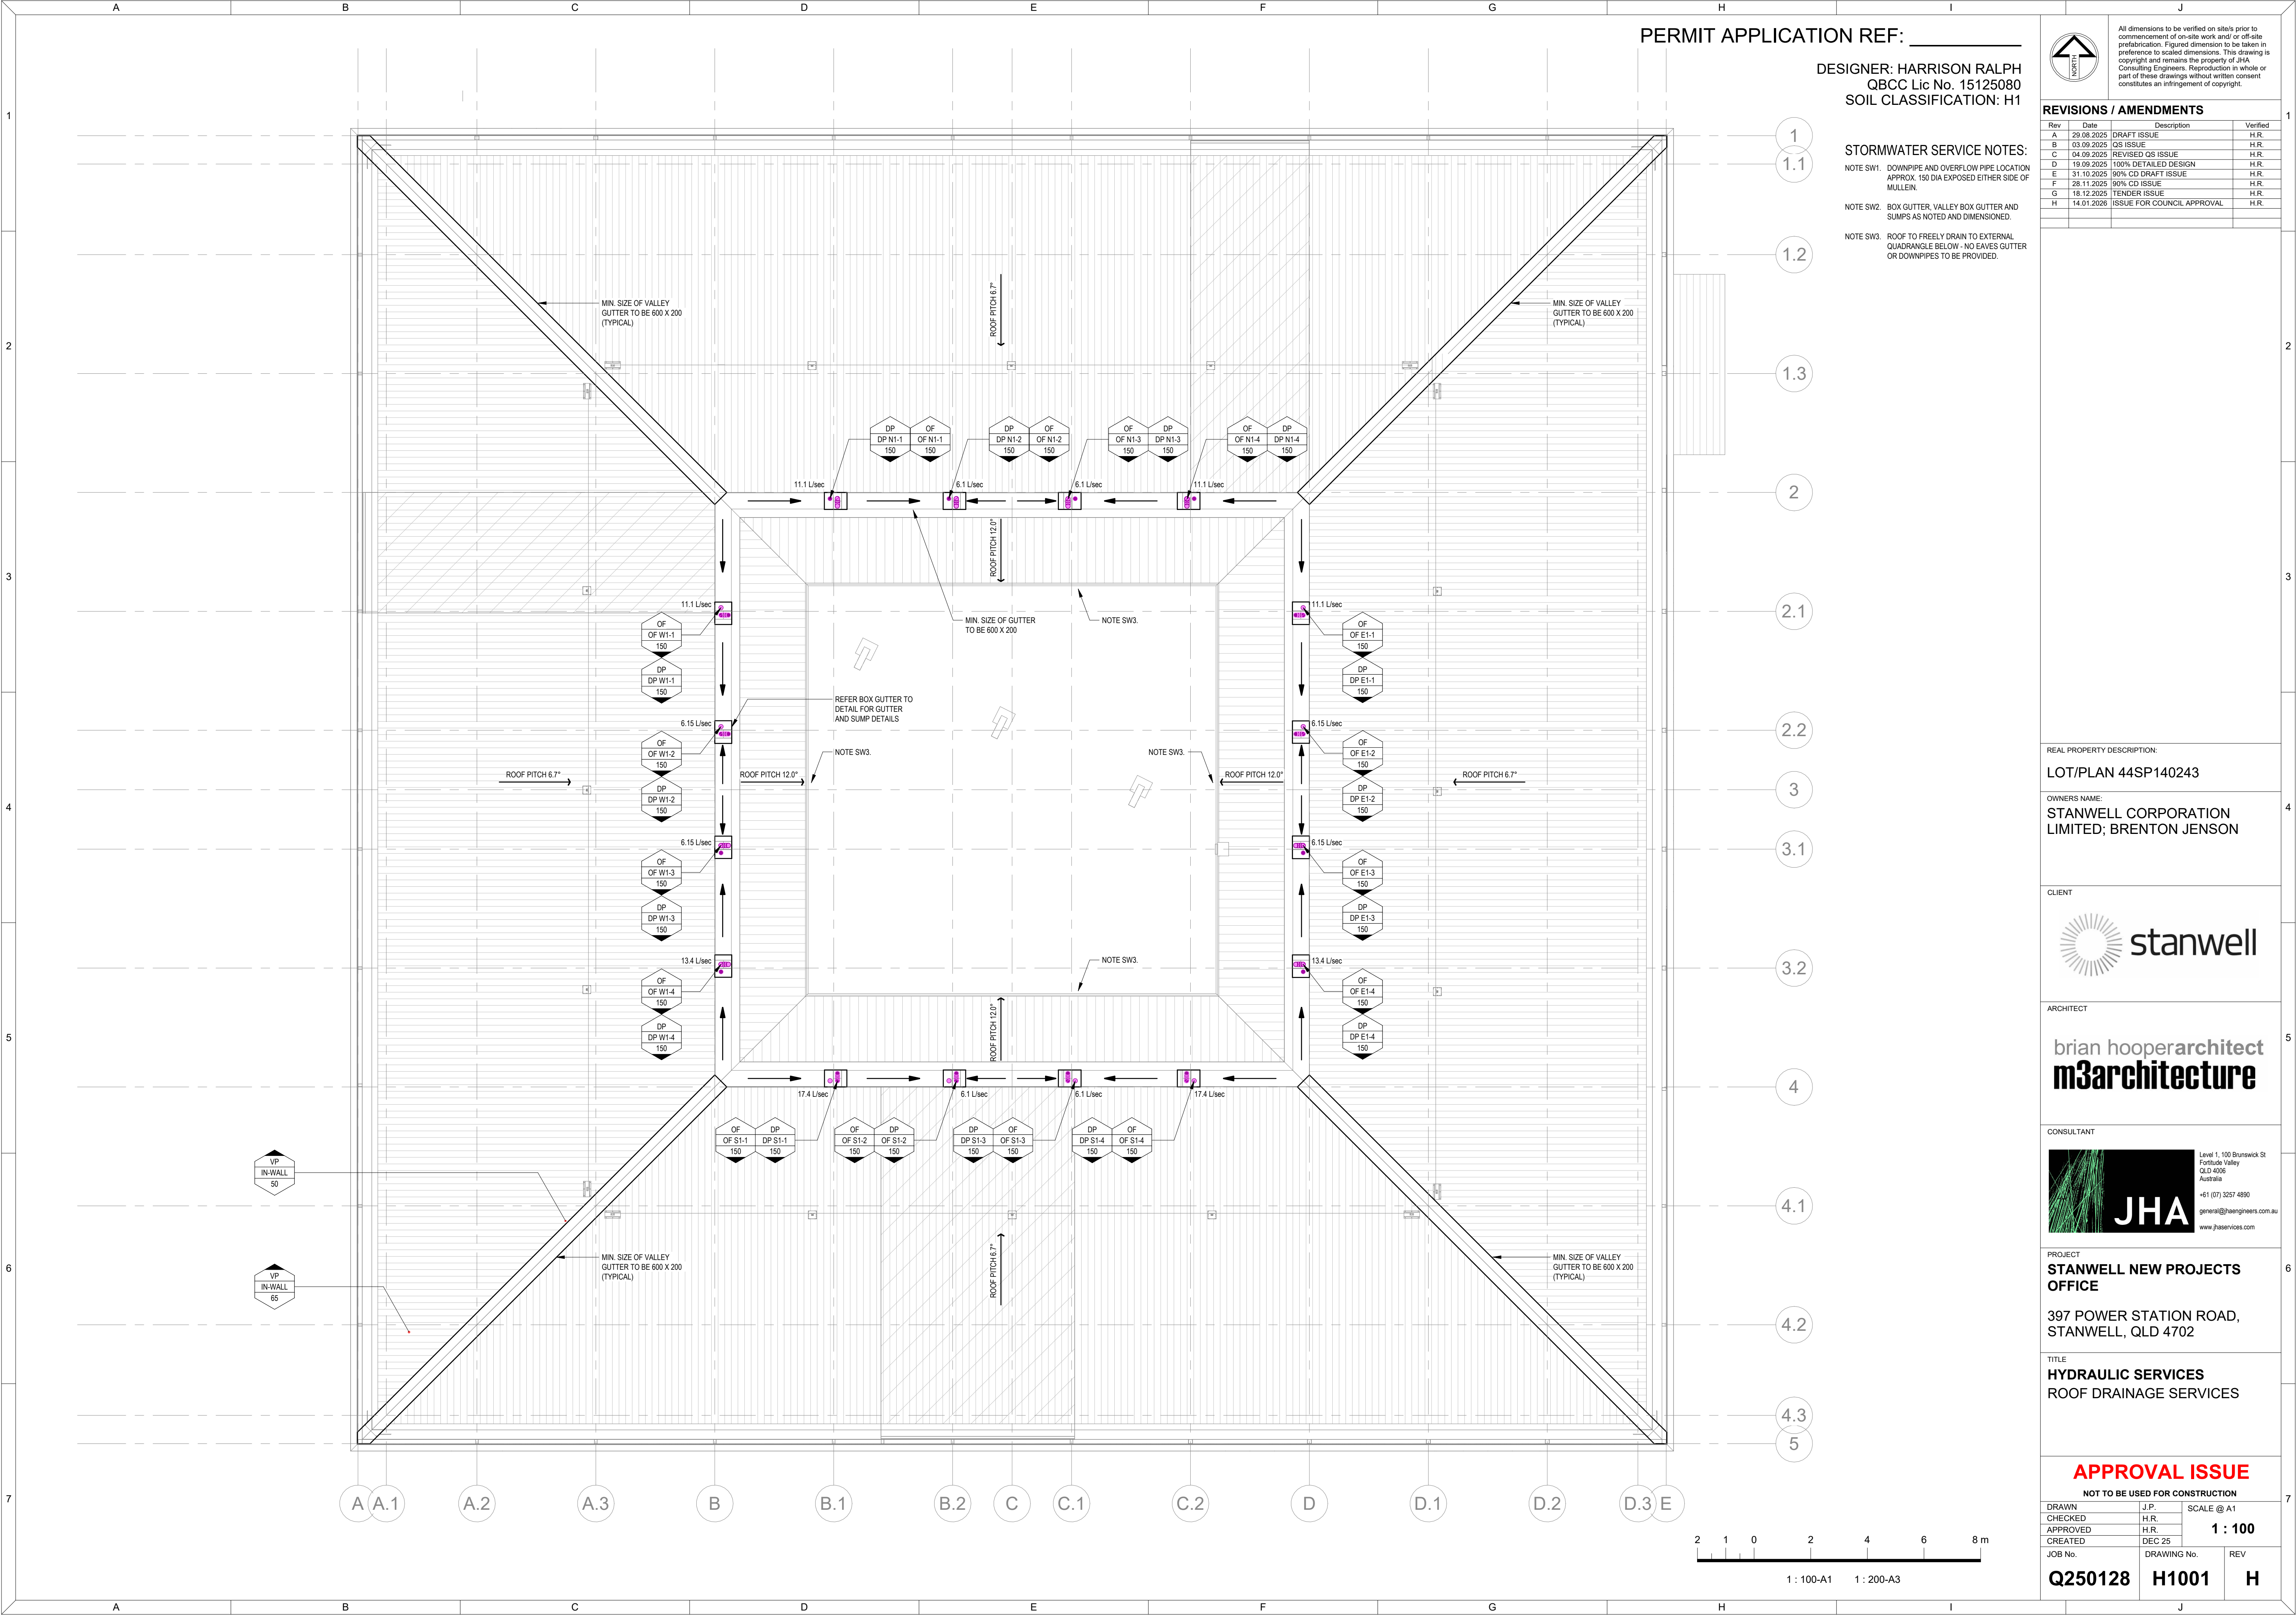

PERMIT APPLICATION REF: _____

DESIGNER: HARRISON RALPH
QBCC Lic No. 15125080
SOIL CLASSIFICATION: H1

STORMWATER SERVICE NOTES:

- NOTE SW1. DOWNPIPE AND OVERFLOW PIPE LOCATION APPROX. 150 DIA EXPOSED EITHER SIDE OF MULLEIN.
- NOTE SW2. BOX GUTTER, VALLEY BOX GUTTER AND SUMPS AS NOTED AND DIMENSIONED.
- NOTE SW3. ROOF TO FREELY DRAIN TO EXTERNAL QUADRANGLE BELOW - NO EAVES GUTTER OR DOWNPIPES TO BE PROVIDED.

All dimensions to be verified on site/s prior to commencement of on-site work and/or off-site prefabrication. Figured dimension to be taken in preference to scaled dimensions. This drawing is copyright and remains the property of JHA Consulting Engineers. Reproduction in whole or part of these drawings without written consent constitutes an infringement of copyright.

REVISIONS / AMENDMENTS			
Rev	Date	Description	Verified
A	29.08.2025	DRAFT ISSUE	H.R.
B	03.09.2025	QS ISSUE	H.R.
C	04.09.2025	REVISED QS ISSUE	H.R.
D	19.09.2025	100% DETAILED DESIGN	H.R.
E	31.10.2025	90% CD DRAFT ISSUE	H.R.
F	28.11.2025	90% CD ISSUE	H.R.
G	18.12.2025	TENDER ISSUE	H.R.
H	14.01.2026	ISSUE FOR COUNCIL APPROVAL	H.R.

REAL PROPERTY DESCRIPTION:
LOT/PLAN 44SP140243

OWNERS NAME:
STANWELL CORPORATION LIMITED; BRENTON JENSON



ARCHITECT

brian hooperarchitect
m3architecture

Level 1, 100 Brunswick St
Fortitude Valley
QLD 4006
Australia
+61 (07) 3257 4890
general@jhaengineers.com.au
www.jhaservices.com

PROJECT
STANWELL NEW PROJECTS OFFICE

397 POWER STATION ROAD,
STANWELL, QLD 4702

TITLE
HYDRAULIC SERVICES
ROOF DRAINAGE SERVICES

APPROVAL ISSUE

NOT TO BE USED FOR CONSTRUCTION

DRAWN	J.P.	SCALE @ A1
CHECKED	H.R.	1 : 100
APPROVED	H.R.	
CREATED	DEC 25	

JOB No.	DRAWING No.	REV
Q250128	H1001	H