


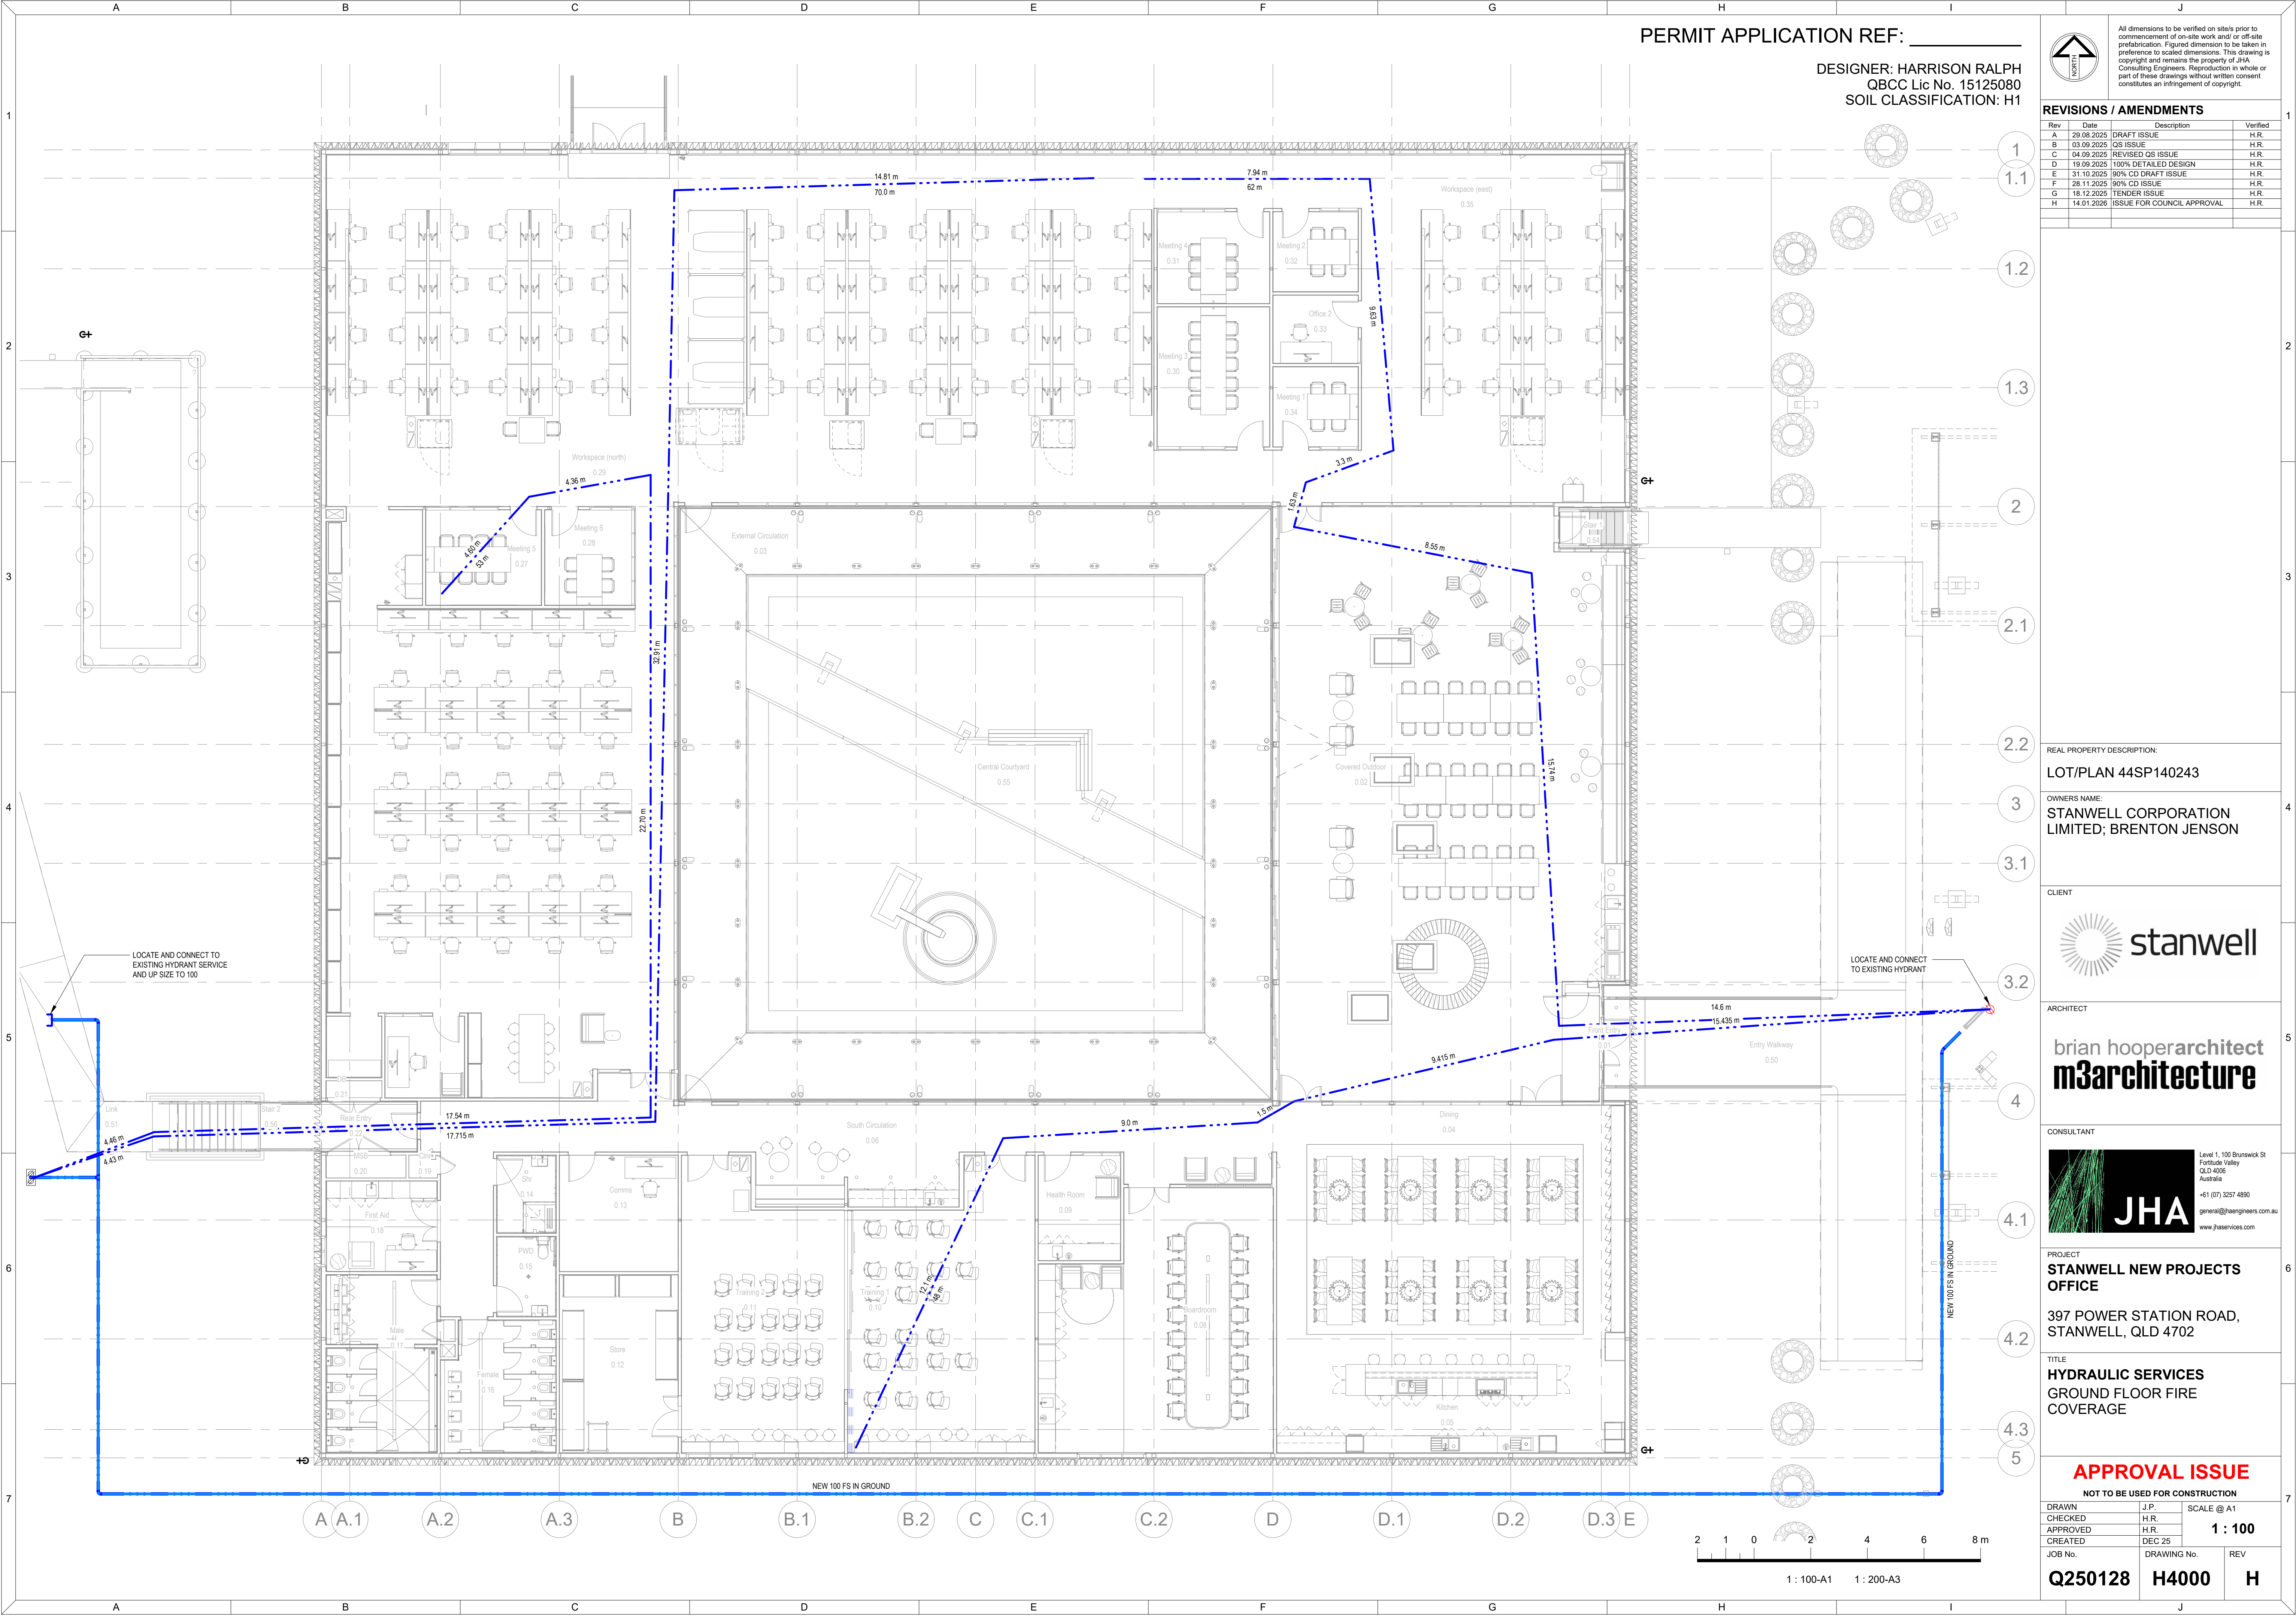

PERMIT APPLICATION REF: \_\_\_\_\_

DESIGNER: HARRISON RALPH  
QBCC Lic No. 15125080  
SOIL CLASSIFICATION: H1



All dimensions to be verified on site prior to commencement of on-site work and/or off-site prefabrication. Figured dimension to be taken in preference to scaled dimensions. This drawing is copyright and remains the property of JHA Consulting Engineers. Reproduction in whole or part of these drawings without written consent constitutes an infringement of copyright.

| REVISIONS / AMENDMENTS |            |                            |          |
|------------------------|------------|----------------------------|----------|
| Rev                    | Date       | Description                | Verified |
| A                      | 29.08.2025 | DRAFT ISSUE                | H.R.     |
| B                      | 03.09.2025 | QS ISSUE                   | H.R.     |
| C                      | 04.09.2025 | REVISED QS ISSUE           | H.R.     |
| D                      | 19.09.2025 | 100% DETAILED DESIGN       | H.R.     |
| E                      | 31.10.2025 | 90% CD DRAFT ISSUE         | H.R.     |
| F                      | 28.11.2025 | 90% CD ISSUE               | H.R.     |
| G                      | 18.12.2025 | TENDER ISSUE               | H.R.     |
| H                      | 14.01.2026 | ISSUE FOR COUNCIL APPROVAL | H.R.     |

REAL PROPERTY DESCRIPTION:  
LOT/PLAN 44SP140243

OWNERS NAME:  
STANWELL CORPORATION LIMITED; BRENTON JENSON



stanwell



brian hooperarchitect  
m3architecture



JHA

Level 1, 100 Brunswick St  
Fortitude Valley  
QLD 4006  
Australia  
+61 (07) 3257 4890  
general@jhaengineers.com.au  
www.jhaservices.com

PROJECT  
STANWELL NEW PROJECTS  
OFFICE

397 POWER STATION ROAD,  
STANWELL, QLD 4702

TITLE  
HYDRAULIC SERVICES  
GROUND FLOOR FIRE  
COVERAGE

APPROVAL ISSUE

NOT TO BE USED FOR CONSTRUCTION

|          |        |            |
|----------|--------|------------|
| DRAWN    | J.P.   | SCALE @ A1 |
| CHECKED  | H.R.   | 1 : 100    |
| APPROVED | H.R.   |            |
| CREATED  | DEC 25 |            |

|         |             |     |
|---------|-------------|-----|
| JOB No. | DRAWING No. | REV |
| Q250128 | H4000       | H   |