


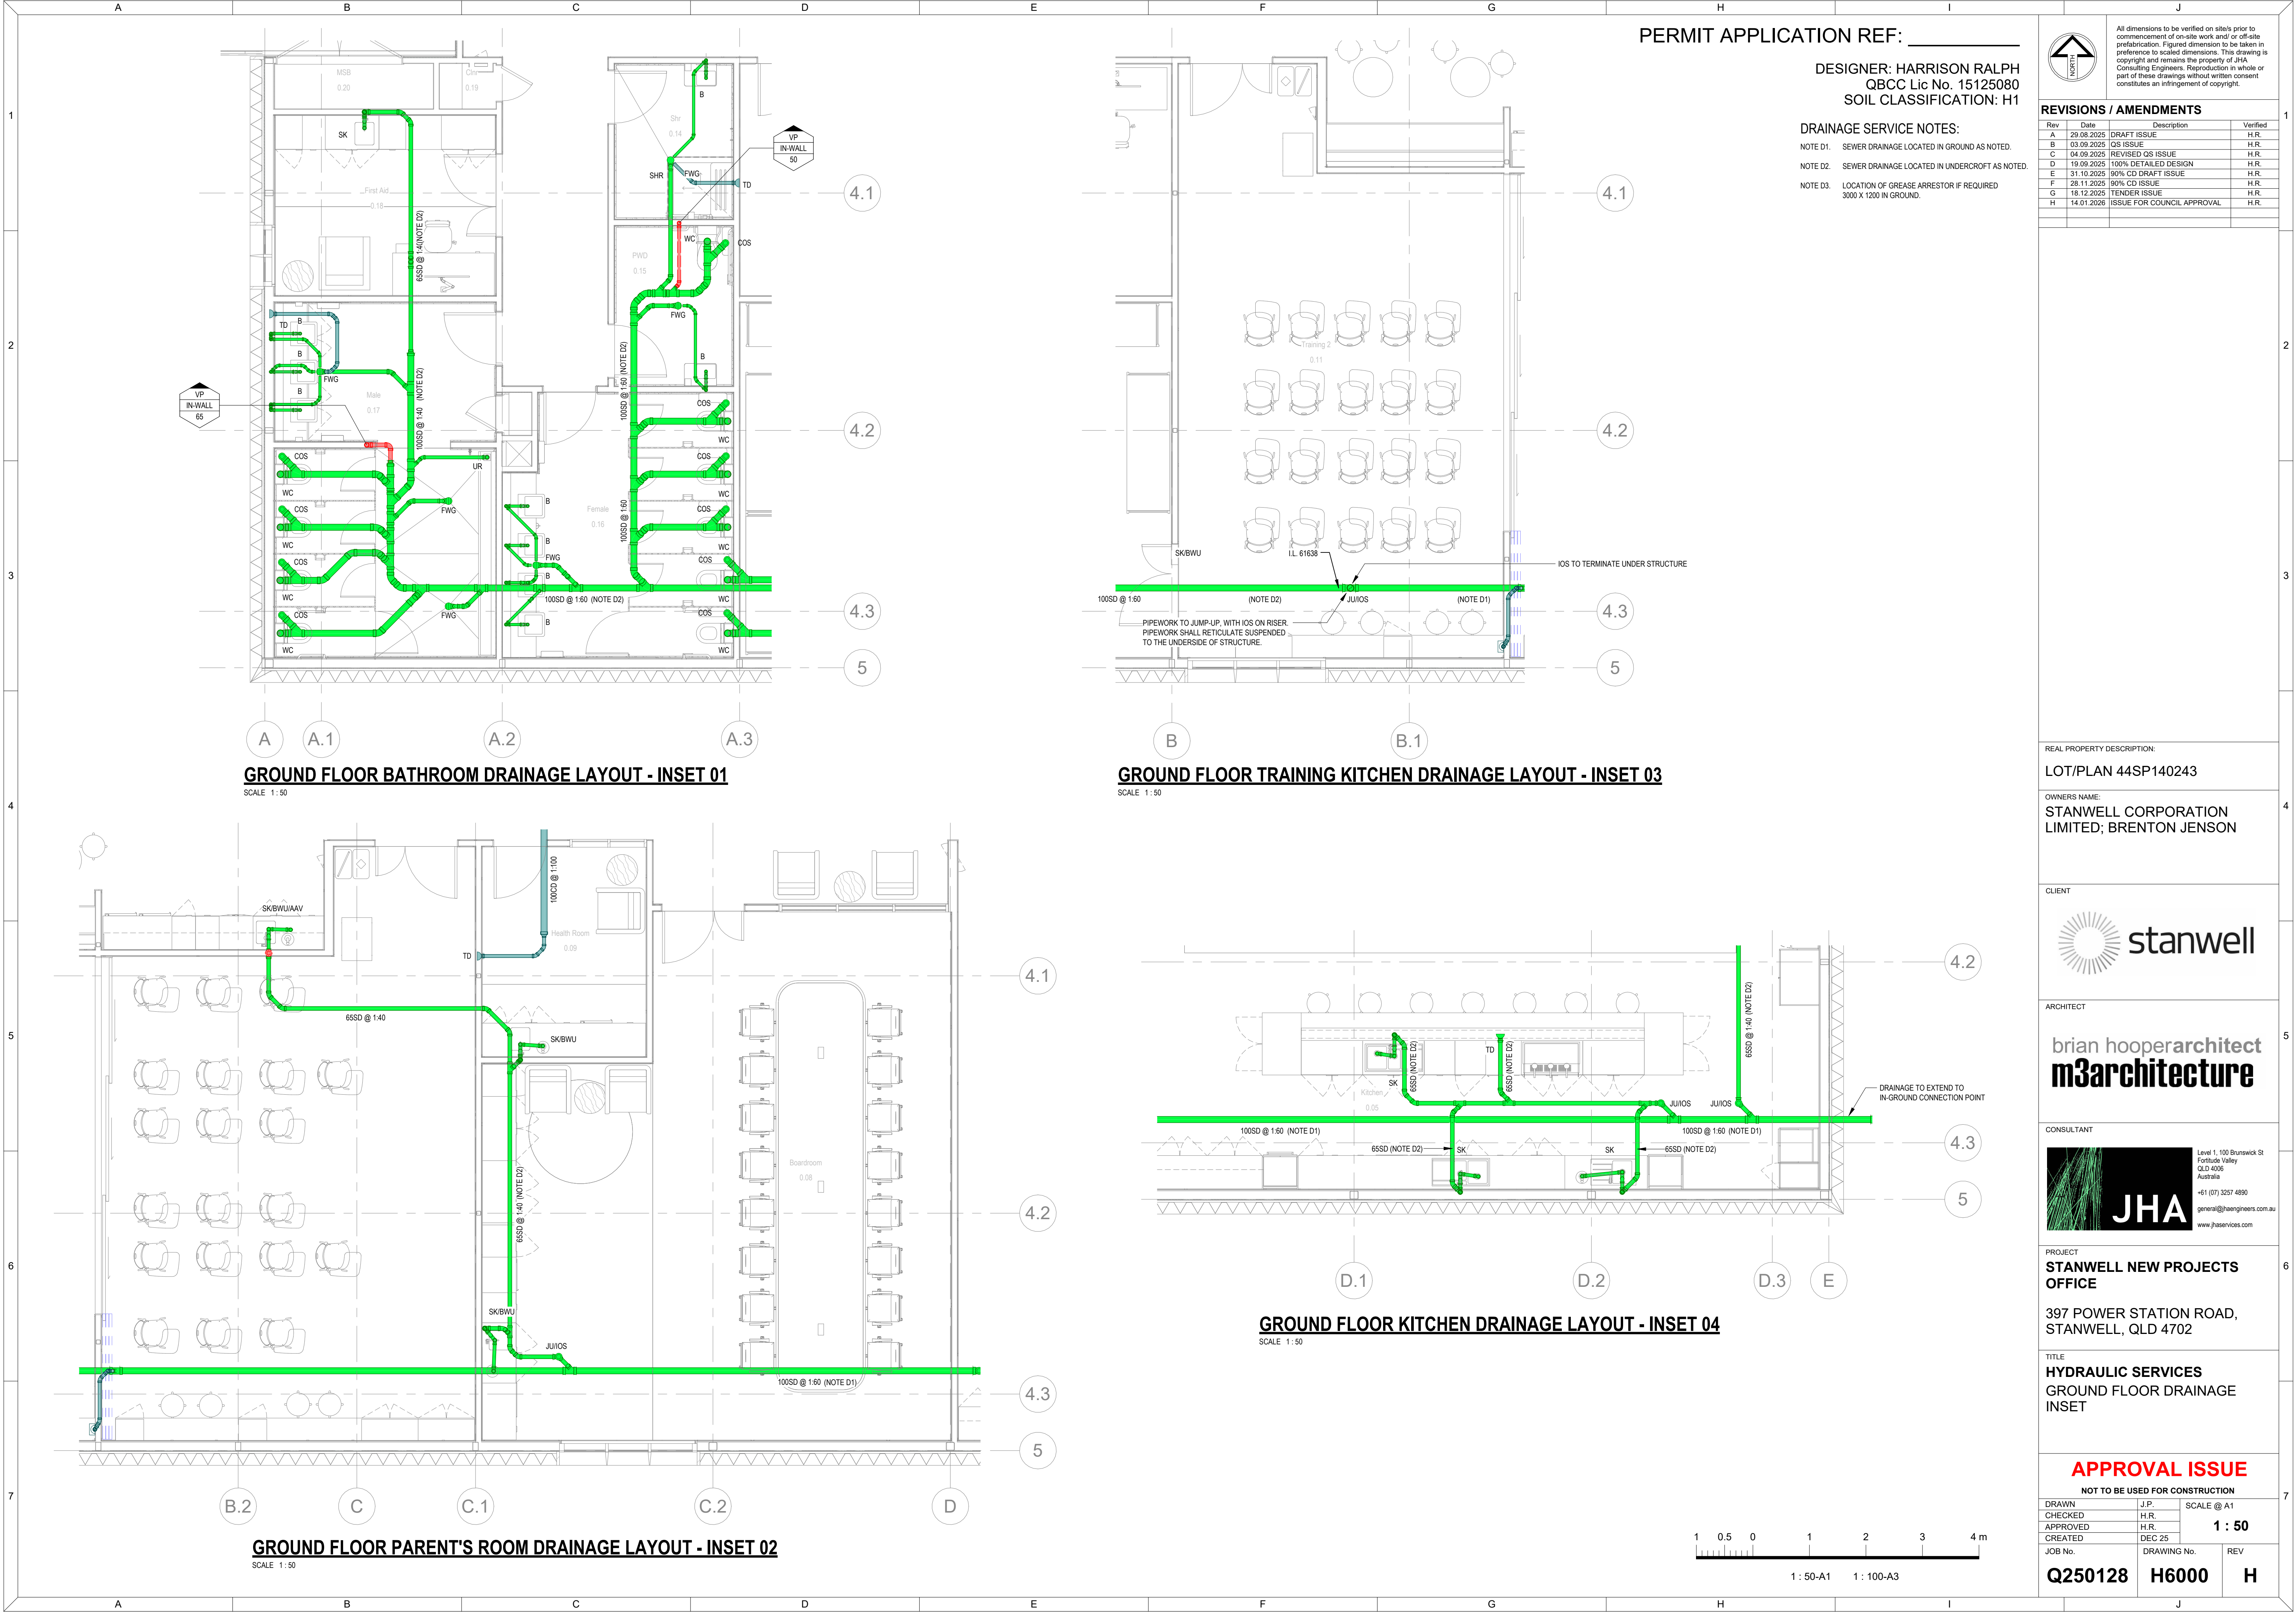

PERMIT APPLICATION REF: \_\_\_\_\_

DESIGNER: HARRISON RALPH  
QBCC Lic No. 15125080  
SOIL CLASSIFICATION: H1

DRAINAGE SERVICE NOTES:

- NOTE D1. SEWER DRAINAGE LOCATED IN GROUND AS NOTED.  
NOTE D2. SEWER DRAINAGE LOCATED IN UNDERCROFT AS NOTED.  
NOTE D3. LOCATION OF GREASE ARRESTOR IF REQUIRED  
3000 X 1200 IN GROUND.



All dimensions to be verified on site prior to commencement of on-site work and/or off-site prefabrication. Figured dimension to be taken in preference to scaled dimensions. This drawing is copyright and remains the property of JHA Consulting Engineers. Reproduction in whole or part of these drawings without written consent constitutes an infringement of copyright.

REVISIONS / AMENDMENTS

| Rev | Date       | Description                | Verified |
|-----|------------|----------------------------|----------|
| A   | 29.08.2025 | DRAFT ISSUE                | H.R.     |
| B   | 03.09.2025 | QS ISSUE                   | H.R.     |
| C   | 04.09.2025 | REVISED QS ISSUE           | H.R.     |
| D   | 19.09.2025 | 100% DETAILED DESIGN       | H.R.     |
| E   | 31.10.2025 | 90% CD DRAFT ISSUE         | H.R.     |
| F   | 28.11.2025 | 90% CD ISSUE               | H.R.     |
| G   | 18.12.2025 | TENDER ISSUE               | H.R.     |
| H   | 14.01.2026 | ISSUE FOR COUNCIL APPROVAL | H.R.     |

REAL PROPERTY DESCRIPTION:

LOT/PLAN 44SP140243

OWNERS NAME:

STANWELL CORPORATION  
LIMITED; BRENTON JENSON

CLIENT



ARCHITECT

brian hooperarchitect  
m3architecture

CONSULTANT



Level 1, 100 Brunswick St  
Fortitude Valley  
QLD 4006  
Australia  
+61 (07) 3257 4890  
general@jhaengineers.com.au  
www.jhaservices.com

PROJECT

STANWELL NEW PROJECTS  
OFFICE

397 POWER STATION ROAD,  
STANWELL, QLD 4702

TITLE

HYDRAULIC SERVICES  
GROUND FLOOR DRAINAGE  
INSET

APPROVAL ISSUE

NOT TO BE USED FOR CONSTRUCTION

|          |             |            |
|----------|-------------|------------|
| DRAWN    | J.P.        | SCALE @ A1 |
| CHECKED  | H.R.        | 1 : 50     |
| APPROVED | H.R.        |            |
| CREATED  | DEC 25      |            |
| JOB No.  | DRAWING No. | REV        |
| Q250128  | H6000       | H          |