



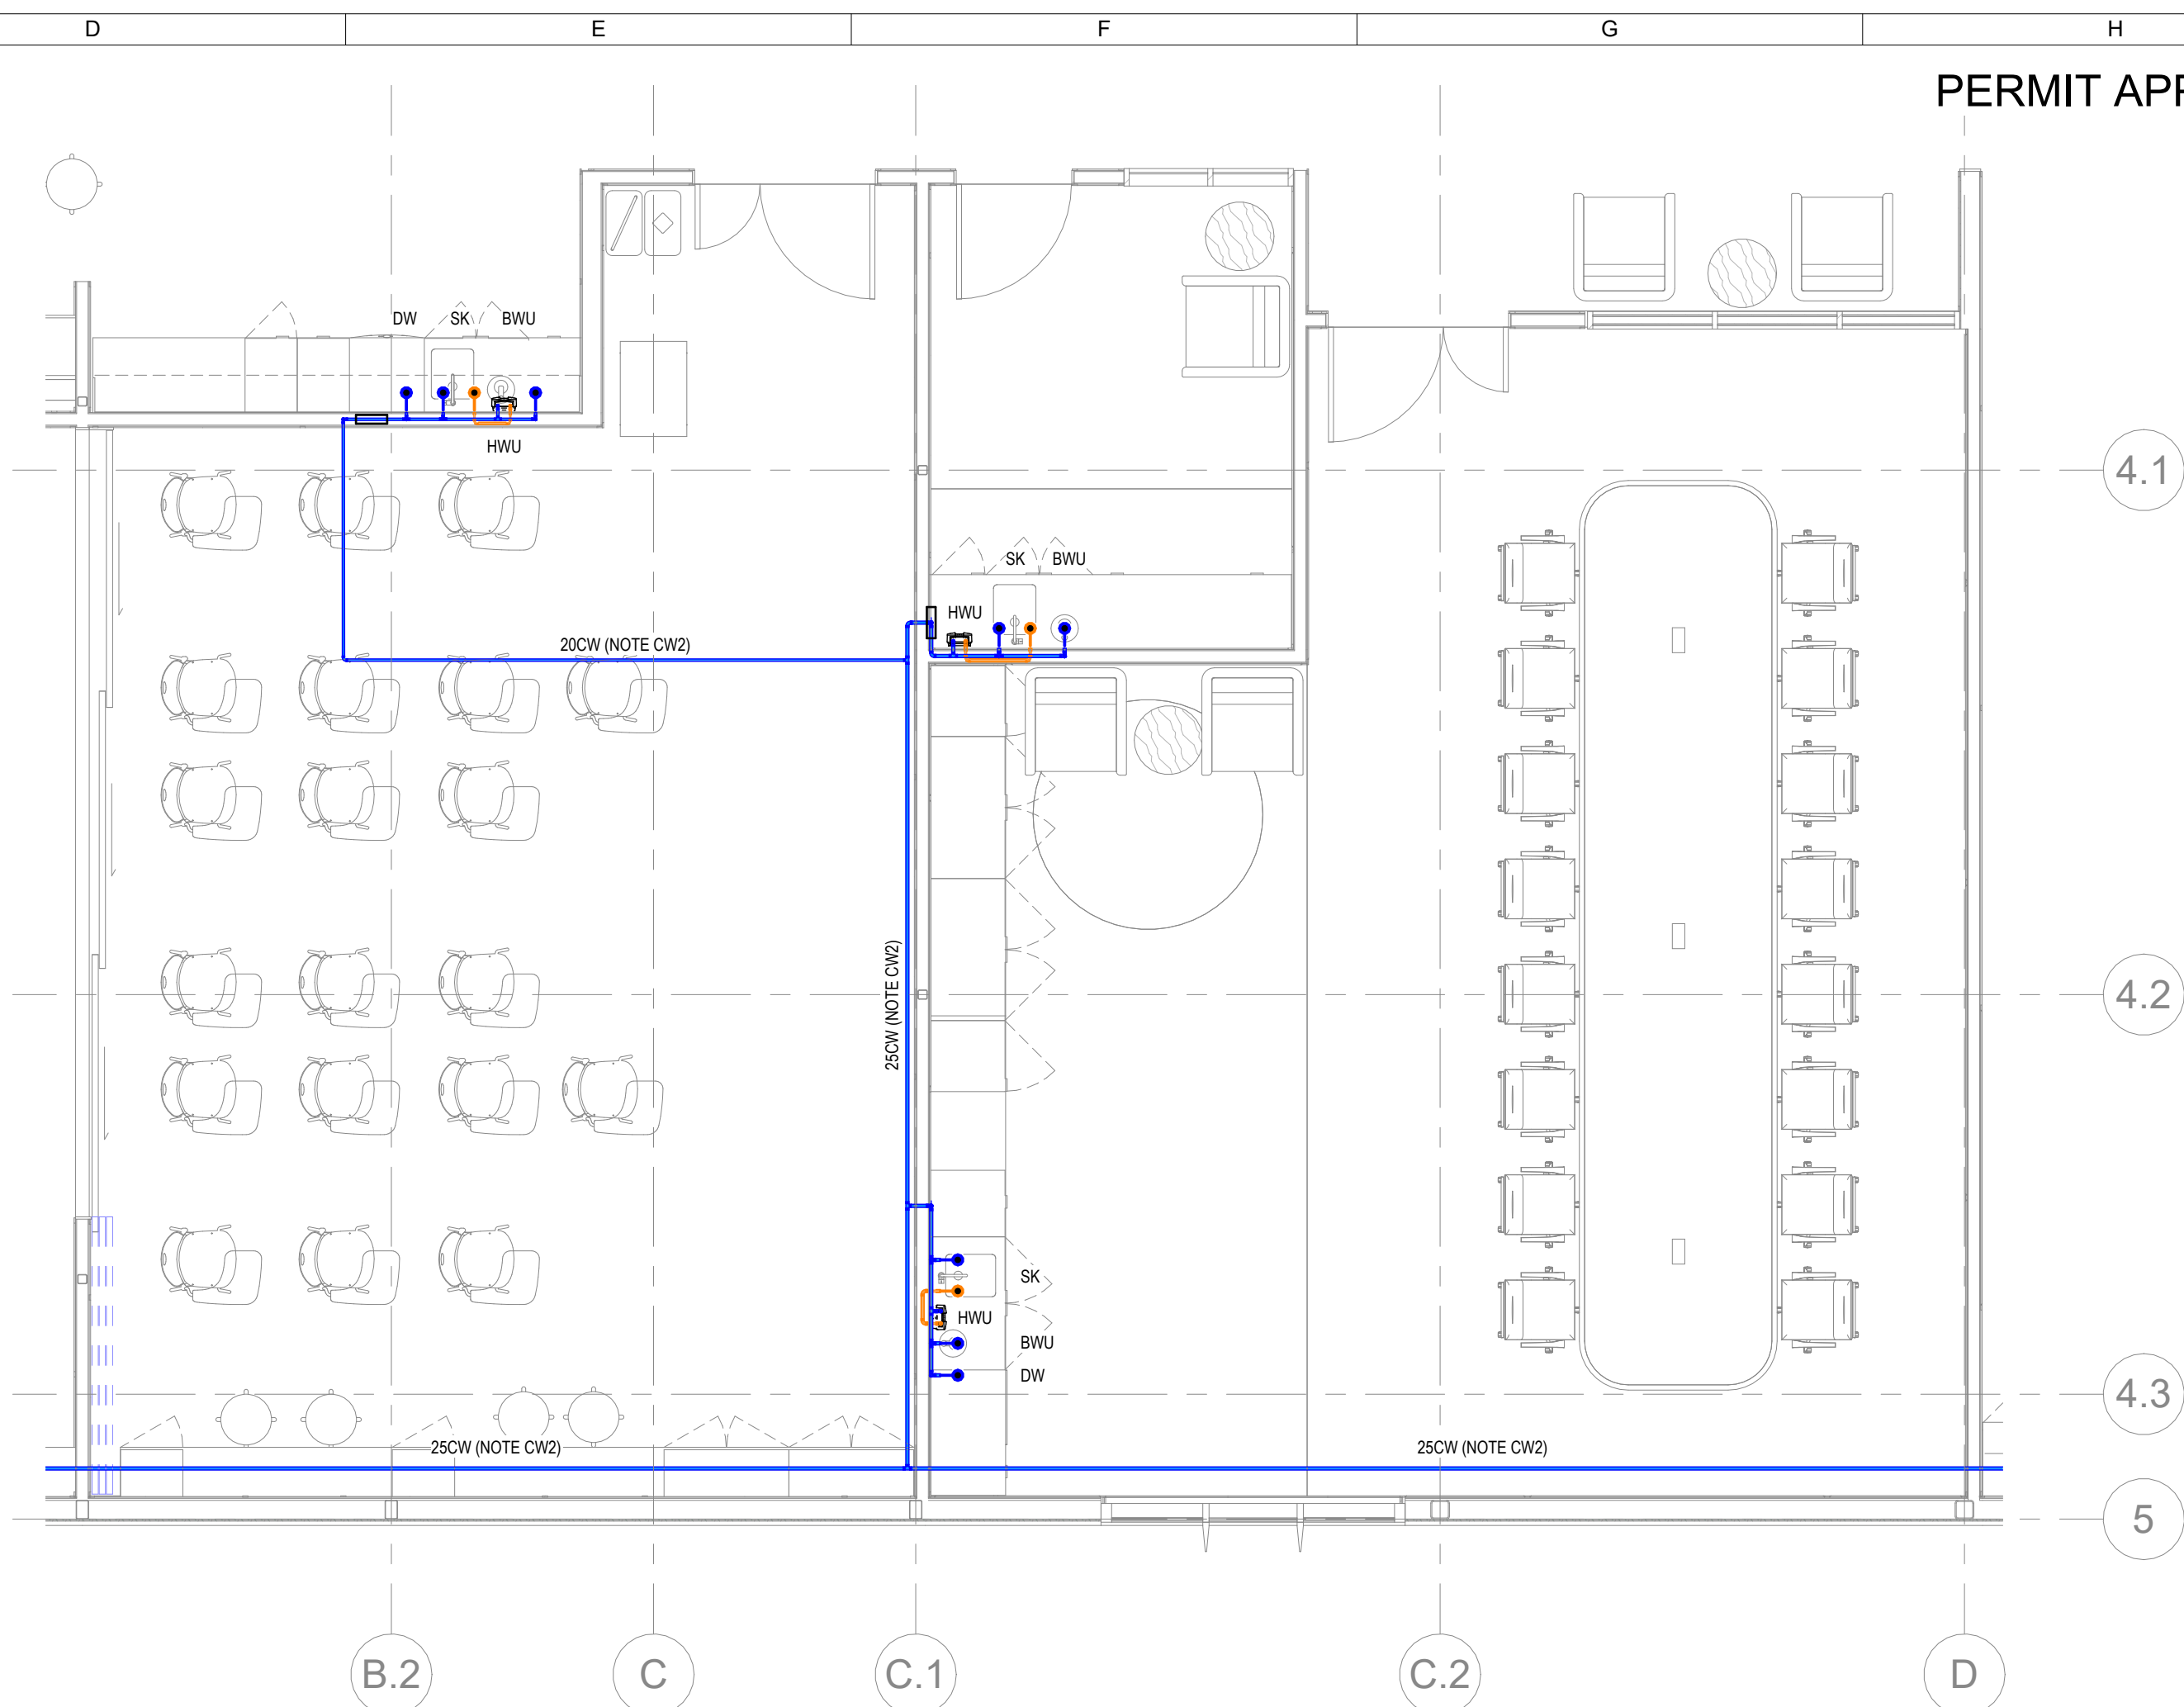

GROUND FLOOR TRAINING KITCHEN WATER LAYOUT - INSET 03

SCALE 1 : 50

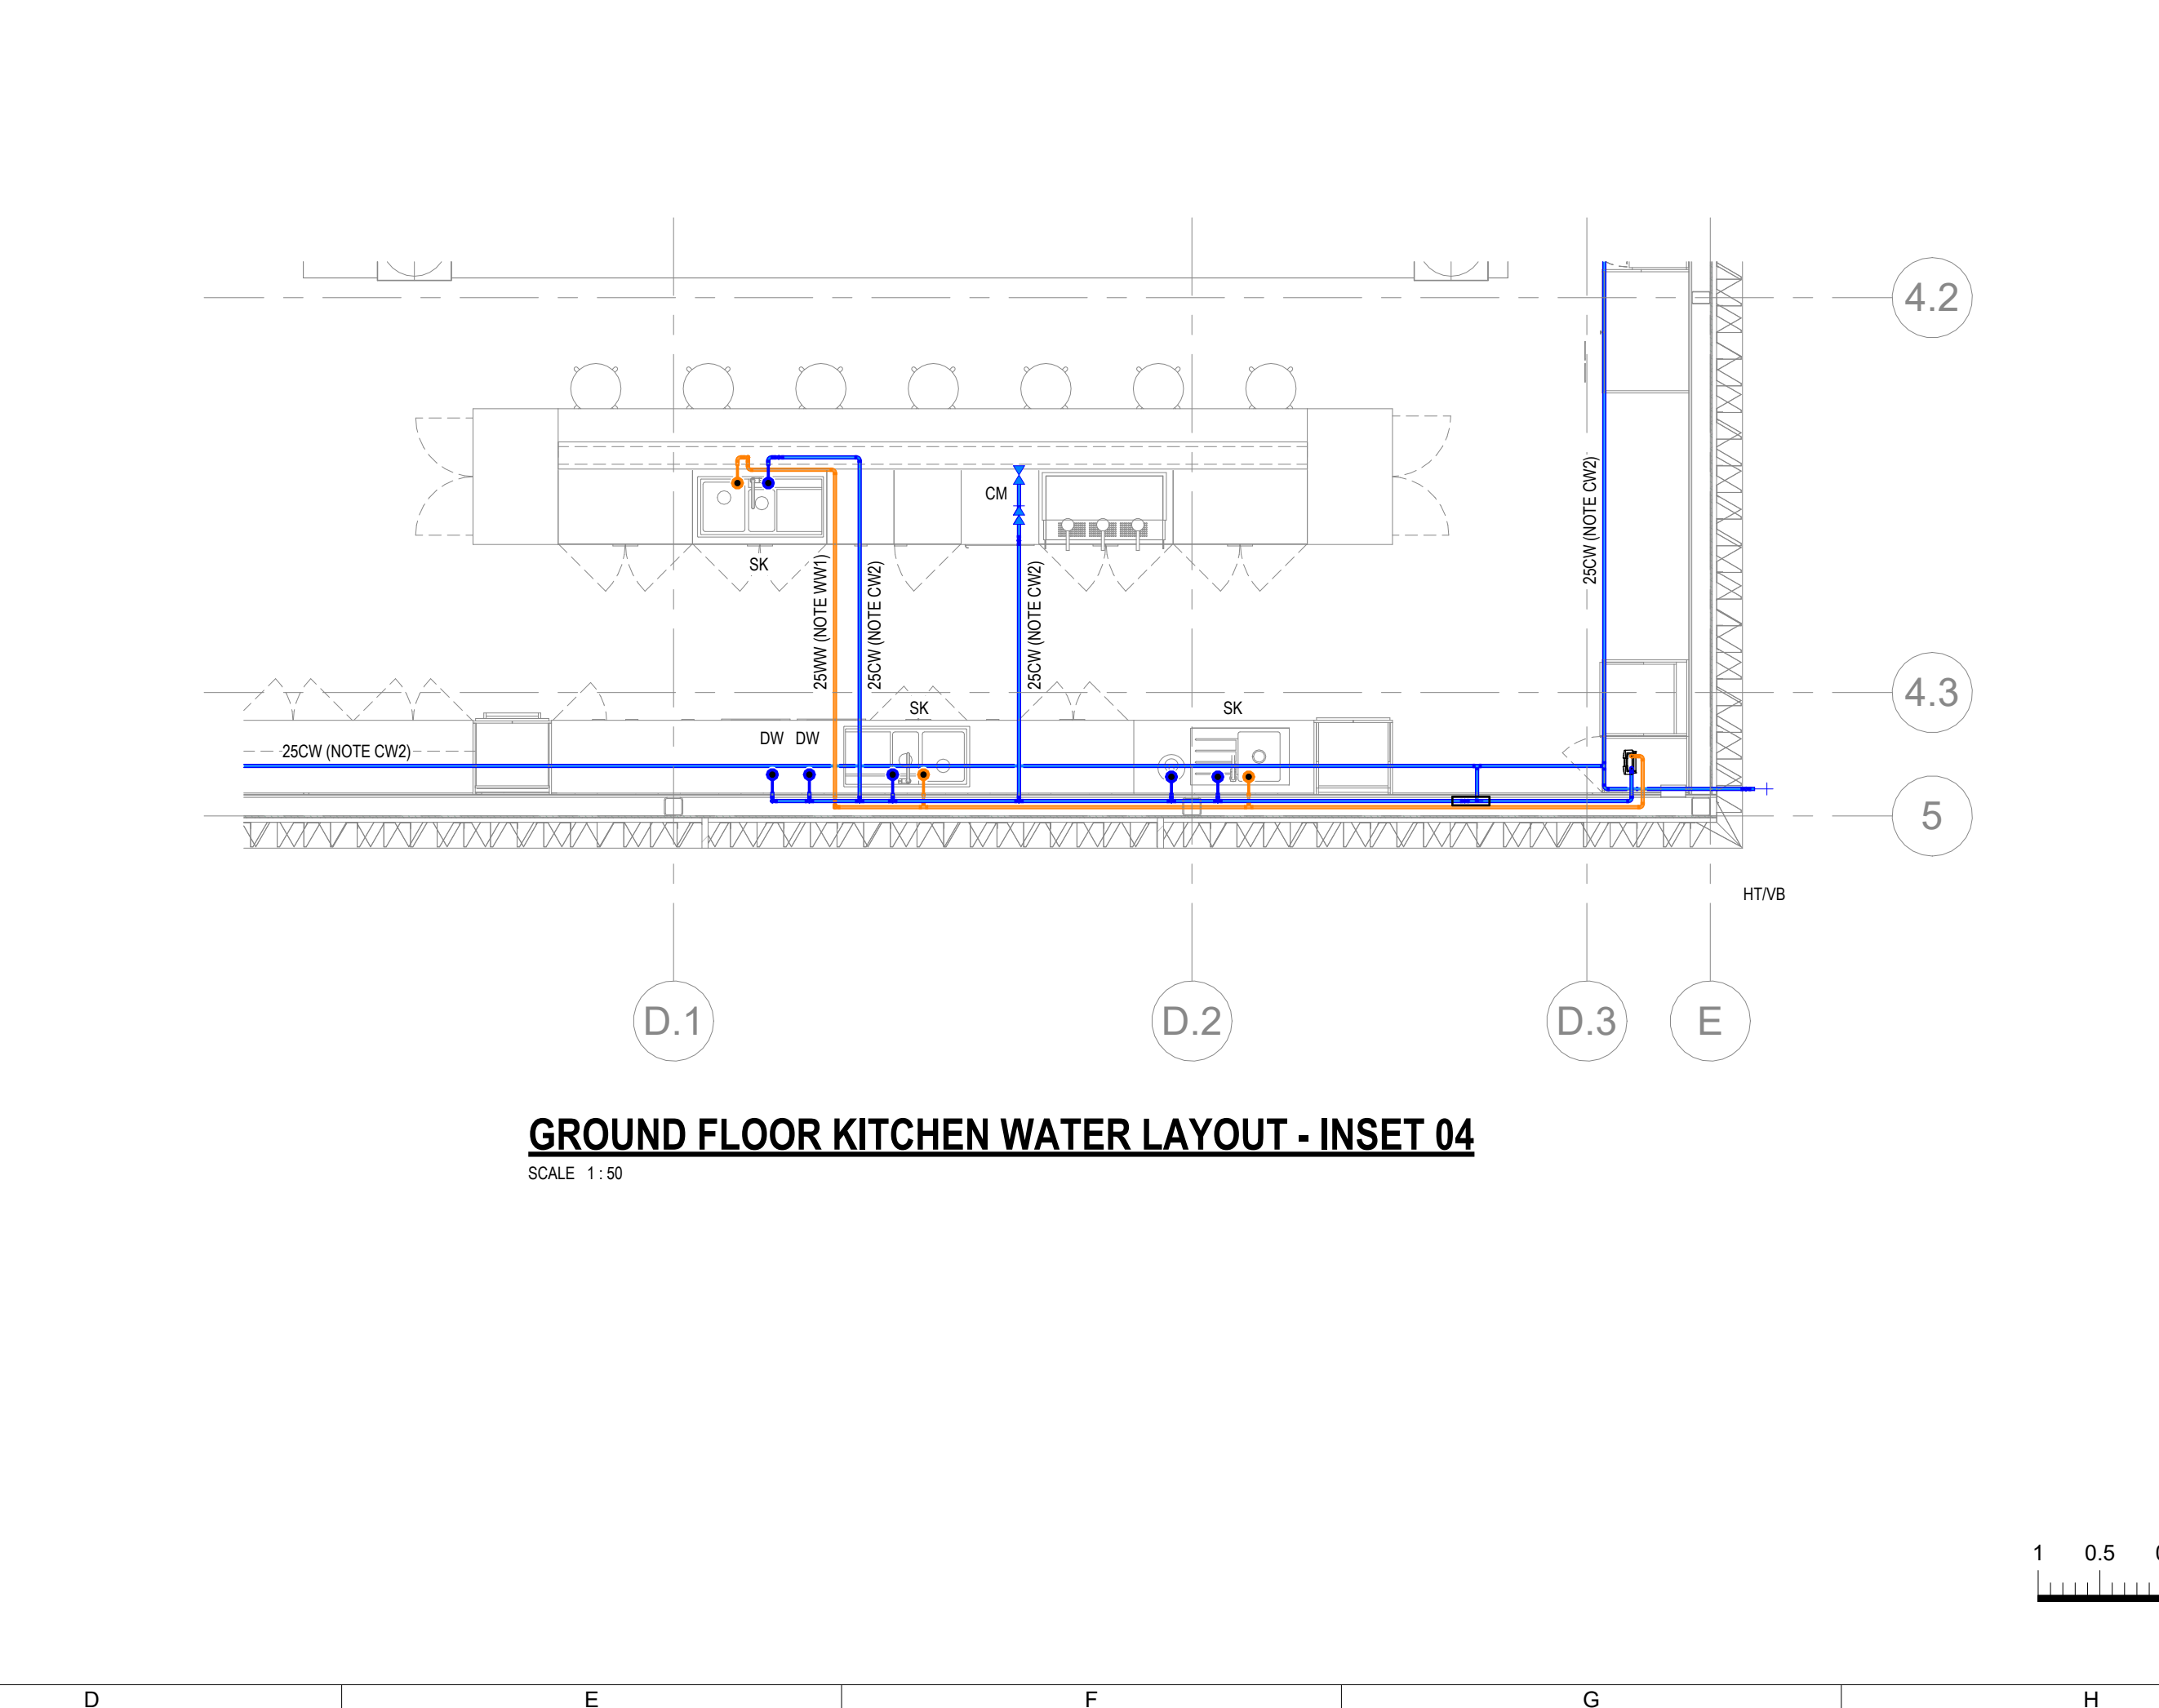

GROUND FLOOR KITCHEN WATER LAYOUT - INSET 04

SCALE 1 : 50

DESIGNER: HARRISON RALPH
QBCC Lic No. 15125080
SOIL CLASSIFICATION: H1

COLD WATER SERVICE NOTES:

NOTE CW1. COLD WATER LOCATED IN GROUND AS NOTED

NOTE CW2. COLD WATER LOCATED IN UNDERCROFT AS NOTED

NOTE CW3. COLD WATER LOCATED IN CEILING AS NOTED

WARM WATER SERVICE NOTES:

NOTE WW1. COLD WATER LOCATED IN UNDERCROFT AS NOTED

NOTE WW2. COLD WATER LOCATED IN CEILING AS NOTED

NORTH	All dimensions to be verified on site prior to commencement of on-site work and/or off-site prefabrication. Figure dimension to be taken in preference to scaled dimensions. This drawing is copyright and remains the property of JWA Consulting Engineers. Reproduction in whole or part of these drawings without written consent constitutes an infringement of copyright.			
	Rev	Date	Verified	
	A	29/08/2025	DRAFT ISSUE	H.R.
	B	03/09/2025	QS ISSUE	H.R.
	C	04/09/2025	REVISED QS ISSUE	H.R.
	D	19/09/2025	100% TENDERED DESIGN	H.R.
EAST	E	31/10/2025	90% CD DRAFT ISSUE	H.R.
	F	28/11/2025	90% CD ISSUE	H.R.
	G	18/12/2025	TENDER ISSUE	H.R.
	H	14/01/2026	ISSUE FOR COUNCIL APPROVAL	H.R.

REAL PROPERTY DESCRIPTION

LOT/PLAN 44SP140243

OWNERS NAME

STANWELL CORPORATION
LIMITED; BRENTON JENSON


CLIENT



ARCHITECT

brian hooperarchitect
m3architecture

CONSULTANT

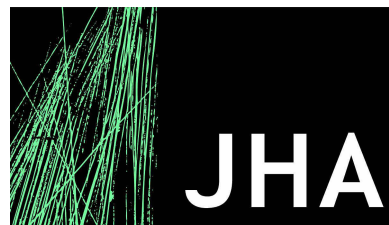

Level 1, 100 Brunswick St
Fortitude Valley
QLD 4006
Australia

+61 (07) 3257 4890

general@ihacengineers.com

புலவர் என்.வி. கிருஷ்ணமூர்த்தி

PROJECT

STANWELL NEW PROJECTS OFFICE

397 POWER STATION ROAD,
STANWELL, QLD 4702

TITLE

HYDRAULIC SERVICES

GROUND FLOOR WATER INSET

APPROVAL ISSUE

NOT TO BE USED FOR CONSTRUCTION

DRAWN	J.P.	SCALE @ A1 1 : 50
CHECKED	H.R.	
APPROVED	H.R.	
CREATED	DEC 25	
JOB No.	DRAWING No.	REV
Q250128	H6001	H

Autodesk Docs://Q250128 Stanwell Office/Q250128 R24 SO MEH.rvt

09/03/2026 1:24:27 pm